


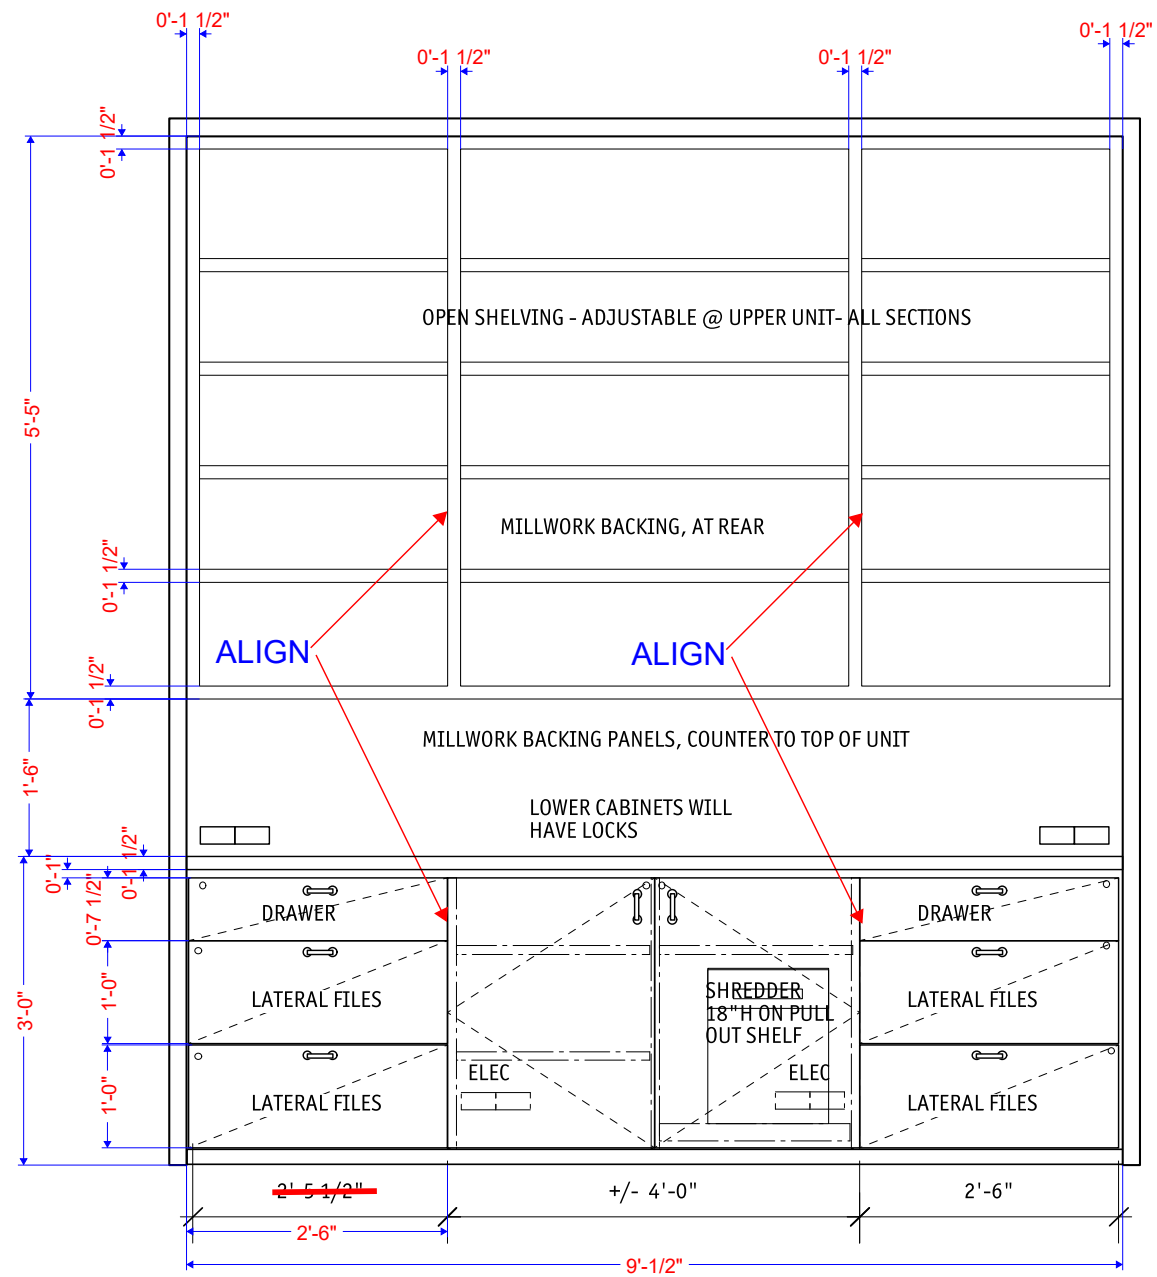


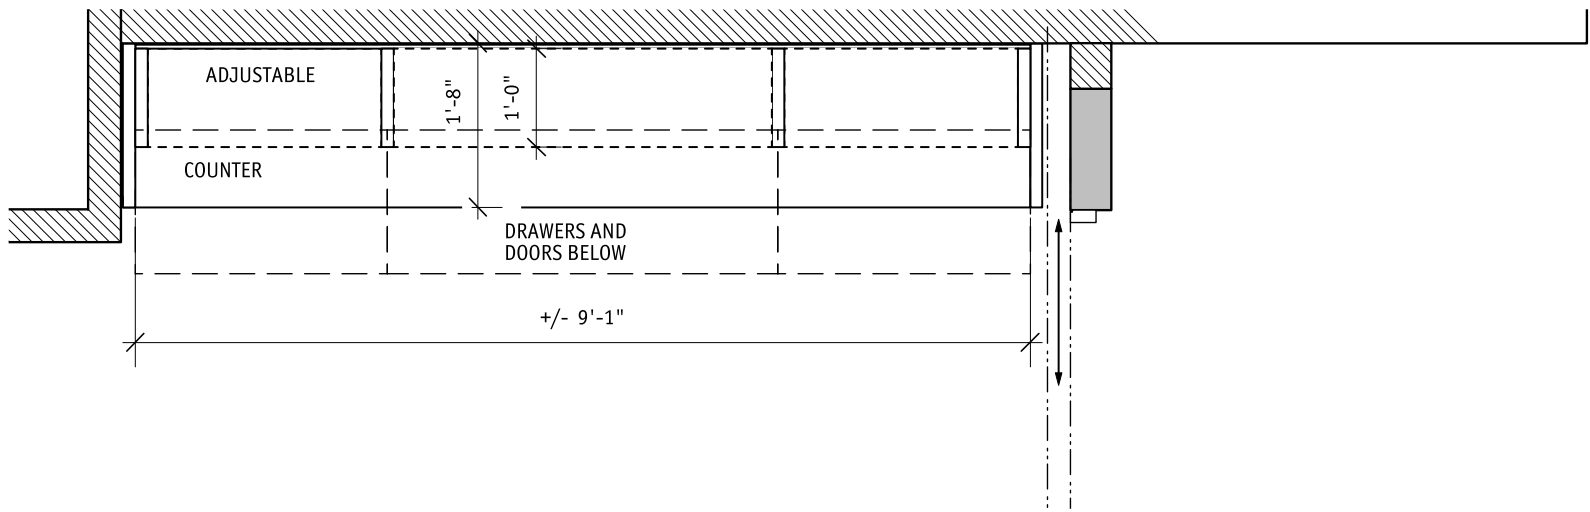


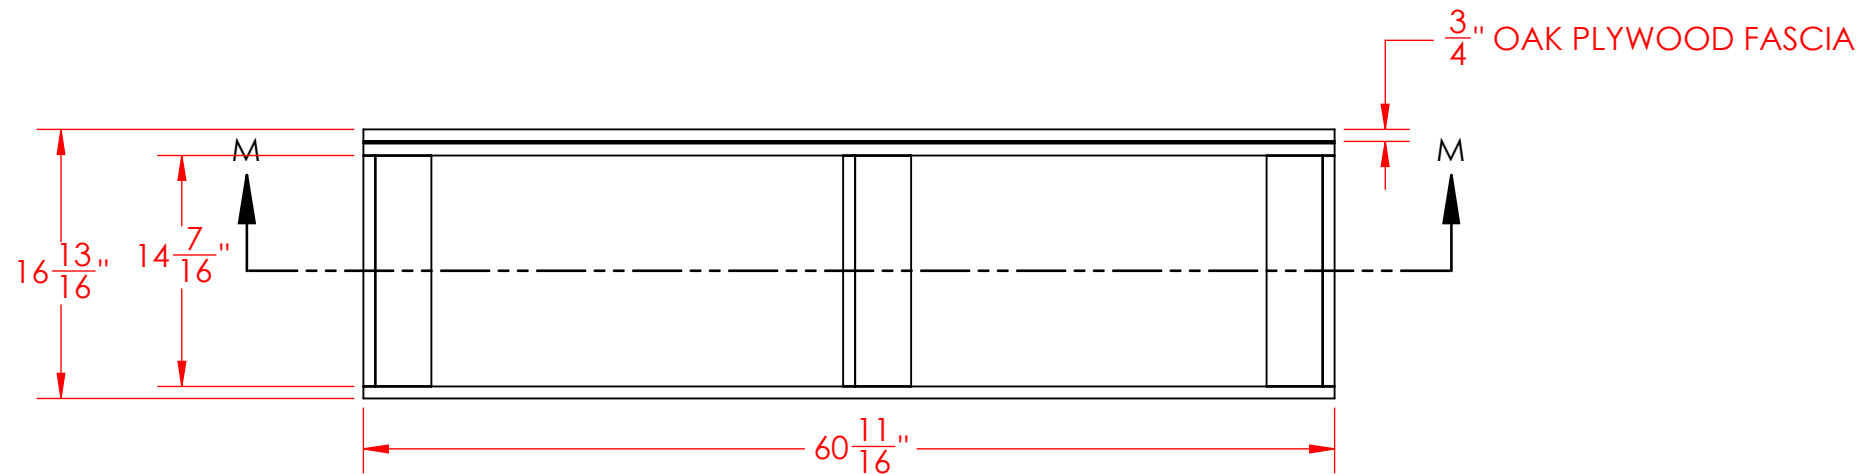

1 FW-03 BASE / TOP VIEW
SCALE 1:12

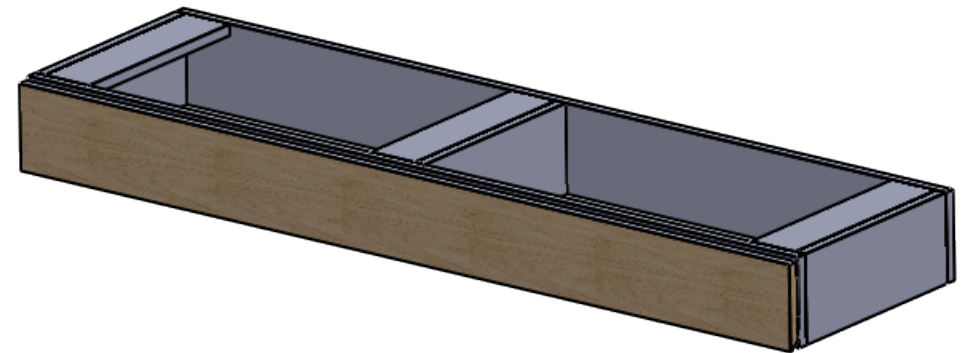

4 FW-03 BASE - DIMETRIC
SCALE 1:12

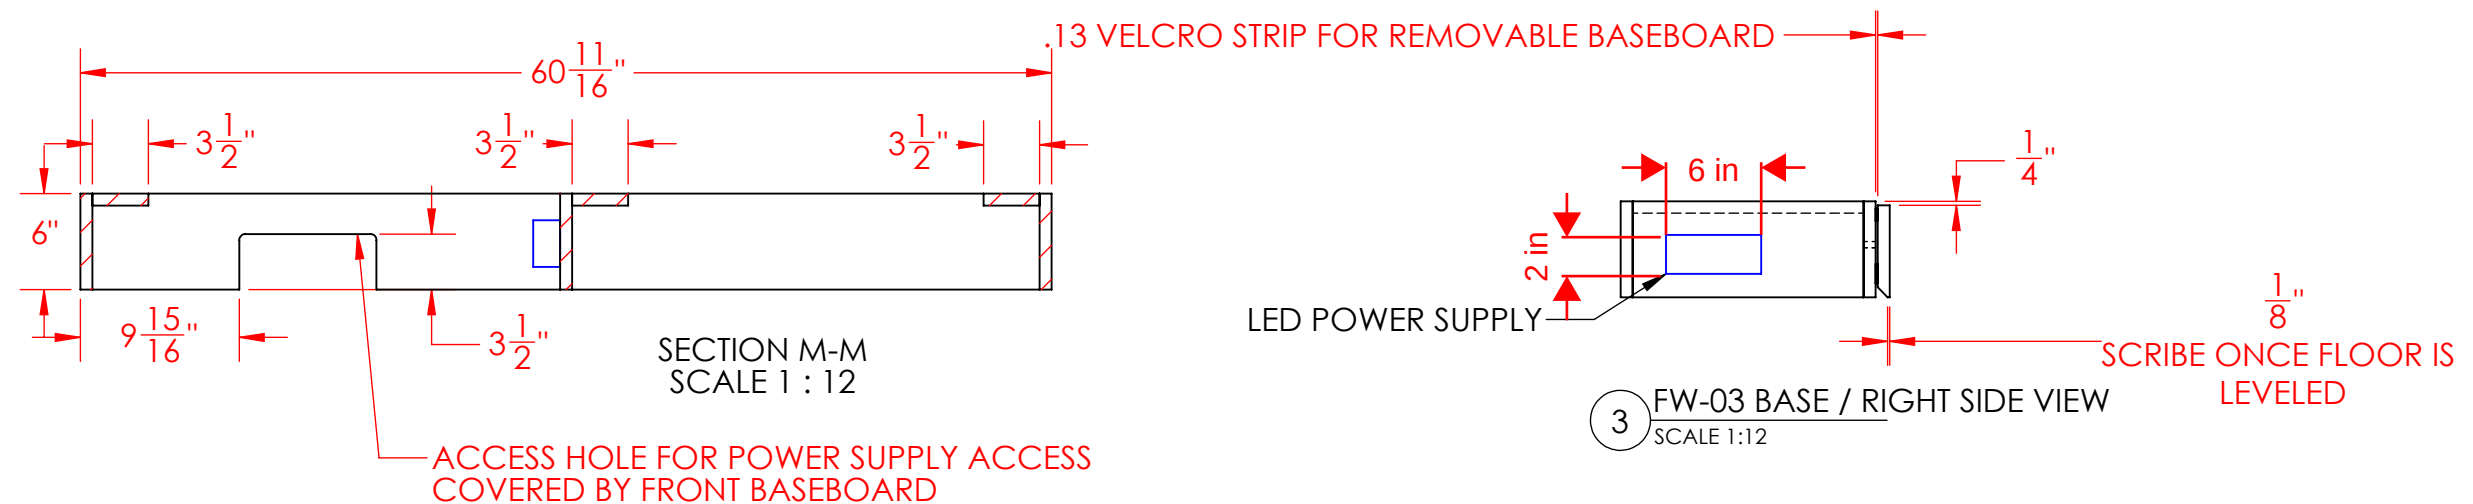

3 FW-03 BASE / RIGHT SIDE VIEW
SCALE 1:12

	CLIENT: Chloé	PM: CHRISTIAN HOOKER	UNIT: FM-03 / BASEBOARD	QTY: 2	DRAWING DATE: 7/11/2022	SHEET NO.
	PROJECT: BAL HARBOUR	DWG BY: Hans Gerlain			VERSION: 1.1	
	ACC DIRECTOR: X	SHEET SCALE: AS NOTED			DELIVERY DATE: XX/XX/2022	

Technical drawing of a cabinet with dimensions and section lines A-A and B-B.

Dimensions:

- Overall width: $108\frac{1}{2}$
- Overall height: $117\frac{1}{4}$
- Top section height: $108\frac{1}{2}$
- Section line A-A width: $111\frac{1}{2}$
- Section line B-B width: $111\frac{1}{2}$
- Top section width: $1\frac{1}{2}$
- Top section height: $1\frac{1}{2}$
- Section line A-A height: $1\frac{1}{2}$
- Section line B-B height: $1\frac{1}{2}$
- Section line A-A width: $7\frac{1}{2}$
- Section line B-B width: $7\frac{1}{2}$
- Section line A-A height: 12
- Section line B-B height: 12
- Section line A-A width: $\frac{3}{4}$
- Section line B-B width: $\frac{3}{4}$


Section Lines:

- Section line A-A: Indicated by a dashed line and arrows labeled A at both ends.
- Section line B-B: Indicated by a dashed line and arrows labeled B at both ends.

The image displays two technical cross-sections, SECTION A-A and SECTION B-B, of a vertical structure. Both sections are drawn to a scale of 0.03 : 0.3.


SECTION A-A: This section shows a vertical profile with a total height of 31½. The top portion is divided into several horizontal layers, with a width of 12 indicated at the top. A horizontal line at a height of 20 from the base indicates a change in the profile. The bottom portion of the section is wider, with a width of 12 indicated at the base.

SECTION B-B: This section shows a similar vertical profile with a total height of 31½. The top portion is divided into several horizontal layers, with a width of 12 indicated at the top. A horizontal line at a height of 20 from the base indicates a change in the profile. The bottom portion of the section is wider, with a width of 12 indicated at the base.

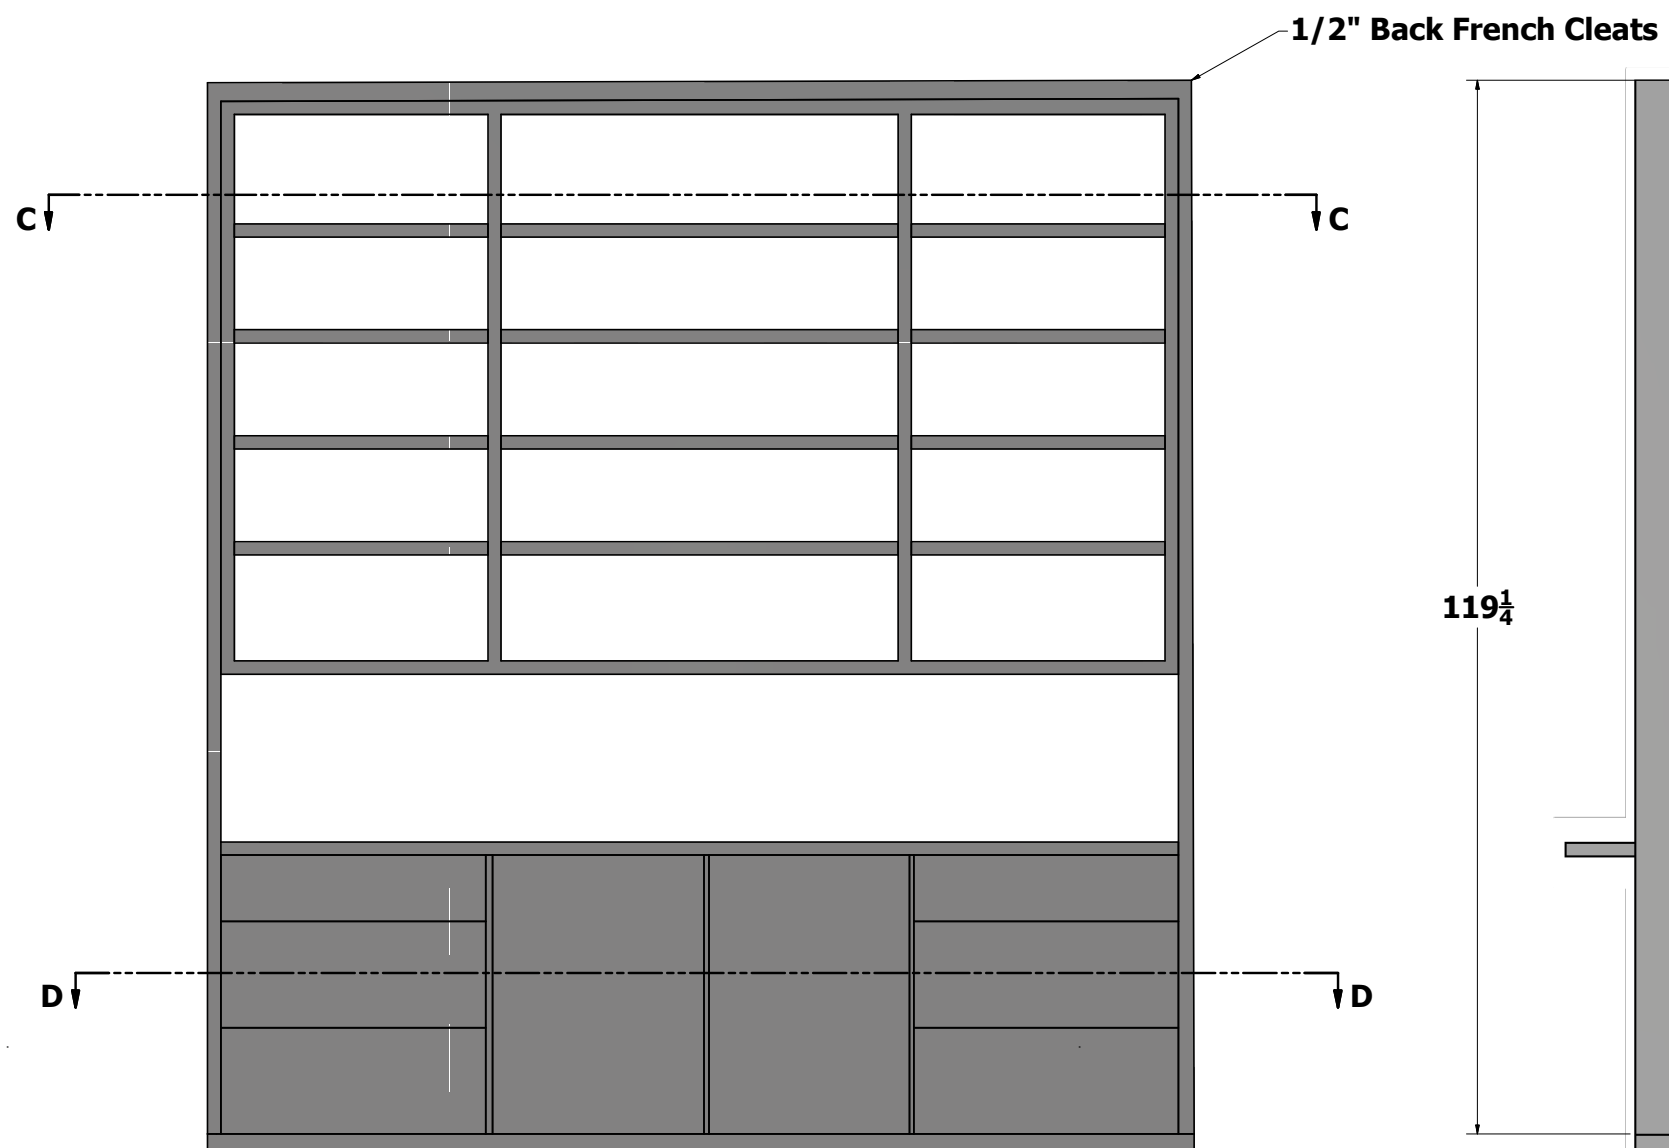

Front View
SCALE 0.03 : 0.3

Right View
SCALE 0.03 : 0.3

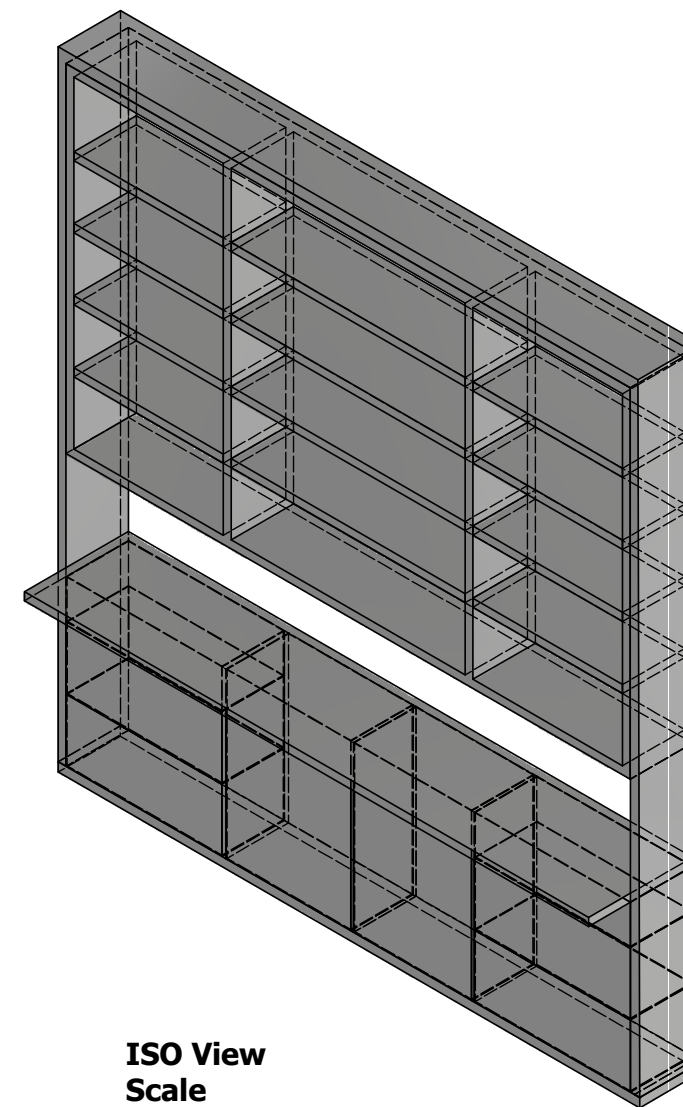

Horizontal Sections

