

AXEL ARIGATO

57 PRINCE STREET
NEW YORK, NY 10012

GROUND LEVEL

MATERIAL LEGEND

FLOOR TILE
(CT-1)
MANF: BY OWNER
STYLE: GRANITE
COLOR: ANTIQUE HAMMERZED
SIZE: 31-1/2"X 31-1/2"X 3/4"
CONTACT:

INSTALLATION: STACKED

GROUT COLOR APPROVAL:
TBD

FLOOR TILE
(CT-2)
MANF: NY STONE
STYLE: SUNNY
COLOR: SUNNY GOLD
SIZE: 24" X 24"X 1/2" THICK
CONTACT:

INSTALLATION: STACKED

GROUT COLOR APPROVAL:
TBD

WALL TILE
(WT-1)
MANF: MOSA
STYLE: GLOBAL COLLECTION/GLOBALGRIP
COLOR: PLAIN NPLES YELLOW #16670
SIZE: 6"X 6"
CONTACT:

GROUT COLOR APPROVAL:
TBD

STONE COUNTERTOP
(ST)
MANF: BY OWNER
STYLE: TBD
COLOR: TBD
SIZE: 3/4"
CONTACT:

DRAWING LEGEND:

CS-001	COVER SHEET, DRAWING LEGEND & MATERIAL LEGEND
T-001	KEYPLAN - GROUND FLOOR
T-100	FLOOR PLAN- GROUND LEVEL
T-101	PLAN/ELEVATIONS - TOILET ROOM
T-102	STONE COUNTERTOP - GROUND LEVEL
T-103	STONE COUNTERTOP - GROUND LEVEL
T-200	DETAILS - TILE
T-201	DETAILS - TILE
T-202	DETAILS - STONE COUNTERTOP
T-203	DETAILS - STONE COUNTERTOP

ARCHITECT TO CONFIRM:

GROUT JOINT AT CT-1 TO BE BUTT JOINT "
GROUT JOINT AT CT-2 TO BE BUTT JOINT"
GROUT JOINT AT WT-1 TO BE 1/8"

PLEASE NOTE:

NO EXPANSION JOINTS ARE SHOWN IN THE TILE FLOORING AS THERE ARE NO EXPANSION JOINTS SHOWN IN THE ARCHITECTURAL DRAWINGS. IF EXPANSION OR MOVEMENT JOINTS ARE REQUIRED, ARCHITECT TO PROVIDE LOCATION AND DETAILS ACCORDINGLY

PER THE TCNA, "USE OF WALL-WASHER AND COVE-TYPE LIGHTING, WHERE THE LIGHTS ARE LOCATED EITHER AT THE WALL/CEILING INTERFACE OR MOUNTED DIRECTLY ON THE WALL, ARE POPULAR TECHNIQUES FOR PRODUCING DRAMATIC ROOM LIGHTING EFFECTS. WHEN PROPER BACKING SURFACES, INSTALLATION MATERIALS AND METHODS, AND LOCATION OF LIGHT FIXTURES ARE NOT CAREFULLY COORDINATED, THESE LIGHTING TECHNIQUES MAY PRODUCE SHADOWS AND UNDESIRABLE EFFECTS WITH CERAMIC TILES, SIMILAR SHADOWS ARE CREATED FROM SIDE LIGHTING INTERIOR WALLS AND FLOORS WHEN LIGHT SHINES AT THAT ANGLE THROUGH WINDOWS AND DOORS."

PLEASE TAKE NOTE OF THIS AS IT RELATES TO THE TILE IN THIS PROJECT.

AUSTRO TILE & STONE, LLC
30-25 93RD STREET
EAST ELMHURST, NY 11369

CONTRACTOR:
JRM CONSTRUCTION
MANAGEMENT, LLC
242 WEST 36TH STREET
11TH FLOOR
NEW YORK, NY 10018

INTERIOR DESIGNER:

ISSUE FOR APPROVAL	04/29/24
ISSUE NAME	DATE

PROJECT:

SARGENT
461 FROM RD SUITE 255,
PARAMUS, NJ 07652
PHONE:972.253.9393

PROJECT NAME:


AXEL ARIGATO
57 PRINCE STREET
NEW YORK, NY 10012

SHEET NAME:

COVER SHEET

DATE:	
PROJECT NO.:	
PRINCIPAL:	
DRAWING BY:	
CHECKED BY:	
SCALE:	AS NOTED
DWG No.:	
CS-001	
1 of 10	

LOCATION

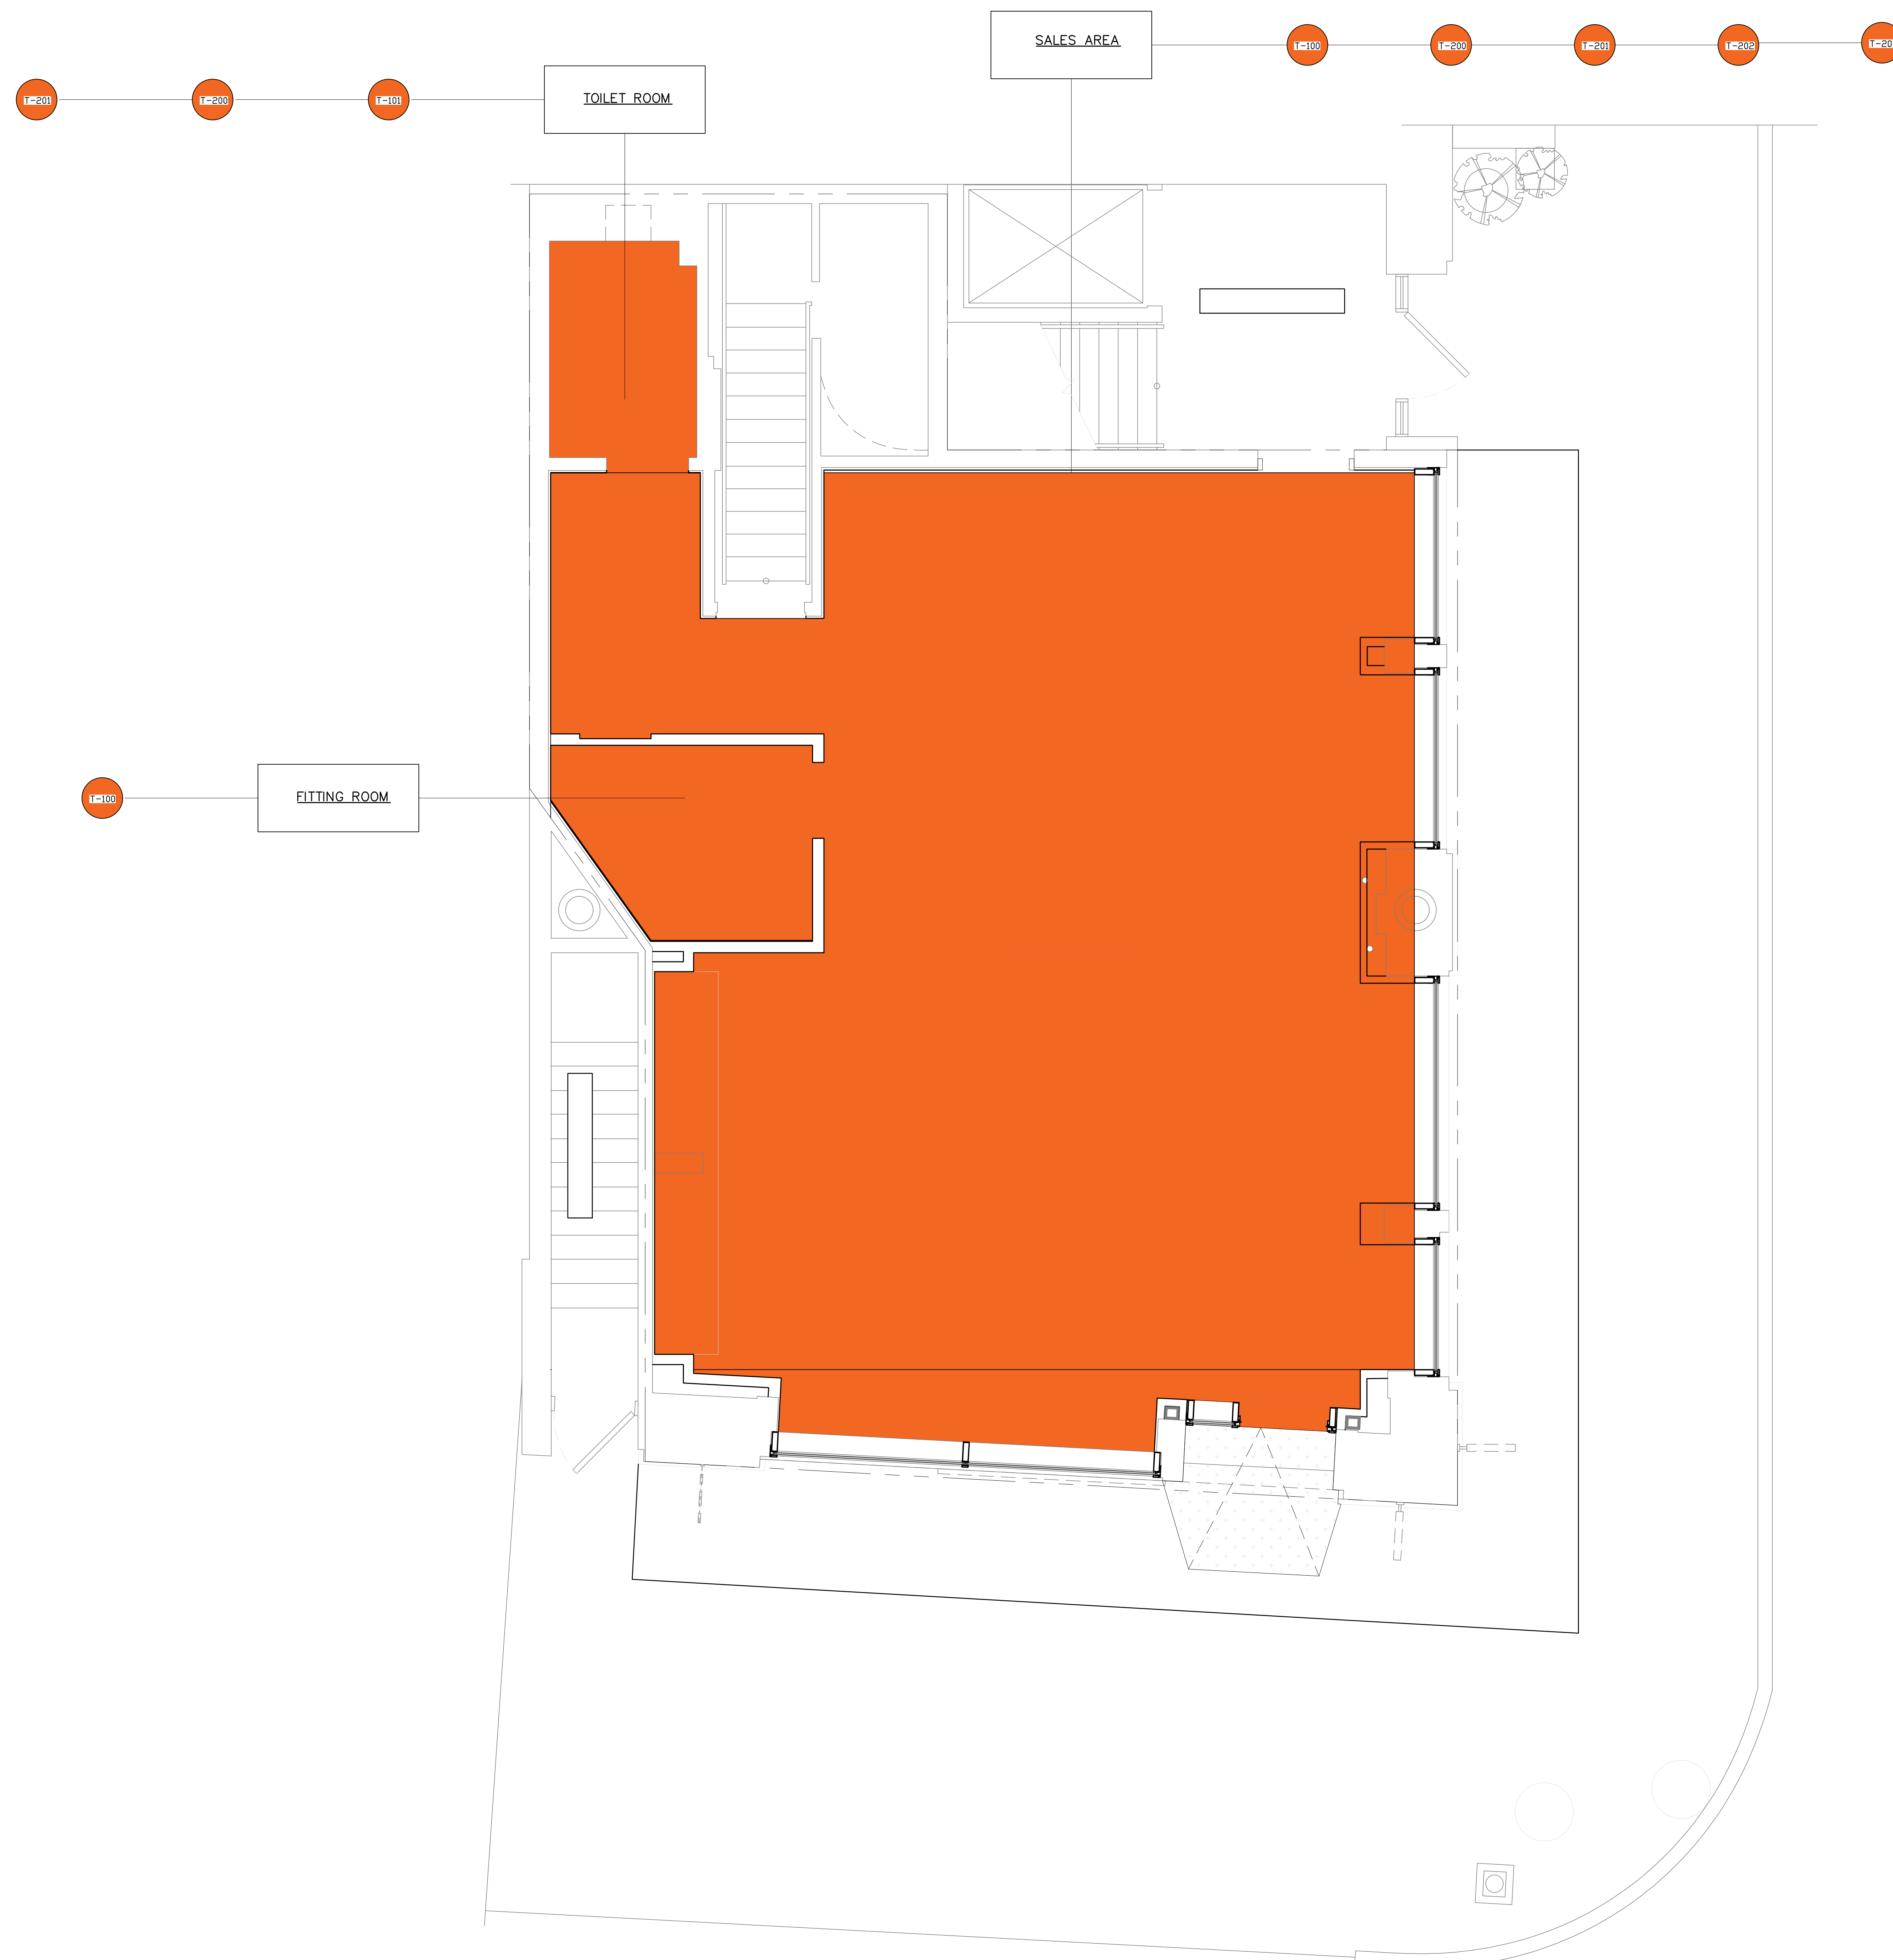

AUSTRO TILE & STONE, LLC
30-25 93RD STREET
EAST ELMHURST, NY 11369

CONTRACTOR:

JRM CONSTRUCTION
MANAGEMENT, LLC
242 WEST 36TH STREET
11TH FLOOR
NEW YORK, NY 10018

INTERIOR DESIGNER:

[illegible]

ISSUE FOR APPROVAL	04/29/24
ISSUE NAME	DATE

SARGENT
461 FROM RD SUITE 255,
PARAMUS, NJ 07652
PHONE:972.253.9393

PROJECT NAME:

AXEL ARIGATO
57 PRINCE STREET
NEW YORK, NY 10012

SHEET NAME:

KEYPLAN
CELLAR


DATE: _____
PROJECT NO.: _____
PRINCIPAL: _____
DRAWING BY: _____
CHECKED BY: _____
SCALE: _____
DWG No.: _____
KY-001
2 of 10



STARTING POINT



01 1/2"=1'-0"	PLAN: GROUND LEVEL
------------------	--------------------

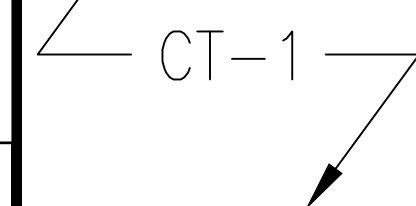

02 ENLARGED PLAN: GROUND LEVEL



AUSTRO TILE & STONE, LLC
30-25 93RD STREET
EAST ELMHURST, NY 11369

CONTRACTOR:
JRM CONSTRUCTION
MANAGEMENT, LLC
242 WEST 36TH STREET
11TH FLOOR
NEW YORK, NY 10018

INTERIOR DESIGNING

[illegible]

ISSUE FOR APPROVAL	04/29/24
ISSUE NAME	DATE

ARCHITECT

SARGENT

461 FROM RD SUITE 255,
PARAMUS, NJ 07652
PHONE:972.253.9393

PROJECT NAME:

AXEL ARIGATO
57 PRINCE STREET
NEW YORK, NY 10012

SHIFT MM


PLAN

DATE:
PROJECT NO.:
PRINCIPAL:
DRAWING BY:
CHECKED BY:
SCALE:

DWG No.:
T-100
3




STARTING POINT

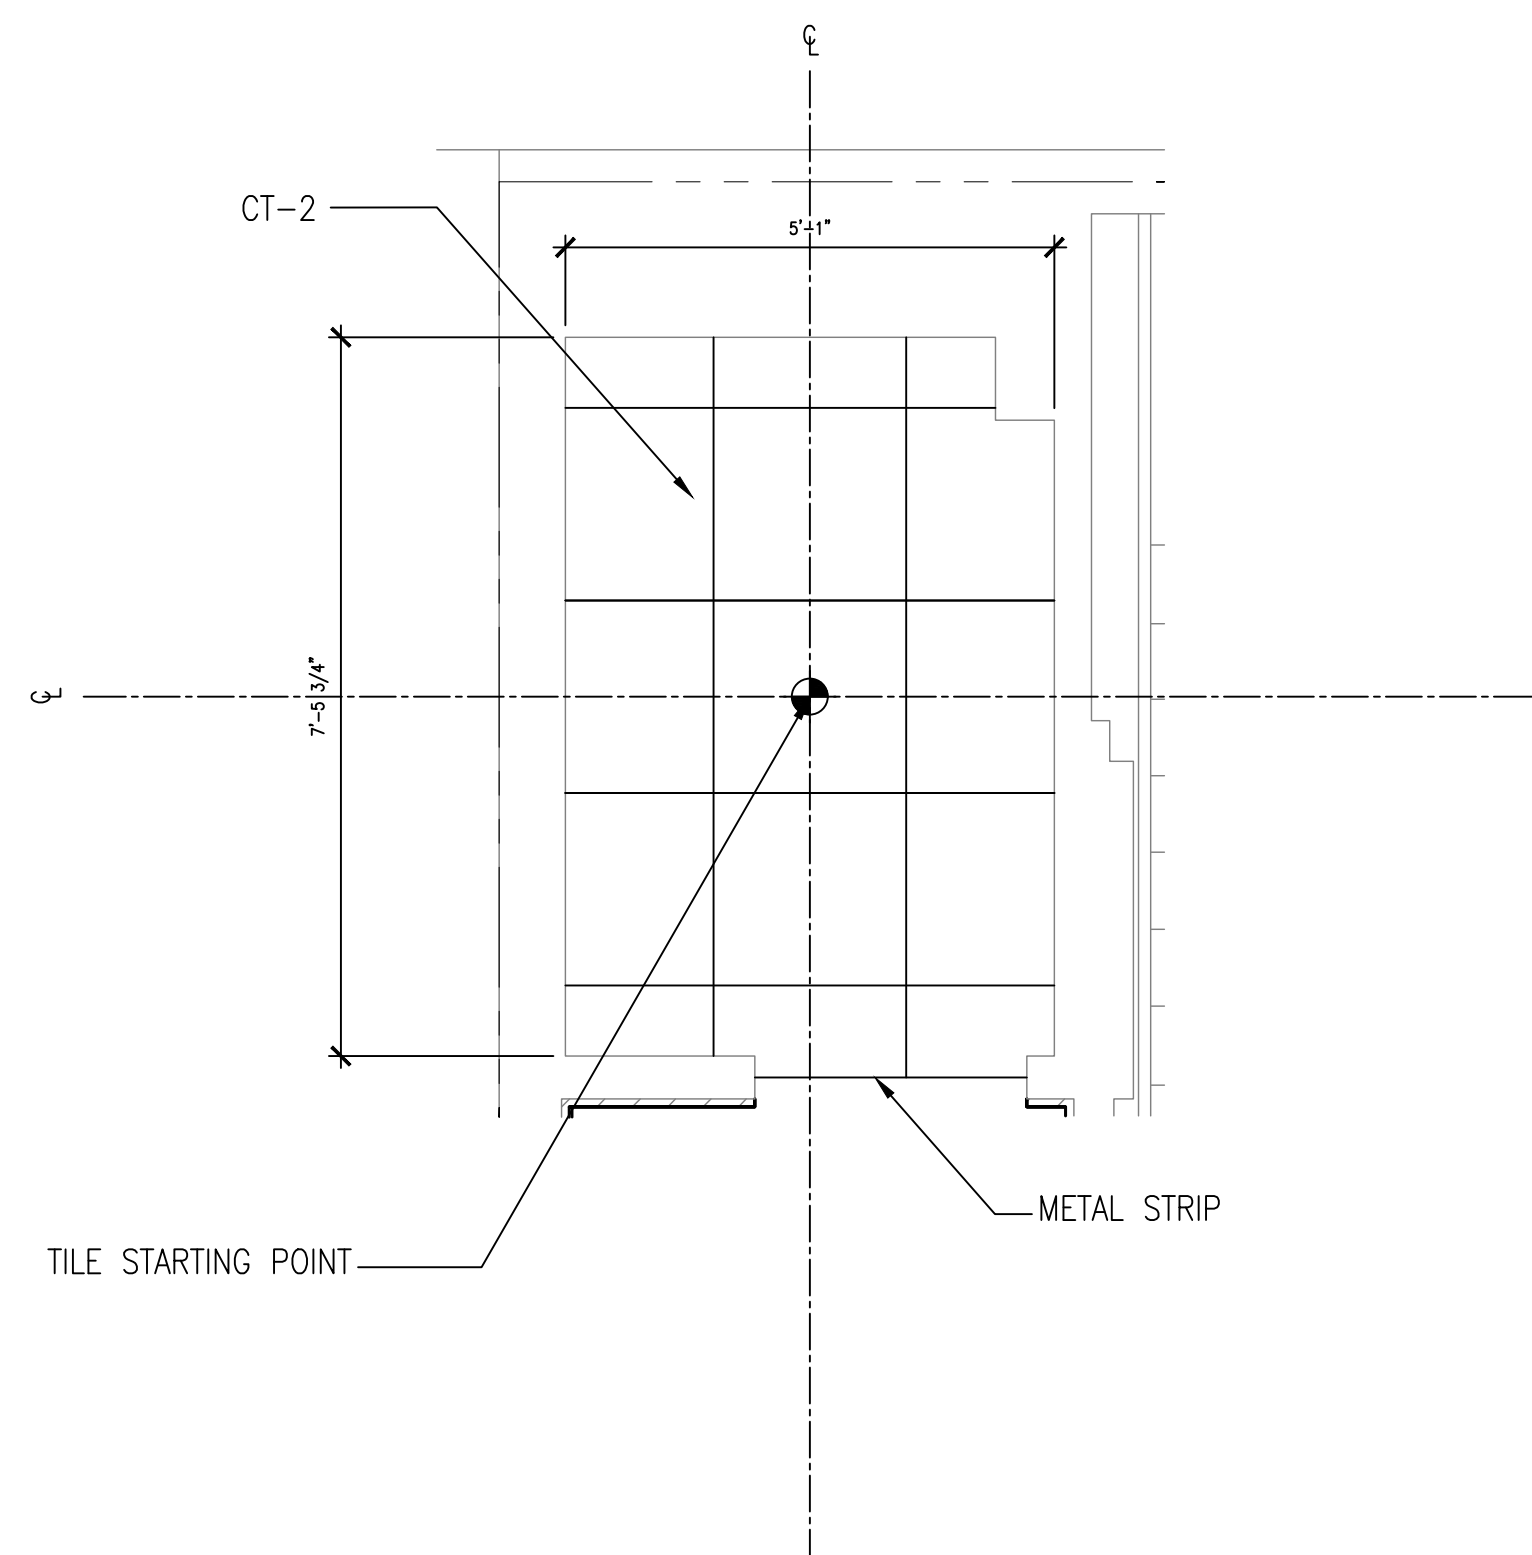


01
1/2"=1'-0"

PLAN: TOILET ROOM

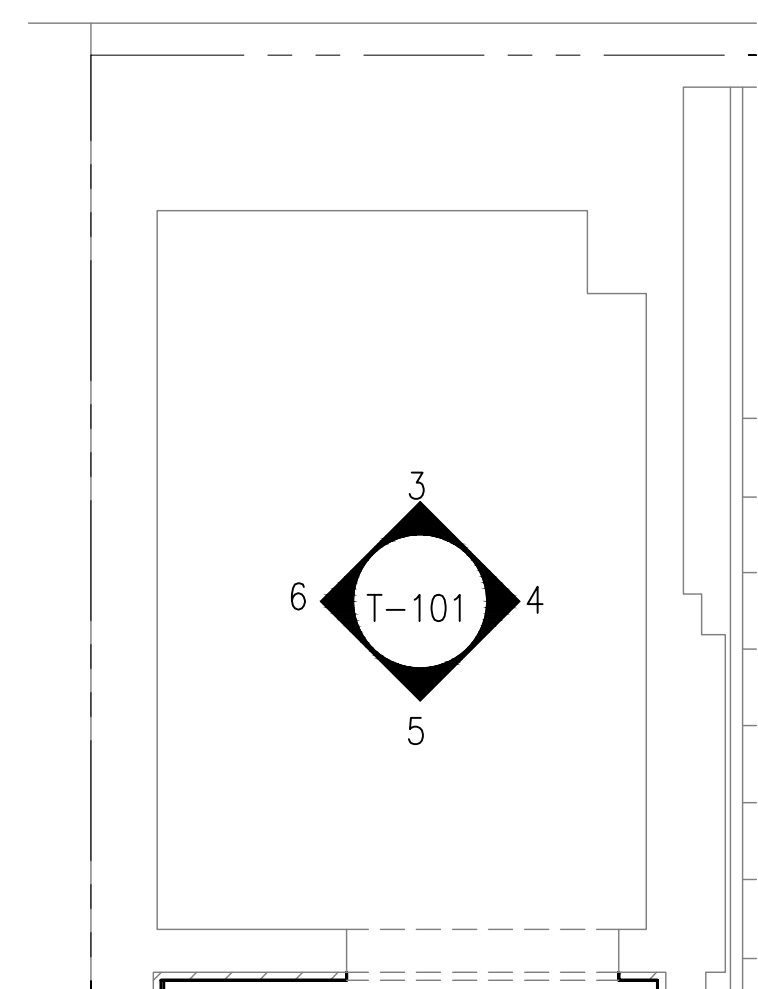


02

PLAN: TOILET ROOM

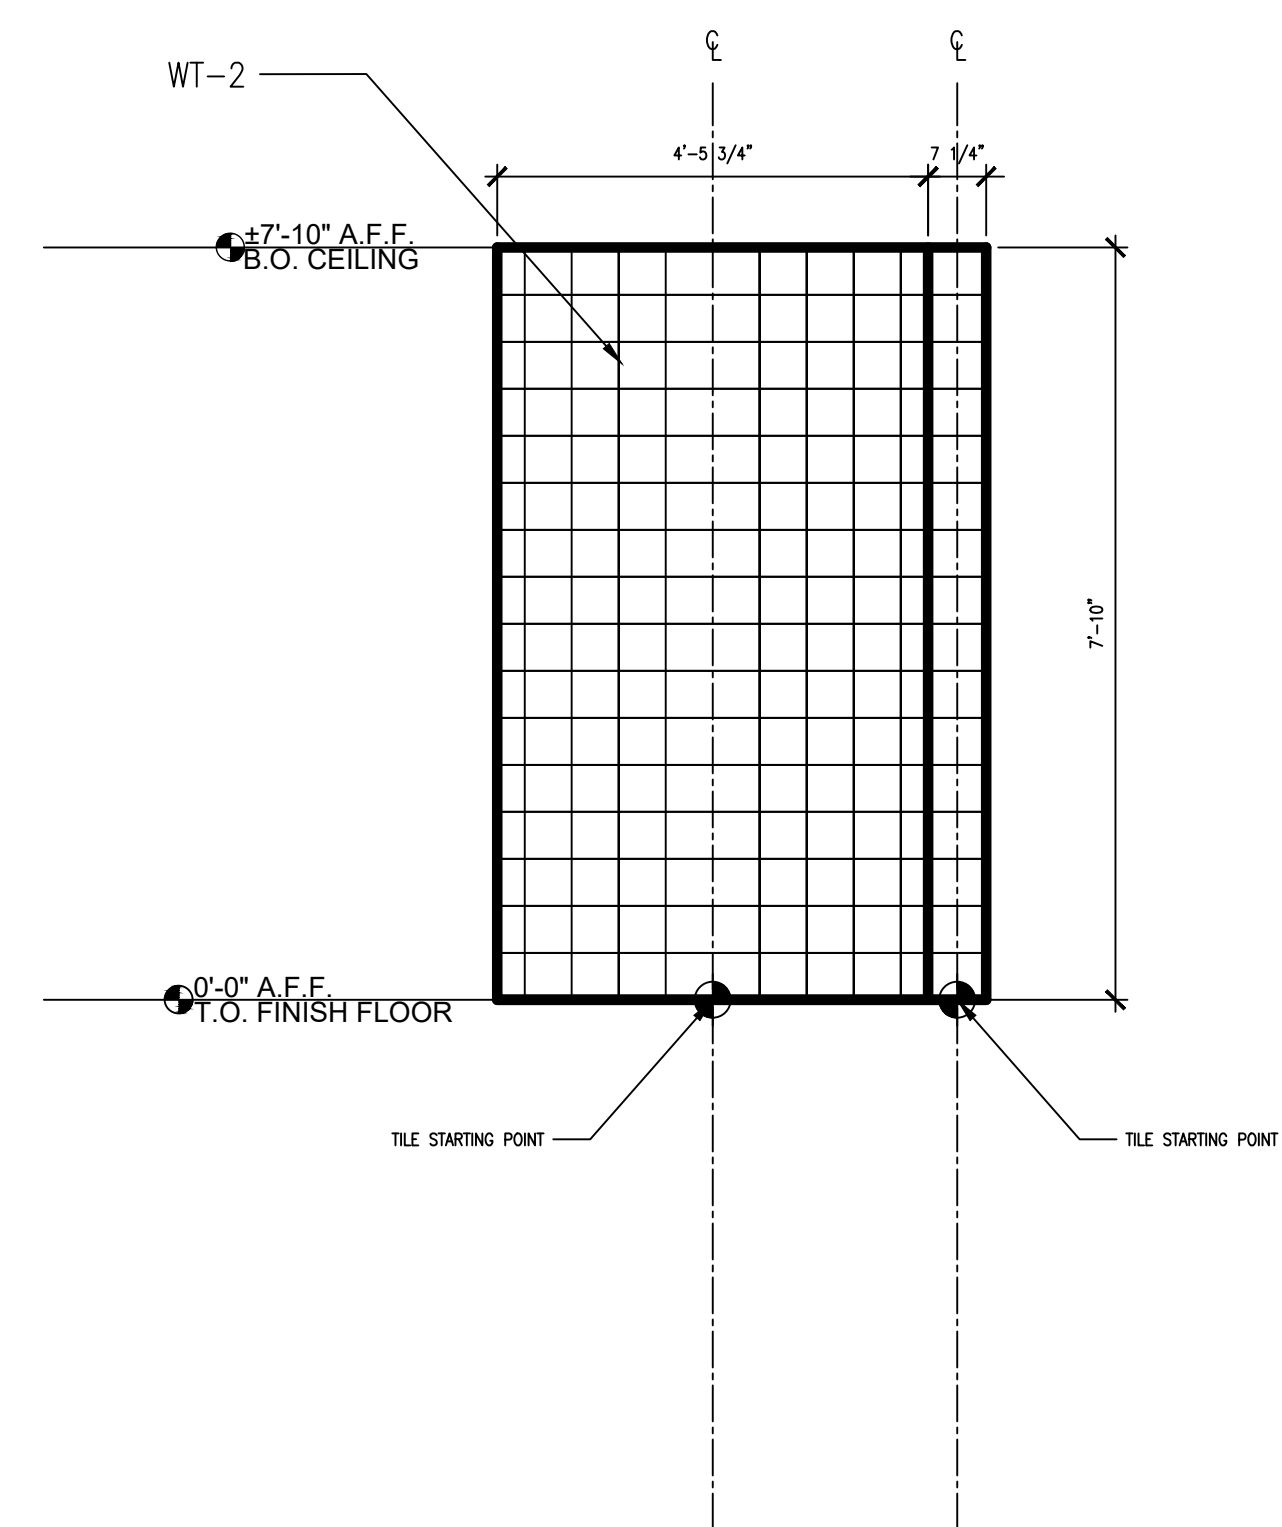


03
1/2"=1'-0"

ELEVATION: NORTH

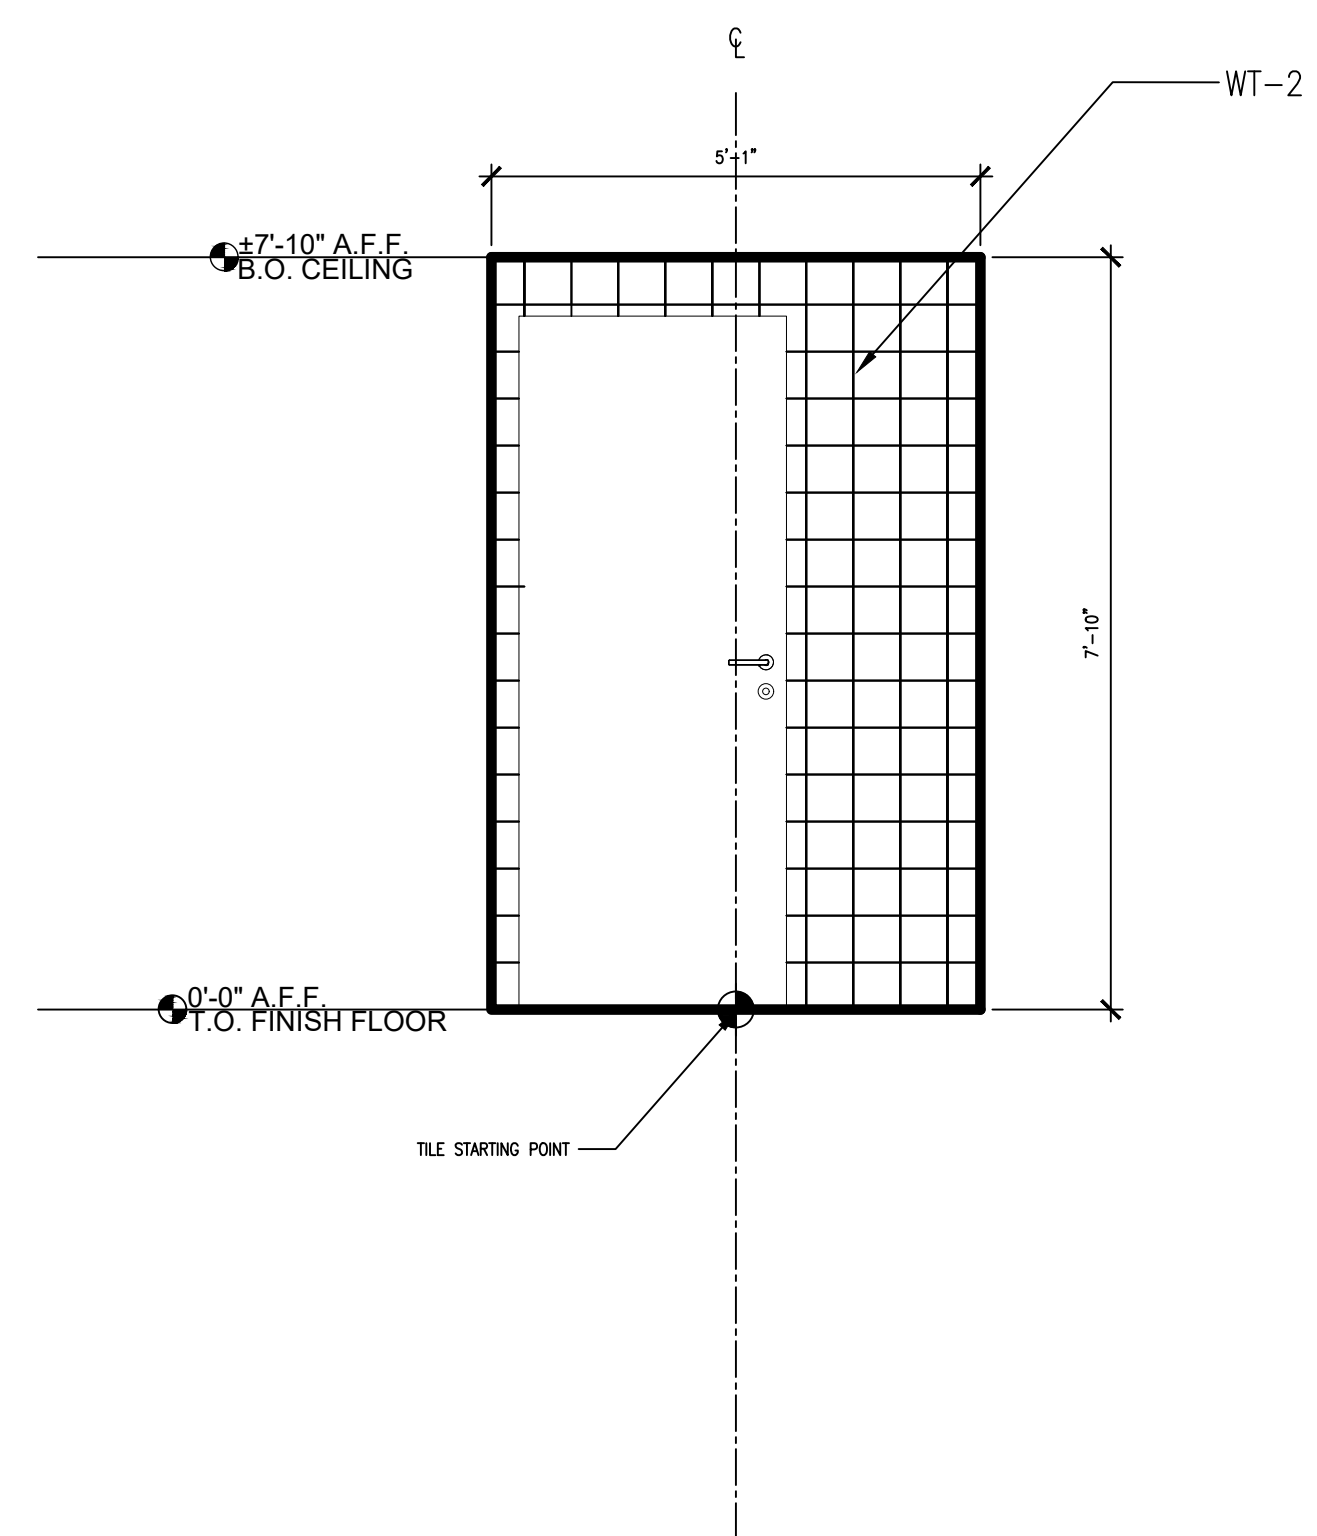


05

ELEVATION: SOUTH

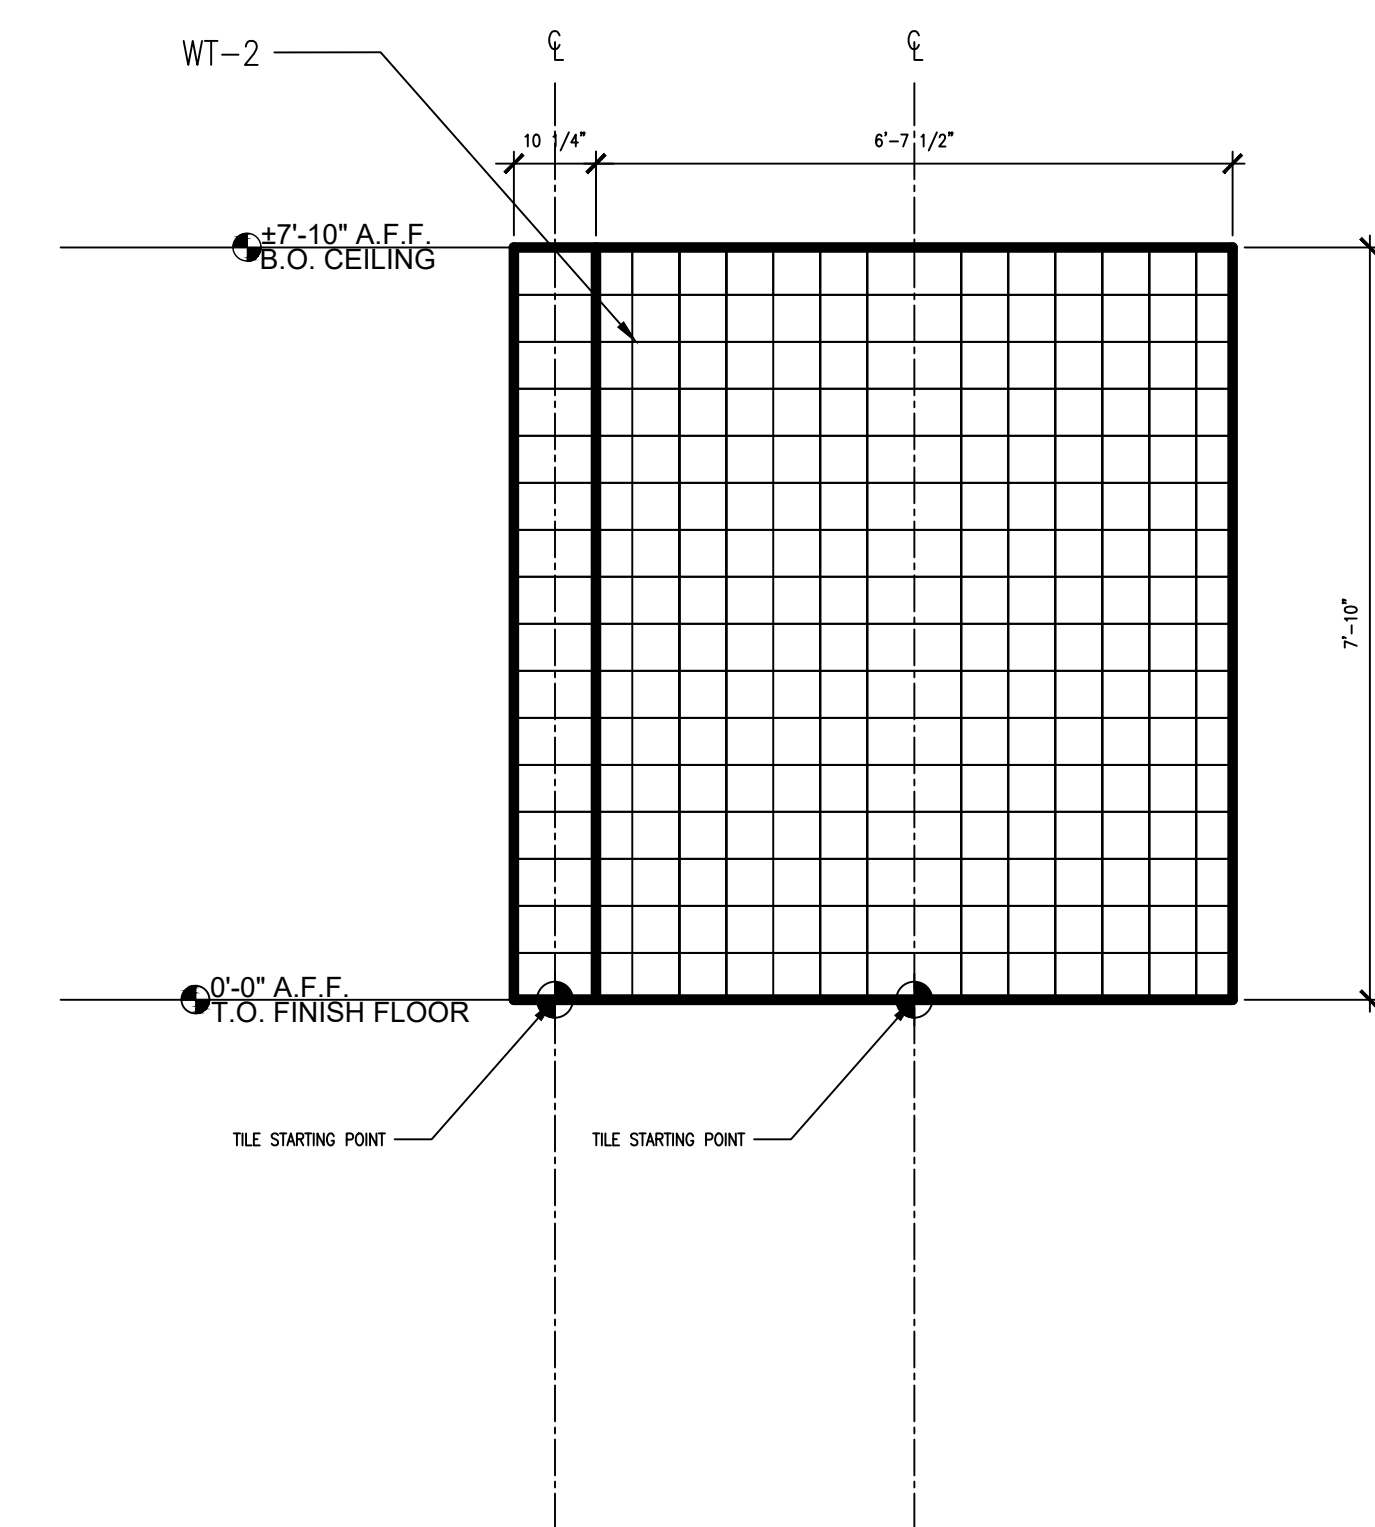

04
1/2"=1'-0"

ELEVATION: EAST

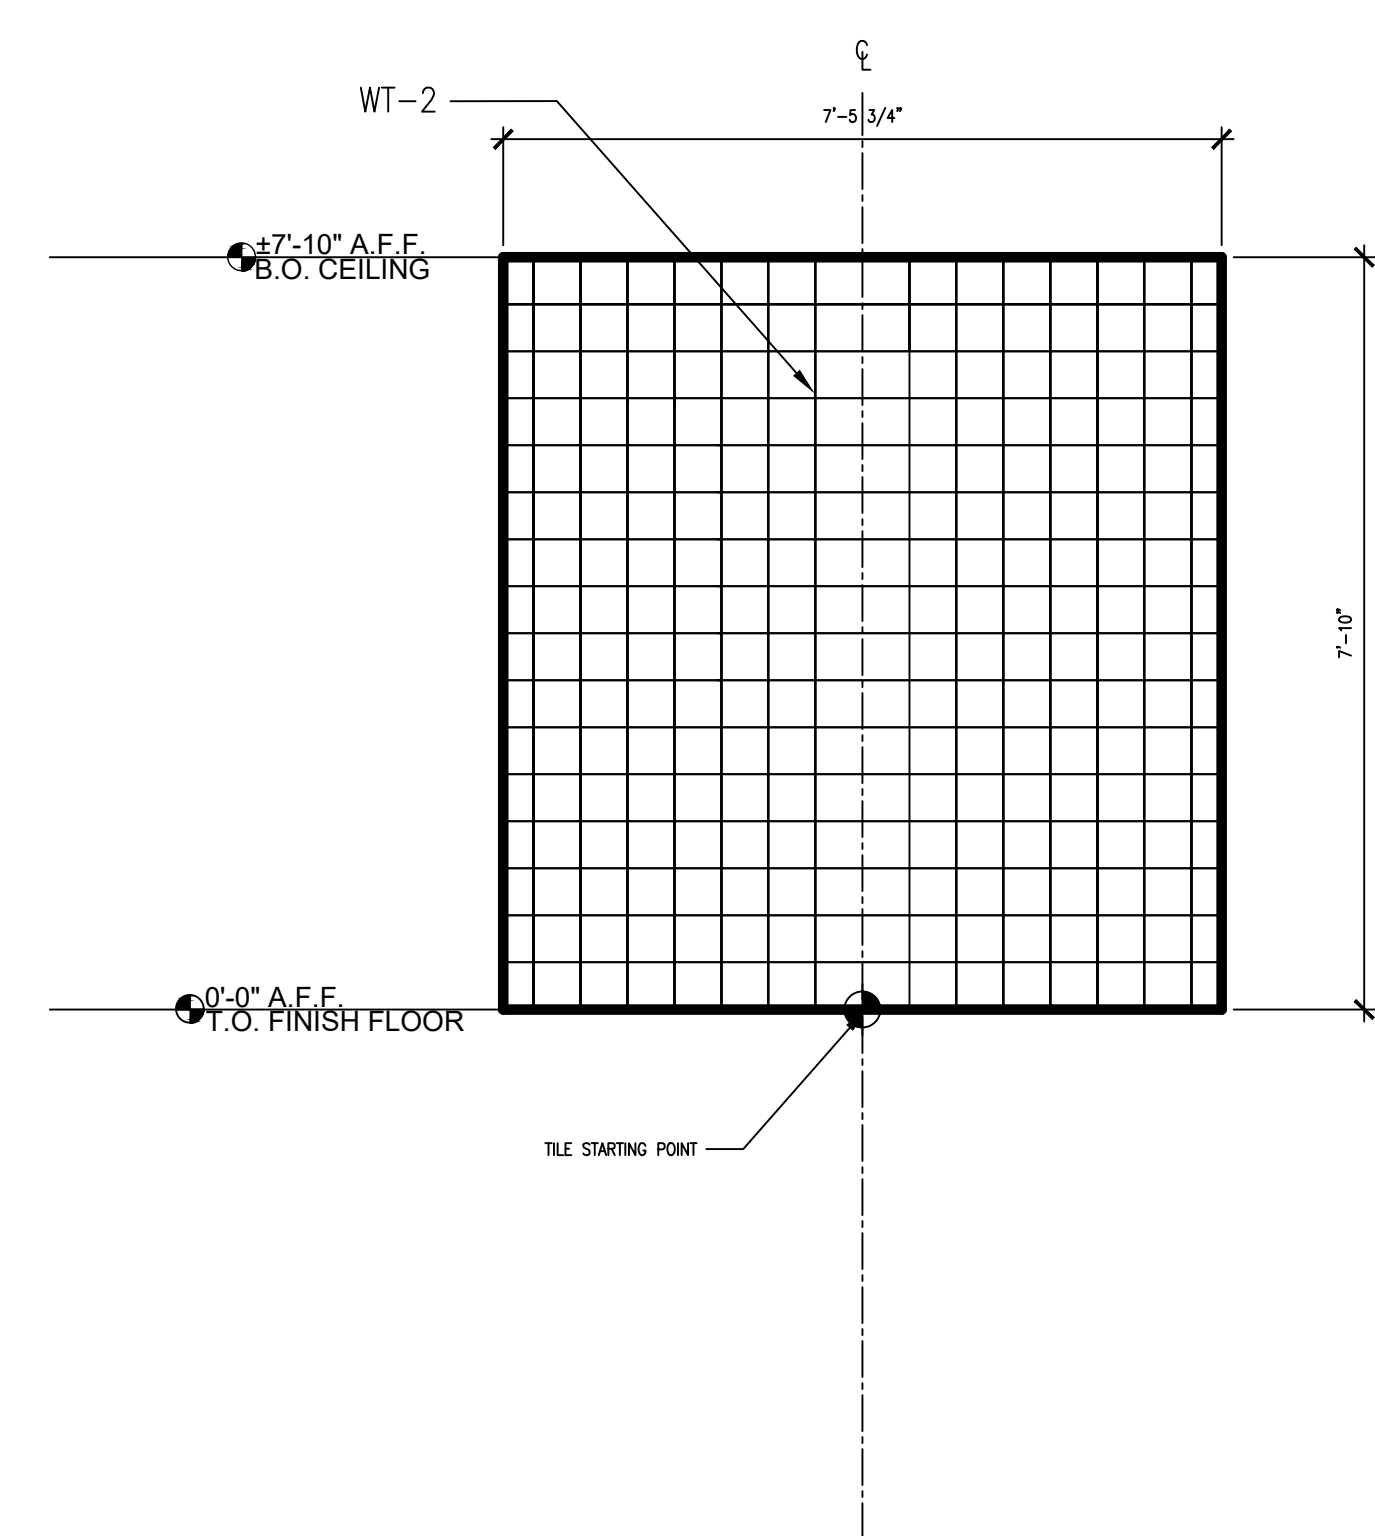

06

ELEVATION: WEST

AUSTRO TILE & STONE, LLC

30-25 93RD STREET
EAST ELMHURST, NY 11369

CONTRACTOR:

JRM CONSTRUCTION
MANAGEMENT, LLC

242 WEST 36TH STREET
11TH FLOOR
NEW YORK, NY 10018

INTERIOR DESIGNER:

ISSUE FOR APPROVAL	04/29/24
--------------------	----------

ISSUE NAME	DATE
------------	------

ARCHITECT:

SARGENT

461 FROM RD SUITE 255,
PARAMUS, NJ 07652

PHONE:972.253.9393




PROJECT NAME:

AXEL ARIGATO
57 PRINCE STREET
NEW YORK, NY 10012

SHEET NAME:

PLAN/
ELEVATIONS

DATE:
PROJECT NO.:
PRINCIPAL:
DRAWING BY:
CHECKED BY:
SCALE:
DWG No.:
T-101

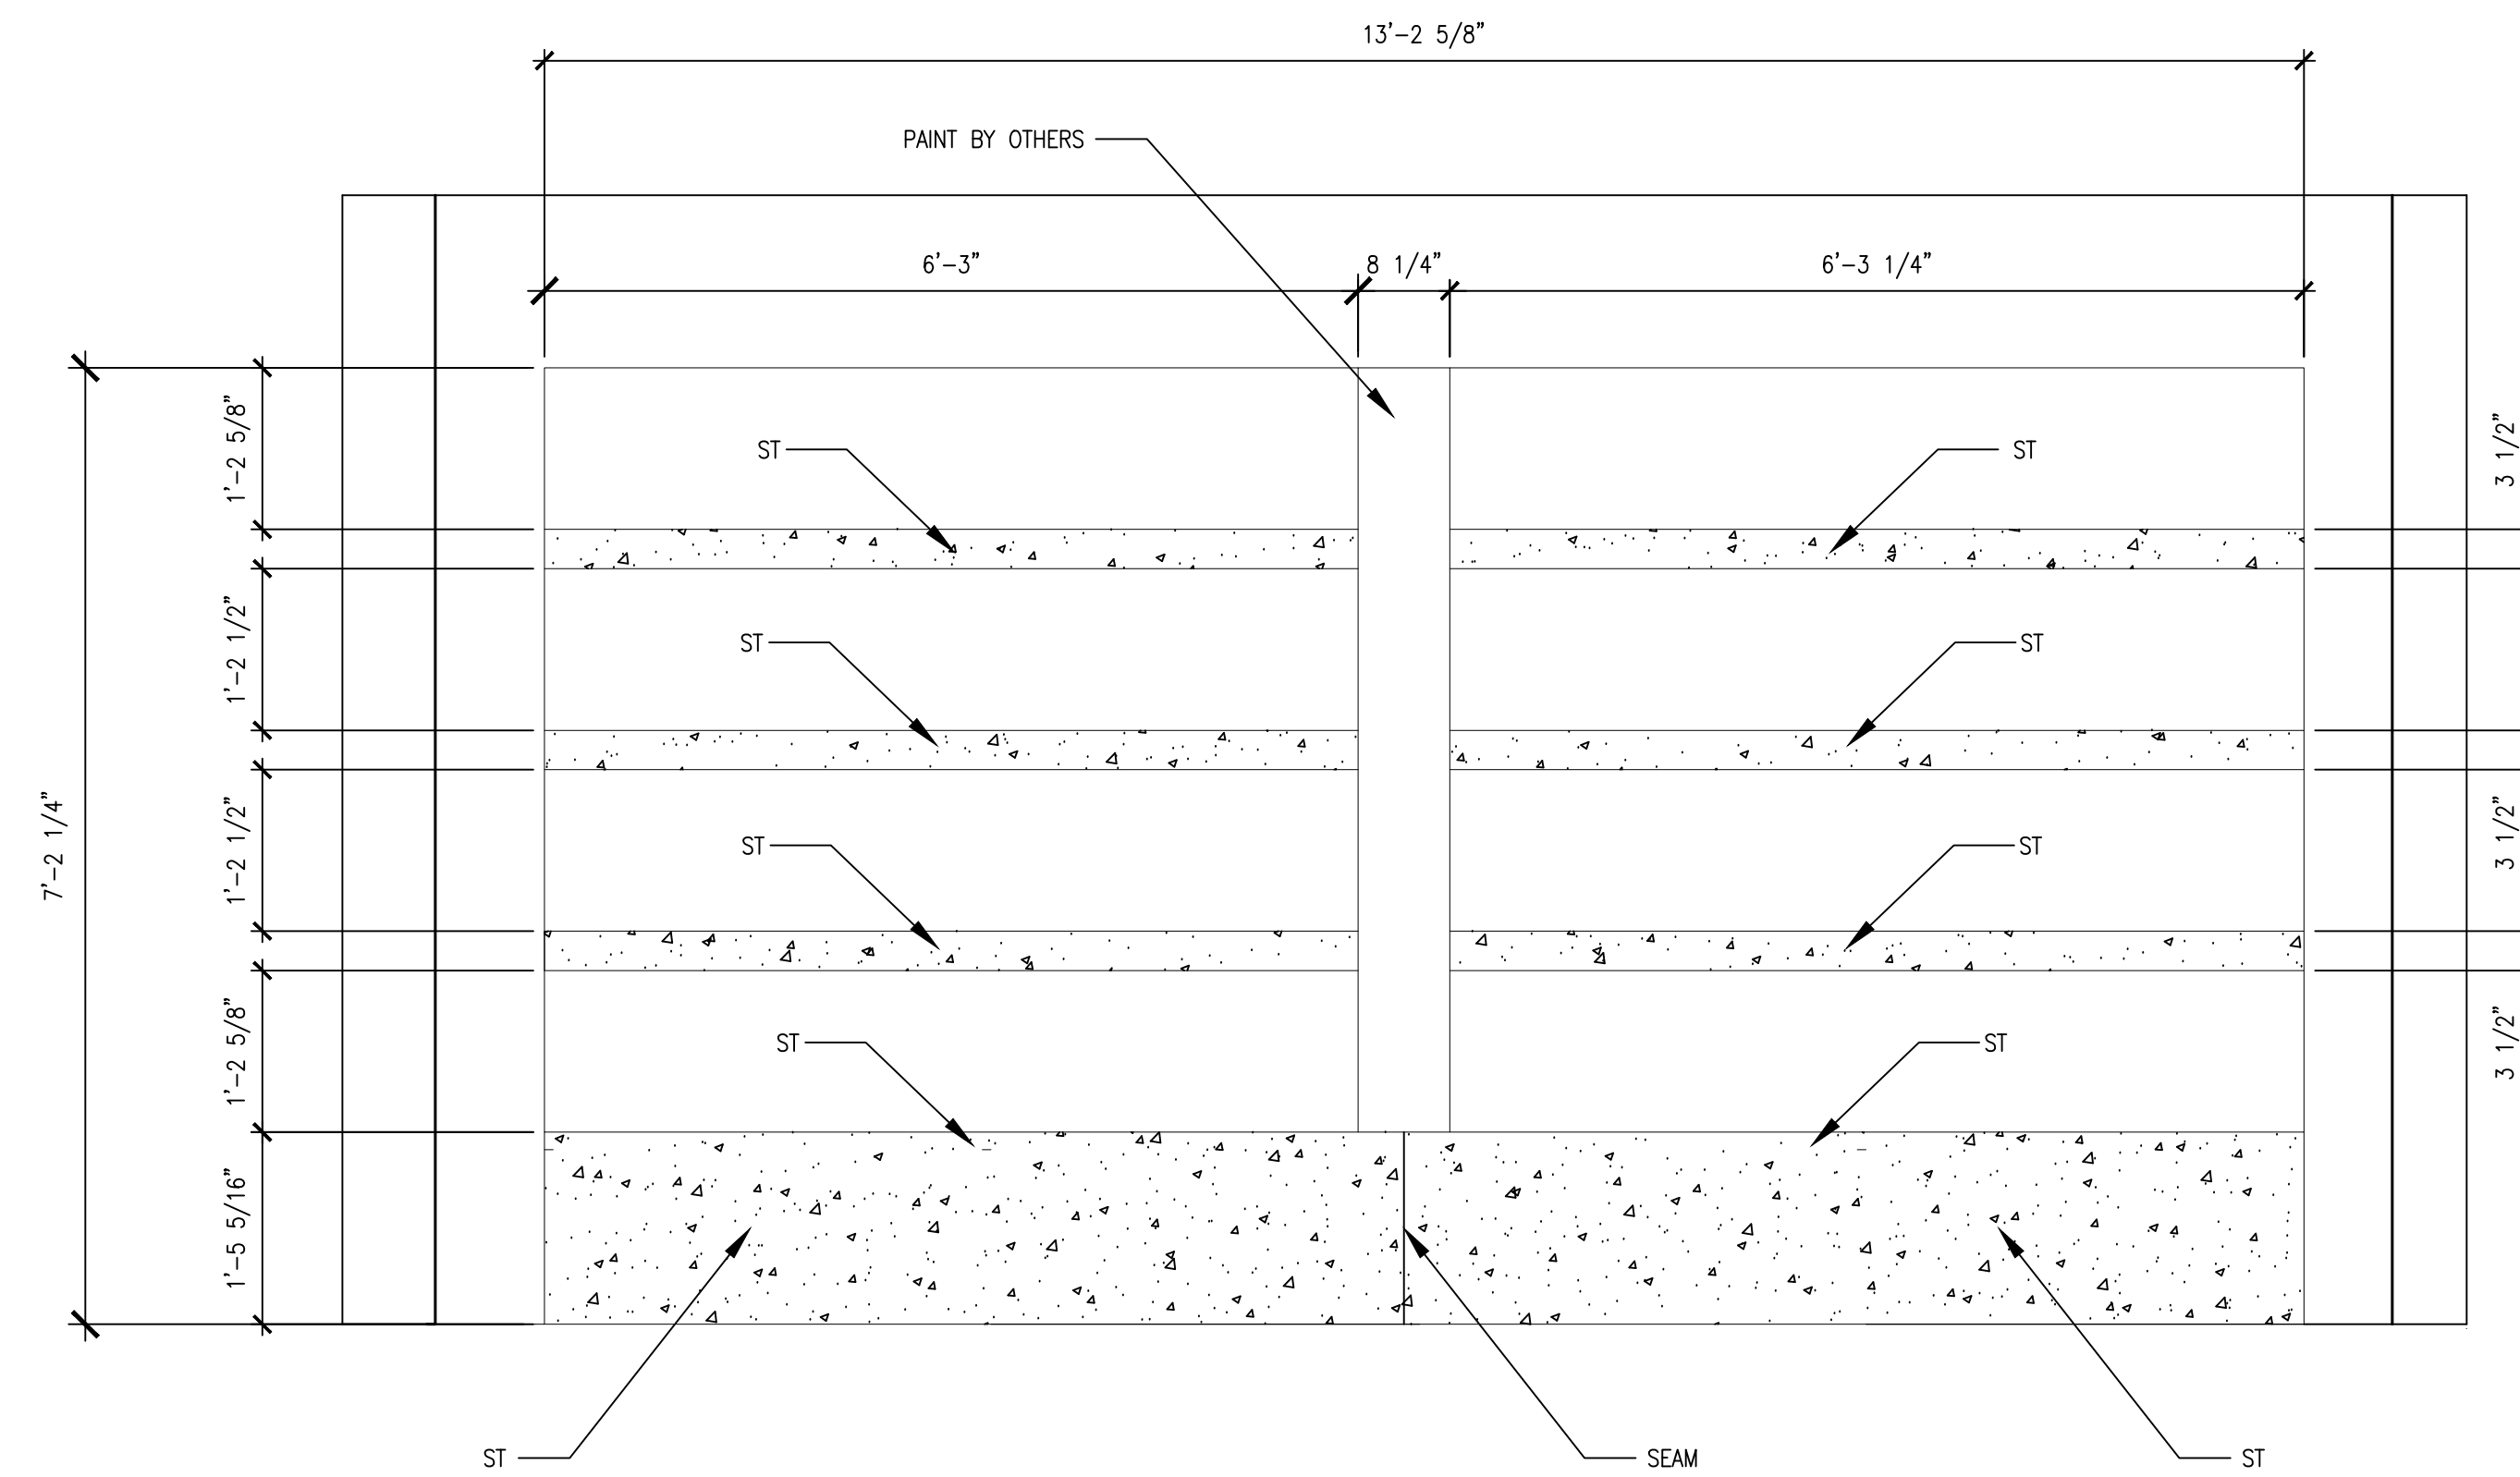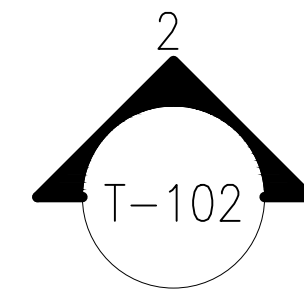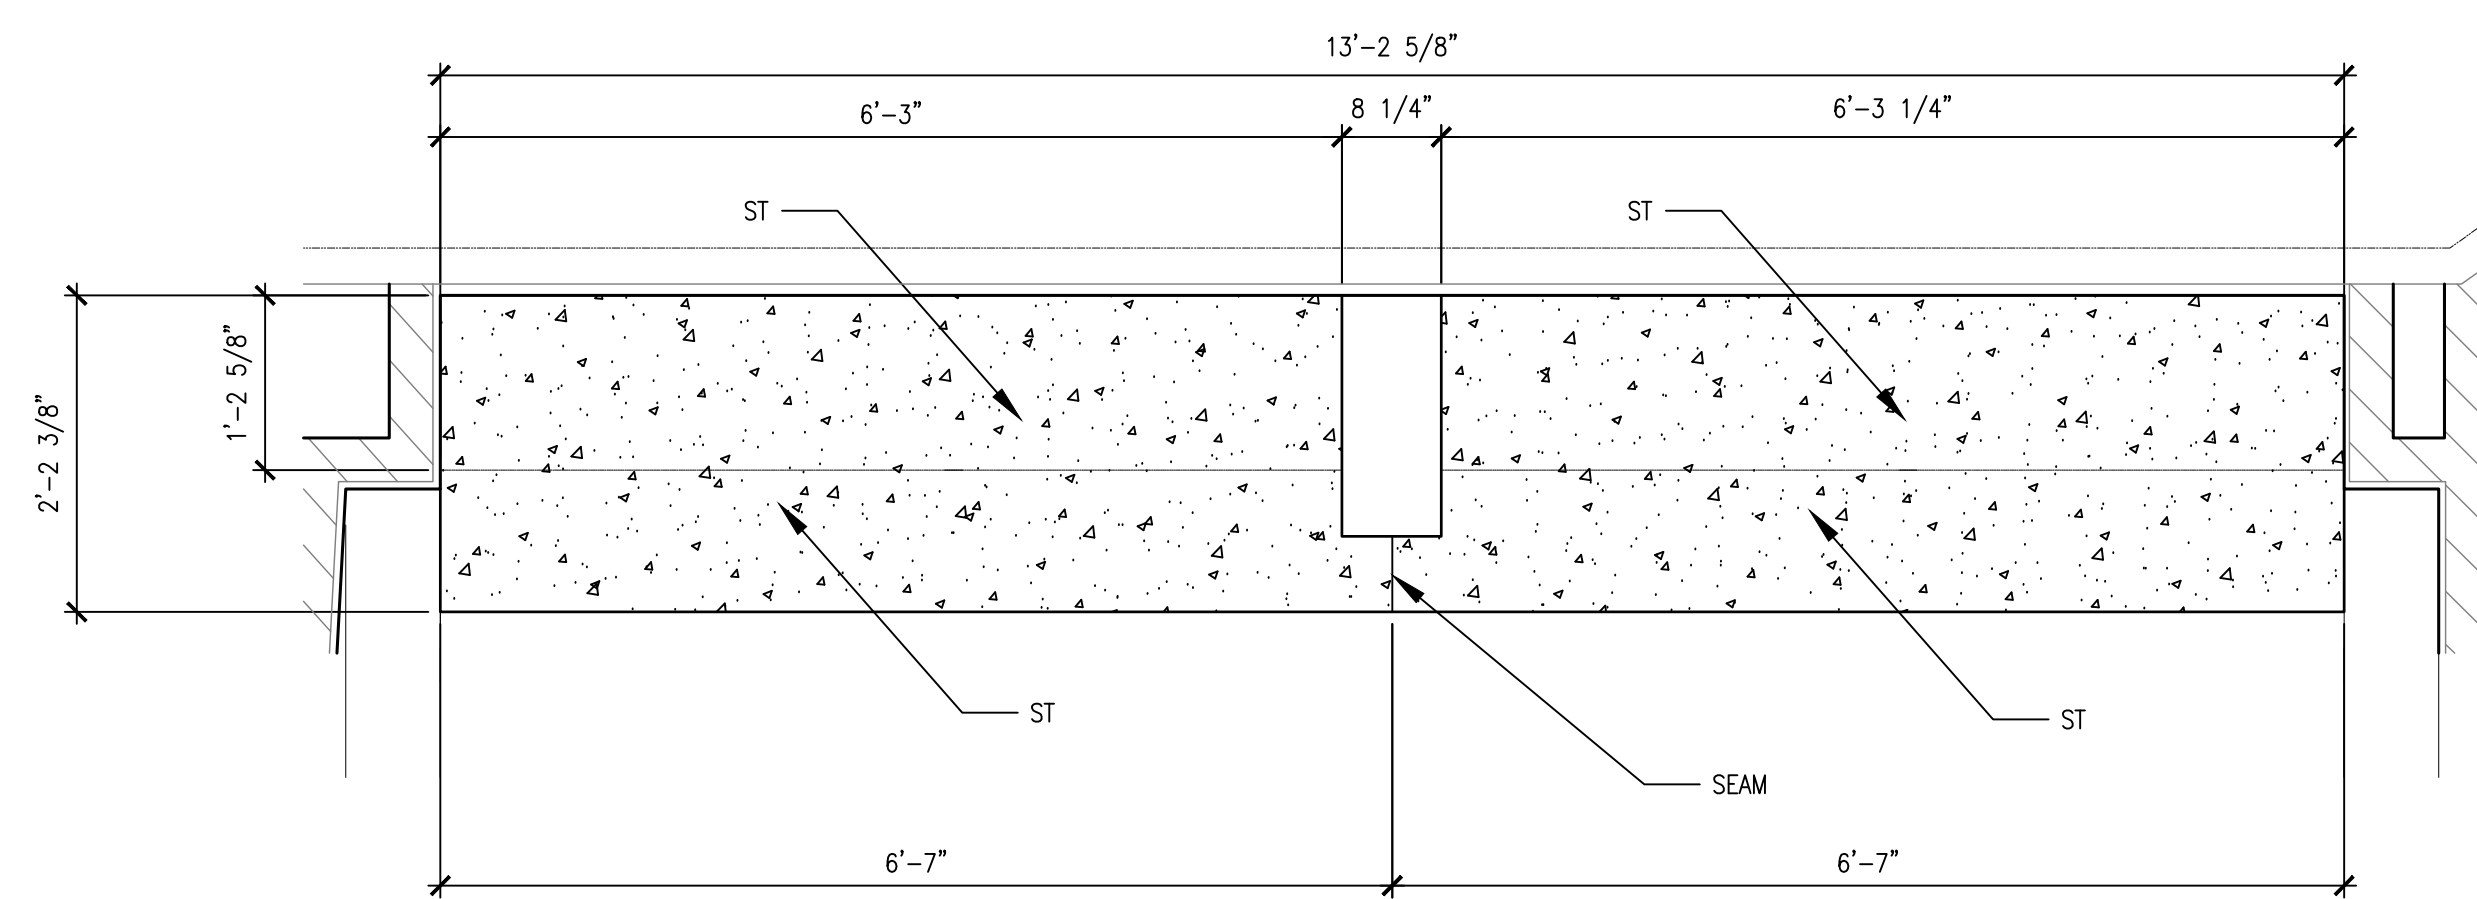

AUSTRO TILE & STONE, LLC
30-25 93RD STREET
EAST ELMHURST, NY 11369

CONTRACTOR
JRM CONSTRUCTION
MANAGEMENT, LLC
242 WEST 36TH STREET
11TH FLOOR
NEW YORK, NY 10018

WORKER DESIGNER

ISSUE FOR APPROVAL 04/29/24
ISSUE NAME DATE

ARCHITECT

SARGENT

461 FROM RD SUITE 255,
PARAMUS, NJ 07652
PHONE: 972.253.9393



PROJECT NAME:

AXEL ARIGATO
57 PRINCE STREET
NEW YORK, NY 10012

SHEET NAME:

PLAN/
ELEVATIONS

DATE:
PROJECT NO.:
PRINCIPAL:
DRAWING BY:
CHECKED BY:
SCALE:
DWG No.:
T-102
5 of 10

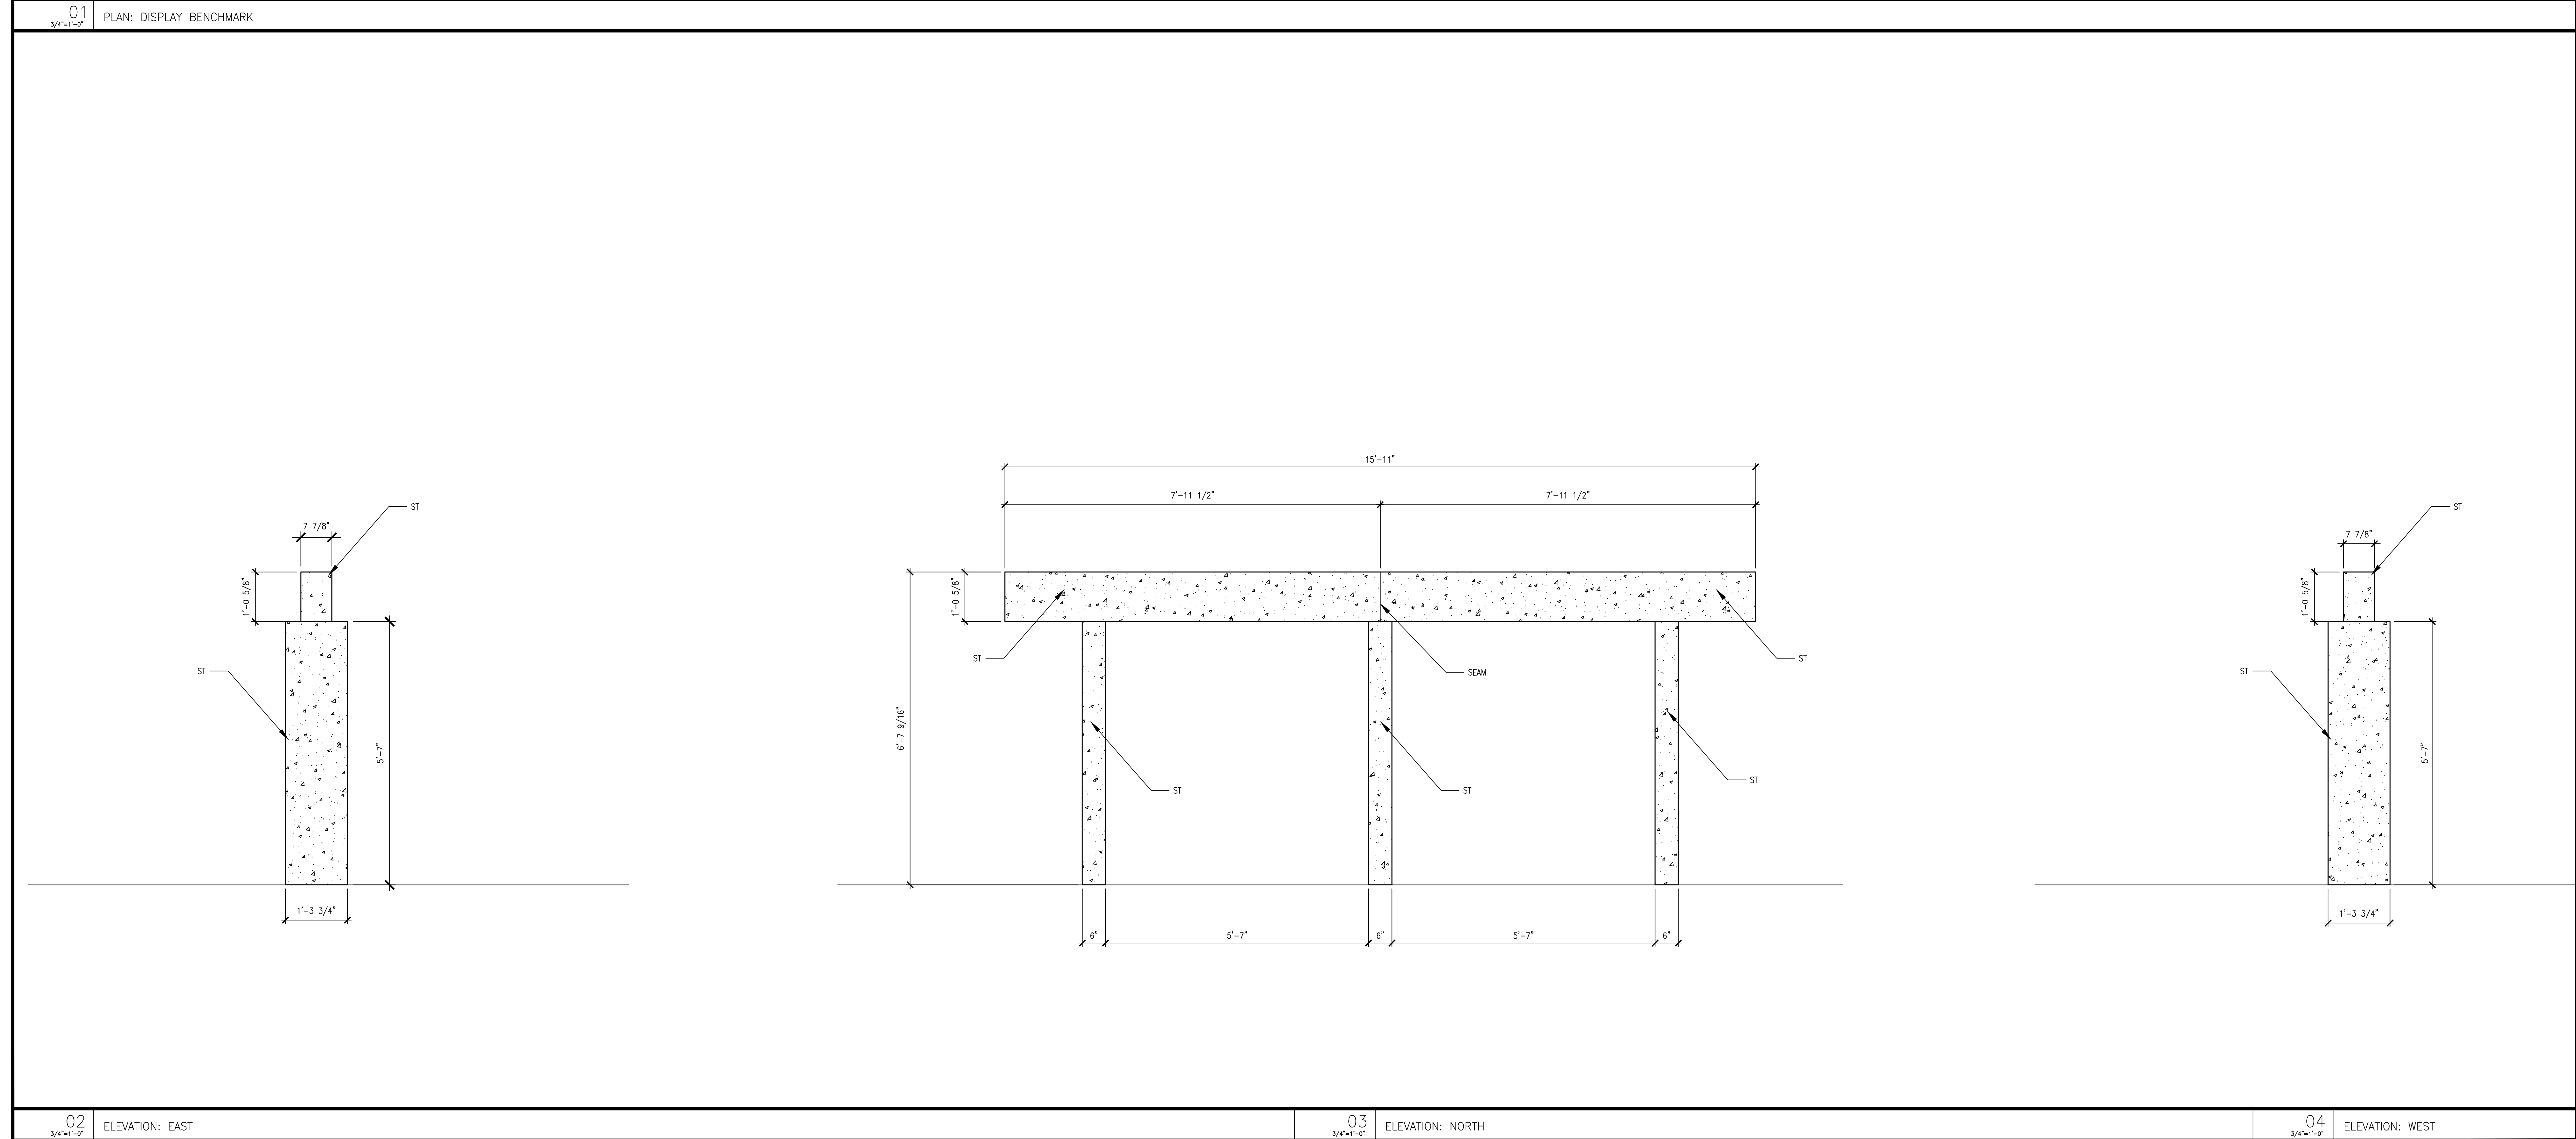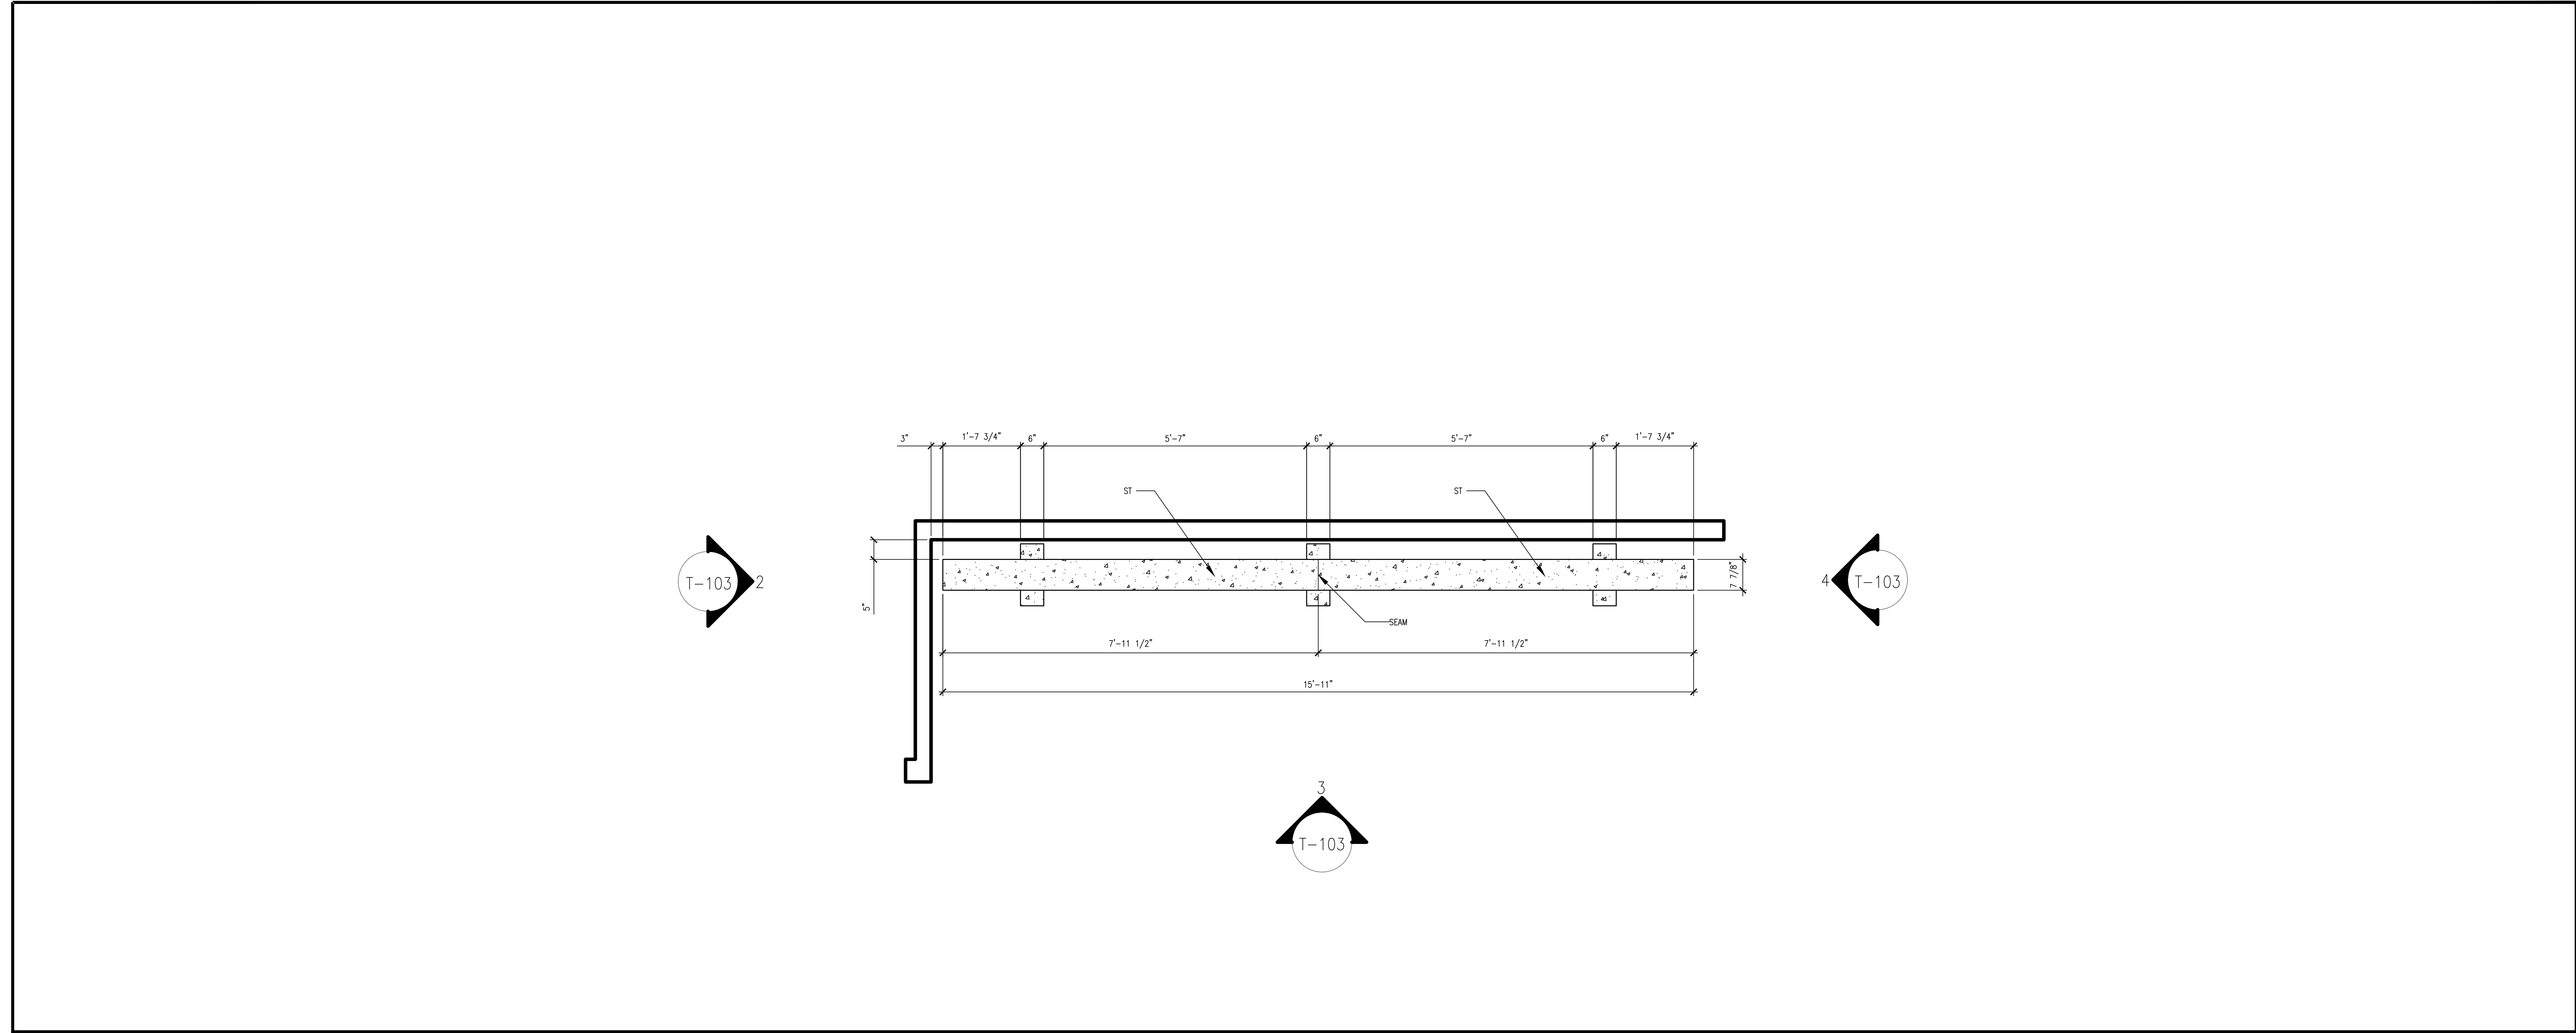

AUSTRO TILE & STONE, LLC
30-25 93RD STREET
EAST ELMHURST, NY 11369

CONTRACTOR
JRM CONSTRUCTION
MANAGEMENT, LLC
242 WEST 36TH STREET
11TH FLOOR
NEW YORK, NY 10018

WORKER DESIGNER

ISSUE FOR APPROVAL
04/29/24

ISSUE NAME
DATE
ARCHITECT
SARGENT
461 FROM RD SUITE 255,
PARAMUS, NJ 07652
PHONE: 972.253.9393

PROJECT NAME
AXEL ARIGATO
57 PRINCE STREET
NEW YORK, NY 10012


PLAN/
ELEVATIONS

DATE:
PROJECT NO.:
PRINCIPAL:
DRAWING BY:
CHECKED BY:
SCALE:
DWG No.:
T-103
6 of 10



JRM CONSTRUCTION
MANAGEMENT, LLC
242 WEST 36TH STREET
11TH FLOOR
NEW YORK, NY 10018

01 DETAIL: FLOOR TRANSITION AT BUILDING LOBBY
6"=1'-0"

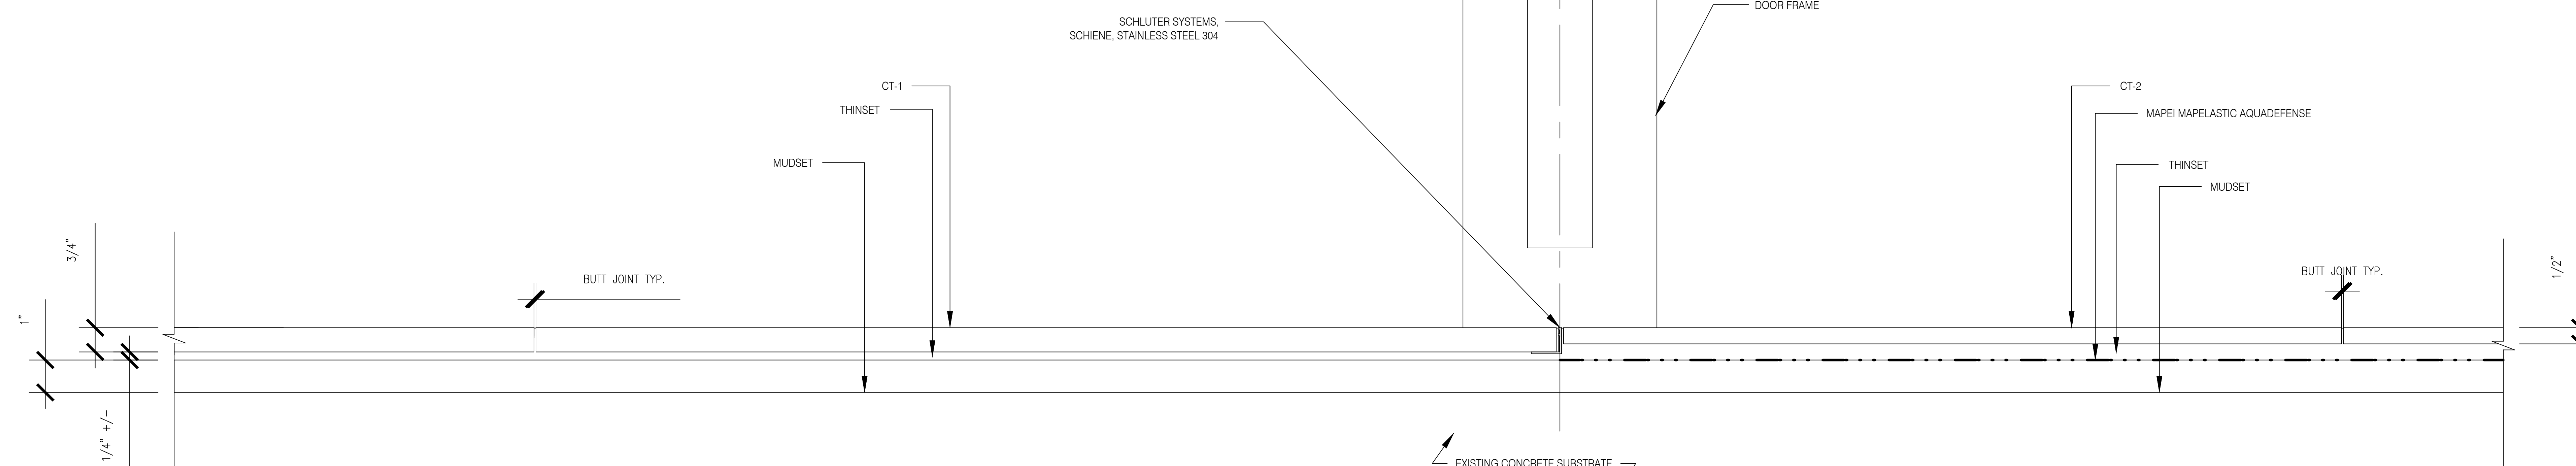

02
6'-1'-0" | DETAIL: FLOOR TRANSITION AT BATHROOM

[illegible]

04/29/24

ISSUE NAME	DATE
------------	------



ARCHITECT:

1 FROM RD SUITE 255,
PARAMUS, NJ 07652
PHONE:972.253.9393

AXEL ARIGATO
57 PRINCE STREET
NEW YORK, NY 10012

DETAILS
TILE

DATE:
PROJECT NO.:
PRINCIPAL:
DRAWING BY:
CHECKED BY:
SCALE:
DWG No.:
T-200
7 of 10

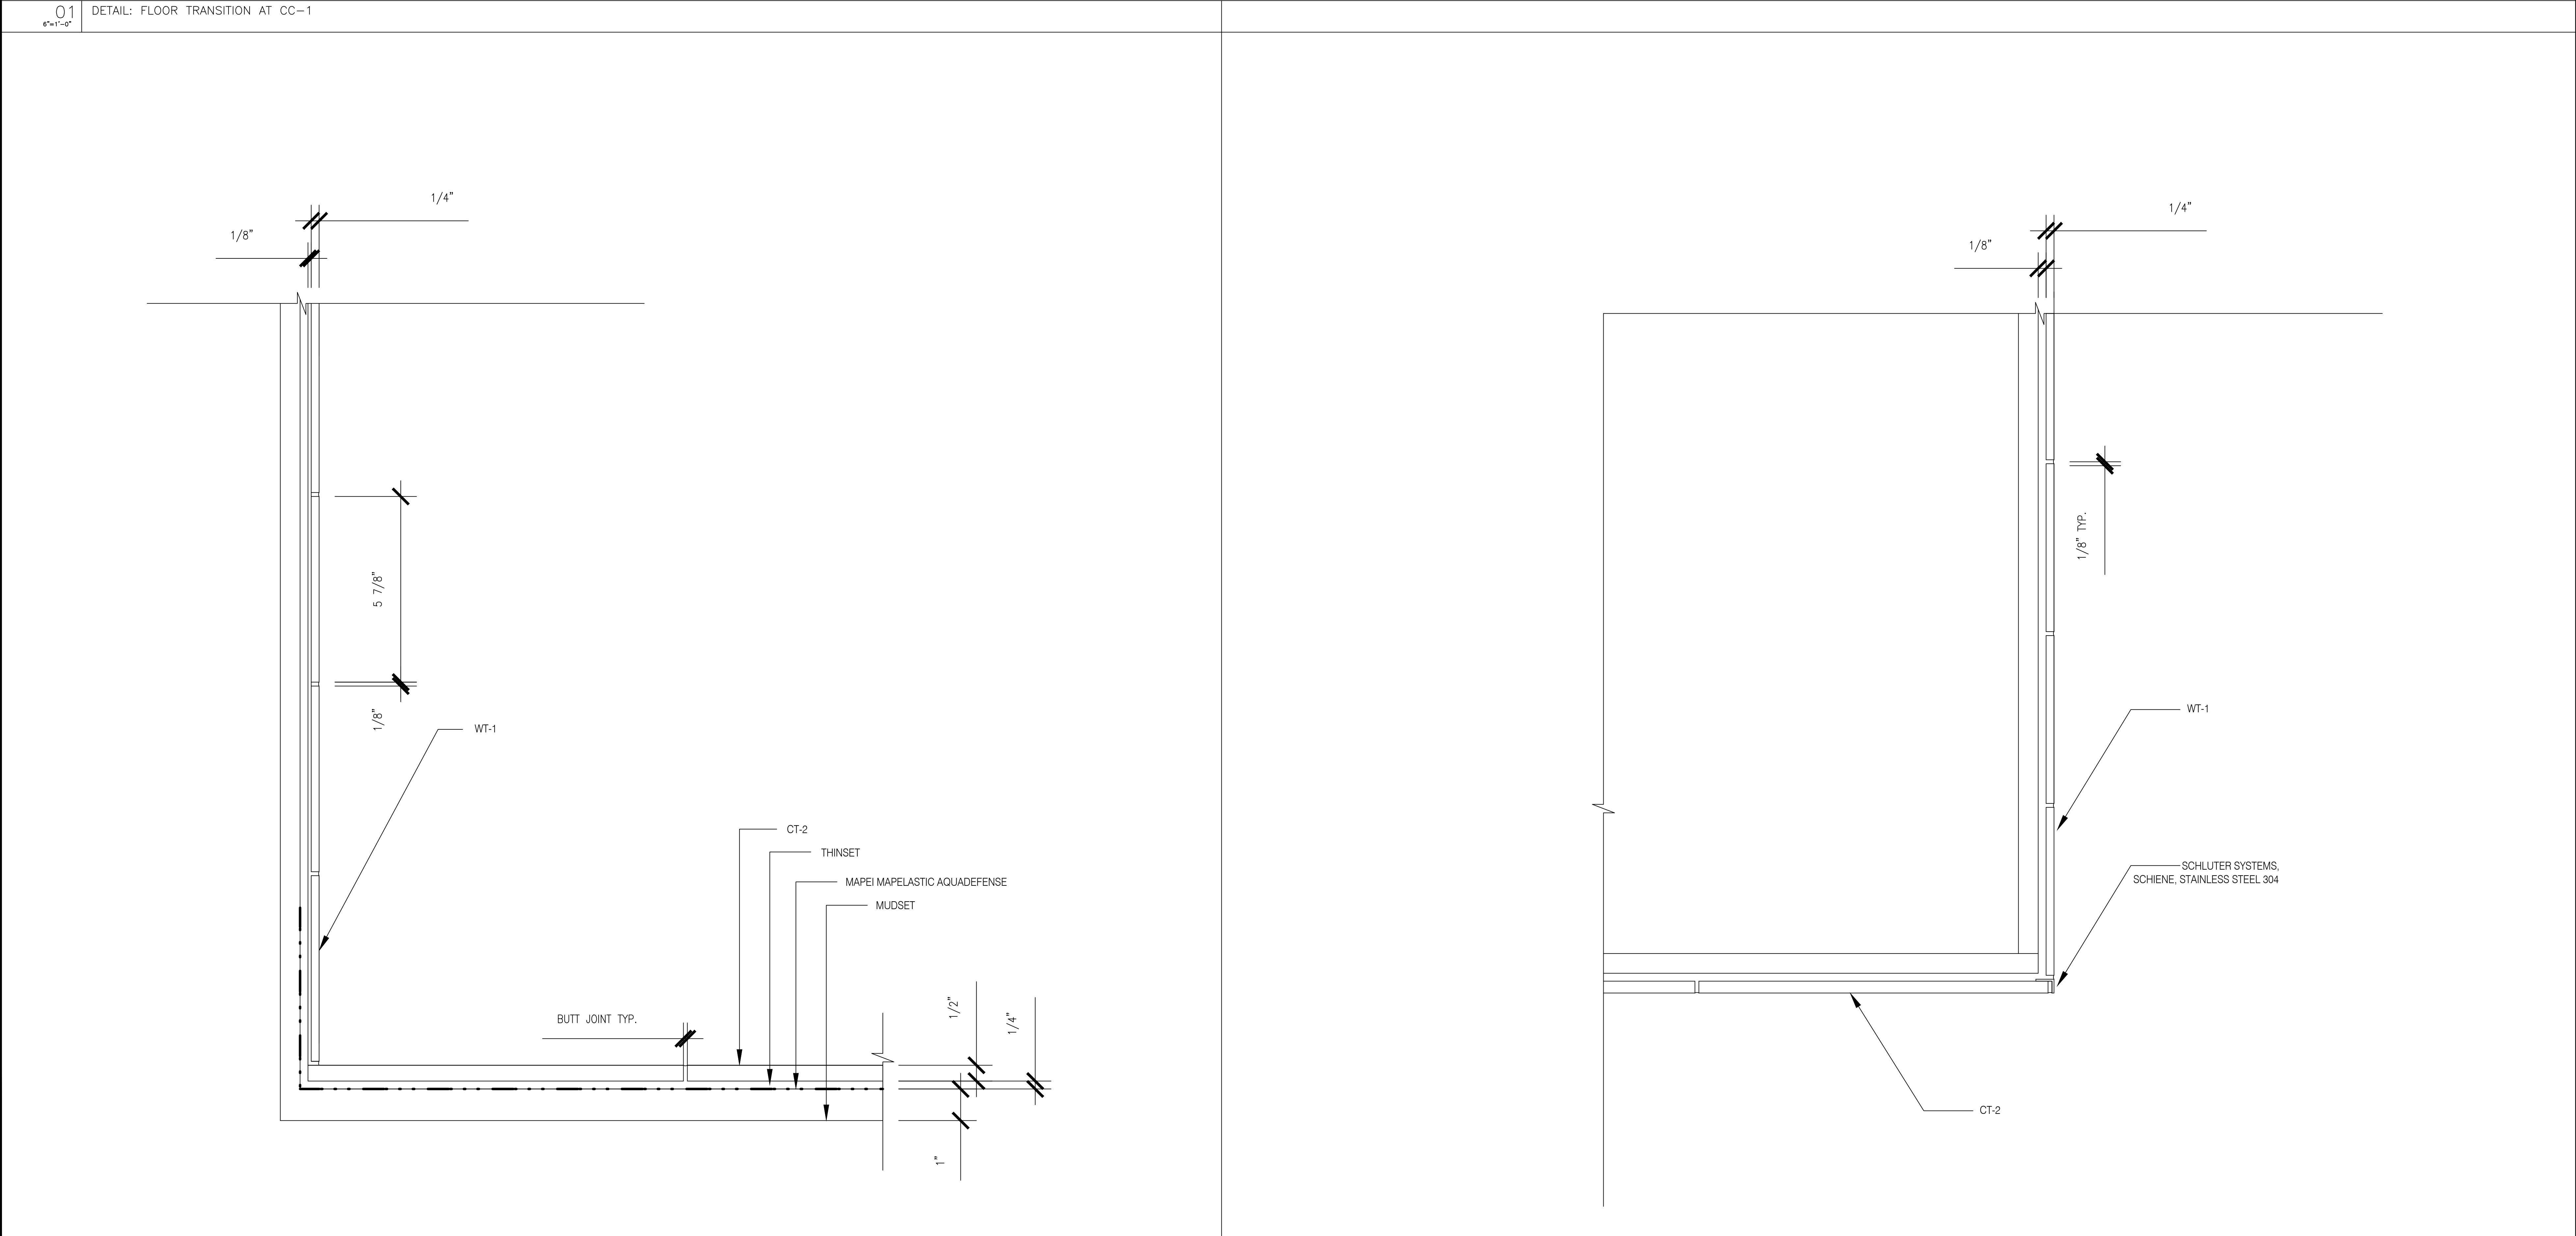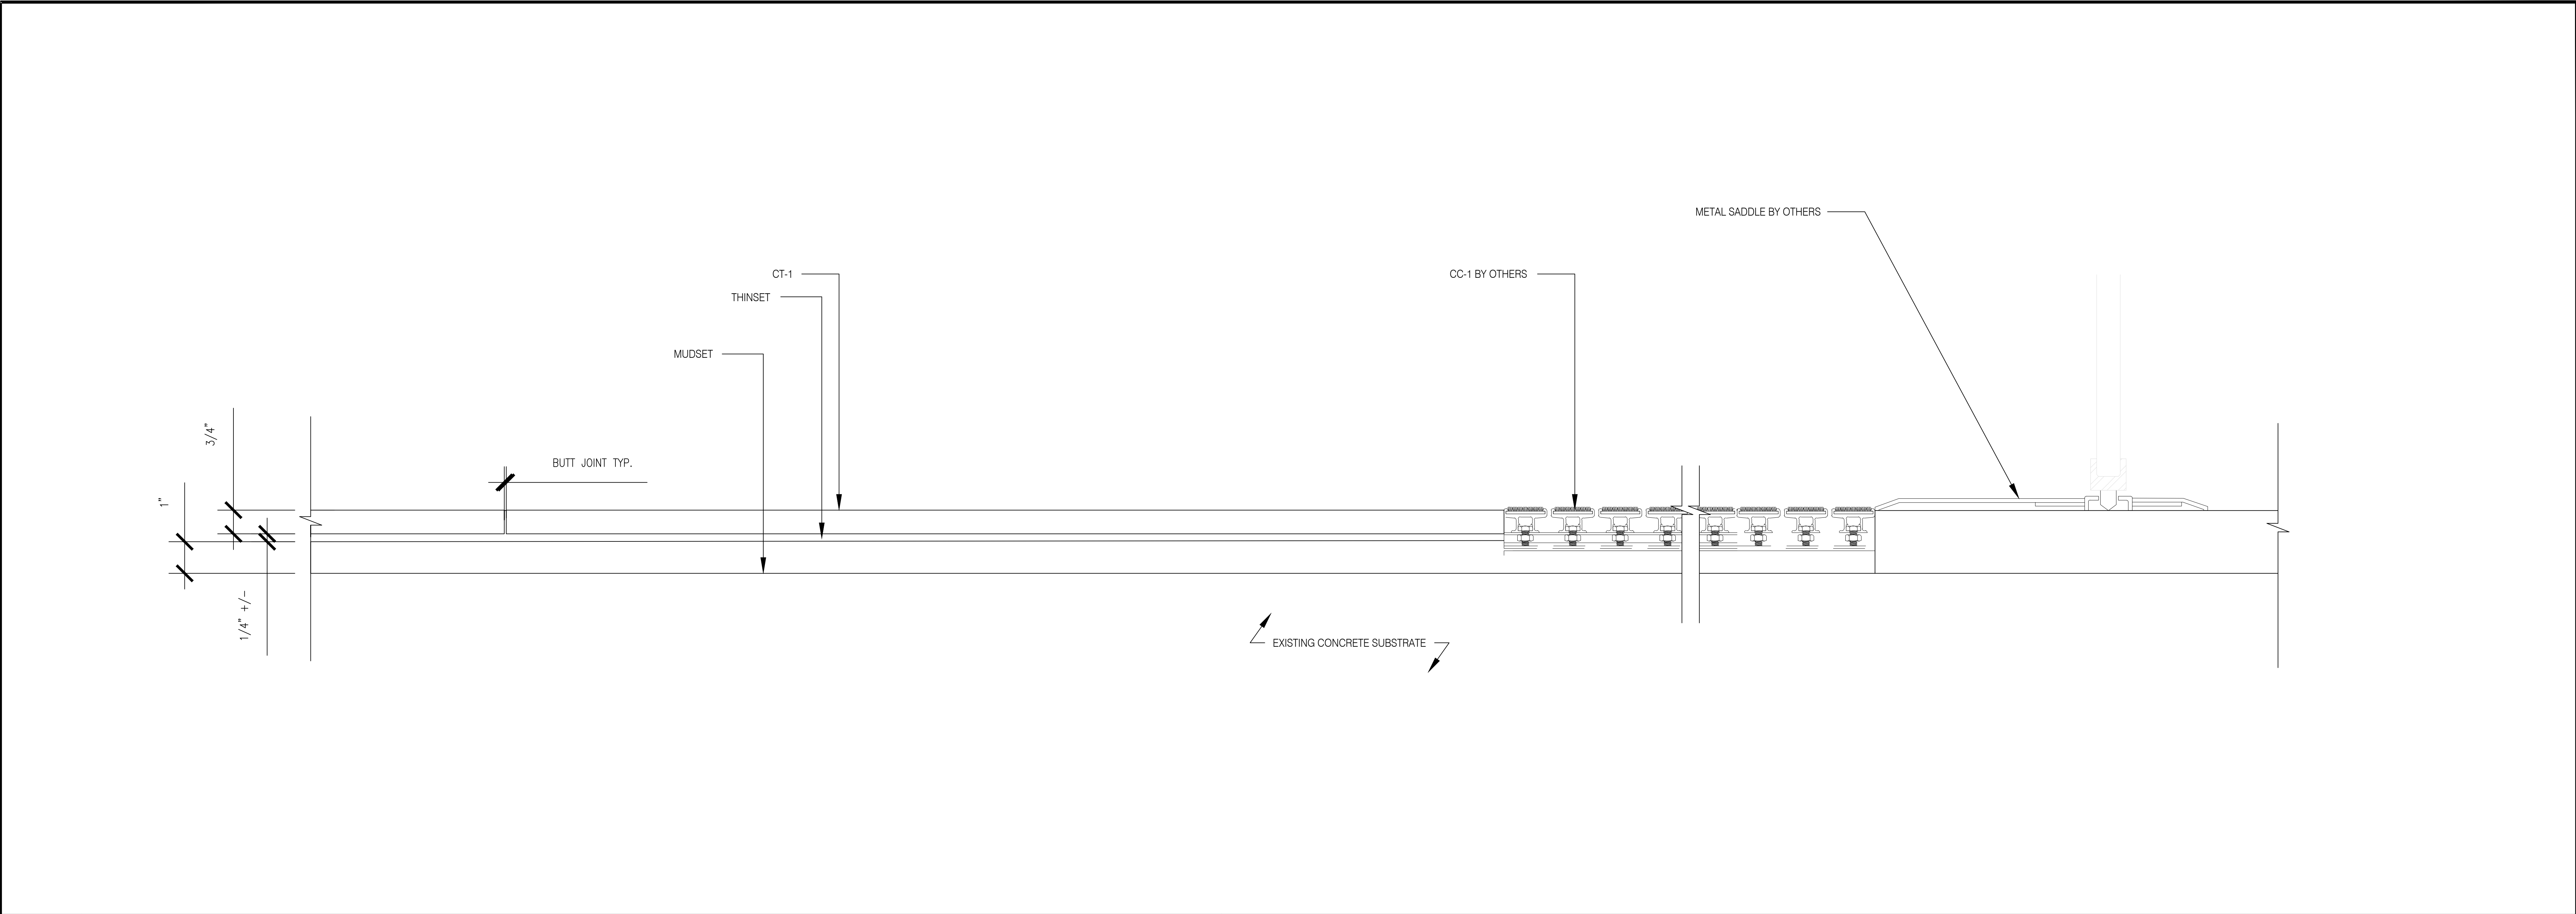

AUSTRO TILE & STONE, LLC
30-25 93RD STREET
EAST ELMHURST, NY 11369

CONTRACTOR:
JRM CONSTRUCTION
MANAGEMENT, LLC
242 WEST 36TH STREET
11TH FLOOR
NEW YORK, NY 10018

INTERIOR DESIGNER:



ISSUE FOR APPROVAL 04/29/24
ISSUE NAME DATE

SARGENT
461 FROM RD SUITE 255,
PARAMUS, NJ 07652
PHONE: 972.253.9393

PROJECT NAME:
AXEL ARIGATO
57 PRINCE STREET
NEW YORK, NY 10012

SHEET NAME:
DETAILS
TILE

DATE:
PROJECT NO.:
PRINCIPAL:
DRAWING BY:
CHECKED BY:
SCALE:
DWG No.:
T-201
8 of 10

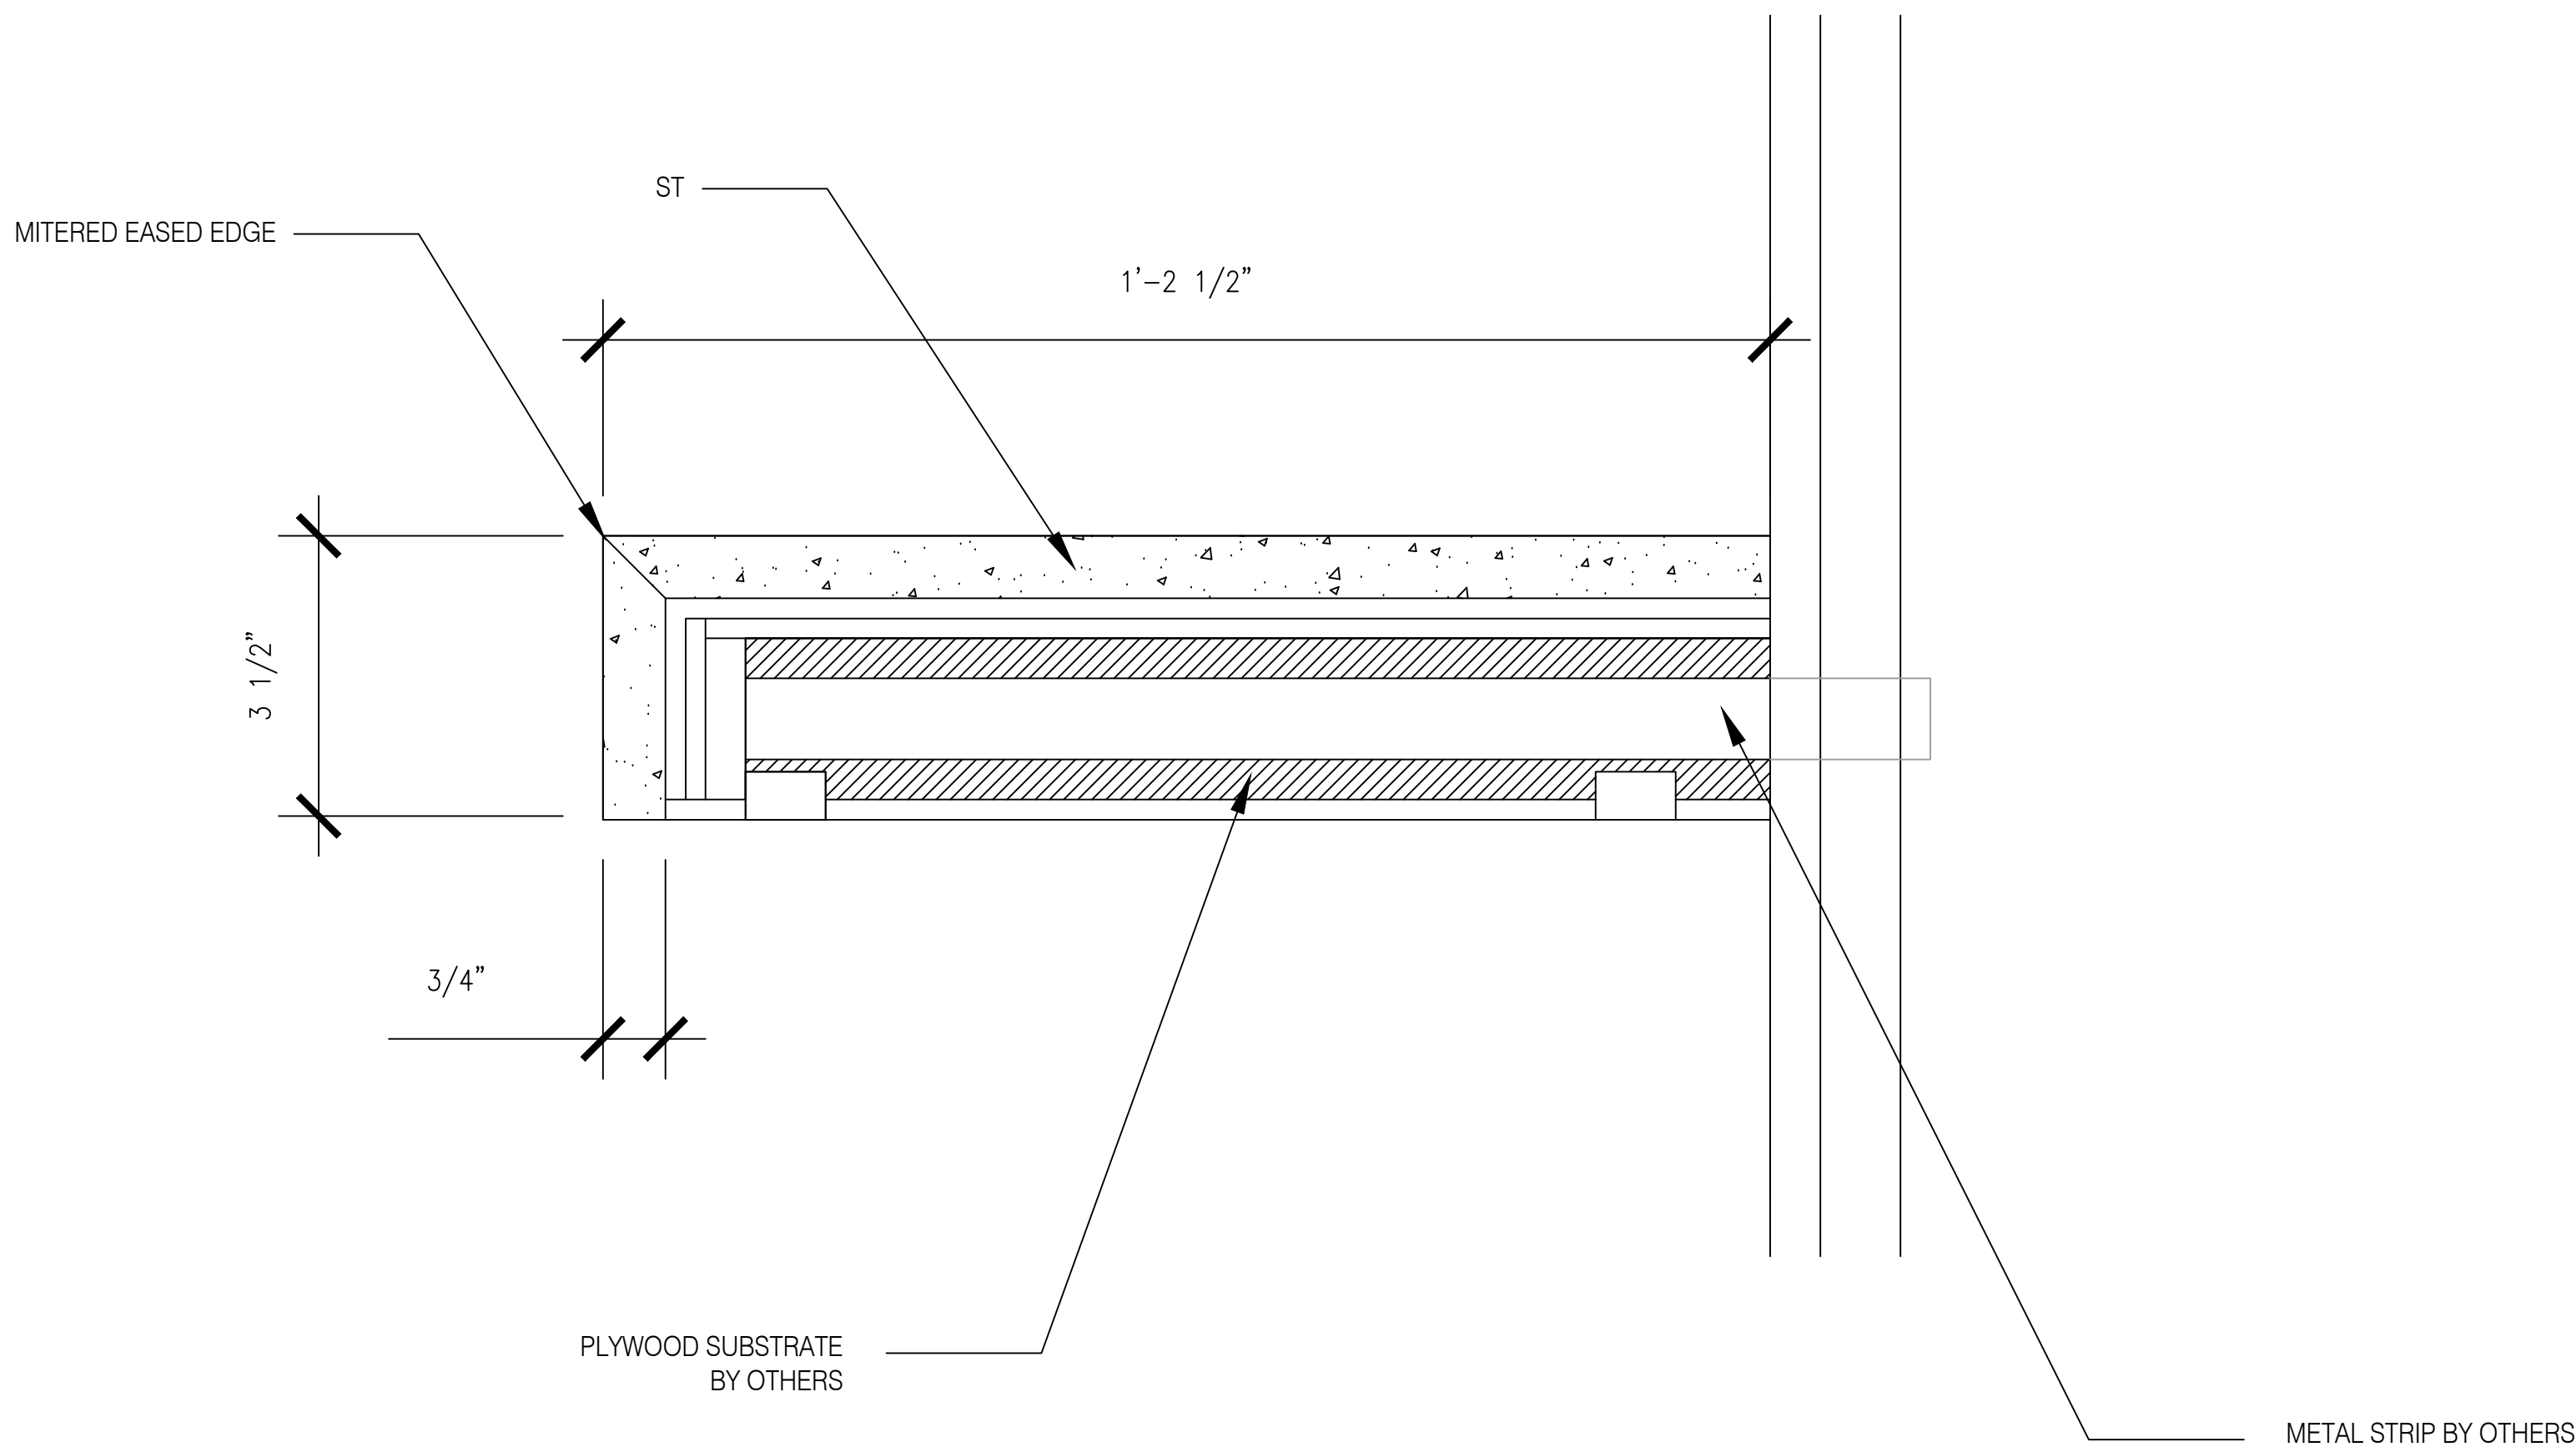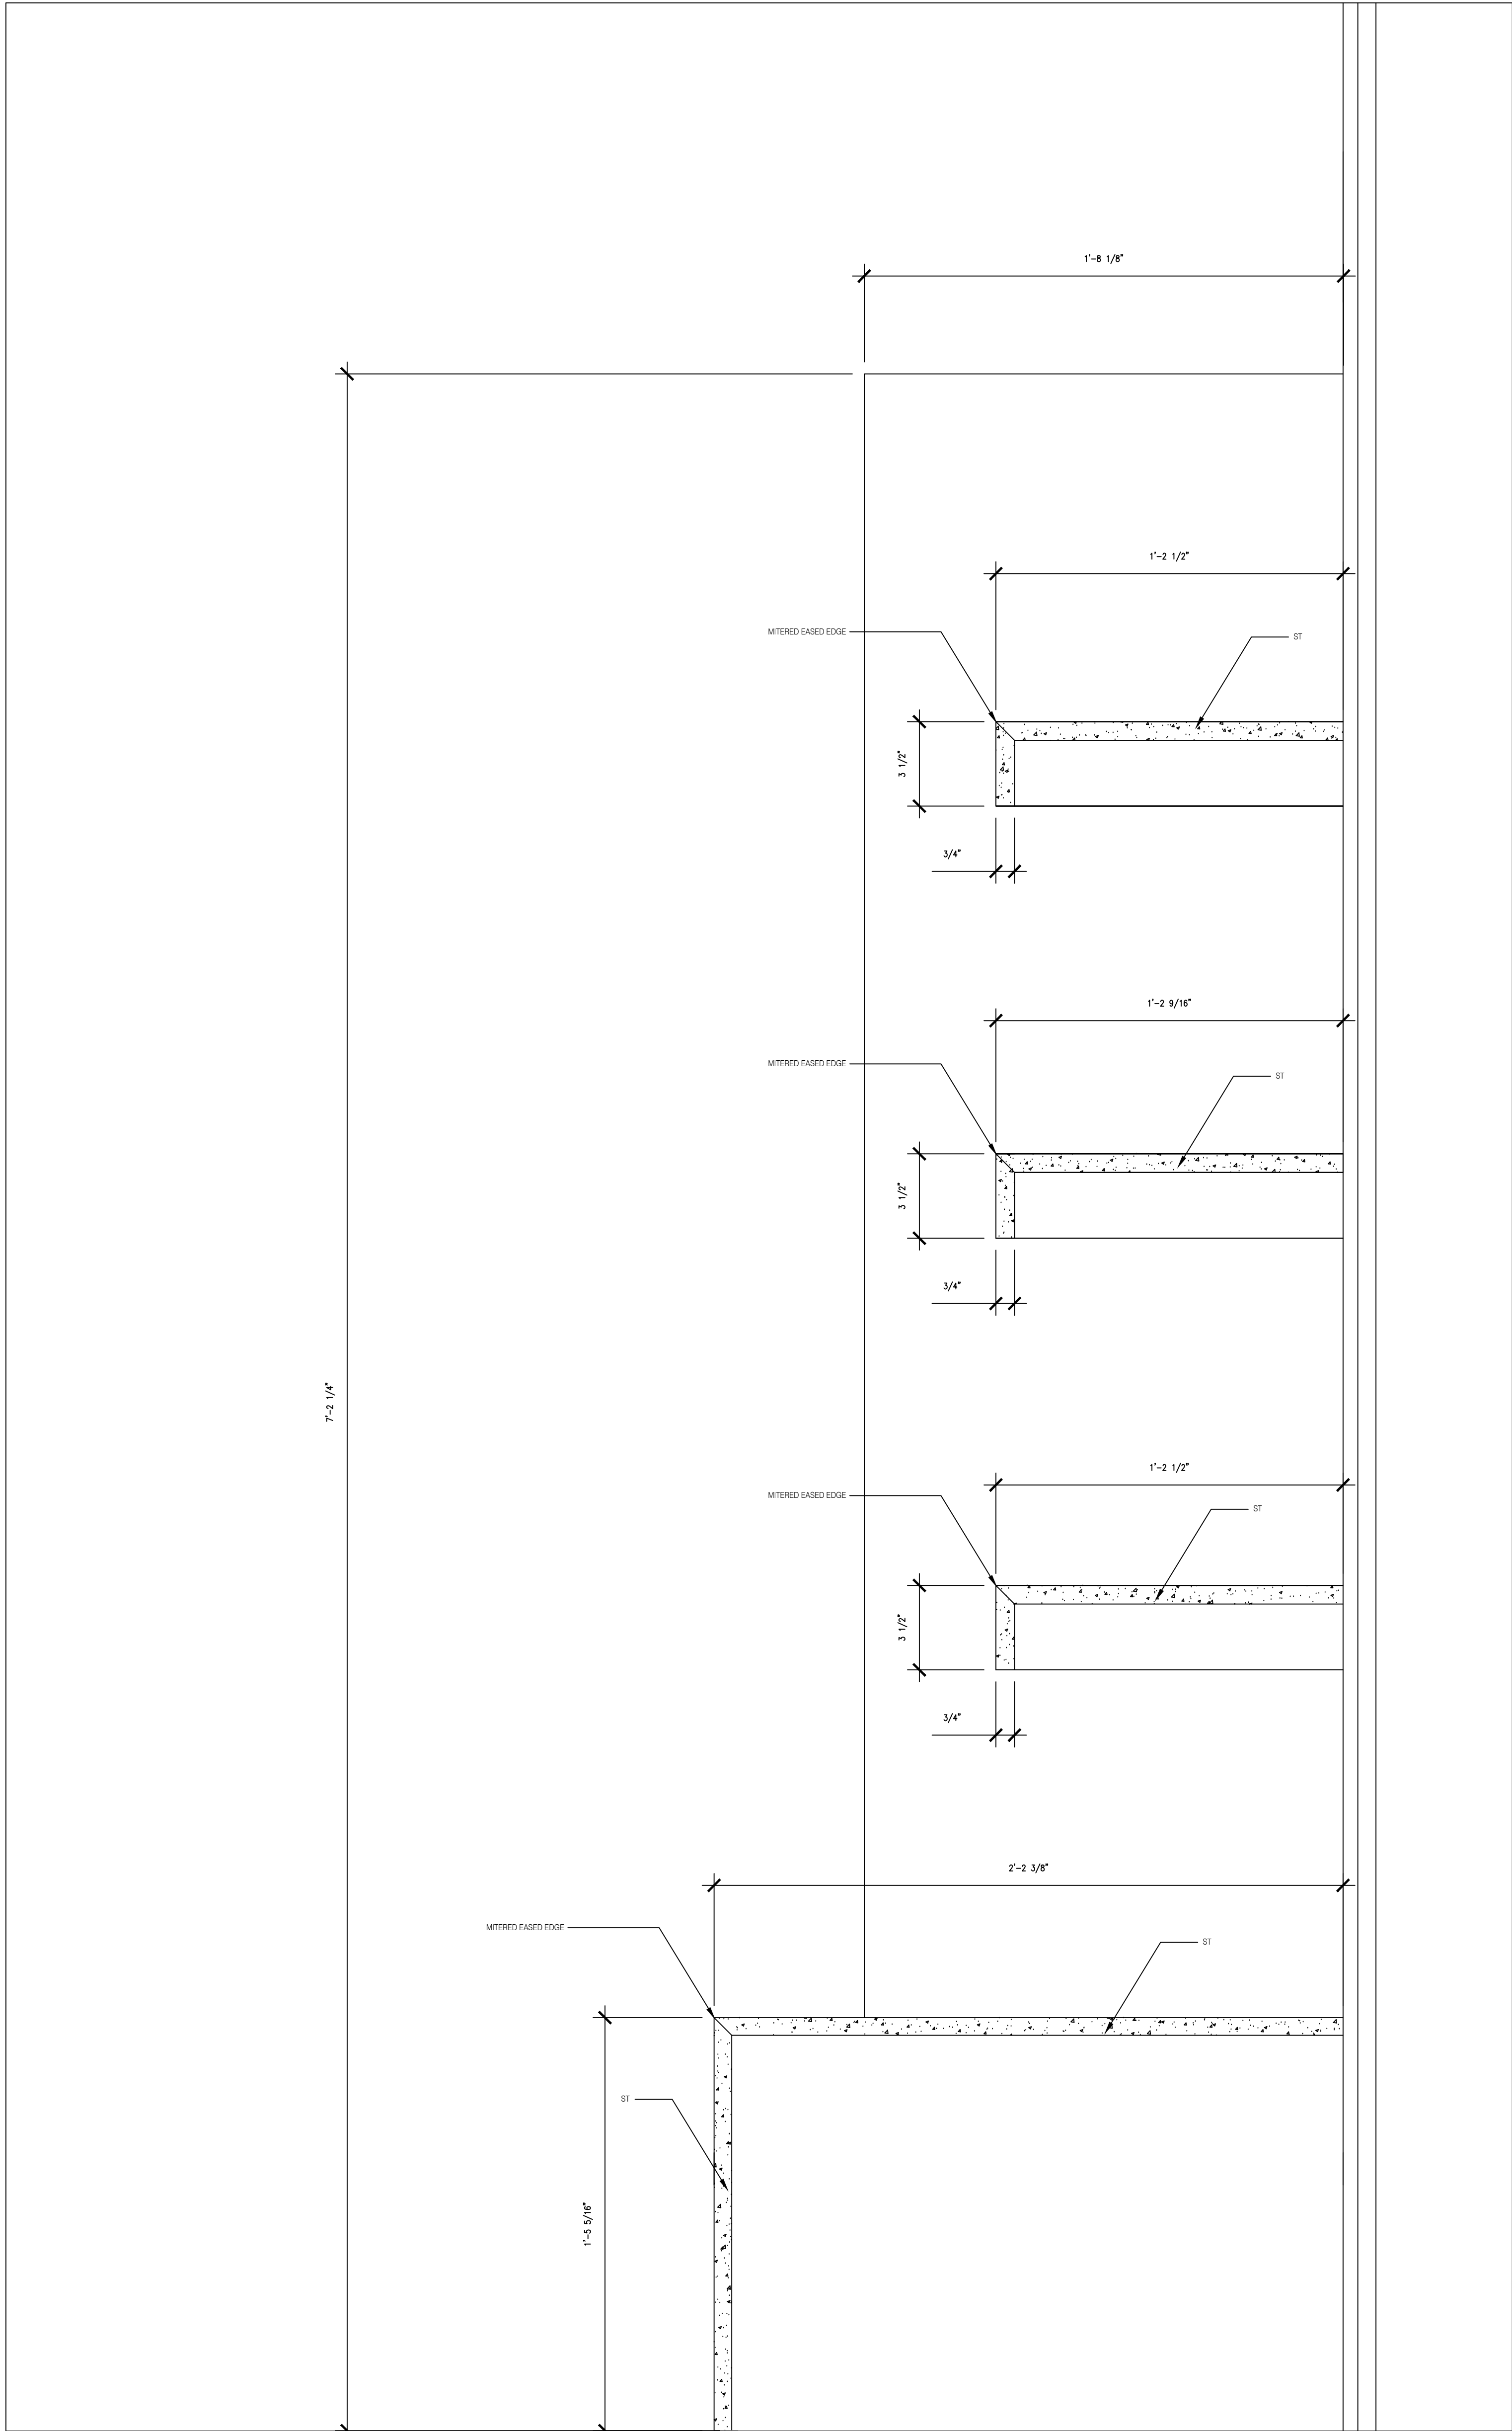

AUSTRO TILE & STONE, LLC
30-25 93RD STREET
EAST ELMHURST, NY 11369

CONTRACTOR:
JRM CONSTRUCTION
MANAGEMENT, LLC
242 WEST 36TH STREET
11TH FLOOR
NEW YORK, NY 10018

INTERIOR DESIGNER:

ISSUE FOR APPROVAL	04/29/24
ISSUE NAME	DATE

PROJECT:

SARGENT
461 FROM RD SUITE 255,
PARAMUS, NJ 07652
PHONE:972.253.9393

PROJECT NAME:

AXEL ARIGATO
57 PRINCE STREET
NEW YORK, NY 10012

SHEET NAME:

DETAILS
STONE COUNTERTOP

DATE:
PROJECT NO.:
PRINCIPAL:
DRAWING BY:
CHECKED BY:
SCALE:
DWG No.:

T-202
9 of 10

