

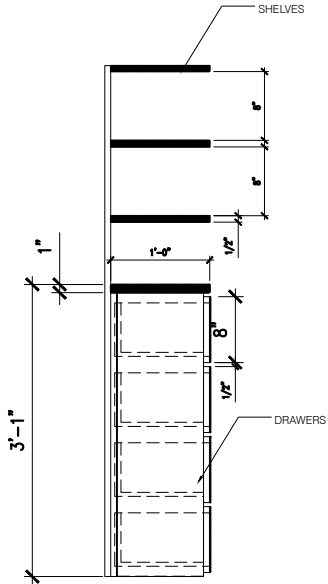
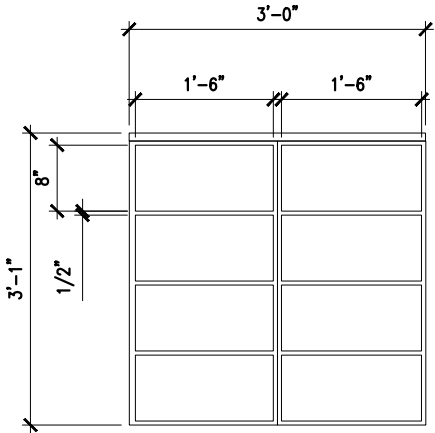
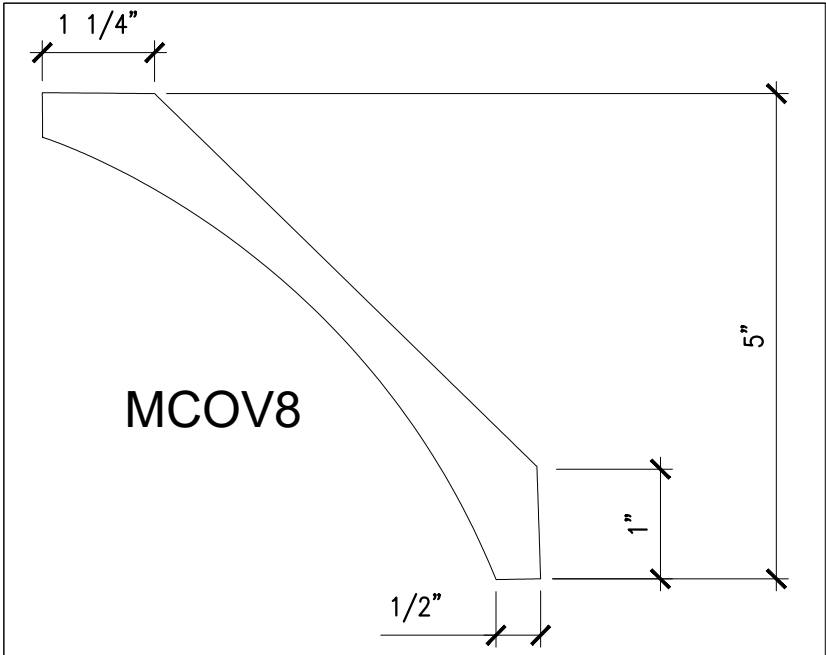
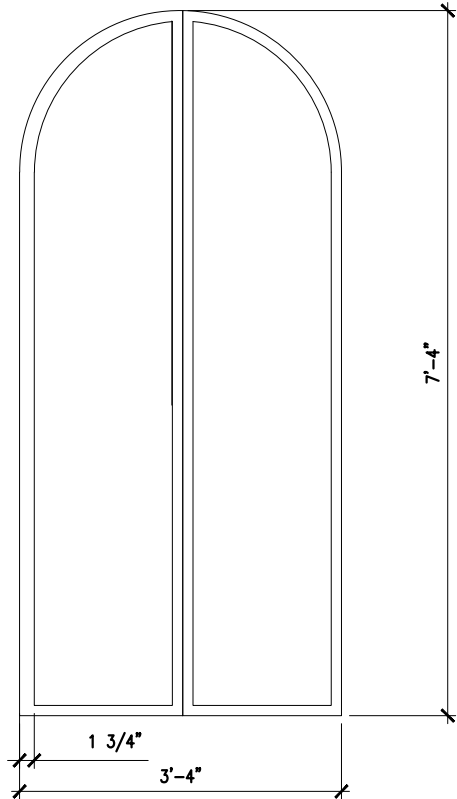


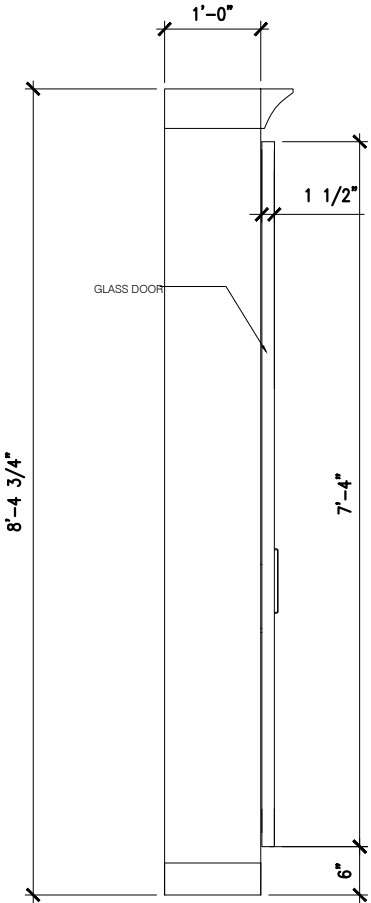

BASE CABINET VIEW

SECTION VIEW (A)

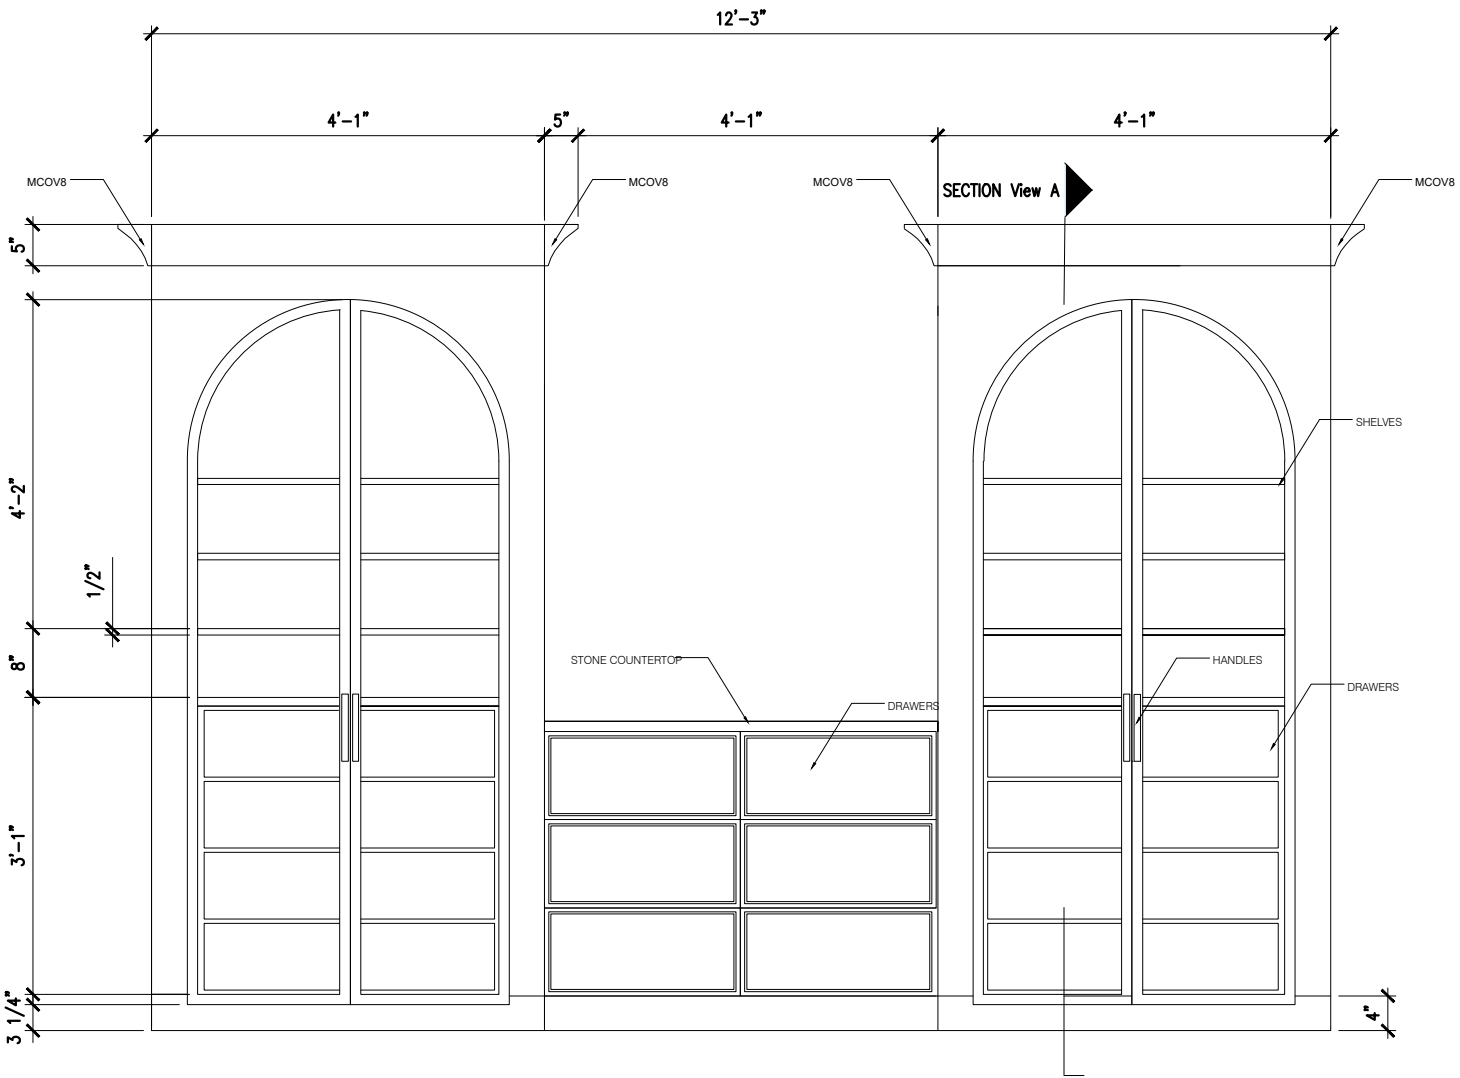

FRONT VIEW

SIDE VIEW

GLASS DOOR

GENERAL NOTES:

All rights reserved. This drawing is the exclusive property of Eastern Yards Custom Woodworking. Reproduction, distribution, or use of this drawing without written consent is prohibited.

The client is responsible for verifying all dimensions prior to approval. Eastern Yards Custom Woodworking is not responsible for errors in measurements provided by the client. Shop drawings must be signed by the client prior to fabrication. Eastern Yards Custom Woodworking is not responsible for site conditions not shown on drawings. All walls must be straight, level, and plumb, and no field conditions are assumed unless supported.

All dimensions are to be verified in the field. Do not scale drawings. All dimensions are in inches unless noted otherwise. Fabrication will begin after receipt of signed shop drawings.

1	REVISION #1	9/9/25
NO.	REVISION	DATE

Project Name:
ALTER RESIDENCE


Project Address:
7-29 Almont Rd Far Rockway, NY 11691

TITLE:
CABINET WITH GLASS DOORS
LEFT AND RIGHT AND MCOV8


JOB:	SHEET 1
DATE: 9/8/25	
SCALE:	




EASTERN YARDS LLC
100 E MINEOLA AVE
VALLEY STREAM, NY 11580

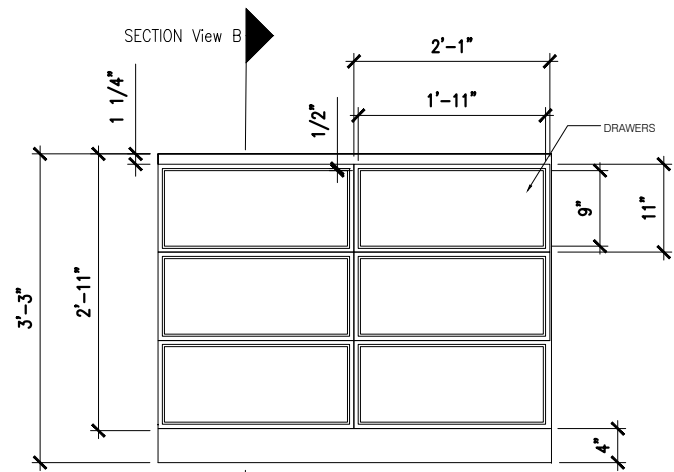


FRONT VIEW

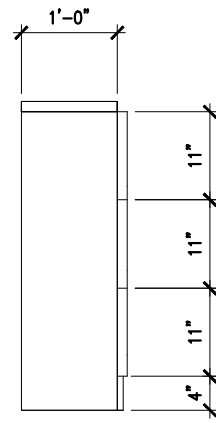

SIDE VIEW

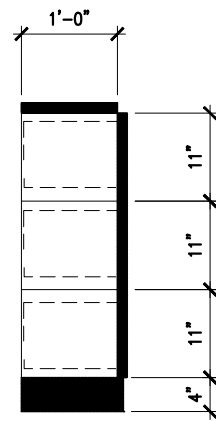

SECTION VIEW (B)

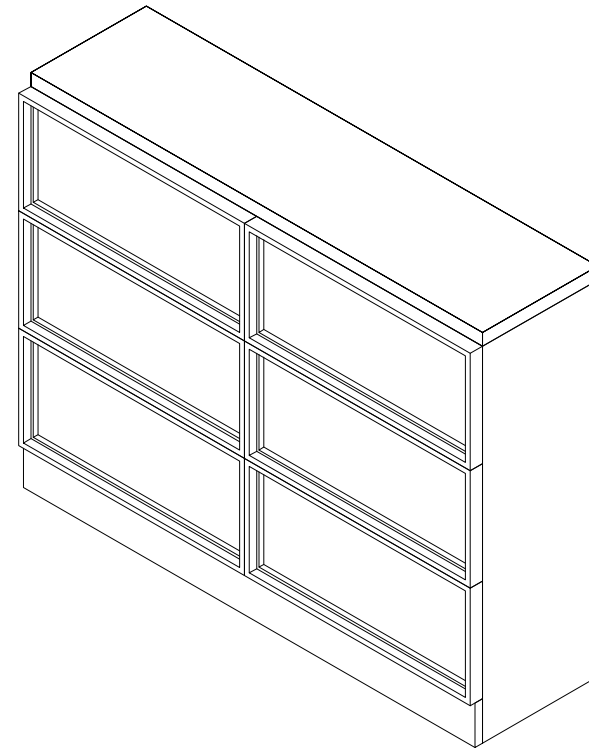

ISOMETRIC VIEW

GENERAL NOTES:

All rights reserved. This drawing is the exclusive property of Eastern Yards Custom Woodworking. Reproduction, distribution, or use of this drawing without written consent is prohibited.

The client is responsible for verifying all dimensions prior to approval. Eastern Yards Custom Woodworking is not responsible for errors in measurements provided by the client. Shop drawings must be signed by the client prior to fabrication. Eastern Yards Custom Woodworking is not responsible for site conditions not shown on drawings. All walls must be straight, level, and plumb, and no field conditions are assumed unless supported.

All dimensions are to be verified in the field. Do not scale drawings. All dimensions are in inches unless noted otherwise. Fabrication will begin after receipt of signed shop drawings.

NO.	REVISION	DATE
-----	----------	------

Project Name:
ALTER RESIDENCE


Project Address:
7-29 Almont Rd Far Rockway,NY 11691

TITLE:
BASE CABINET WITH 8 DRAWERS
WITH 2 CABINETS EACH SIDE


JOB:	SHEET 2
DATE: 9/9/25	
SCALE:	



EASTERN YARDS LLC
100 E MINEOLA AVE
VALLEY STREAM, NY 11580

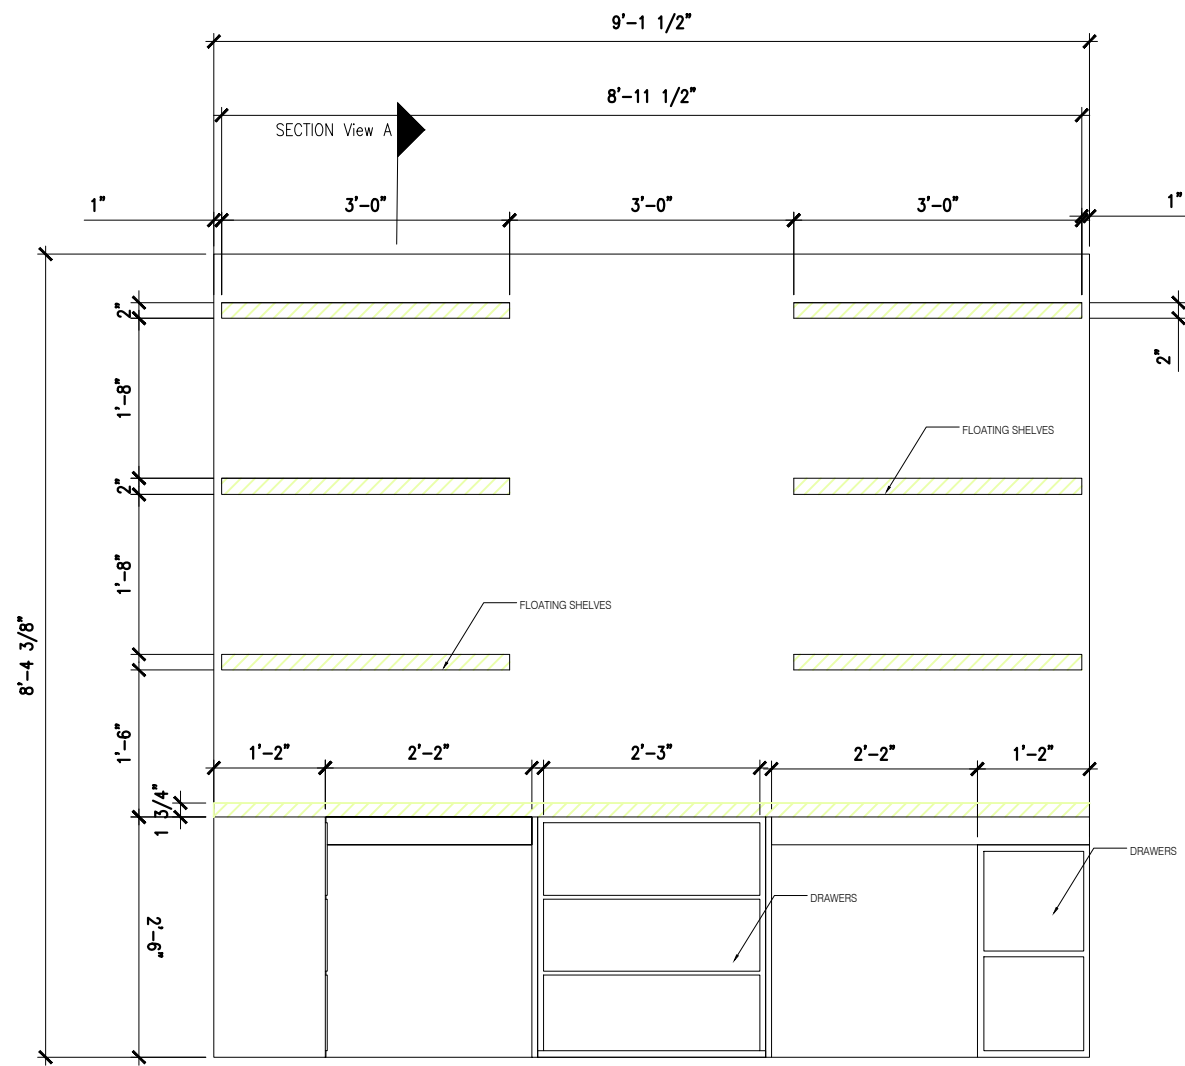

FRONT VIEW

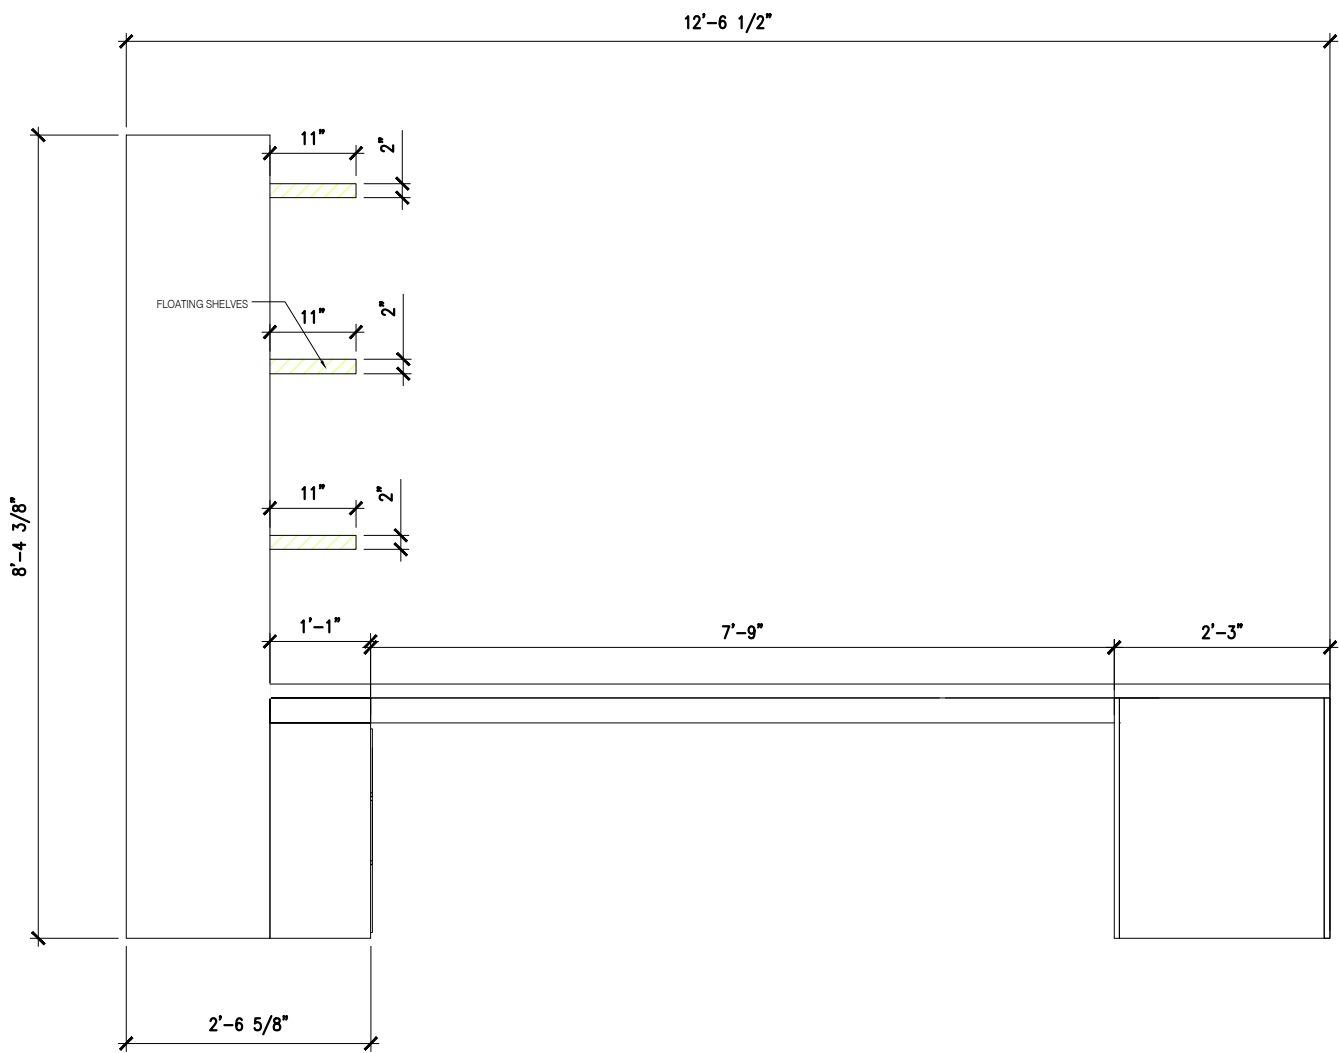

SIDE VIEW

GENERAL NOTES:

All rights reserved. This drawing is the exclusive property of Eastern Yards Custom Woodworking. Reproduction, distribution, or use of this drawing without written consent is prohibited.

The client is responsible for verifying all dimensions prior to approval. Eastern Yards Custom Woodworking is not responsible for errors in measurements provided by the client. Shop drawings must be signed by the client prior to fabrication. Eastern Yards Custom Woodworking is not responsible for site conditions not shown on drawings. All walls must be straight, level, and plumb, and no field conditions are assumed unless supported.

All dimensions are to be verified in the field. Do not scale drawings. All dimensions are in inches unless noted otherwise. Fabrication will begin after receipt of signed shop drawings.

NO.	REVISION	DATE
-----	----------	------

Project Name:

Project Address:

TITLE:

L-SHAPE DESK CABINET
WITH FLOATING SHELVES

JOB:

DATE: 9/16/25


SCALE:

SHEET


1



EASTERN YARDS LLC
100 E MINEOLA AVE
VALLEY STREAM, NY 11580

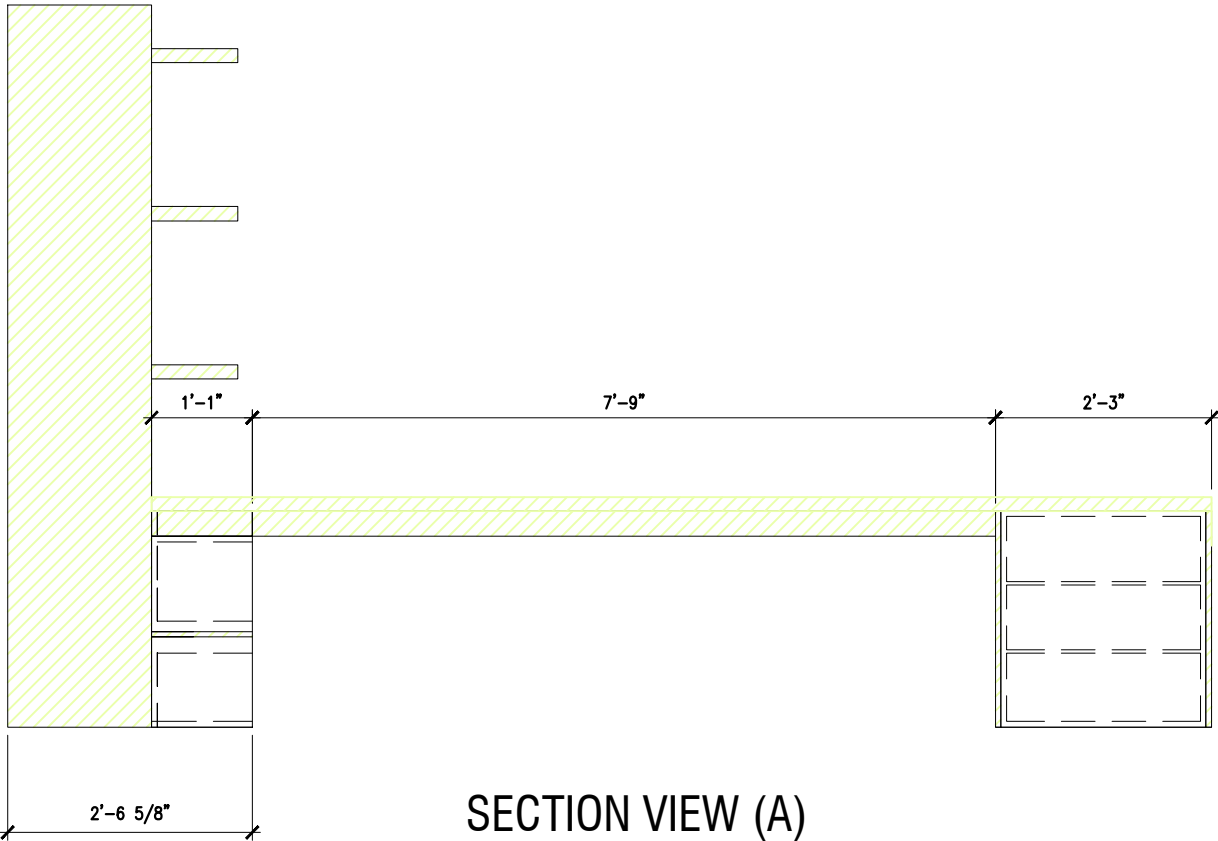

SECTION VIEW (A)

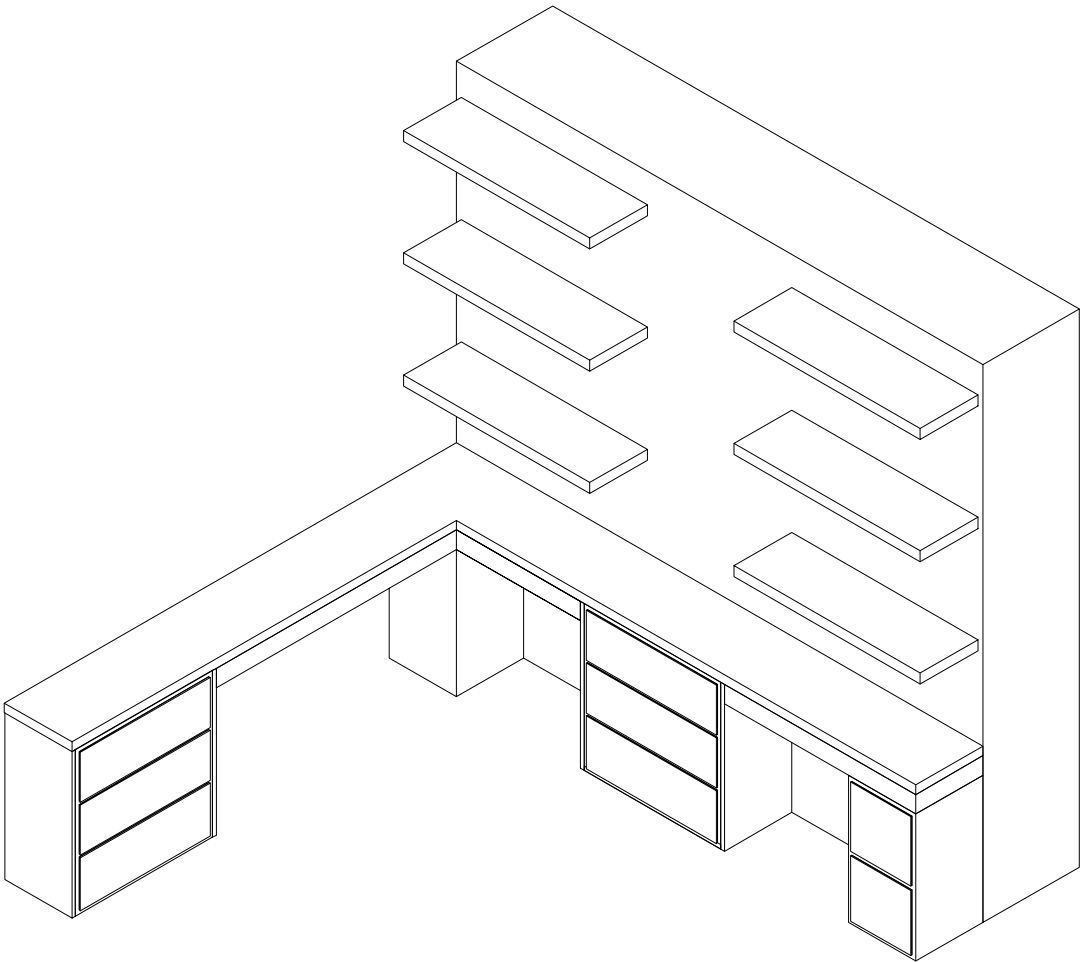

ISOMETRIC VIEW

GENERAL NOTES:

All rights reserved. This drawing is the exclusive property of Eastern Yards Custom Woodworking. Reproduction, distribution, or use of this drawing without written consent is prohibited.

The client is responsible for verifying all dimensions prior to approval. Eastern Yards Custom Woodworking is not responsible for errors in measurements provided by the client. Shop drawings must be signed by the client prior to fabrication. Eastern Yards Custom Woodworking is not responsible for site conditions not shown on drawings. All walls must be straight, level, and plumb, and no field conditions are assumed unless supported.

All dimensions are to be verified in the field. Do not scale drawings. All dimensions are in inches unless noted otherwise. Fabrication will begin after receipt of signed shop drawings.

NO.	REVISION	DATE

Project Name:

Project Address:

TITLE:

L-SHAPE DESK CABINET
WITH FLOATING SHELVES

JOB:

DATE: 9/16/25

SCALE:

SHEET

2



EASTERN YARDS LLC
100 E MINEOLA AVE
VALLEY STREAM, NY 11580