

EKIMETRICS

525 E 72ND STREET, NEW YORK NY 10021

29TH FLOOR

MATERIAL LEGEND

FLOOR TILE
(CT-1)
MANF: CROSSVILLE
STYLE: SHADES 2.0
COLOR: SHD48 THUNDER
SIZE: 12"x24"
CONTACT:

INSTALLATION: STACKED

GROUT COLOR APPROVAL:
TBD

WALL TILE
(T-1)
MANF: NEMO TILE
STYLE: ARA
COLOR: NATURALE,GLOSSY FINISH
SIZE: 2"x10"
CONTACT:

INSTALLATION: STACKED

GROUT COLOR APPROVAL:
TBD

STONE COUNTERTOP
(SS2)
MANF: WILSONART
STYLE: MOUNTAIN CARRARA Q6021
COLOR: POLISHED FINISH
SIZE: 3/4" THICK
CONTACT:

STONE COUNTERTOP
(SS3)
MANF: CAESARSTONE
STYLE: #5131 CALACATTA NUVO
COLOR: POLISHED FINISH
SIZE: 3/4"THICK
CONTACT:

DRAWING LEGEND:

- CS-001COVER SHEET, DRAWING LEGEND & MATERIAL LEGEND
- KY-001KEY PLAN - 29TH FLOOR
- KY-001KEY PLAN - 29TH FLOOR
- T-100PLAN/ELEVATIONS - BATHROOMS
- T-101PLAN/ELEVATIONS - BATHROOMS
- T-102PLAN/ELEVATIONS - JANITOR'S CLOSET
- T-103PLAN/ELEVATIONS - PANTRY
- T-200STONE COUNTERTOPS - WOMEN'S BATHROOM
- T-201STONE COUNTERTOPS - MEN'S BATHROOM
- T-300DETAILS - TILE
- T-301DETAILS - TILE
- T-302DETAILS - TILE
- T-400DETAILS - STONE COUNTERTOPS
- T-401DETAILS - STONE COUNTERTOPS
- T-402DETAILS - STONE COUNTERTOPS

ARCHITECT TO CONFIRM:

GROUT JOINT AT CT-1 TO BE 1/8"
GROUT JOINT AT T-1 TO BE 1/16"

PLEASE NOTE:

NO EXPANSION JOINTS ARE SHOWN IN THE TILE FLOORING AS THERE ARE NO EXPANSION JOINTS SHOWN IN THE ARCHITECTURAL DRAWINGS. IF EXPANSION OR MOVEMENT JOINTS ARE REQUIRED, ARCHITECT TO PROVIDE LOCATION AND DETAILS ACCORDINGLY

PER THE TCNA, "USE OF WALL-WASHER AND COVE-TYPE LIGHTING, WHERE THE LIGHTS ARE LOCATED EITHER AT THE WALL/CEILING INTERFACE OR MOUNTED DIRECTLY ON THE WALL, ARE POPULAR TECHNIQUES FOR PRODUCING DRAMATIC ROOM LIGHTING EFFECTS. WHEN PROPER BACKING SURFACES, INSTALLATION MATERIALS AND METHODS, AND LOCATION OF LIGHT FIXTURES ARE NOT CAREFULLY COORDINATED, THESE LIGHTING TECHNIQUES MAY PRODUCE SHADOWS AND UNDESIRABLE EFFECTS WITH CERAMIC TILES, SIMILAR SHADOWS ARE CREATED FROM SIDE LIGHTING INTERIOR WALLS AND FLOORS WHEN LIGHT SHINES AT THAT ANGLE THROUGH WINDOWS AND DOORS."

PLEASE TAKE NOTE OF THIS AS IT RELATES TO THE TILE IN THIS PROJECT.

AUSTRO TILE & STONE, LLC
30-25 93RD STREET
EAST ELMHURST, NY 11369

CONTRACTOR:
JRM CONSTRUCTION
MANAGEMENT, LLC
242 WEST 36TH STREET
11TH FLOOR
NEW YORK, NY 10018

INTERIOR DESIGNER:

ISSUE FOR APPROVAL	09/30/24
ISSUE NAME	DATE

PROJECT:

SDGI
200 WEST 41ST STREET
NEW YORK, NY 10036
PHONE: 212-704-0734

PROJECT NAME:

EKIMETRICS
120 BROADWAY
NEW YORK, NY 10271

SHEET NAME:

COVER SHEET

DATE:	
PROJECT NO.:	
PRINCIPAL:	
DRAWING BY:	
CHECKED BY:	
SCALE:	AS NOTED
DWG No.:	
CS-001	
1	of 9

[illegible]

--	--

INTERIOR DESIGNER:

[illegible]

SDGI
200 WEST 41ST STREET
NEW YORK, NY 10036
PHONE: 212-704-0734

SHEET NAME:

KEYPLAN
29TH FLOOR

DATE: _____
PROJECT NO.: _____
PRINCIPAL: _____
DRAWING BY: _____
CHECKED BY: _____
SCALE: _____
DWG No.: _____
KY-001
2 of 15

LOCATION

The floor plan shows a large rectangular space with several rooms and open areas. The rooms are labeled as follows:

- OPEN AREA 29.22
- OPEN AREA 29.23
- COAT 29.14 1A
- GAME RM. 29.13
- SEATING AREA 29.24
- PANTRY 29.26 (highlighted in orange)

The plan also shows a large open area at the bottom, a staircase, and a large rectangular area on the right side. The drawing is a detailed architectural plan with walls, doors, and furniture indicated by symbols.

AUSTRO TILE & STONE, LLC
30-25 93RD STREET
EAST ELMHURST, NY 11369

CONTRACTOR:
JRM CONSTRUCTION
MANAGEMENT, LLC
242 WEST 36TH STREET
11TH FLOOR
NEW YORK, NY 10018

INTERIOR DESIGNER:

ISSUE FOR APPROVAL
09/30/24

ISSUE NAME
DATE

ARCHITECT:
SDGI
200 WEST 41ST STREET
NEW YORK, NY 10036
PHONE: 212-704-0734

PROJECT NAME:
EKIMETRICS
120 BROADWAY
NEW YORK, NY 10271

SHEET NAME:
KEYPLAN
29TH FLOOR

DATE:
PROJECT NO.:
PRINCIPAL:
DRAWING BY:
CHECKED BY:
SCALE:
DWG No.:
KY-002
3 of 10

01
3/32"=1'-0"

PLAN: 29TH FLOOR (WEST SIDE)

DATE: _____
PROJECT NO.: _____
PRINCIPAL: _____
DRAWING BY: _____
CHECKED BY: _____
SCALE: _____
DWG No.: _____
KY-002
3 of 15

01 3/32"=1'-0"	PLAN: 29TH FLOOR (WEST SIDE)
-------------------	------------------------------





WOMEN'S
29.04

MEN'S
29.05


J.CLO.
29.06

01
1/2"=1'-0" PLAN: WOMEN'S BATHROOM (29.04)

 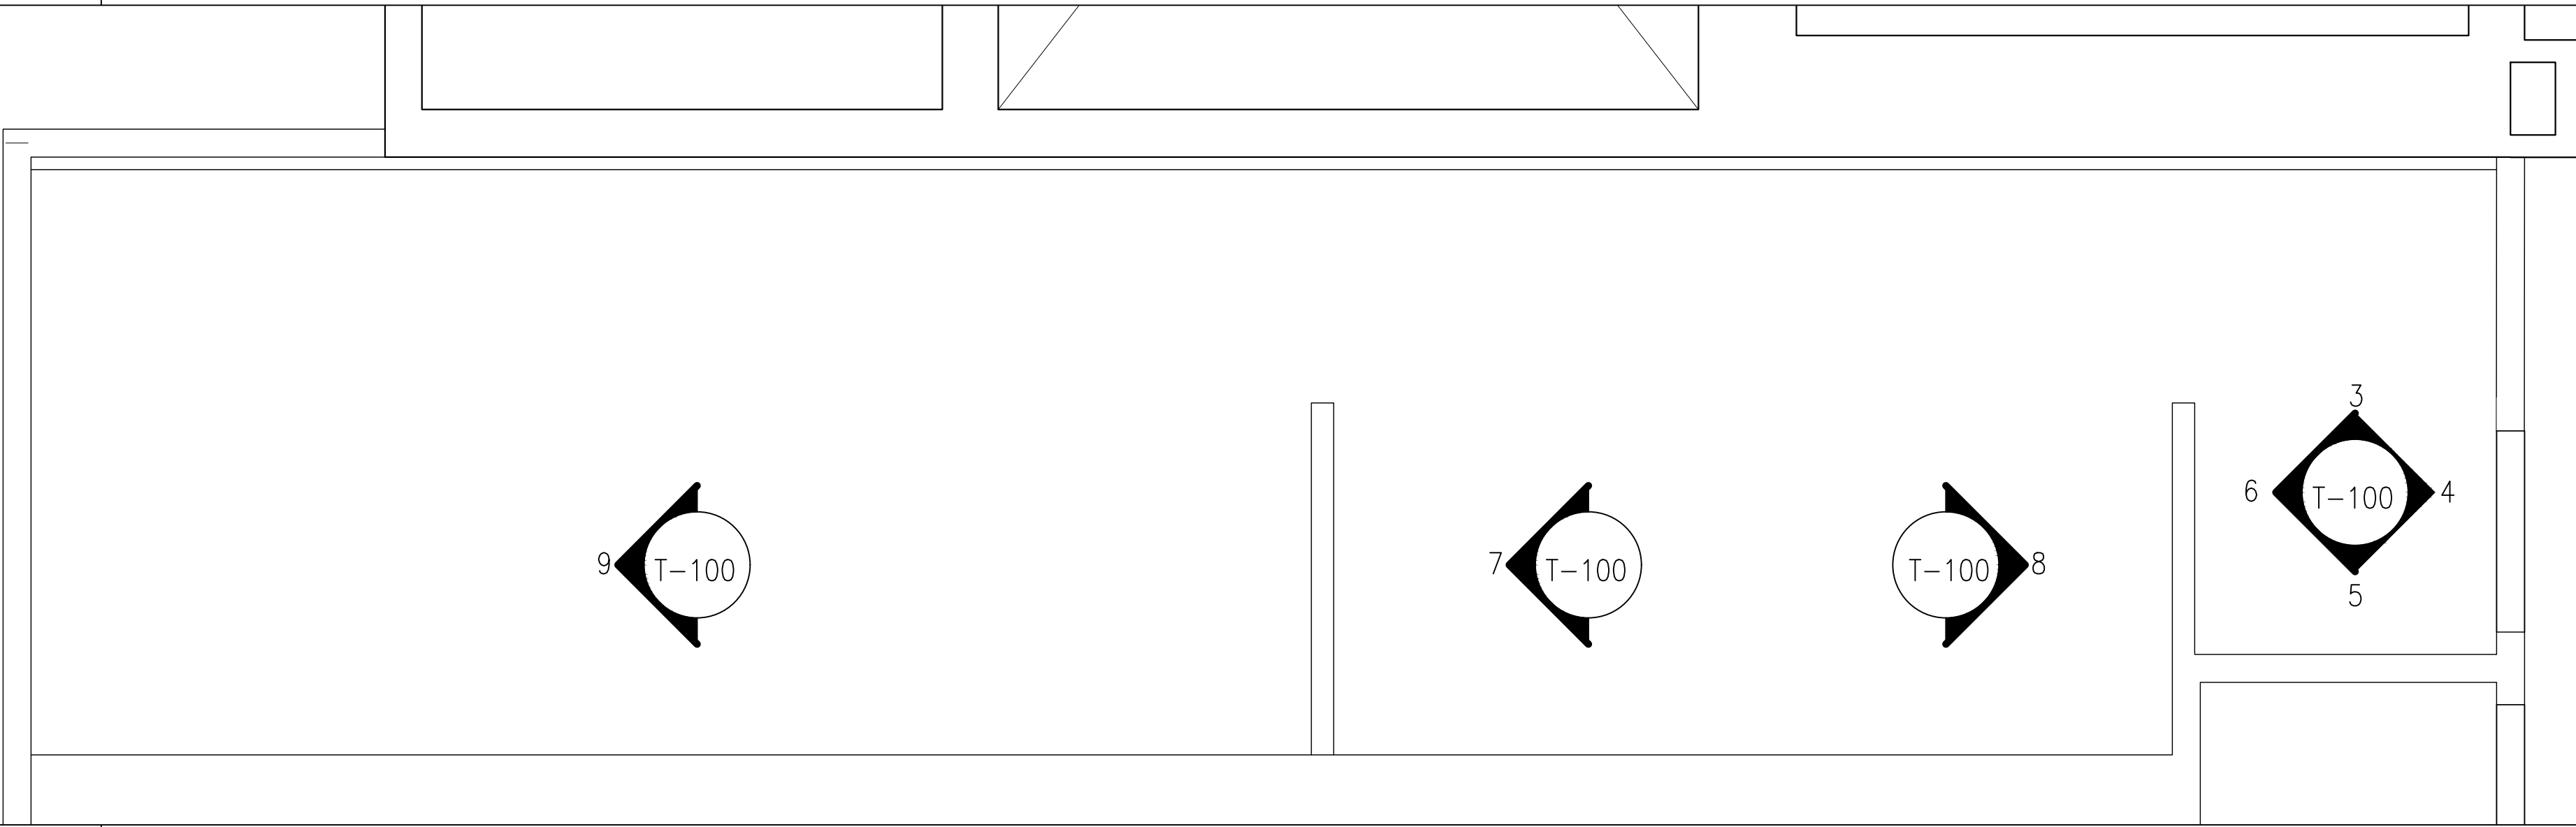


03
1/2"=1'-0" ELEVATION: NORTH


02
1/2"=1'-0" PLAN: WOMEN'S BATHROOM (29.04)

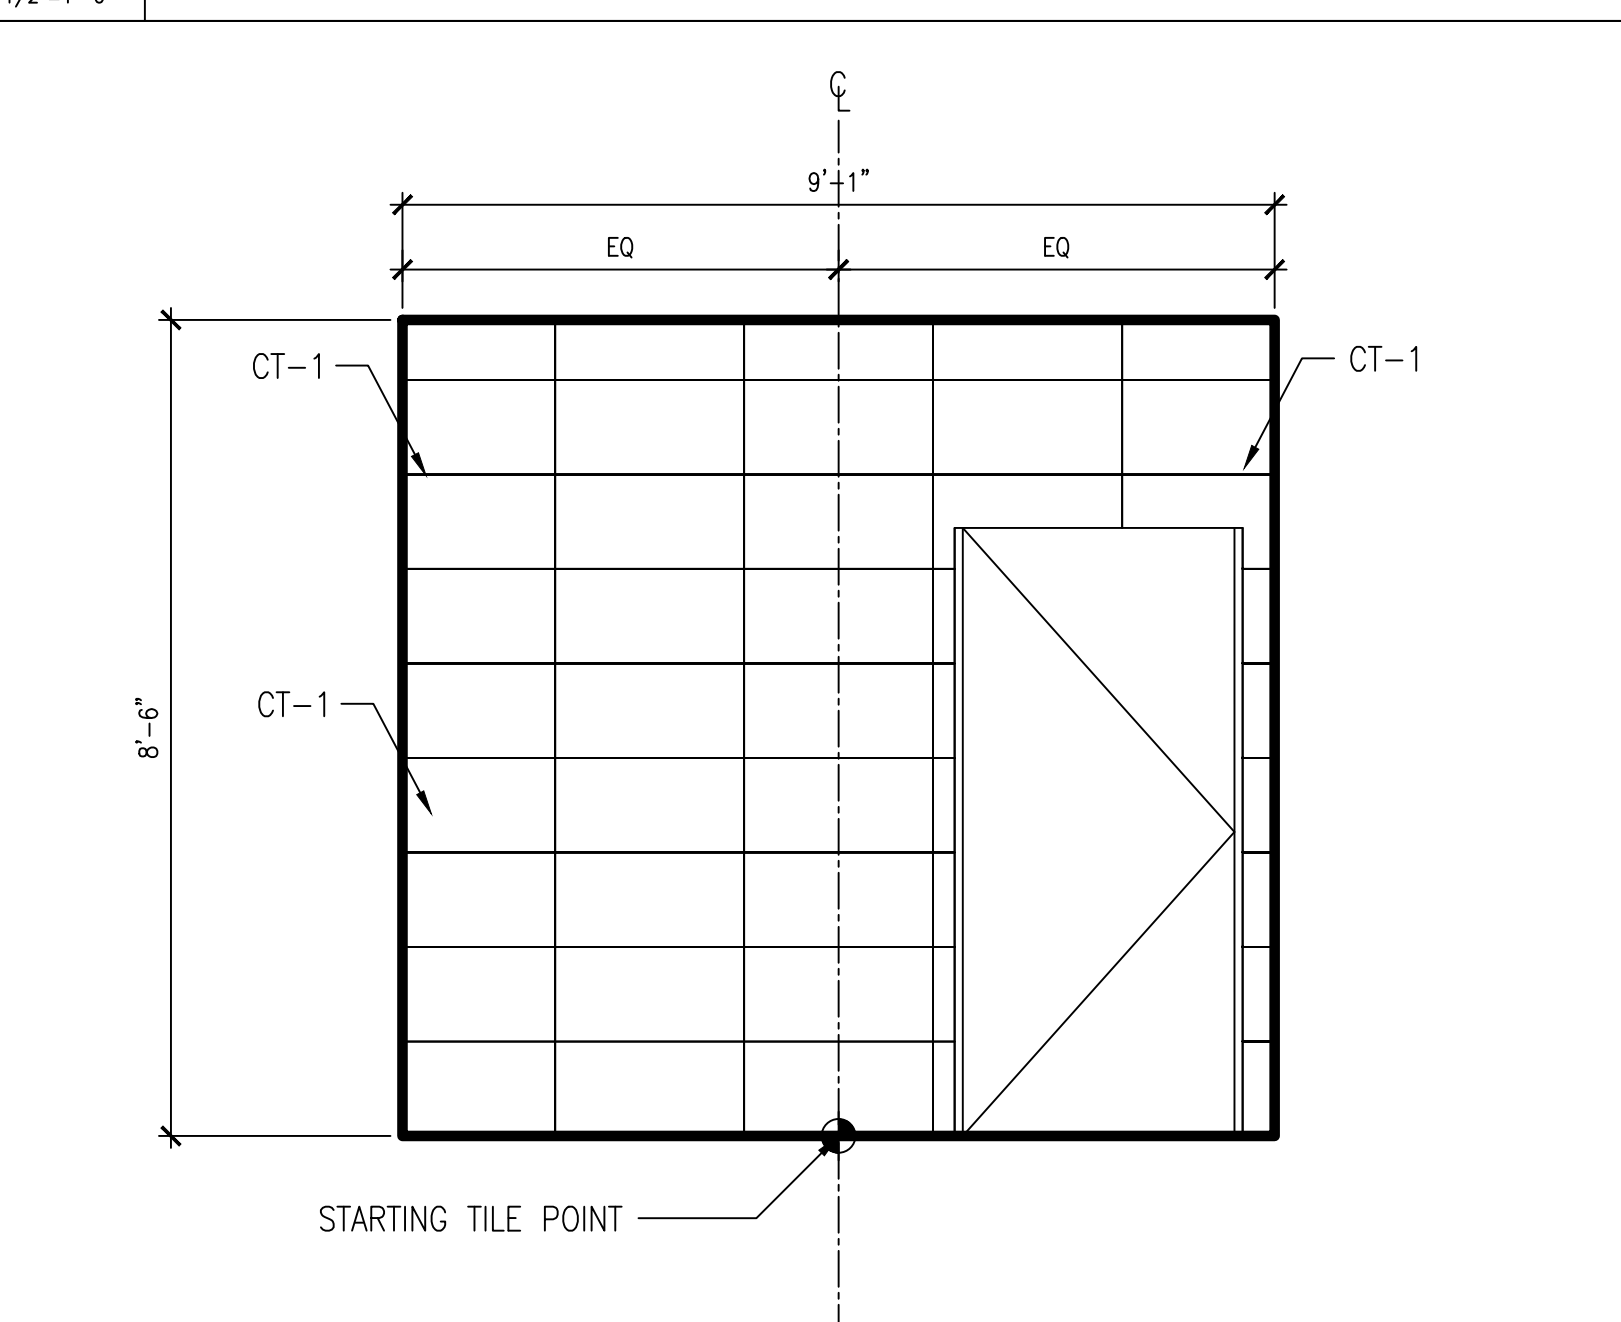


04
1/2"=1'-0" ELEVATION: EAST

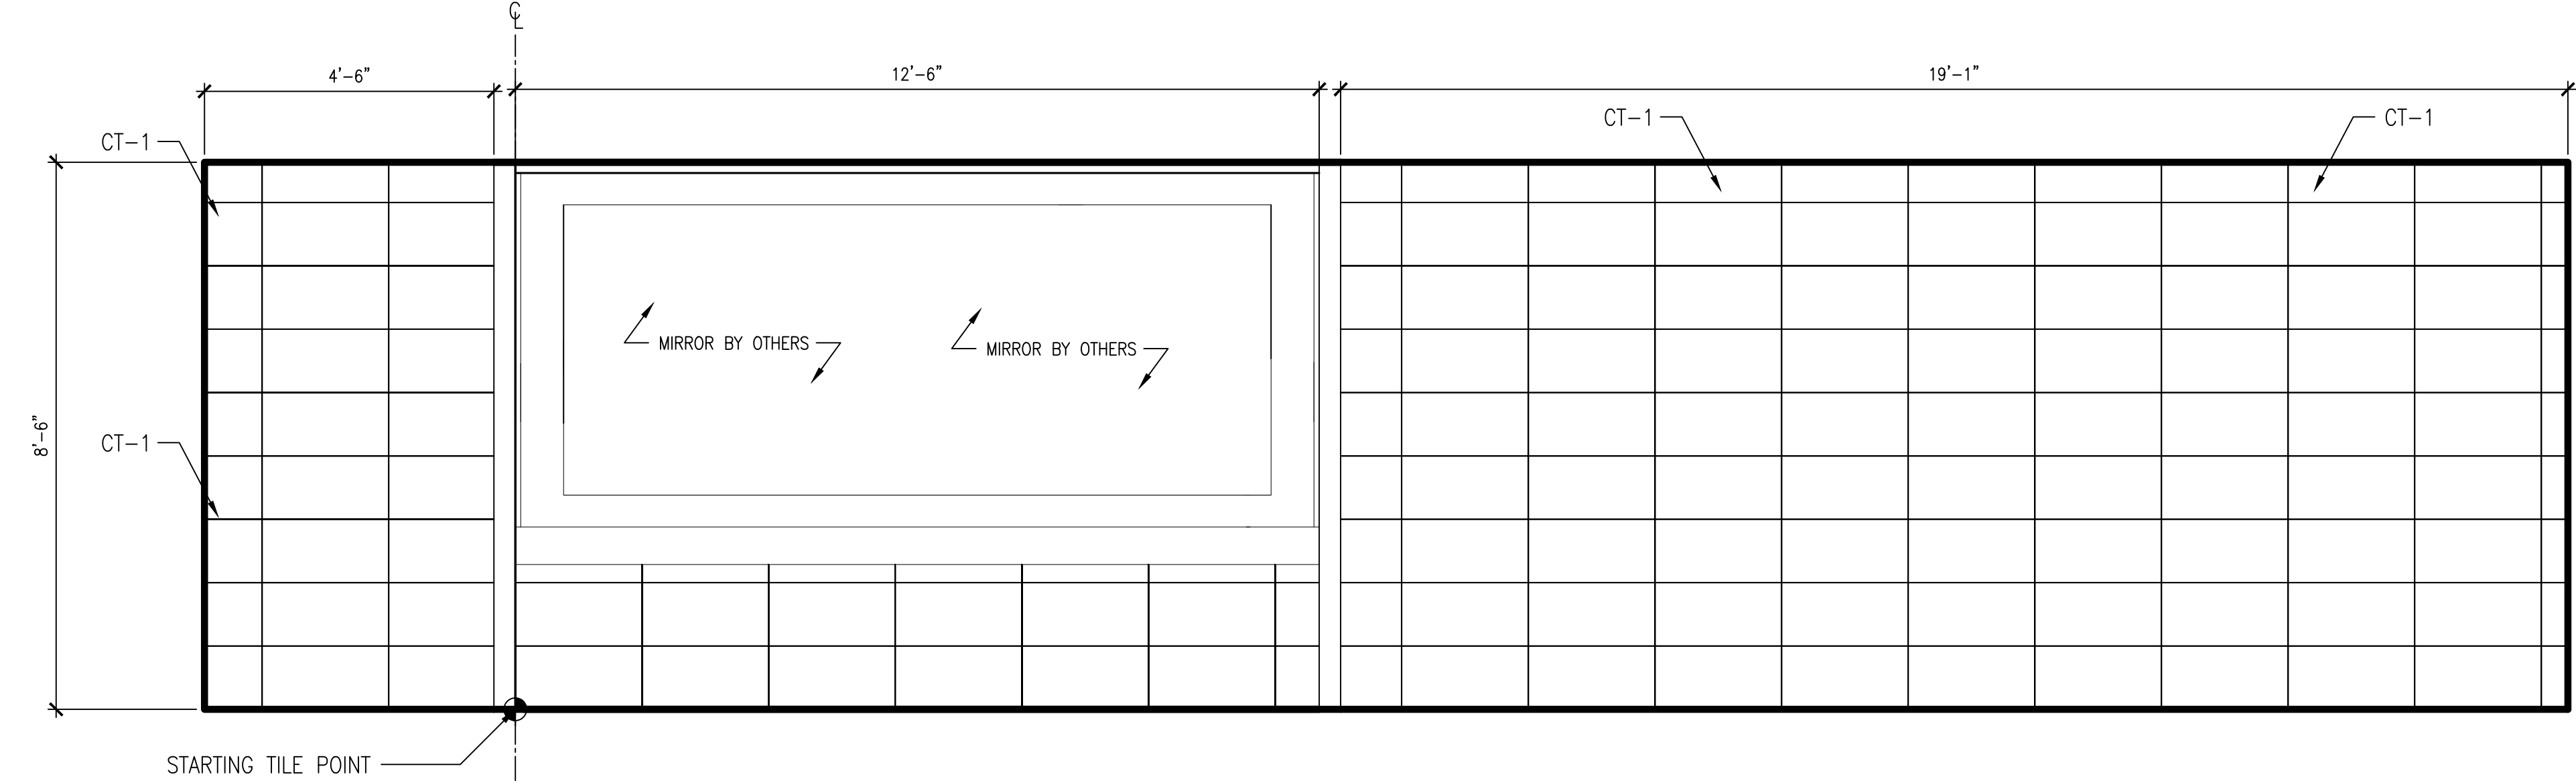


05
1/2"=1'-0" ELEVATION: SOUTH

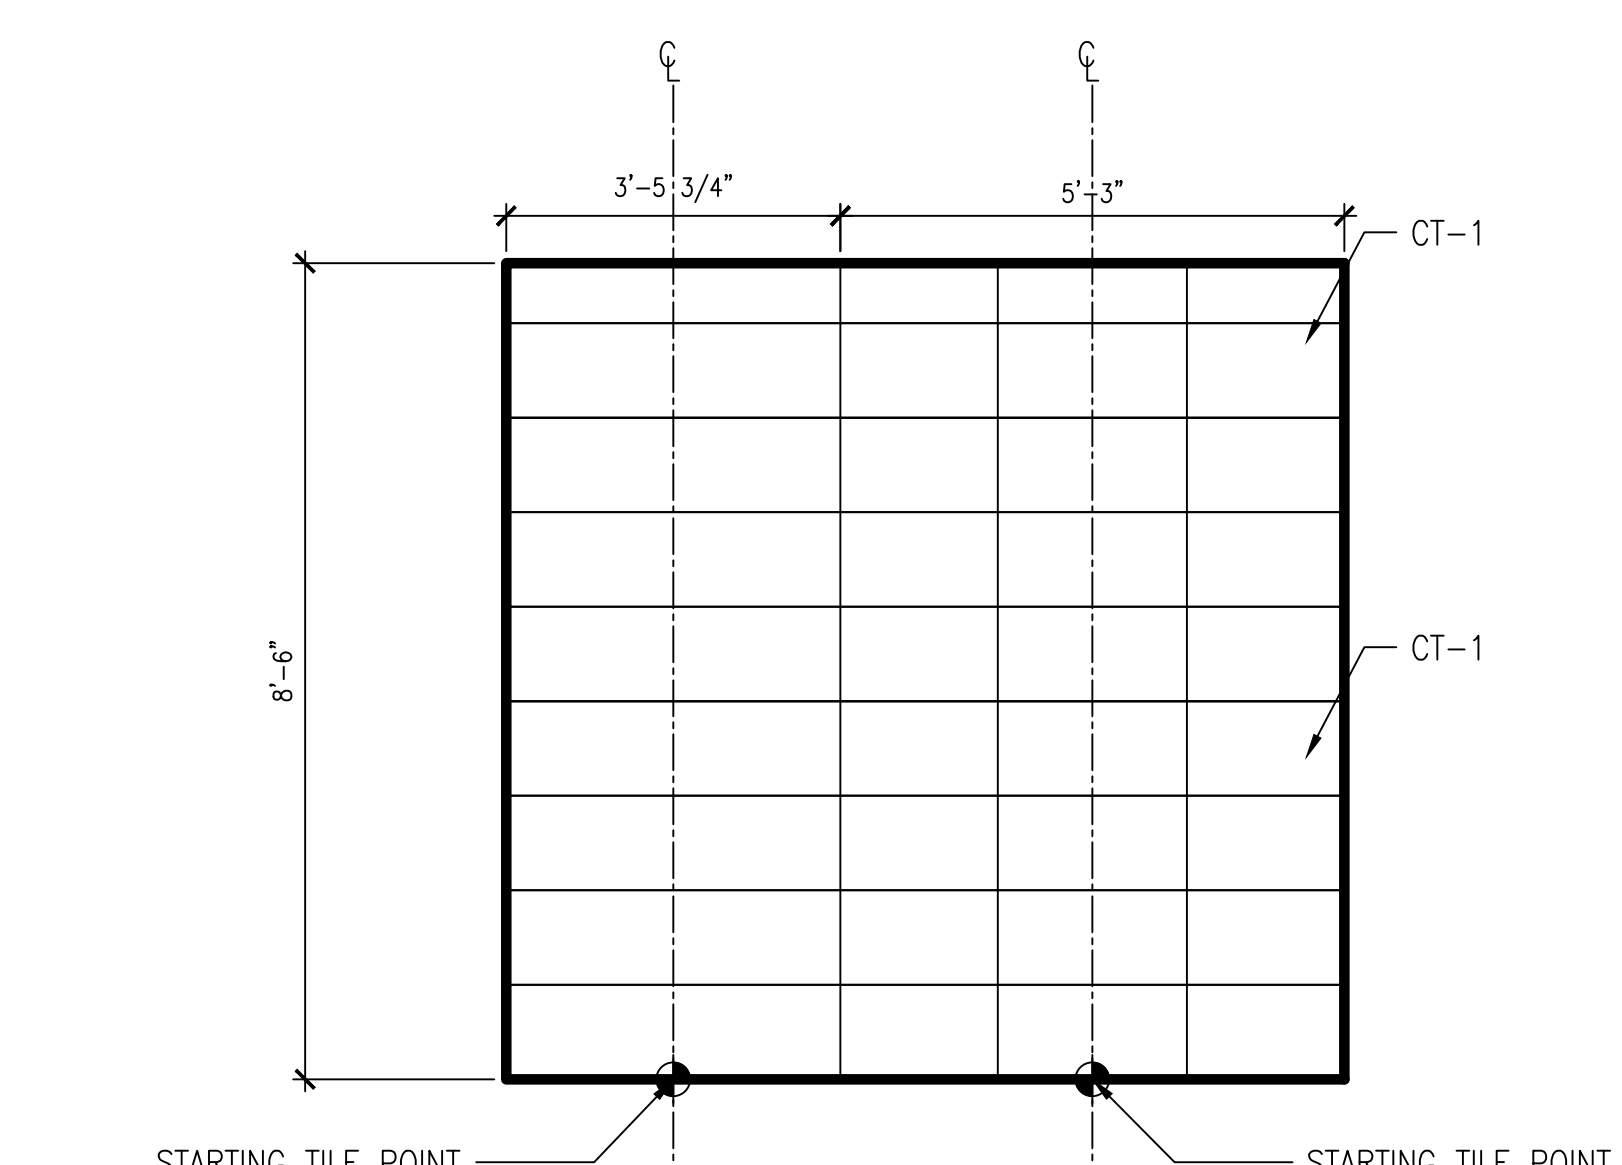


06
1/2"=1'-0" ELEVATION: WEST

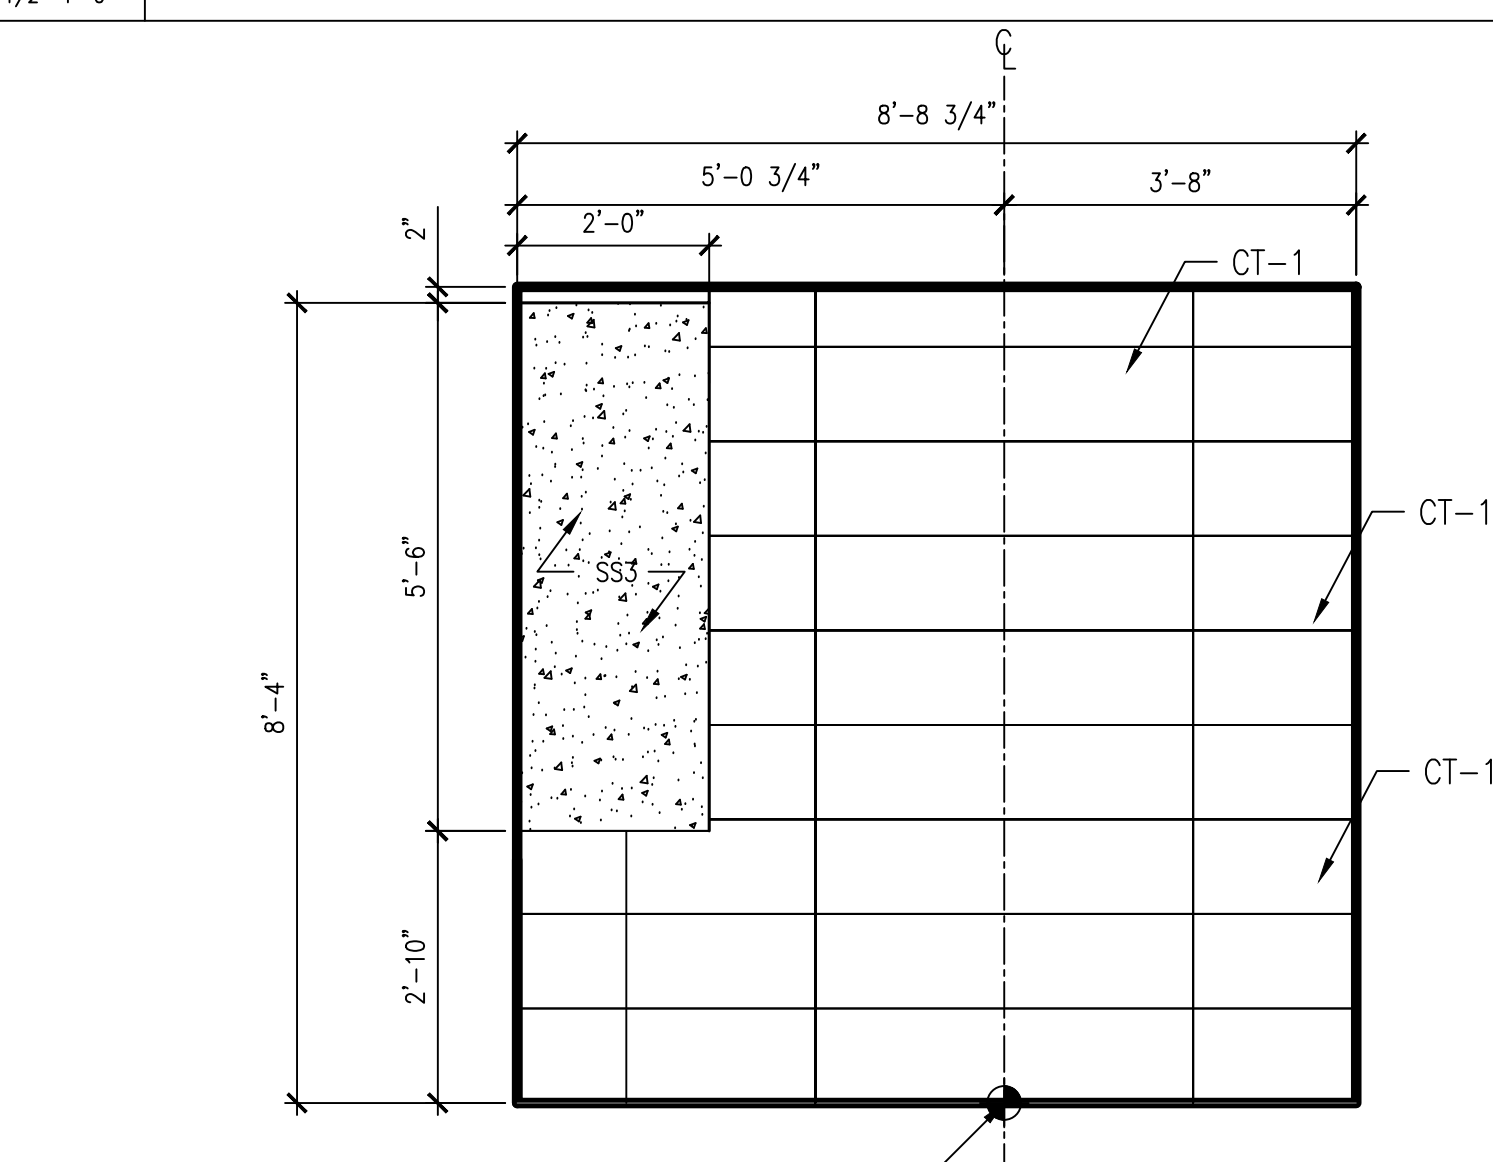

07
1/2"=1'-0" ELEVATION: WEST

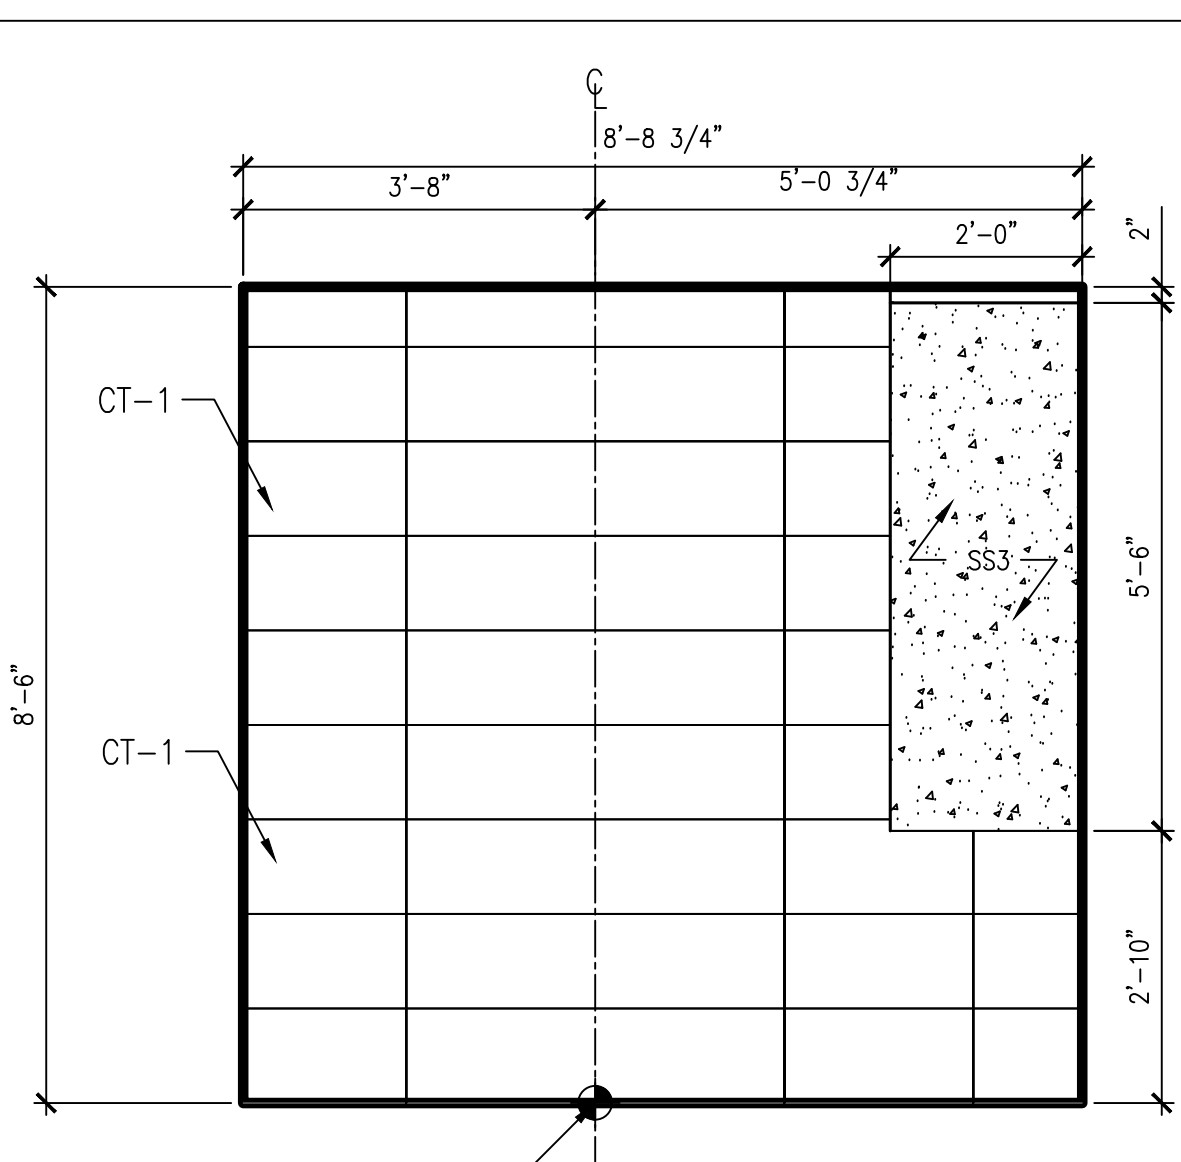

08
1/2"=1'-0" ELEVATION: EAST

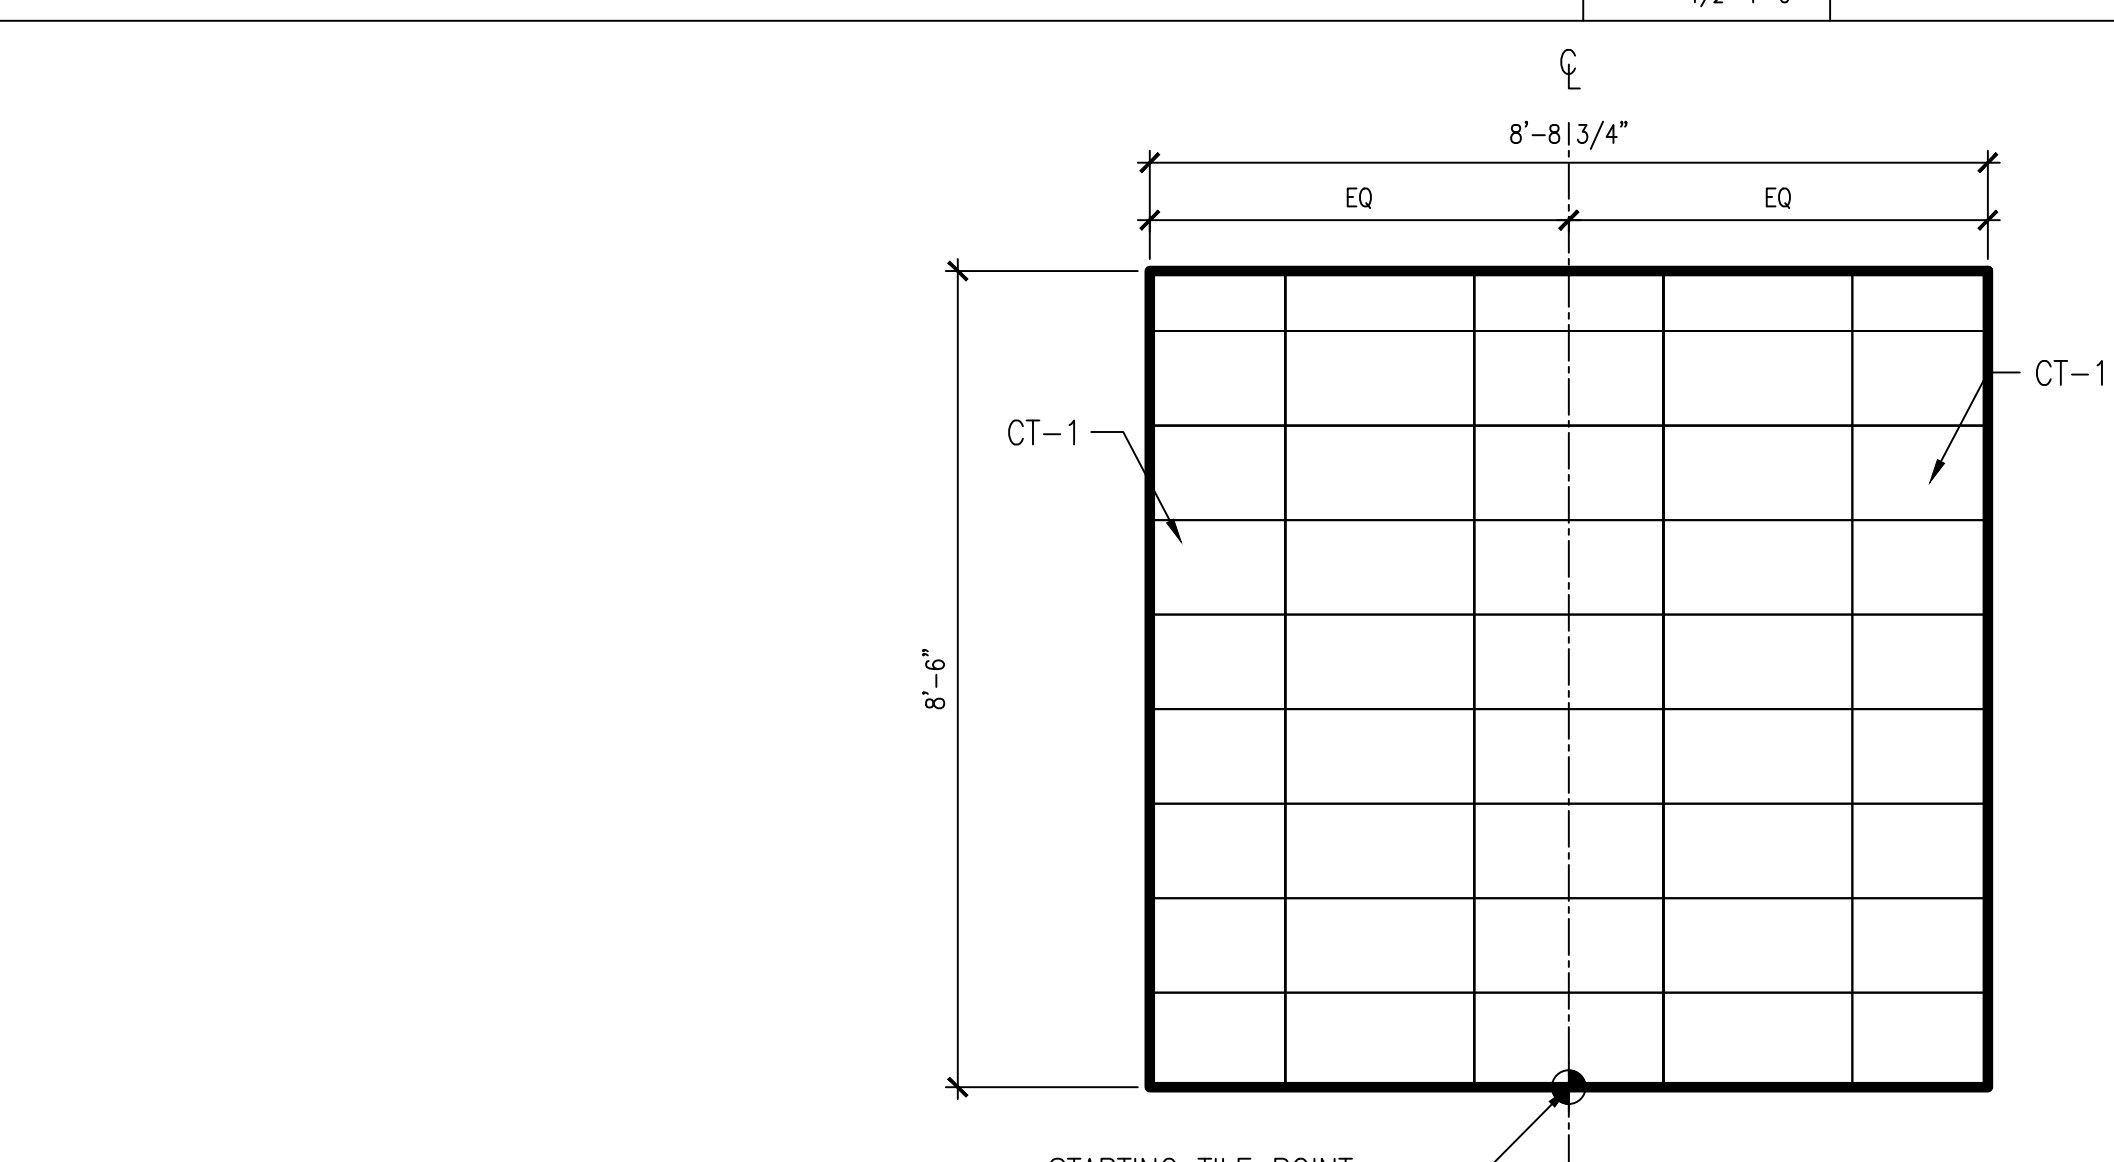

09
1/2"=1'-0" ELEVATION: EAST

AUSTRO TILE & STONE, LLC
30-25 93RD STREET
EAST ELMHURST, NY 11369

CONTRACTOR: JRM CONSTRUCTION
MANAGEMENT, LLC
242 WEST 36TH STREET
11TH FLOOR
NEW YORK, NY 10018

INTERIOR DESIGNER:

ISSUE FOR APPROVAL 09/30/24

ISSUE NAME DATE

PROJECT: SDGI
200 WEST 41ST STREET
NEW YORK, NY 10036
PHONE: 212-704-0734

PROJECT NAME: EKIMETRICS
120 BROADWAY
NEW YORK, NY 10271

SHEET NAME: PLAN/ELEVATIONS
BATHROOMS

DATE:
PROJECT NO.:
PRINCIPAL:
DRAWING BY:
CHECKED BY:
SCALE:
DWG No.:
T-100
4 of 15




WOMEN'S
29.04


MEN'S
29.05

J.CLO.
29.06


01
1/2"=1'-0" PLAN: MEN'S BATHROOMS (29.05)

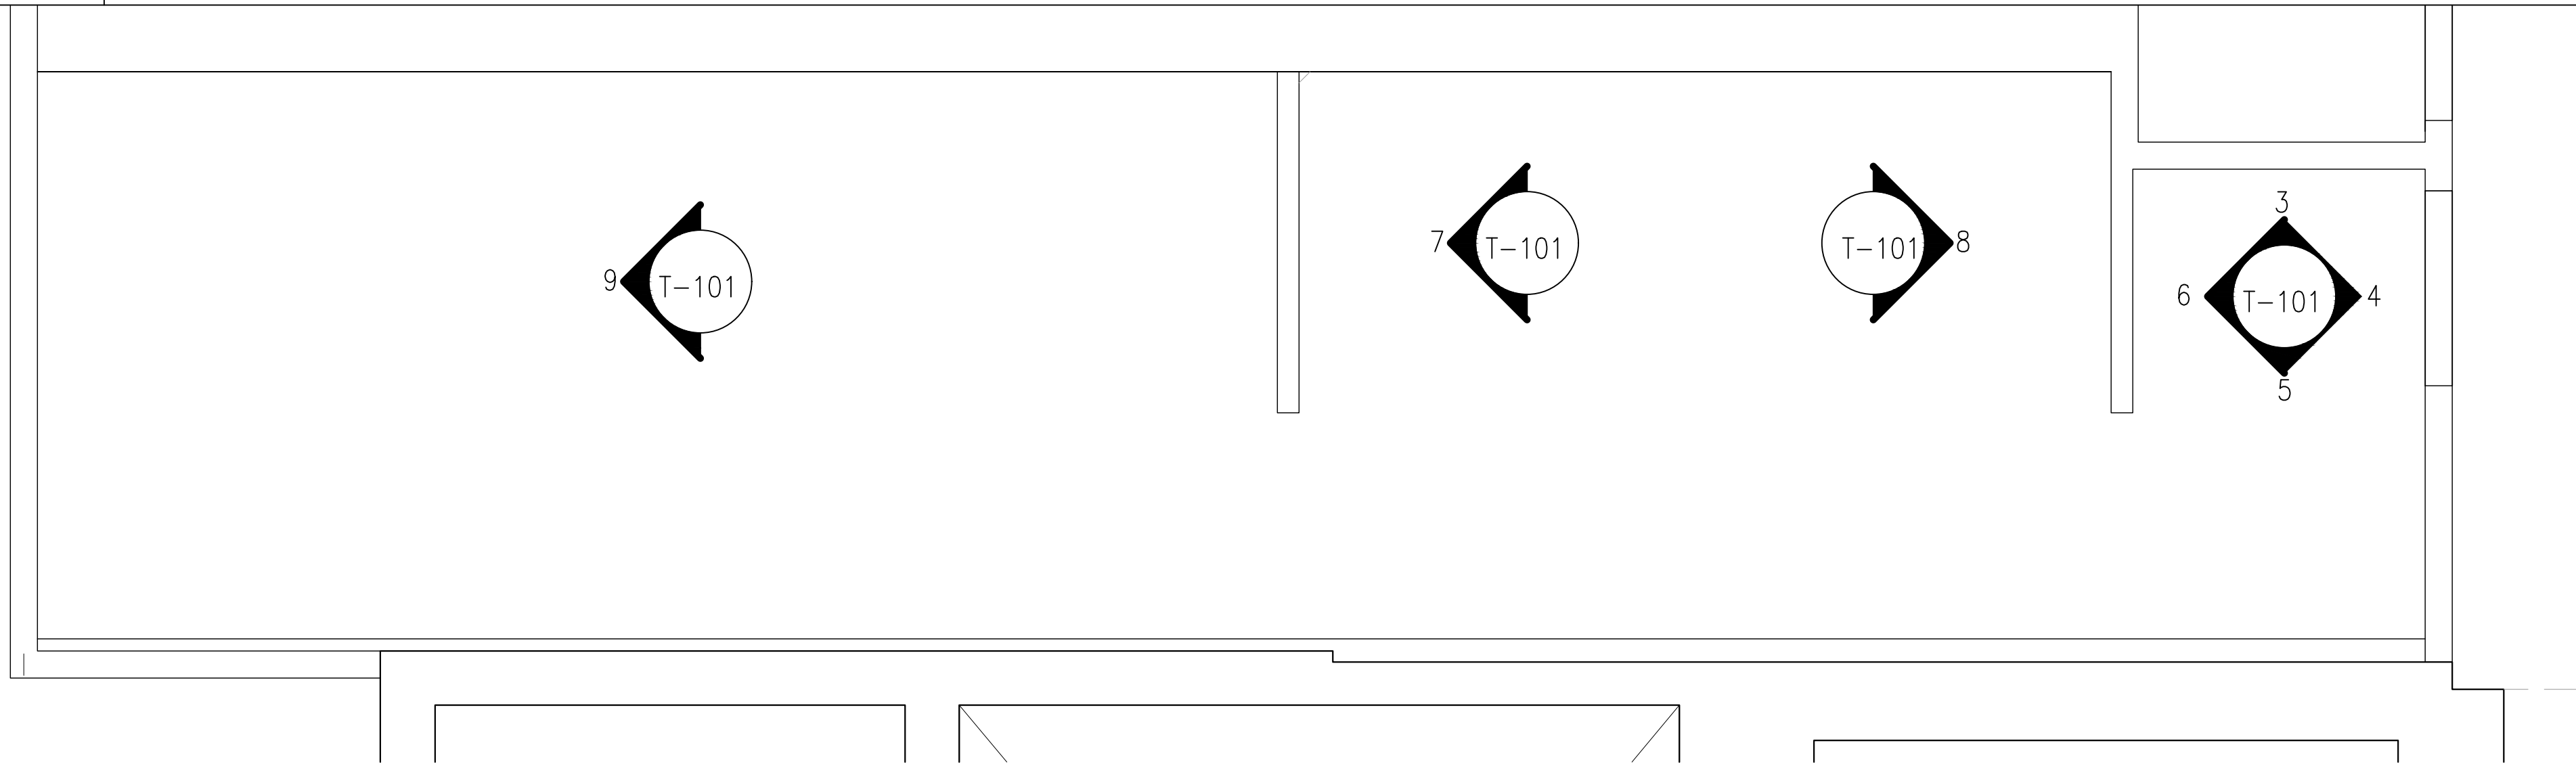


03
1/2"=1'-0" ELEVATION: NORTH

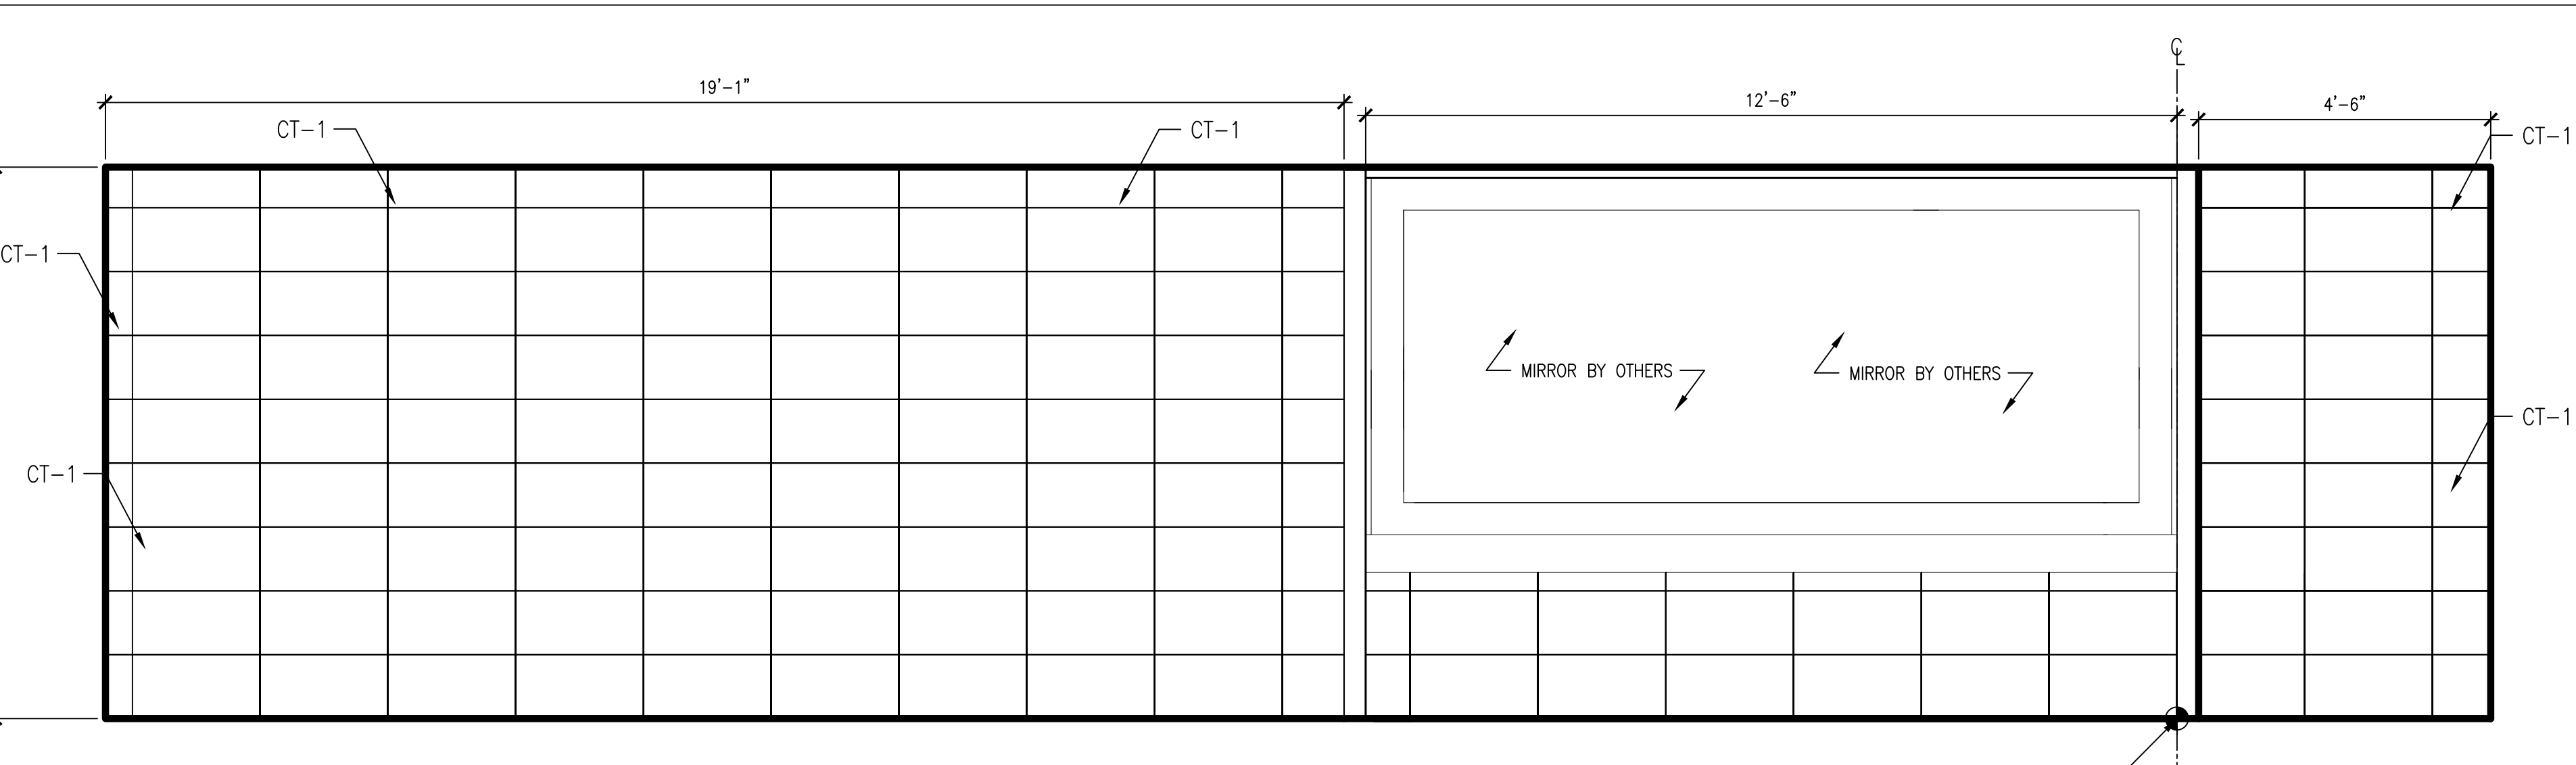


02
1/2"=1'-0" PLAN: MEN'S BATHROOMS (29.05)

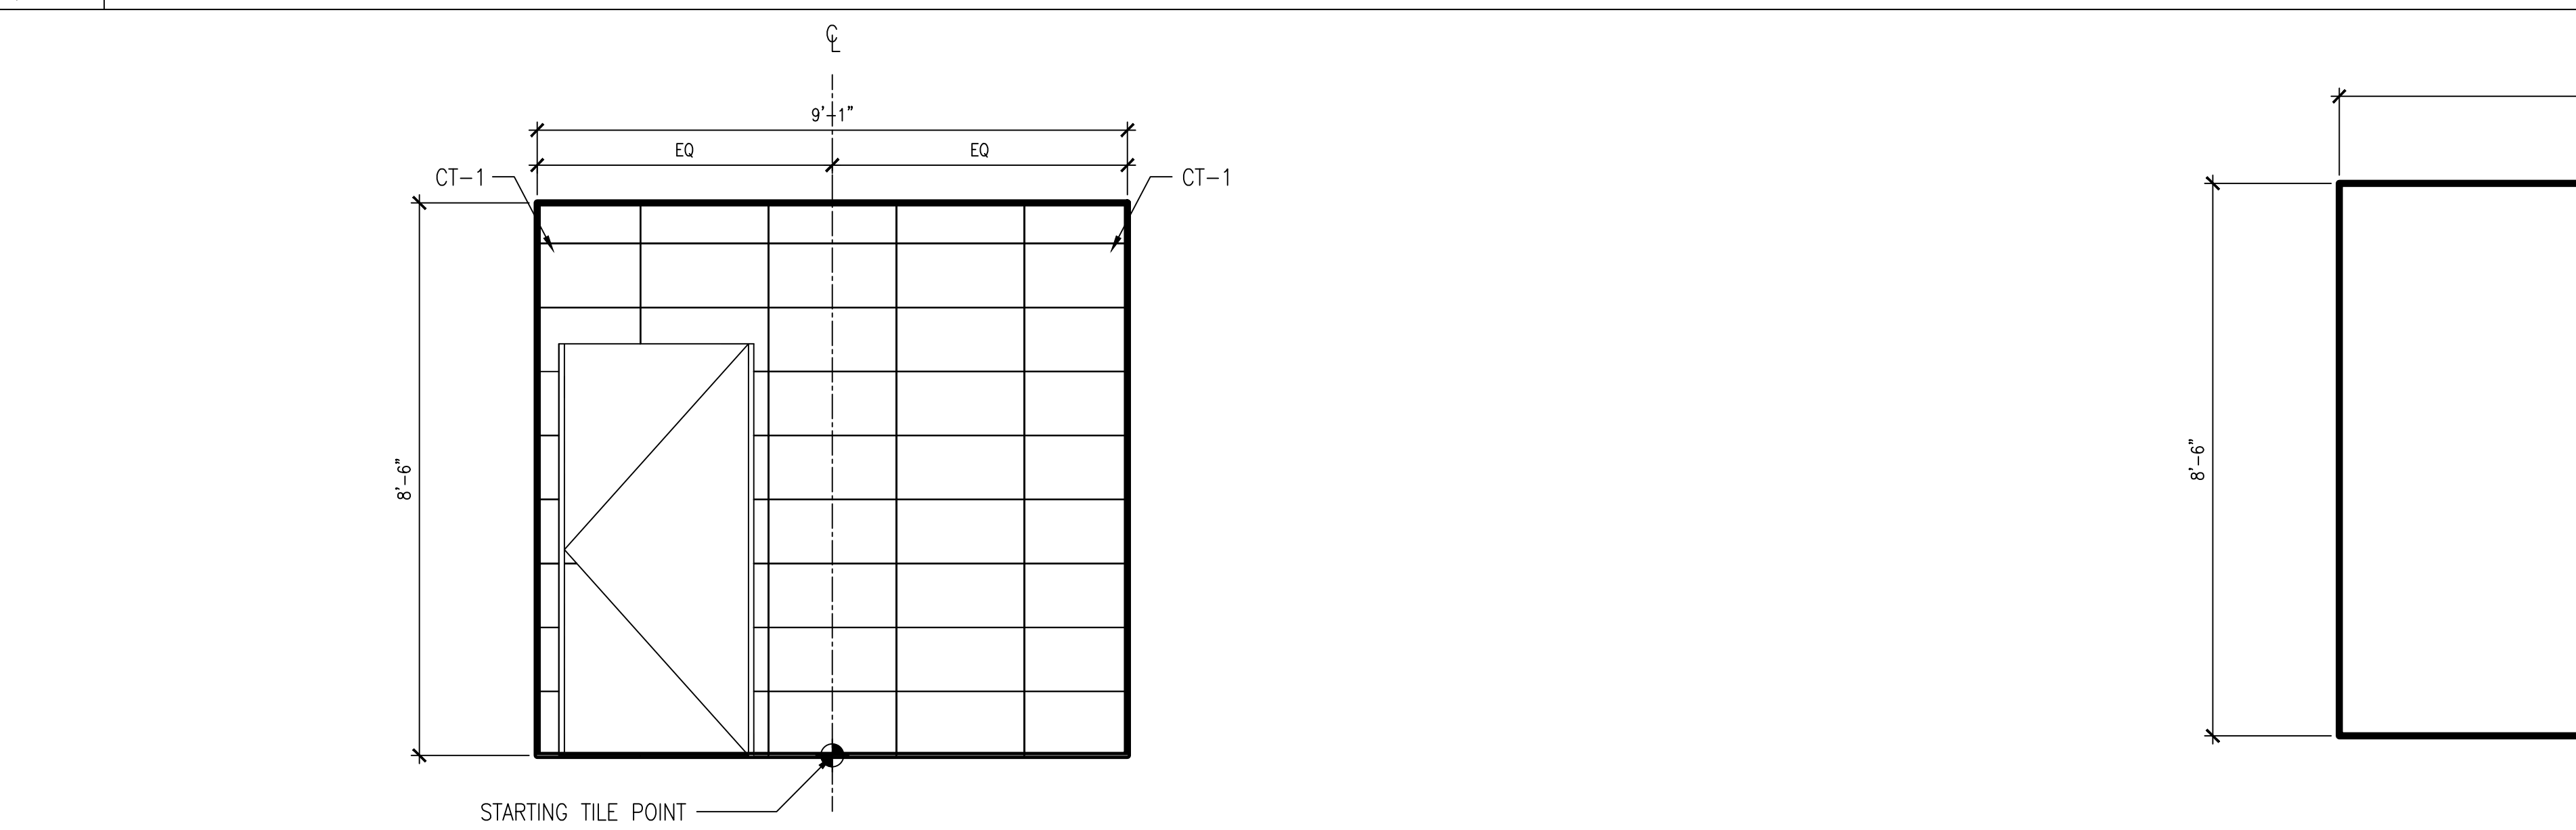


03
1/2"=1'-0" ELEVATION: NORTH

 


04
1/2"=1'-0" ELEVATION: EAST

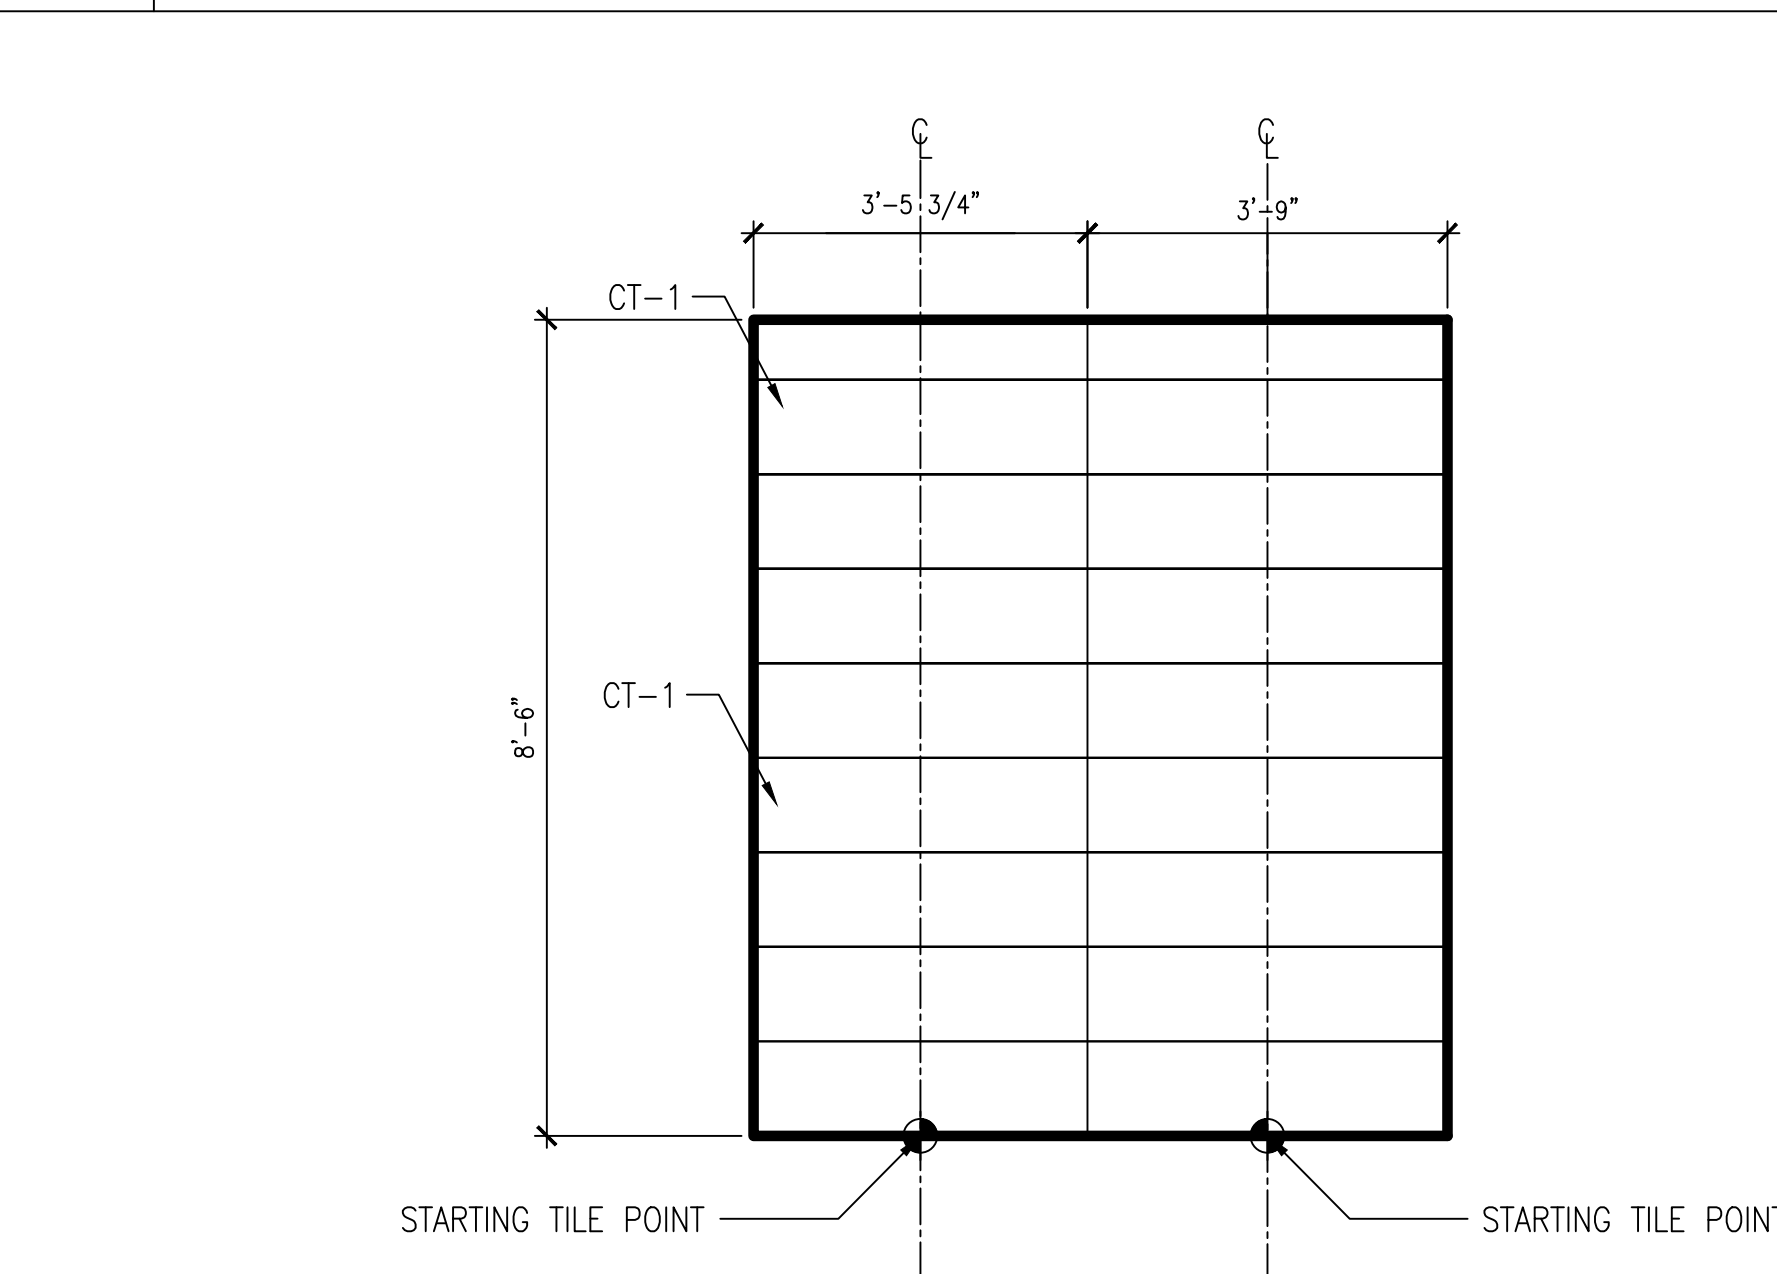


05
1/2"=1'-0" ELEVATION: SOUTH

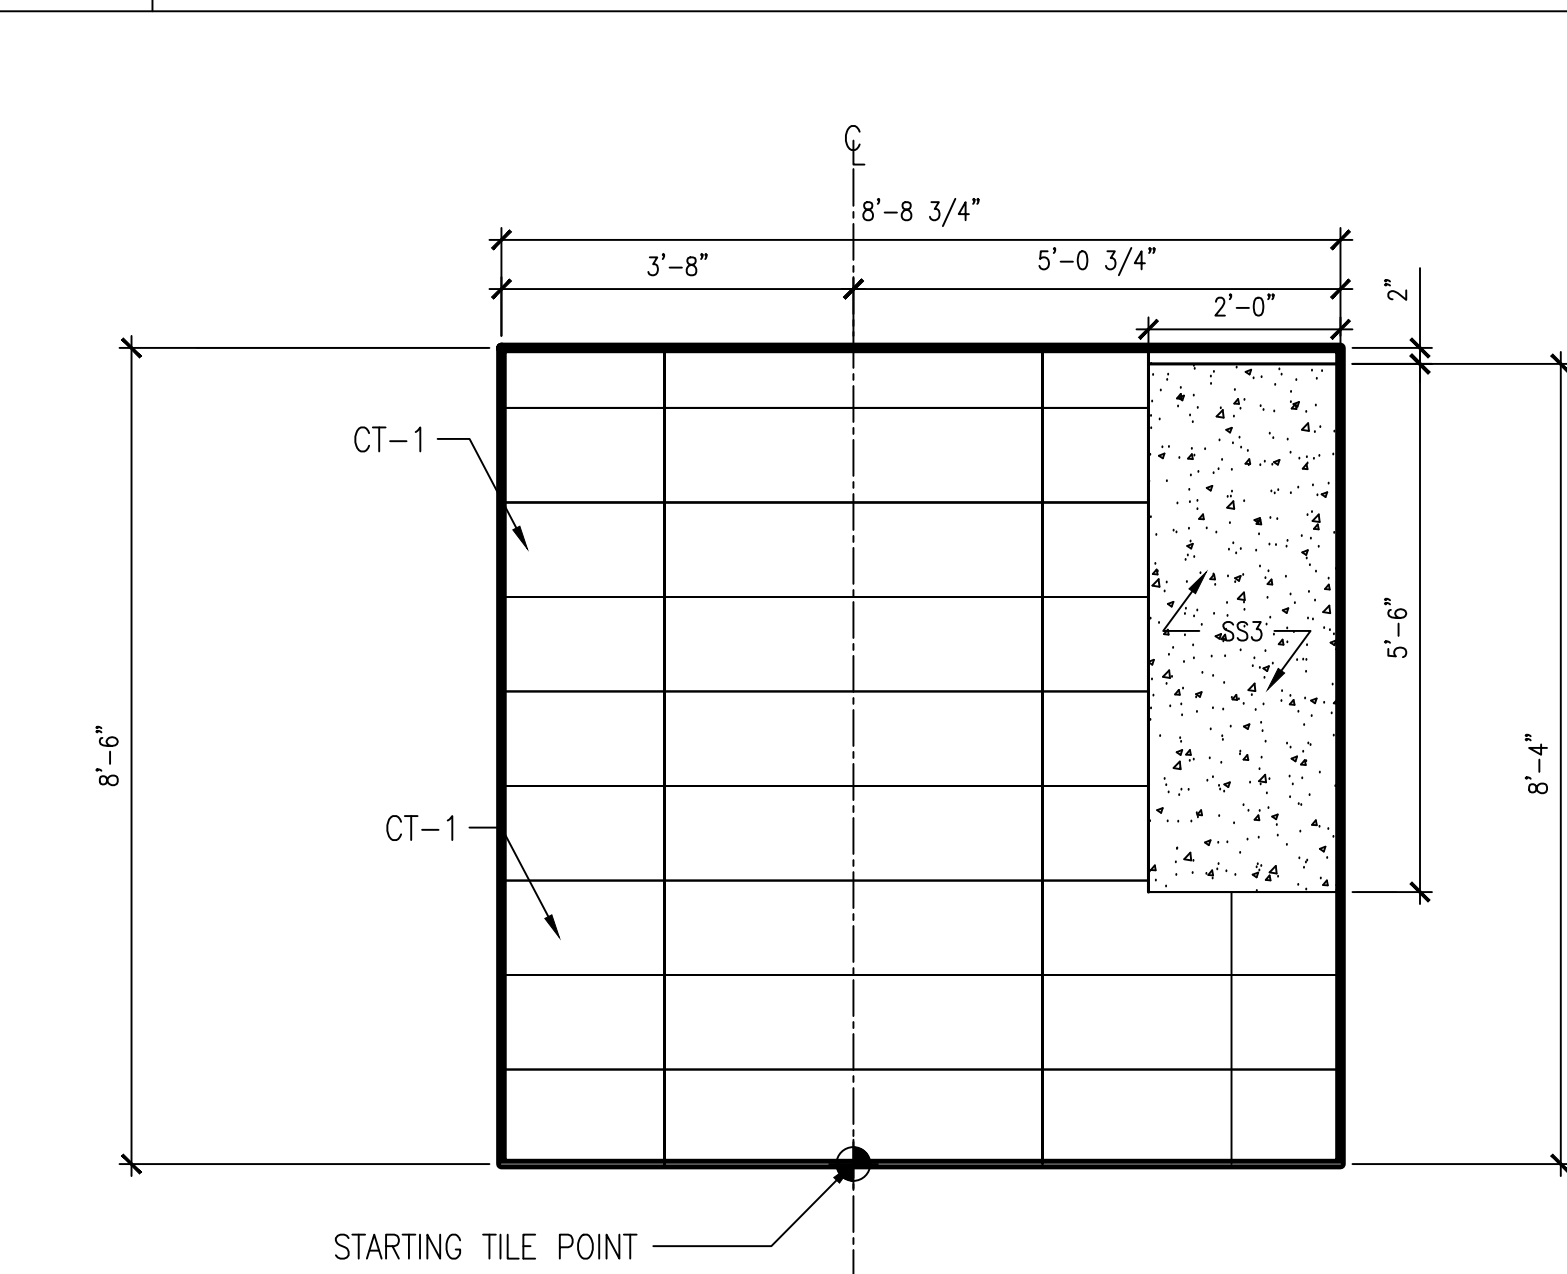


06
1/2"=1'-0" ELEVATION: WEST

 


07
1/2"=1'-0" ELEVATIONS: WEST

 

08
1/2"=1'-0" ELEVATIONS: EAST

 

09
1/2"=1'-0" ELEVATIONS: WEST

 

AUSTRO TILE & STONE, LLC
30-25 93RD STREET
EAST ELMHURST, NY 11369

CONTRACTOR
JRM CONSTRUCTION
MANAGEMENT, LLC
242 WEST 36TH STREET
11TH FLOOR
NEW YORK, NY 10018

INTERIOR DESIGNER

ISSUE FOR APPROVAL
09/30/24

ISSUE NAME
DATE




PROJECT

SDGI
200 WEST 41ST STREET
NEW YORK, NY 10036
PHONE: 212-704-0734

PROJECT NAME
EKIMETRICS
120 BROADWAY
NEW YORK, NY 10271

SHEET NAME
PLAN/ELEVATIONS
BATHROOMS




DATE:
PROJECT NO.:
PRINCIPAL:
DRAWING BY:
CHECKED BY:
SCALE:
DWG No.:
T-101
5 of 15

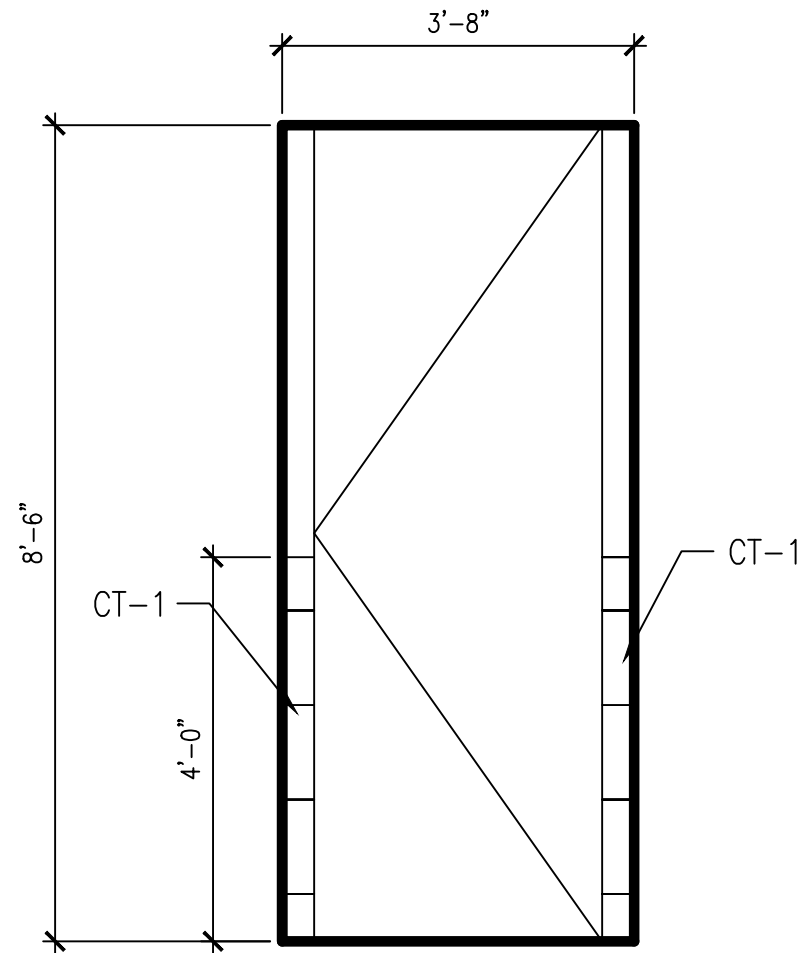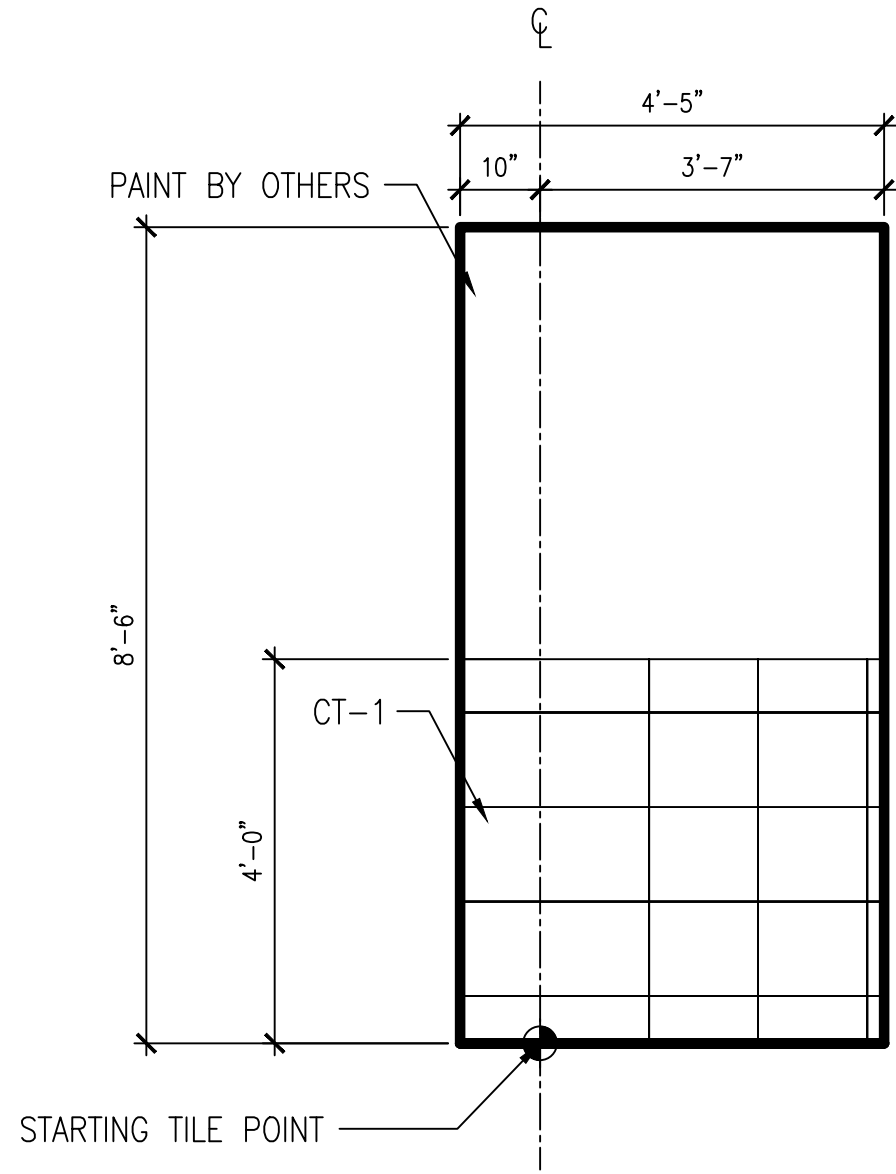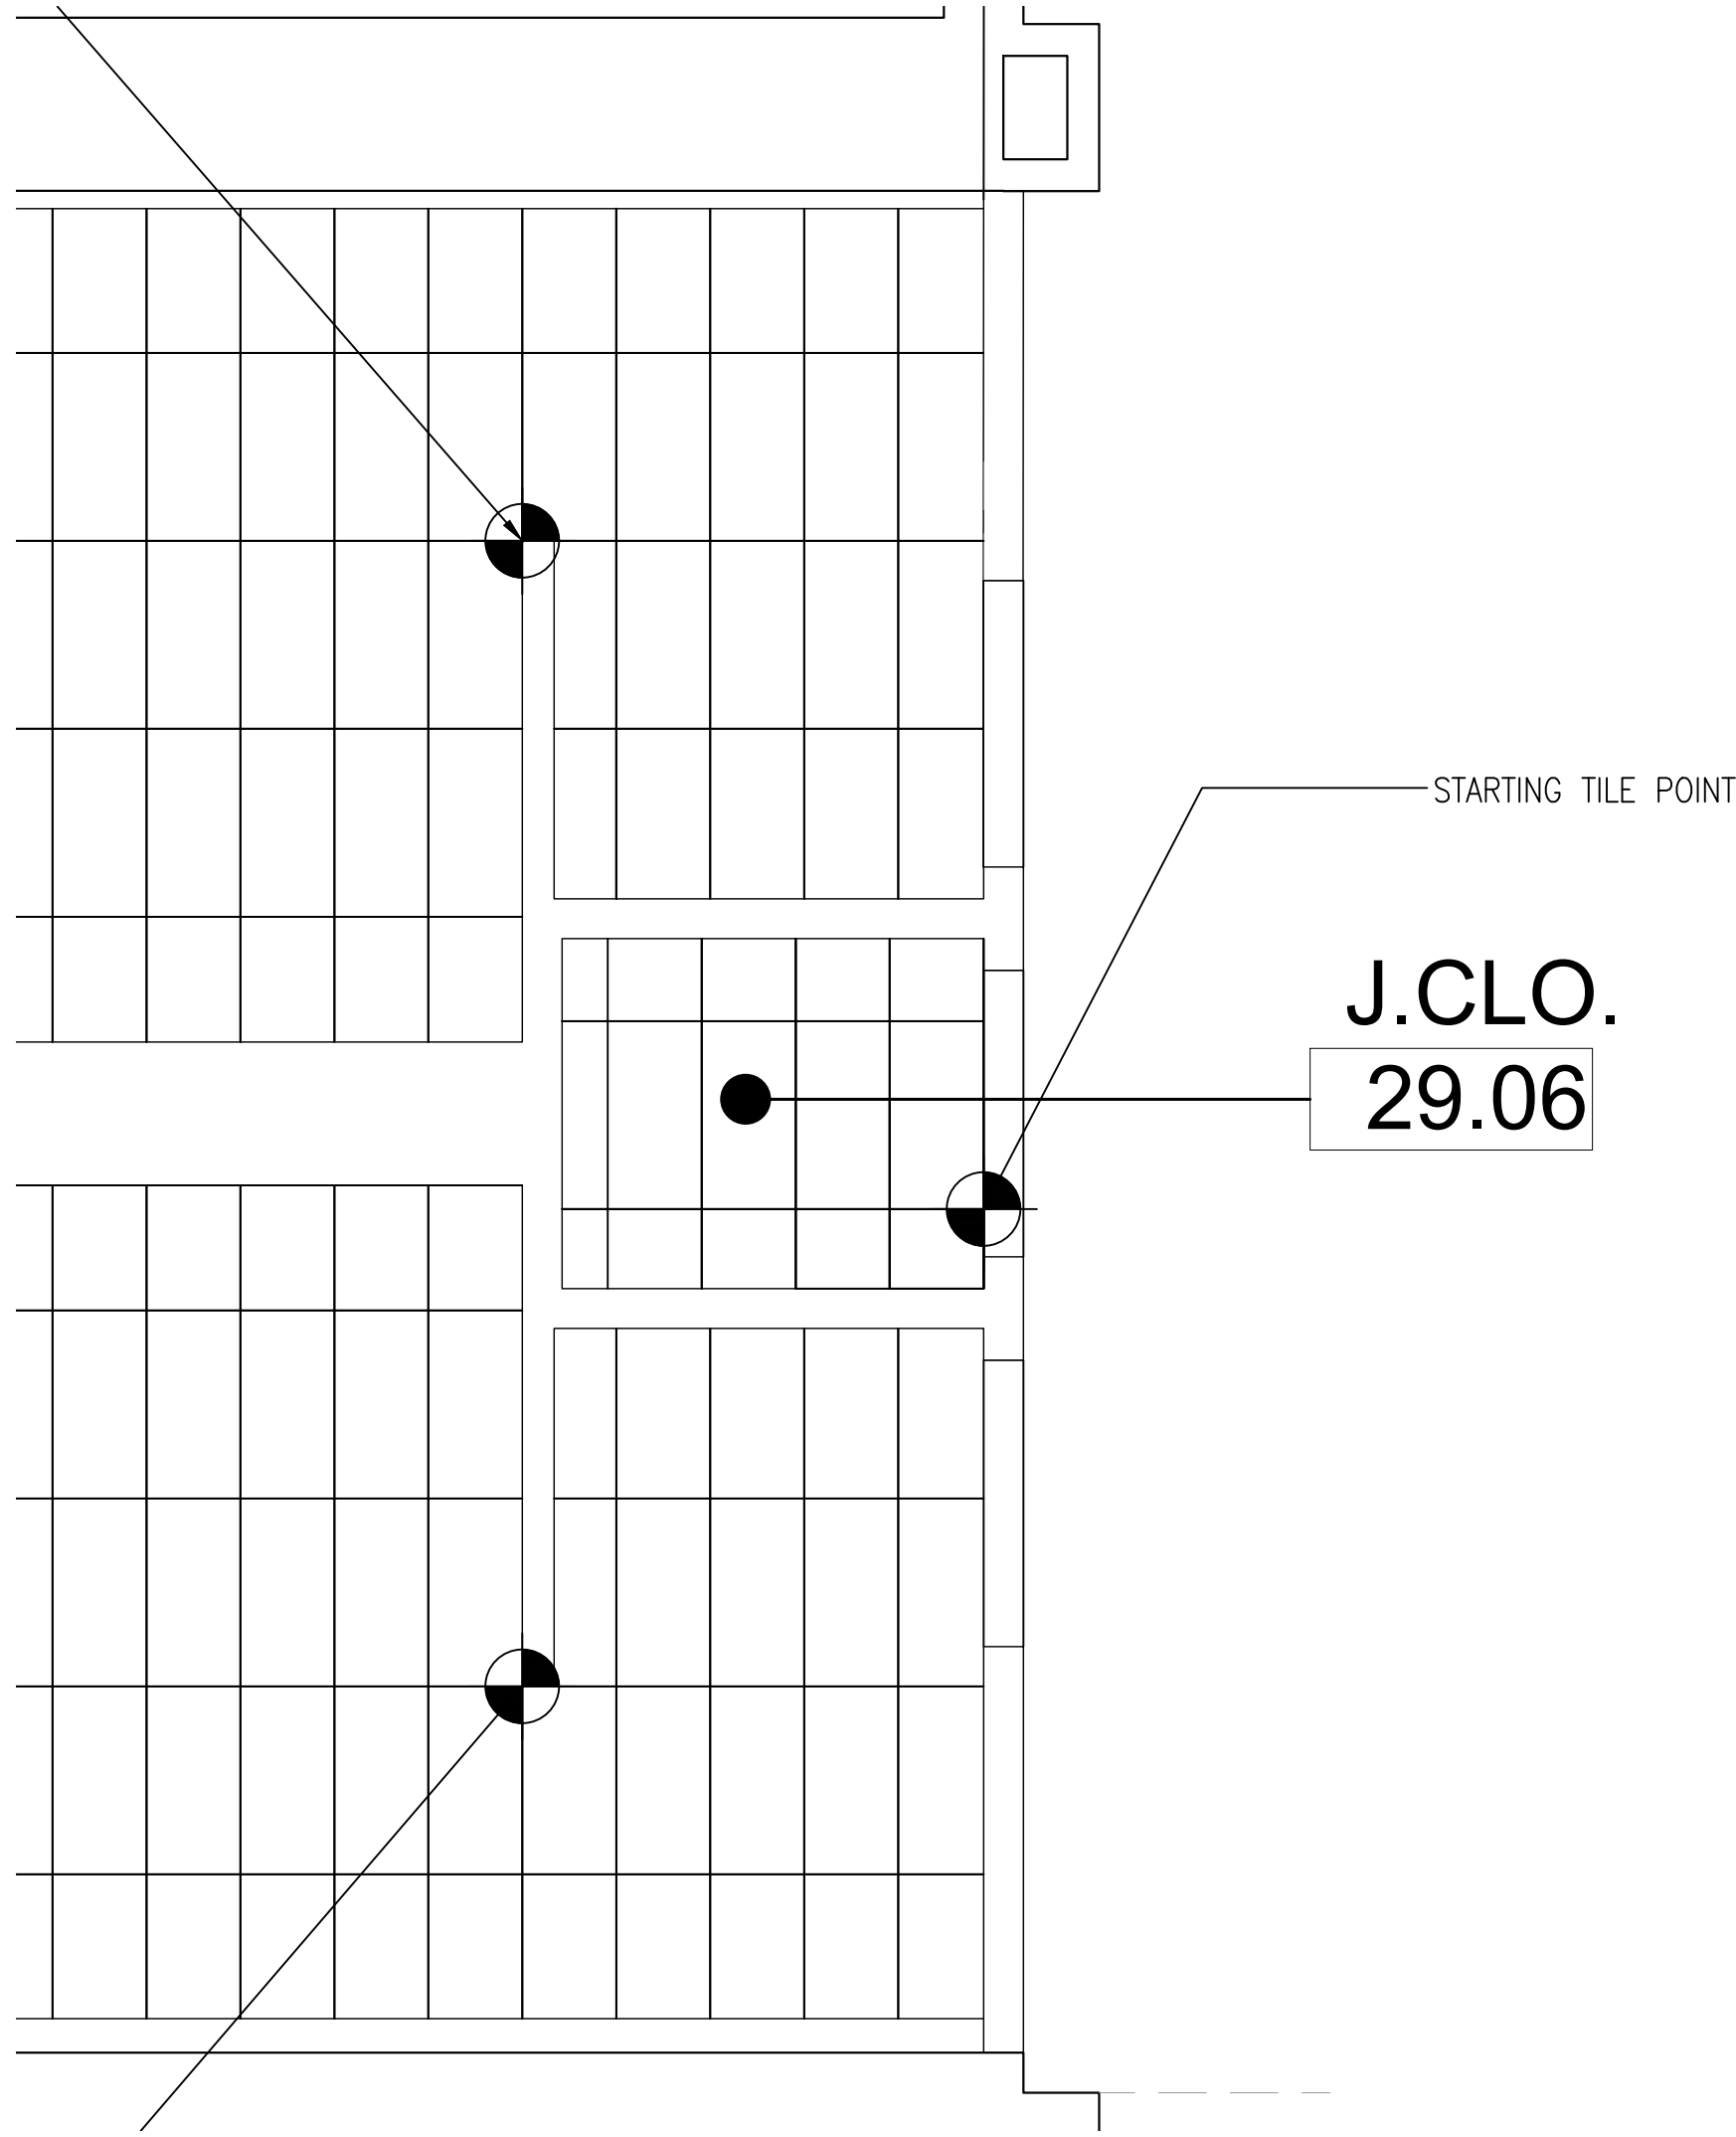

01 PLAN: JANITOR'S CLOSET (29.06)

03 ELEVATION: NORTH

04 ELEVATION: EAST

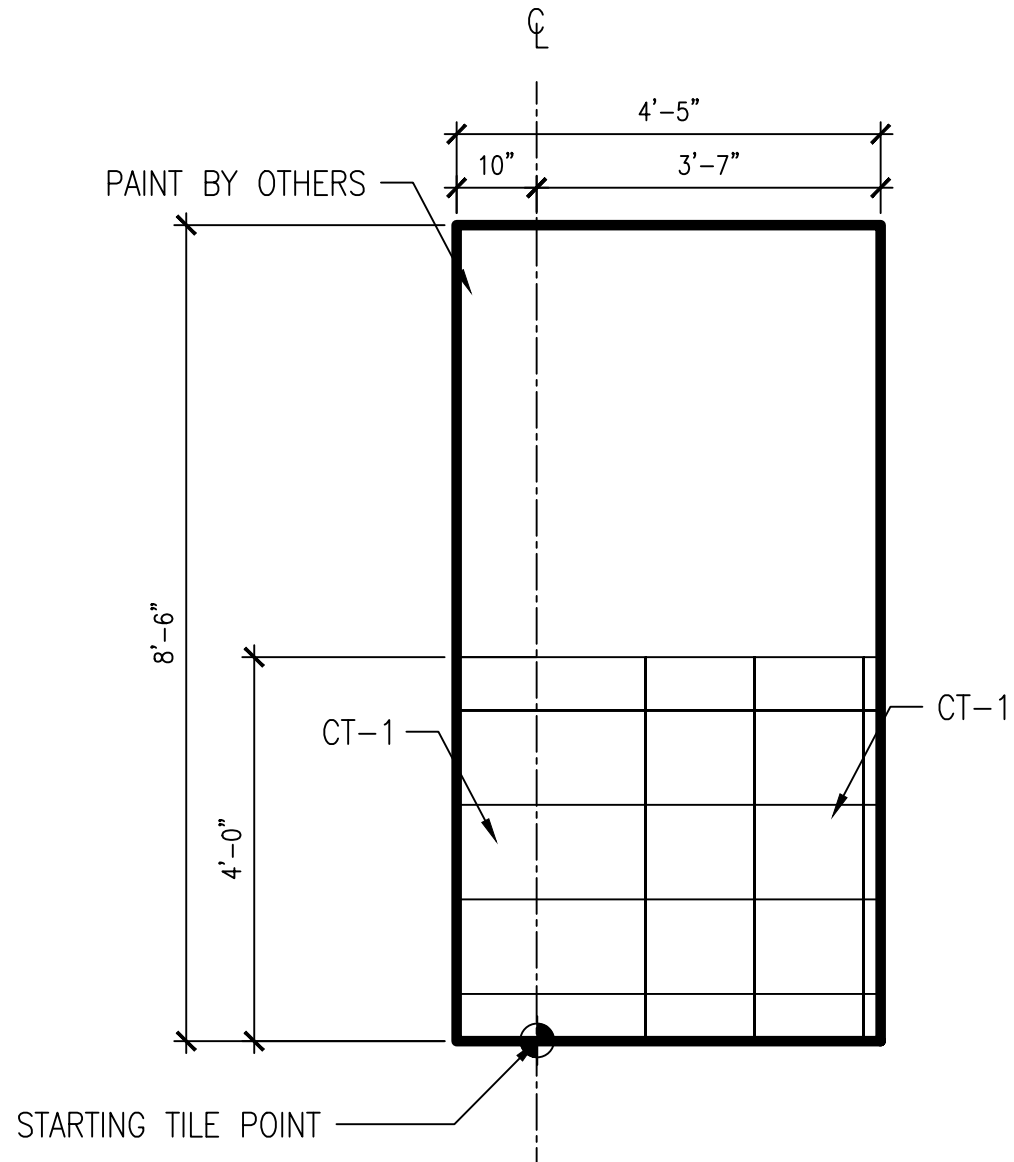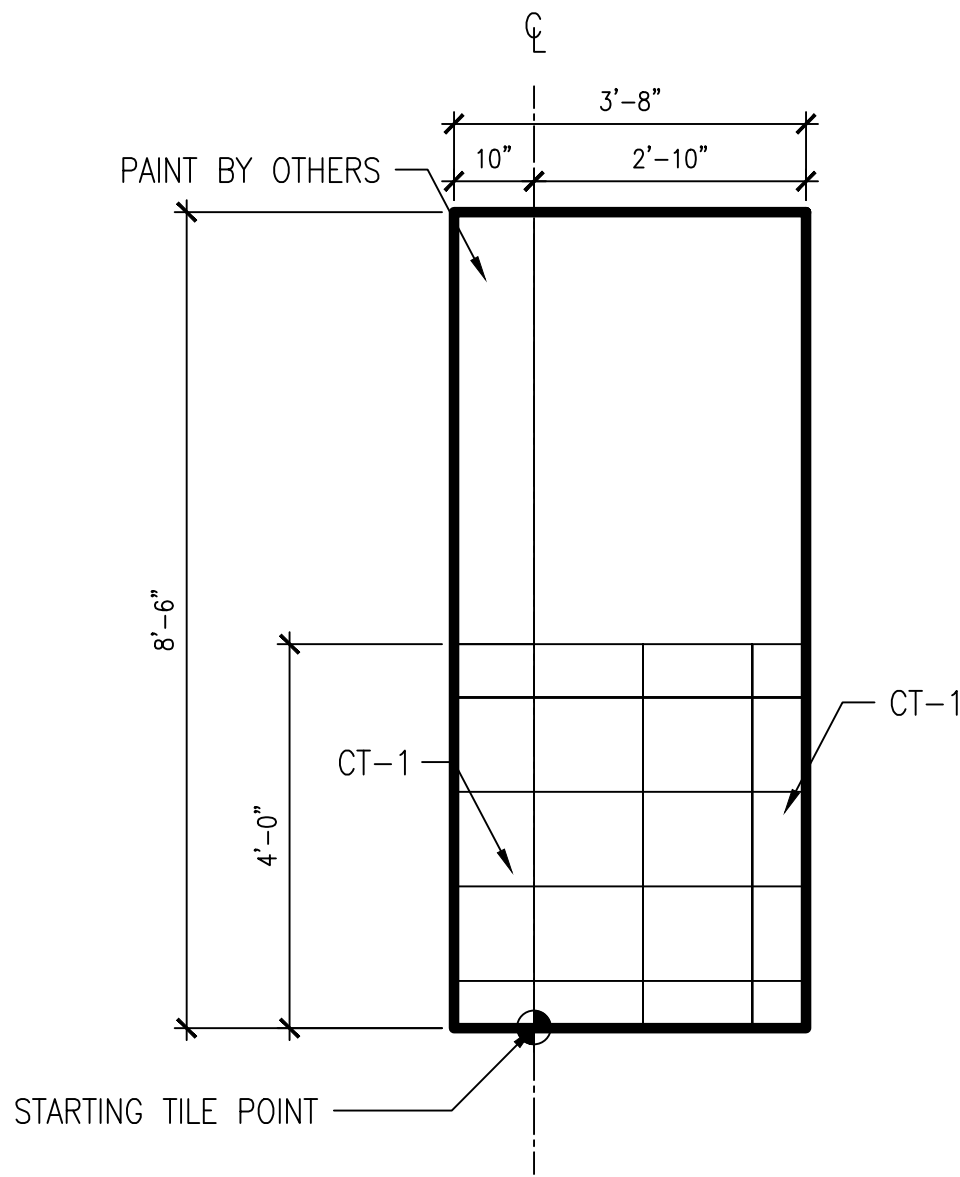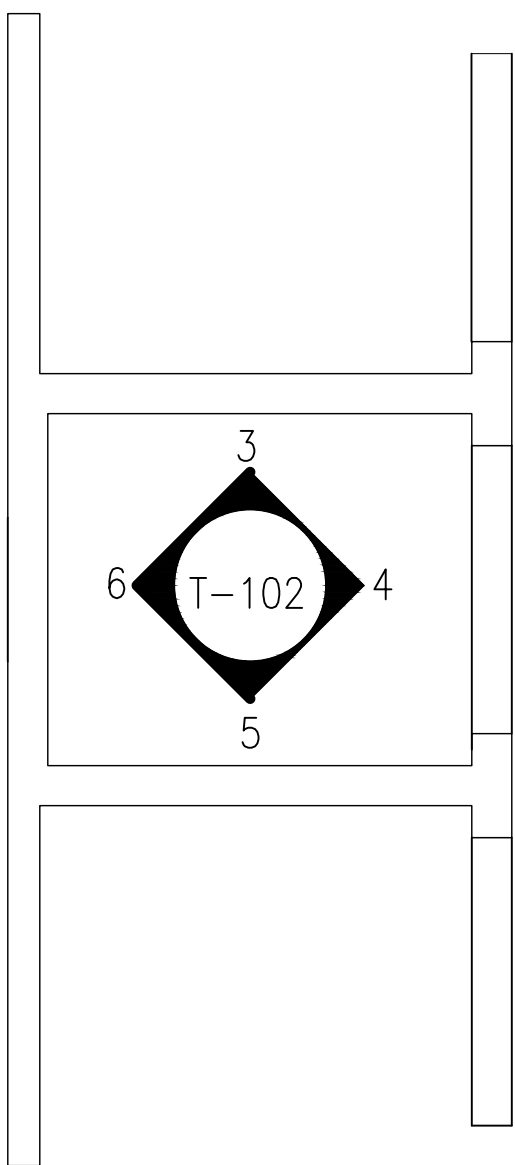

02 JANITOR'S CLOSET (29.06)

05 ELEVATION: SOUTH

06 ELEVATION: WEST

AUSTRO TILE & STONE, LLC
30-25 93RD STREET
EAST ELMHURST, NY 11369

CONTRACTOR: JRM CONSTRUCTION
MANAGEMENT, LLC
242 WEST 36TH STREET
11TH FLOOR
NEW YORK, NY 10018

INTERIOR DESIGNER:

ISSUE FOR APPROVAL 09/30/24
ISSUE NAME DATE

PROJECT: SDGI
200 WEST 41ST STREET
NEW YORK, NY 10036
PHONE: 212-704-0734



PROJECT NAME: EKIMETRICS
120 BROADWAY
NEW YORK, NY 10271

SHEET NAME: PLAN/ELEVATIONS
JANITOR'S CLOSET


DATE:
PROJECT NO.:
PRINCIPAL:
DRAWING BY:
CHECKED BY:
SCALE:
DWG No.:
T-102
6 of 15




PANTRY
29.26

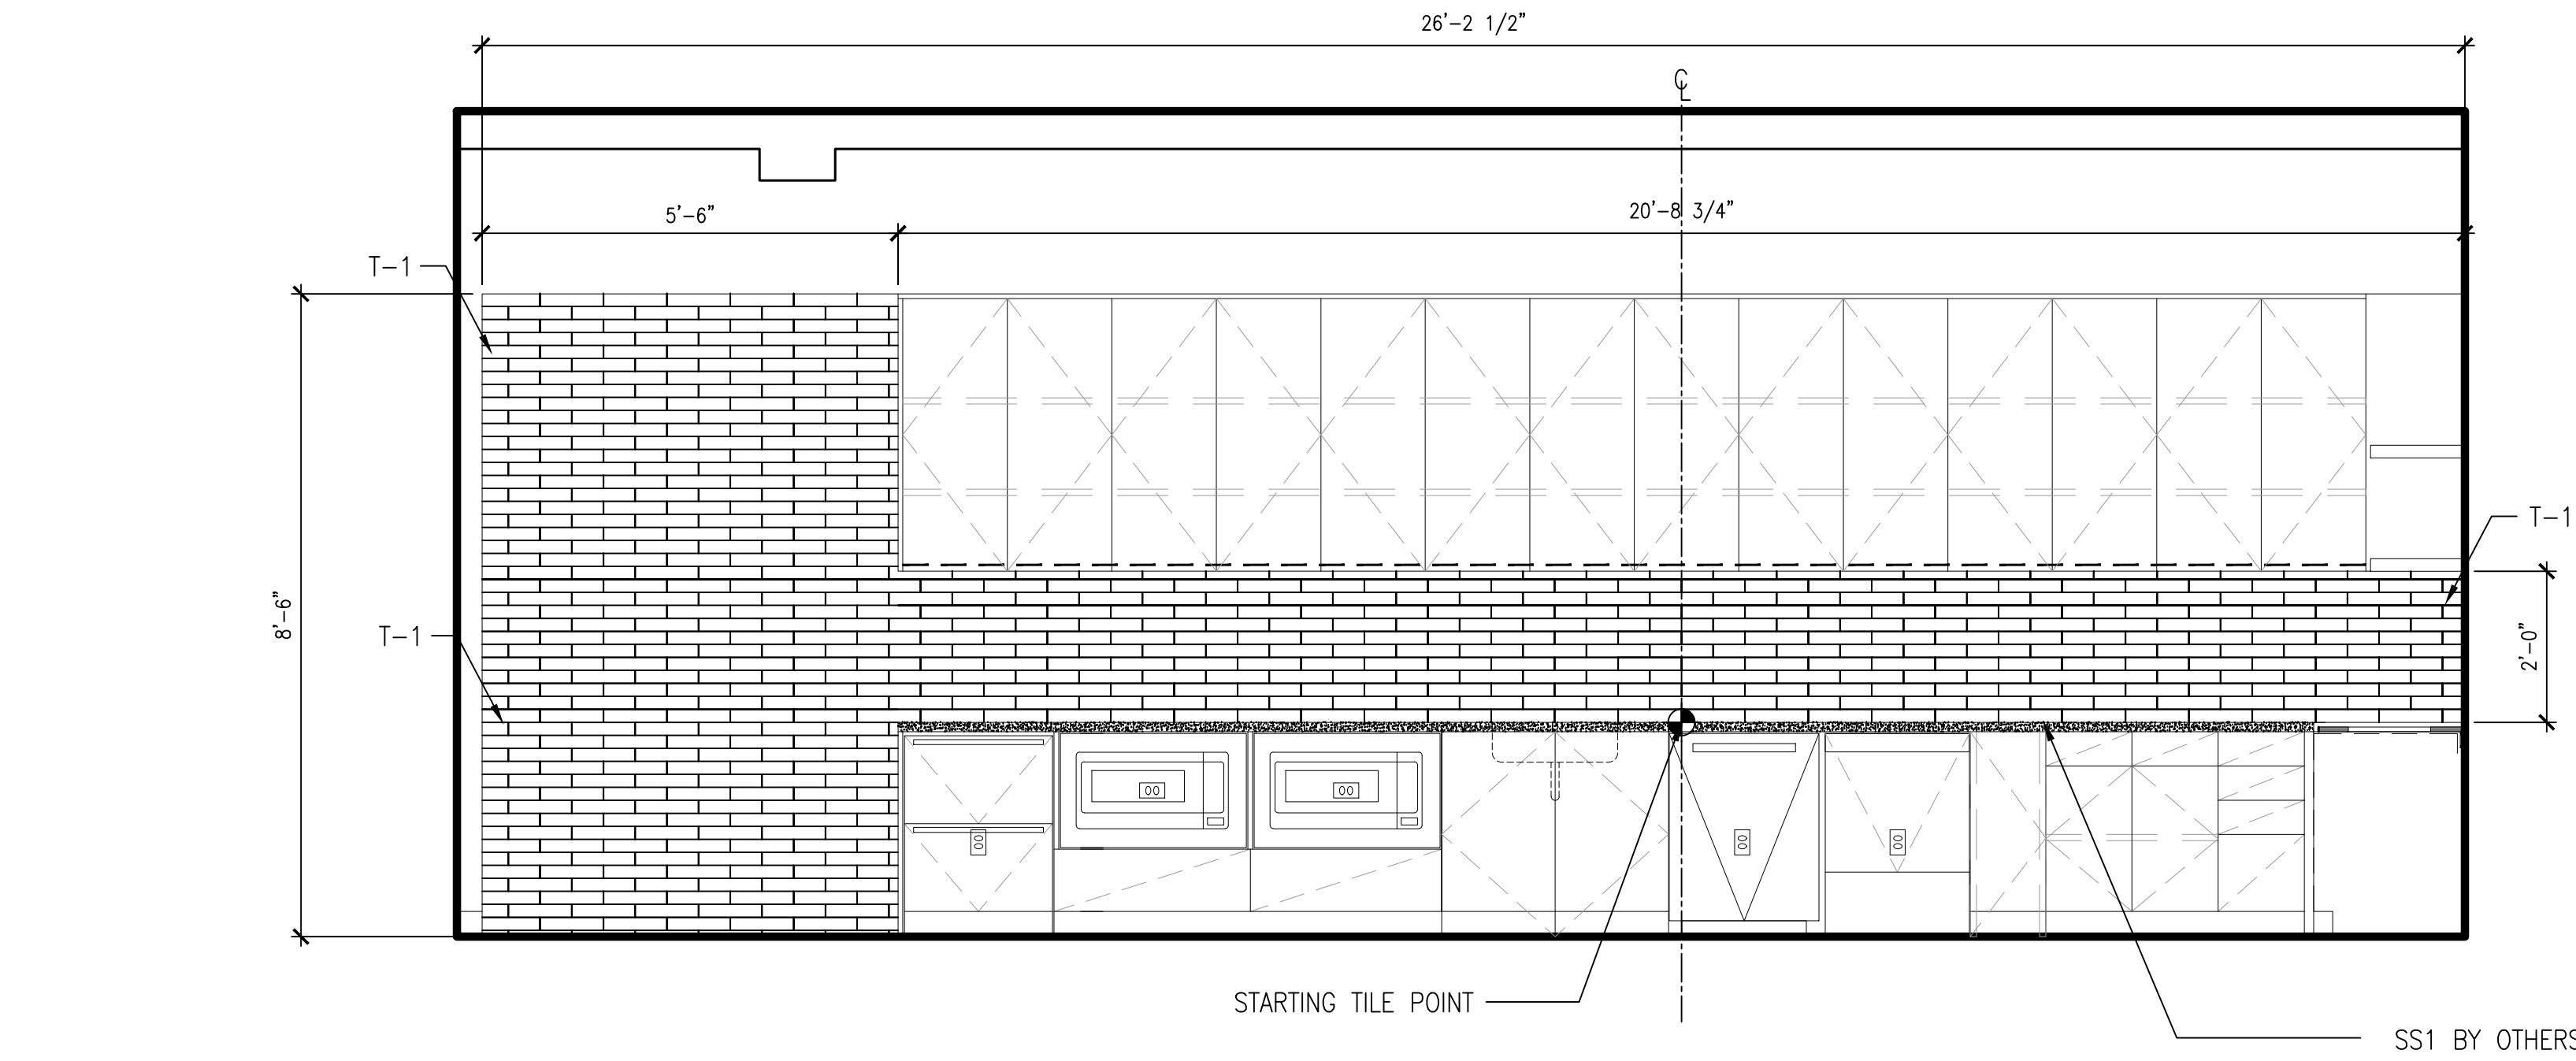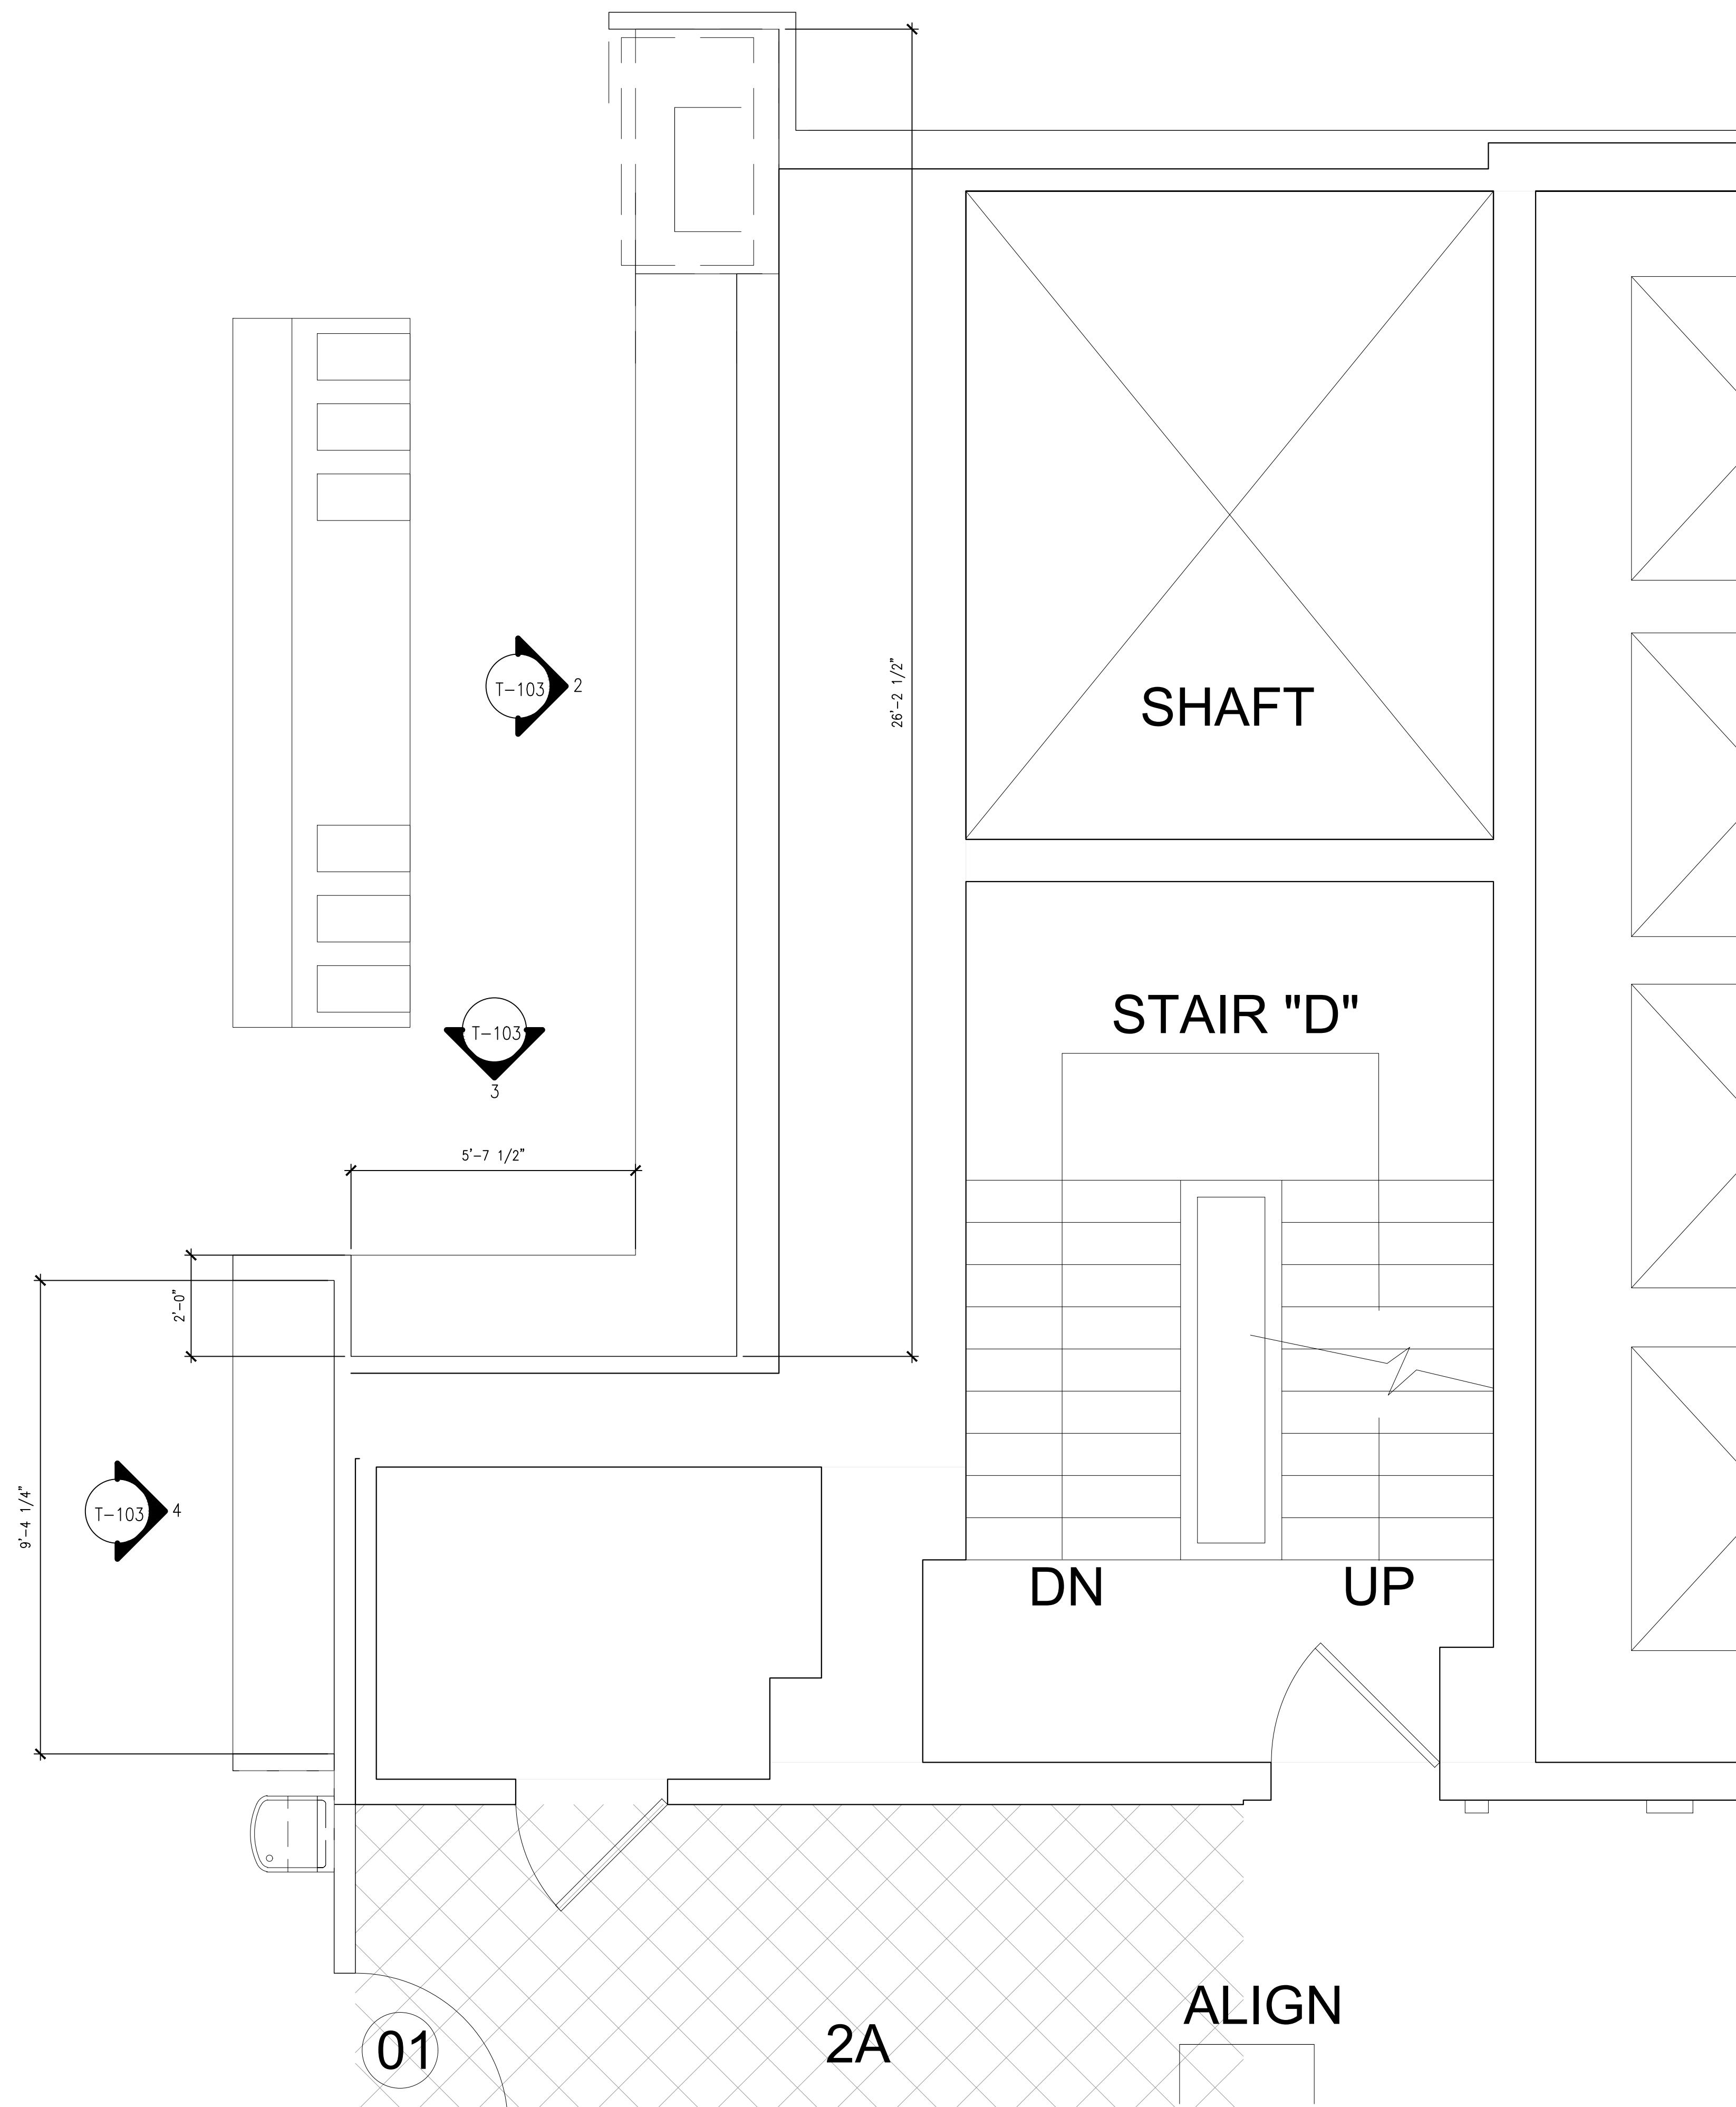

02
1/2"=1'-0" ELEVATION: EAST

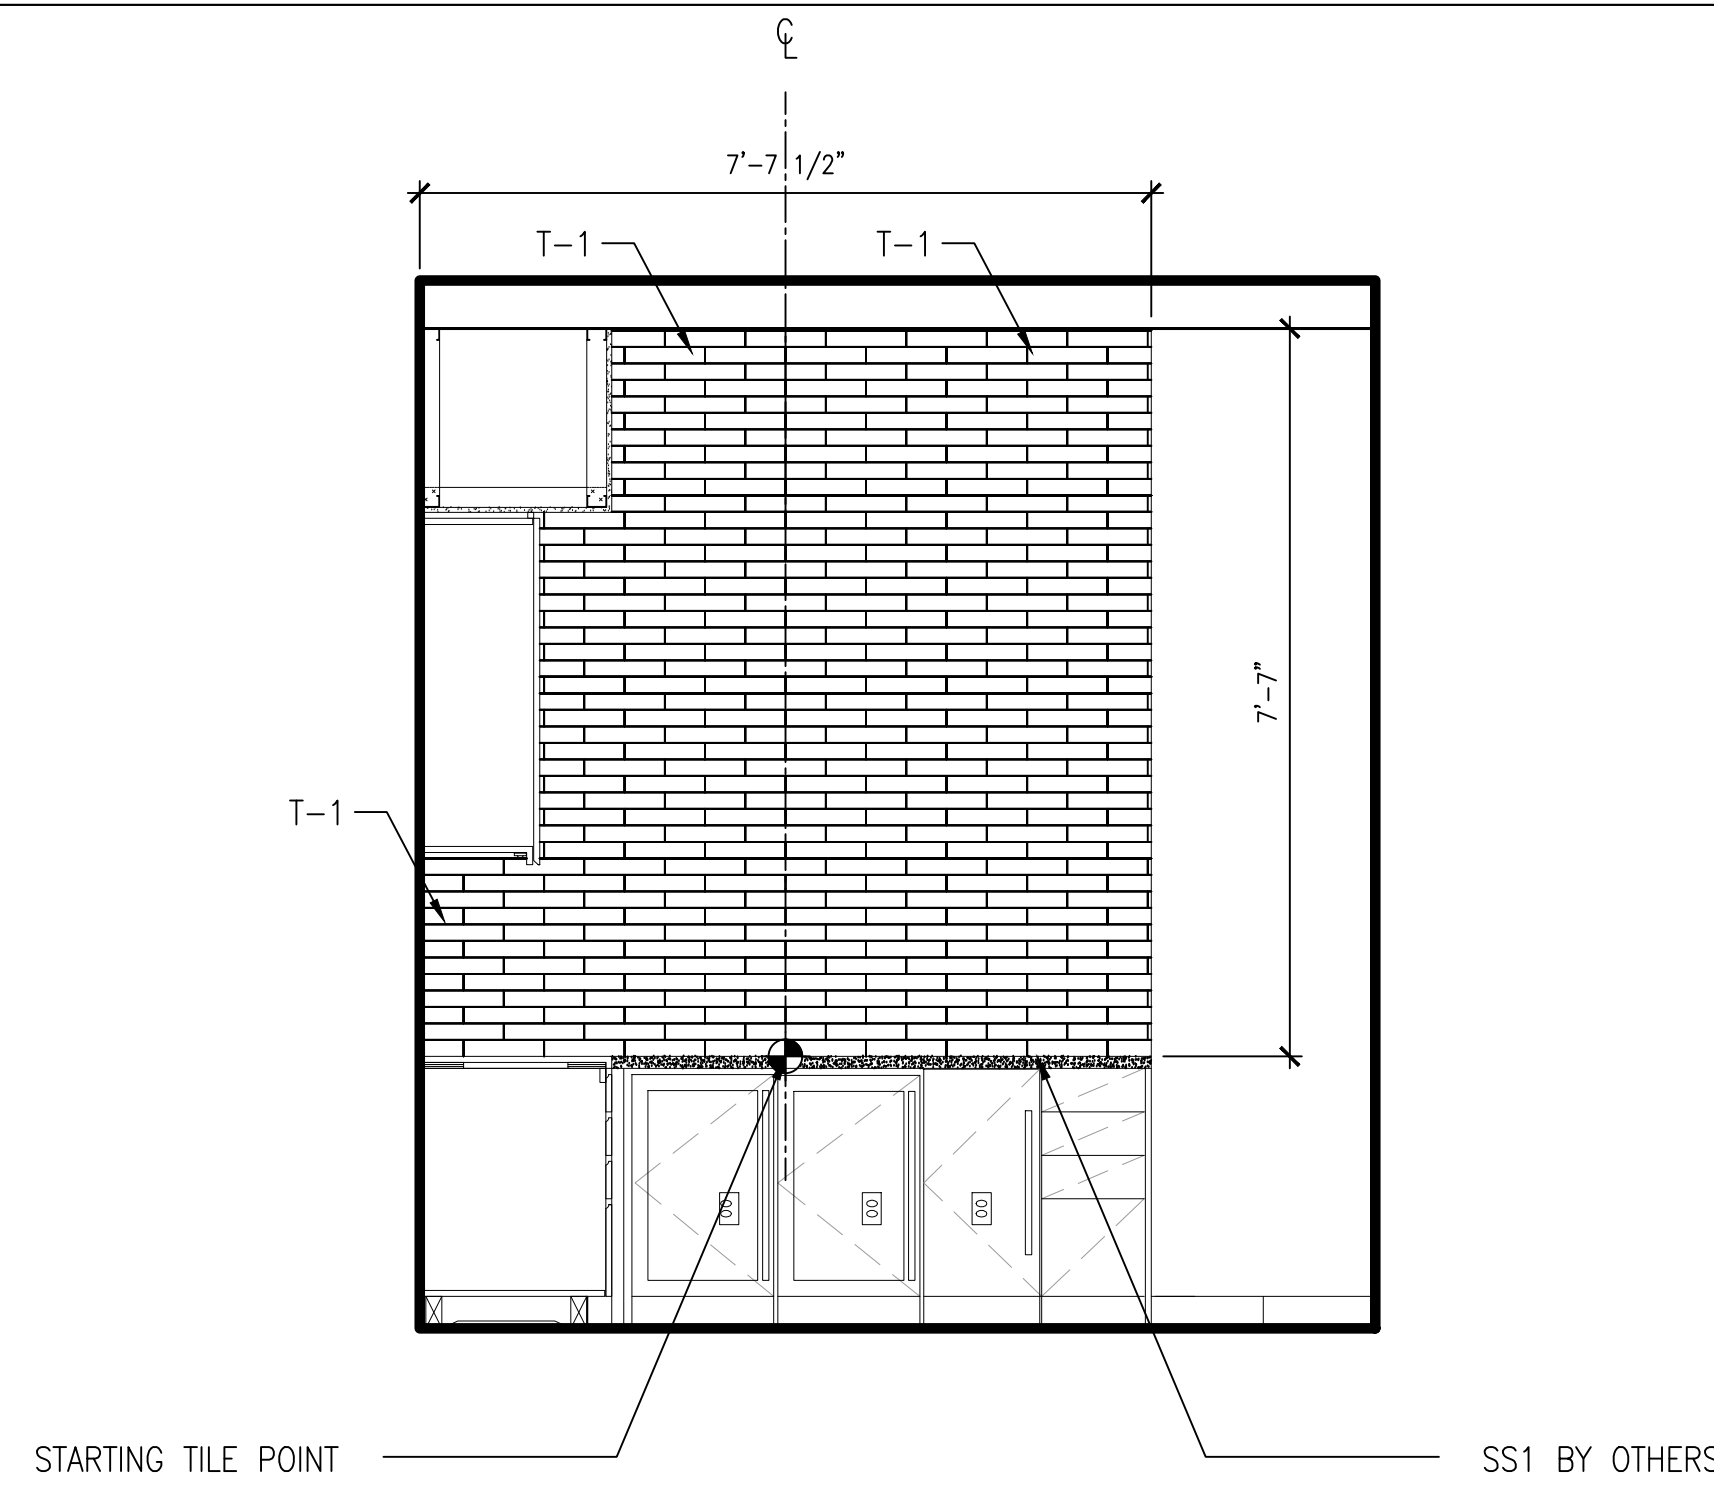

03
1/2"=1'-0" ELEVATION: SOUTH

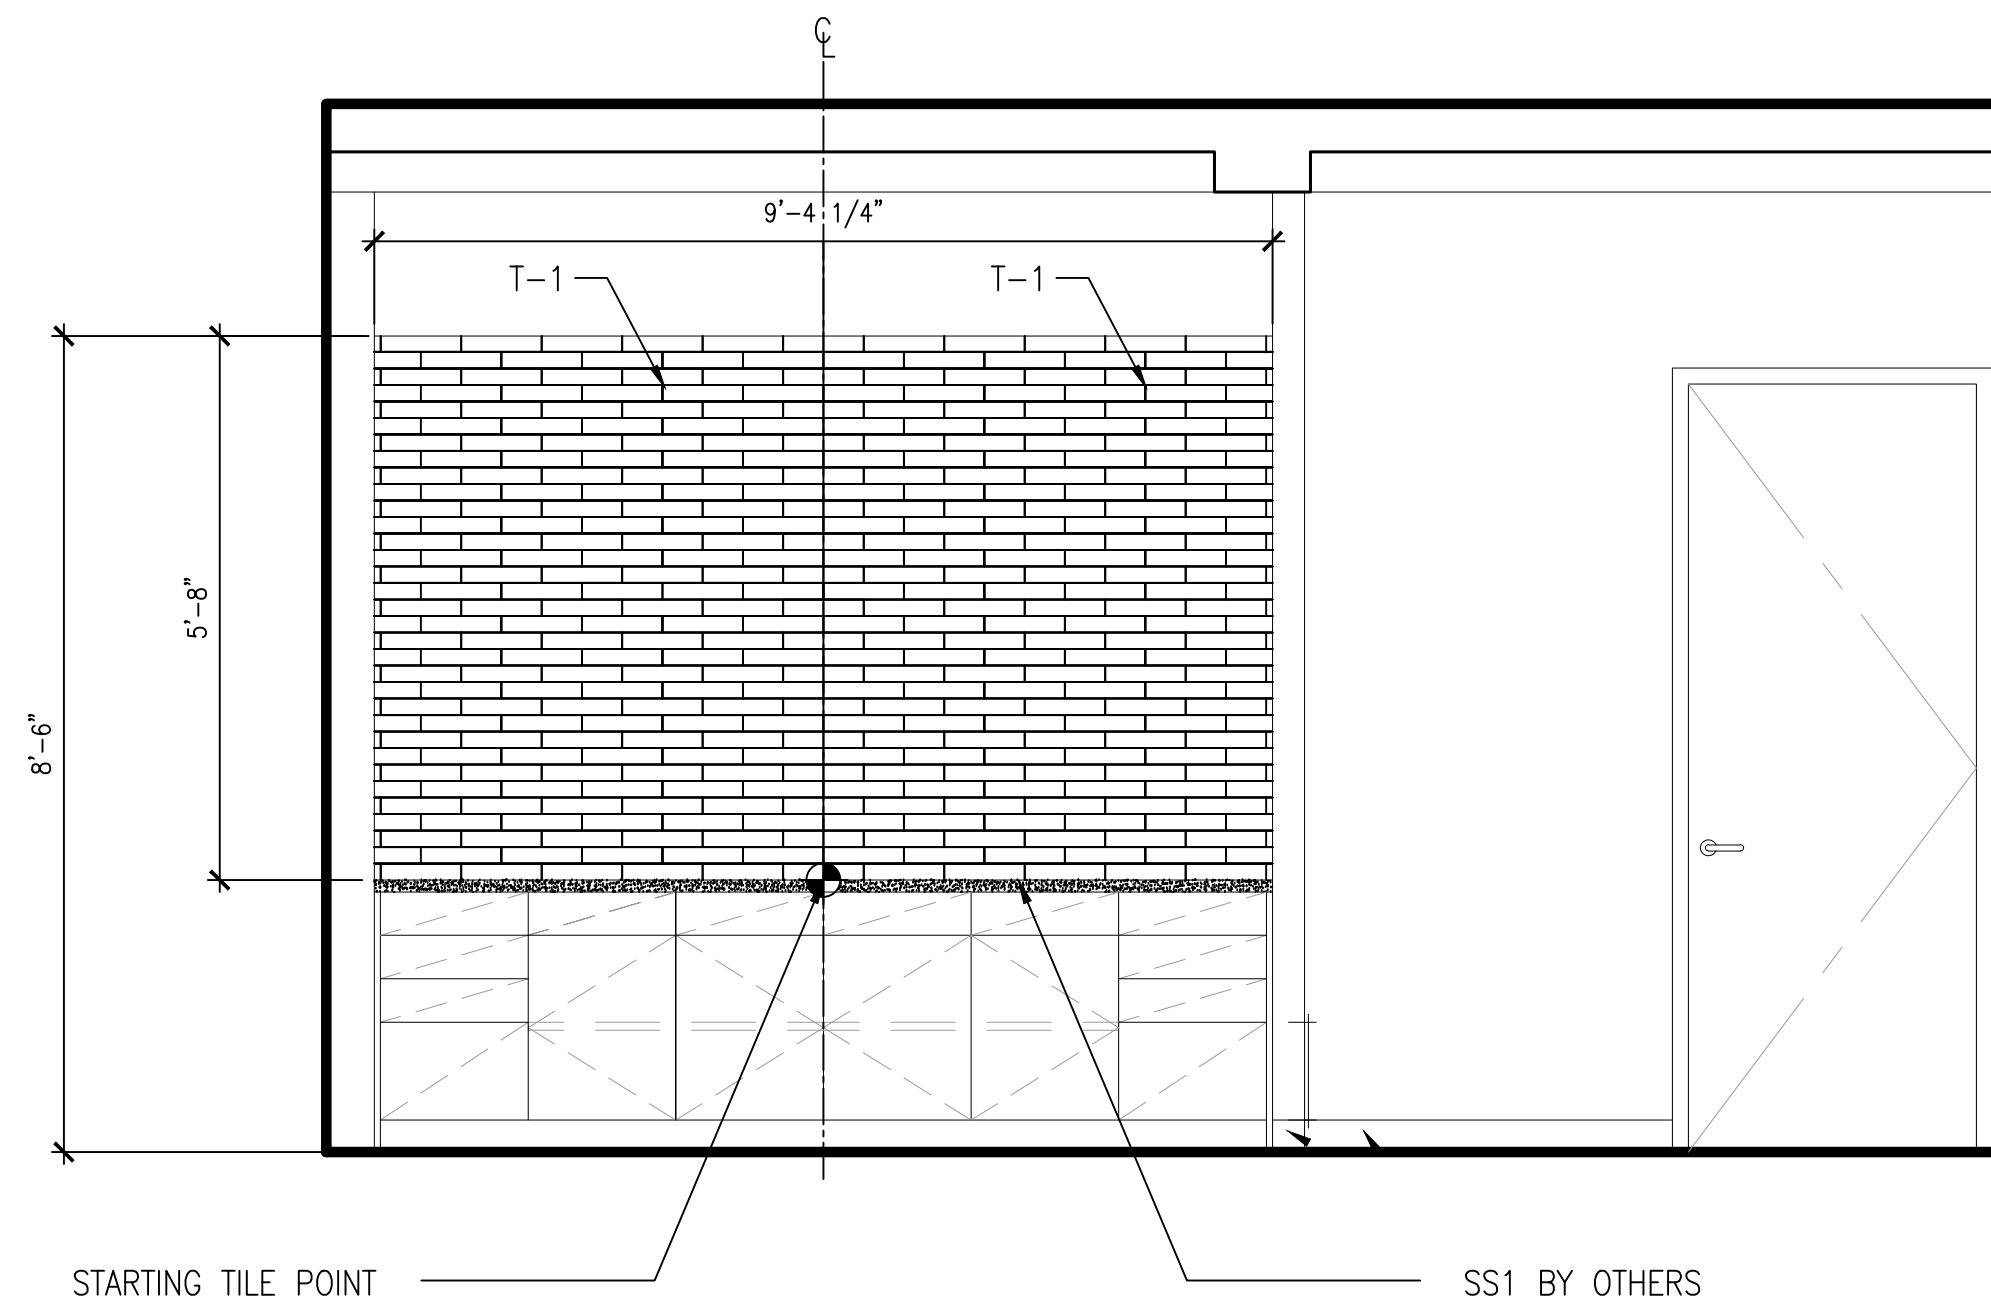

04
1/2"=1'-0" ELEVATION: EAST

AUSTRO TILE & STONE, LLC
30-25 93RD STREET
EAST ELMHURST, NY 11369

CONTRACTOR:
JRM CONSTRUCTION
MANAGEMENT, LLC
242 WEST 36TH STREET
11TH FLOOR
NEW YORK, NY 10018

INTERIOR DESIGNER:


ISSUE FOR APPROVAL 09/30/24
ISSUE NAME DATE

PROJECT:
SDGI
200 WEST 41ST STREET
NEW YORK, NY 10036
PHONE: 212-704-0734


PROJECT NAME:
EKIMETRICS
120 BROADWAY
NEW YORK, NY 10271

SHEET NAME:
PLAN/ELEVATIONS
PANTRY

DATE:
PROJECT NO.:
PRINCIPAL:
DRAWING BY:
CHECKED BY:
SCALE:
DWG No.:
T-103
7 of 15

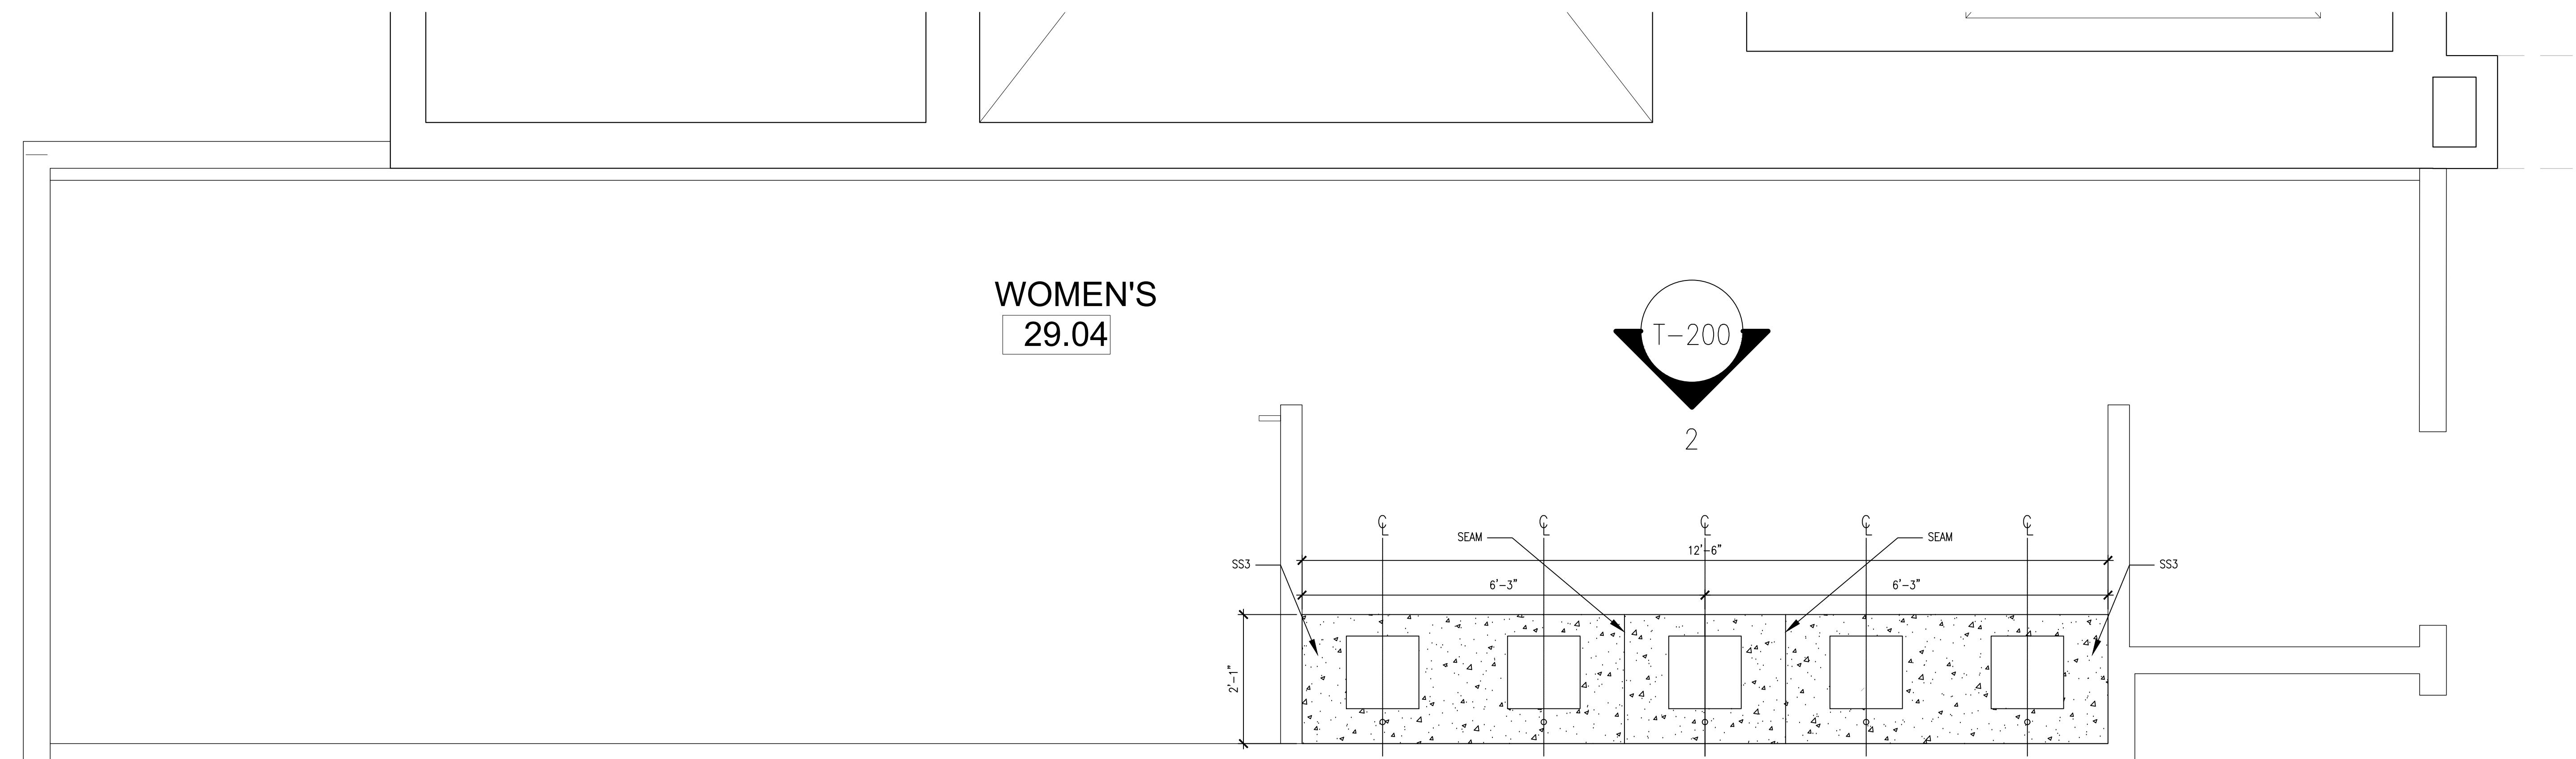

01 3/4"=1'-0"	PLAN: WOMEN'S BATHROOM (29.04)
------------------	--------------------------------

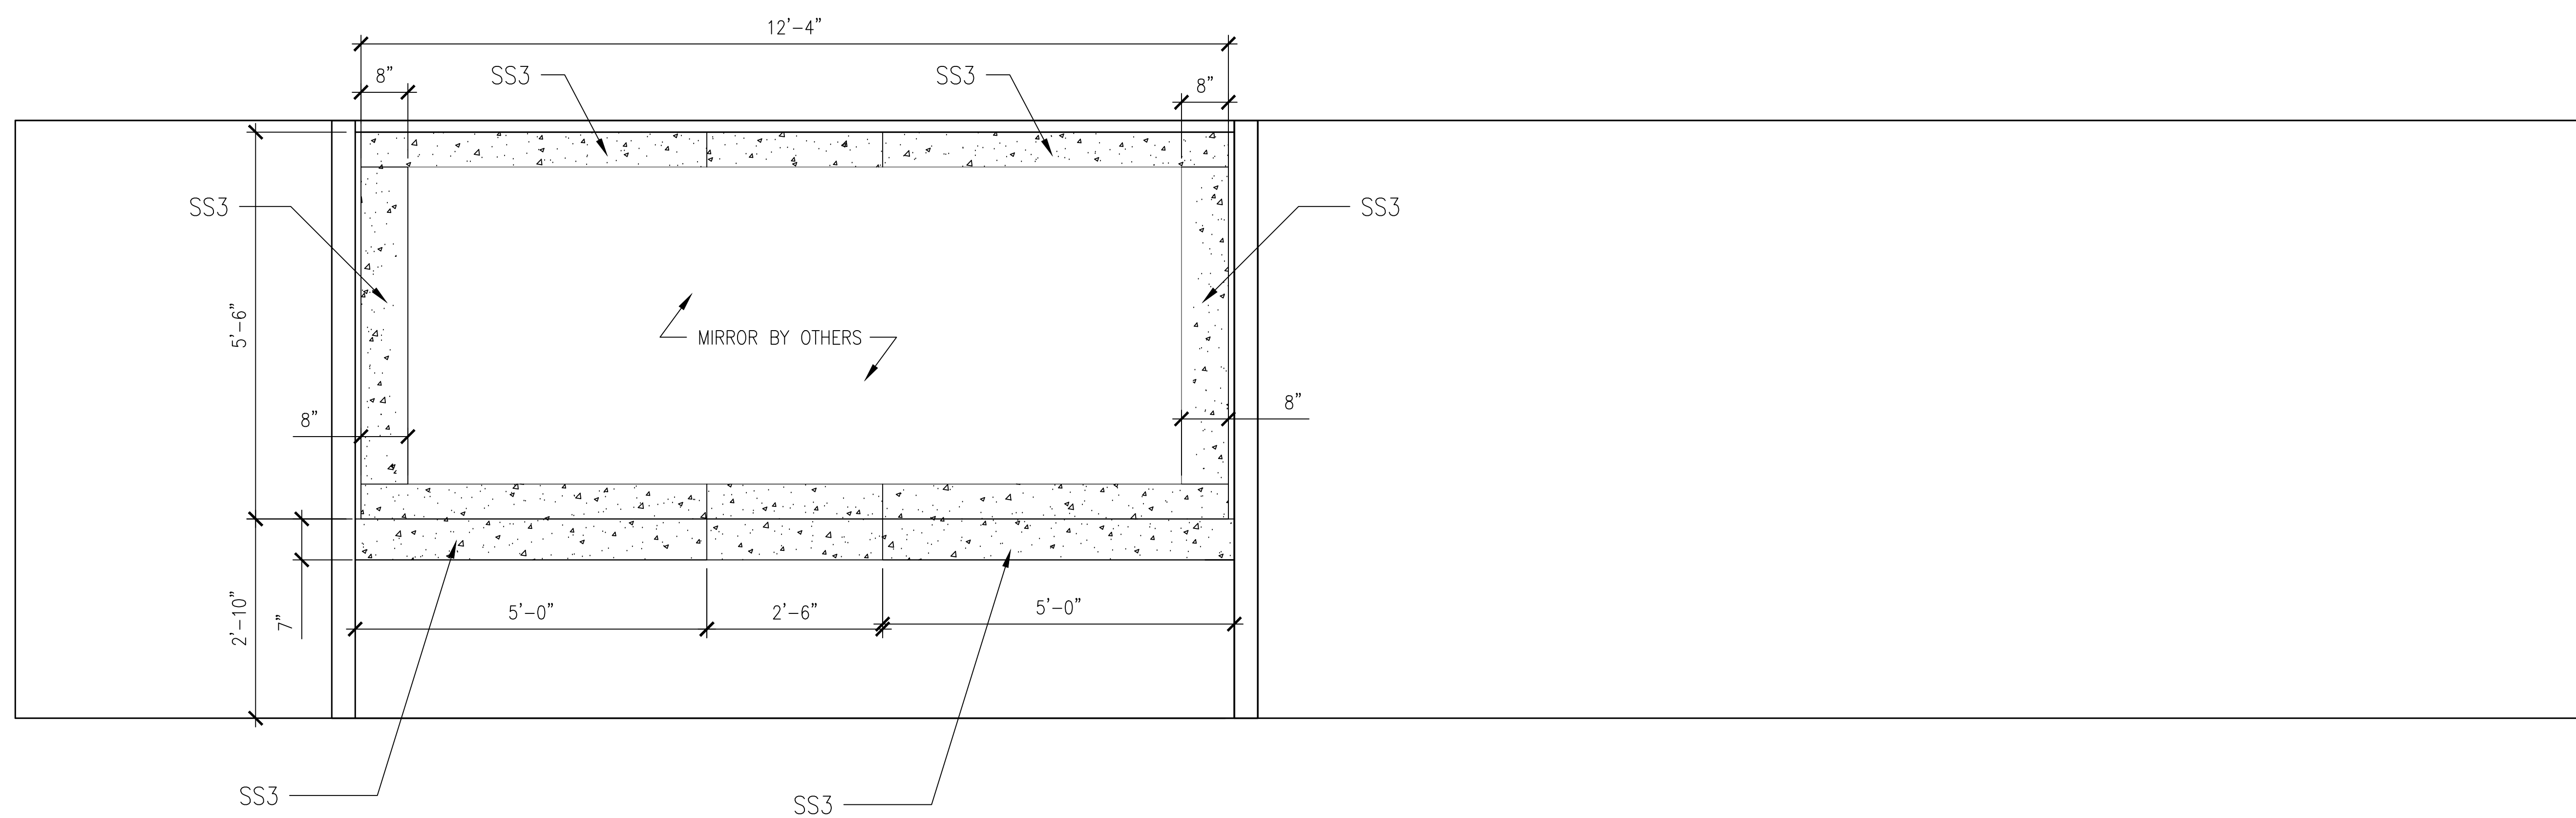

02 1/4"=1'-0"	ELEVATION: SOUTH
------------------	------------------

CONTRACTOR:
JRM CONSTRUCTION
MANAGEMENT, LLC
242 WEST 36TH STREET
11TH FLOOR
NEW YORK, NY 10018

INTERIOR DESIGNER:

[illegible]

ISSUE FOR APPROVAL	09/30/24
ISSUE NAME	DATE

ARCHITECT:

SDGI
200 WEST 41ST STREET
NEW YORK, NY 10036
PHONE: 212-704-0734


PROJECT NAME:

EKIMETRICS
120 BROADWAY
NEW YORK, NY 10271

SHEET NAME:

STONE COUNTERTOPS


DATE: _____
PROJECT NO.: _____
PRINCIPAL: _____
DRAWING BY: _____
CHECKED BY: _____
SCALE: _____
DWG No.: _____
T-200
8 of 15

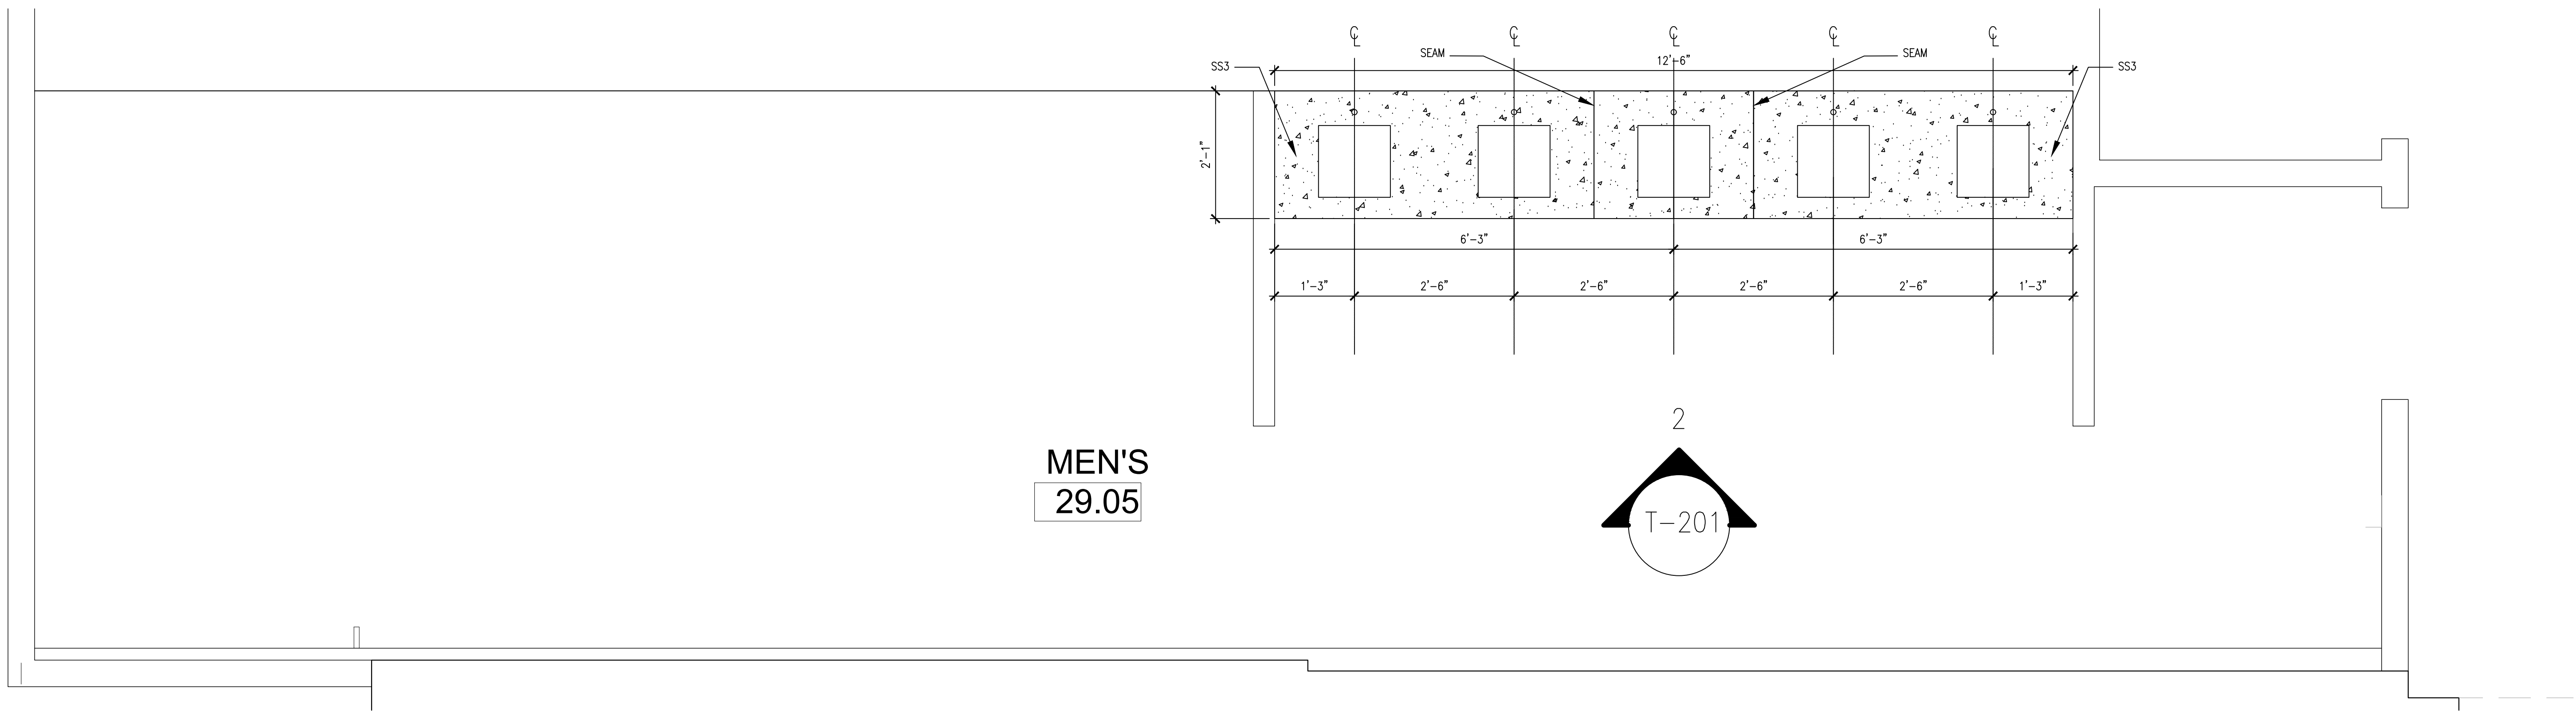

MEN'S
29.05

2
T-201

01
3/4"=1'-0" PLAN: MEN'S BATHROOM (29.05)

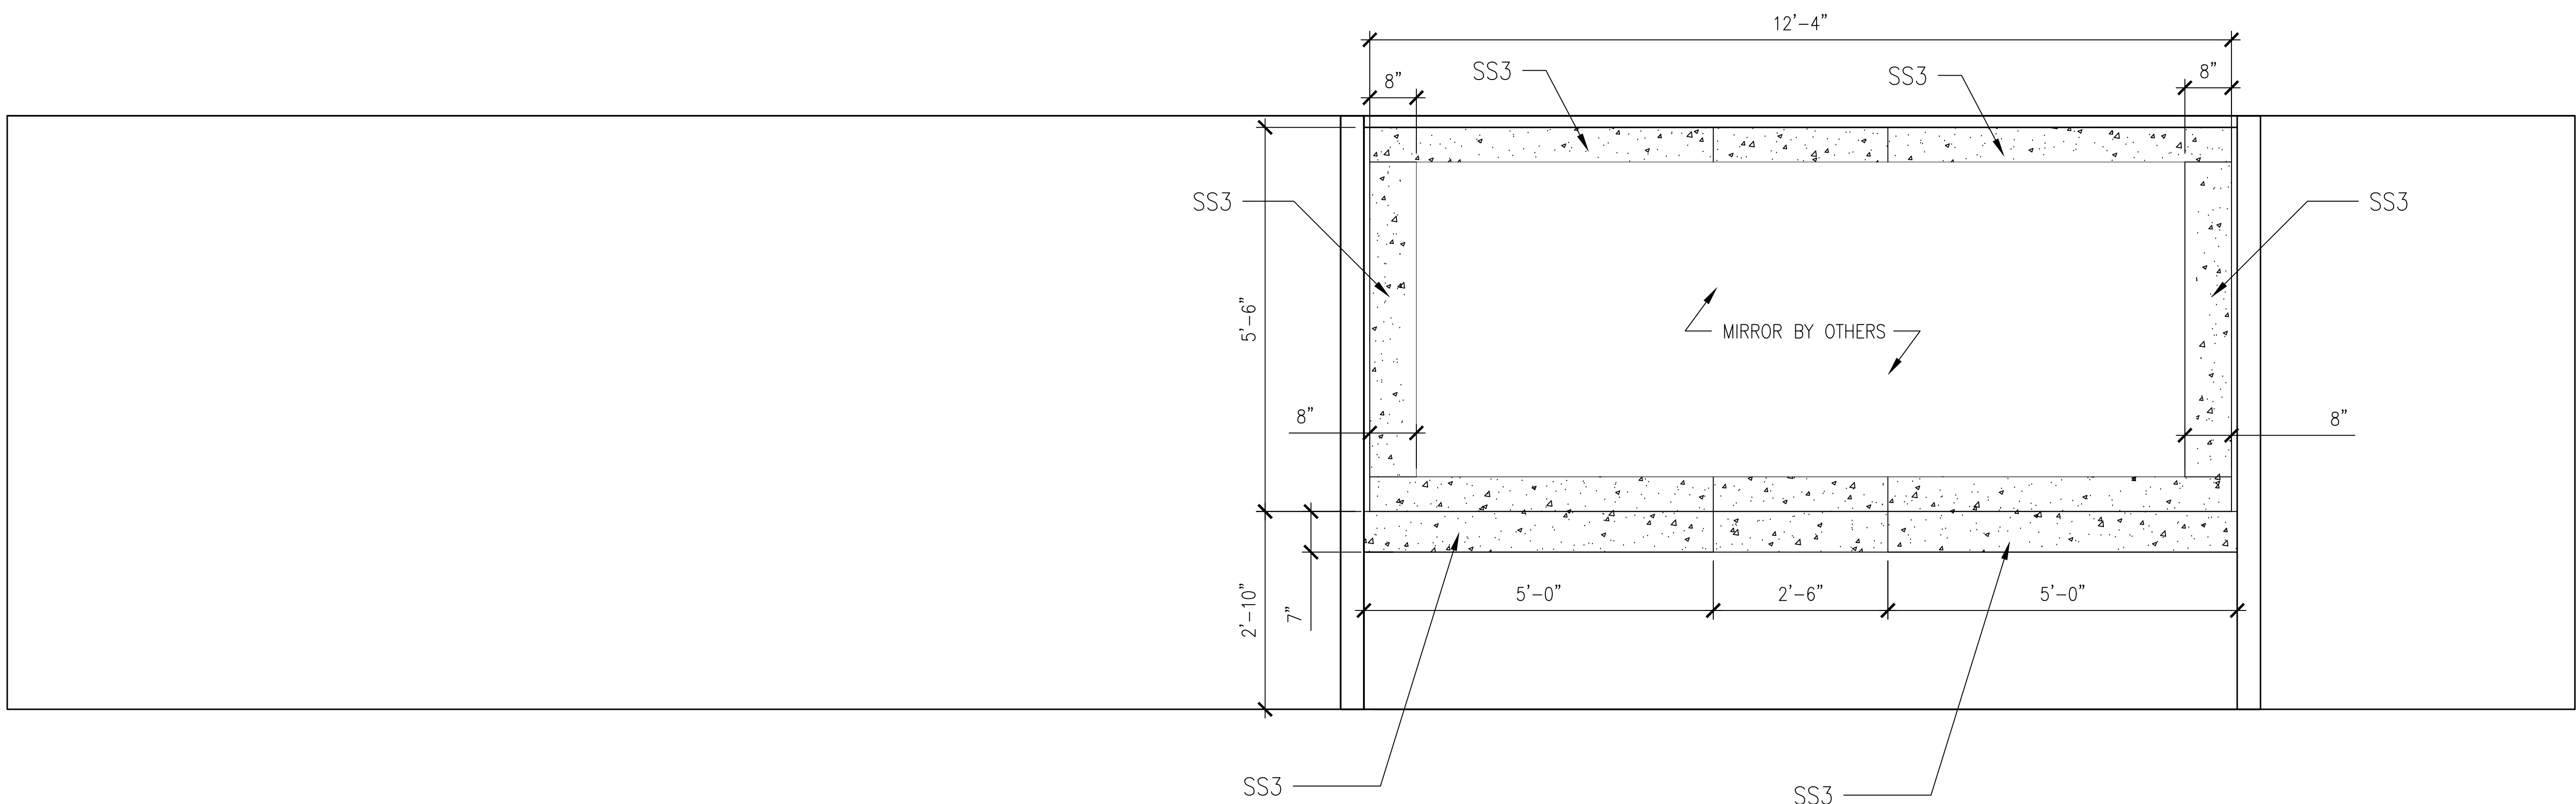

02
3/4"=1'-0" ELEVATION: SOUTH

AUSTRO TILE & STONE, LLC
30-25 93RD STREET
EAST ELMHURST, NY 11369

CONTRACTOR:
JRM CONSTRUCTION
MANAGEMENT, LLC
242 WEST 36TH STREET
11TH FLOOR
NEW YORK, NY 10018

INTERIOR DESIGNER:

ISSUE FOR APPROVAL 09/30/24
ISSUE NAME DATE

PROJECTED:
SDGI
200 WEST 41ST STREET
NEW YORK, NY 10036
PHONE: 212-704-0734

PROJECT NAME:
EKIMETRICS
120 BROADWAY
NEW YORK, NY 10271

SHEET NAME:
STONE COUNTERTOPS

DATE:
PROJECT NO.:
PRINCIPAL:
DRAWING BY:
CHECKED BY:
SCALE:
DWG No.:
T-201
9 of 15

30-25 93RD STREET
EAST ELMHURST, NY 11369

JRM CONSTRUCTION
MANAGEMENT, LLC
242 WEST 36TH STREET
11TH FLOOR
NEW YORK, NY 10018

INTERIOR DESIGNER

[illegible]

ISSUE FOR APPROVAL	09/30/2
ISSUE NAME	DATE

ARCHITECTS

SDGI
100 WEST 41ST STREET
NEW YORK, NY 10036
PHONE: 212-704-0734


PROJECT N.


EKIMETRICS
120 BROADWAY
NEW YORK, NY 10271

SHEFT NAW

DETAILS
TILE

DATE:
PROJECT NO.:
PRINCIPAL:
DRAWING BY:
CHECKED BY:
SCALE:
DWG No.:
T-300
10 of 1

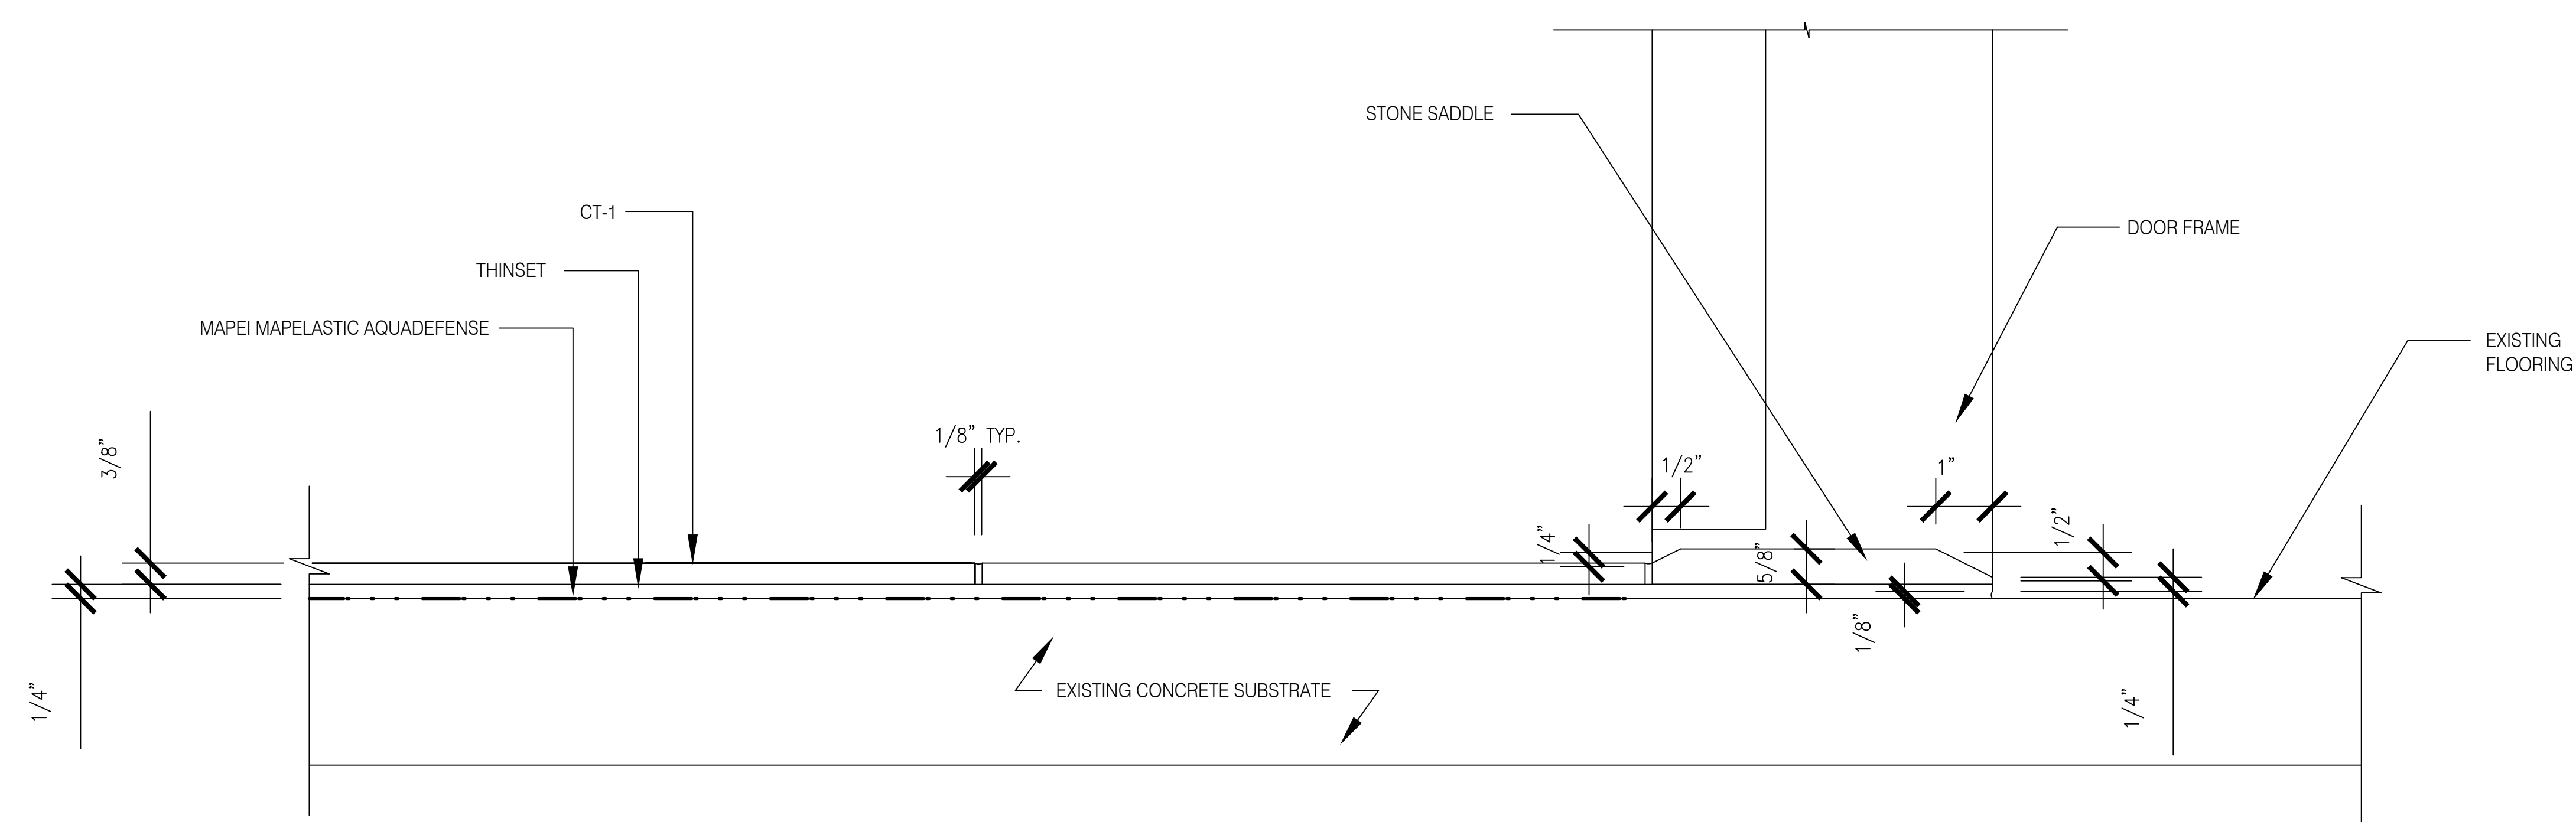

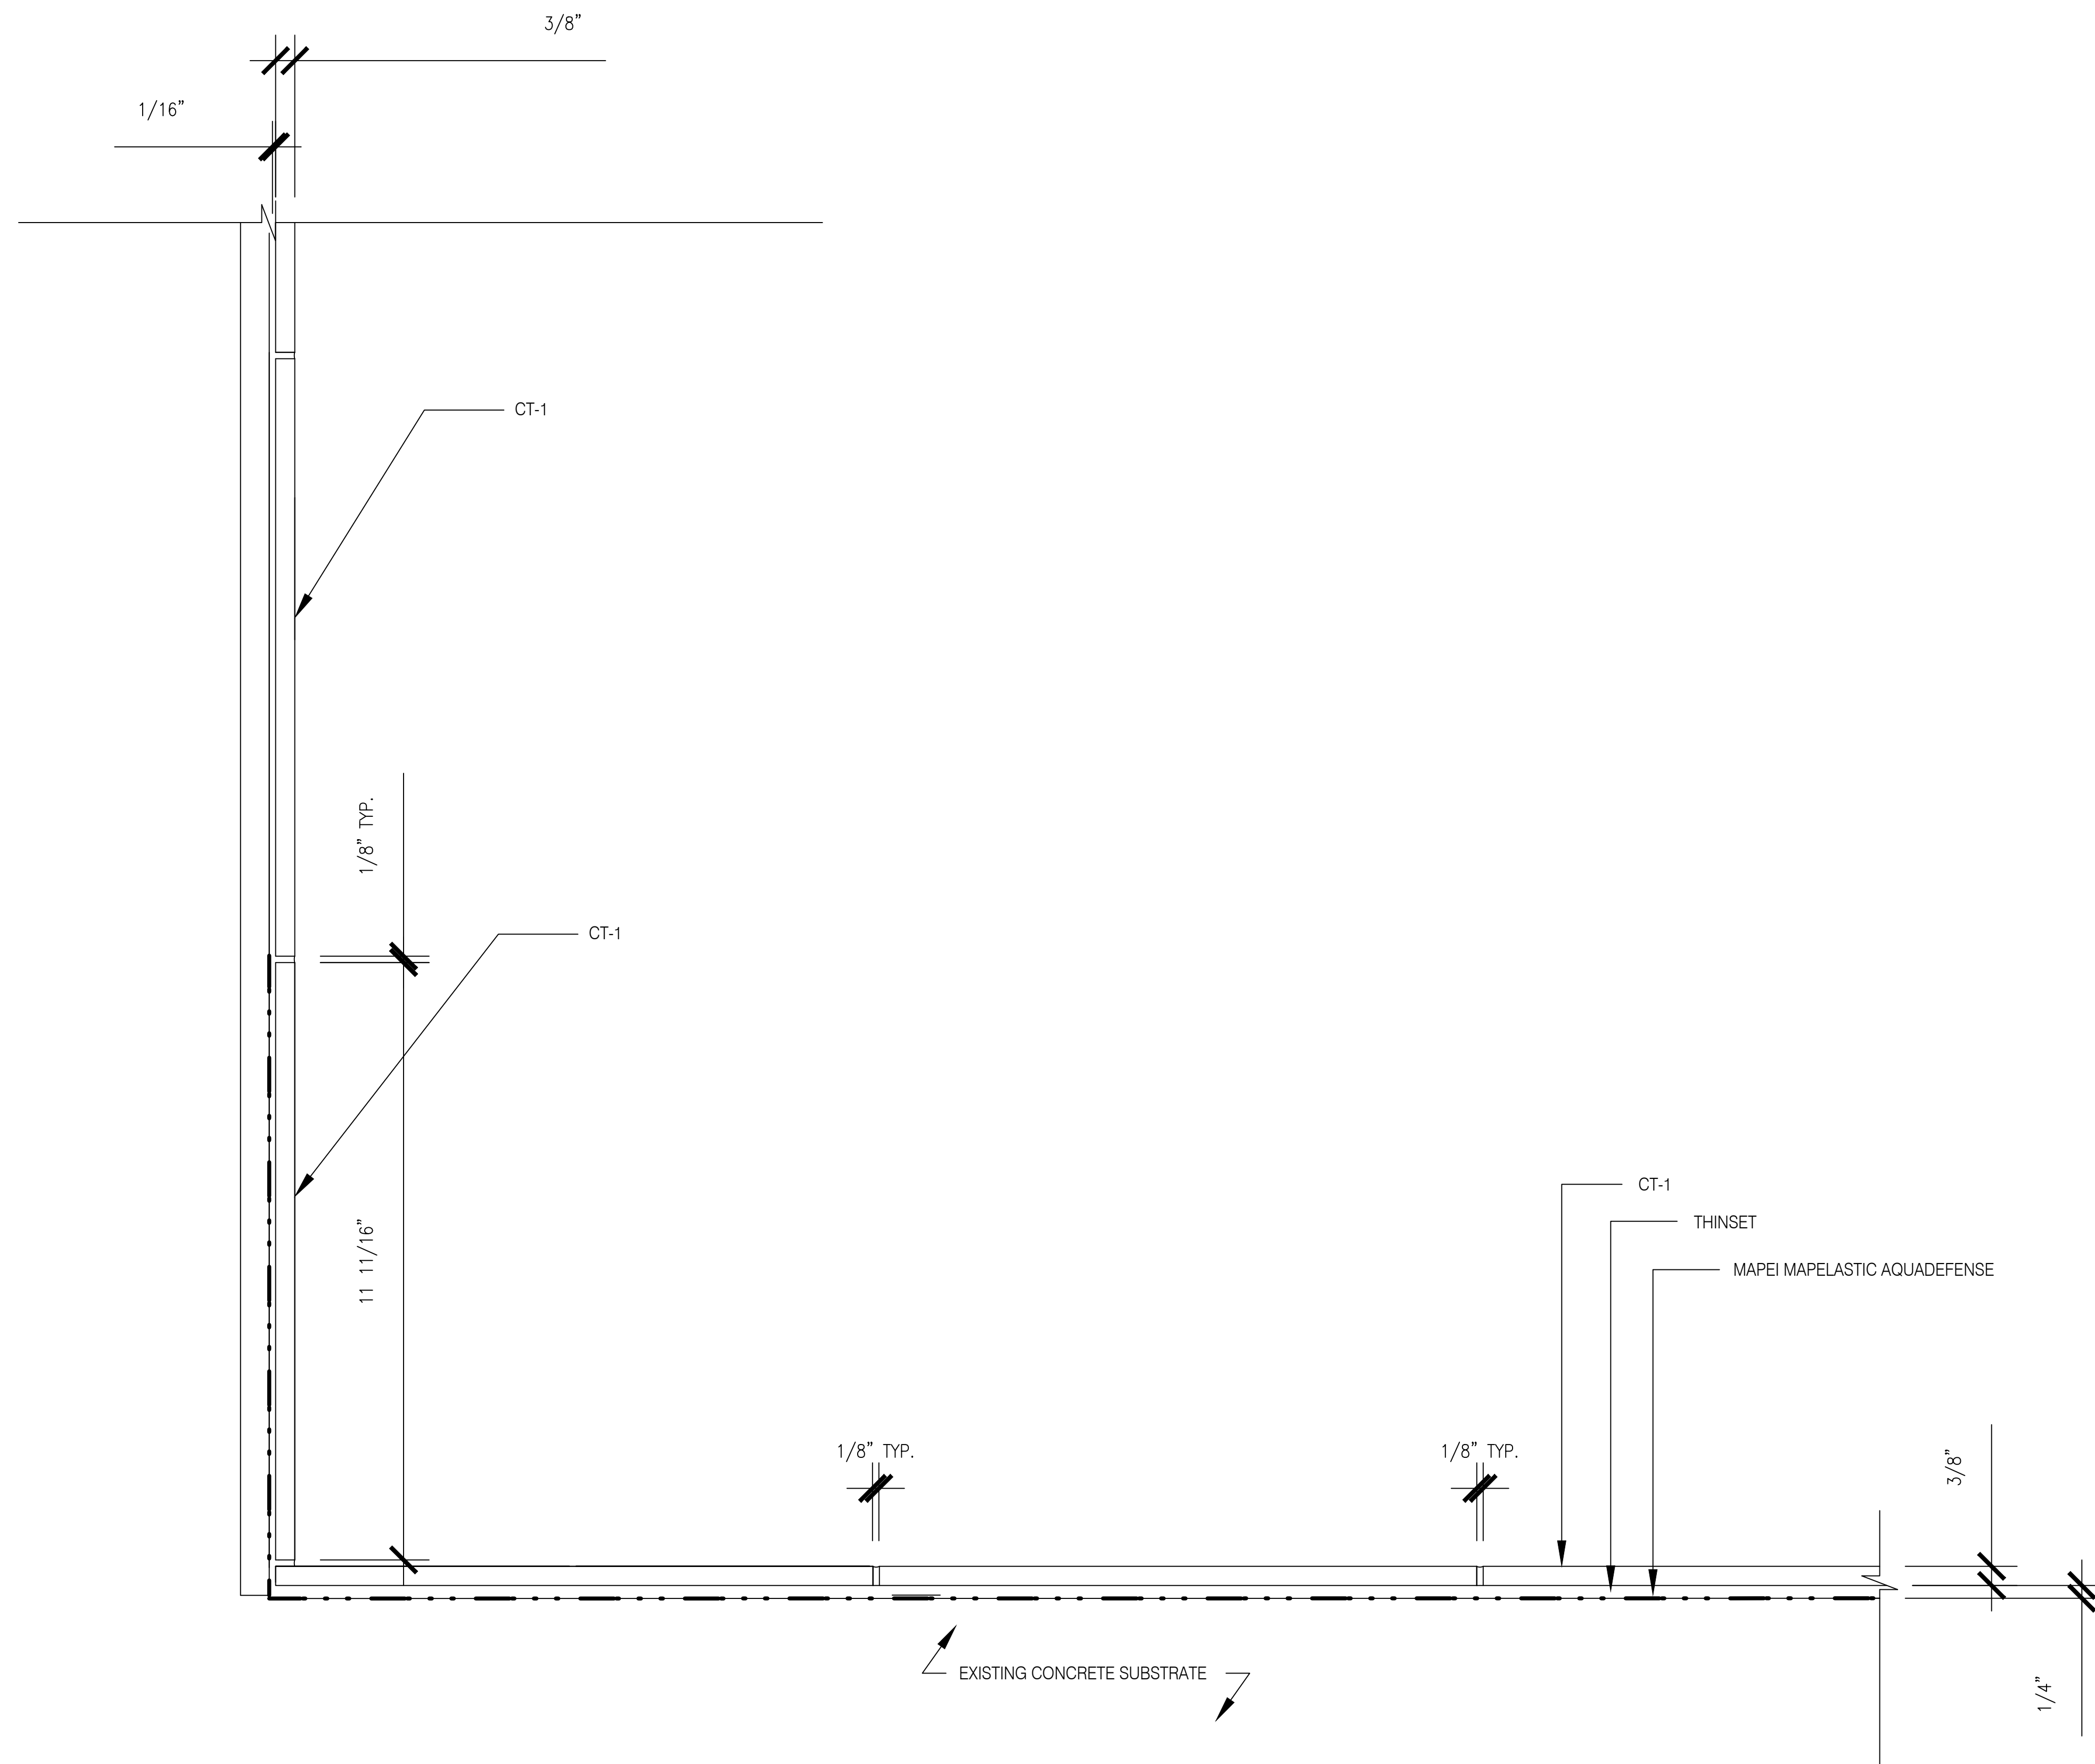

AUSTRO TILE & STONE, LLC
30-25 93RD STREET
EAST ELMHURST, NY 11369

CONTRACTOR:
JRM CONSTRUCTION
MANAGEMENT, LLC
242 WEST 36TH STREET
11TH FLOOR
NEW YORK, NY 10018

INTERIOR DESIGNER:

ISSUE FOR APPROVAL	09/30/24
ISSUE NAME	DATE

PROJECT:

SDGI
200 WEST 41ST STREET
NEW YORK, NY 10036
PHONE: 212-704-0734



PROJECT NAME:

EKIMETRICS
120 BROADWAY
NEW YORK, NY 10271

SHEET NAME:

DETAILS
TILE

DATE:	
PROJECT NO.:	
PRINCIPAL:	
DRAWING BY:	
CHECKED BY:	
SCALE:	
DWG No.:	
T-301	
11 of 15	

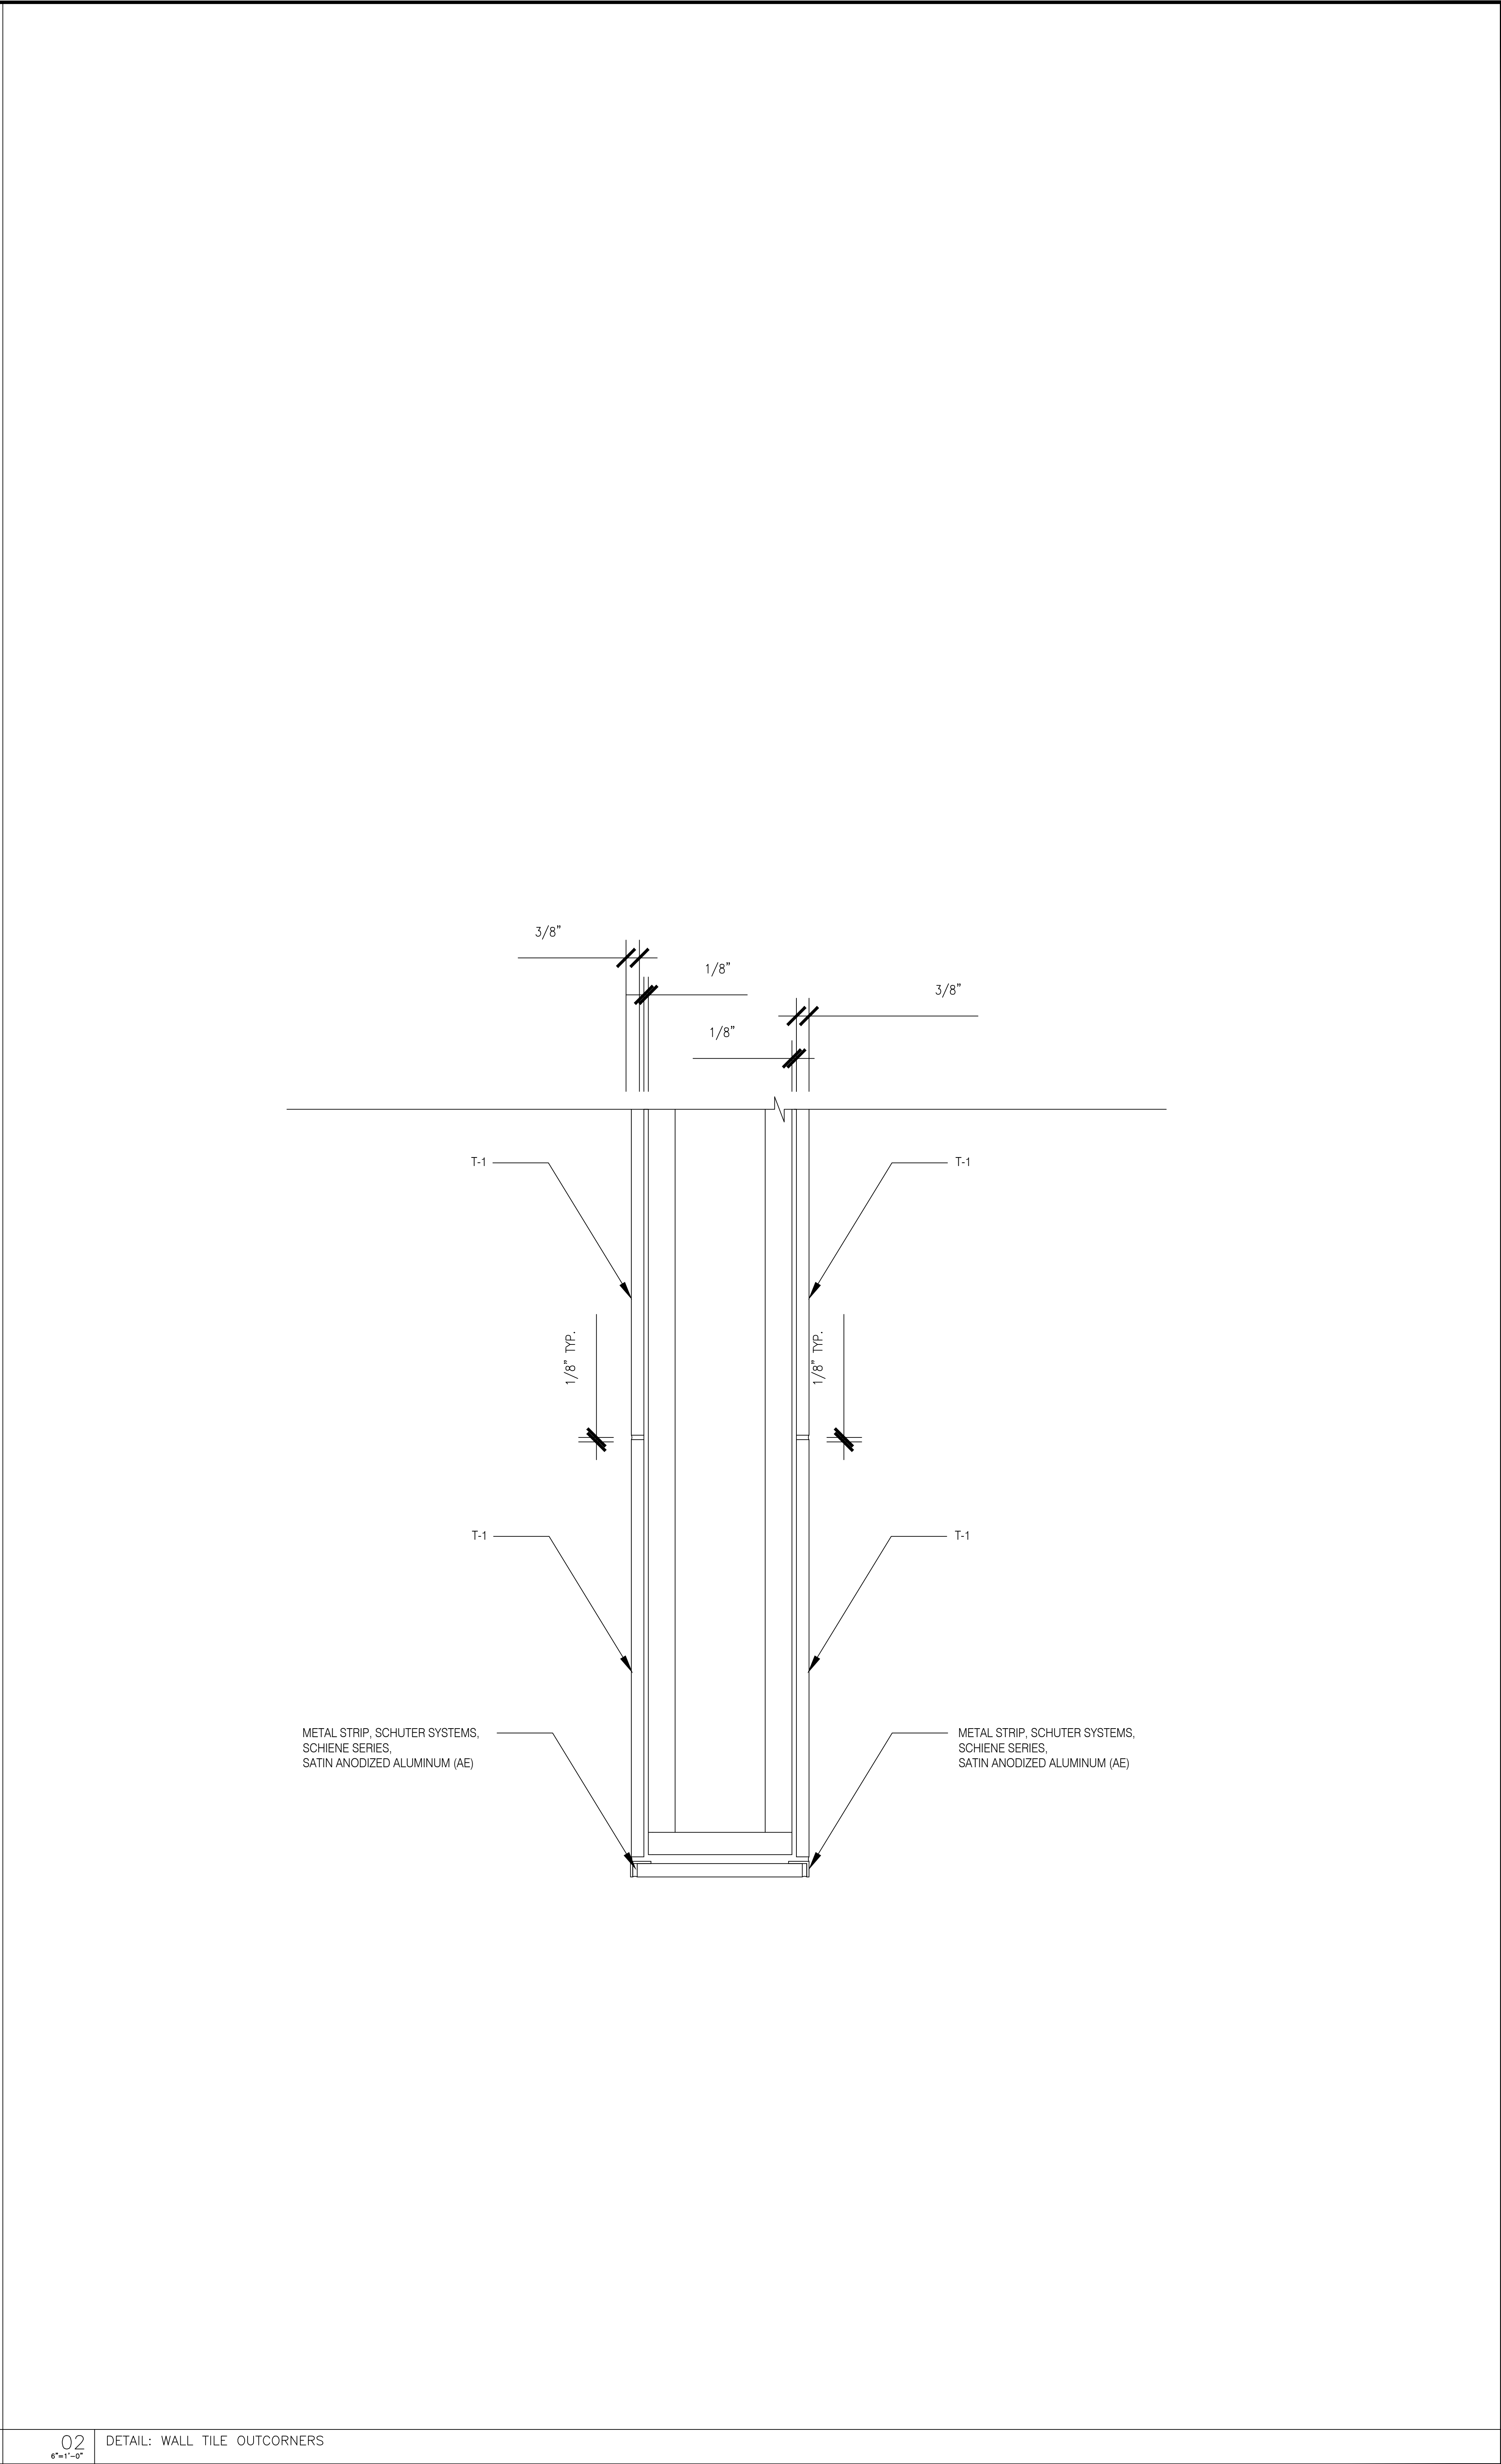 

AUSTRO TILE & STONE, LLC
30-25 93RD STREET
EAST ELMHURST, NY 11369

JRM CONSTRUCTION
MANAGEMENT, LLC
242 WEST 36TH STREET
11TH FLOOR
NEW YORK, NY 10018

SDGI
200 WEST 41ST STREET
NEW YORK, NY 10036
PHONE: 212-704-0734

EKIMETRICS
120 BROADWAY
NEW YORK, NY 10271

DETAILS
TILE

DATE:
PROJECT NO.:
PRINCIPAL:
DRAWING BY:
CHECKED BY:
SCALE:
DWG No.:
T-302
12 of 15

MIRROR BY OTHERS

SS3

SS3

SS3

MITERED EASED EDGE

AMERICAN STANDARD STUDIO
CARRE#0426.00 BY OTHERS


SS3

PLYWOOD SUBSTRATE
BY OTHERS

02

8" x 11" - 0"

ENLARGED DETAIL: WOMEN'S BATHROOM

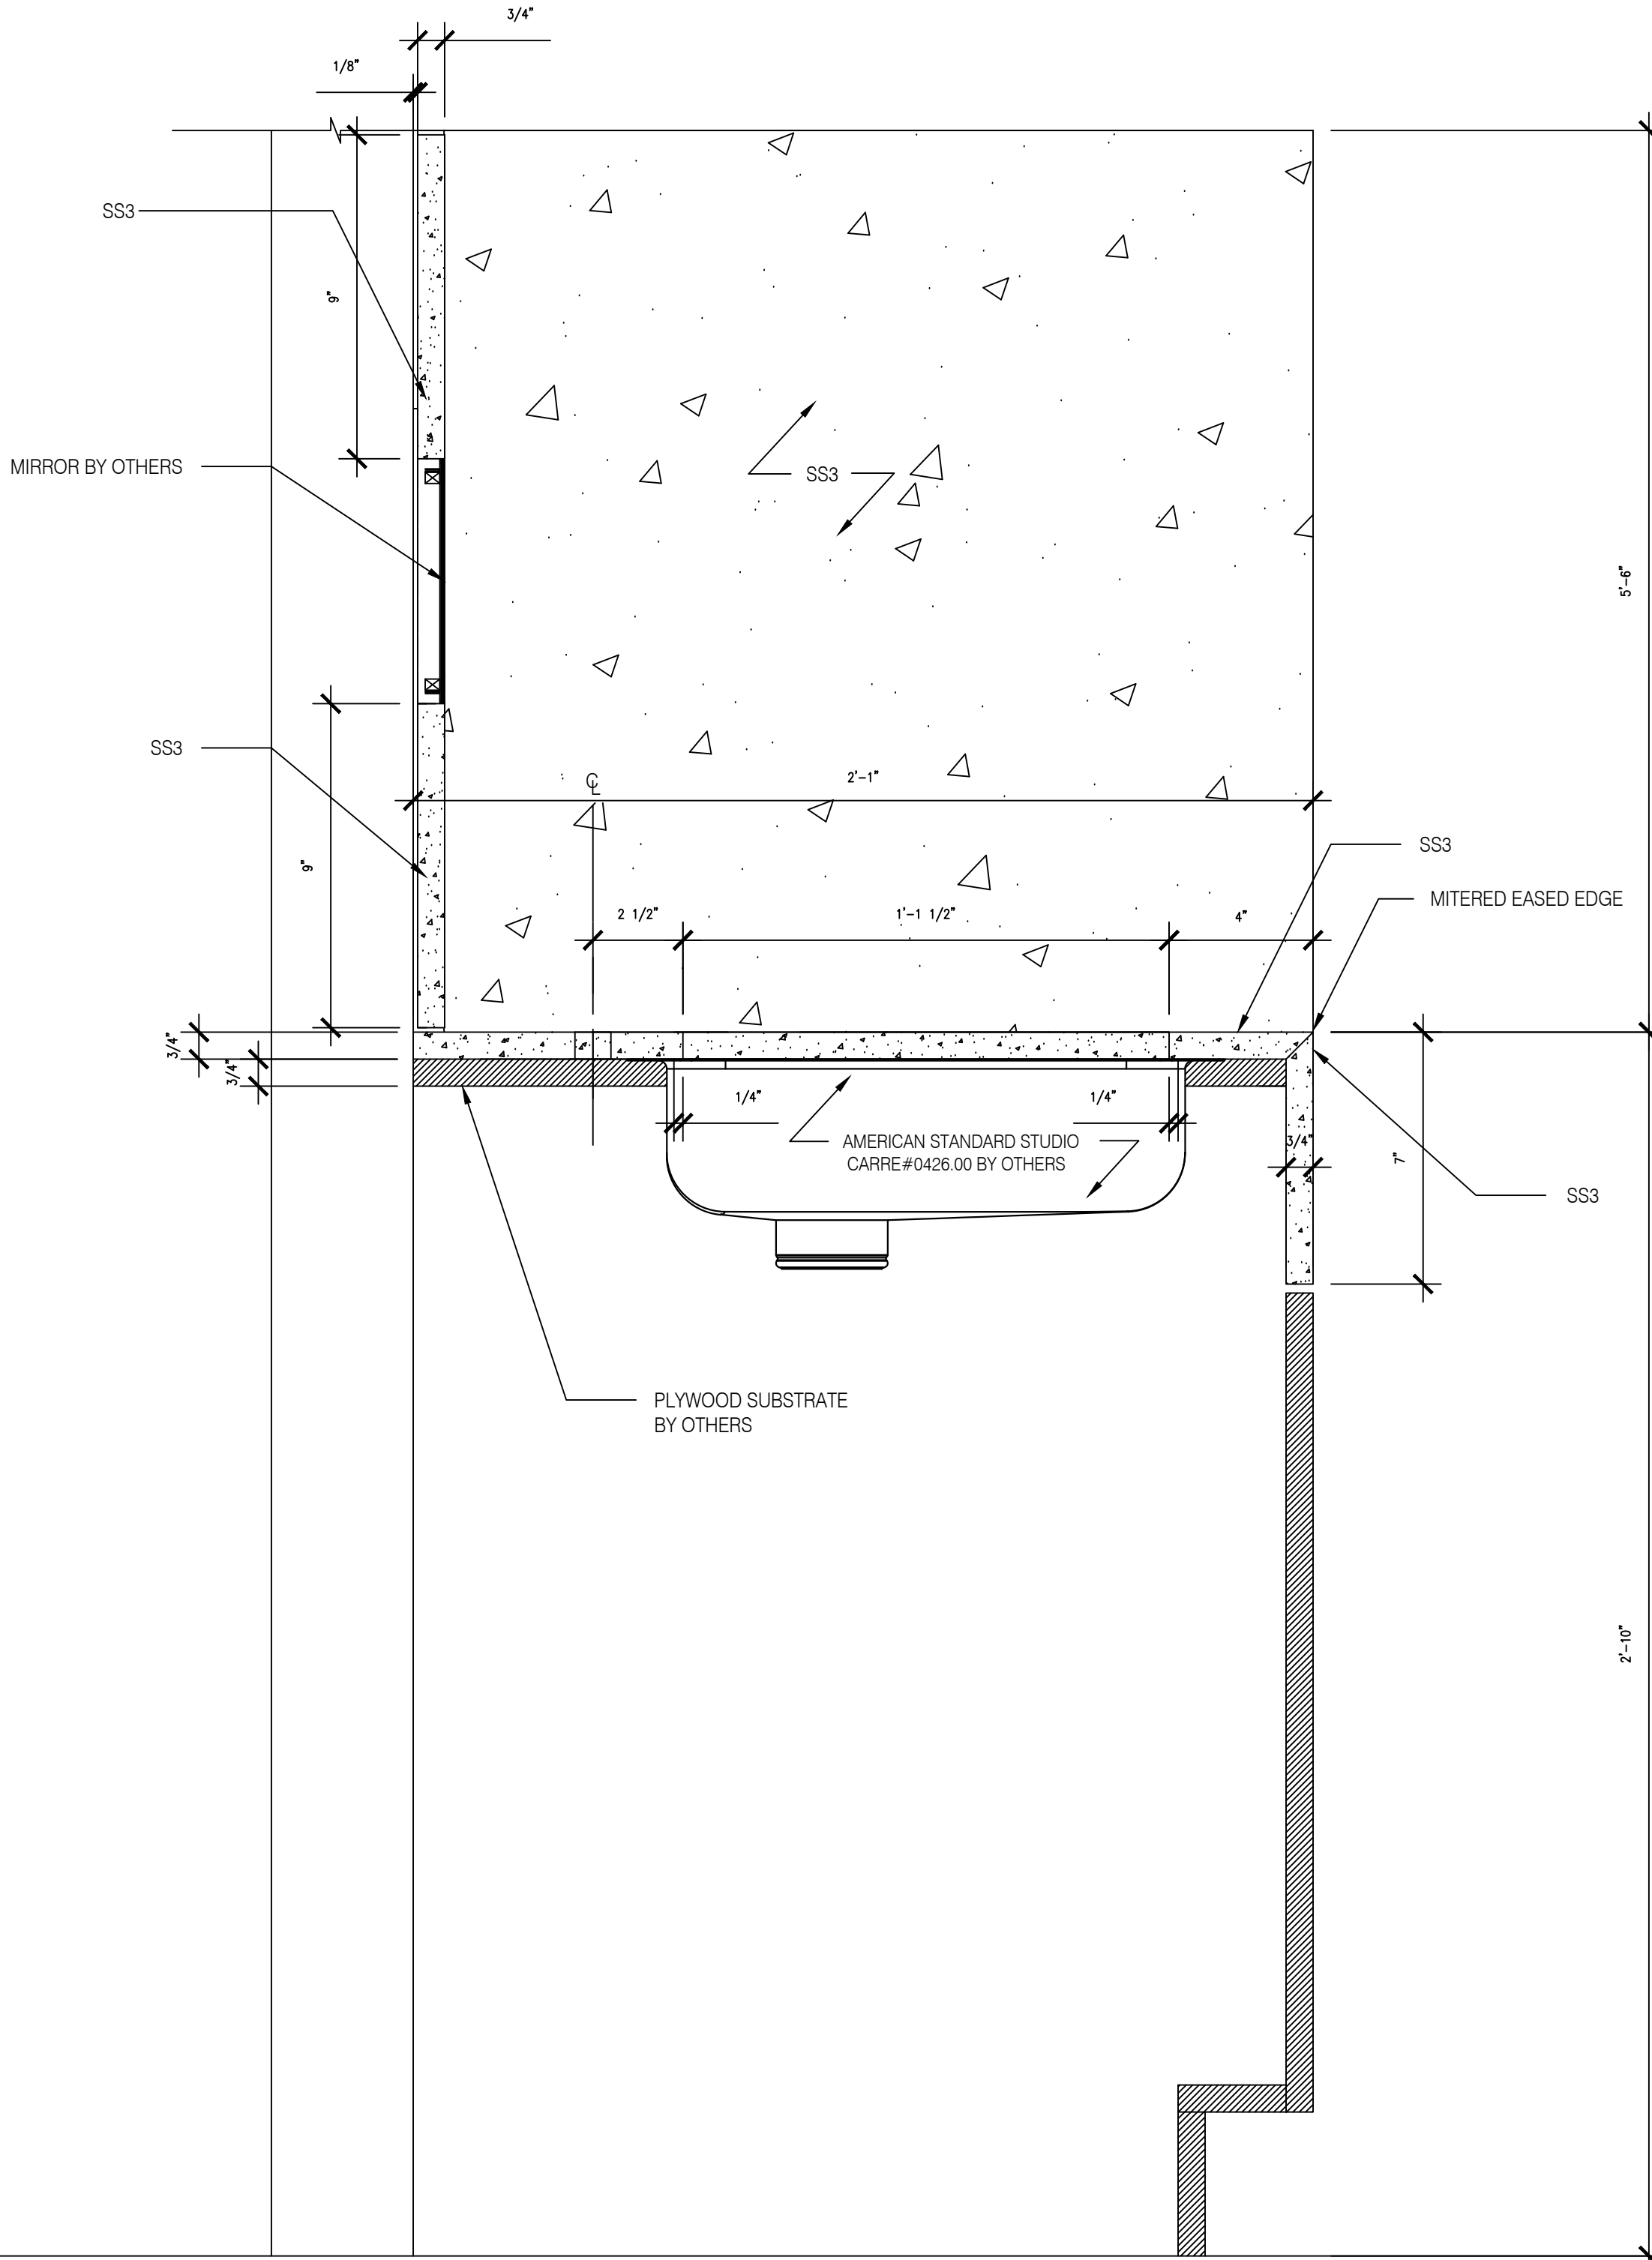

01

8" x 11" - 0"

DETAIL: WOMEN'S BATHROOM

AUSTRO TILE & STONE, LLC
30-25 93RD STREET
EAST ELMHURST, NY 11369

CONTRACTOR:

JRM CONSTRUCTION
MANAGEMENT, LLC
242 WEST 36TH STREET
11TH FLOOR
NEW YORK, NY 10018

INTERIOR DESIGNER:

ISSUE FOR APPROVAL 09/30/24

ISSUE NAME DATE

PROJECT:

SDGI
200 WEST 41ST STREET
NEW YORK, NY 10036
PHONE: 212-704-0734

PROJECT NAME:


EKIMETRICS
120 BROADWAY
NEW YORK, NY 10271

SHEET NAME:

DETAILS
STONE COUNTERTOPS


DATE:
PROJECT NO.:
PRINCIPAL:
DRAWING BY:
CHECKED BY:
SCALE:
DWG No.:
T-400

13 of 15

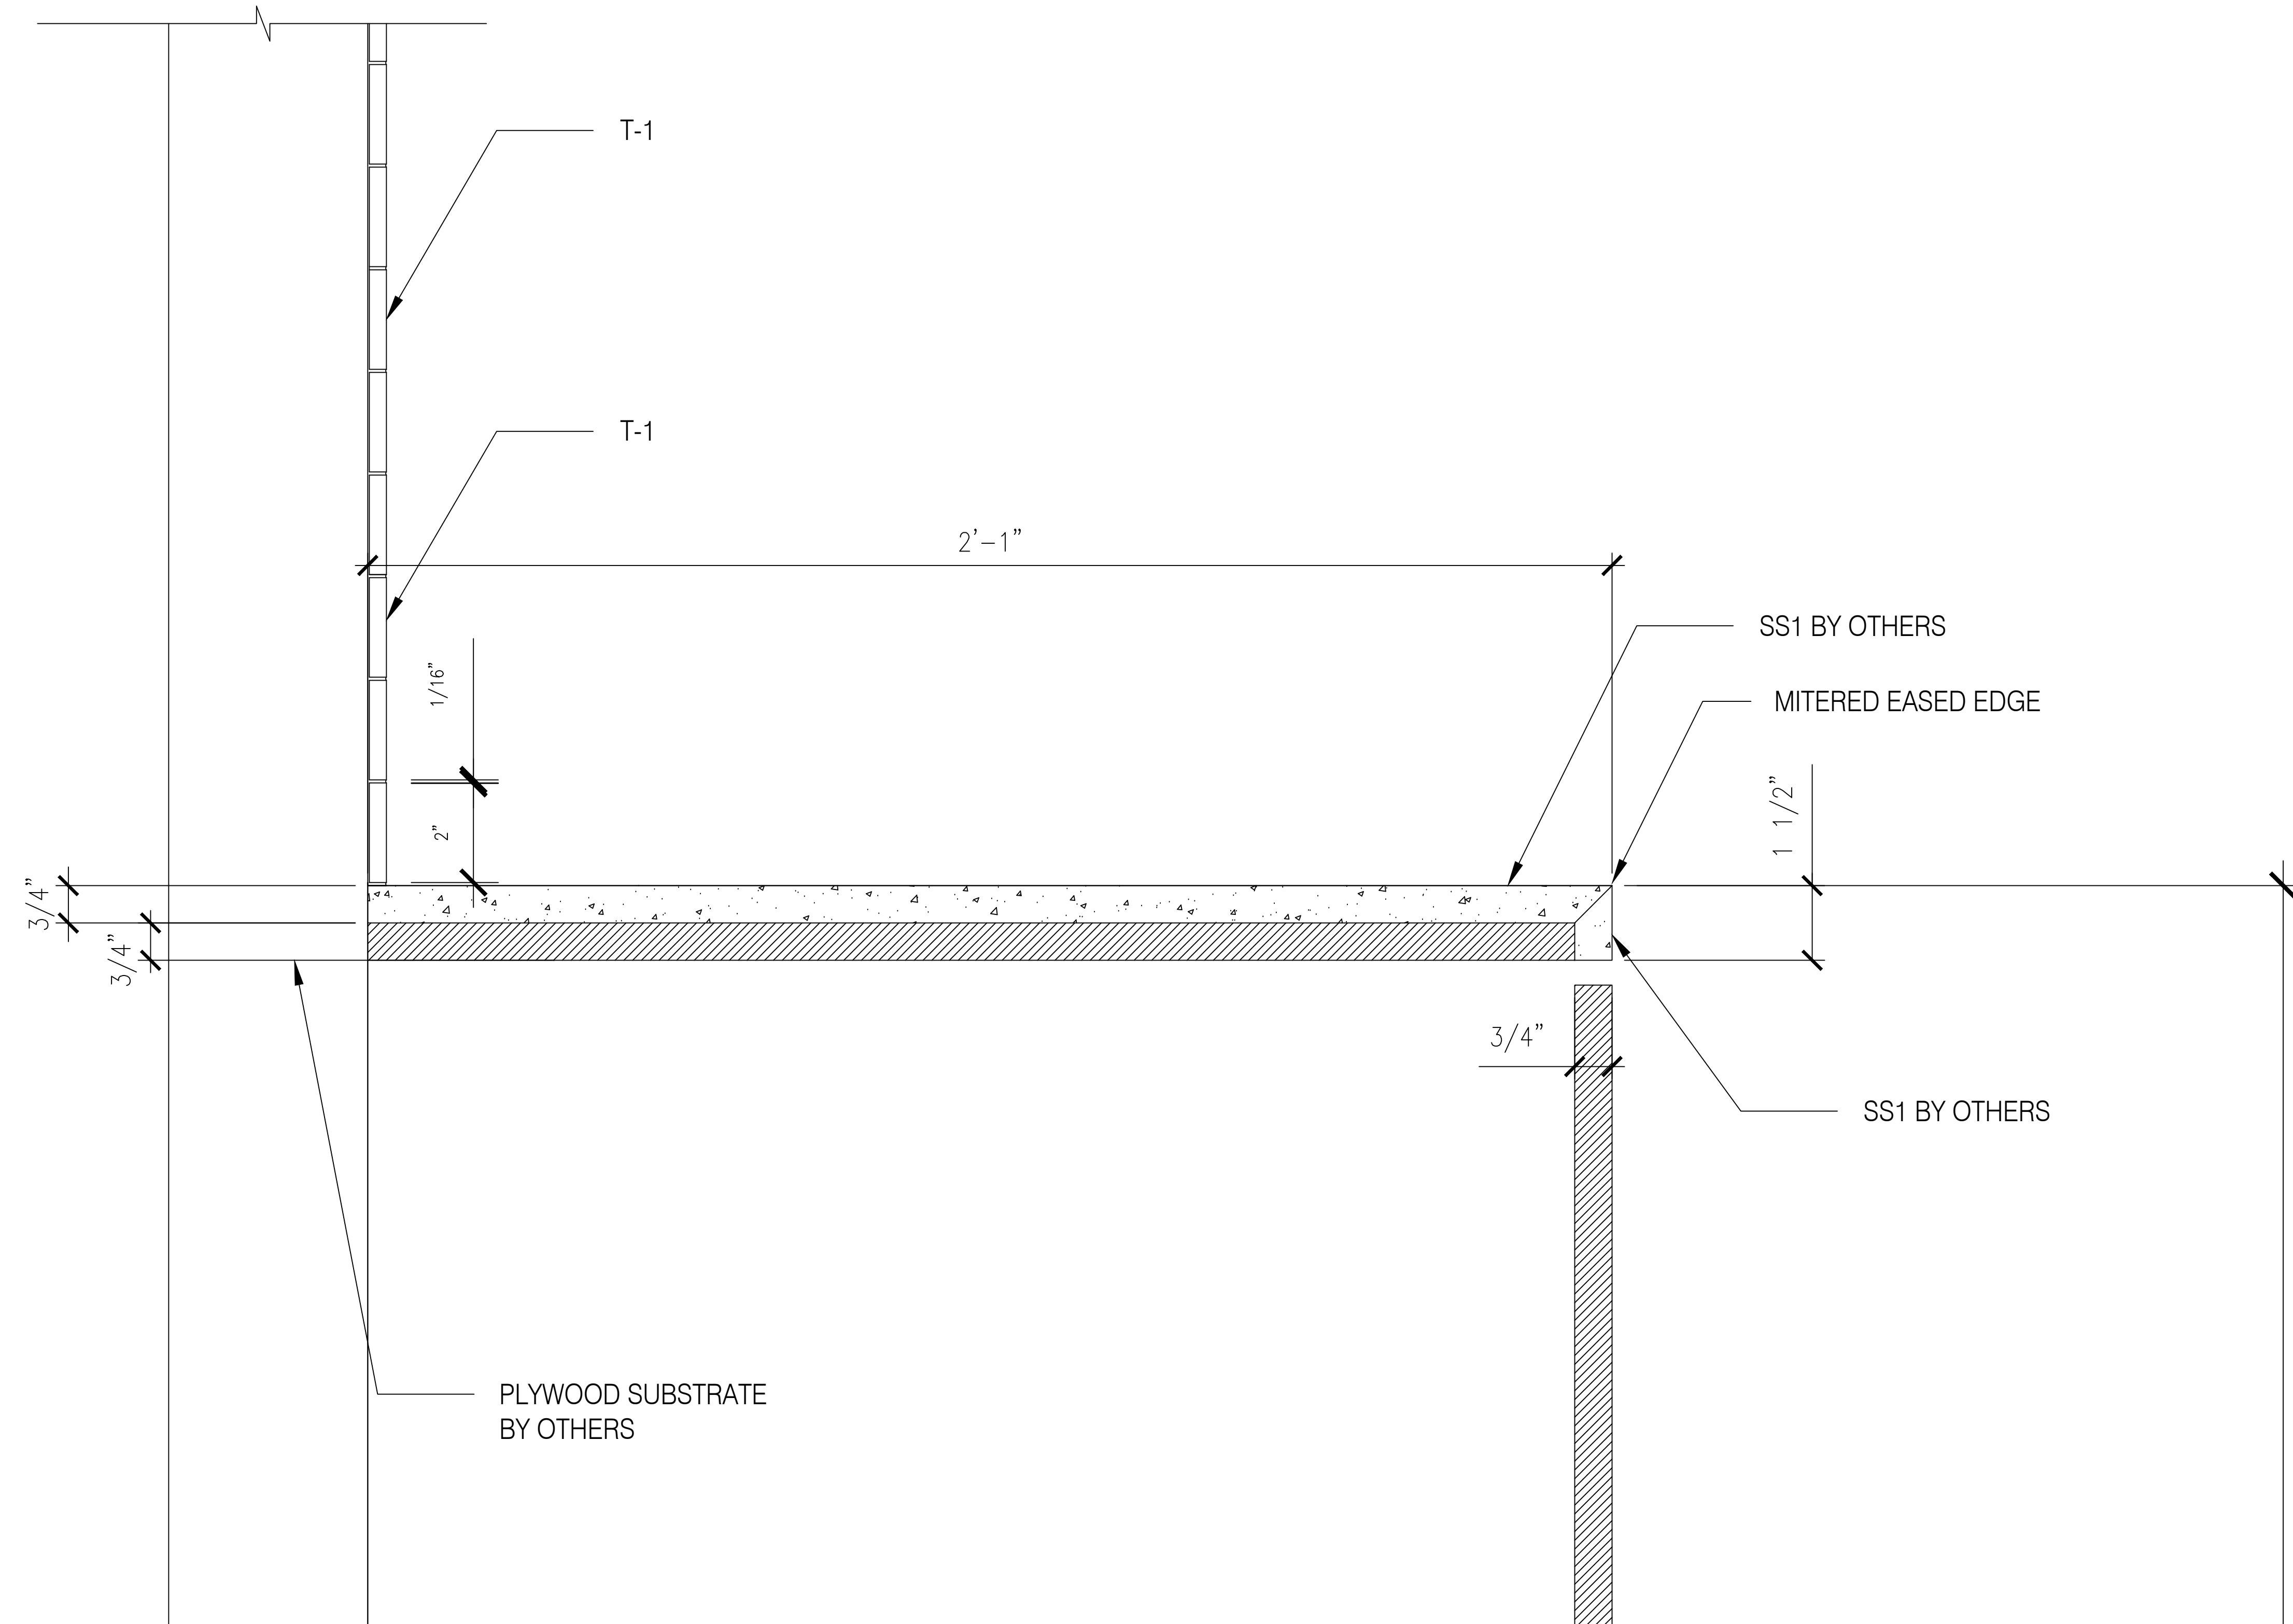

02
6" x 11" - 0"

ENLARGED DETAIL: PANTRY

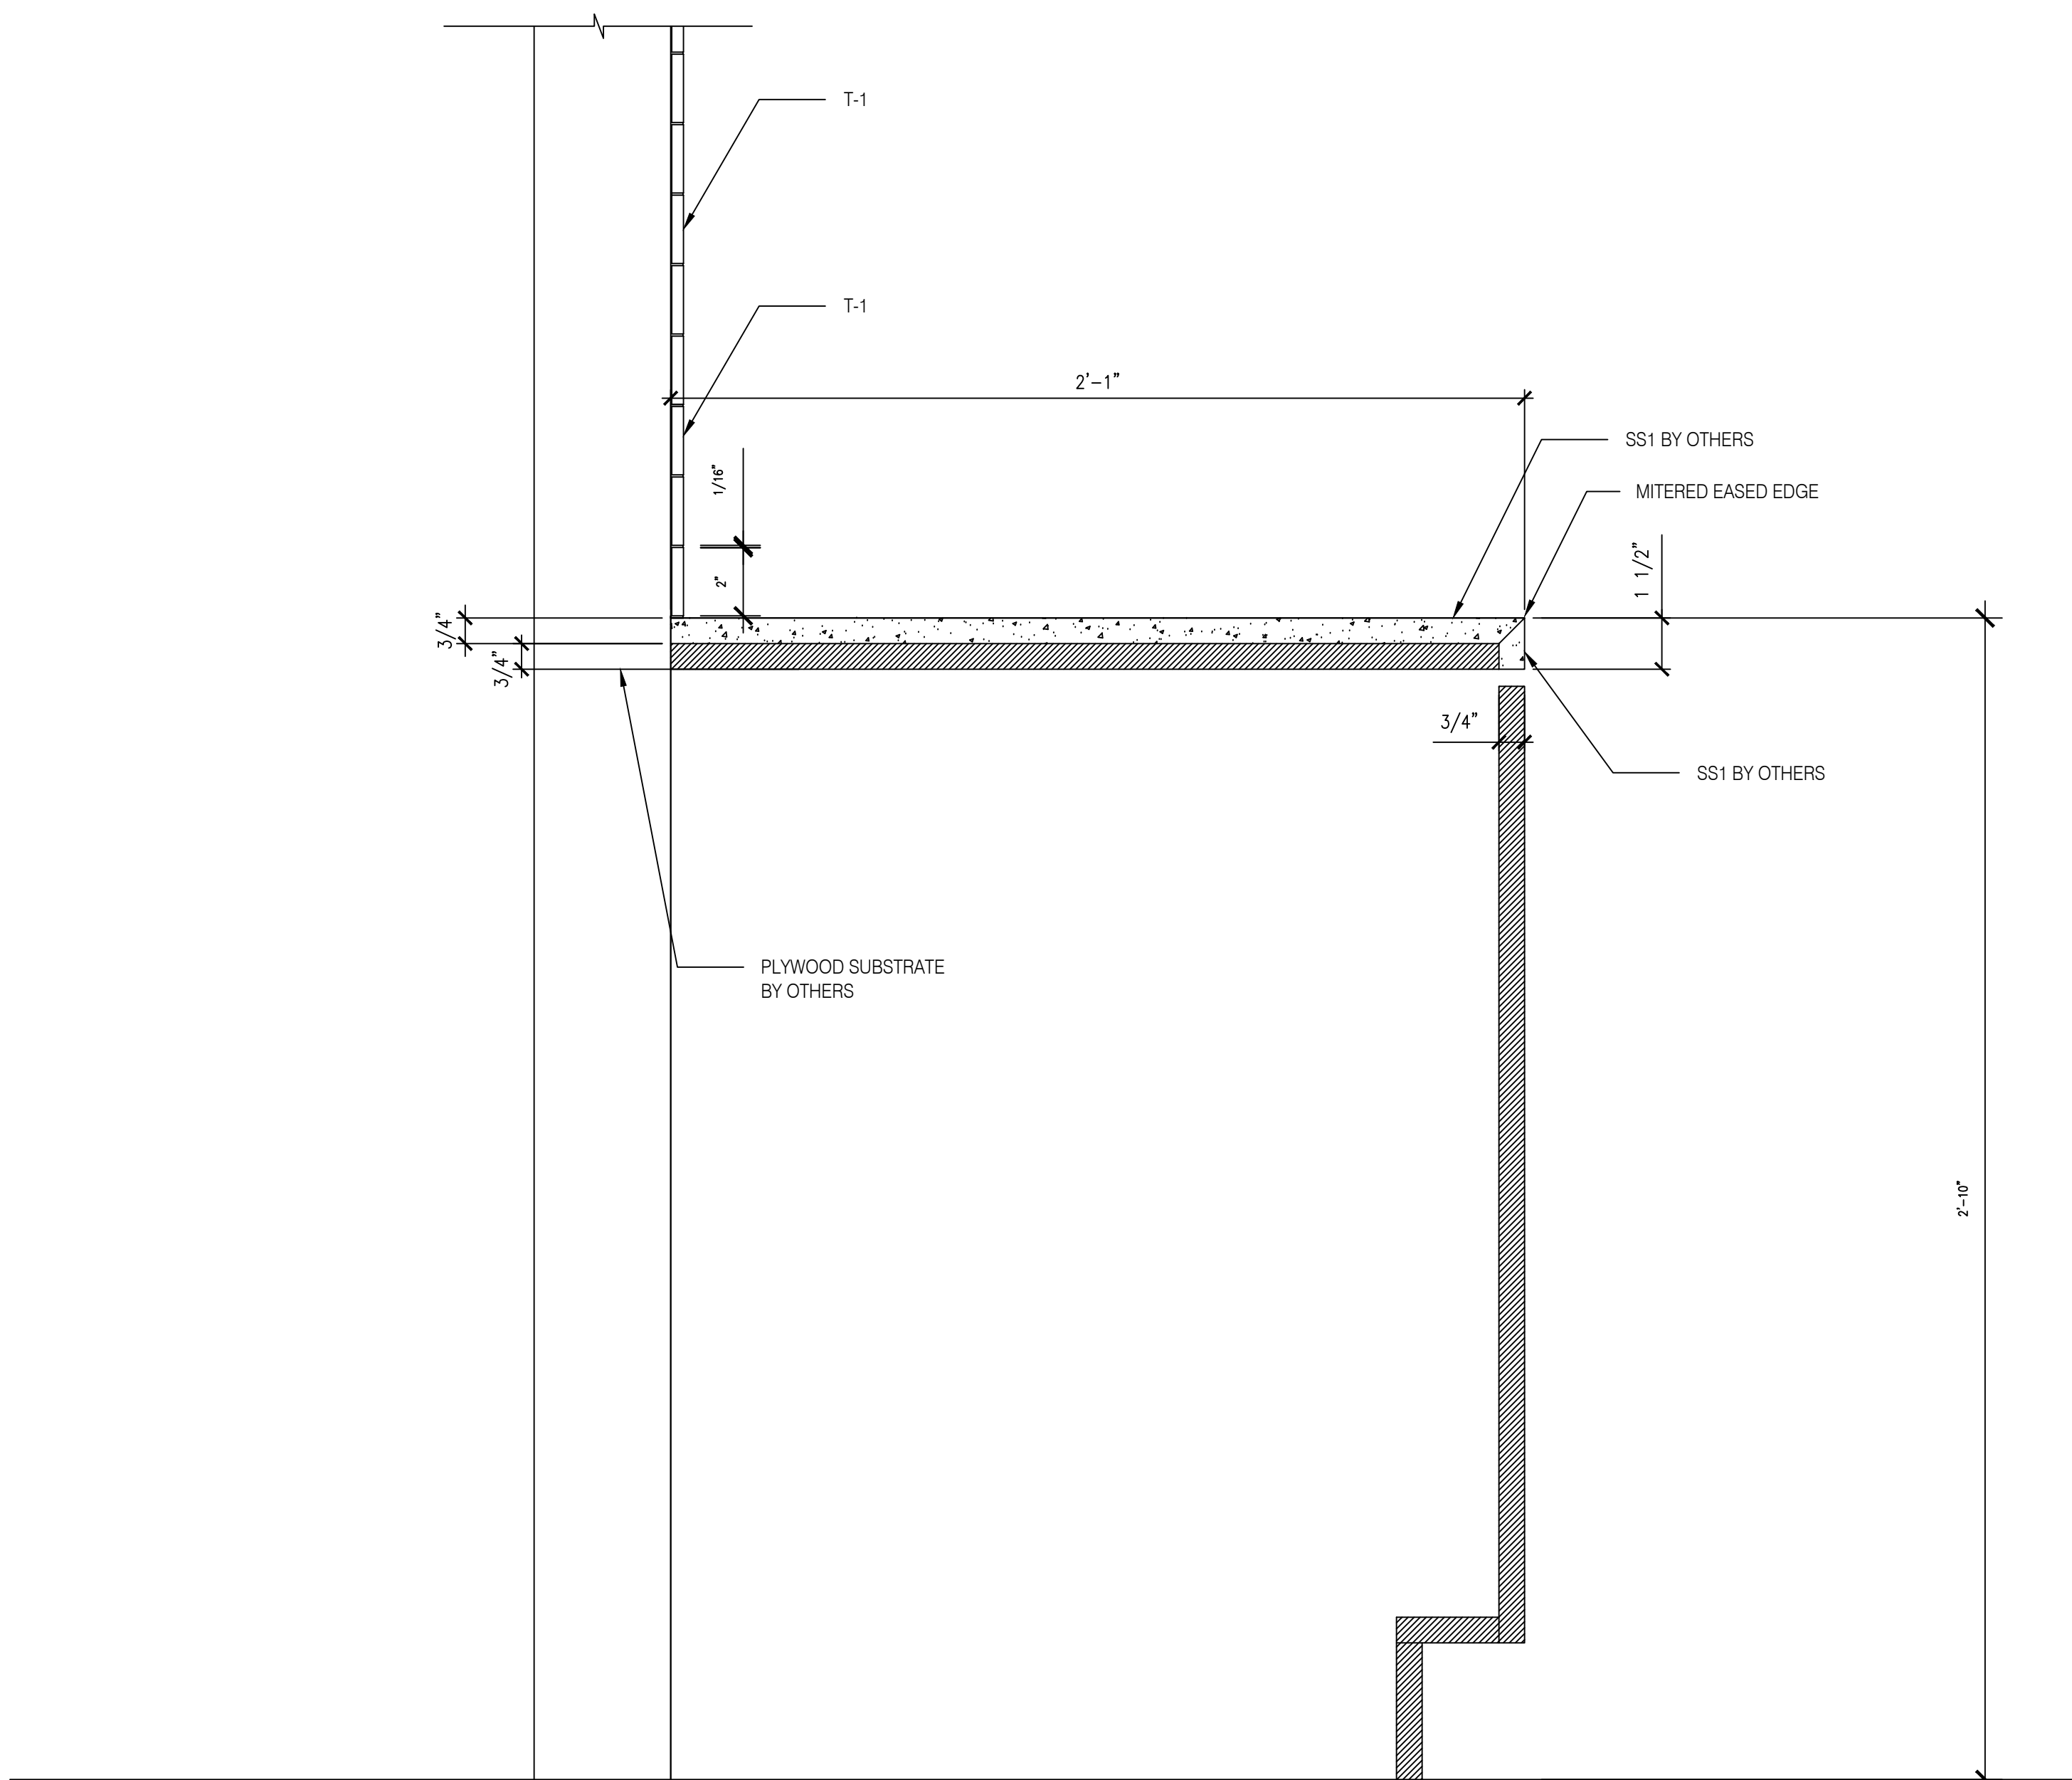

01
6" x 11" - 0"

DETAIL: PANTRY

AUSTRO TILE & STONE, LLC
30-25 93RD STREET
EAST ELMHURST, NY 11369

CONTRACTOR:
JRM CONSTRUCTION
MANAGEMENT, LLC
242 WEST 36TH STREET
11TH FLOOR
NEW YORK, NY 10018

INTERIOR DESIGNER:

ISSUE FOR APPROVAL	09/30/24
ISSUE NAME	DATE

PROJECT:
SDGI
200 WEST 41ST STREET
NEW YORK, NY 10036
PHONE: 212-704-0734

PROJECT NAME:
EKIMETRICS
120 BROADWAY
NEW YORK, NY 10271

SHEET NAME:
DETAILS
STONE COUNTERTOPS

DATE:
PROJECT NO.:
PRINCIPAL:
DRAWING BY:
CHECKED BY:
SCALE:
DWG No.:

T-402
15 of 15