

LACOSTE NYC

575 5TH AVENUE,
NEW YORK NY 10017

1ST-3RD FLOORS

MATERIAL LEGEND

FLOOR TILE (T-1) MANF: MIRAGE STYLE: KORU COLOR: APRICOT KO 03 MATTE SIZE: 8"x48" CONTACT: INSTALLATION: STACKED	WALL TILE (T-1) MANF: MIRAGE STYLE: KORU COLOR: APRICOT KO 03 MATTE, CUSTOM MANUFACTURED TREADS SIZE: 13"x48" CONTACT: INSTALLATION: STACKED	FLOOR TILE (T-2) MANF: DAL TILE STYLE: NATURAL HUES COLOR: SPRING GREEN NH29 SIZE: 6"x6" CONTACT: INSTALLATION: STACKED	WALL TILE (T-3) MANF: DAL TILE STYLE: NATURAL HUES COLOR: CARNATION NH48 SIZE: 6"x6" CONTACT: INSTALLATION: STACKED	WALL COVERBASE (B-6) MANF: DAL TILE STYLE: NATURAL HUES COLOR: SPRING GREEN NH29 SIZE: 6"x6" COVEBASE P36C9 CONTACT: INSTALLATION: STACKED	WALL COVERBASE (B-7) MANF: DAL TILE STYLE: NATURAL HUES COLOR: SPRING GREEN NH29 SIZE: 6"x6" COVEBASE P36C9 CONTACT: INSTALLATION: STACKED
GROUT COLOR APPROVAL: LACTICRETE, PERMACOLOR, COLOR: TBD	GROUT COLOR APPROVAL: LACTICRETE, PERMACOLOR, COLOR: TBD	GROUT COLOR APPROVAL: LITIKOL, STARLIKE, COLOR: TBD	GROUT COLOR APPROVAL: LITIKOL, STARLIKE, COLOR: TBD	GROUT COLOR APPROVAL: LITIKOL, STARLIKE, COLOR: TBD	GROUT COLOR APPROVAL: LITIKOL, STARLIKE, COLOR: TBD

ARCHITECT TO CONFIRM:

GROUT JOINT AT T-1 TO BE 1/8"
GROUT JOINT AT T-2 TO BE 1/8"
GROUT JOINT AT T-3 TO BE 1/8"

PLEASE NOTE:

NO EXPANSION JOINTS ARE SHOWN IN THE TILE FLOORING AS THERE ARE NO EXPANSION JOINTS SHOWN IN THE ARCHITECTURAL DRAWINGS. IF EXPANSION OR MOVEMENT JOINTS ARE REQUIRED, ARCHITECT TO PROVIDE LOCATION AND DETAILS ACCORDINGLY

PER THE TCNA, "USE OF WALL-WASHER AND COVE-TYPE LIGHTING, WHERE THE LIGHTS ARE LOCATED EITHER AT THE WALL/CEILING INTERFACE OR MOUNTED DIRECTLY ON THE WALL, ARE POPULAR TECHNIQUES FOR PRODUCING DRAMATIC ROOM LIGHTING EFFECTS. WHEN PROPER BACKING SURFACES, INSTALLATION MATERIALS AND METHODS, AND LOCATION OF LIGHT FIXTURES ARE NOT CAREFULLY COORDINATED, THESE LIGHTING TECHNIQUES MAY PRODUCE SHADOWS AND UNDESIRABLE EFFECTS WITH CERAMIC TILES, SIMILAR SHADOWS ARE CREATED FROM SIDE LIGHTING INTERIOR WALLS AND FLOORS WHEN LIGHT SHINES AT THAT ANGLE THROUGH WINDOWS AND DOORS."

PLEASE TAKE NOTE OF THIS AS IT RELATES TO THE TILE IN THIS PROJECT.

DRAWING LEGEND:

CS-001	COVER SHEET, DRAWING LEGEND & MATERIAL LEGEND
KY-001	KEYPLAN - 1ST FLOOR
KY-002	KEYPLAN - 2ND FLOOR
KY-003	KEYPLAN - 3RD FLOOR
T-100	PLAN -1ST FLOOR
T-101	ENLARGED PLAN- 1ST FLOOR
T-102	ENLARGED PLAN- 1ST FLOOR
T-103	ENLARGED PLAN- 1ST FLOOR
T-104	PLAN -2ND FLOOR
T-105	ENLARGED PLAN -2ND FLOOR
T-106	ENLARGED PLAN -2ND FLOOR
T-107	ENLARGED PLAN -2ND FLOOR
T-108	ENLARGED PLAN -2ND FLOOR
T-109	ENLARGED PLAN -2ND FLOOR
T-110	PLAN/ELEVATIONS -2ND FLOOR FITTING ROOMS
T-111	PLAN/ELEVATIONS -3RD FLOOR RESTROOMS
T-112	PLAN/ELEVATIONS -3RD FLOOR RESTROOMS
T-113	PLAN/ELEVATIONS -3RD FLOOR PANTRY
T-200	DETAILS - TILE
T-201	DETAILS - TILE
T-202	DETAILS - TILE

AUSTRO TILE & STONE, LLC
30-25 93RD STREET
EAST ELMHURST, NY 11369

CONTRACTOR:
JRM CONSTRUCTION
MANAGEMENT, LLC
242 WEST 36TH STREET
11TH FLOOR
NEW YORK, NY 10018

INTERIOR DESIGNER:

[illegible]

ISSUE FOR APPROVAL	09/09/24
ISSUE NAME	DATE

KENNETH PARK ARCHITECTS
360 LEXINGTON AVENUE
NEW YORK, NY 10017PHONE:
212-599-0044

PROJECT NAME:


LACOSTE
575 5TH AVENUE
NEW YORK, NY 10017

SHEET NAME

COVER SHEET

DATE:	
PROJECT NO.:	
PRINCIPAL:	
DRAWING BY:	
CHECKED BY:	
SCALE:	AS NOTED
DWG No.:	
CS-001	
1 of 21	

LOCATION

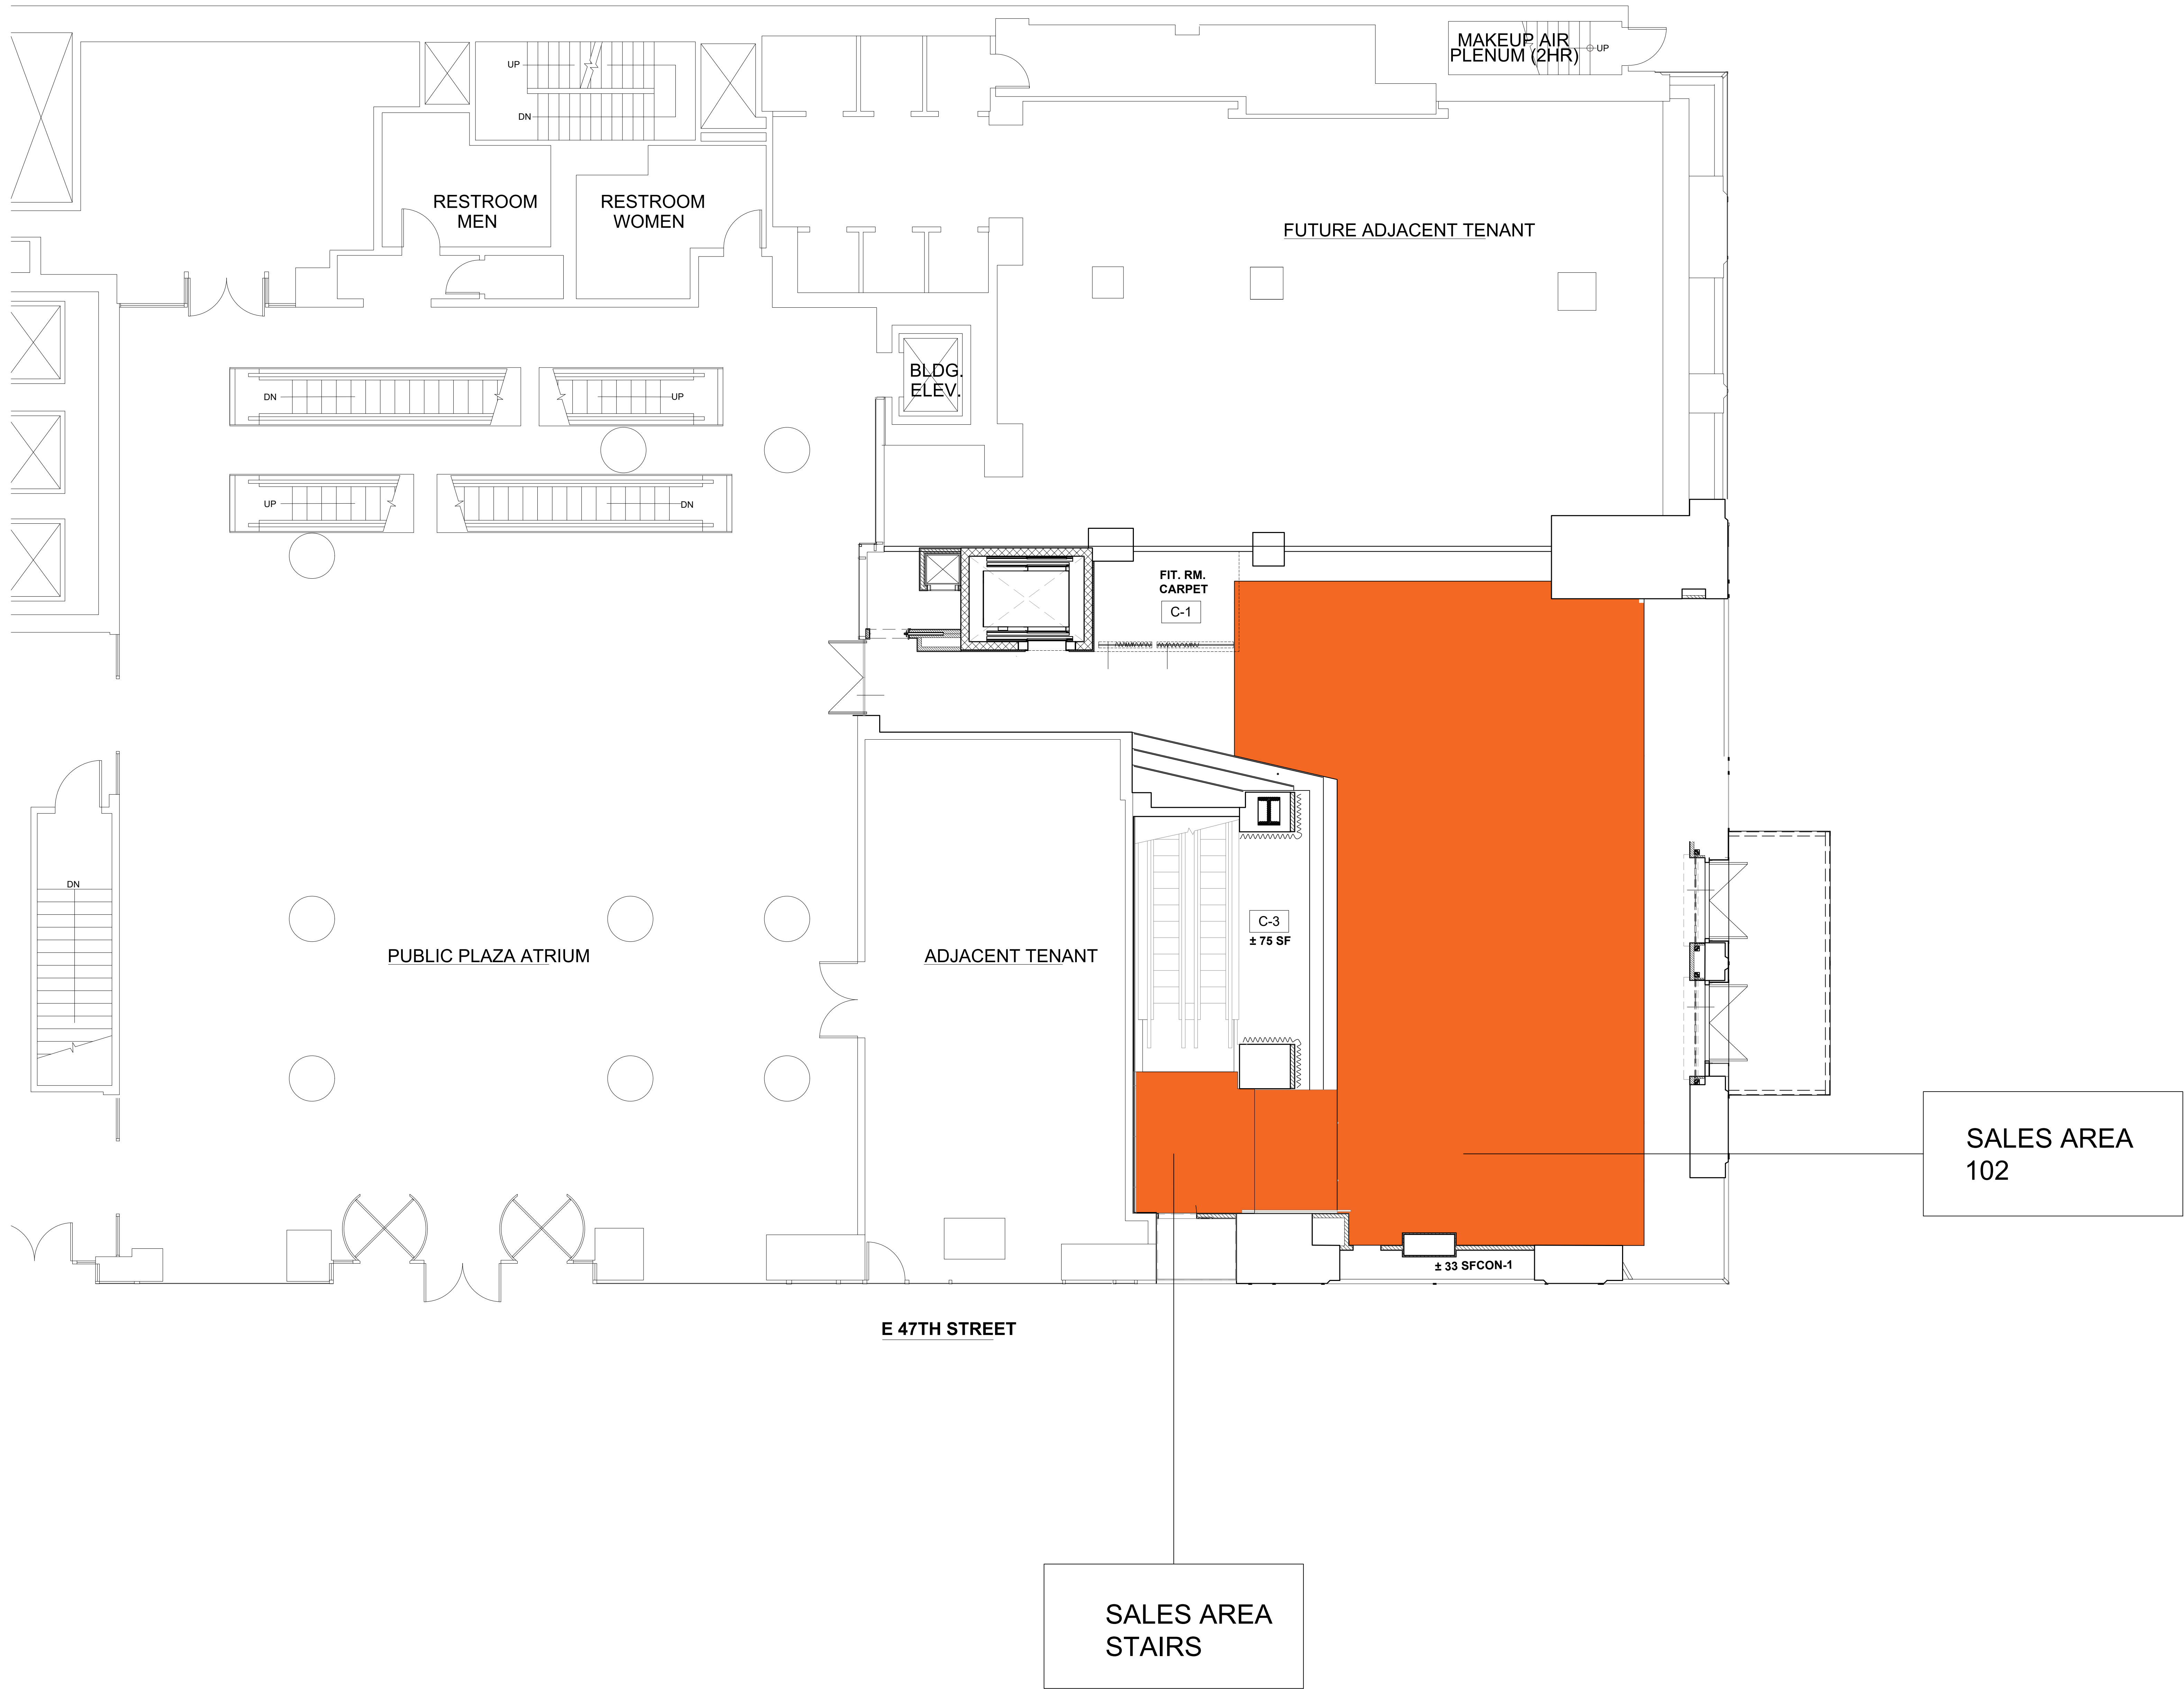

AUSTRO TILE & STONE, LLC
30-25 93RD STREET
EAST ELMHURST, NY 11369

CONTRACTOR:
JRM CONSTRUCTION
MANAGEMENT, LLC
242 WEST 36TH STREET
11TH FLOOR
NEW YORK, NY 10018

INTERIOR DESIGNER:

ISSUE FOR APPROVAL	DATE
ISSUE NAME	DATE

PROJECTED:
KENNETH PARK ARCHITECTS
360 LEXINGTON AVENUE
NEW YORK, NY 10017PHONE:
212-599-0044

PROJECT NAME:


LACOSTE
575 5TH AVENUE
NEW YORK, NY 10017

SHEET NAME:

KEYPLAN
1ST FLOOR

DATE:
PROJECT NO.:
PRINCIPAL:
DRAWING BY:
CHECKED BY:
SCALE:
DWG No.:
KY-001
2 of 21

LOCATION

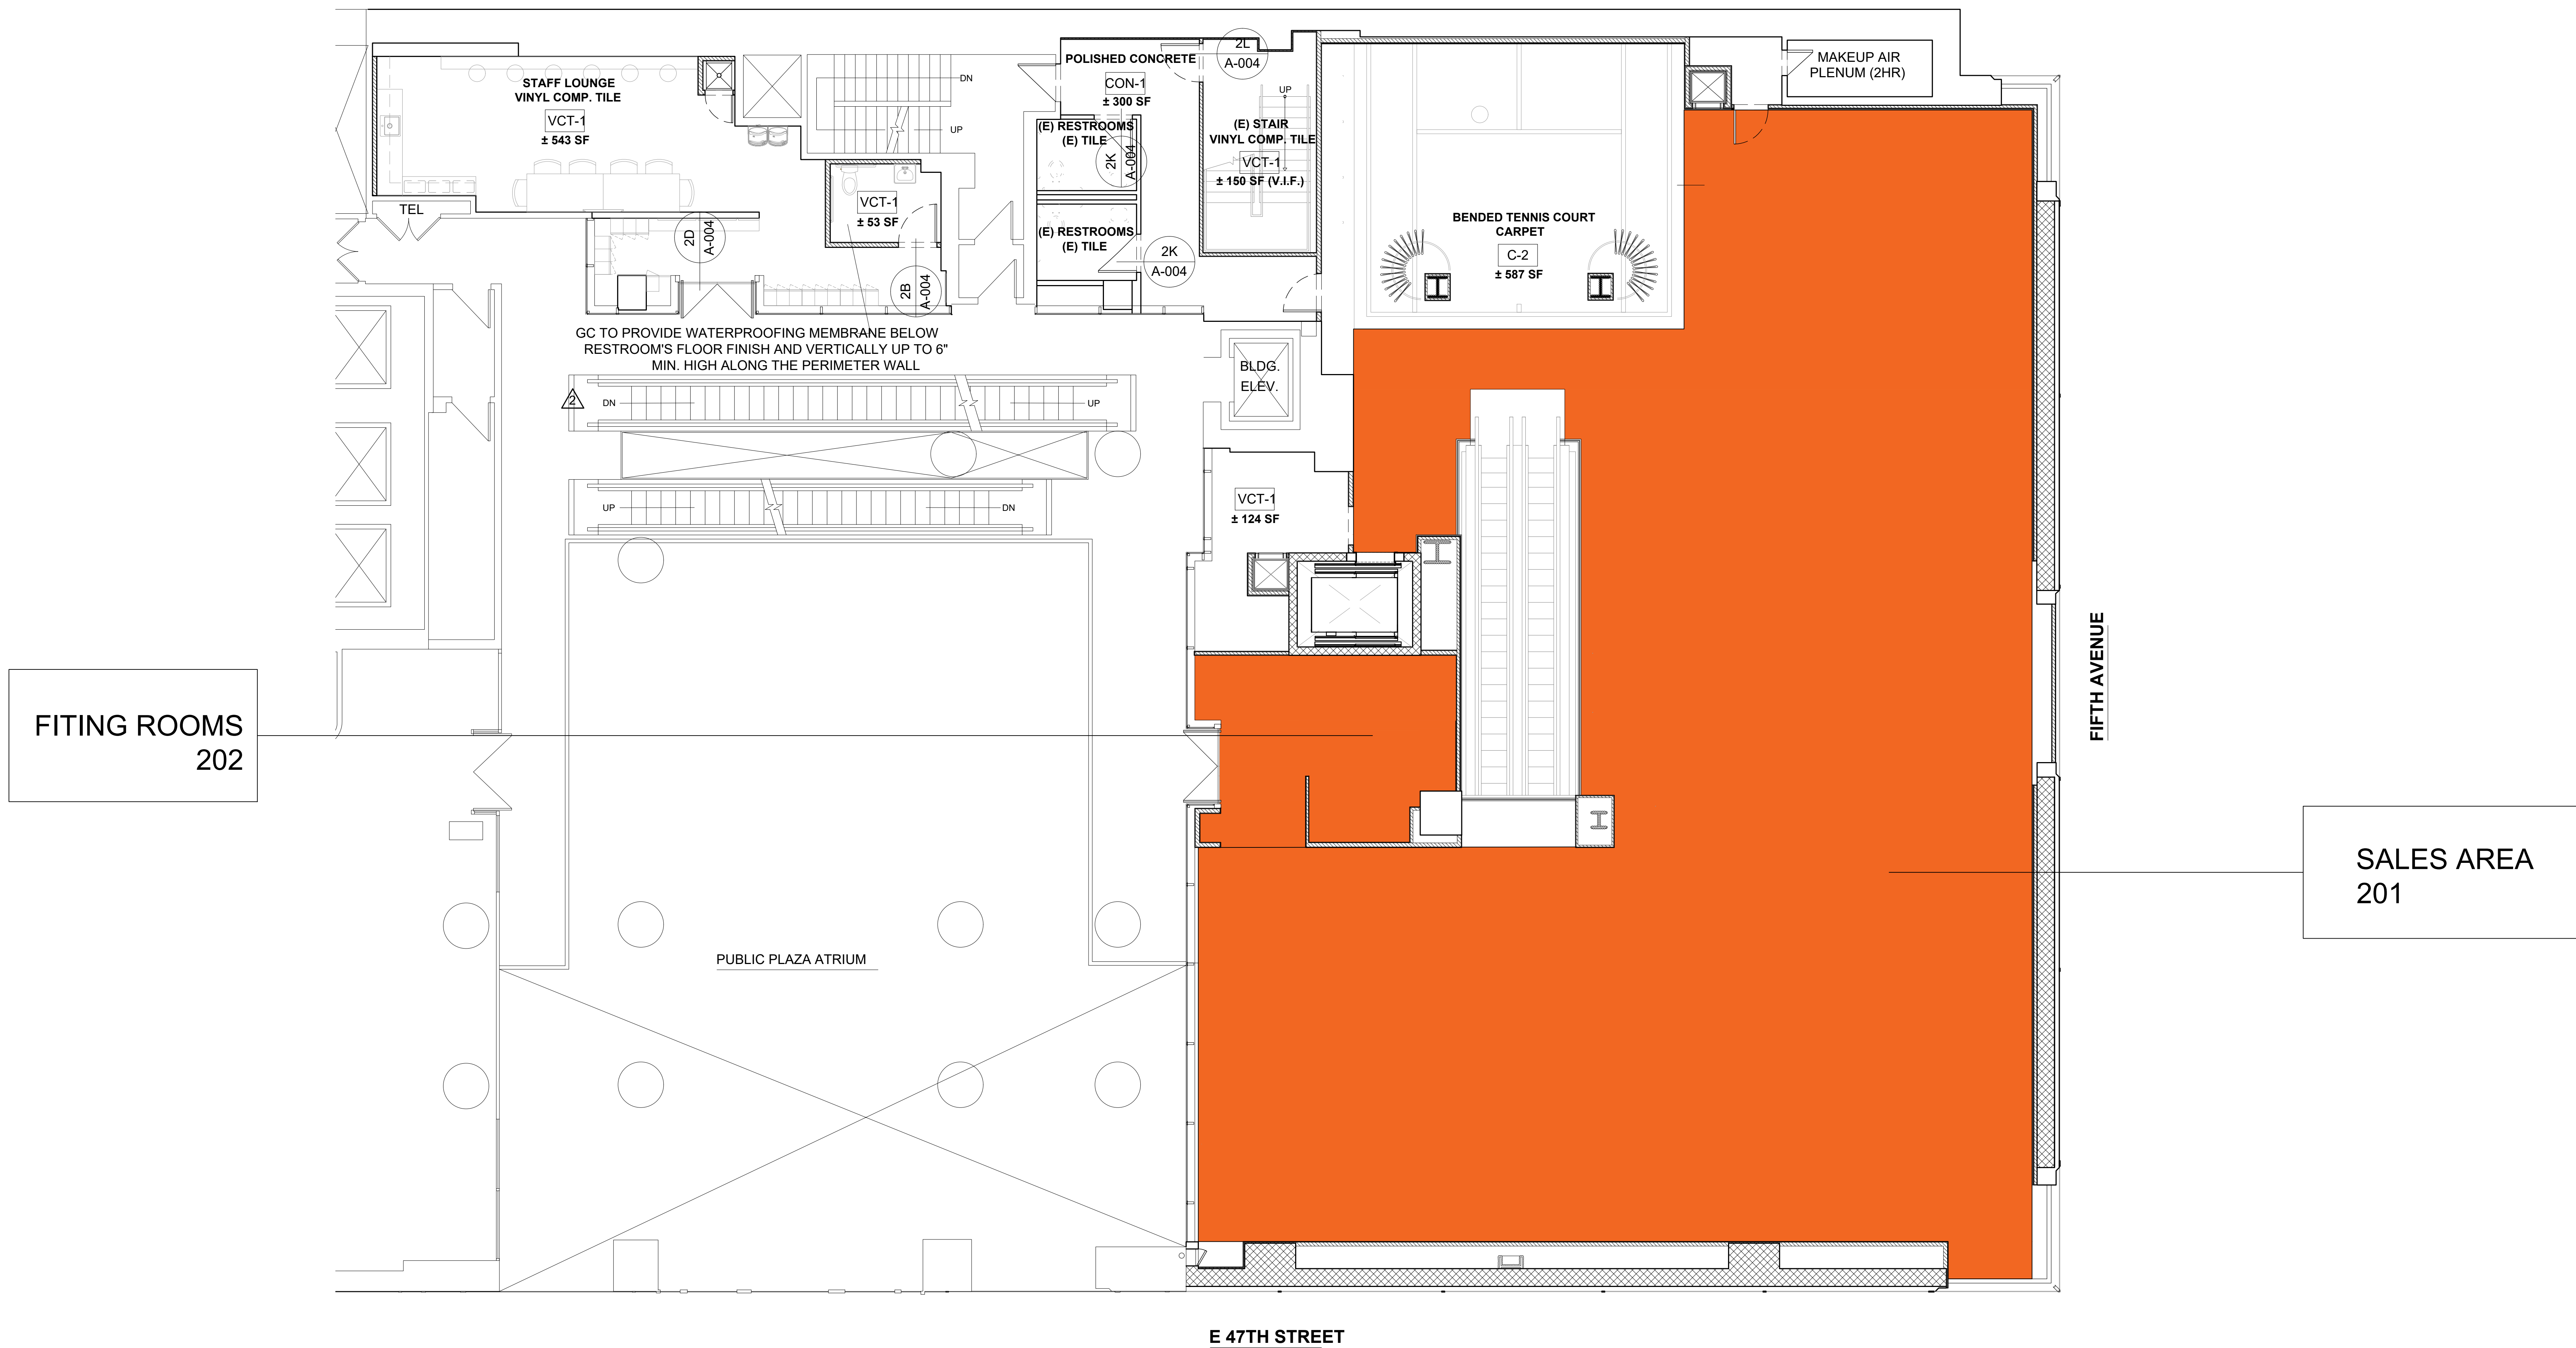

AUSTRO TILE & STONE, LLC
30-25 93RD STREET
EAST ELMHURST, NY 11369

CONTRACTOR:
JRM CONSTRUCTION
MANAGEMENT, LLC
242 WEST 36TH STREET
11TH FLOOR
NEW YORK, NY 10018

INTERIOR DESIGNER:

ISSUE FOR APPROVAL 09/09/24
ISSUE NAME DATE

PROJECTS:
KENNETH PARK ARCHITECTS
360 LEXINGTON AVENUE
NEW YORK, NY 10017PHONE:
212-599-0044

PROJECT NAME:
LACOSTE
575 5TH AVENUE
NEW YORK, NY 10017

SHEET NAME:
KEYPLAN
2ND FLOOR

DATE:
PROJECT NO.:
PRINCIPAL:
DRAWING BY:
CHECKED BY:
SCALE:
DWG No.:
KY-002
3 of 21

LOCATION

Architectural floor plan of the 3rd floor. The plan includes a large Public Plaza Atrium, a Storage Area, a Manager Room, Showroom Storage #1, Showroom Restroom (W) 306, Showroom Restroom (M) 306, and Showroom Pantry 311. It also shows an adjacent tenant area, stairs, and various tile specifications like VCT-1 and Vinyl Comp. Tile. A keyplan at the bottom right shows the building's location on Fifth Avenue.

AUSTRO TILE & STONE, LLC
30-25 93RD STREET
EAST ELMHURST, NY 11369

CONTRACTOR:
JRM CONSTRUCTION
MANAGEMENT, LLC
242 WEST 36TH STREET
11TH FLOOR
NEW YORK, NY 10018

INTERIOR DESIGNER:

ISSUE FOR APPROVAL: 09/09/24
ISSUE NAME: DATE:

ARCHITECT:
KENNETH PARK ARCHITECTS
360 LEXINGTON AVENUE
NEW YORK, NY 10017
PHONE: 212-599-0044

PROJECT NAME:
LACOSTE
575 5TH AVENUE
NEW YORK, NY 10017

SHEET NAME:
KEYPLAN
3RD FLOOR

DATE:
PROJECT NO.:
PRINCIPAL:
DRAWING BY:
CHECKED BY:
SCALE:
DWG No.:
KY-003
4 of 2

DATE: _____
PROJECT NO.: _____
PRINCIPAL: _____
DRAWING BY: _____
CHECKED BY: _____
SCALE: _____
DWG No.: _____
KY-003
4 of 21

SHOWROOM RESTROOM (M)
306

WOMEN

FUTURE ADJACENT TENANT

STARTING POINT

AUSTRO TILE & STONE, LLC
30-25 93RD STREET
EAST ELMHURST, NY 11369

BLDG.
ELEV.

UP

DN

FIT. RM.
CARPET
C-1

VCT-2
± 78 SF

FIFTH AVENUE

WEATHERPROOF
FLOOR MAT
± 216 SF
C-4

E 47TH STREET

01 PLAN: 1ST FLOOR

CONTRACTOR:
JRM CONSTRUCTION
MANAGEMENT, LLC
242 WEST 36TH STREET
11TH FLOOR
NEW YORK, NY 10018

INTERIOR DESIGNER:


ISSUE FOR APPROVAL 09/09/24
ISSUE NAME DATE

ARCHITECT:
KENNETH PARK ARCHITECTS
360 LEXINGTON AVENUE
NEW YORK, NY 10017PHONE:
212-599-0044

PROJECT NAME:
LACOSTE
575 5TH AVENUE
NEW YORK, NY 10017

SHEET NAME:
FLOOR PLAN
1ST FLOOR

DATE:
PROJECT NO.:
PRINCIPAL:
DRAWING BY:
CHECKED BY:
SCALE:
DWG No.:
T-100
5 of 21

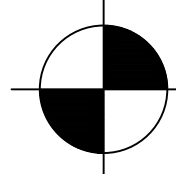

STARTING POINT

± 78 SF

AUSTRO TILE & STONE, LLC
30-25 93RD STREET
EAST ELMHURST, NY 11369

WEATHERPROOF
FLOOR MAT
± 216 SF

C-4

CONTRACTOR:
JRM CONSTRUCTION
MANAGEMENT, LLC
242 WEST 36TH STREET
11TH FLOOR
NEW YORK, NY 10018

INTERIOR DESIGNER:


ISSUE FOR APPROVAL 09/09/24
ISSUE NAME DATE

ARCHITECT:
KENNETH PARK ARCHITECTS
360 LEXINGTON AVENUE
NEW YORK, NY 10017PHONE:
212-599-0044

PROJECT NAME:
LACOSTE
575 5TH AVENUE
NEW YORK, NY 10017

SHEET NAME:
ENLARGED FLOOR PLAN
1ST FLOOR

DATE:
PROJECT NO.:
PRINCIPAL:
DRAWING BY:
CHECKED BY:
SCALE:
DWG No.:
T-101
5 of 21

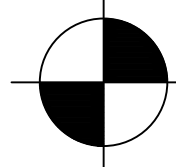

STARTING POINT

FIT. RM.
CARPET

C-1

CONCRETE BY OTHERS

VCT-2
± 78 SF

FIFTH AVENUE

CONCRETE BY OTHERS

WEATHERPROOF
FLOOR MAT
± 216 SF

C-4

METAL STRIP
SCHLUTER SYSTEMS
DECO SERIES
STAINLESS STEEL (TYP.)

T-1

T-1

3 1/4"

EQ

EQ

EQ

9'-5"

6'-6 1/4"

T-1 CUSTOM MANUFACTURED TREADS

01
3/4"x11'-0"

ENLARGED PLAN: 1ST FLOOR

AUSTRO TILE & STONE, LLC
30-25 93RD STREET
EAST ELMHURST, NY 11369

CONTRACTOR:
JRM CONSTRUCTION
MANAGEMENT, LLC
242 WEST 36TH STREET
11TH FLOOR
NEW YORK, NY 10018

INTERIOR DESIGNER:


ISSUE FOR APPROVAL 09/09/24
ISSUE NAME DATE

ARCHITECT:
KENNETH PARK ARCHITECTS
360 LEXINGTON AVENUE
NEW YORK, NY 10017PHONE:
212-599-0044

PROJECT NAME:
LACOSTE
575 5TH AVENUE
NEW YORK, NY 10017

SHEET NAME:
ENLARGED FLOOR PLAN
1ST FLOOR

DATE:
PROJECT NO.:
PRINCIPAL:
DRAWING BY:
CHECKED BY:
SCALE:
DWG No.:
T-102
5 of 21

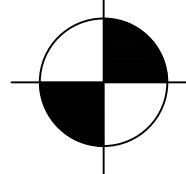

STARTING POINT

AUSTRO TILE & STONE, LLC
30-25 93RD STREET
EAST ELMHURST, NY 11369

CONTRACTOR:
JRM CONSTRUCTION
MANAGEMENT, LLC
242 WEST 36TH STREET
11TH FLOOR
NEW YORK, NY 10018

INTERIOR DESIGNER:

ISSUE FOR APPROVAL 09/09/24
ISSUE NAME DATE

ARCHITECT:
KENNETH PARK ARCHITECTS
360 LEXINGTON AVENUE
NEW YORK, NY 10017PHONE:
212-599-0044

PROJECT NAME:
LACOSTE
575 5TH AVENUE
NEW YORK, NY 10017

SHEET NAME:
ENLARGED FLOOR PLAN
1ST FLOOR

DATE:
PROJECT NO.:
PRINCIPAL:
DRAWING BY:
CHECKED BY:
SCALE:
DWG No.:
T-103
5 of 21

11'-1 1/4"

T-1 9'-5"

6'-6 1/4"

T-1 CUSTOM MANUFACTURED TREADS

50% TYP.

1'-1" TYP.

CUT
FULL TILE
EQ

9'-4 1/4"

FULL TILE

CUT

TREAD 7/LANDING

TREAD 6

TREAD 5

TREAD 4

TREAD 3


TREAD 2

TREAD 1

1'-1"

TILE STARTING POINT

T-1 CUSTOM MANUFACTURED TREADS

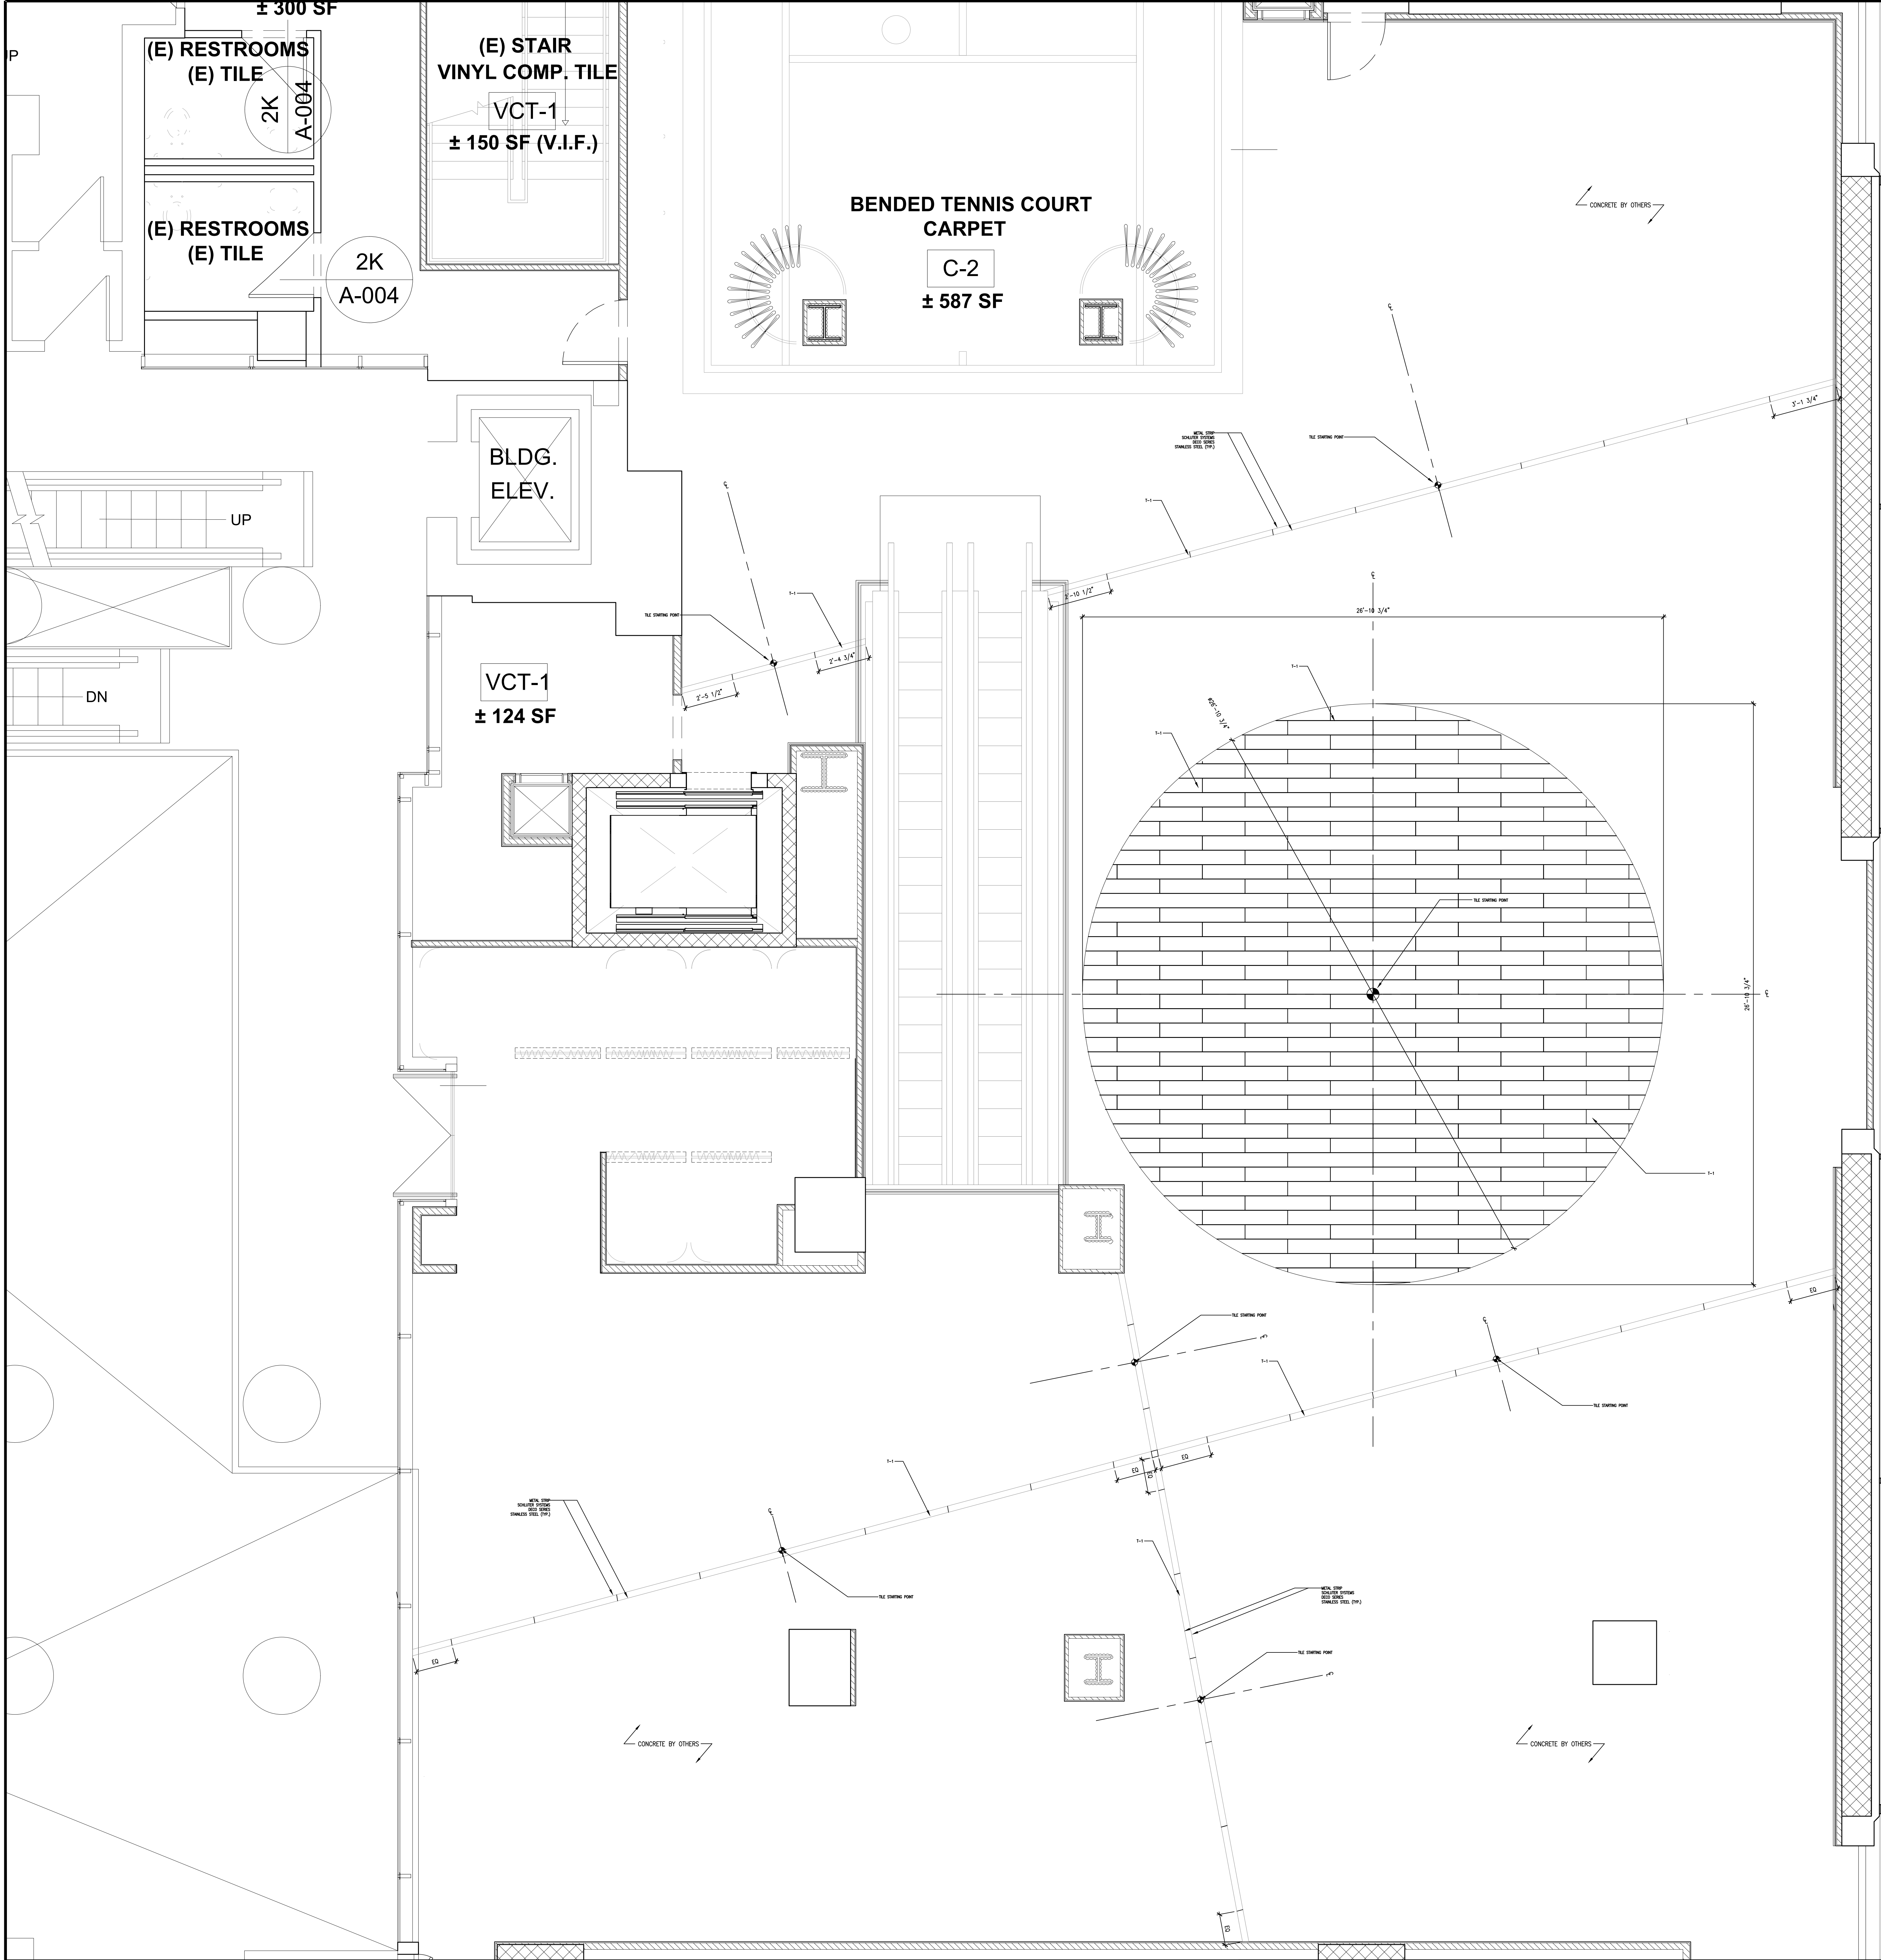

AUSTRO TILE & STONE, LLC
30-25 93RD STREET
EAST ELMHURST, NY 11369

CONTRACTOR:
JRM CONSTRUCTION
MANAGEMENT, LLC
242 WEST 36TH STREET
11TH FLOOR
NEW YORK, NY 10018

INTERIOR DESIGNER:

ISSUE FOR APPROVAL 09/09/24
ISSUE NAME DATE

ARCHITECT:
KENNETH PARK ARCHITECTS
360 LEXINGTON AVENUE
NEW YORK, NY 10017
PHONE: 212-599-0044

PROJECT NAME:
LACOSTE
575 5TH AVENUE
NEW YORK, NY 10017

SHEET NAME:
ENLARGED FLOOR PLAN
2ND FLOOR

DATE:
PROJECT NO.:
PRINCIPAL:
DRAWING BY:
CHECKED BY:
SCALE:
DWG No.:
T-104
6 of 21

FIFTH AVENUE



AUSTRO TILE & STONE, LLC
30-25 93RD STREET
EAST ELMHURST, NY 11369

CONTRACTOR:
JRM CONSTRUCTION
MANAGEMENT, LLC
242 WEST 36TH STREET
11TH FLOOR
NEW YORK, NY 10018

INTERIOR DESIGNER:

[illegible]

ISSUE FOR APPROVAL	09/09/24
ISSUE NAME	DATE

ARCHITECT:
KENNETH PARK ARCHITECTS
360 LEXINGTON AVENUE
NEW YORK, NY 10017PHONE:
212-599-0044

PROJECT NAME:
LACOSTE
575 5TH AVENUE
NEW YORK, NY 10017

SHEET NAME

ENLARGED FLOOR PLAN
2ND FLOOR

DATE: _____
PROJECT NO.: _____
PRINCIPAL: _____
DRAWING BY: _____
CHECKED BY: _____
SCALE: _____
DWG No.: T-105
6 of 21



CONTRACTOR:

JRM CONSTRUCTION
MANAGEMENT, LLC
242 WEST 36TH STREET
11TH FLOOR
NEW YORK, NY 10018

INTERIOR DESIGNER:

[illegible]

ISSUE FOR APPROVAL	09/09/24
ISSUE NAME	DATE

KENNETH PARK ARCHITECTS
360 LEXINGTON AVENUE
NEW YORK, NY 10017PHONE:
212-599-0044


PROJECT NAME:

LACOSTE
575 5TH AVENUE
NEW YORK, NY 10017

SHEET NAME:

ENLARGED FLOOR PLAN
2ND FLOOR

DATE: _____
PROJECT NO.: _____
PRINCIPAL: _____
DRAWING BY: _____
CHECKED BY: _____
SCALE: _____
DWG No.: _____
T-106
6 of 21

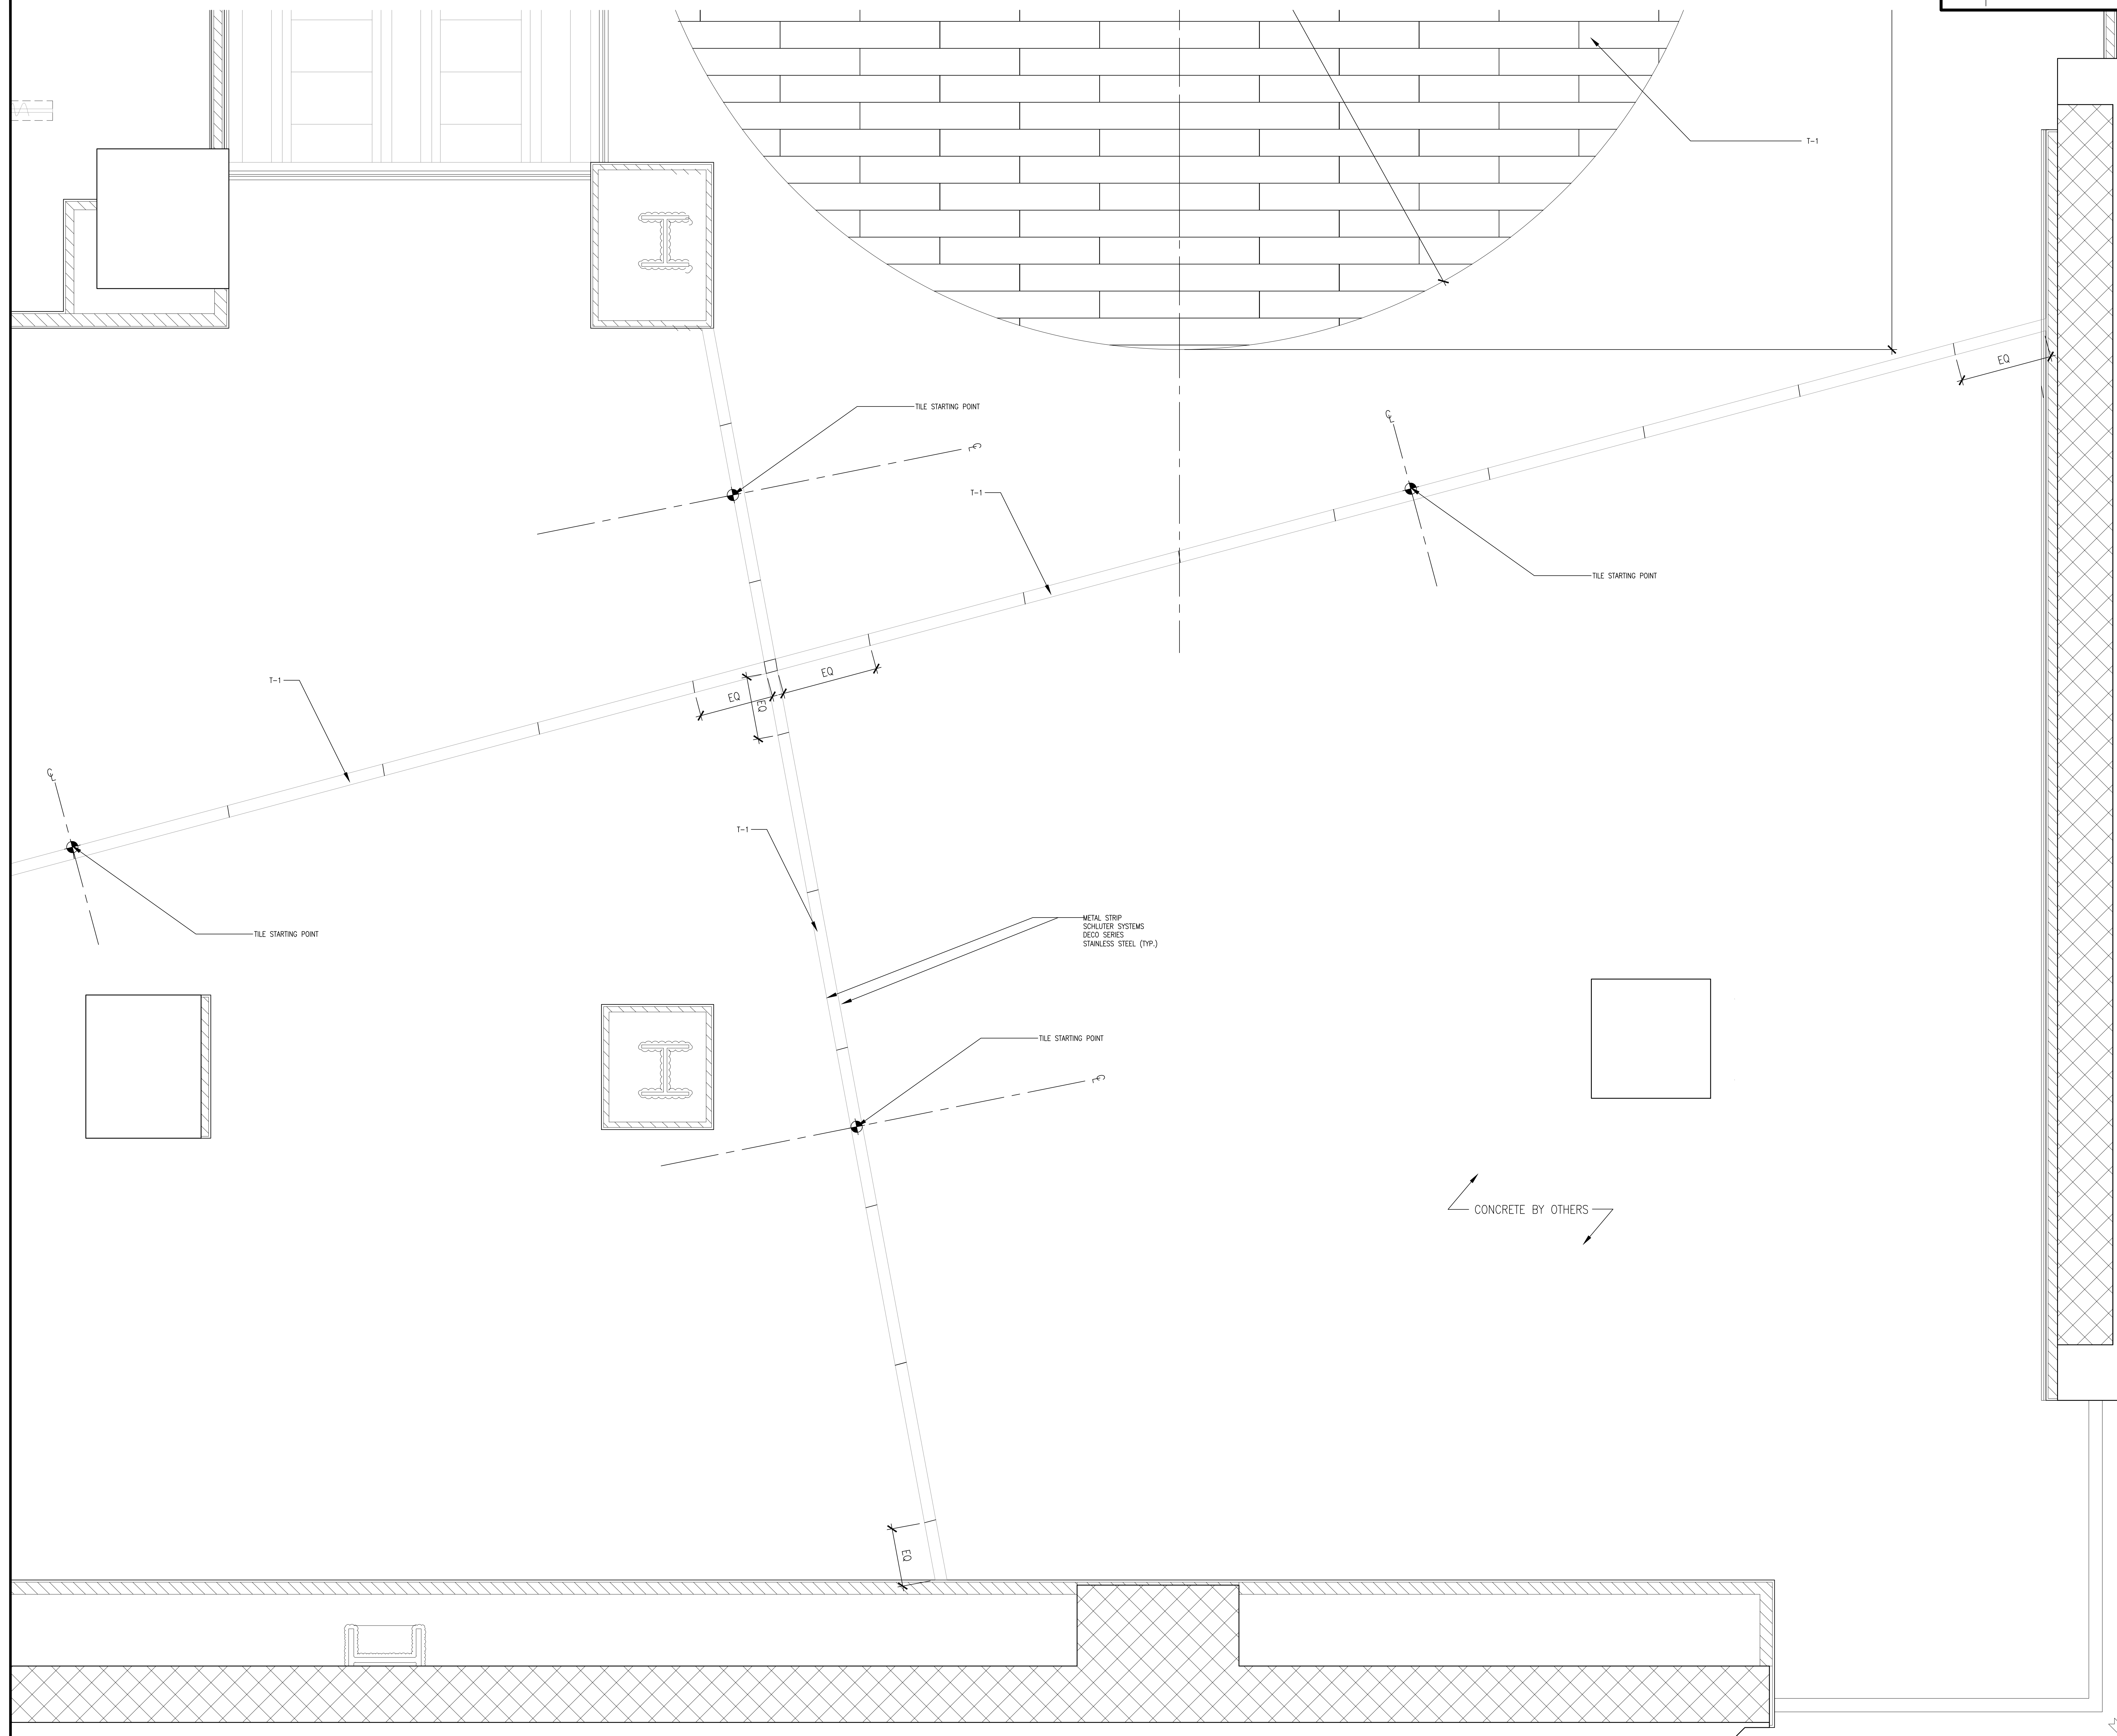



AUSTRO TILE & STONE, LLC
30-25 93RD STREET
EAST ELMHURST, NY 11369

CONTRACTOR:
JRM CONSTRUCTION
MANAGEMENT, LLC
242 WEST 36TH STREET
11TH FLOOR
NEW YORK, NY 10018

INTERIOR DESIGNER:

[illegible]

ISSUE FOR APPROVAL	09/09/24
ISSUE NAME	DATE

ARCHITECT:

KENNETH PARK ARCHITECTS
360 LEXINGTON AVENUE
NEW YORK, NY 10017PHONE:
212-599-0044

PROJECT NAME:

LACOSTE
575 5TH AVENUE
NEW YORK, NY 10017

(SHEET NAME)

ENLARGED FLOOR PLAN
2ND FLOOR

DATE: _____
PROJECT NO.: _____
PRINCIPAL: _____
DRAWING BY: _____
CHECKED BY: _____
SCALE: _____
DWG No.: T-107
6 of 21

6 of 21

FIFTH AVENUE

26'-10 3/4"

2'-10 1/2"

[1—

I-1-

026-1051

T-1—

— TILE STARTING POINT

26'-10 3/4"

— 101 —

50

—TILE STARTING POINT

I-1-

—TILE STARTING POINT

01
3/4"=1'-0"

PLAN: 2ND FLOOR



STARTING POINT

CONTRACTOR:

JRM CONSTRUCTION
MANAGEMENT, LLC
242 WEST 36TH STREET
11TH FLOOR
NEW YORK, NY 10018

INTERIOR DESIGNER:

ISSUE FOR APPROVAL	09/09/24
ISSUE NAME	DATE

KENNETH PARK ARCHITECTS
360 LEXINGTON AVENUE
NEW YORK, NY 10017PHONE:
212-599-0044


PROJECT NAME:

LACOSTE
575 5TH AVENUE
NEW YORK, NY 10017

HEET NAME:

ENLARGED FLOOR PLAN
2ND FLOOR

DATE: _____
PROJECT NO.: _____
PRINCIPAL: _____
DRAWING BY: _____
CHECKED BY: _____
SCALE: _____
WG No.: _____
T-108
6 of 21

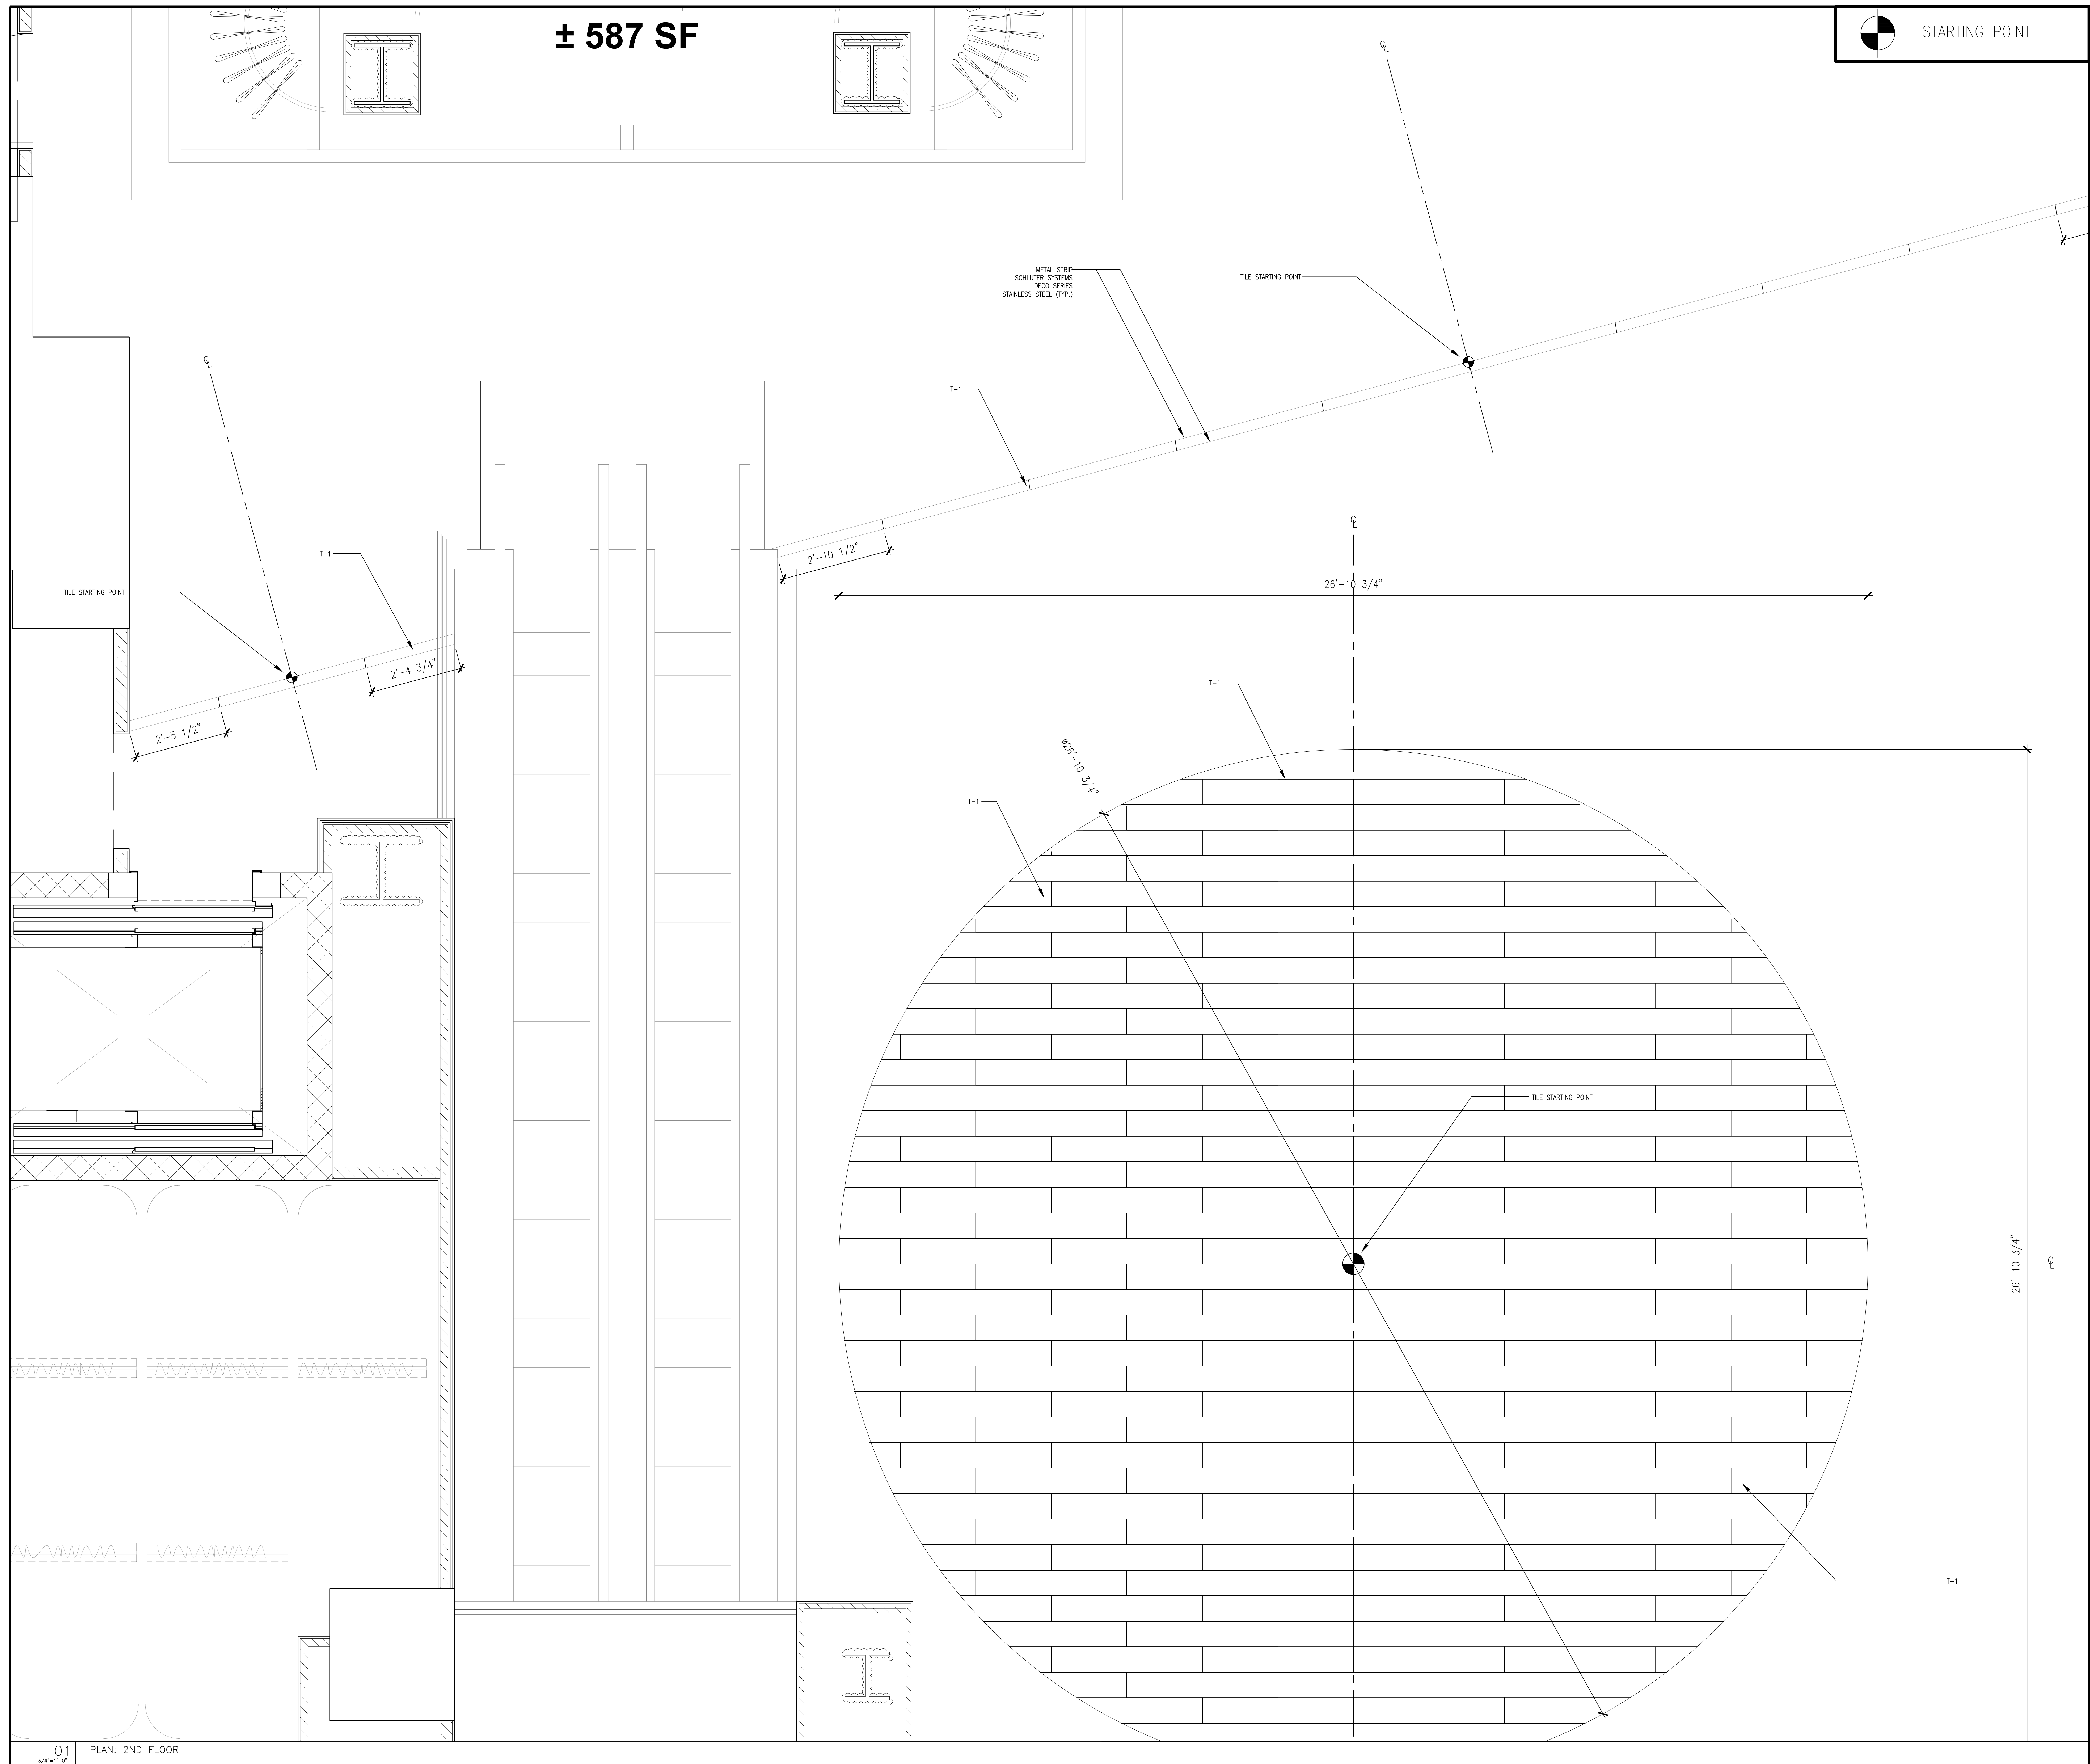

 STARTING POINT

CONCRETE BY OTHERS —

METAL STRIP
SCHLUTER SYSTEMS
DECO SERIES
STAINLESS STEEL (TYP.)

TILE STARTING POINT

3'-1 3/4"

CONTRACTOR:

JRM CONSTRUCTION
MANAGEMENT, LLC
242 WEST 36TH STREET
11TH FLOOR
NEW YORK, NY 10018

INTERIOR DESIGNER:

ISSUE FOR APPROVAL	09/09/24
ISSUE NAME	DATE

KENNETH PARK ARCHITECTS
360 LEXINGTON AVENUE
NEW YORK, NY 10017PHONE:
212-599-0044


PROJECT NAME:

LACOSTE
575 5TH AVENUE
NEW YORK, NY 10017



SHEET NAME:

ENLARGED FLOOR PLAN
2ND FLOOR


DATE: _____
PROJECT NO.: _____
PRINCIPAL: _____
DRAWING BY: _____
CHECKED BY: _____
SCALE: _____
DWG No.: T-109
6 of 21

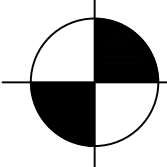


STARTING POINT

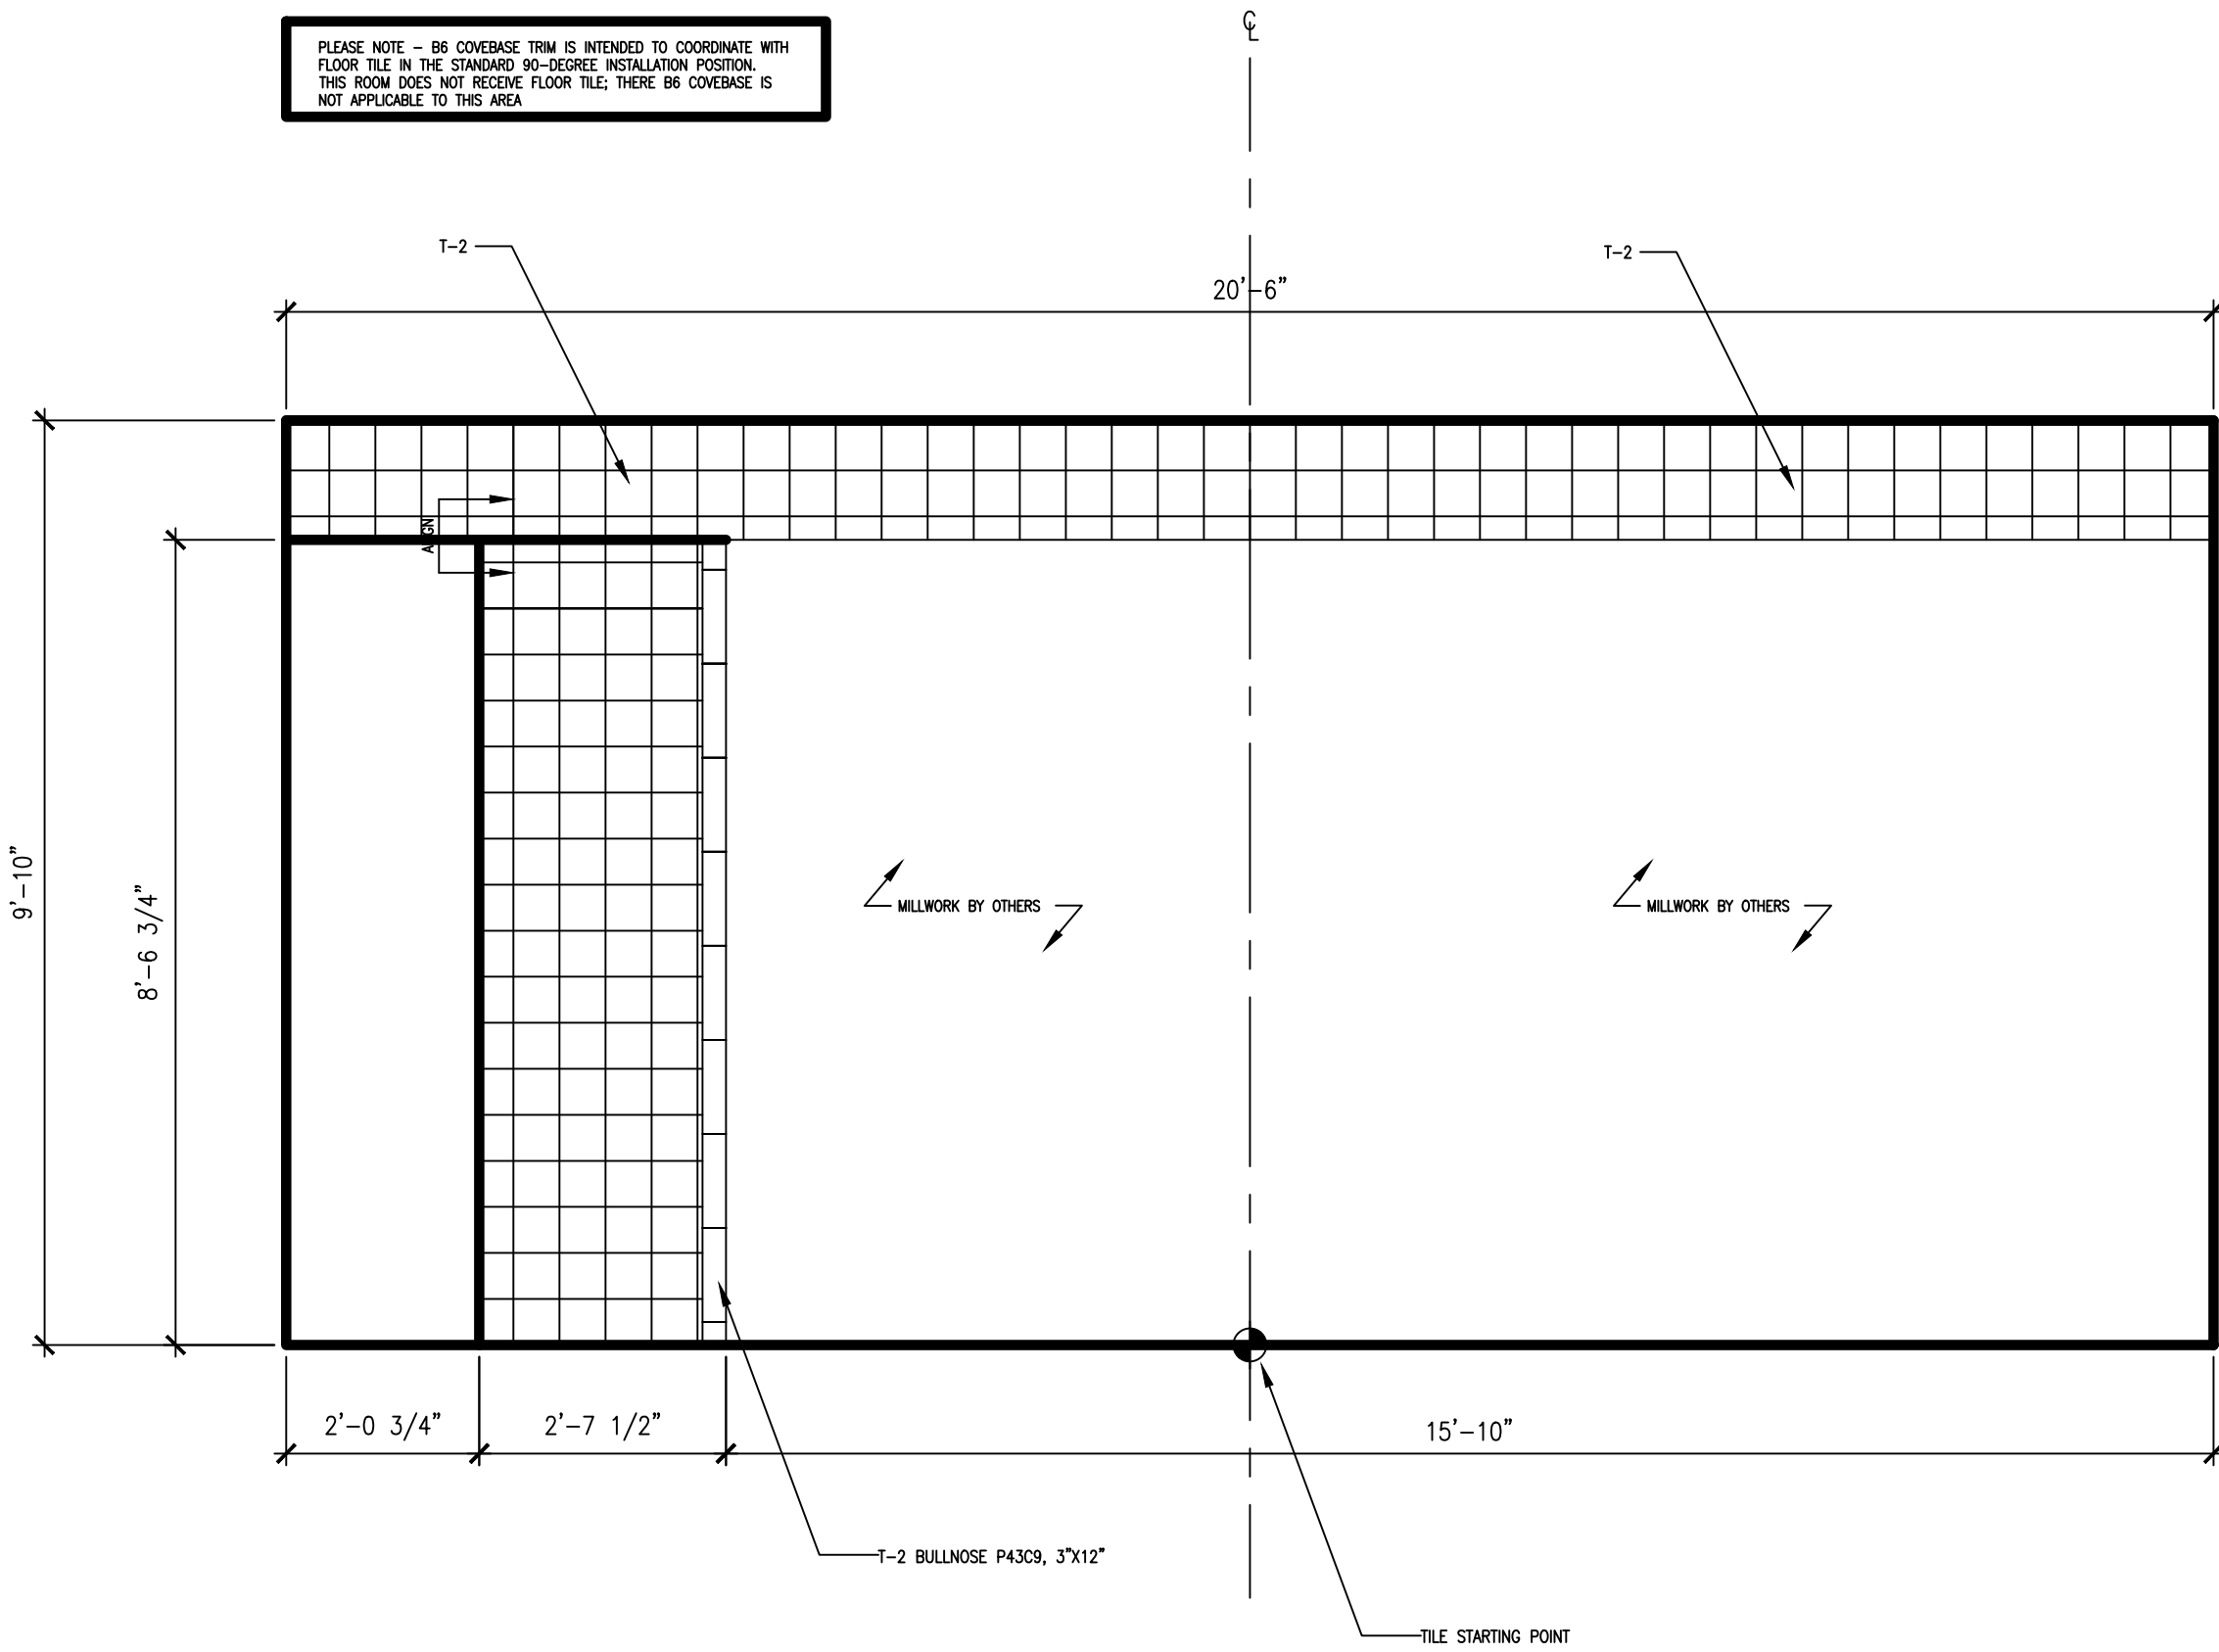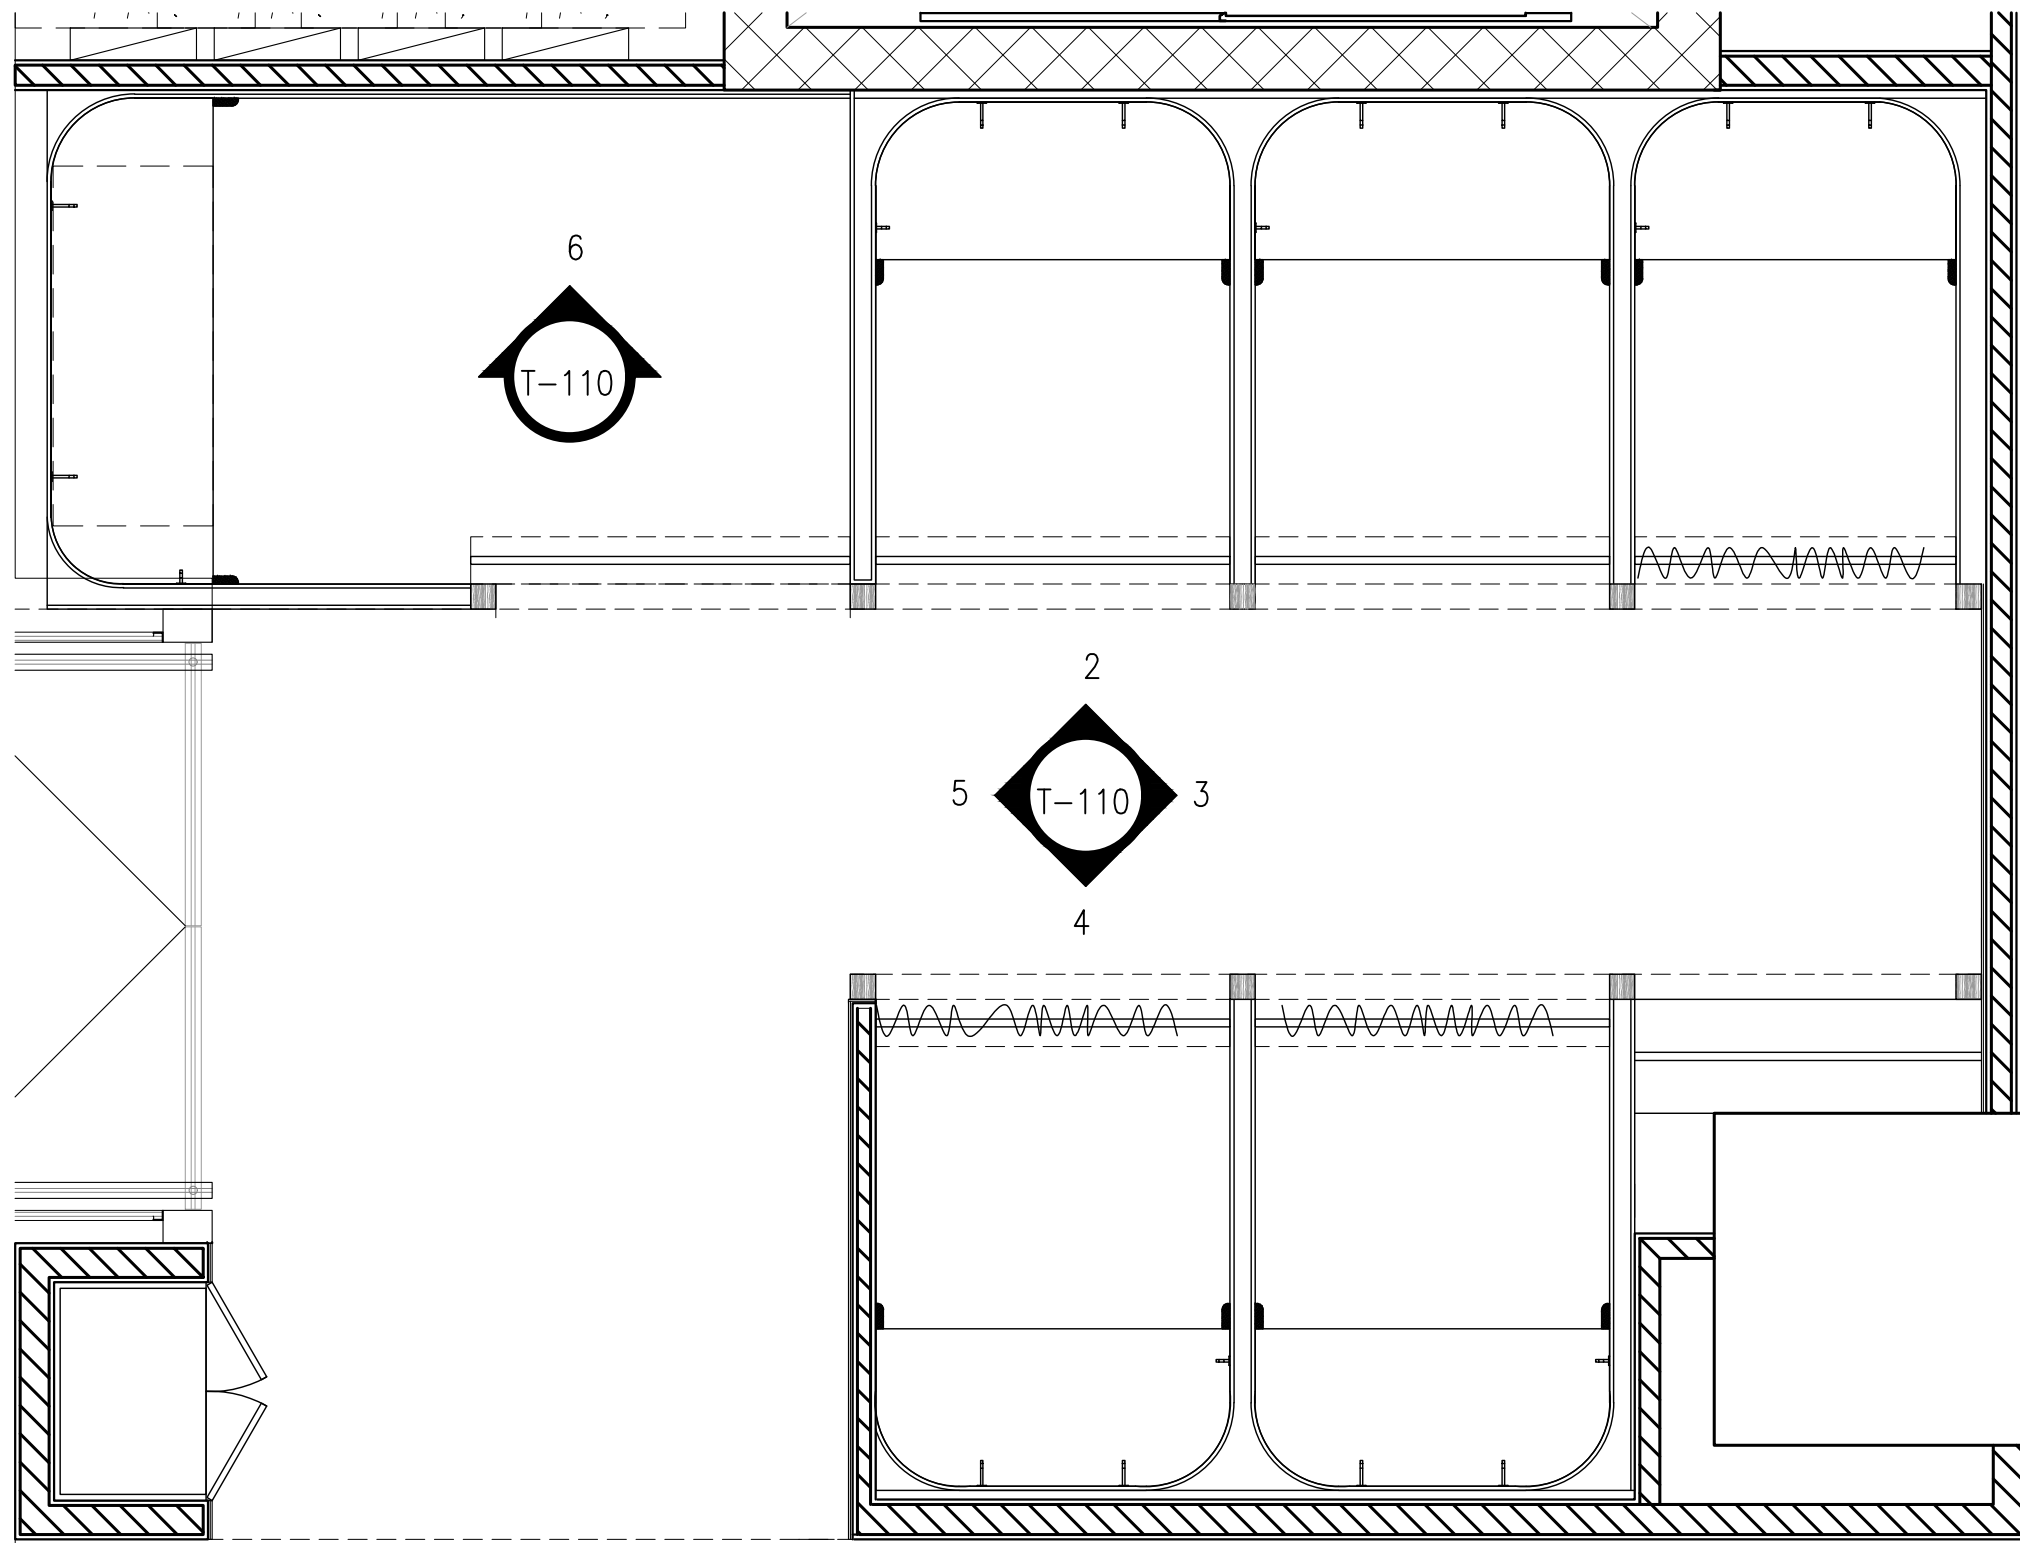


02 ELEVATION: NORTH
1/2"=1'-0"

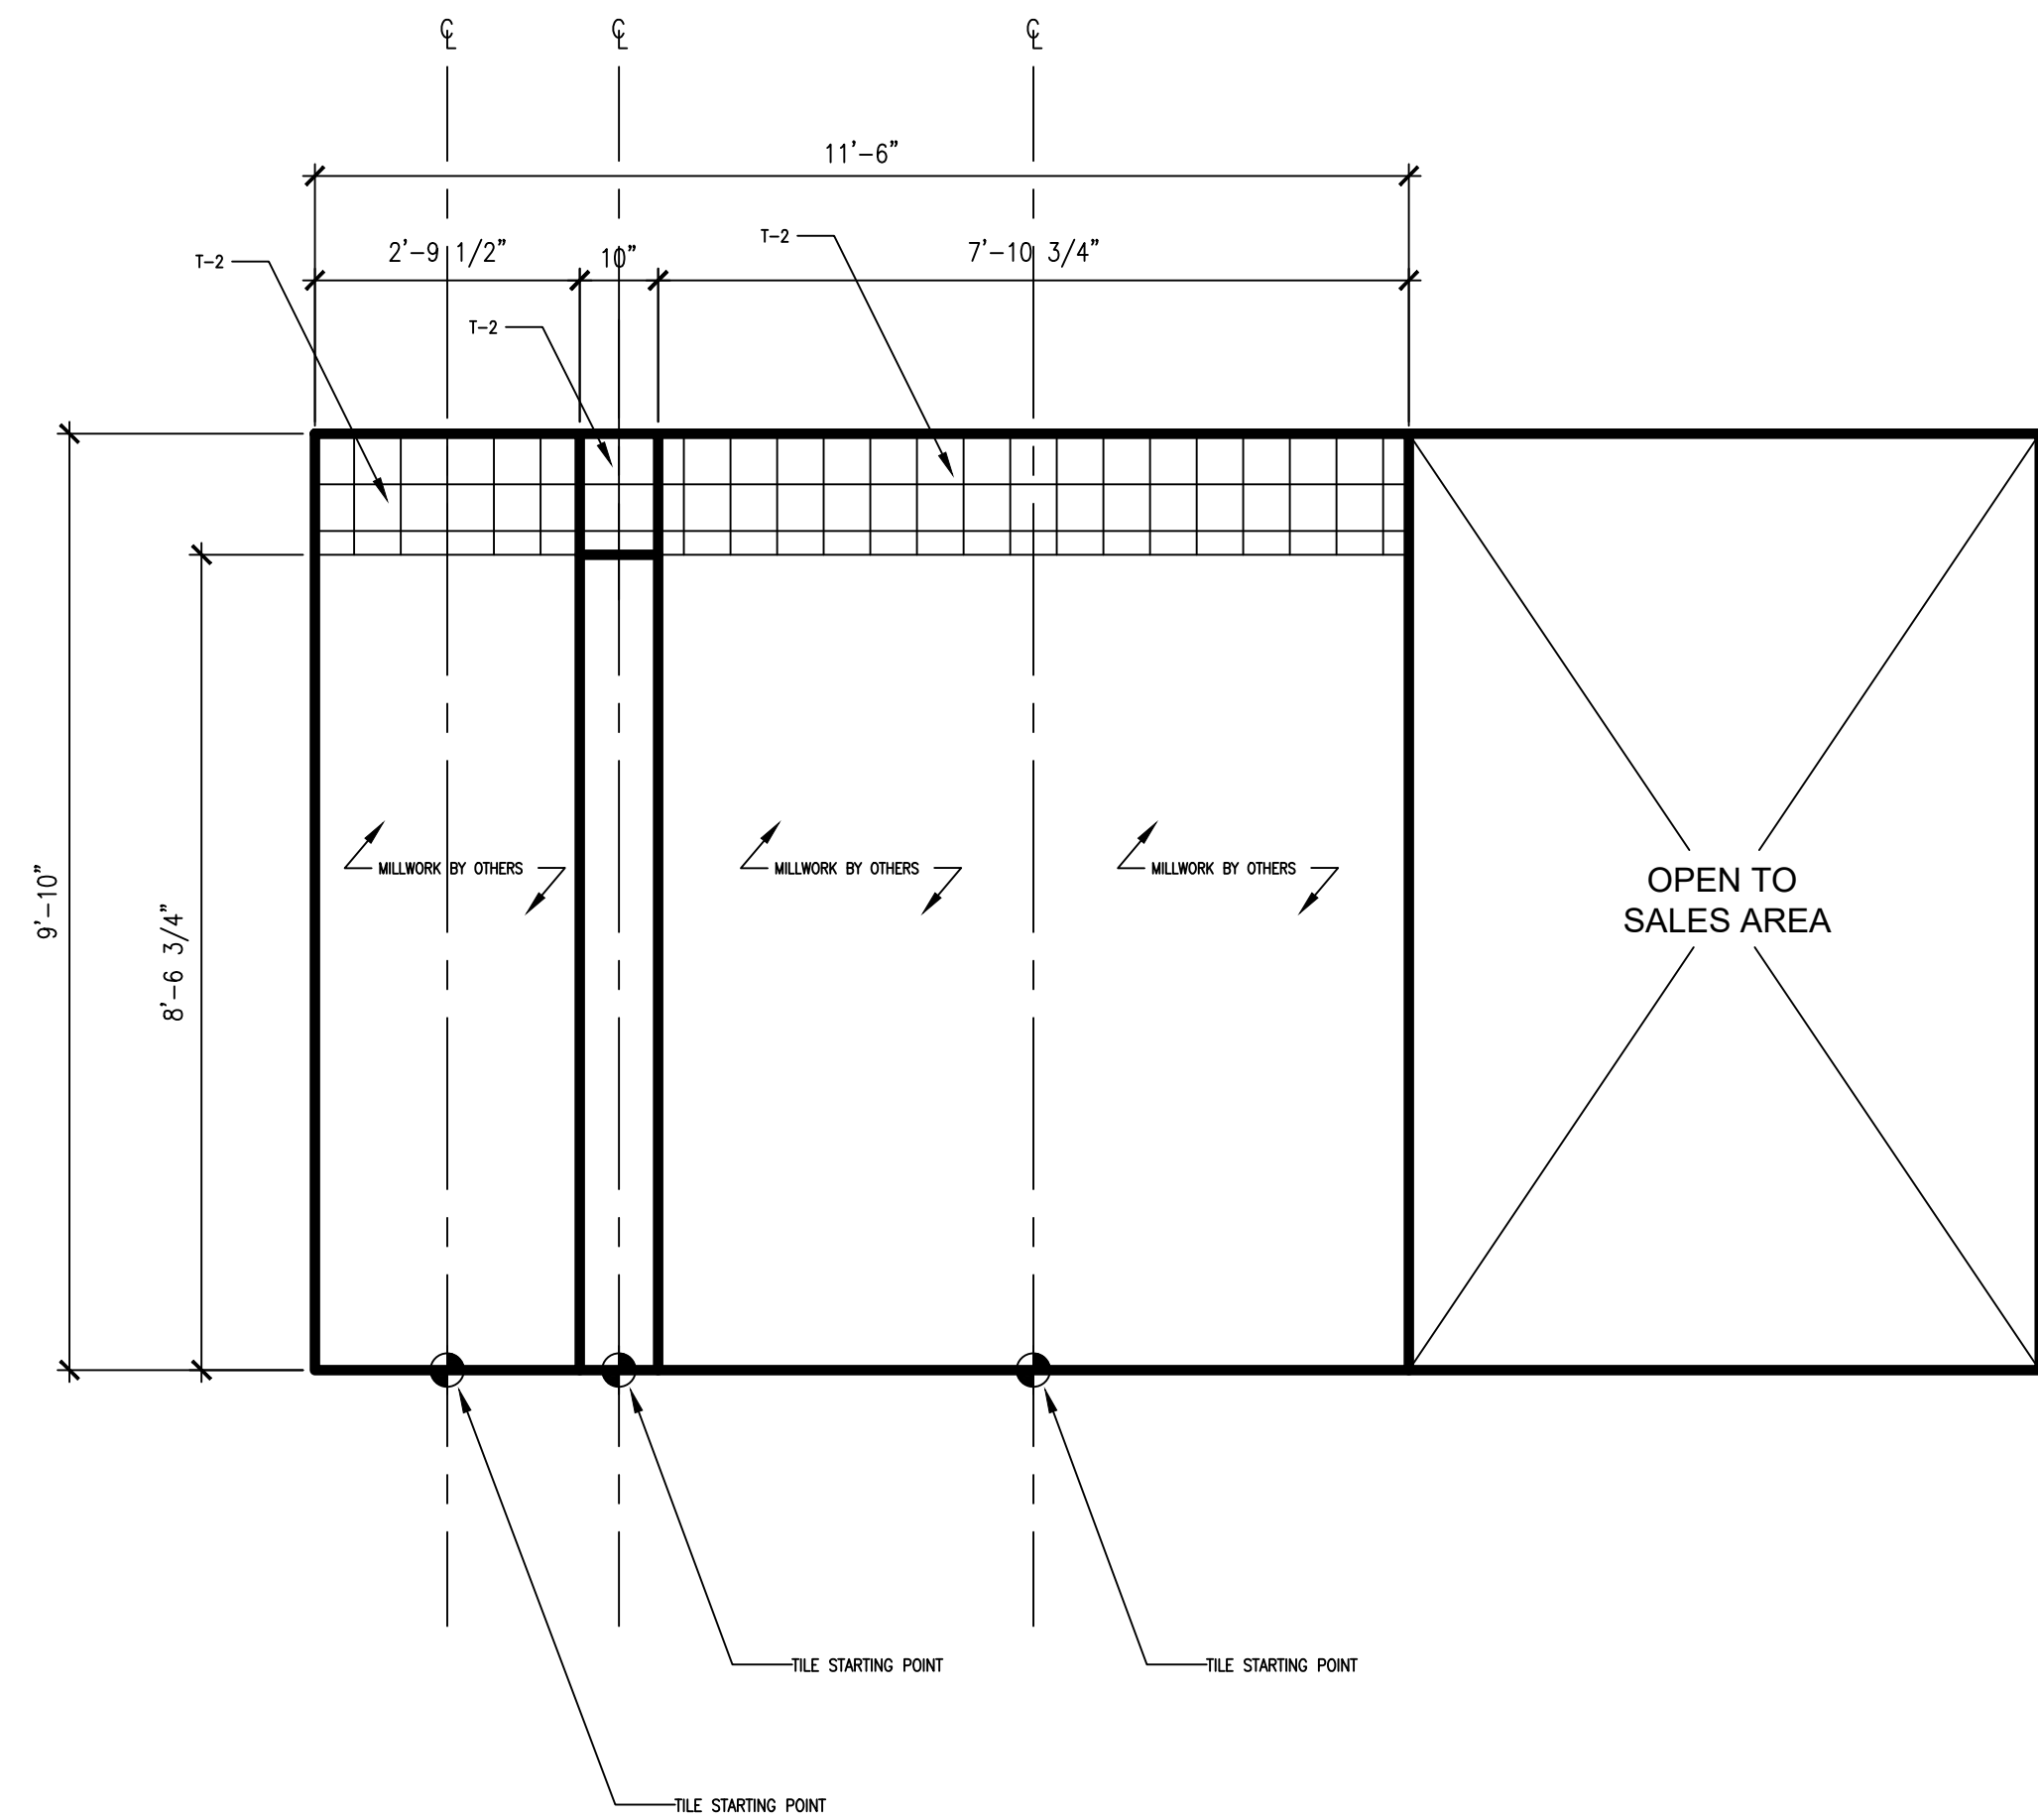


04 ELEVATION: SOUTH
1/2"=1'-0"

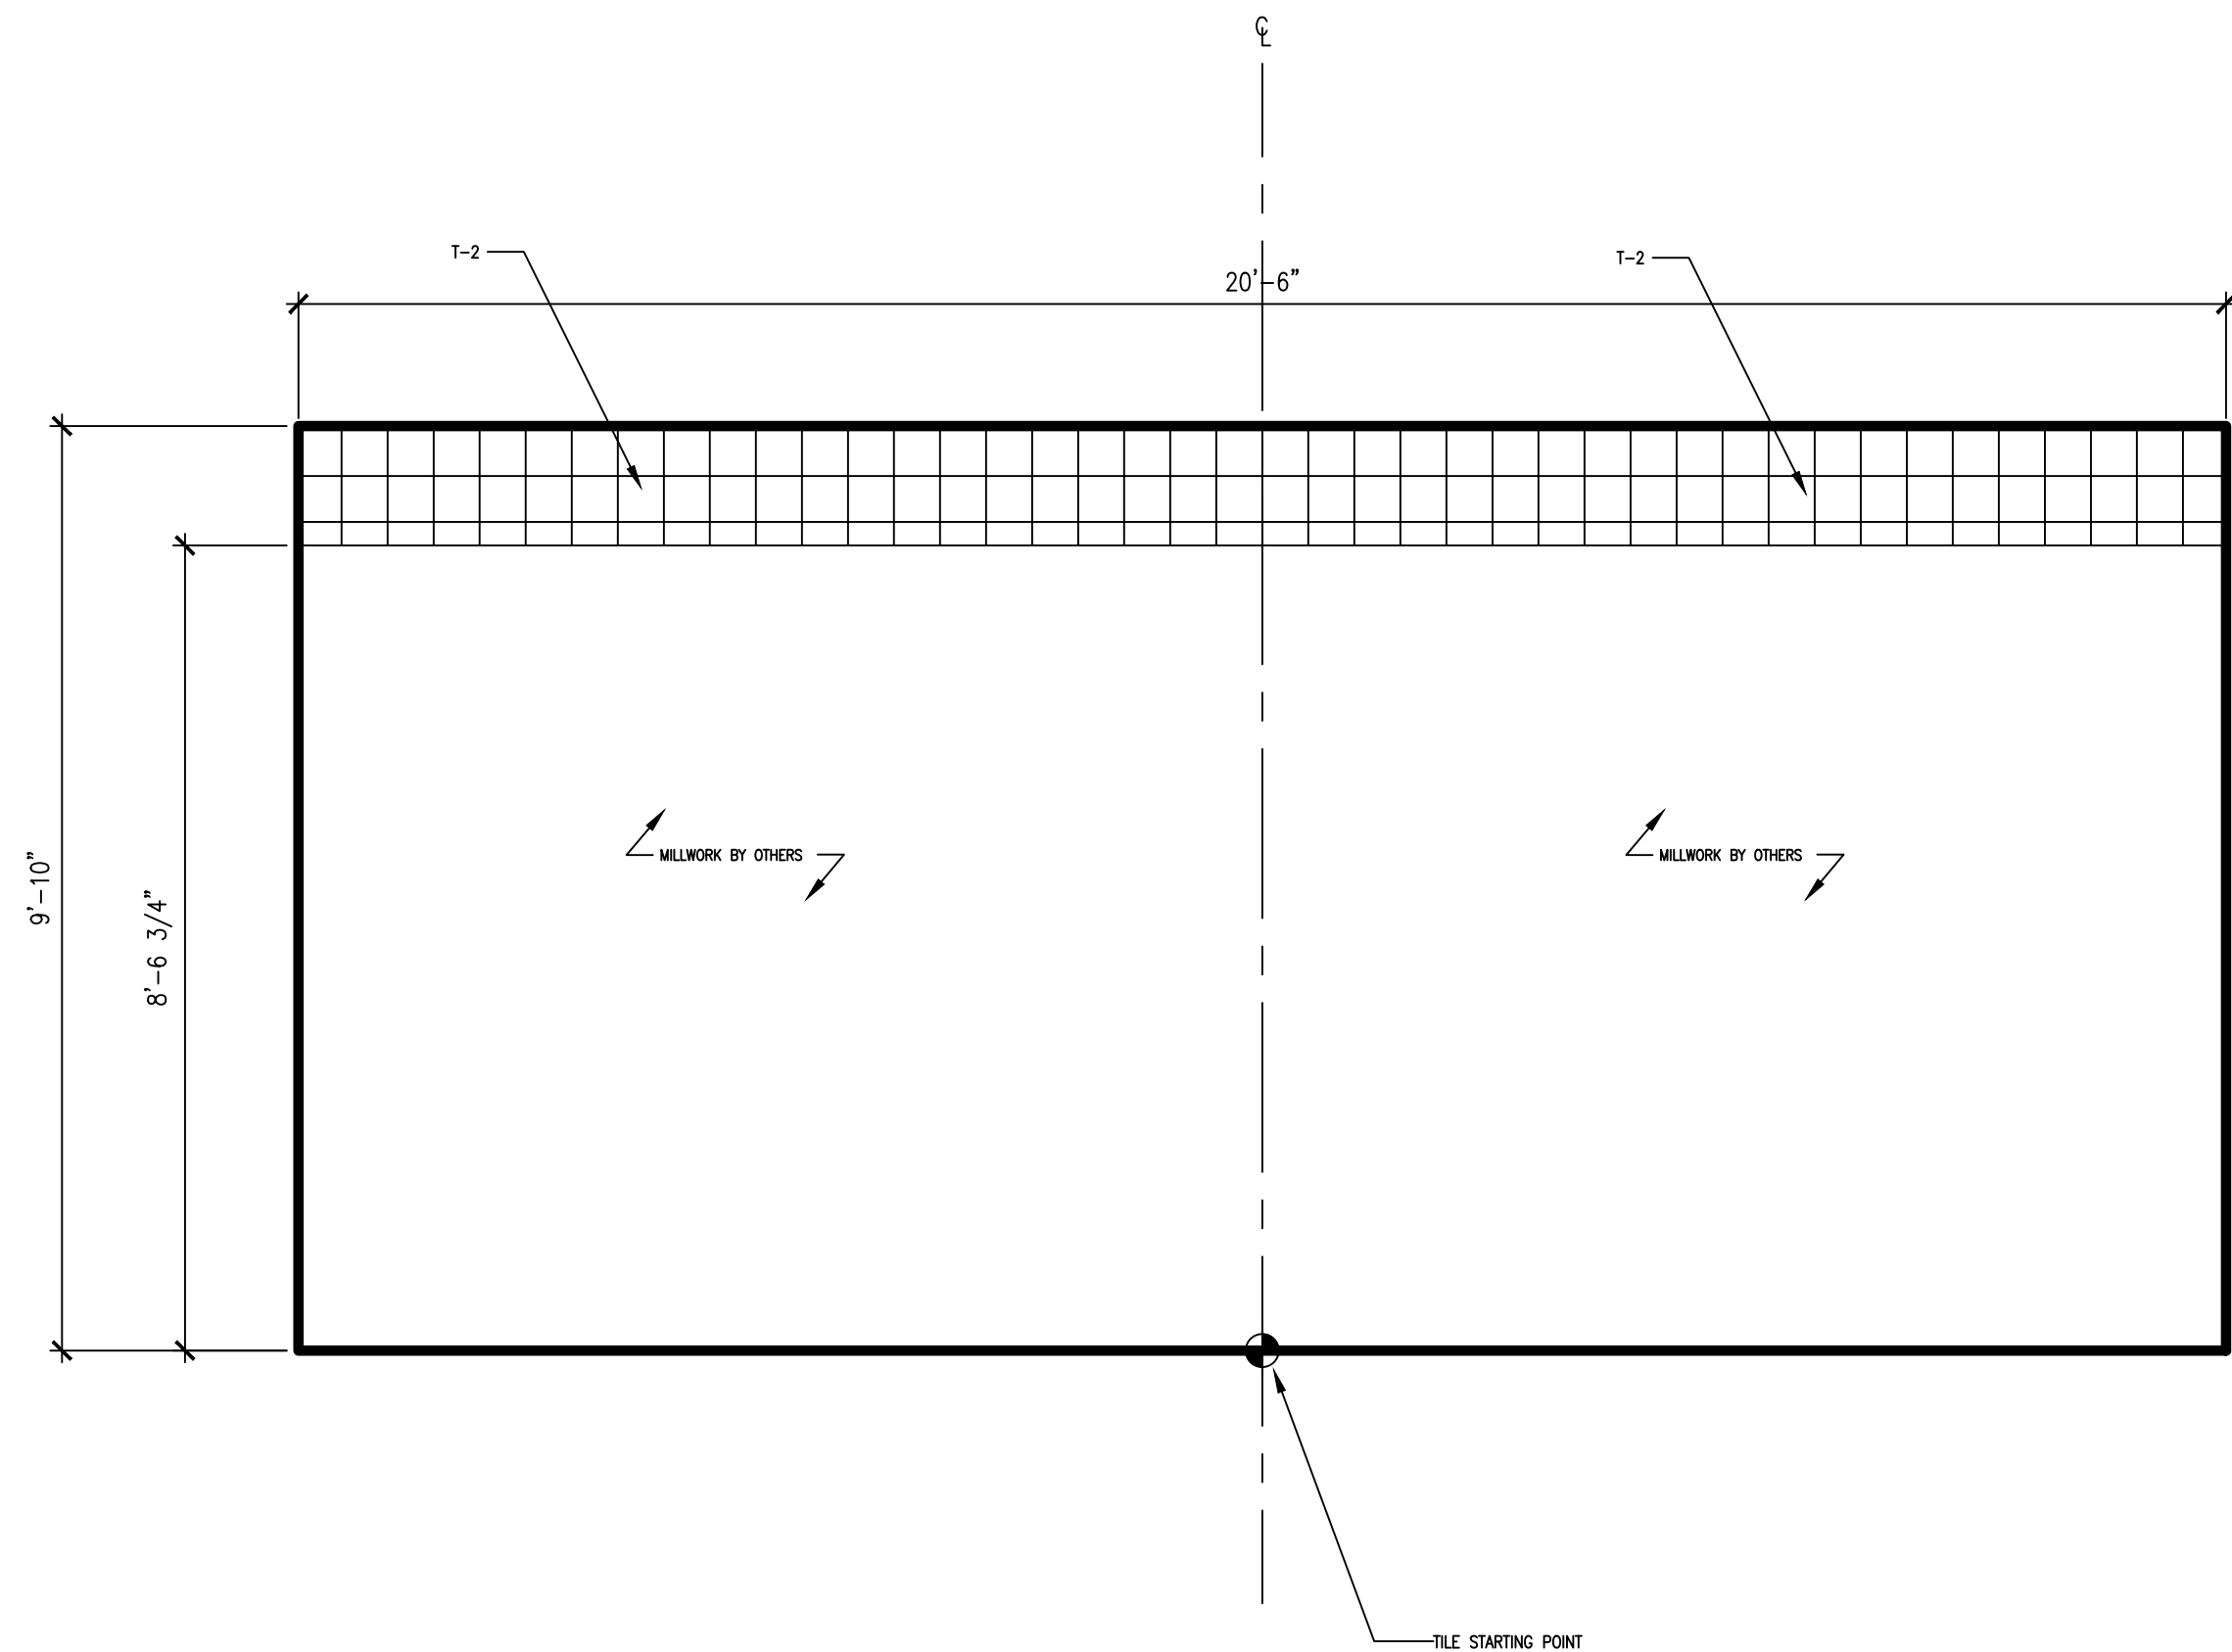

06 ELEVATION: NORTH
1/2"=1'-0"

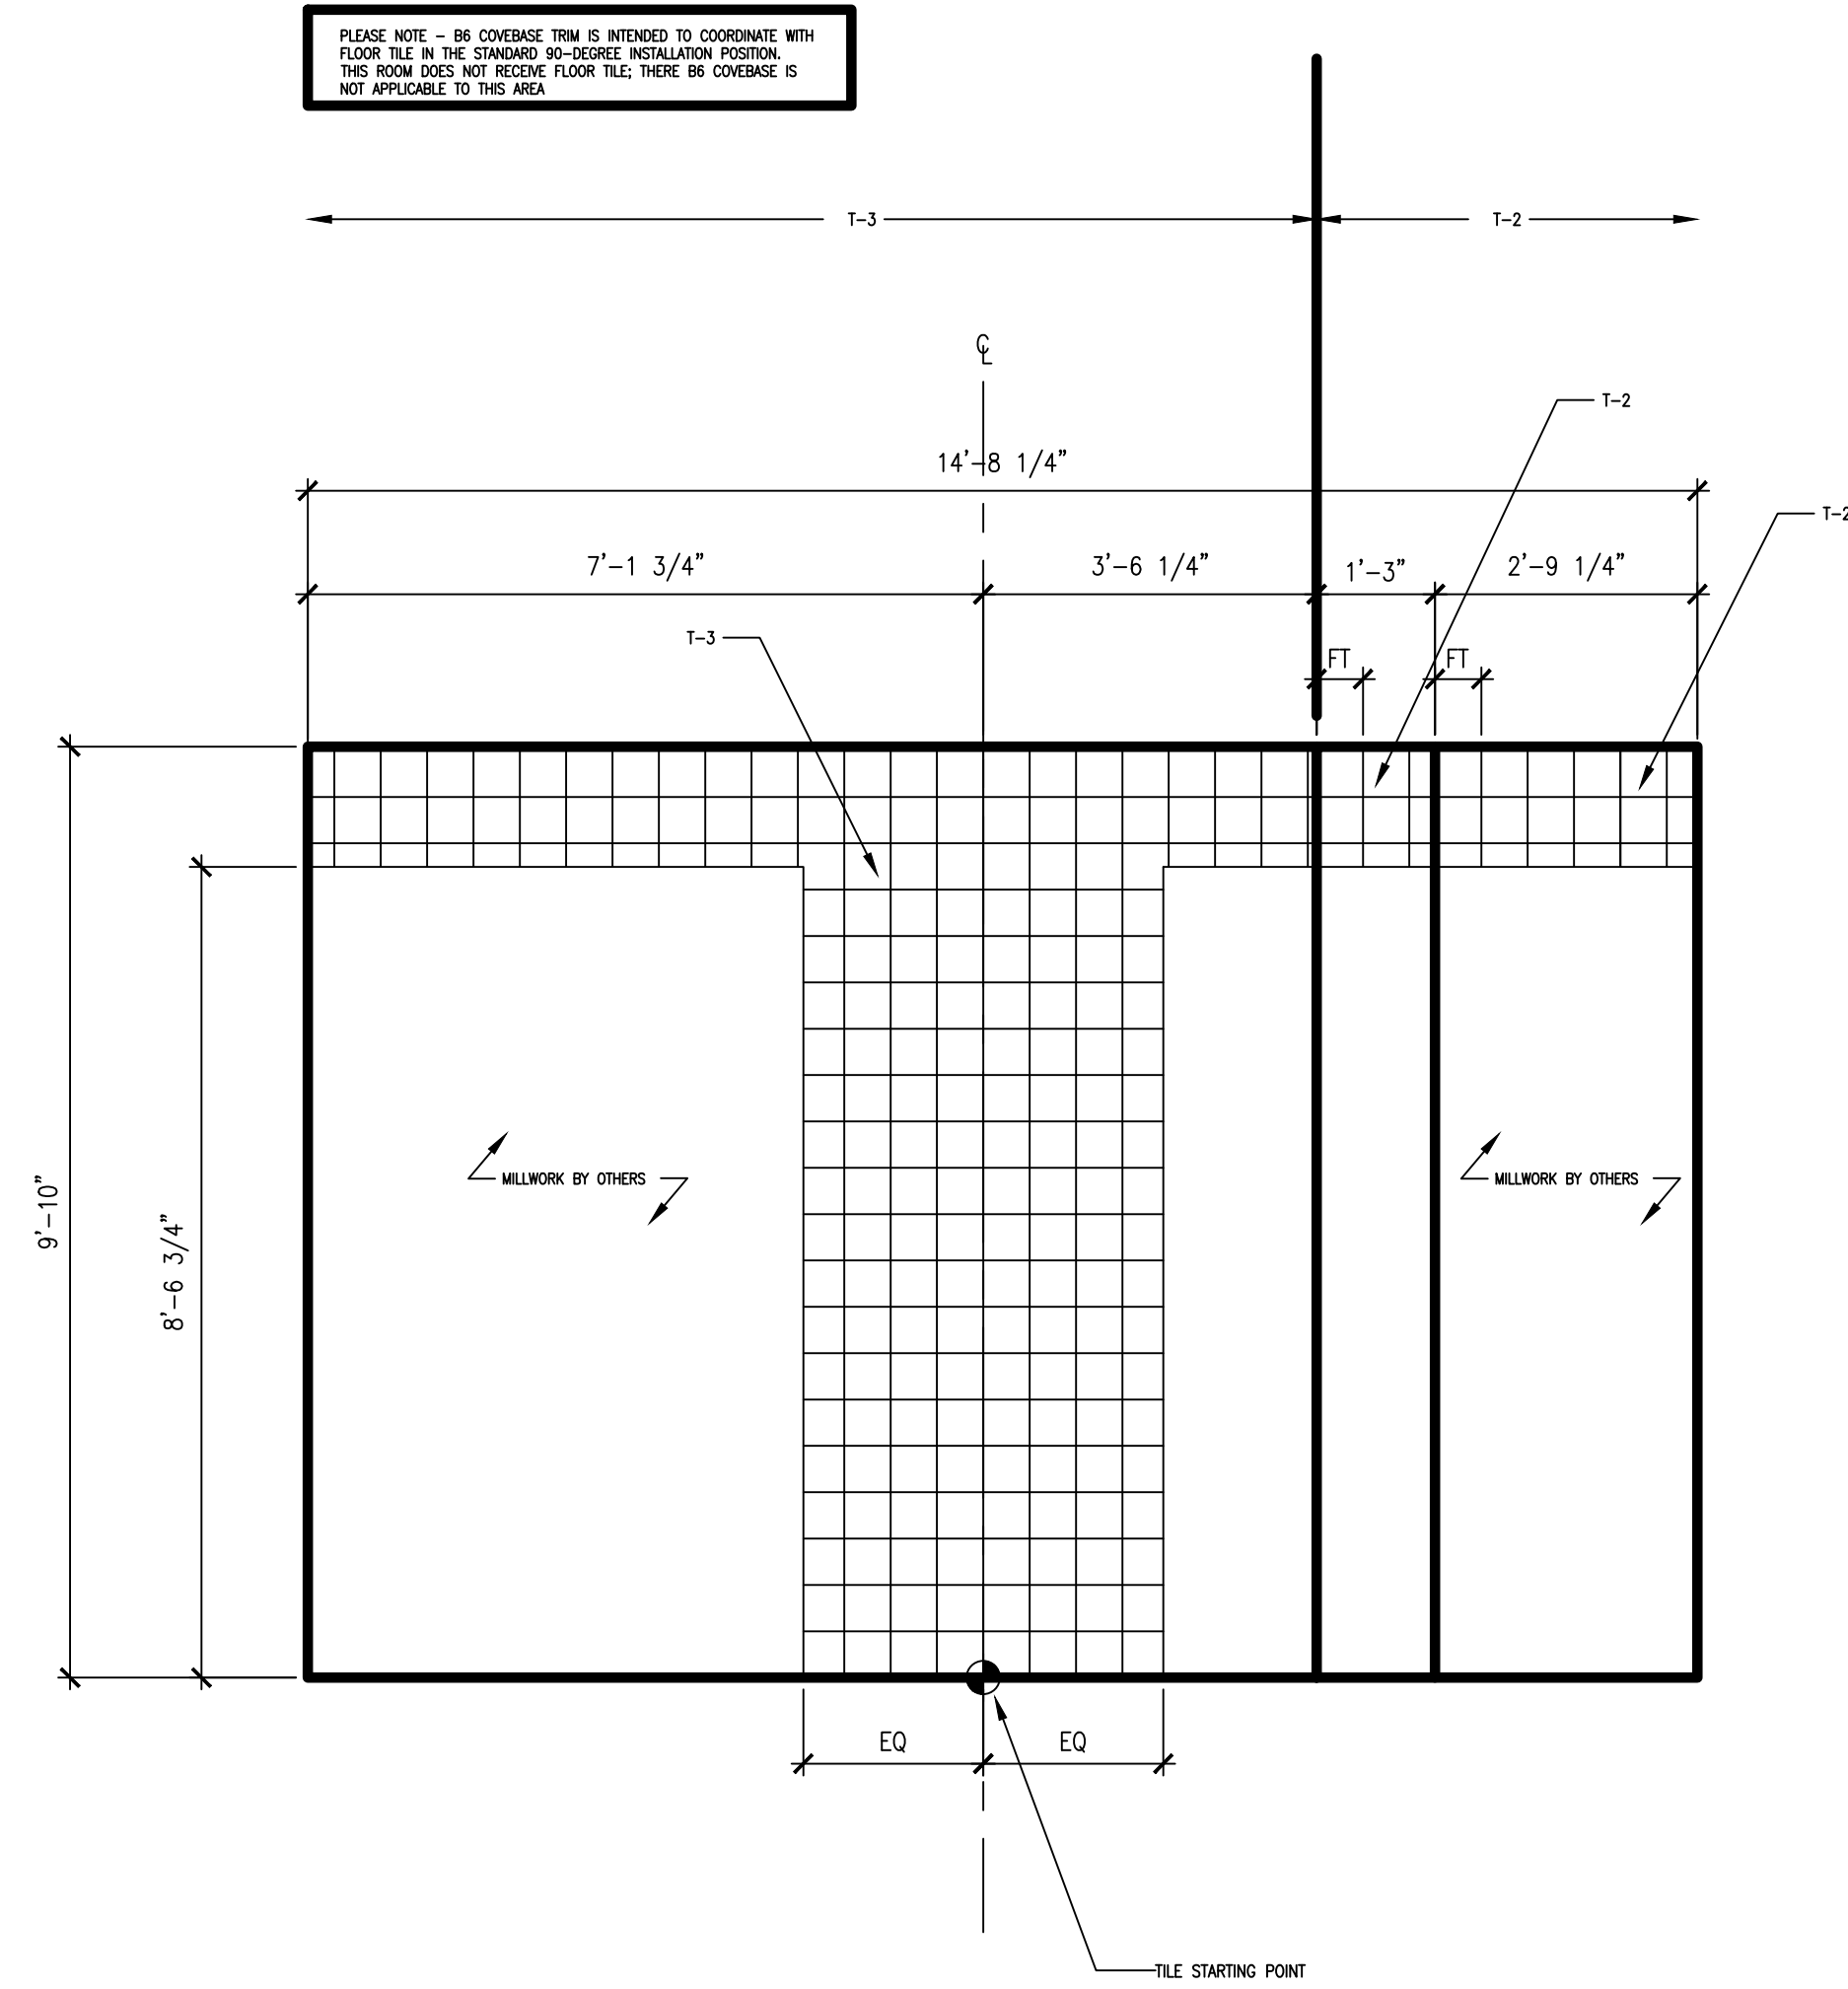

03 ELEVATION: EAST
1/2"=1'-0"

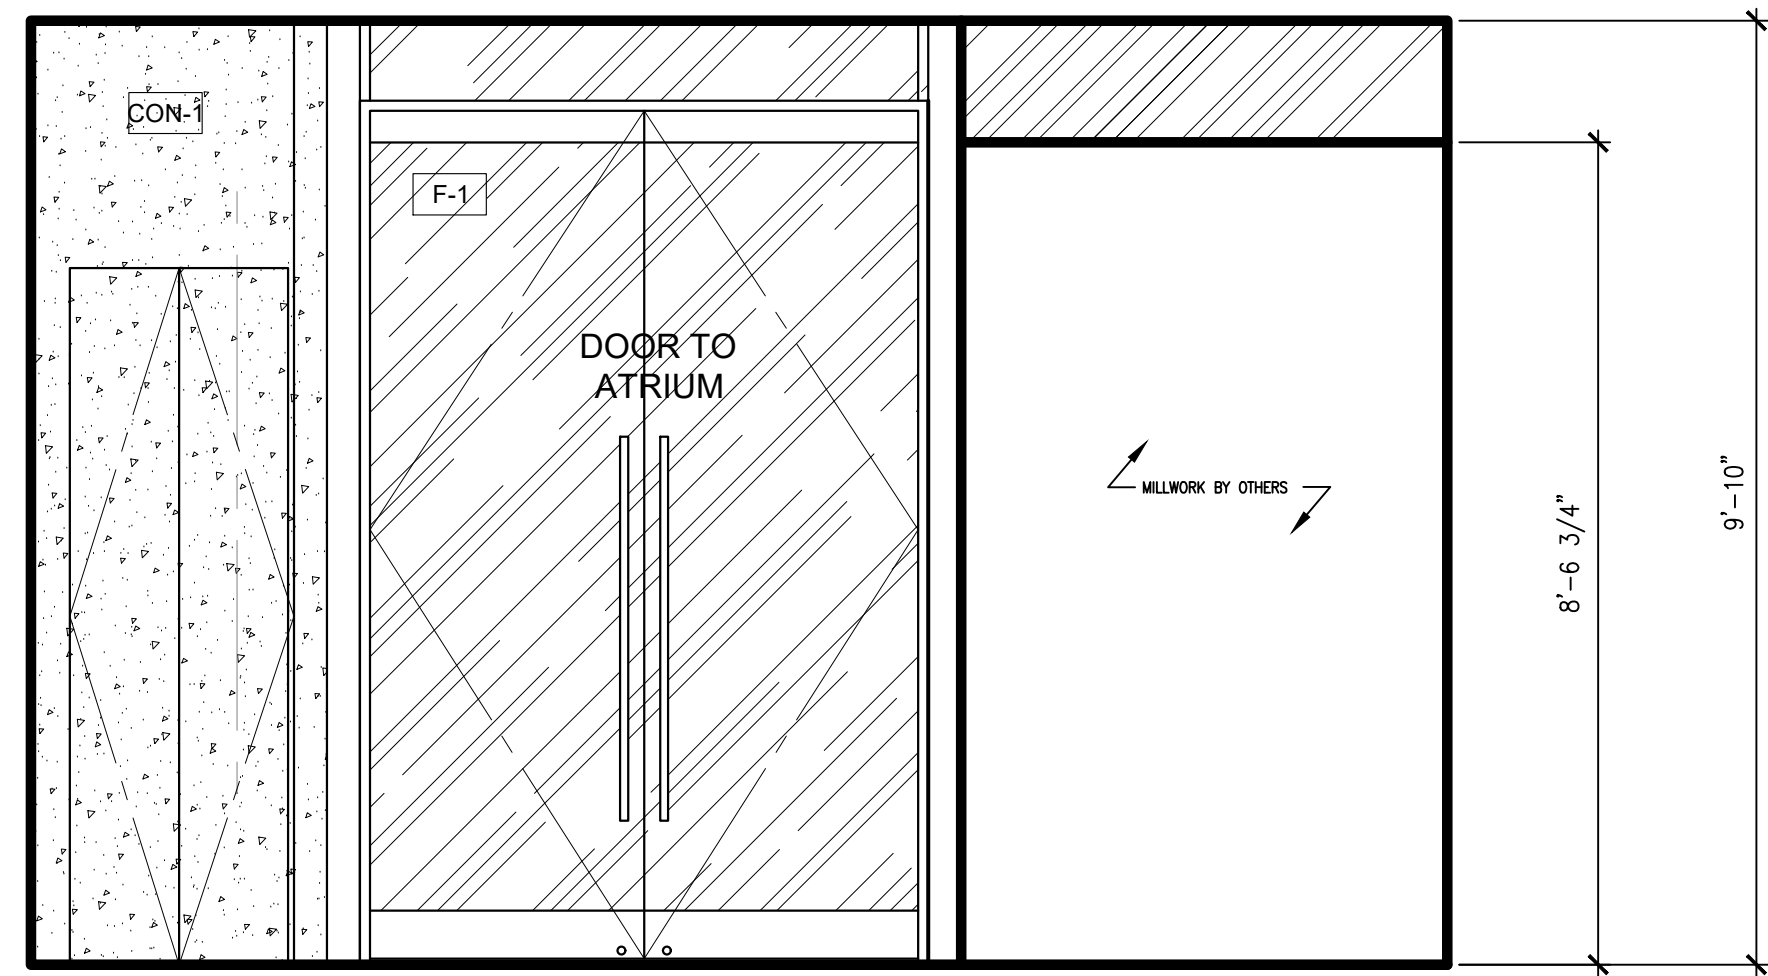

05 ELEVATION: WEST
1/2"=1'-0"

AUSTRO TILE & STONE, LLC
30-25 93RD STREET
EAST ELMHURST, NY 11369

CONTRACTOR:
JRM CONSTRUCTION
MANAGEMENT, LLC
242 WEST 36TH STREET
11TH FLOOR
NEW YORK, NY 10018

INTERIOR DESIGNER:

ISSUE FOR APPROVAL 09/09/24
ISSUE NAME DATE


ARCHITECT:
KENNETH PARK ARCHITECTS
360 LEXINGTON AVENUE
NEW YORK, NY 10017PHONE:
212-599-0044

PROJECT NAME:
LACOSTE
575 5TH AVENUE
NEW YORK, NY 10017


SHEET NAME:
2ND FLOOR FITTING ROOMS
PLAN/ELEVATIONS

DATE:
PROJECT NO.:
PRINCIPAL:
DRAWING BY:
CHECKED BY:
SCALE:
DWG No.:
T-110
7 of 21



01 PLAN: 2ND FLOOR FITTING ROOMS
1/2"=1'-0"

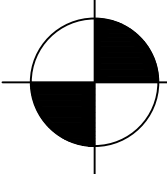

STARTING POINT

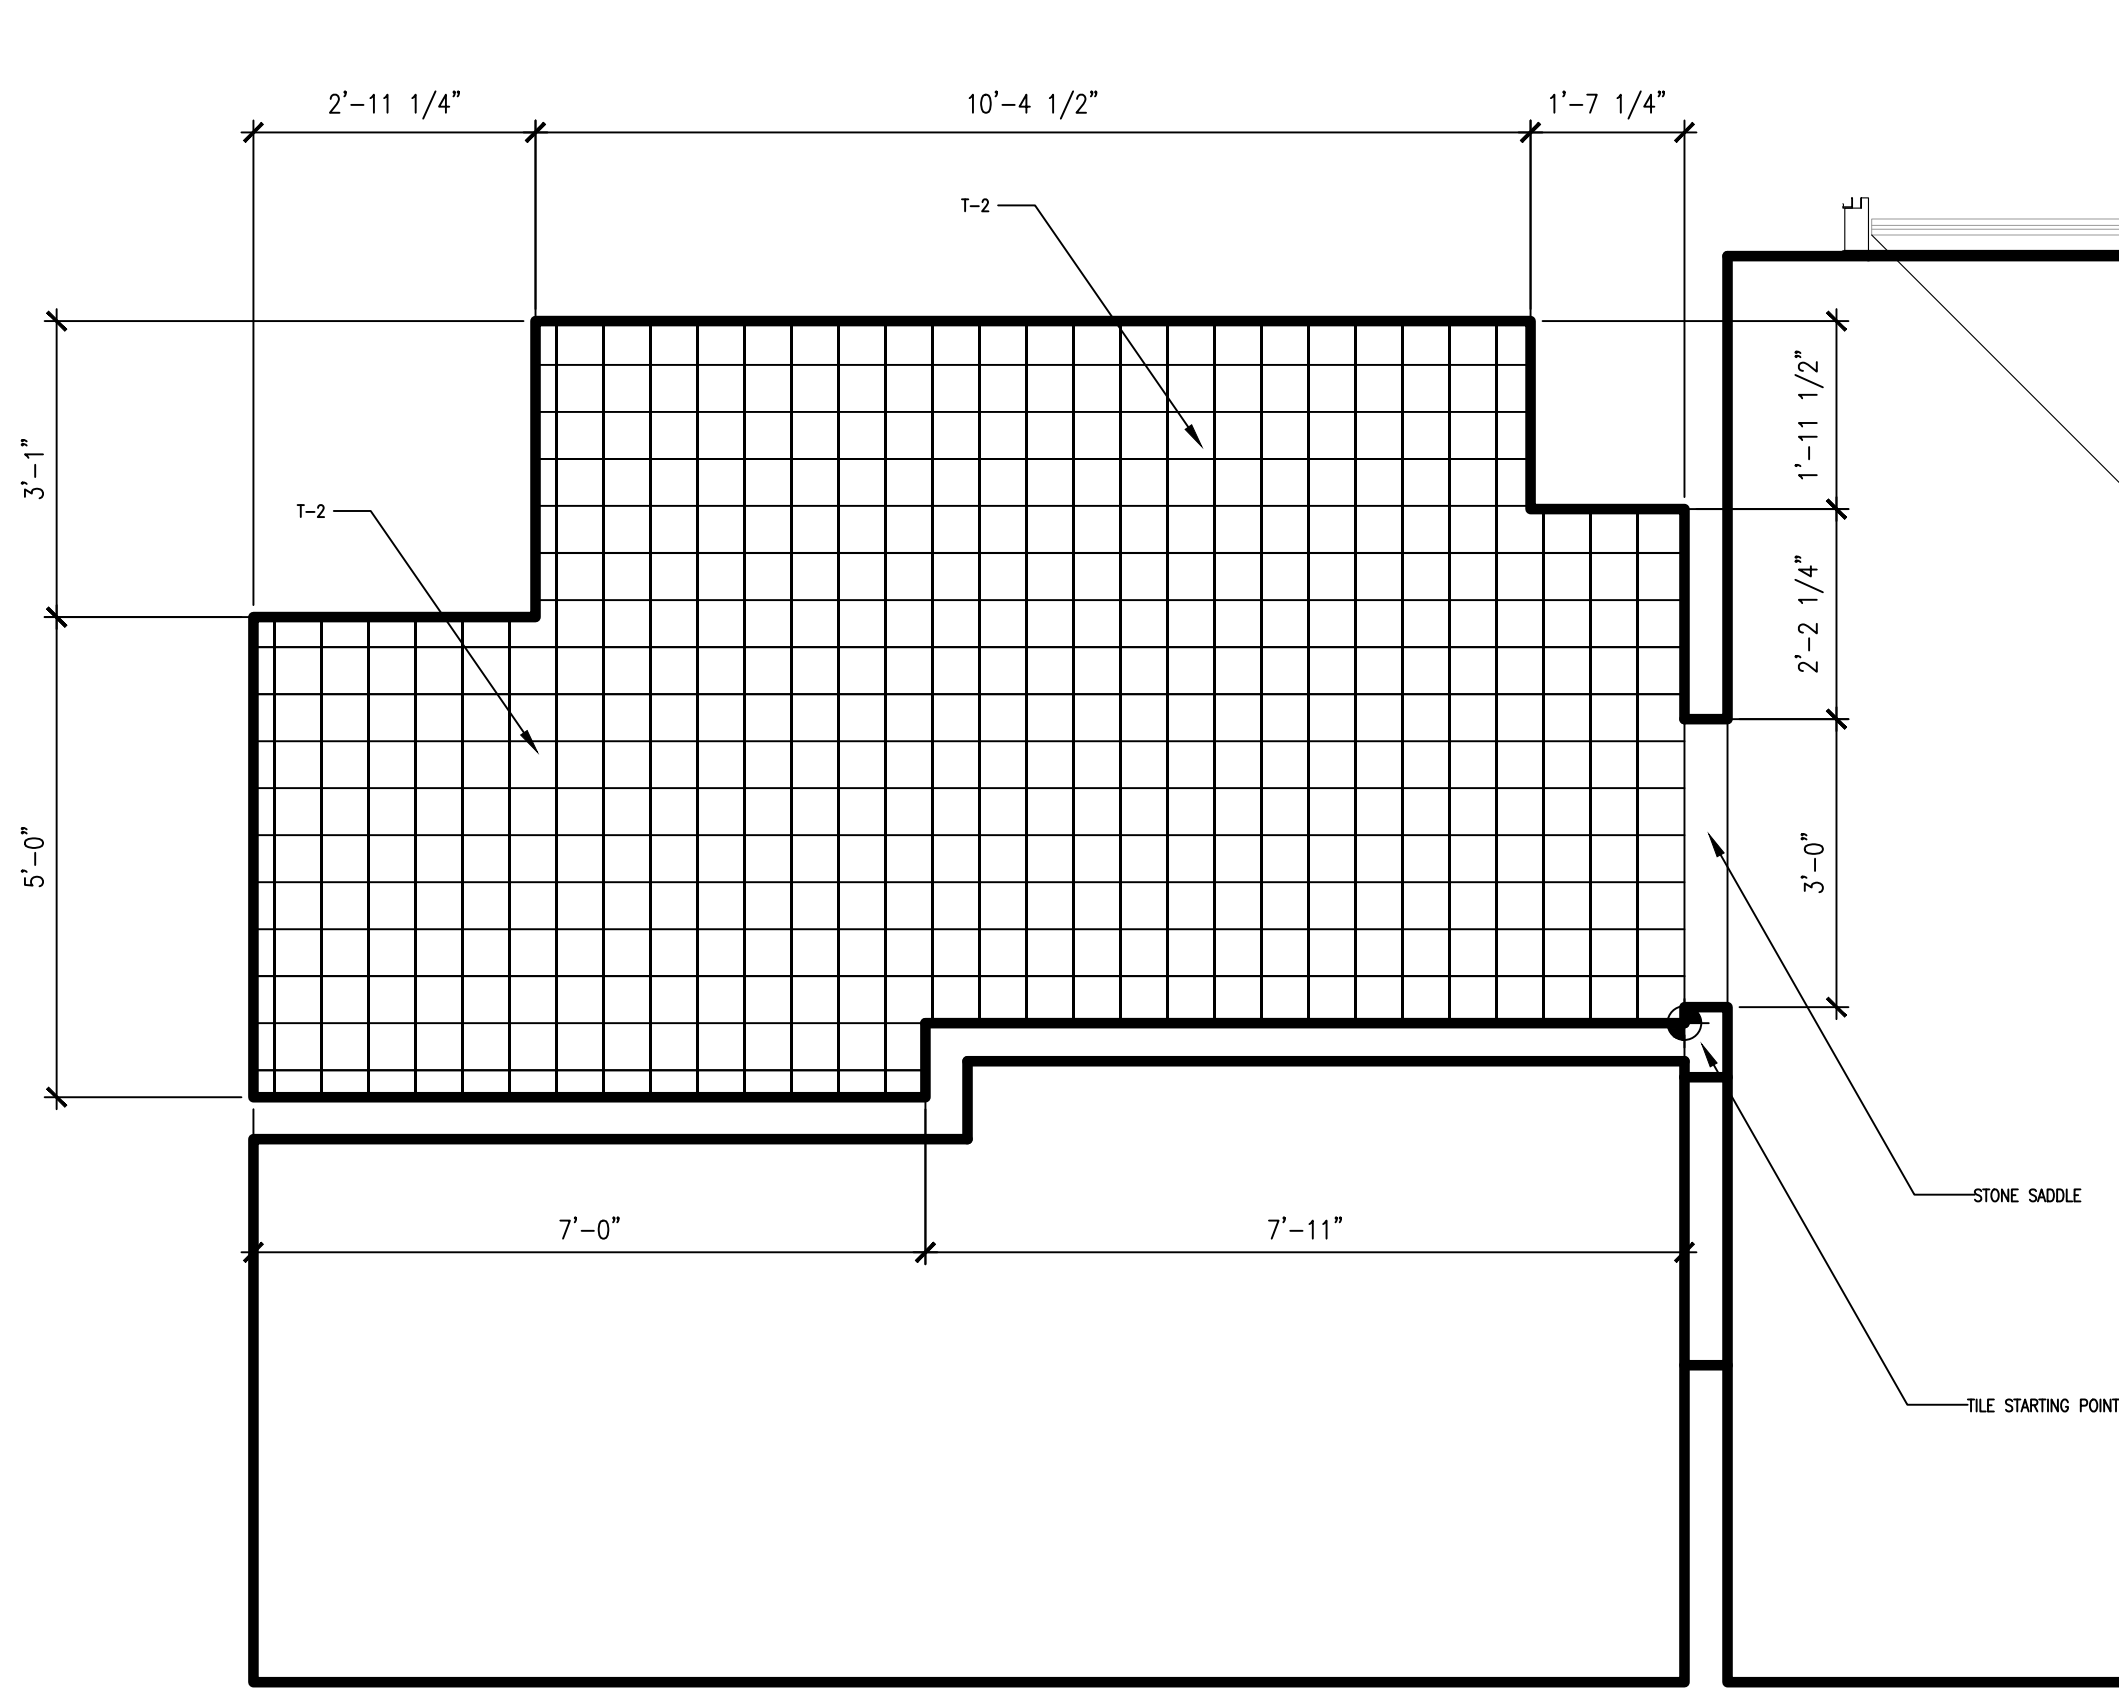

PLEASE NOTE - BASE GRANT JOINTS TO MATCH FLOOR/WALL TILE
GRANT JOINTS WHERE POSSIBLE OTHERWISE GRANT JOINTS WILL BE
STANDARD

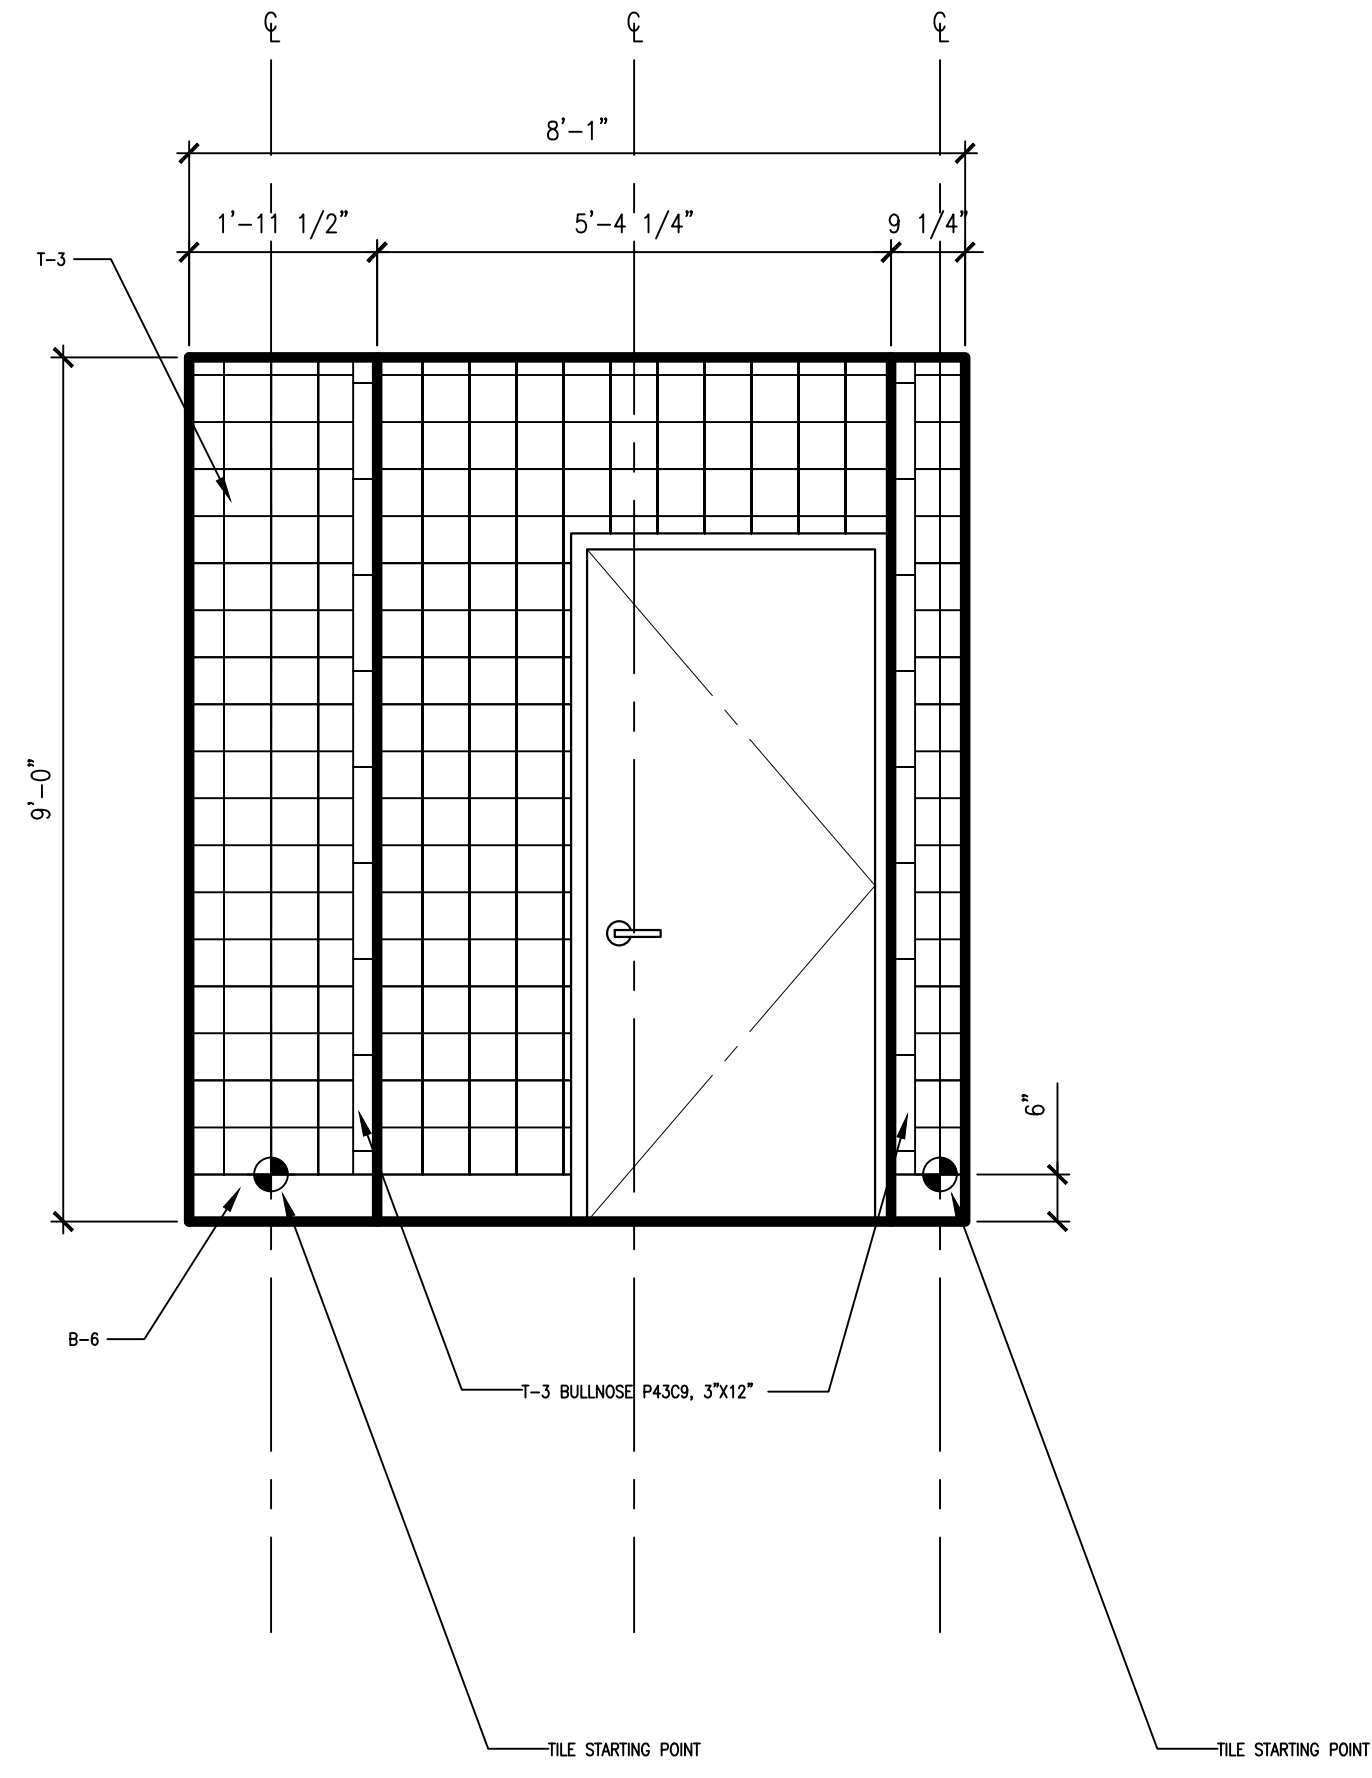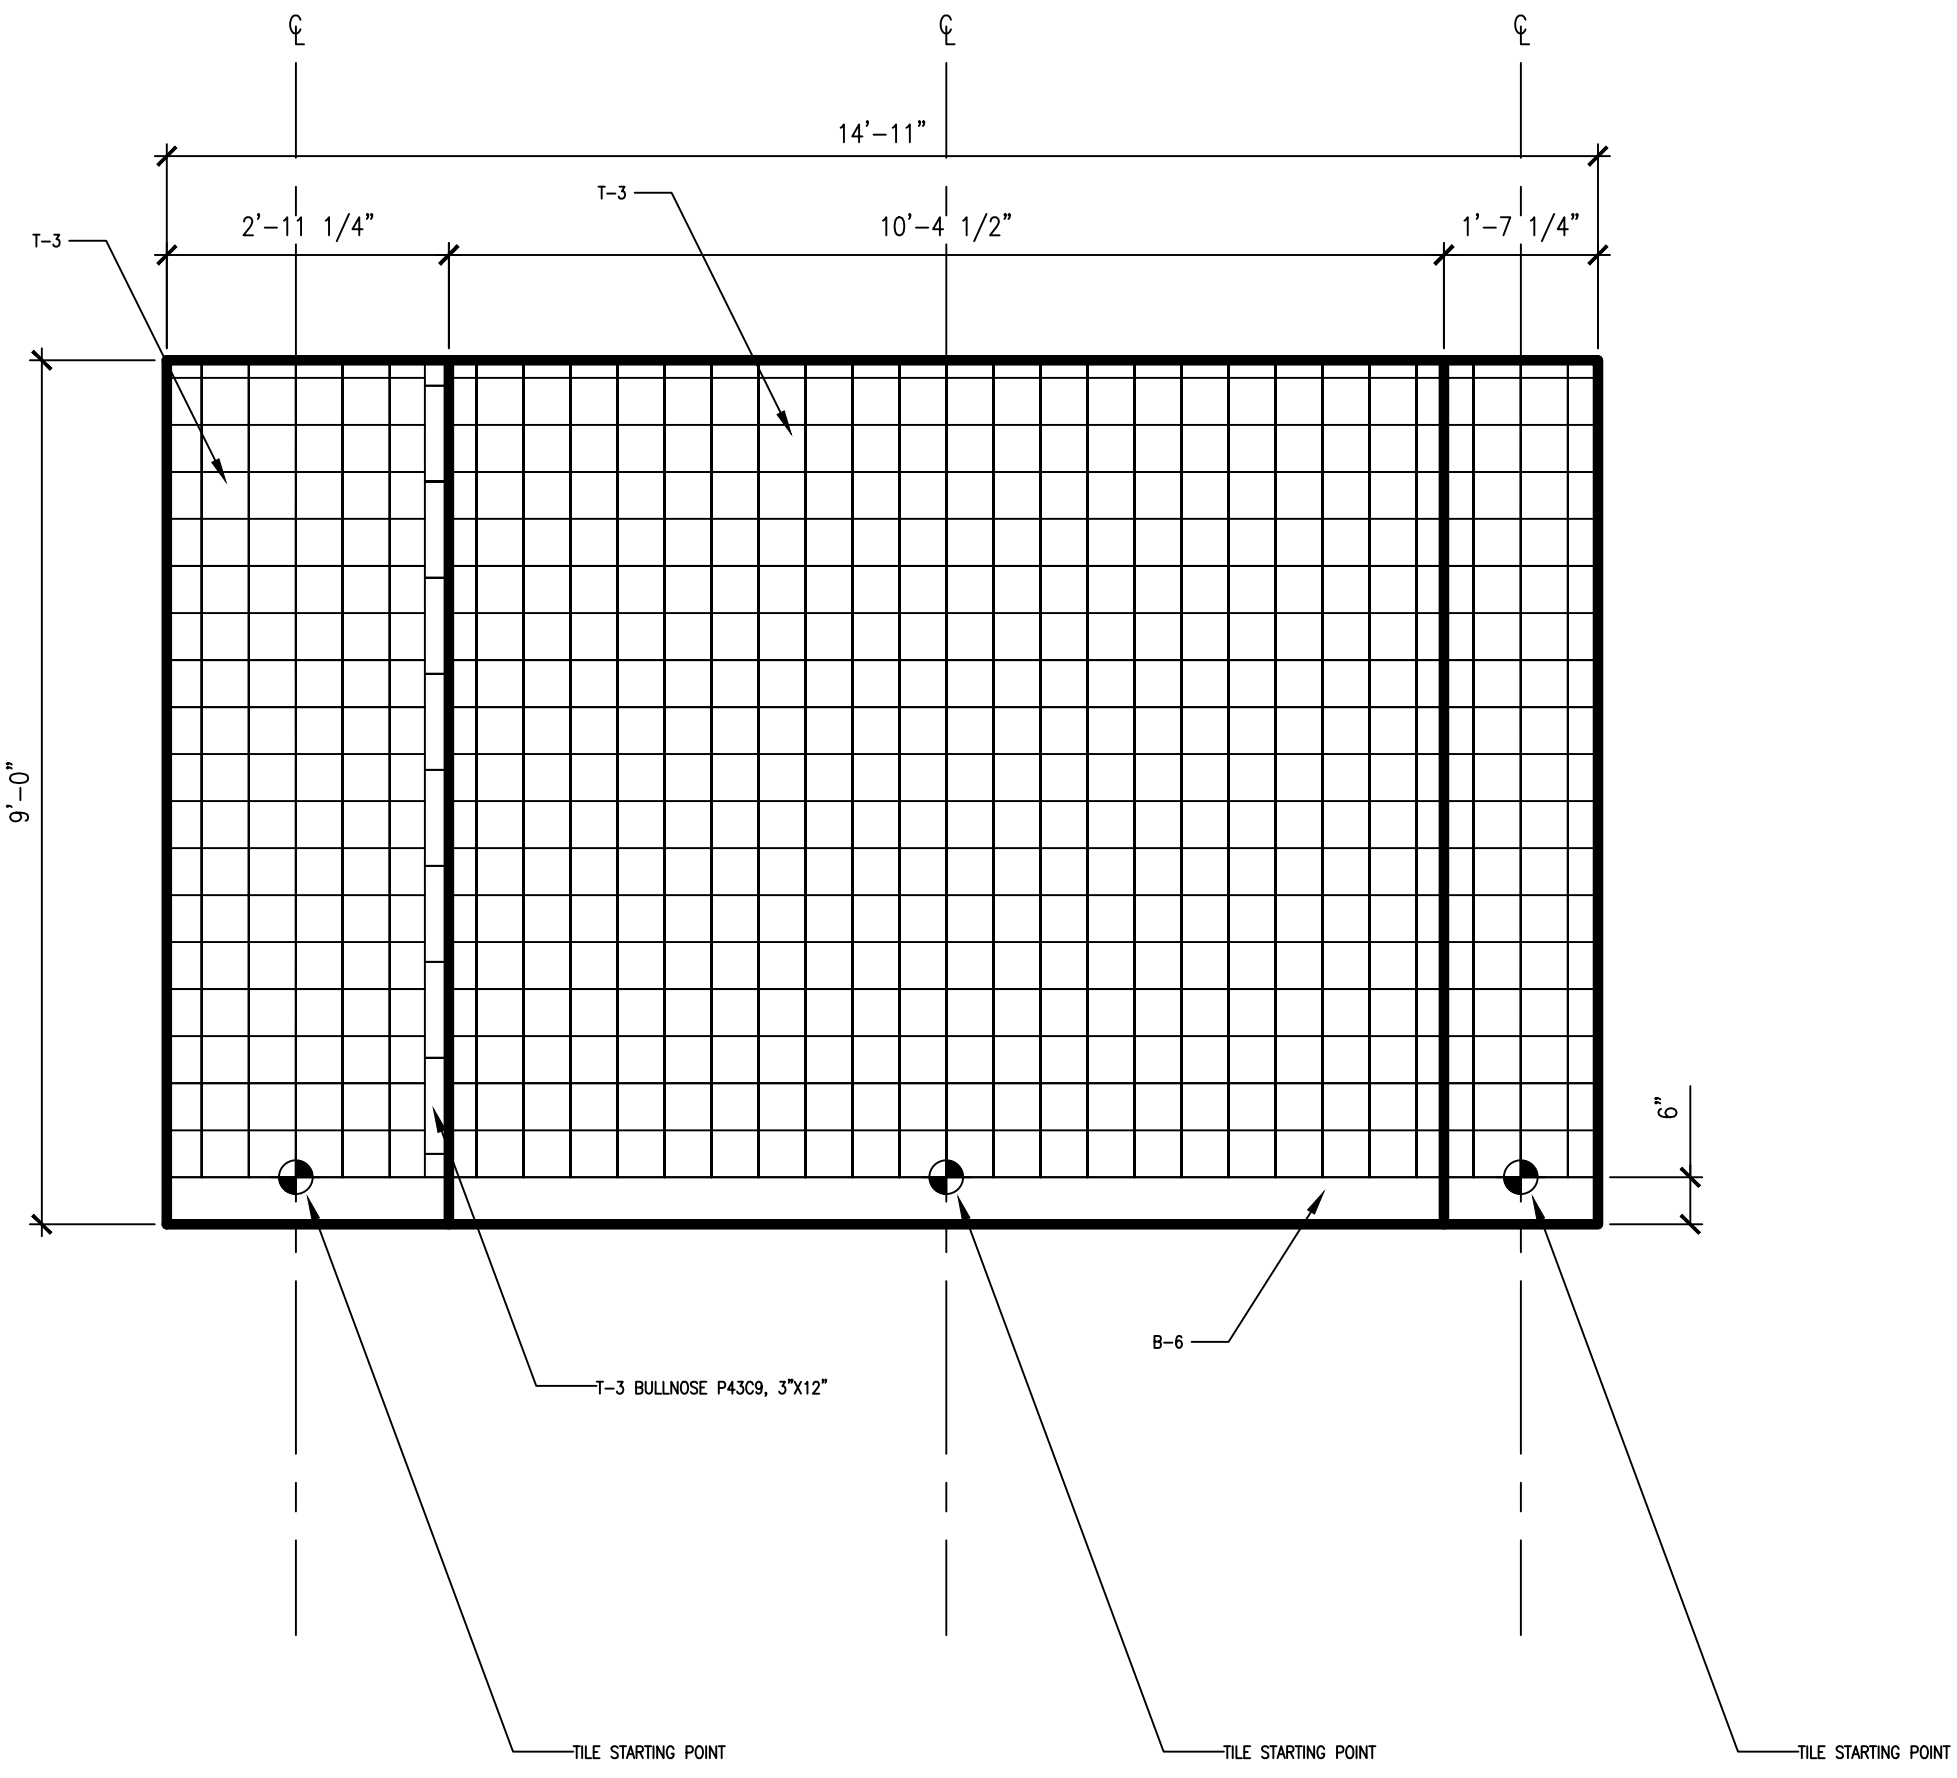

01
1/2"=1'-0"




PLAN: SHOWROOM RESTROOM (W) 306

03
1/2"=1'-0"

ELEVATION: NORTH

04
1/2"=1'-0"

ELEVATION: EAST

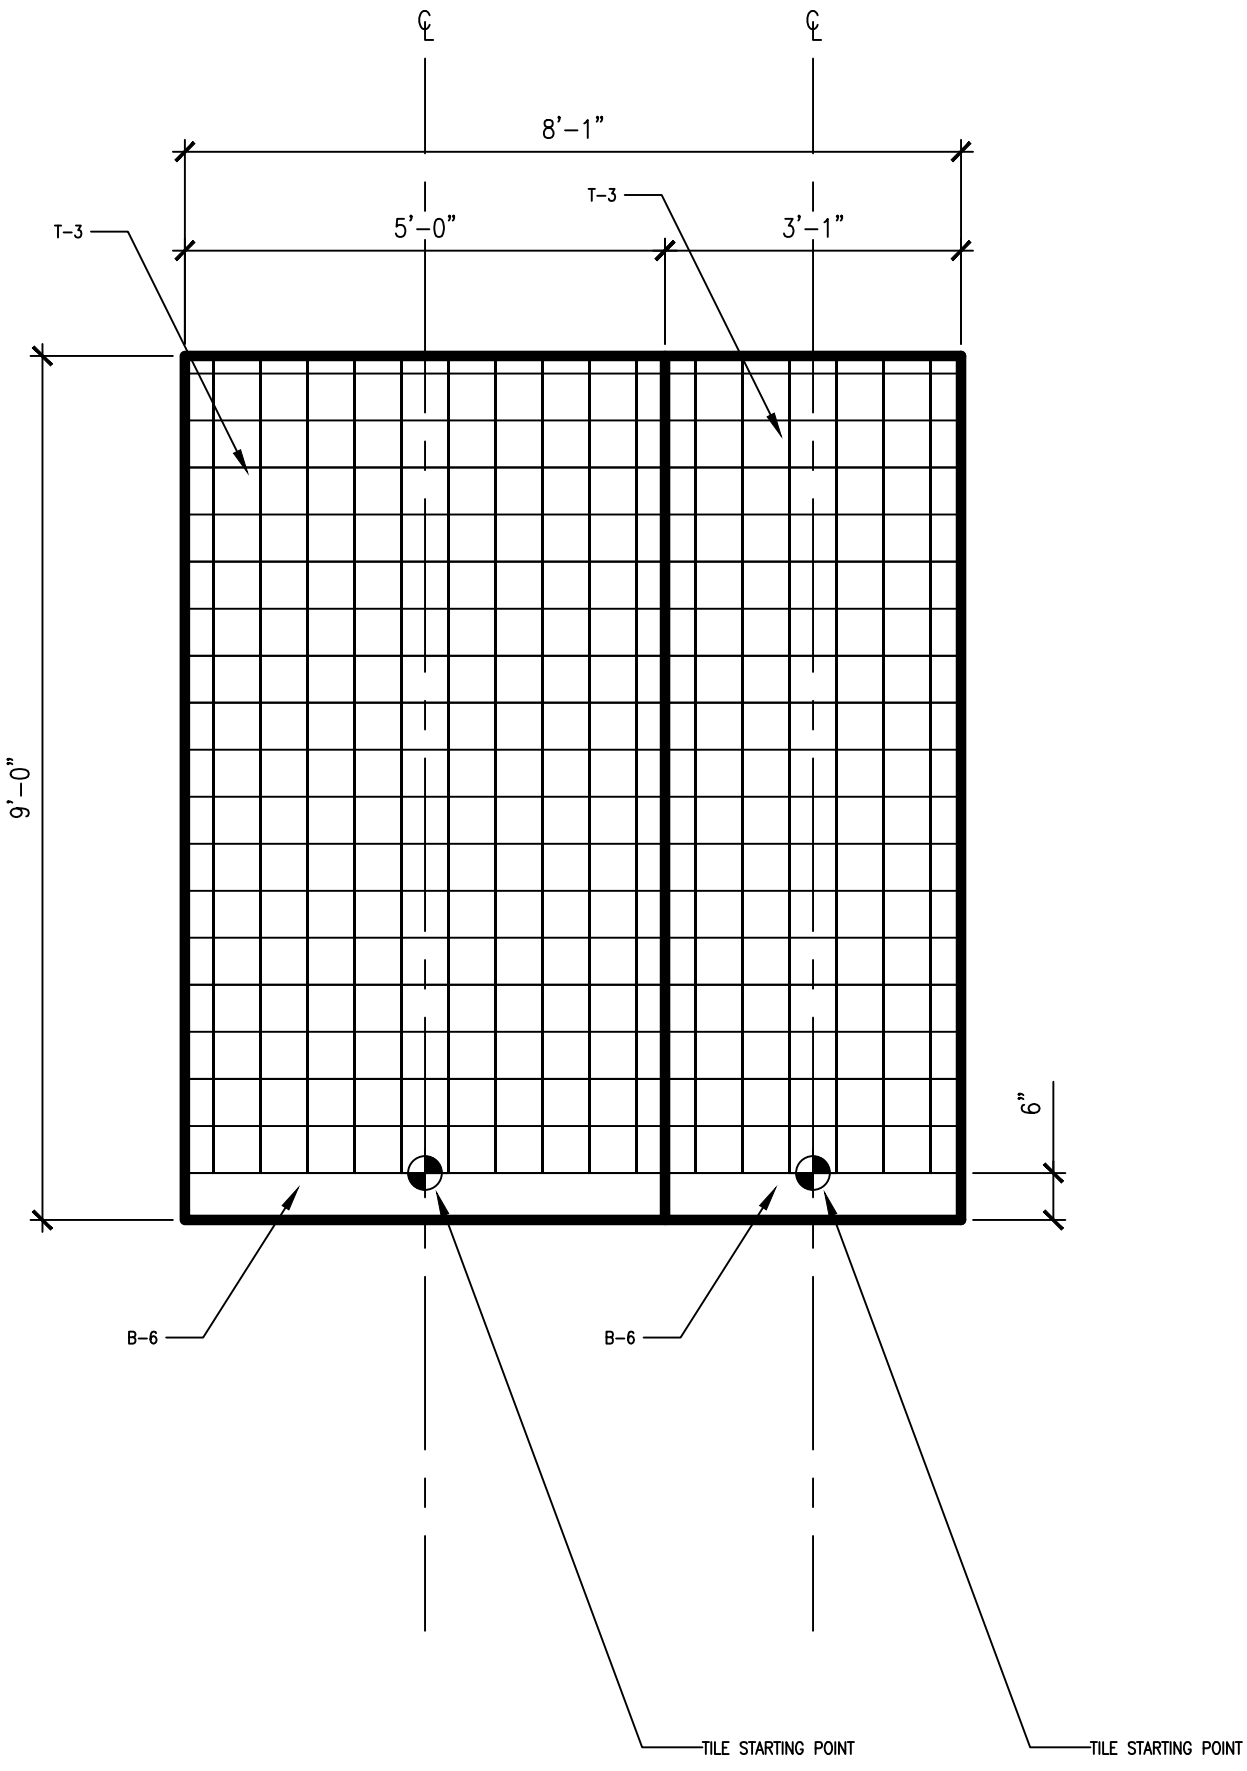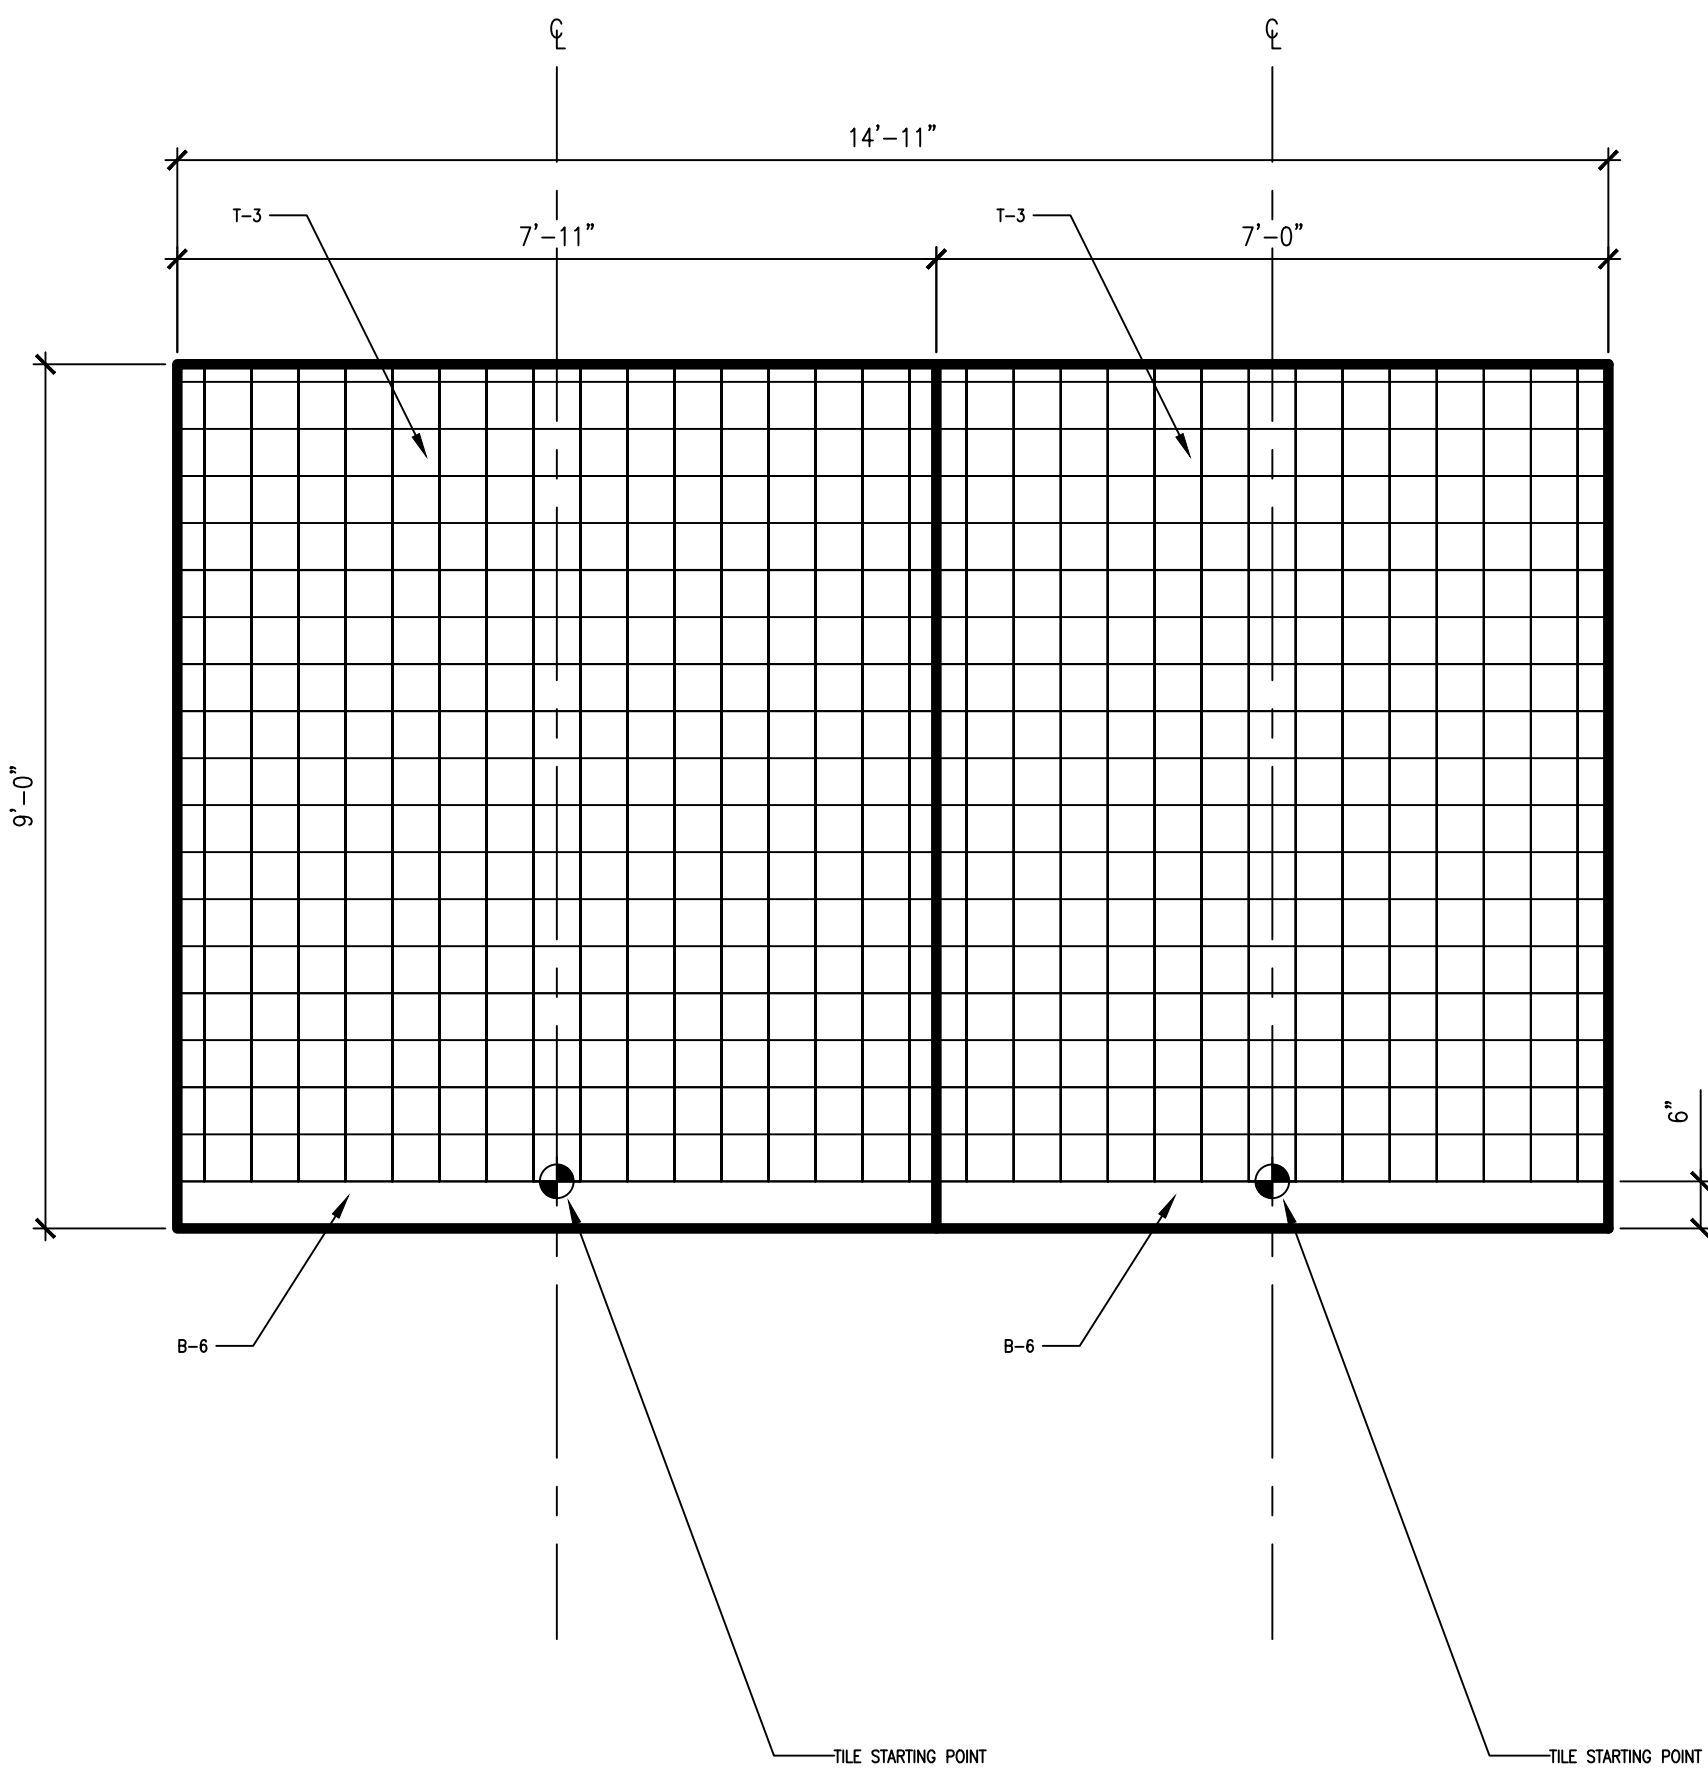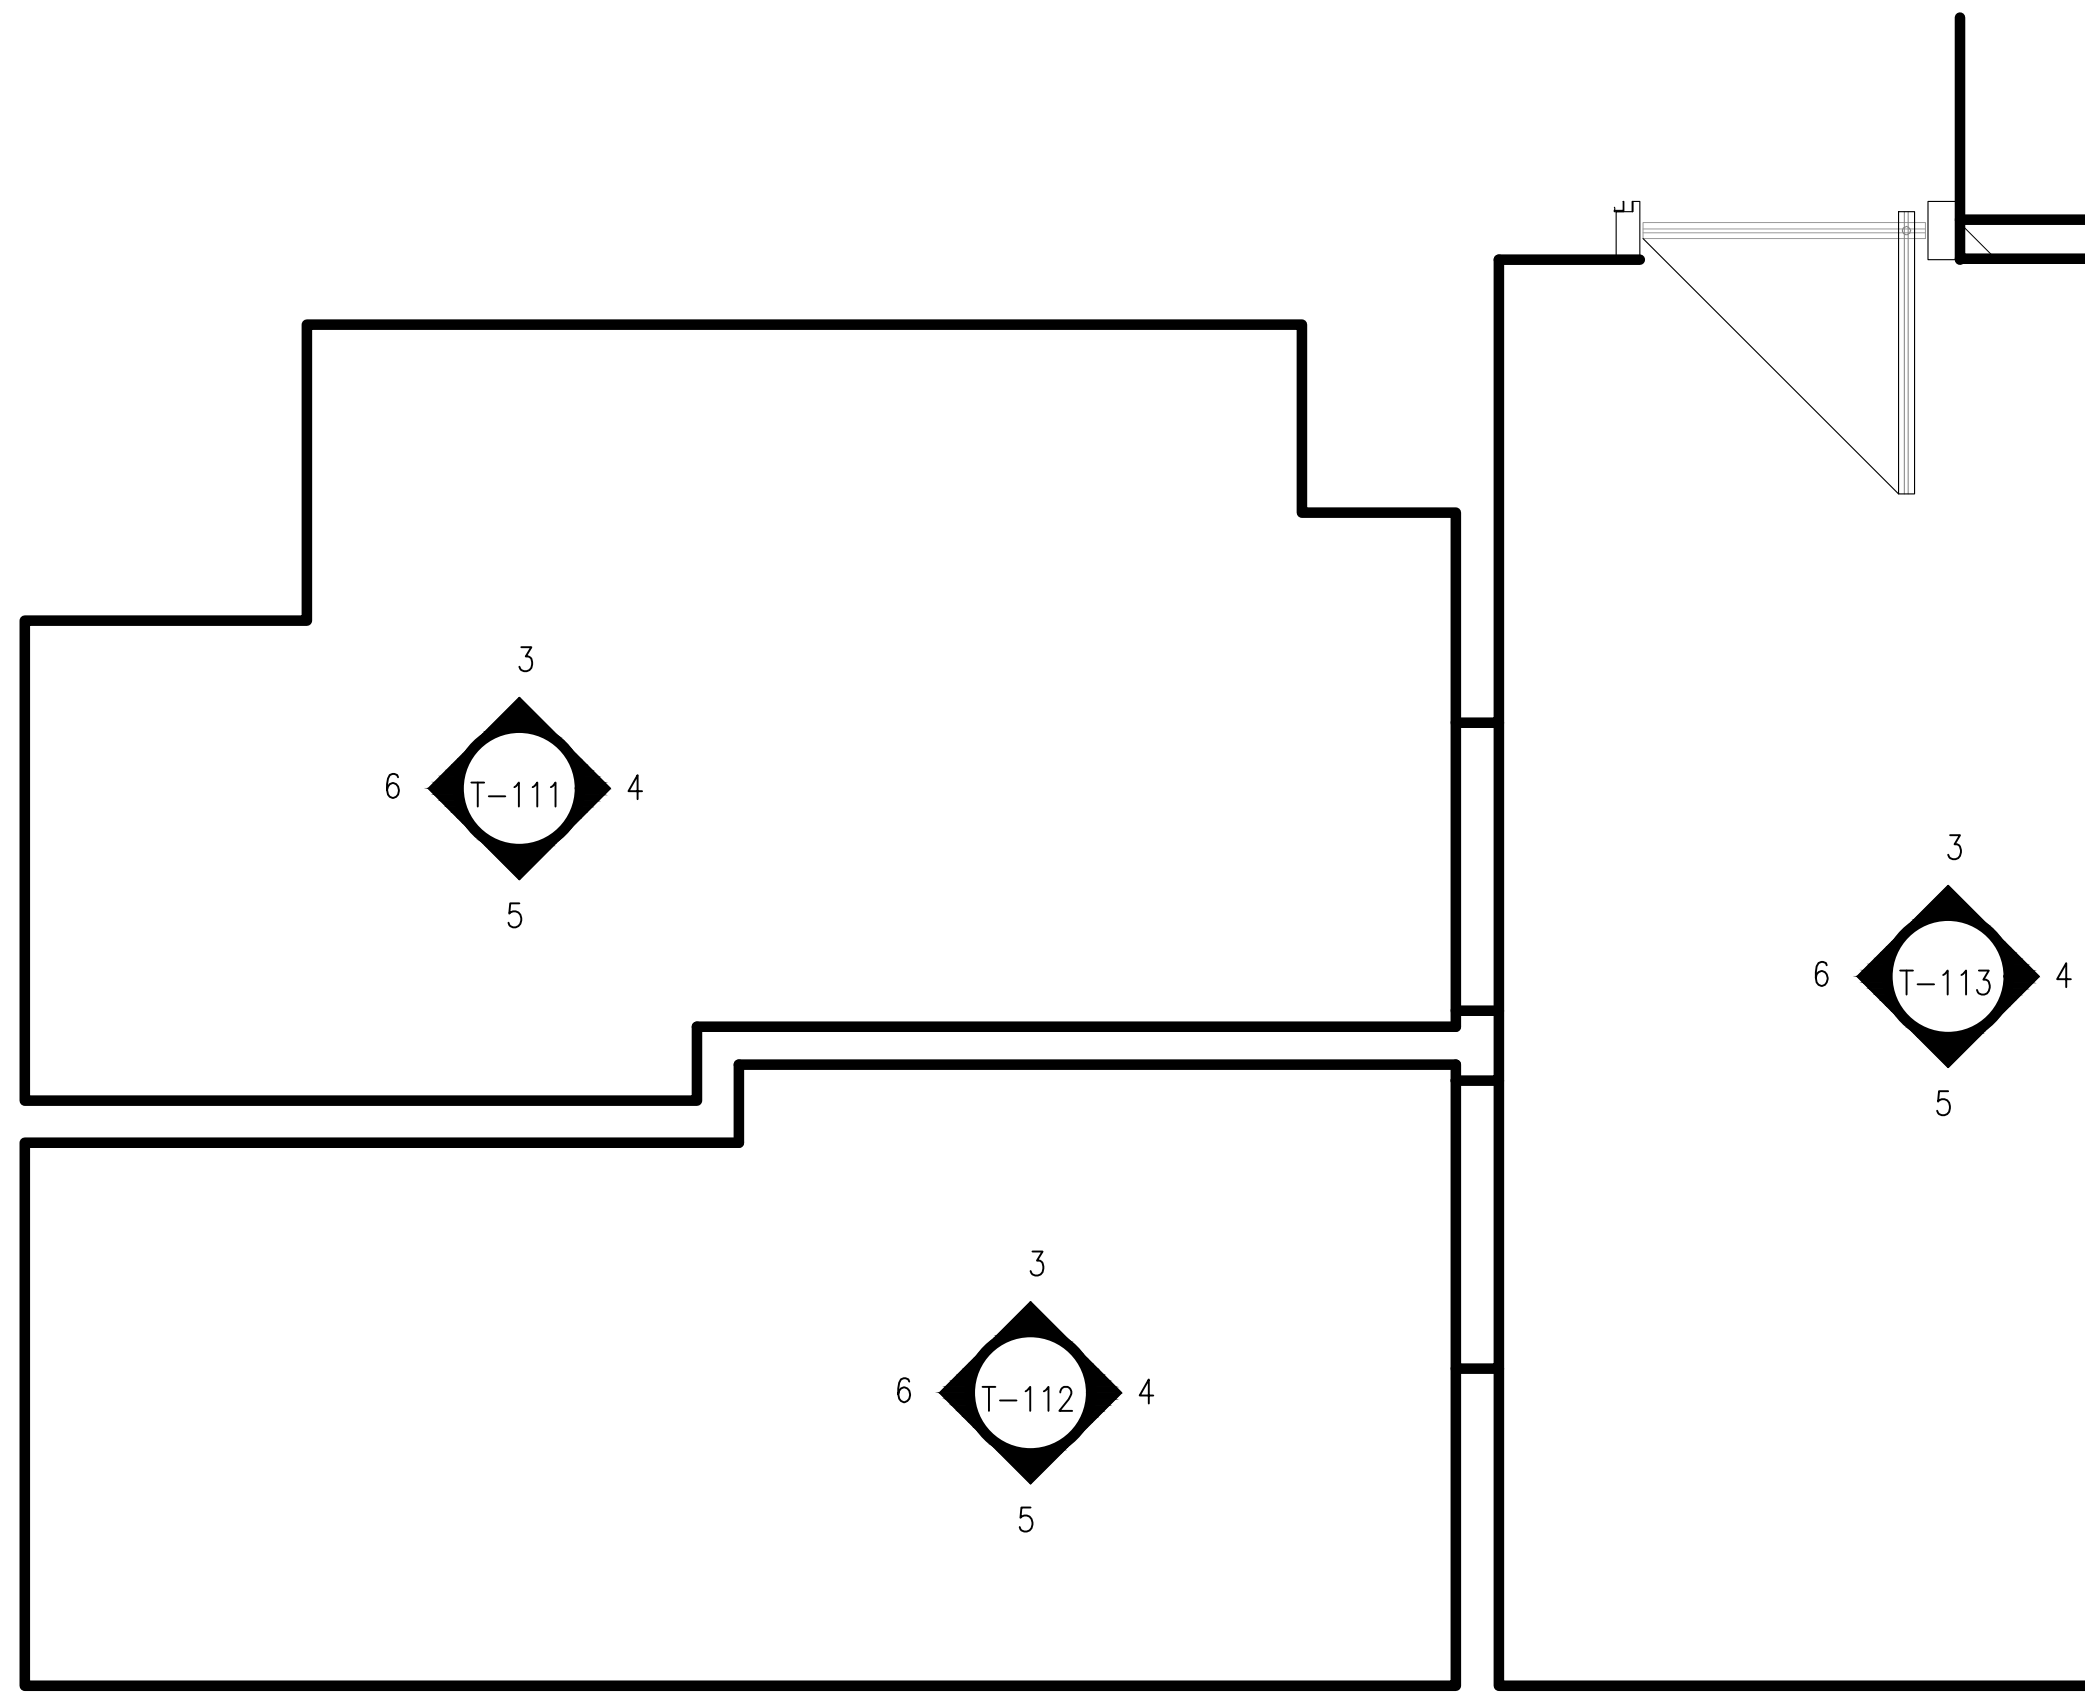

02
1/2"=1'-0"

PLAN: SHOWROOM RESTROOM (W) 306

05
1/2"=1'-0"

ELEVATION: SOUTH

06
1/2"=1'-0"

ELEVATION: WEST

AUSTRO TILE & STONE, LLC
30-25 93RD STREET
EAST ELMHURST, NY 11369

CONTRACTOR:
JRM CONSTRUCTION
MANAGEMENT, LLC
242 WEST 36TH STREET
11TH FLOOR
NEW YORK, NY 10018

INTERIOR DESIGNER:


ISSUE FOR APPROVAL 09/09/24
ISSUE NAME DATE

ARCHITECT:
KENNETH PARK ARCHITECTS
360 LEXINGTON AVENUE
NEW YORK, NY 10017PHONE:
212-599-0044


PROJECT NAME:
LACOSTE
575 5TH AVENUE
NEW YORK, NY 10017

SHEET NAME:
3RD FLOOR RESTROOMS
PLAN/ELEVATIONS


DATE:
PROJECT NO.:
PRINCIPAL:
DRAWING BY:
CHECKED BY:
SCALE:
DWG No.:
T-111
8 of 21

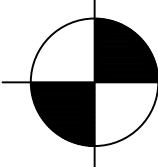

STARTING POINT

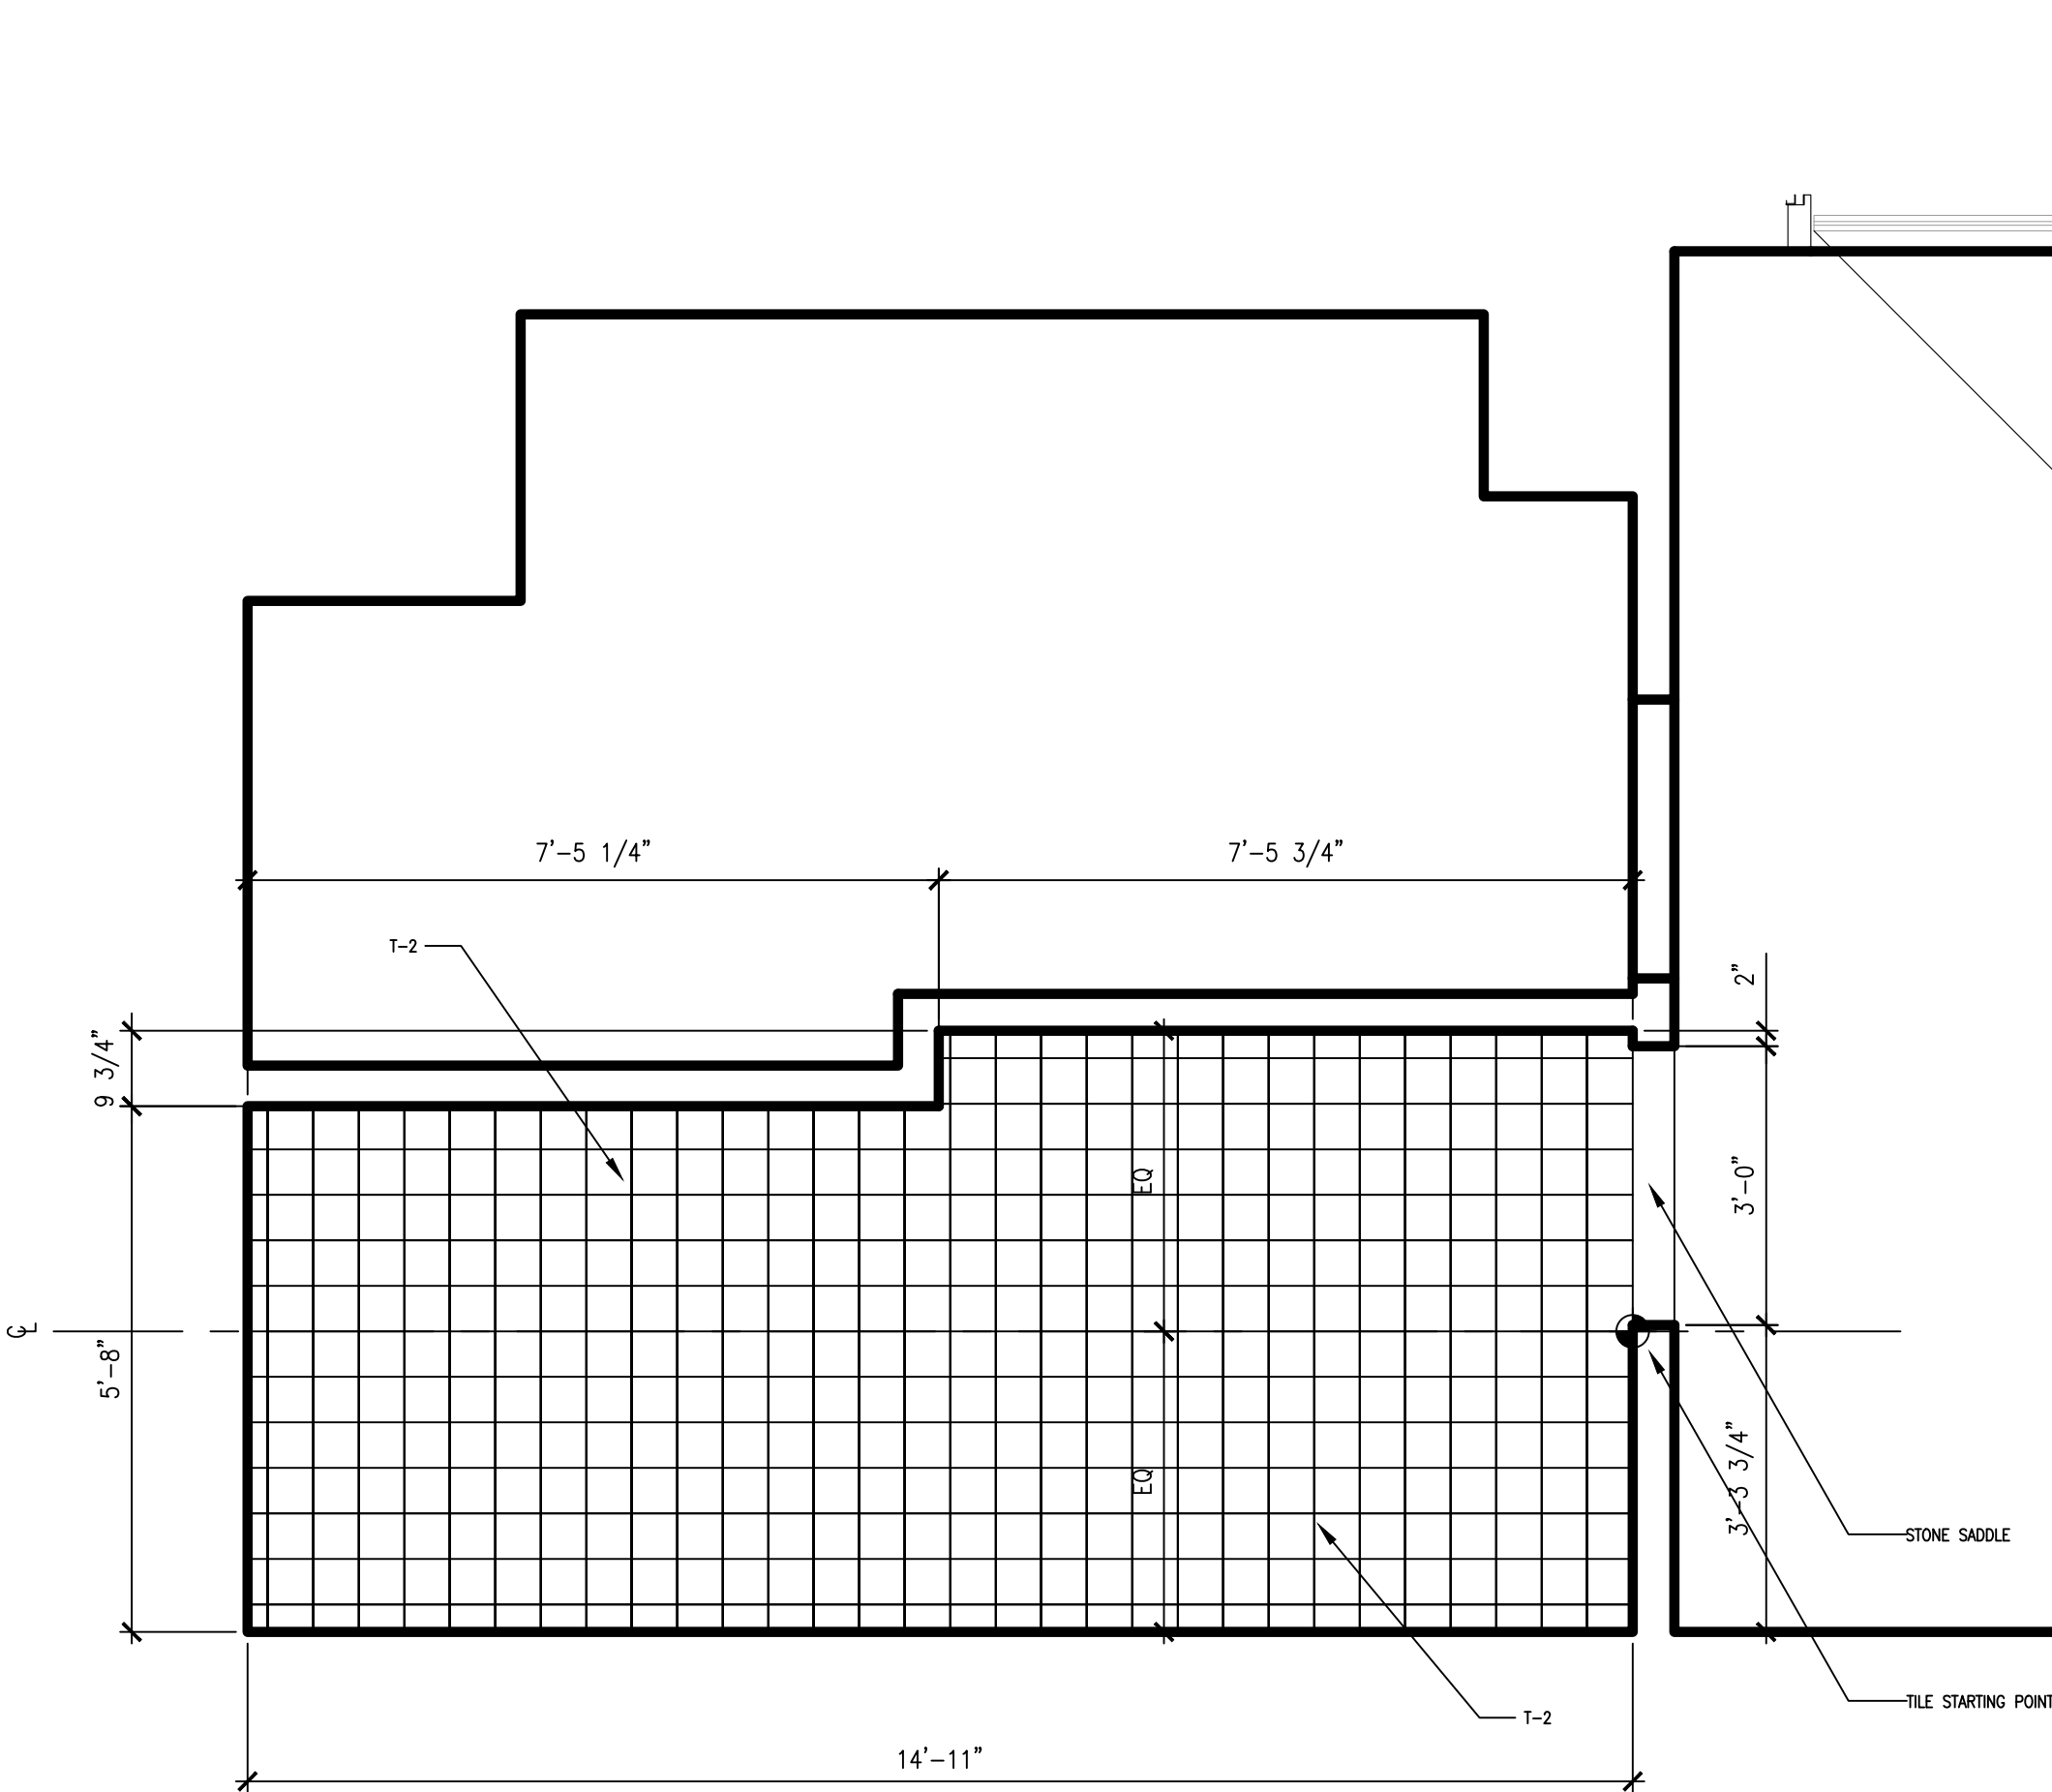


01 PLAN: SHOWROOM RESTROOM (M) 306
1/2"=1'-0"

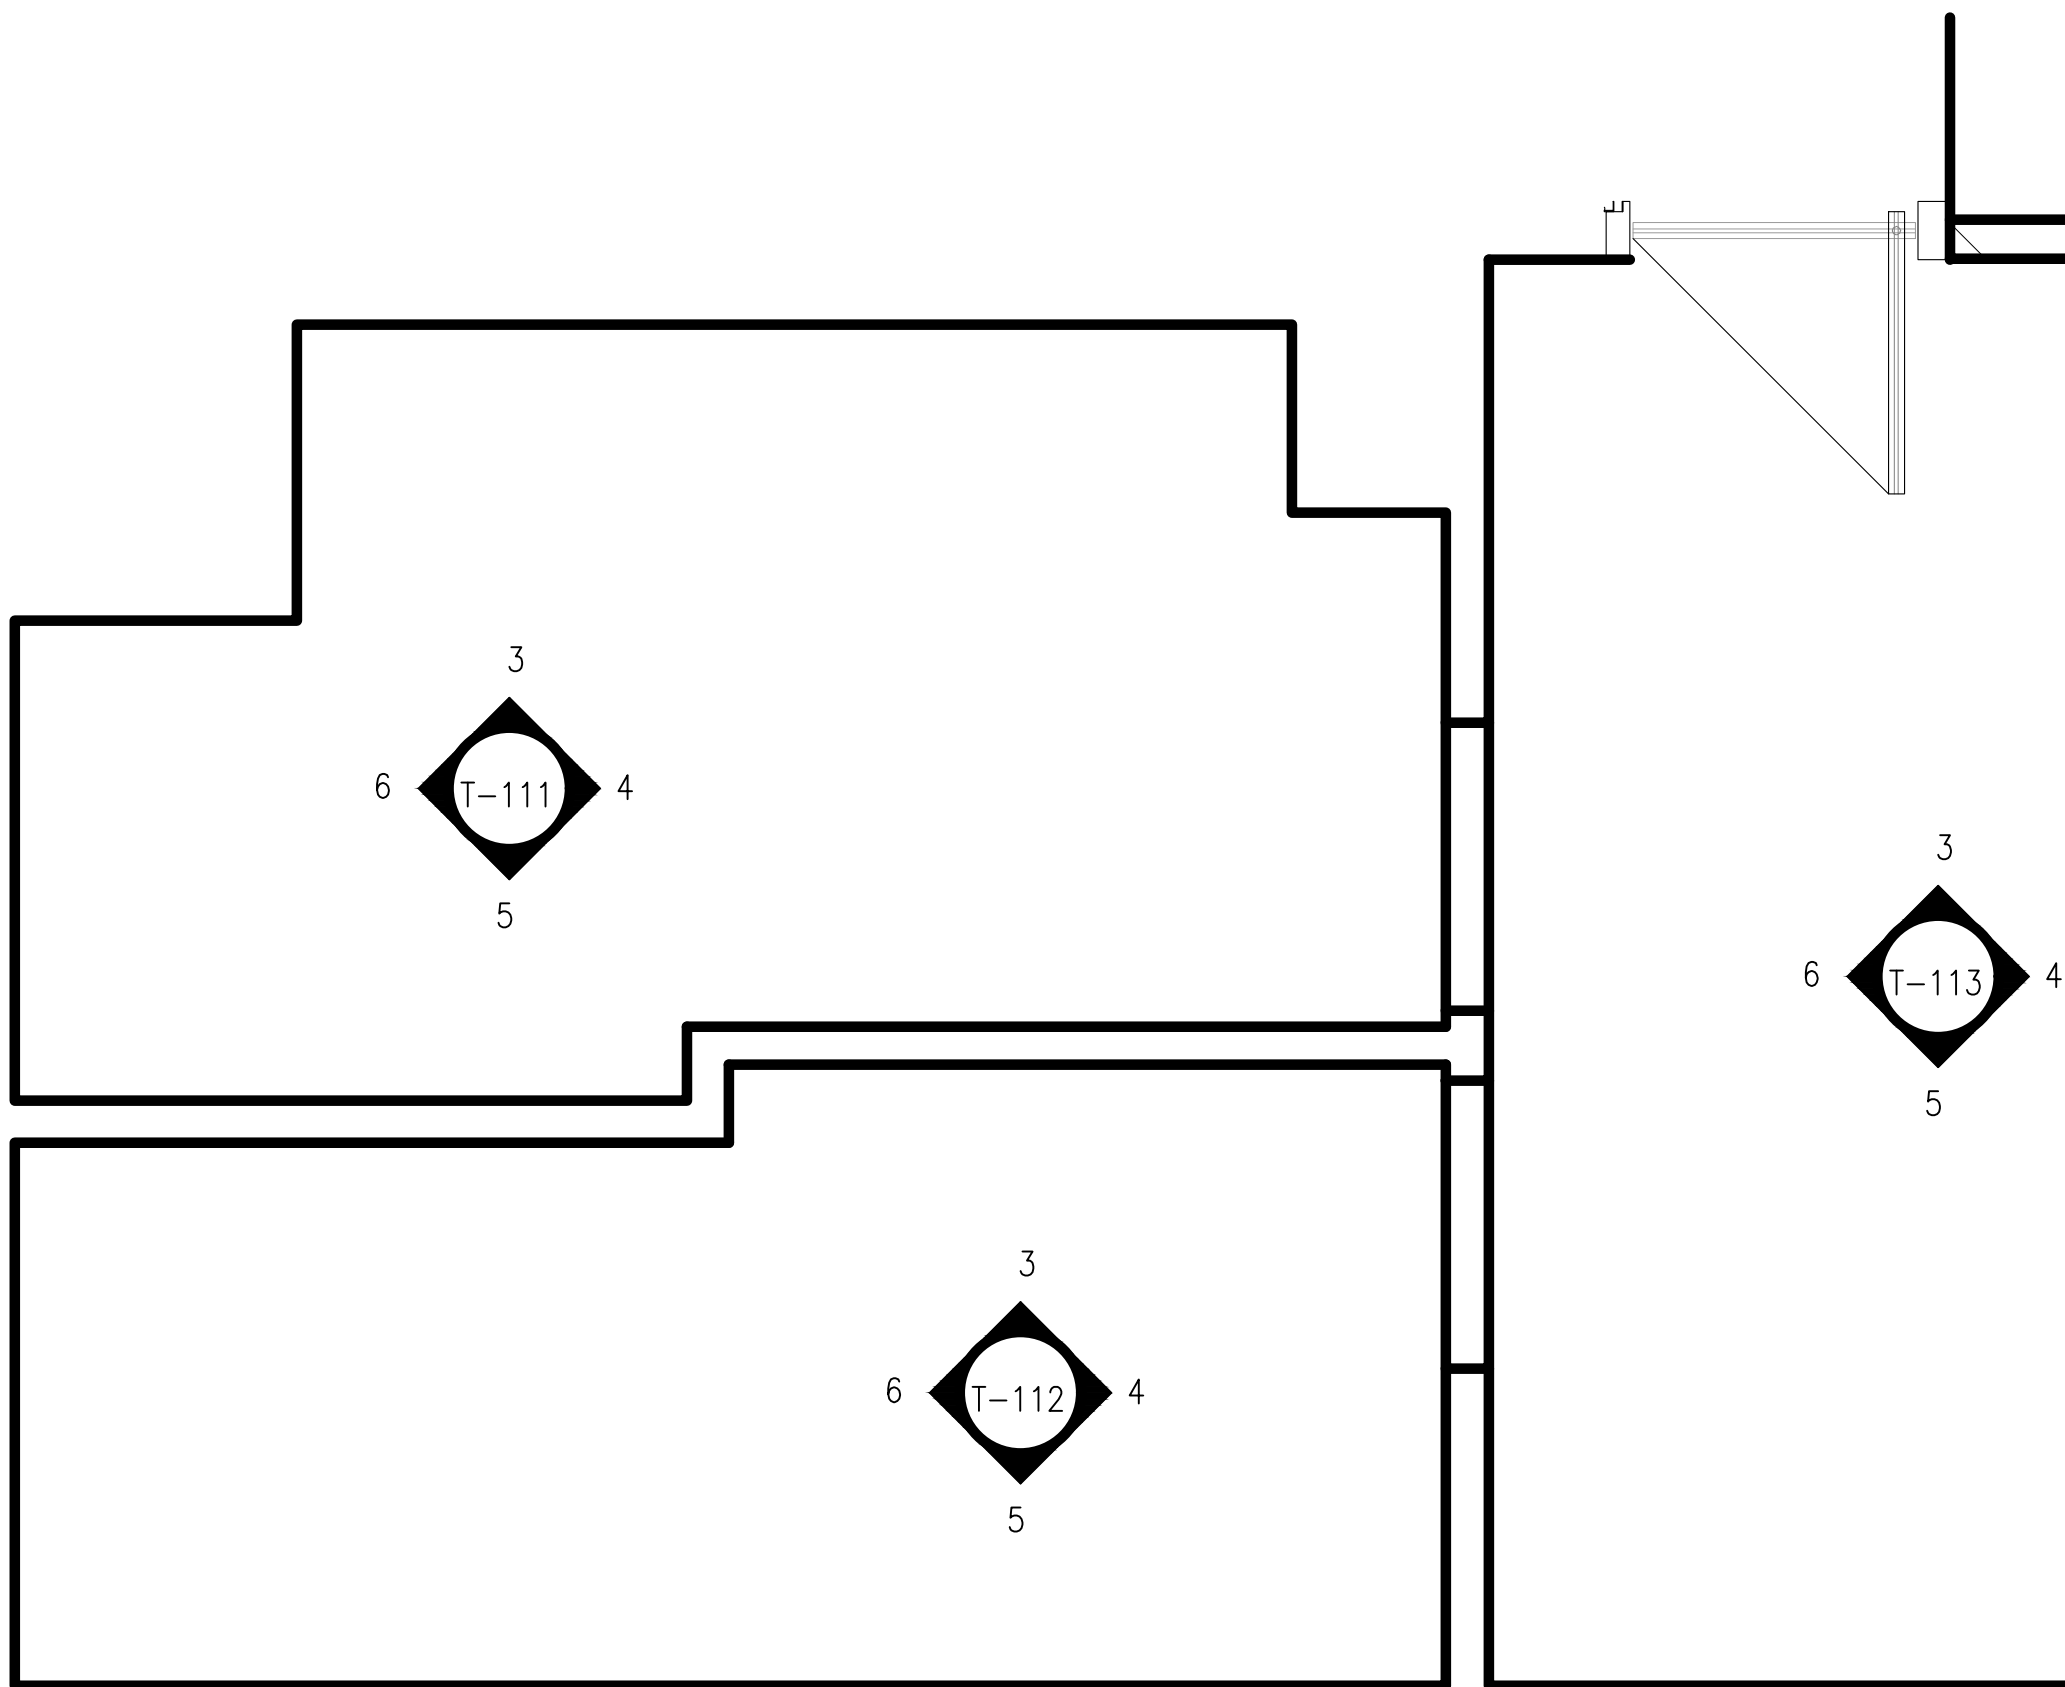


02 PLAN: SHOWROOM RESTROOM (M) 306
1/2"=1'-0"


PLEASE NOTE - MAKE SURE JOINTS TO MATCH FLOOR/WALL TILE
JOINT JOINTS WHERE POSSIBLE OTHERWISE GREAT JOINTS WILL BE
INDICATED

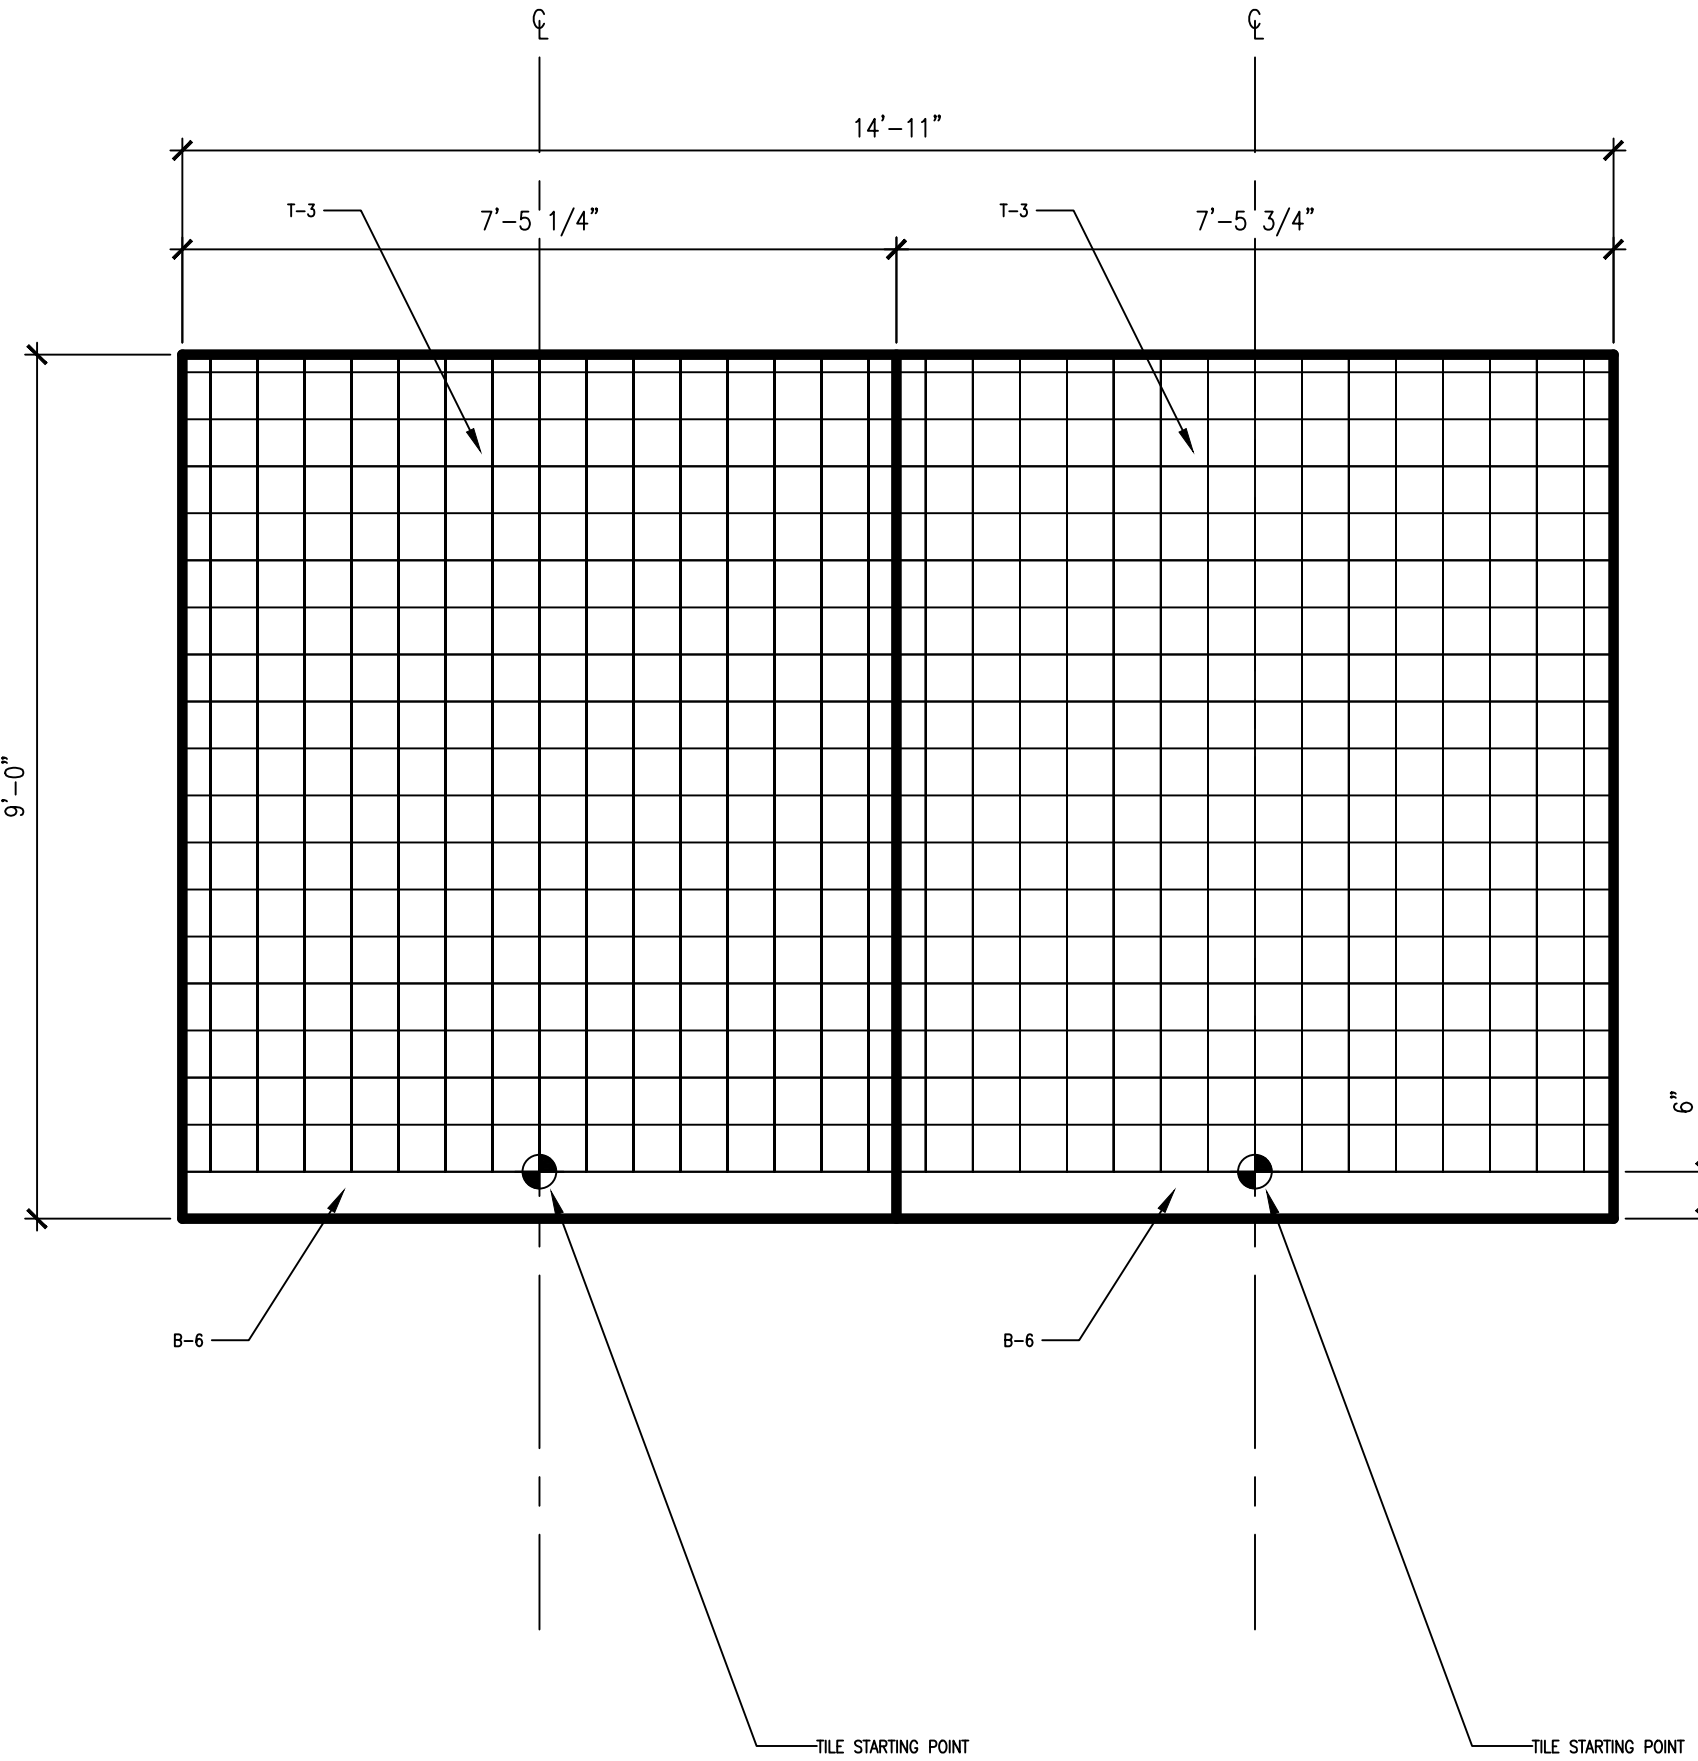


03 ELEVATION: NORTH
1/2"=1'-0"

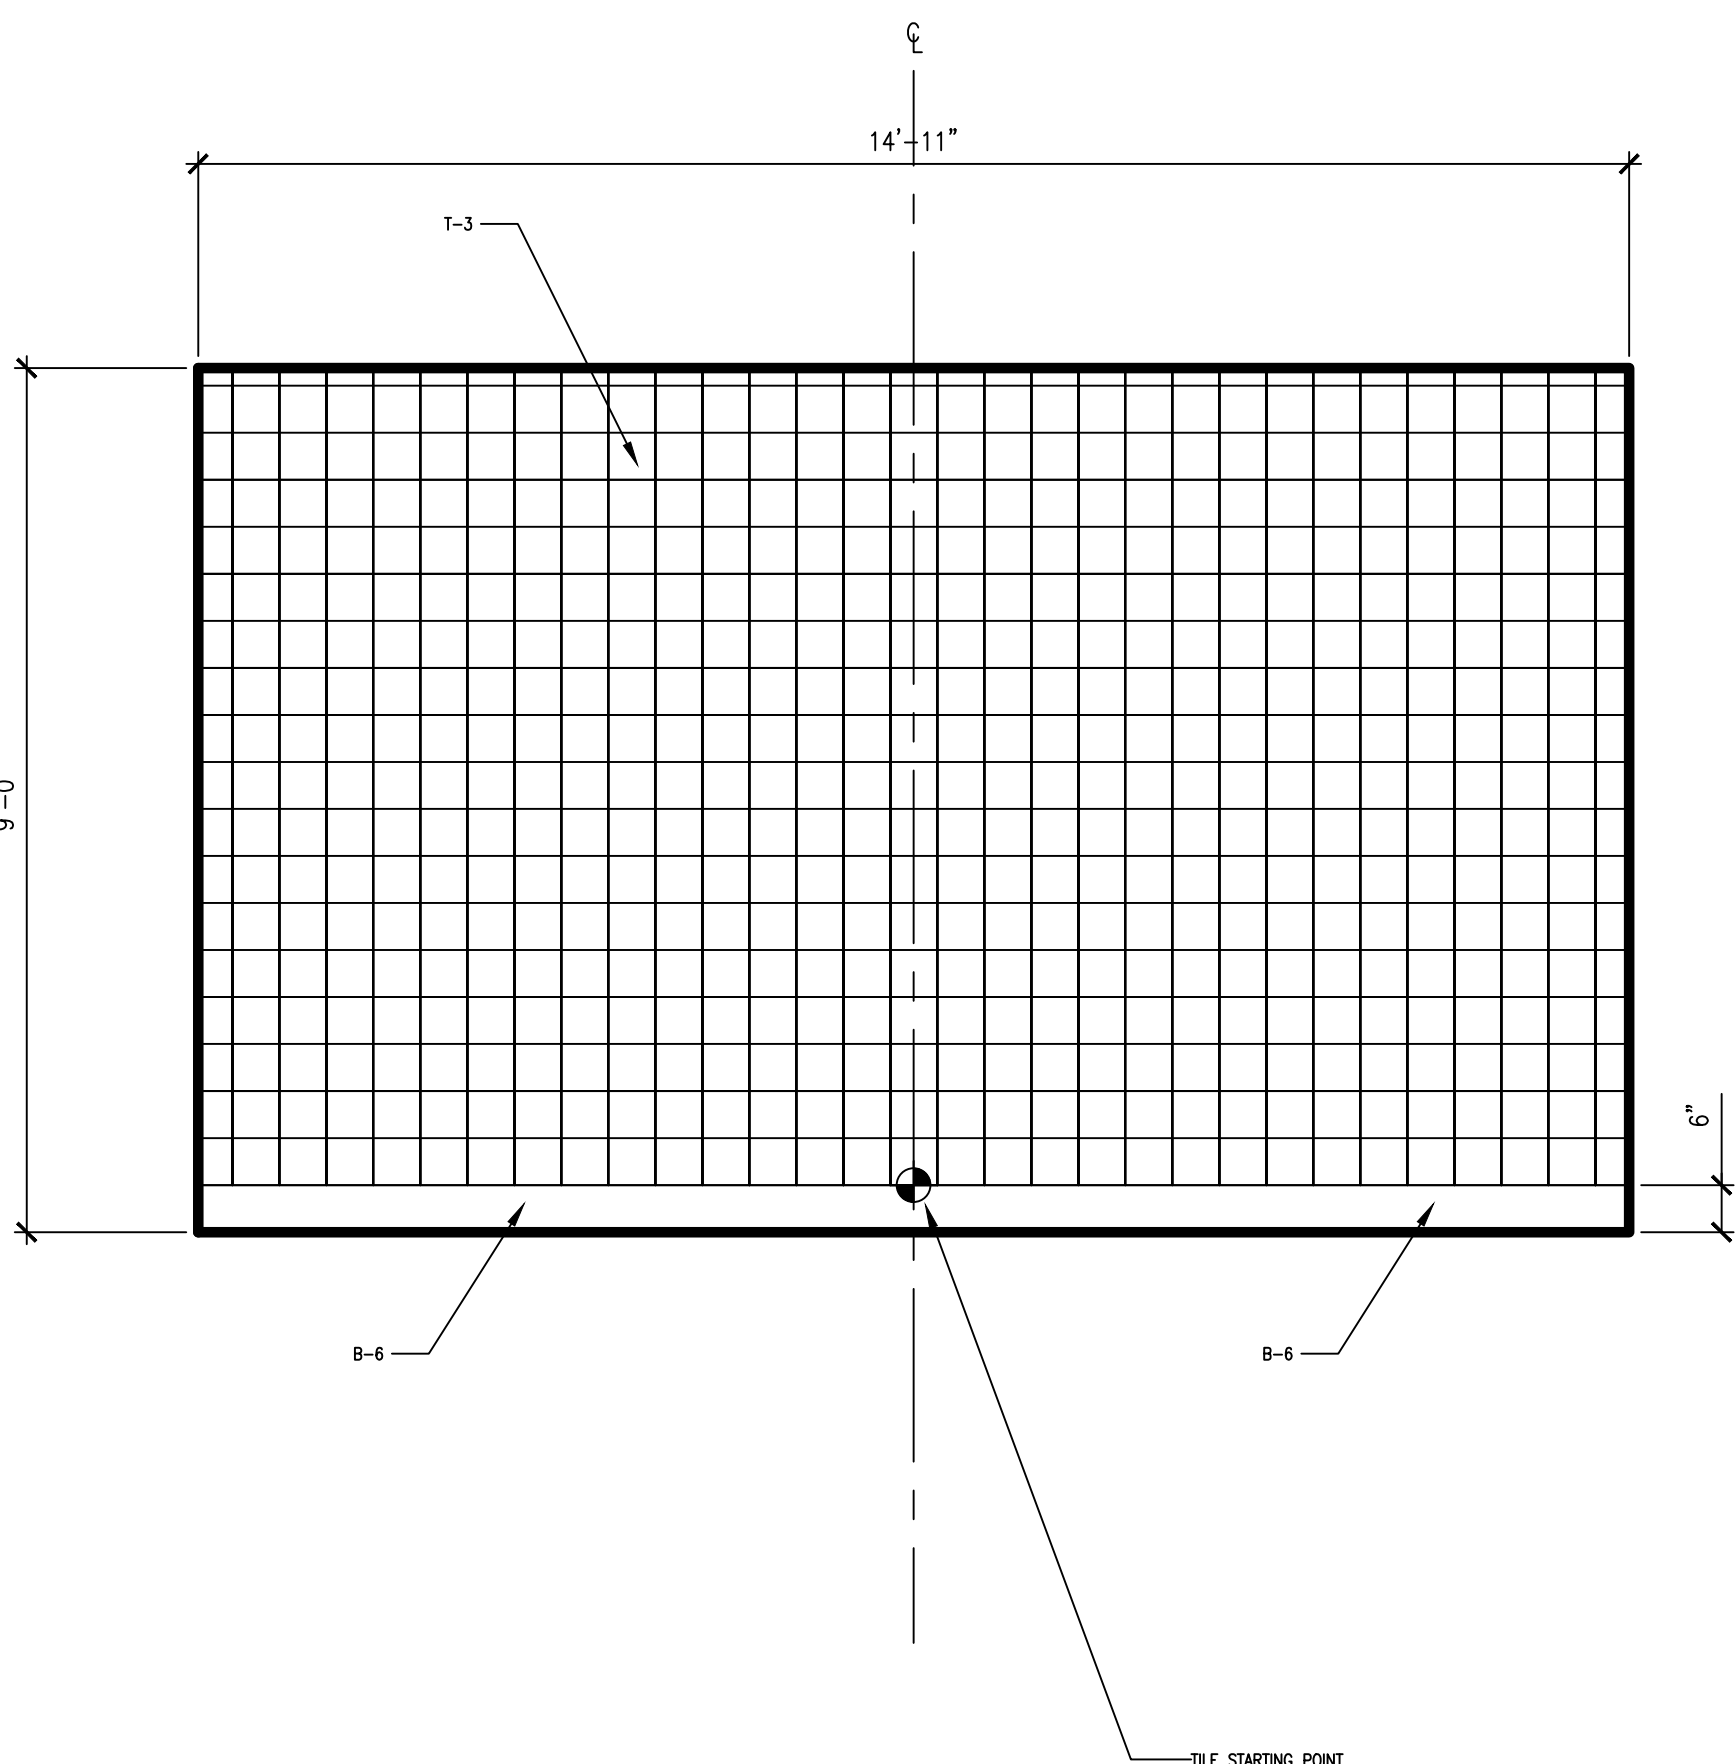

05 ELEVATION: SOUTH
1/2"=1'-0"

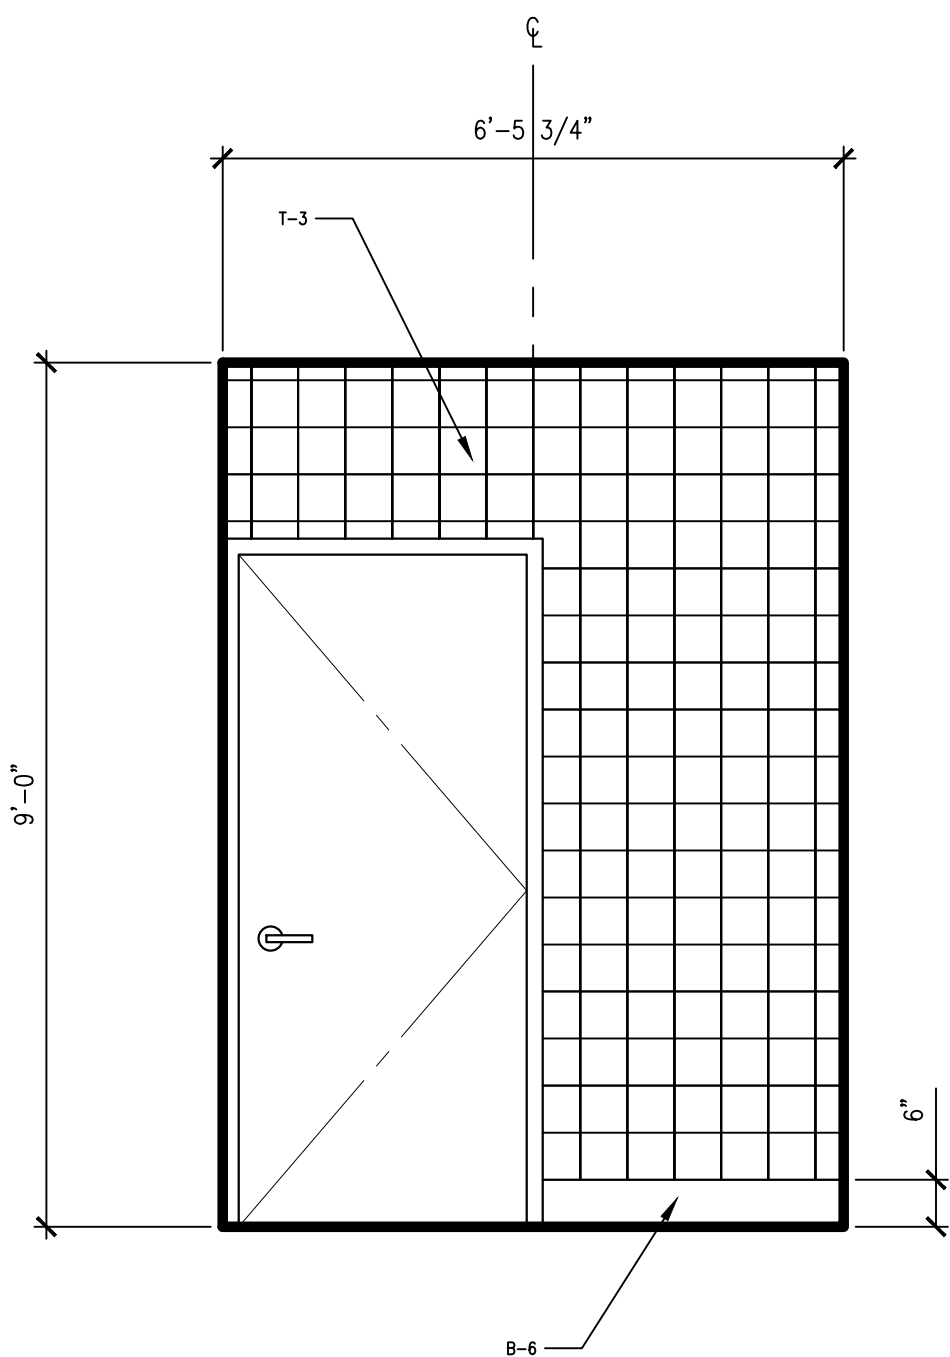

04 ELEVATION: EAST
1/2"=1'-0"

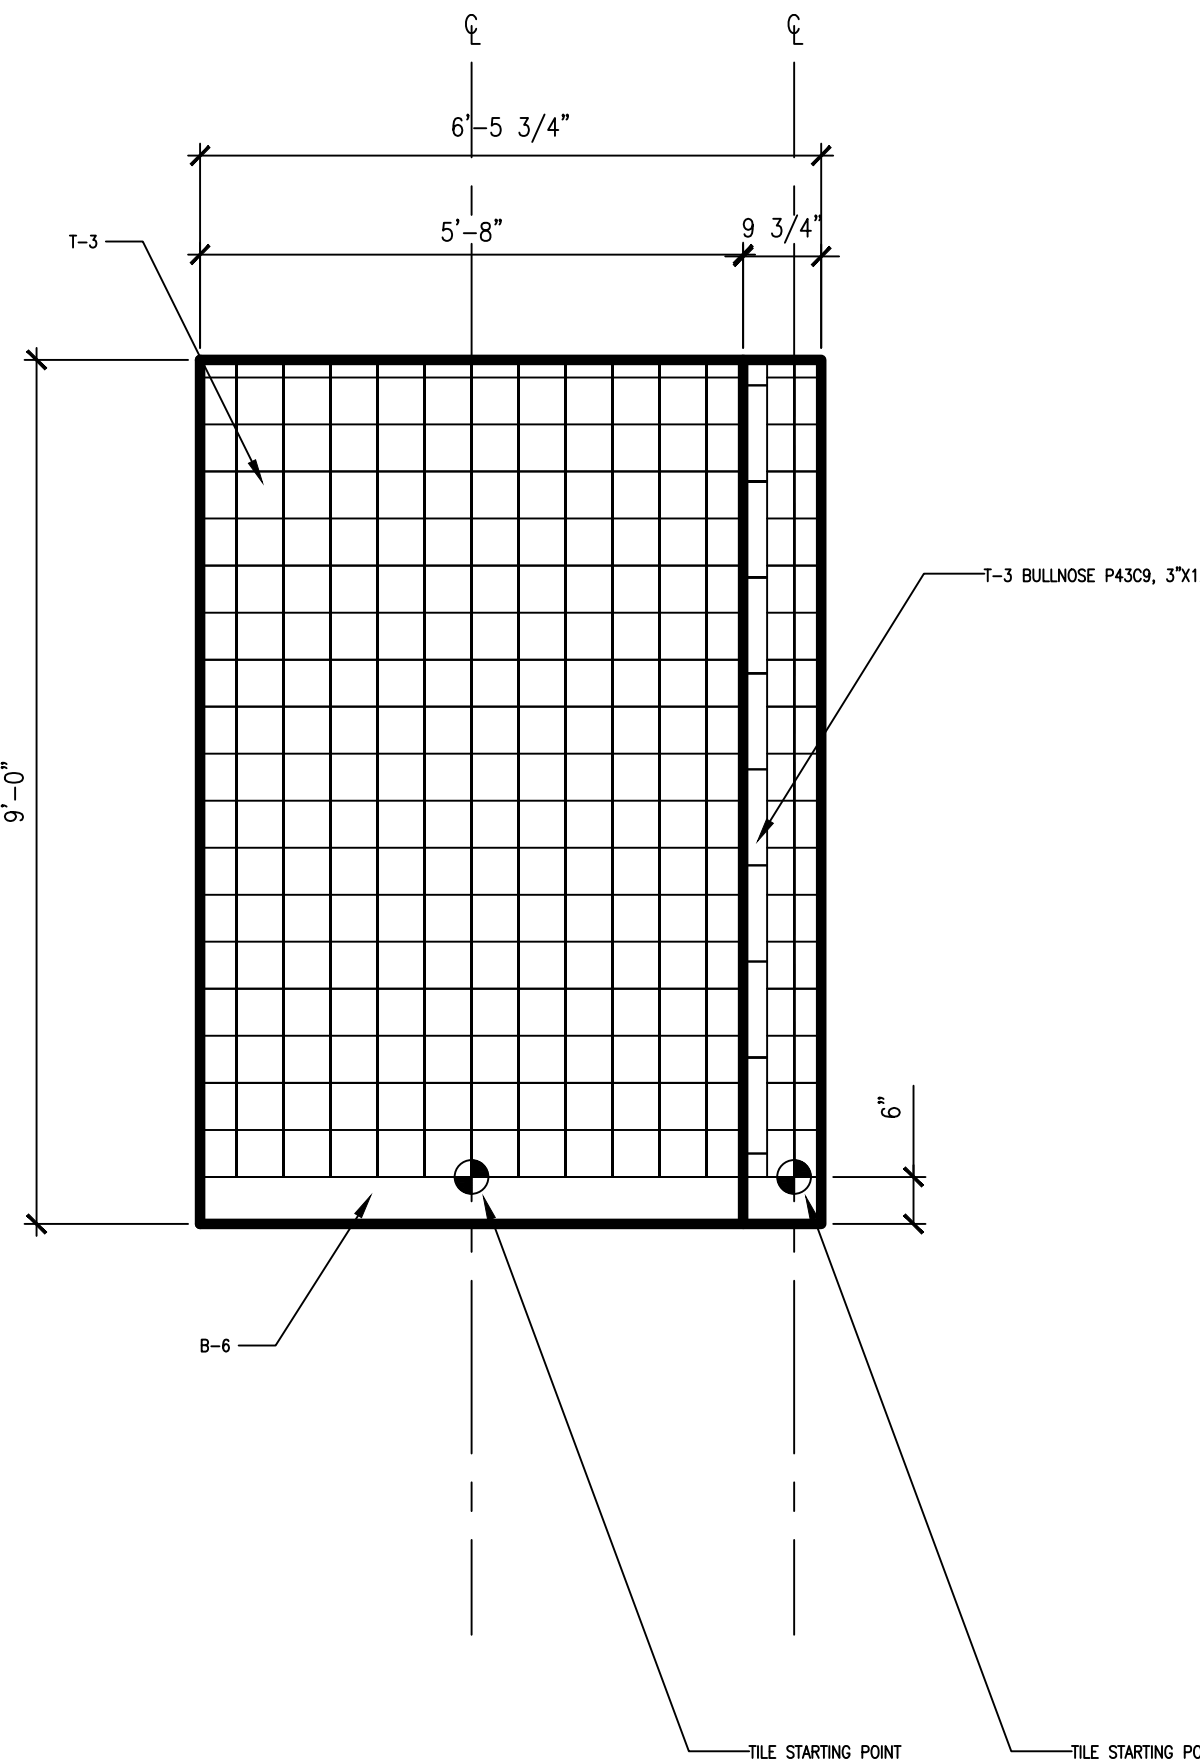

06 ELEVATION: WEST
1/2"=1'-0"

AUSTRO TILE & STONE, LLC
30-25 93RD STREET
EAST ELMHURST, NY 11369

CONTRACTOR:
JRM CONSTRUCTION
MANAGEMENT, LLC
242 WEST 36TH STREET
11TH FLOOR
NEW YORK, NY 10018

INTERIOR DESIGNER:


ISSUE FOR APPROVAL 09/09/24
ISSUE NAME DATE

ARCHITECT:
KENNETH PARK ARCHITECTS
360 LEXINGTON AVENUE
NEW YORK, NY 10017PHONE:
212-599-0044


PROJECT NAME:
LACOSTE
575 5TH AVENUE
NEW YORK, NY 10017

SHEET NAME:
3RD FLOOR RESTROOMS
PLAN/ELEVATIONS


DATE:
PROJECT NO.:
PRINCIPAL:
DRAWING BY:
CHECKED BY:
SCALE:
DWG No.:
T-112
8 of 21

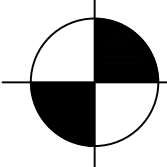

STARTING POINT

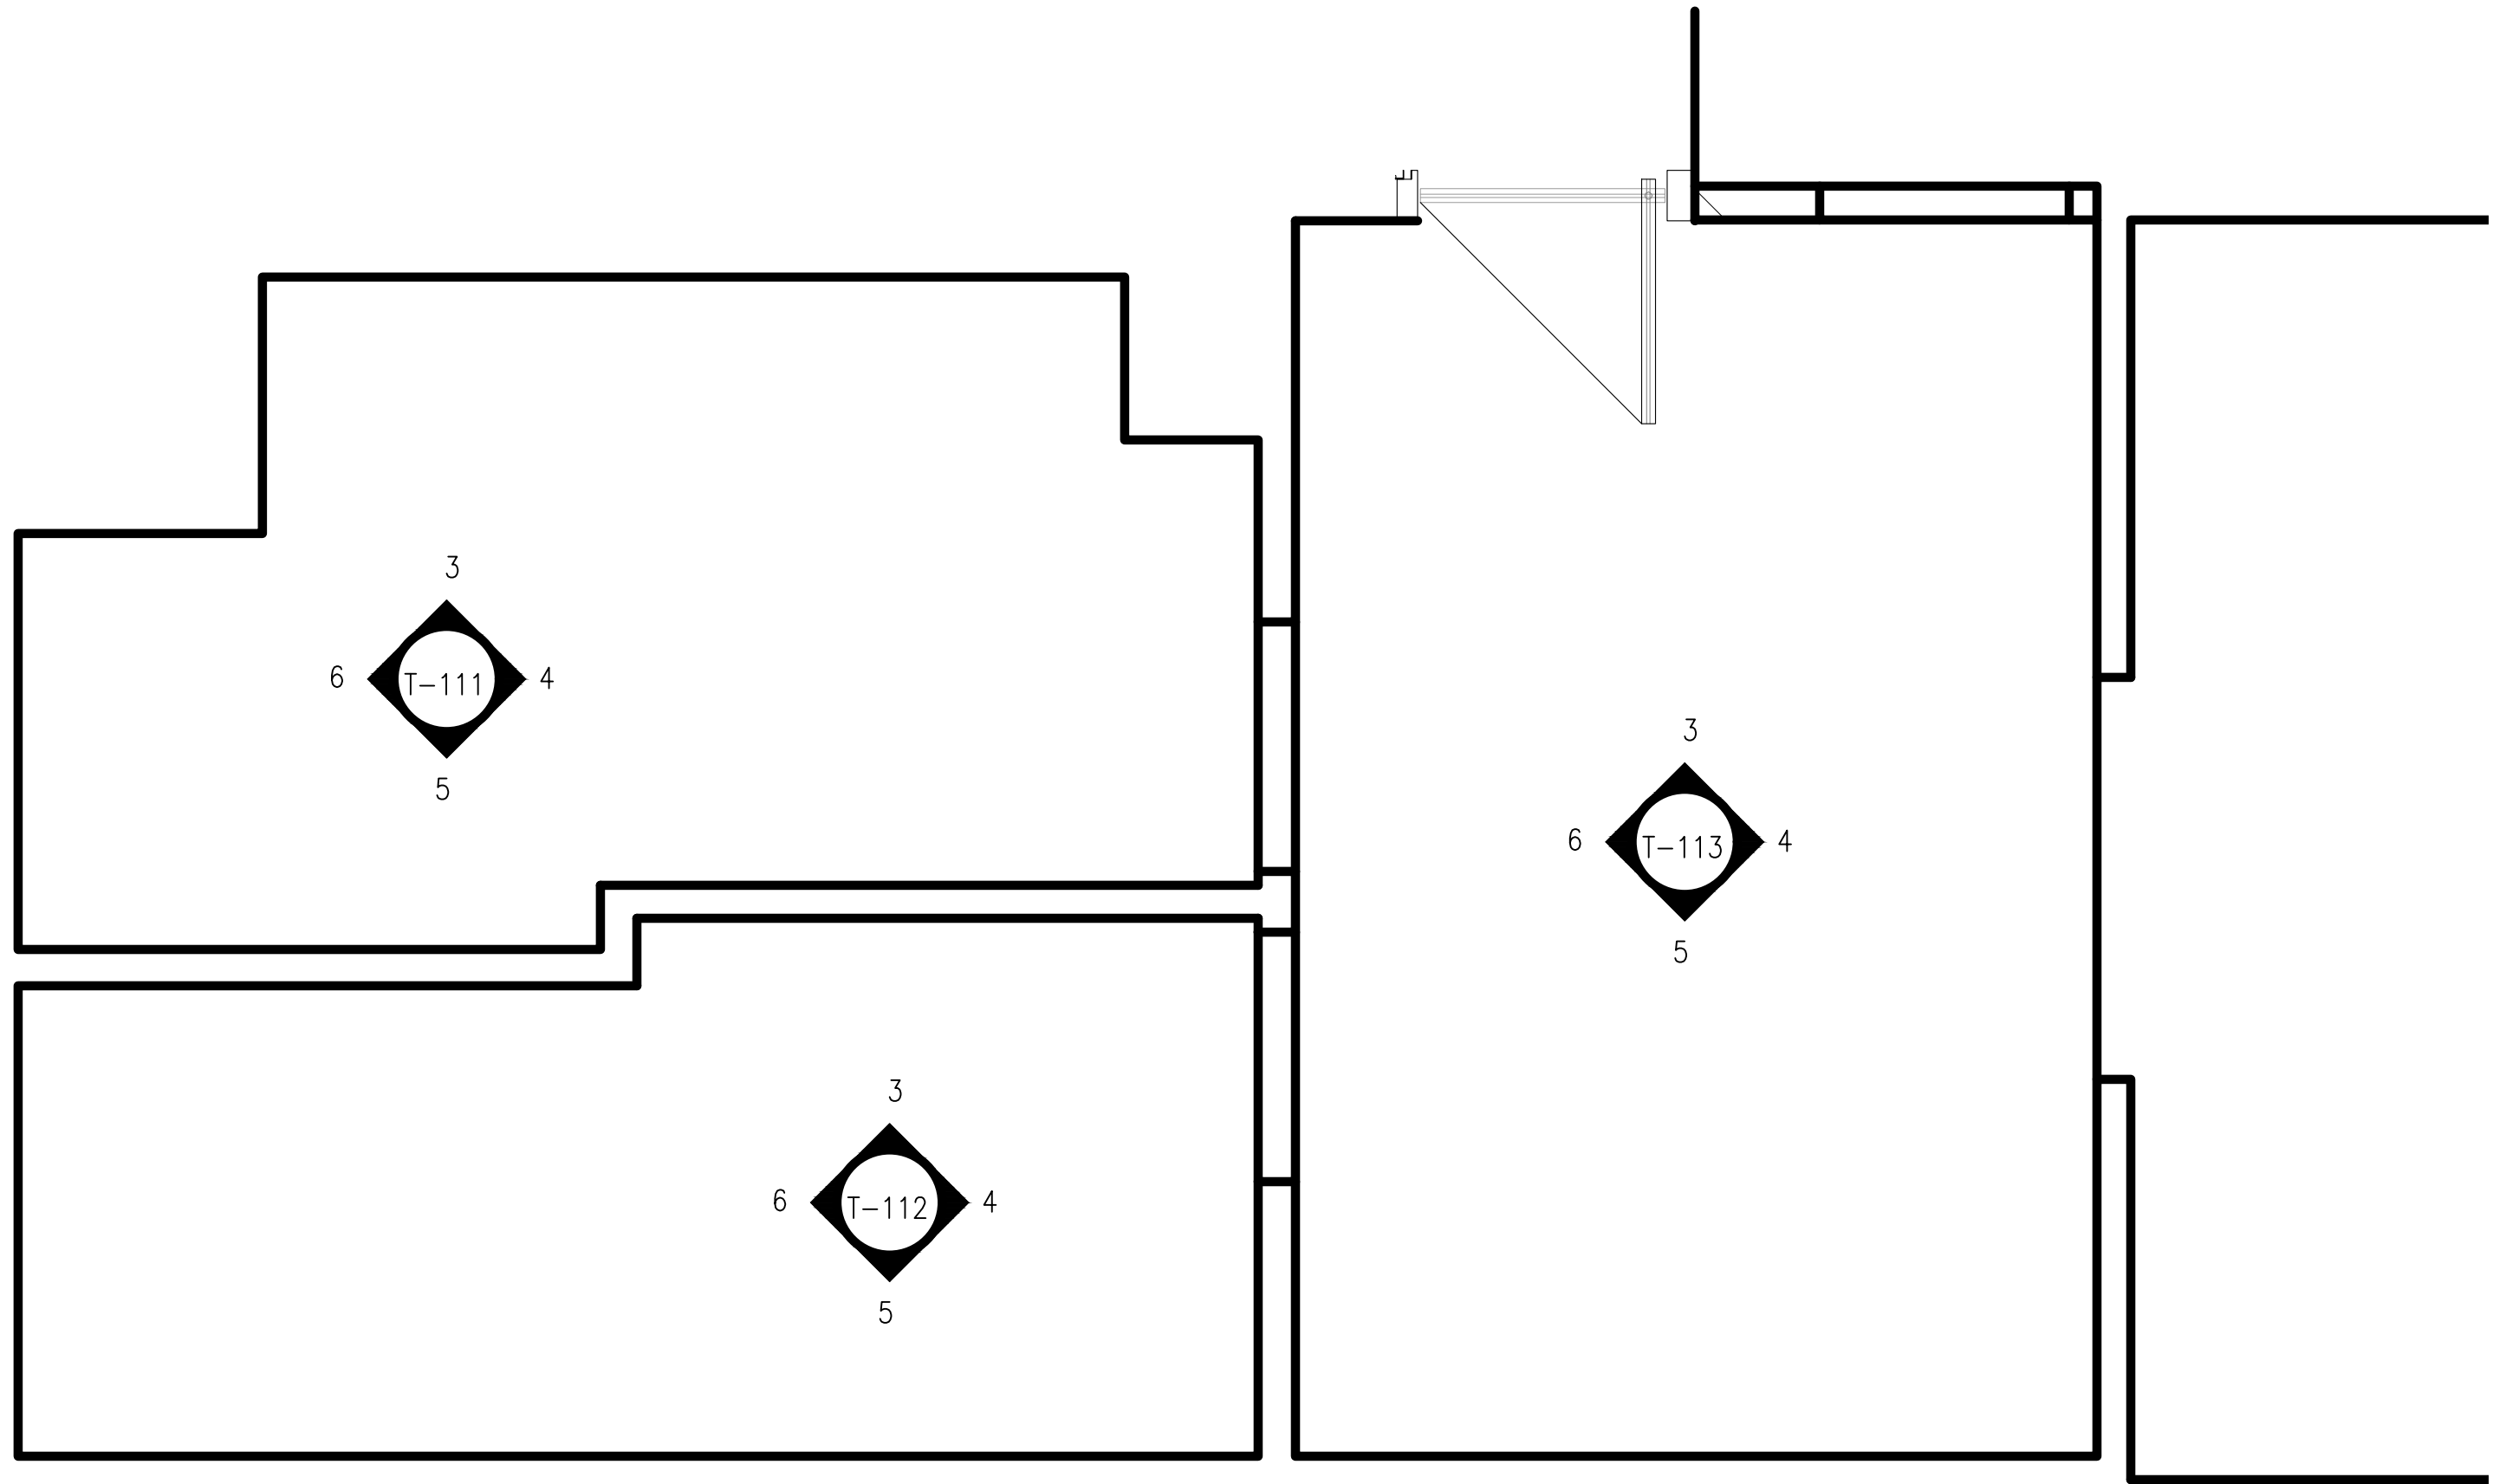


03 PLAN: SHOWROOM PANTRY 311
1/2"=1'-0"

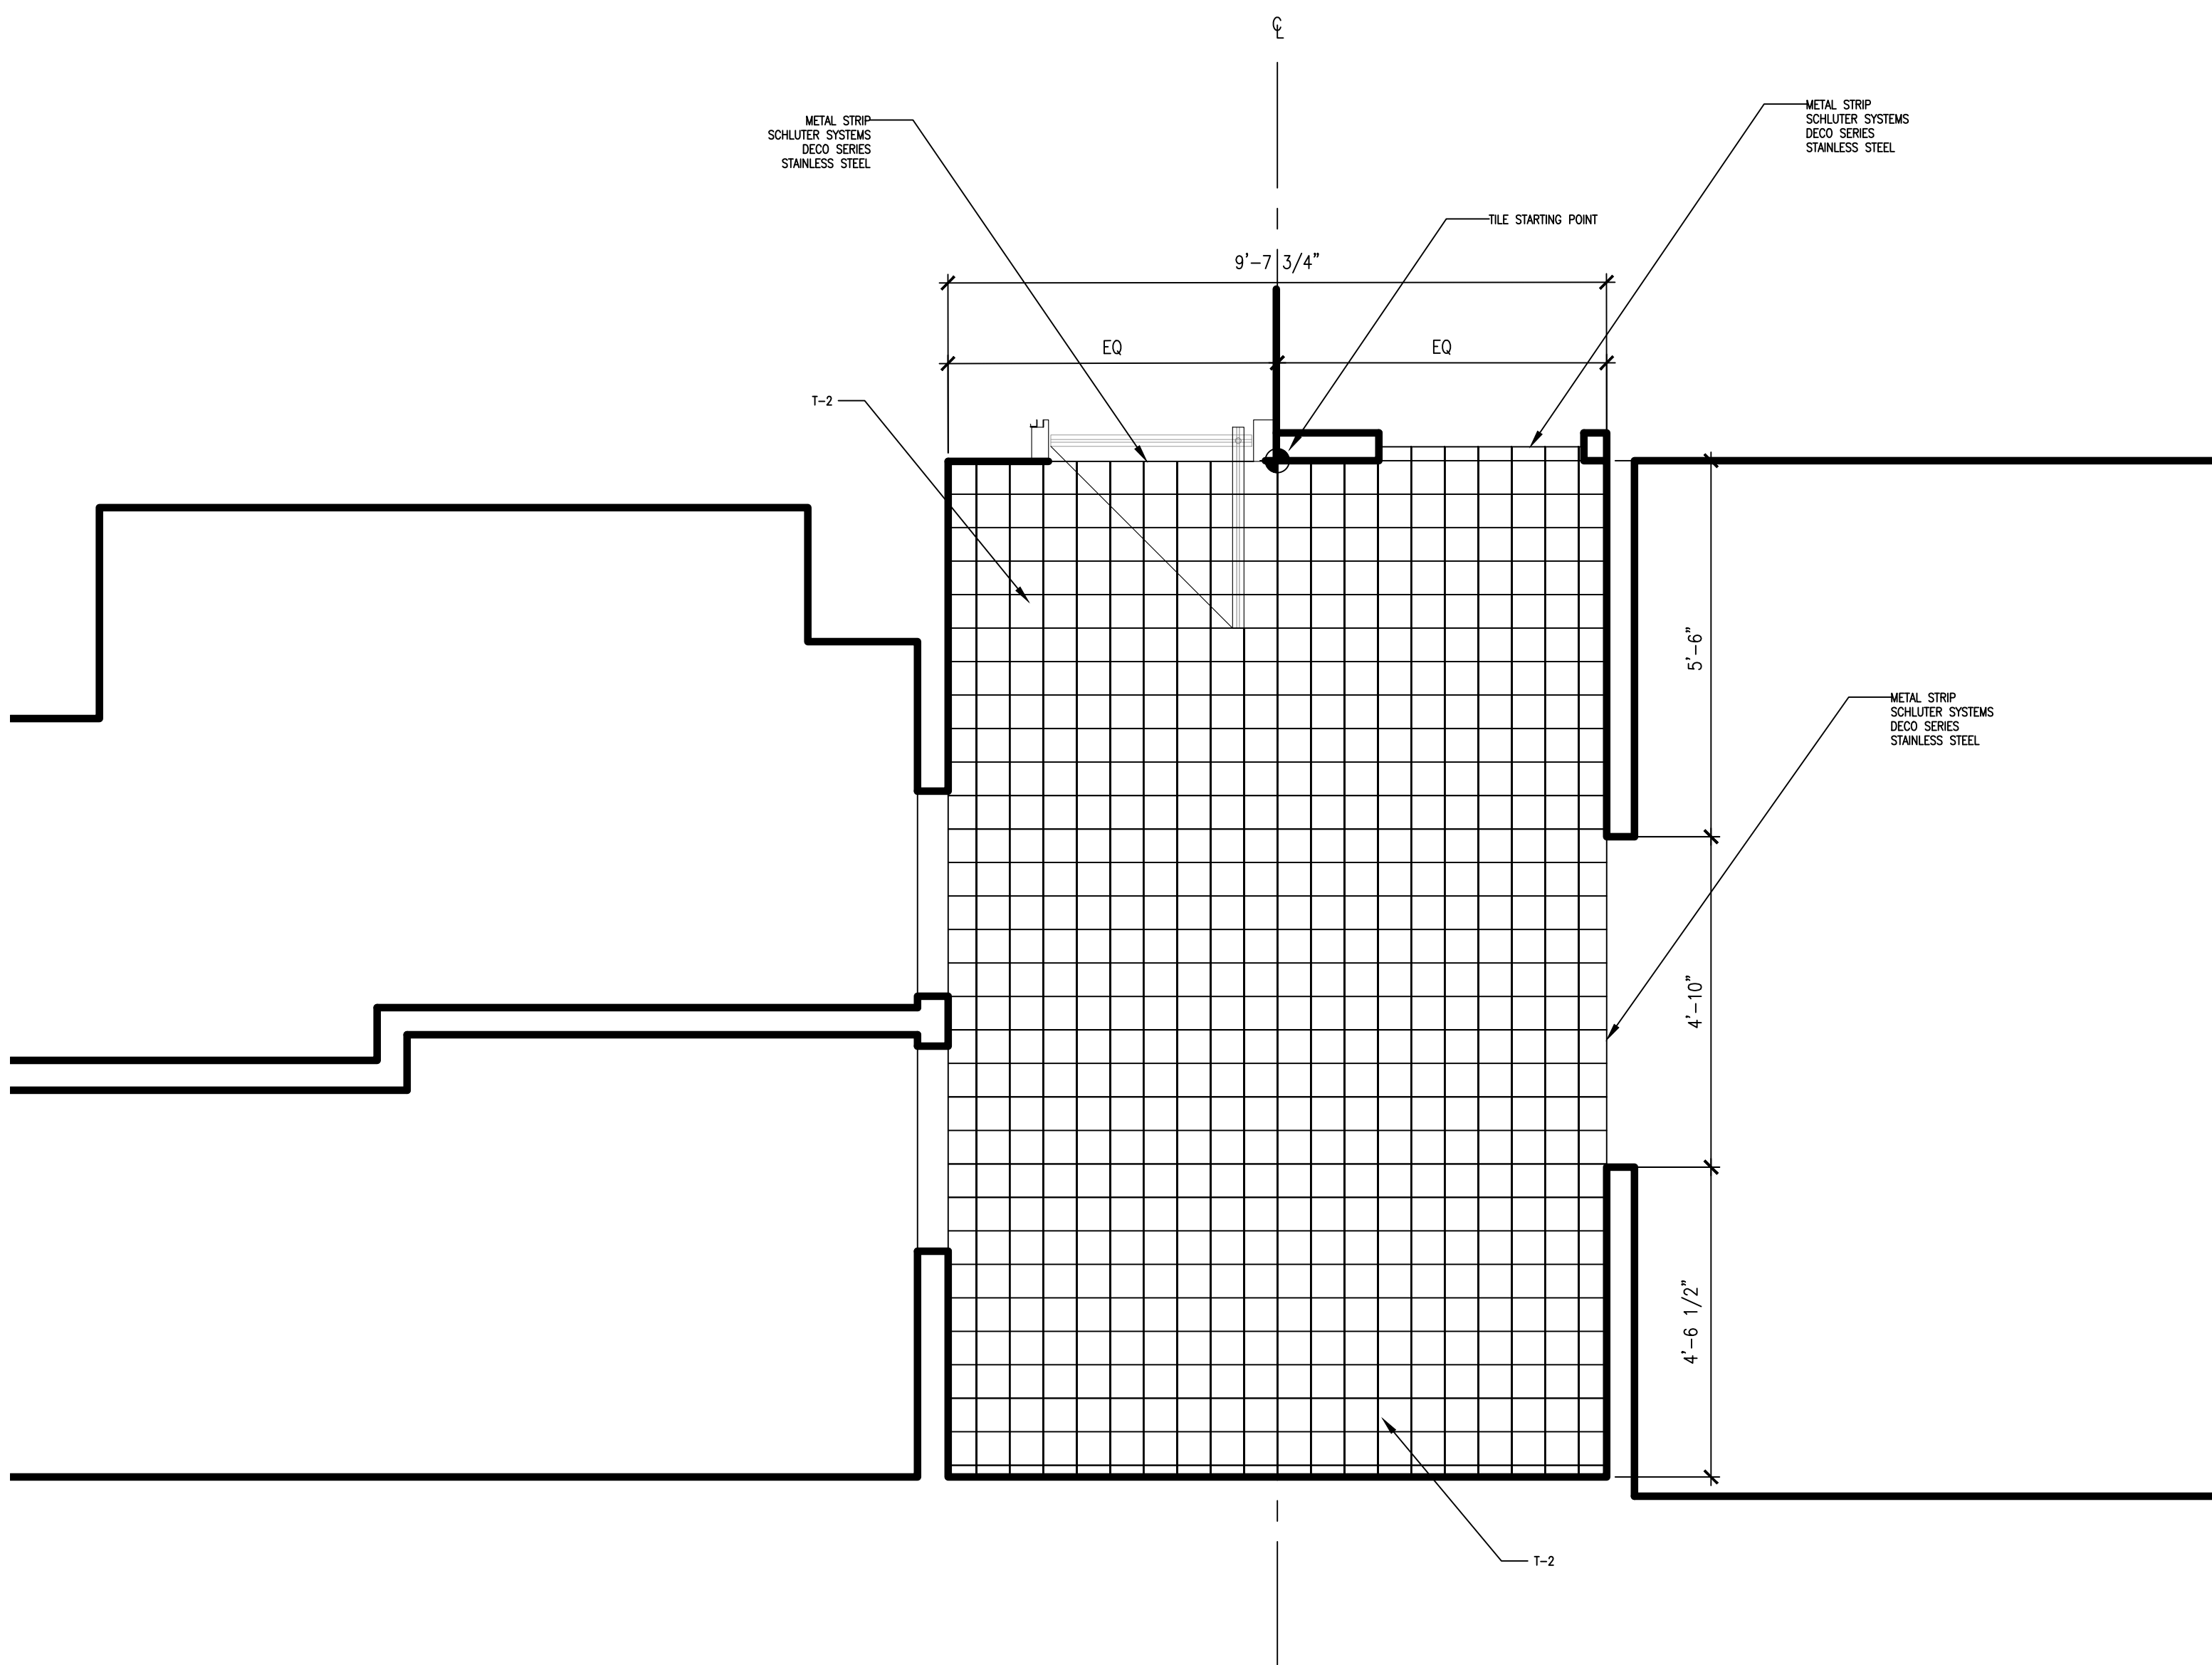


01 PLAN: SHOWROOM PANTRY 311
1/2"=1'-0"


PLEASE NOTE - BASE GRAY JOINTS TO MATCH FLOOR TILE GROUT
JOINTS WHERE POSSIBLE OTHERWISE GRAY JOINTS WILL BE
INCLUDED

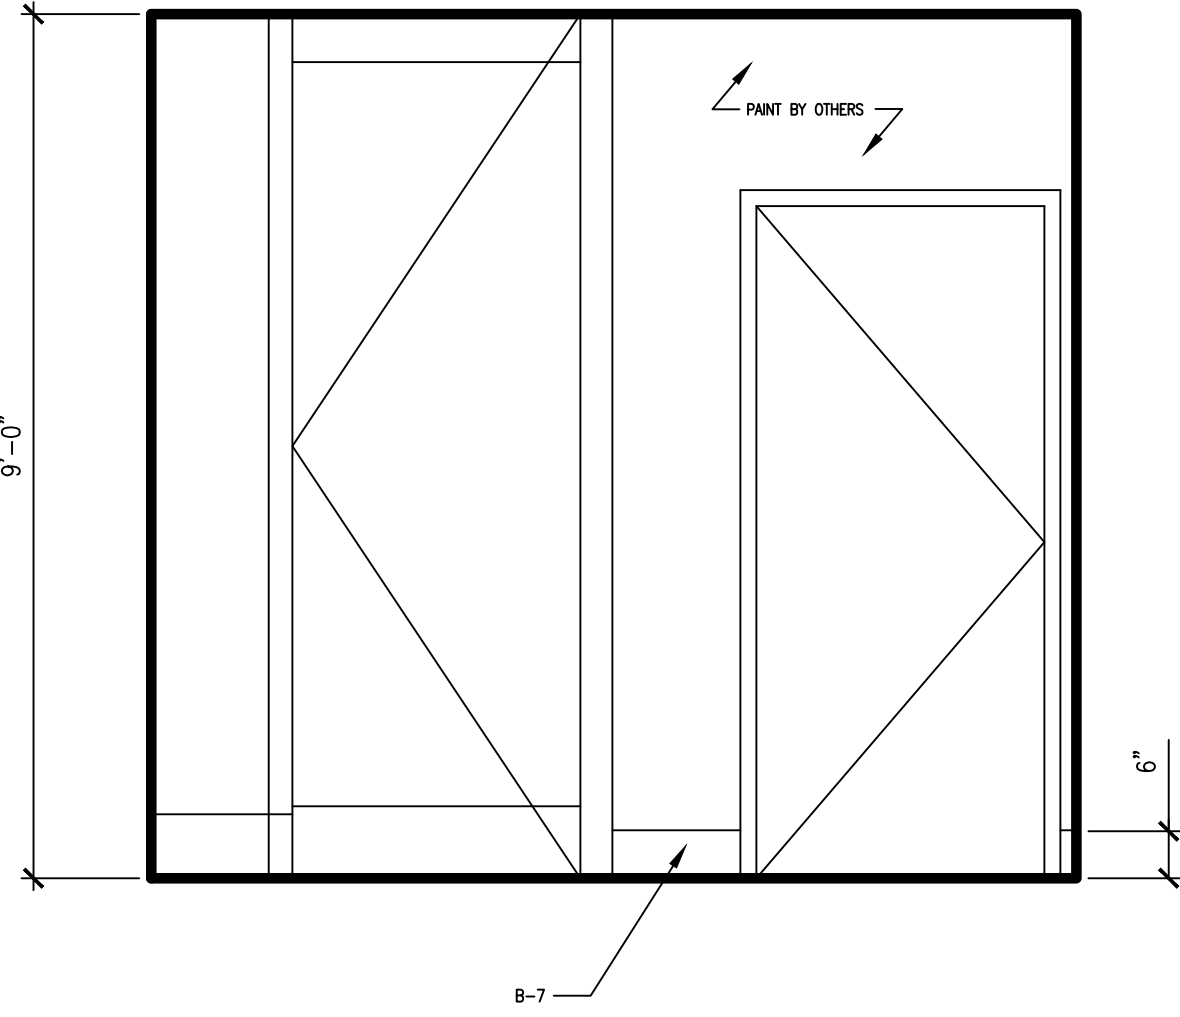


04 ELEVATION: NORTH
1/2"=1'-0"

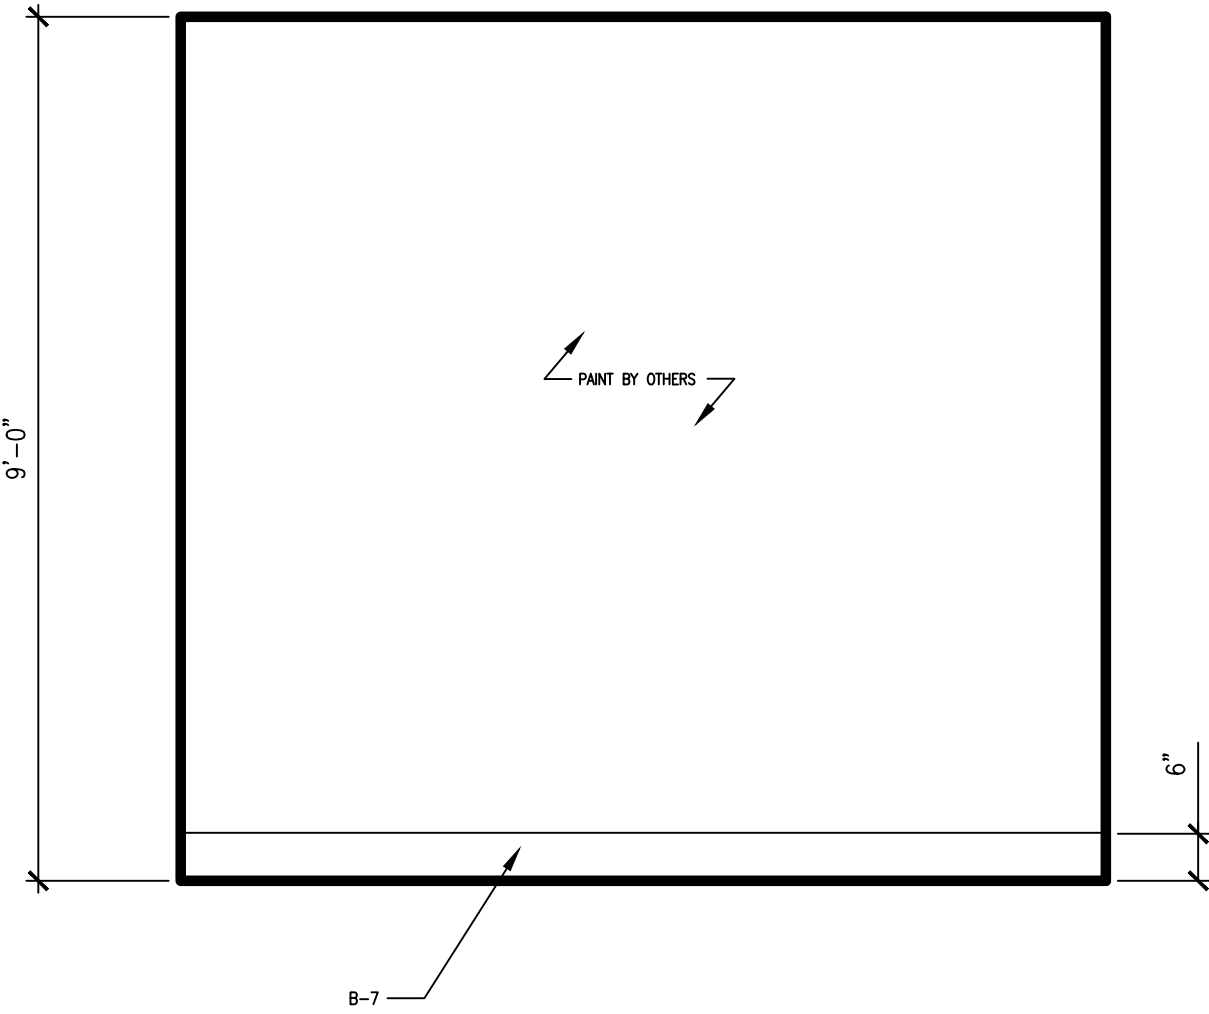


06 ELEVATION: SOUTH
1/2"=1'-0"

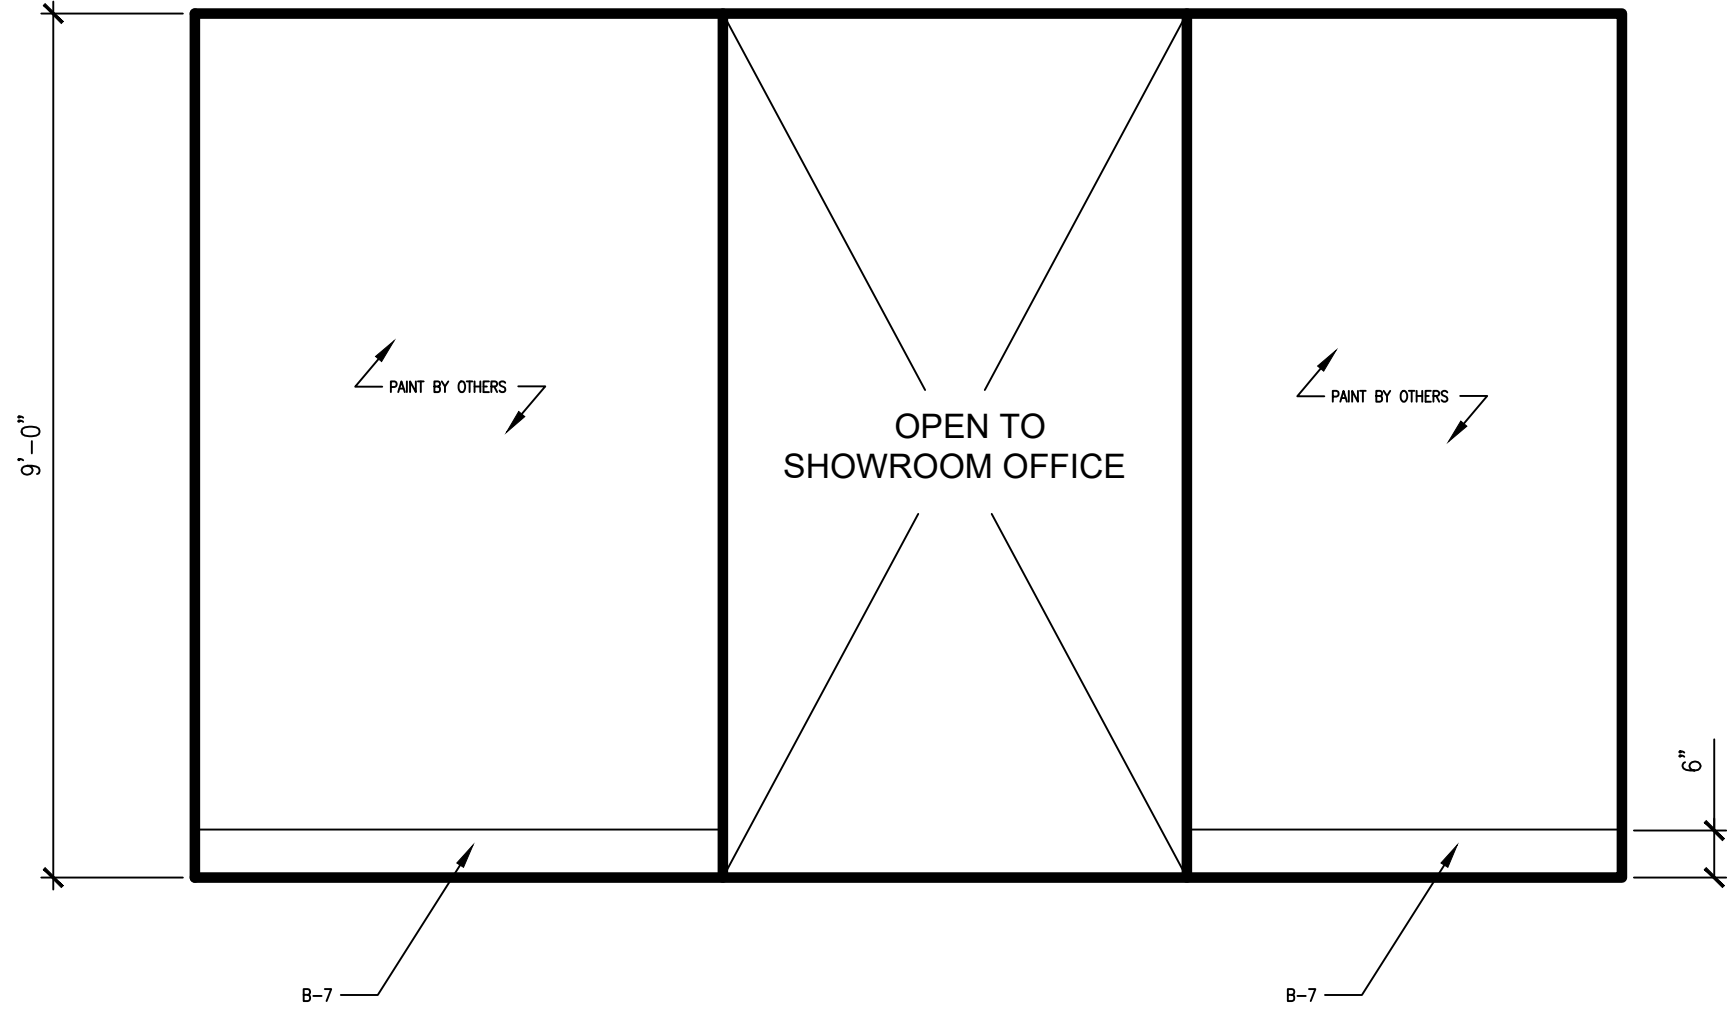

05 ELEVATION: EAST
1/2"=1'-0"

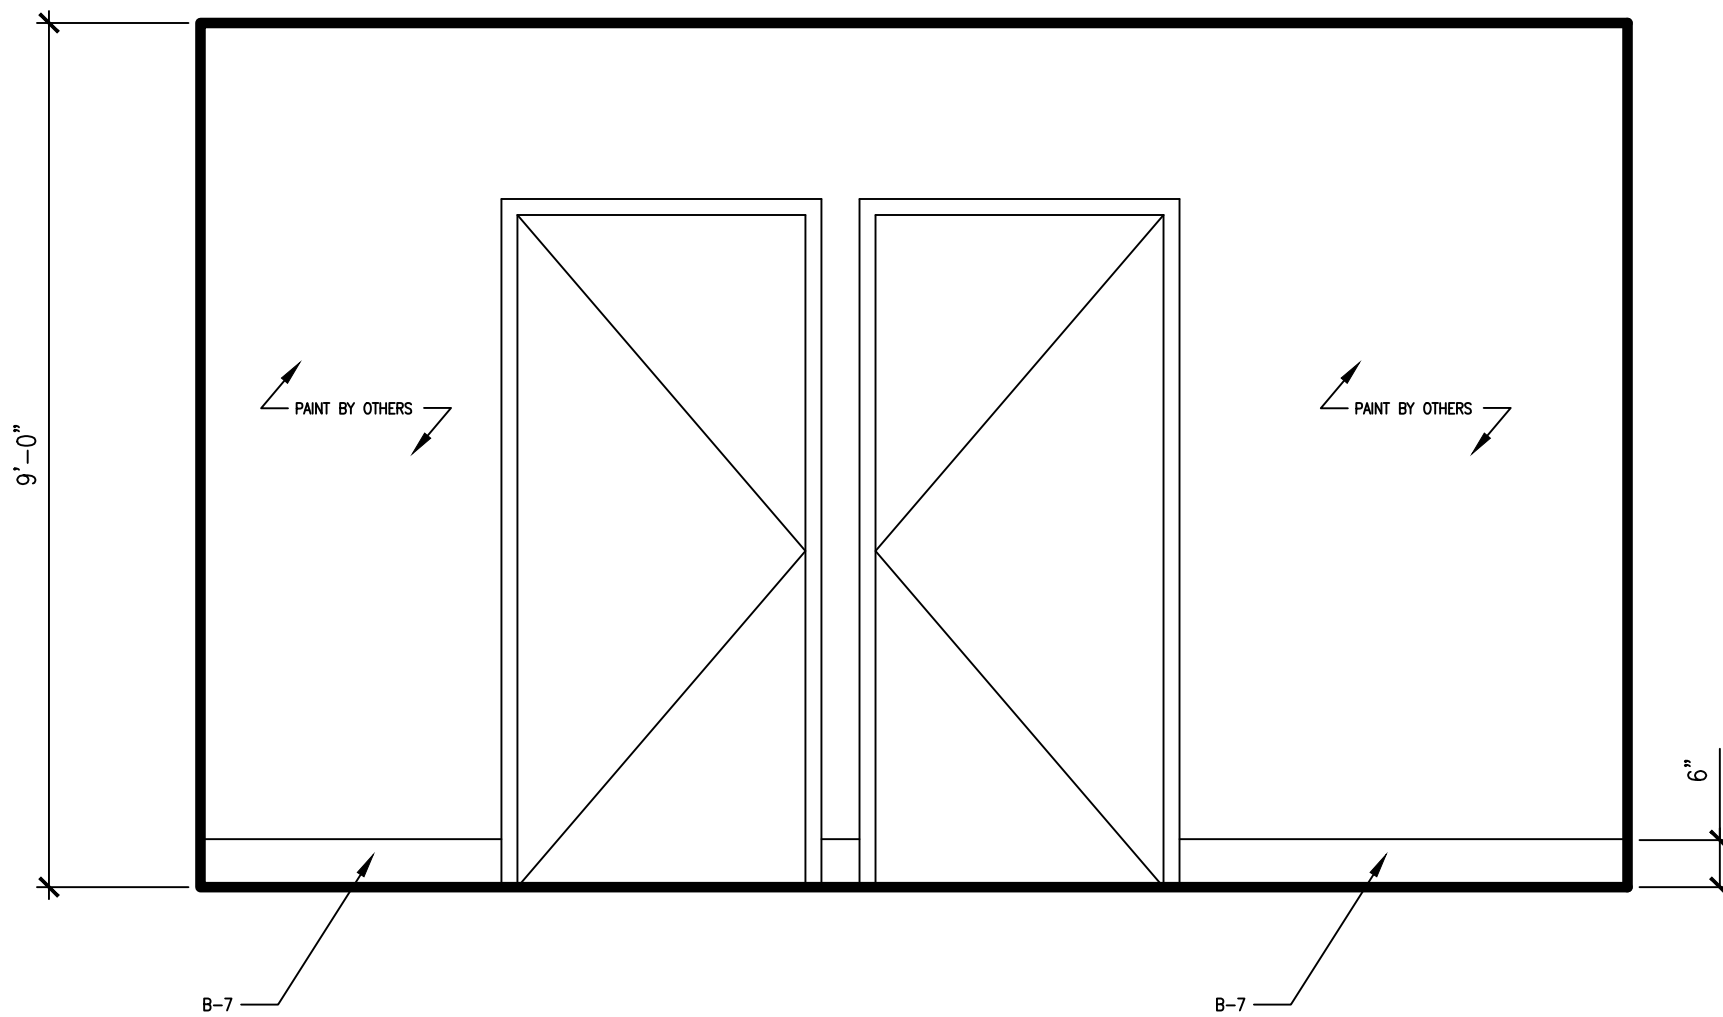

07 ELEVATION: WEST
1/2"=1'-0"

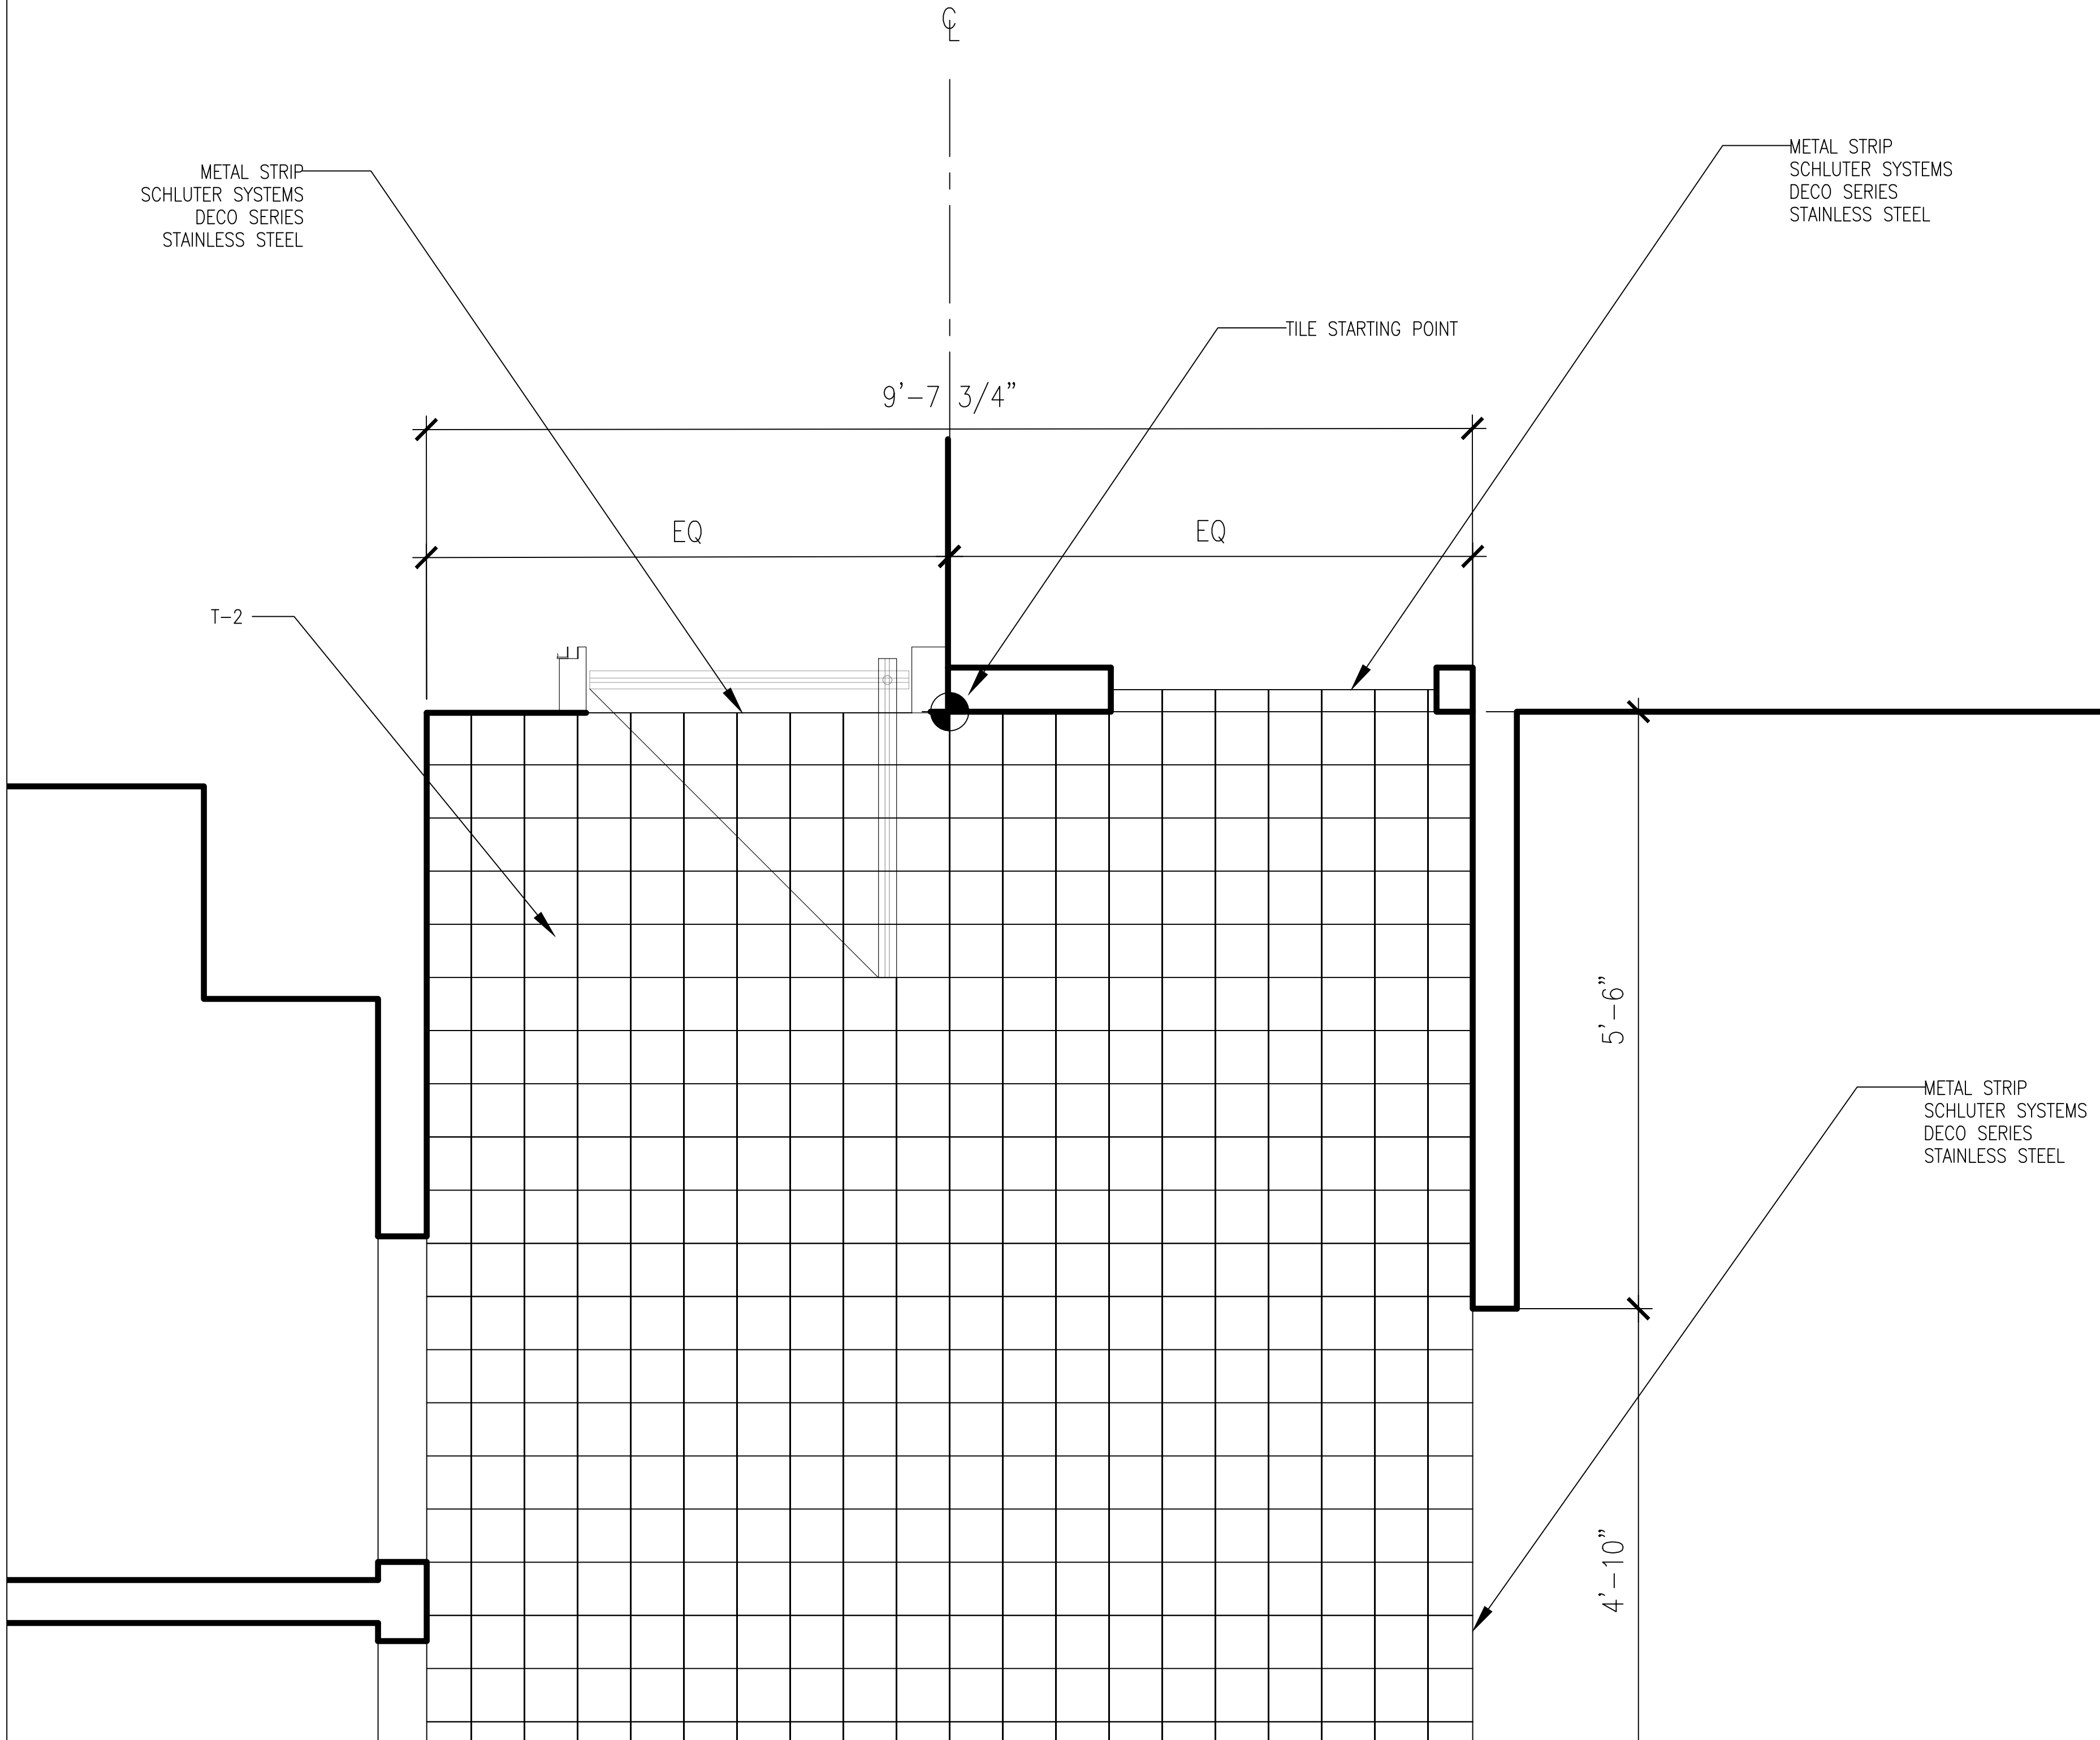

02 ENLARGED PLAN: SHOWROOM PANTRY 311
1/2"=1'-0"

AUSTRO TILE & STONE, LLC
30-25 93RD STREET
EAST ELMHURST, NY 11369

CONTRACTOR:
JRM CONSTRUCTION
MANAGEMENT, LLC
242 WEST 36TH STREET
11TH FLOOR
NEW YORK, NY 10018

INTERIOR DESIGNER:



ISSUE FOR APPROVAL 09/09/24
ISSUE NAME DATE

ARCHITECT:
KENNETH PARK ARCHITECTS
360 LEXINGTON AVENUE
NEW YORK, NY 10017PHONE:
212-599-0044

PROJECT NAME:
LACOSTE
575 5TH AVENUE
NEW YORK, NY 10017



SHEET NAME:
3RD FLOOR PANTRY
PLAN/ELEVATIONS

DATE:
PROJECT NO.:
PRINCIPAL:
DRAWING BY:
CHECKED BY:
SCALE:
DWG No.:
T-113
9 of 21

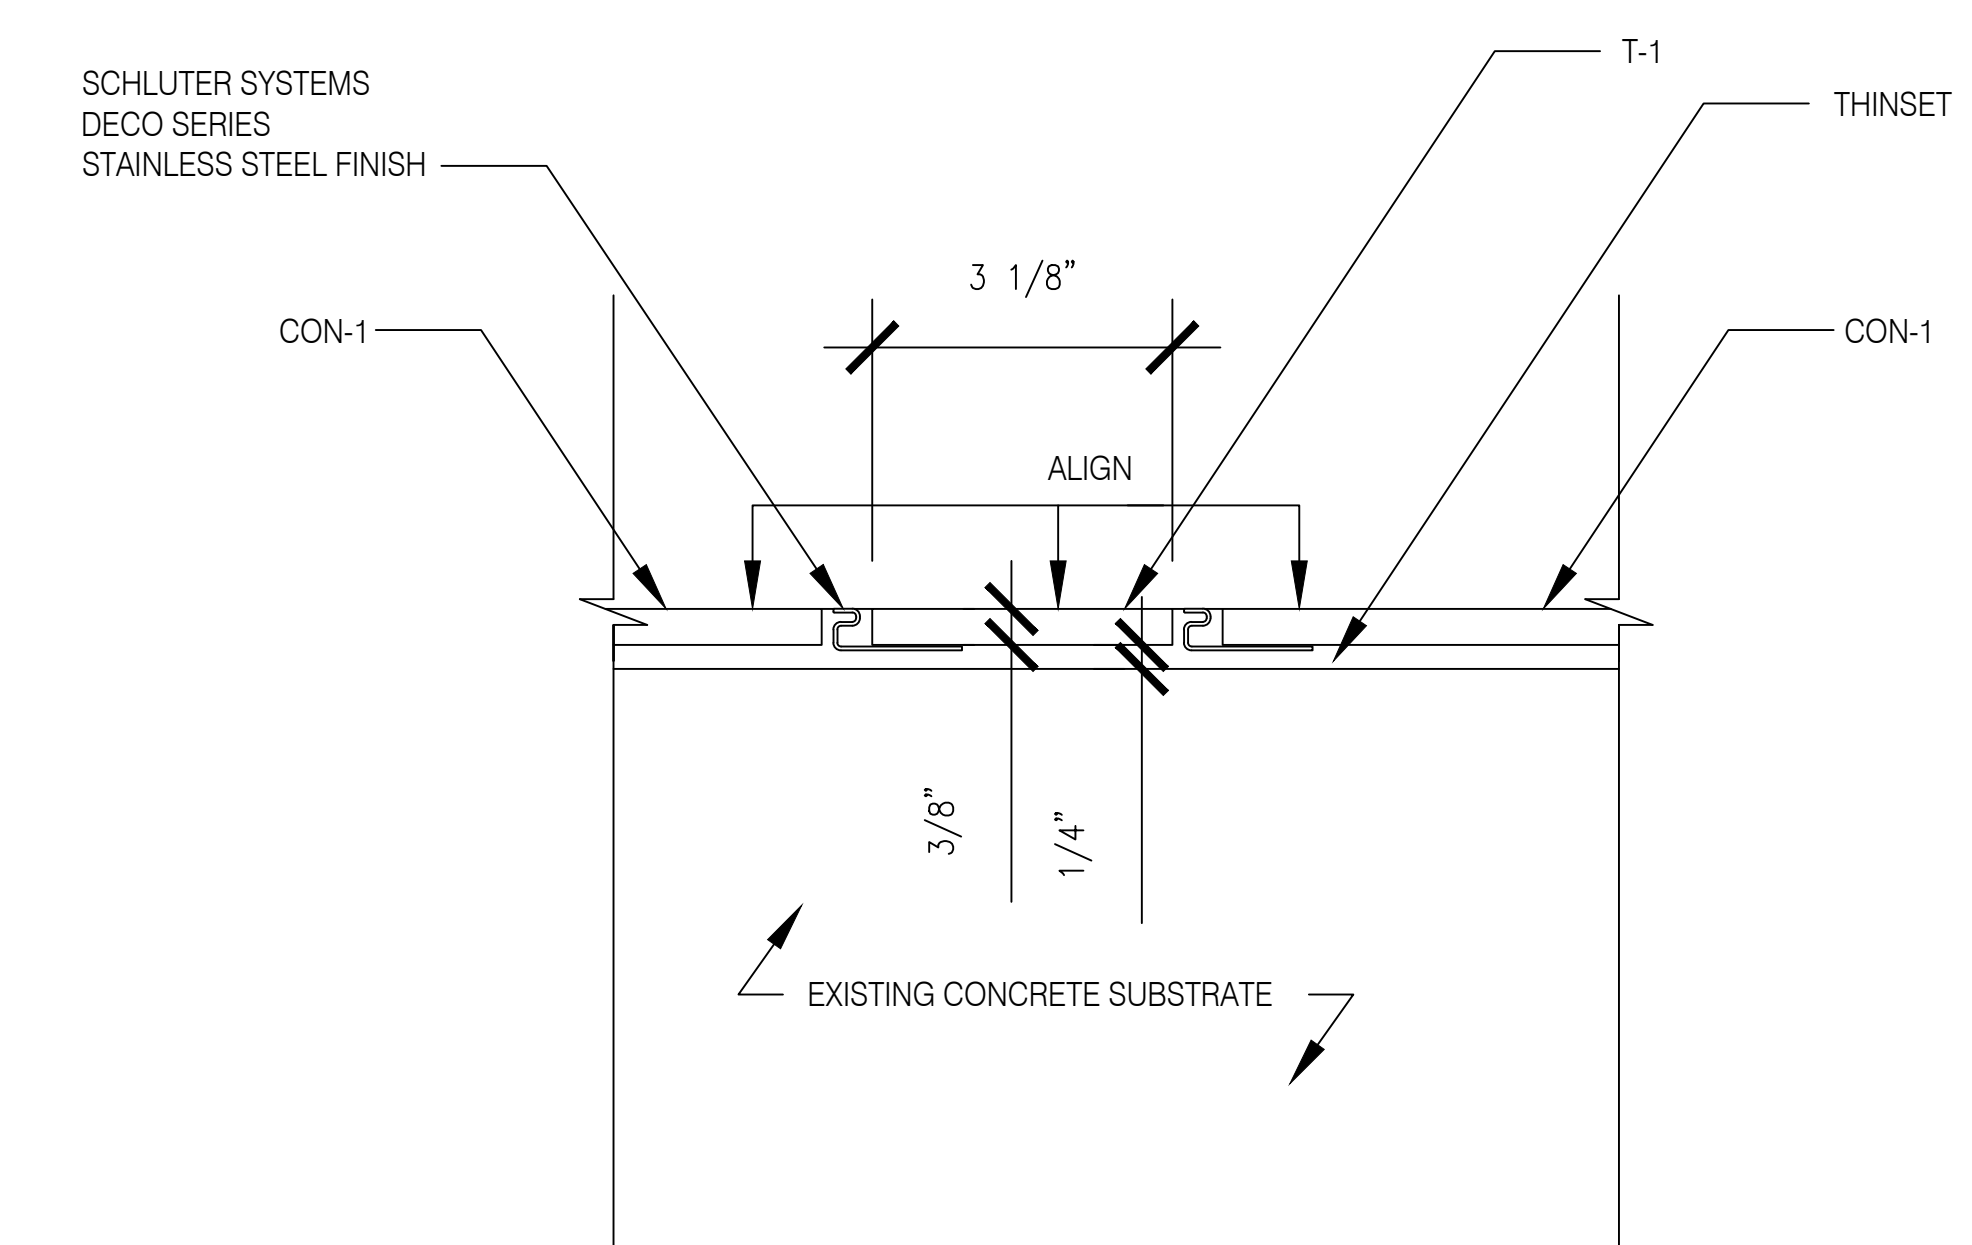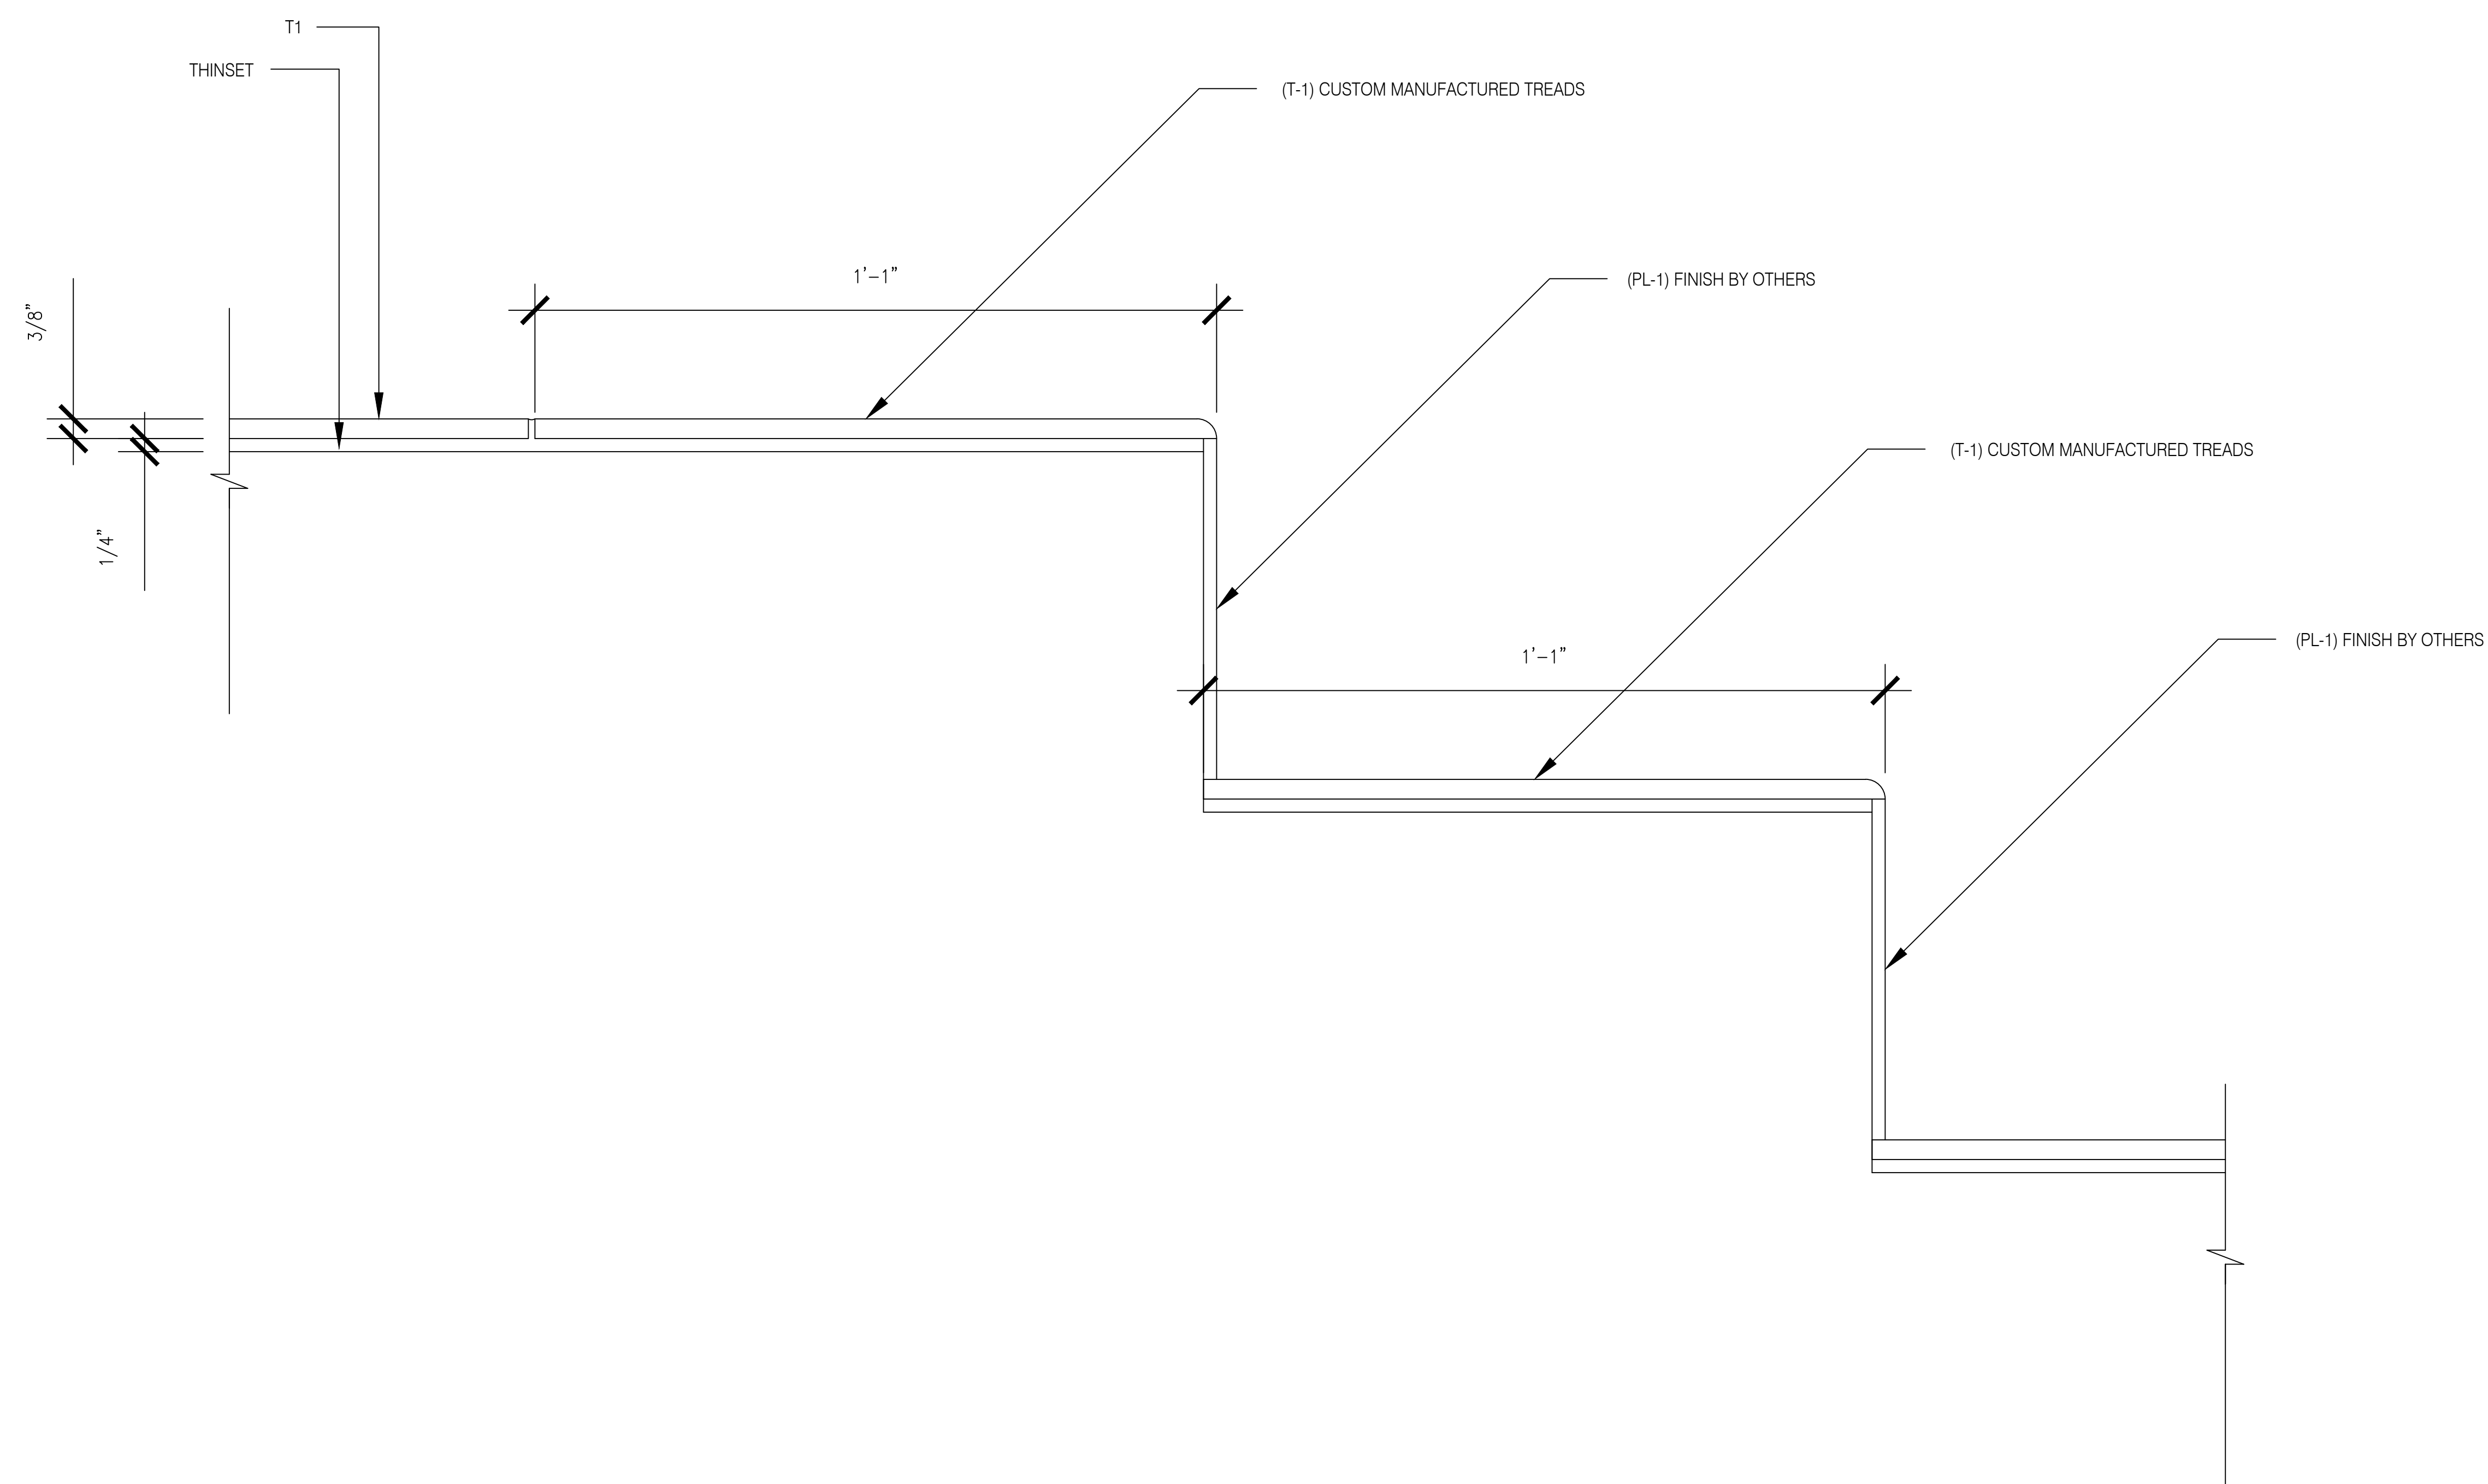

01
6"=1'-0"

DETAIL: ESCALATOR STAIR AT SALES AREA 102

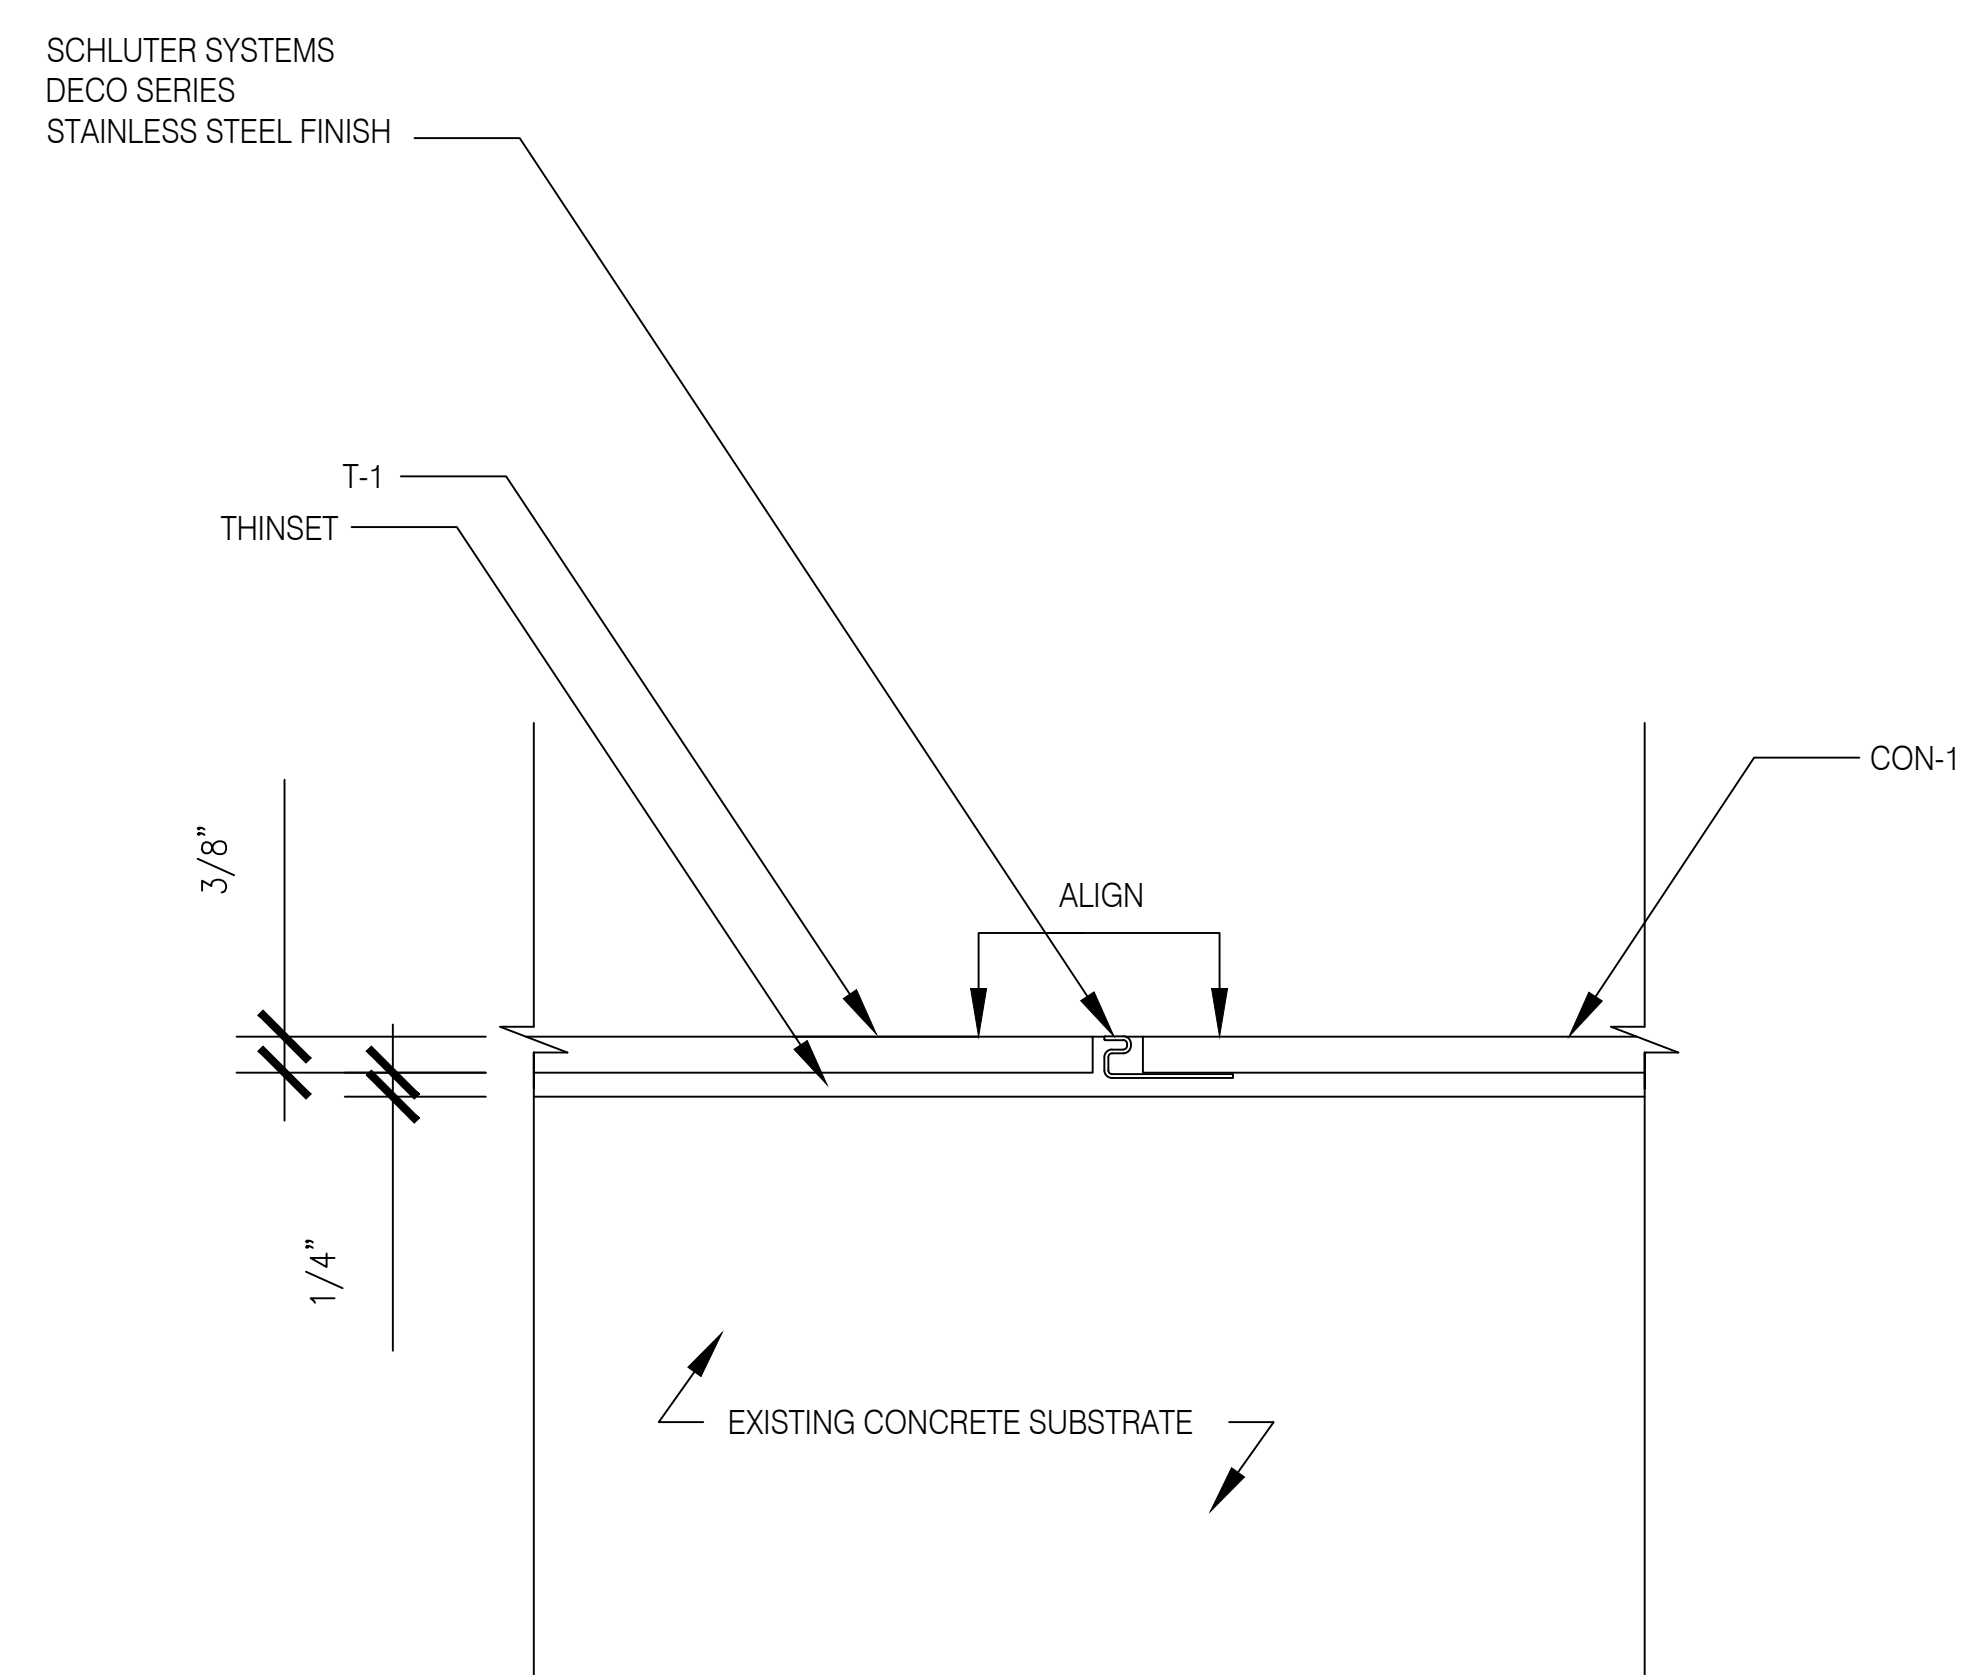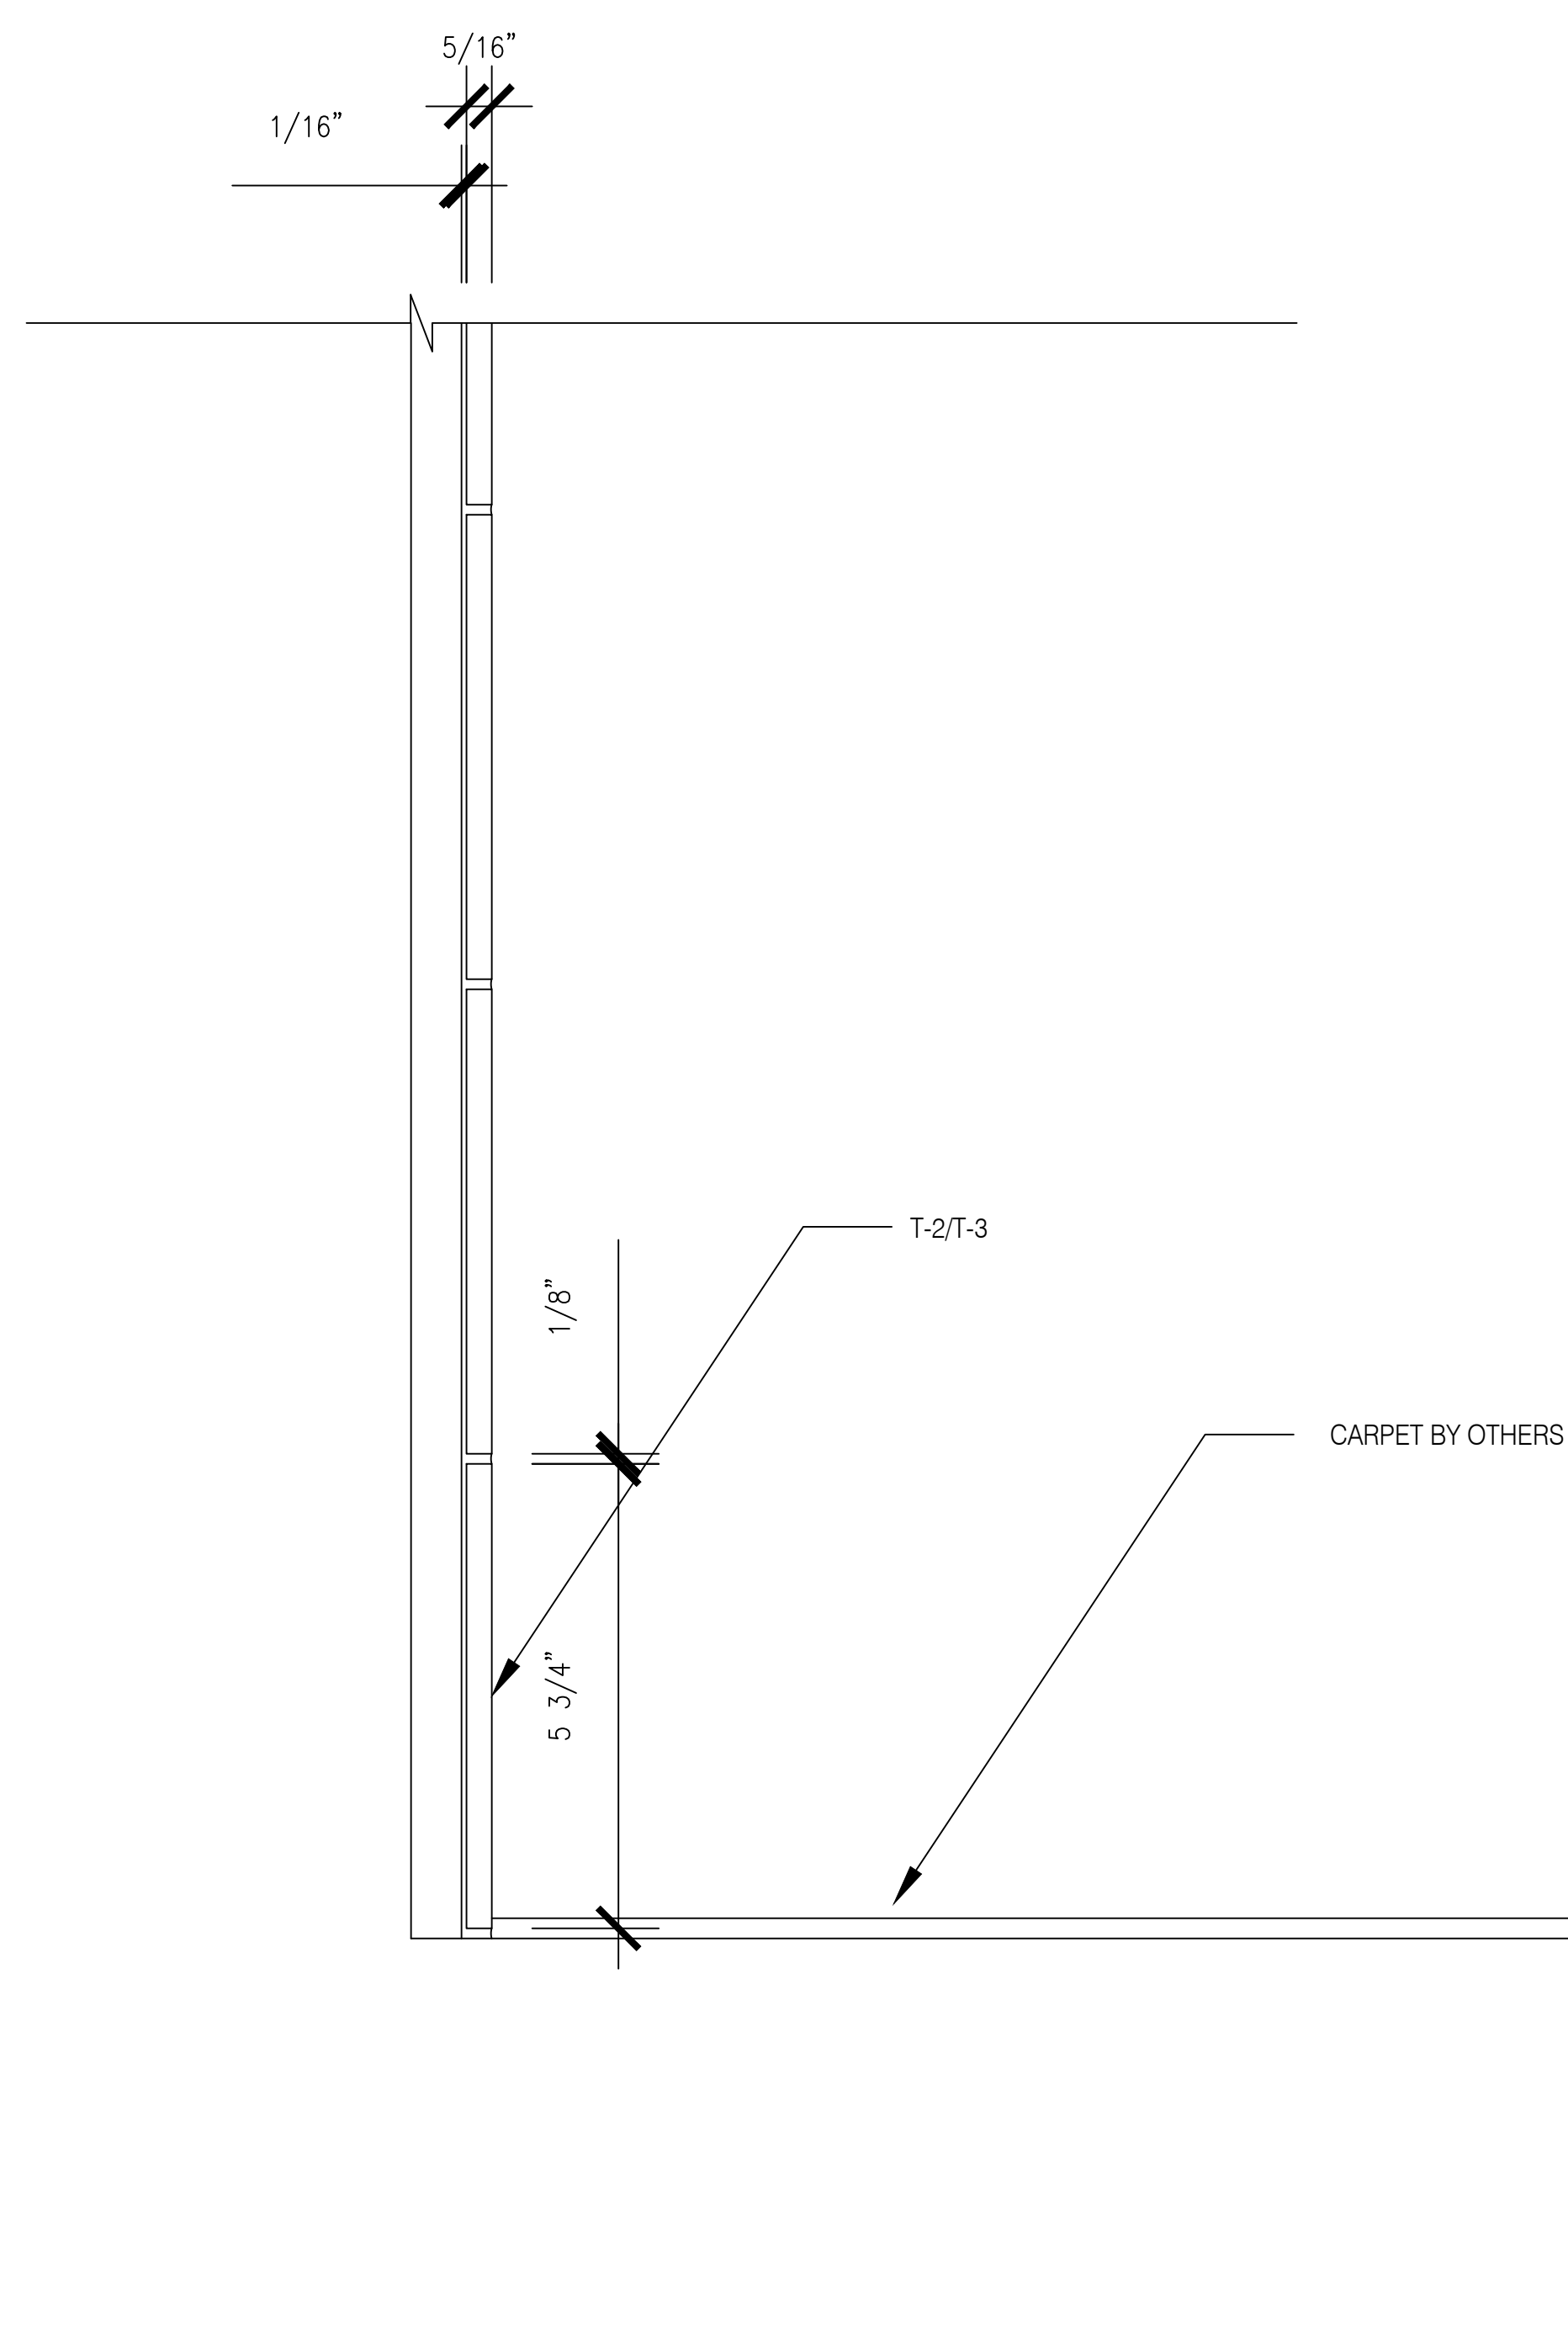


03
6"=1'-0"

04
6"=1'-0"

DETAIL: TILE/CONCRETE TRANSITION AT SALES AREA 201

02
6"=1'-0"

DETAIL: TILE/CONCRETE TRANSITION AT SALES AREA 102/201

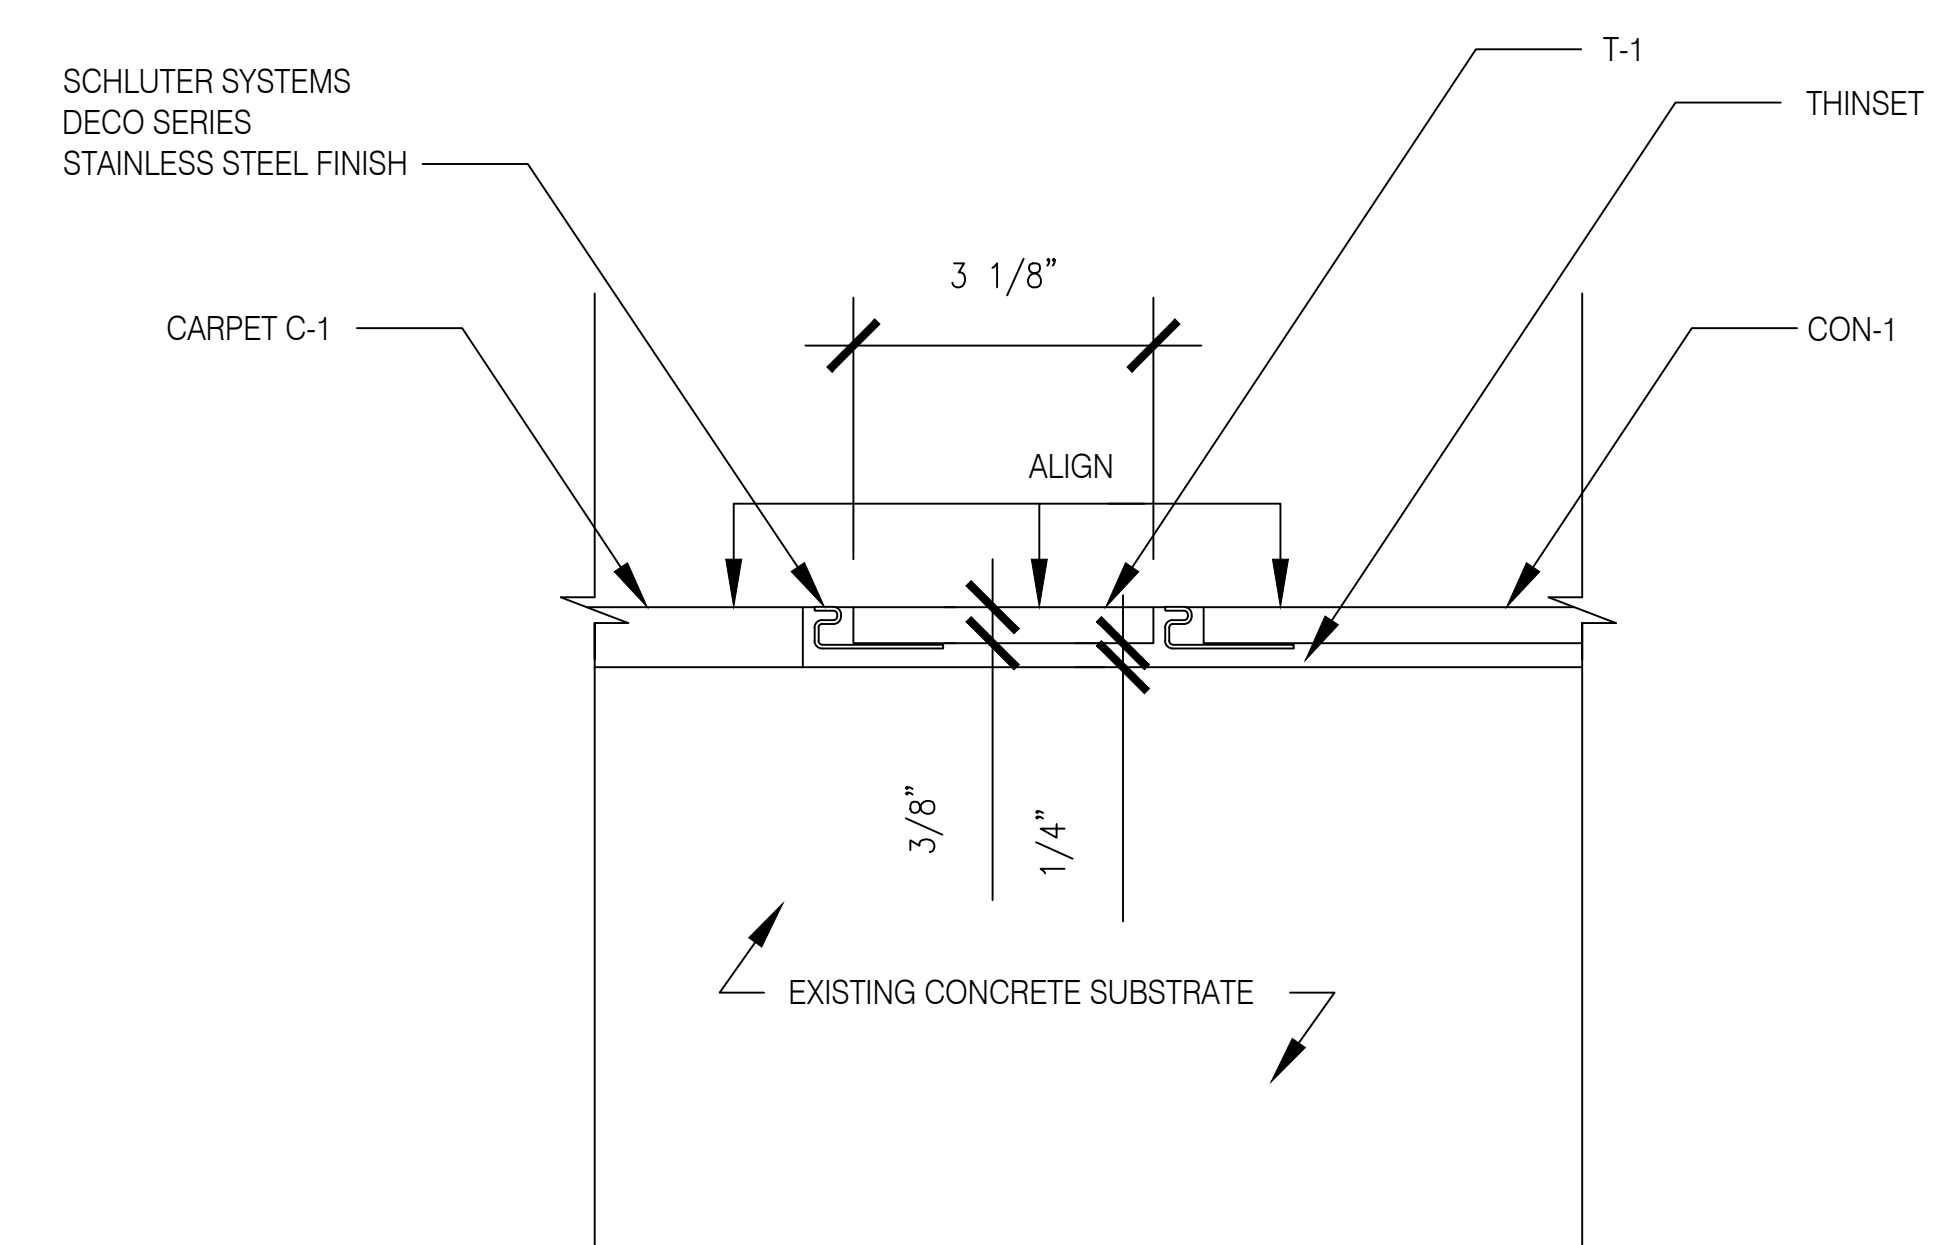

05
6'-1'-0"

DETAIL: TILE/CARPET/CONCRETE TRANSITION AT SALES AREA 201

AUSTRO TILE & STONE, LLC
30-25 93RD STREET
EAST ELMHURST, NY 11369

CONTRACTOR:
JRM CONSTRUCTION
MANAGEMENT, LLC
242 WEST 36TH STREET
11TH FLOOR
NEW YORK, NY 10018

INTERIOR DESIGNER:

[illegible]

ISSUE FOR APPROVAL	09/09/24
ISSUE NAME	DATE

KENNETH PARK ARCHITECTS
360 LEXINGTON AVENUE
NEW YORK, NY 10017PHONE:
212-599-0044

PROJECT NAME:
LACOSTE
575 5TH AVENUE
NEW YORK, NY 10017


SHEET NAME:

DETAILS
TILE


DATE: _____
PROJECT NO.: _____
PRINCIPAL: _____
DRAWING BY: _____
CHECKED BY: _____
SCALE: _____
DWG No.: **T-200**
10 of 21



DATE:
PROJECT NO.:
PRINCIPAL:
DRAWING BY:
CHECKED BY:
SCALE:
DWG No.:
T-201
11 of 21

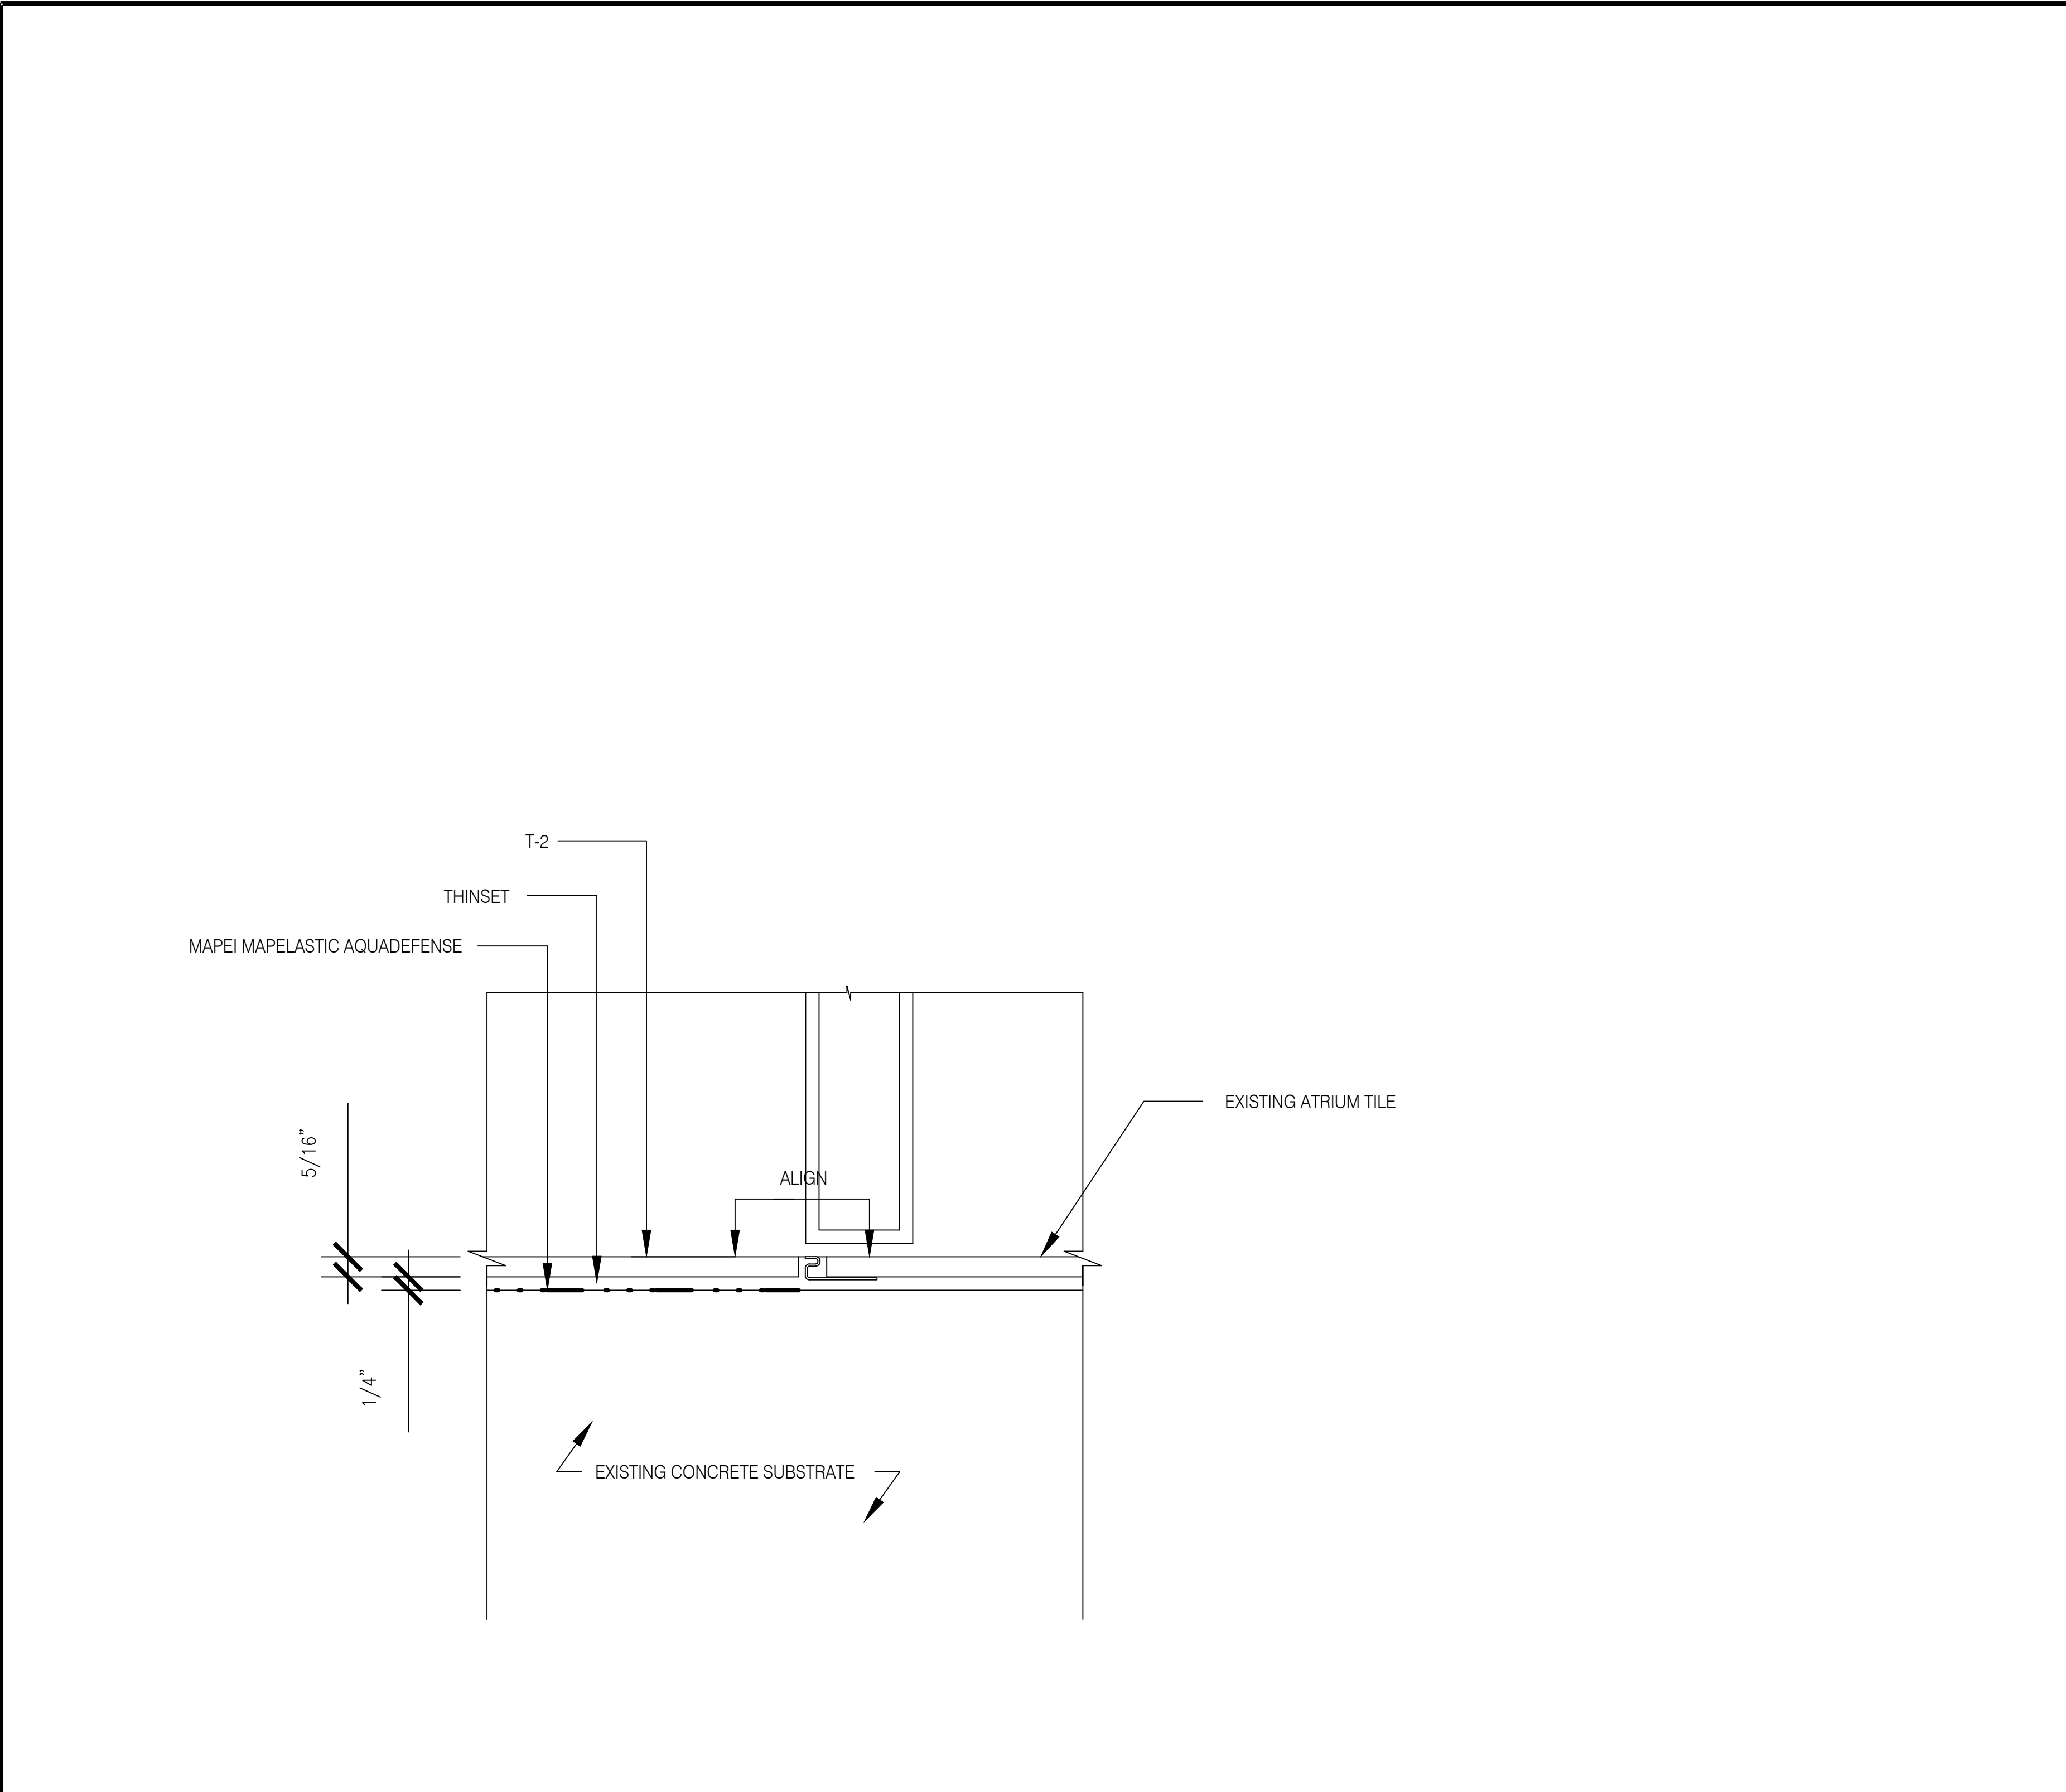


03
8" x 11" - 0" DETAIL: TILE/EXISTING FLOORING TRANSITION AT SHOWROOM PANTRY 311

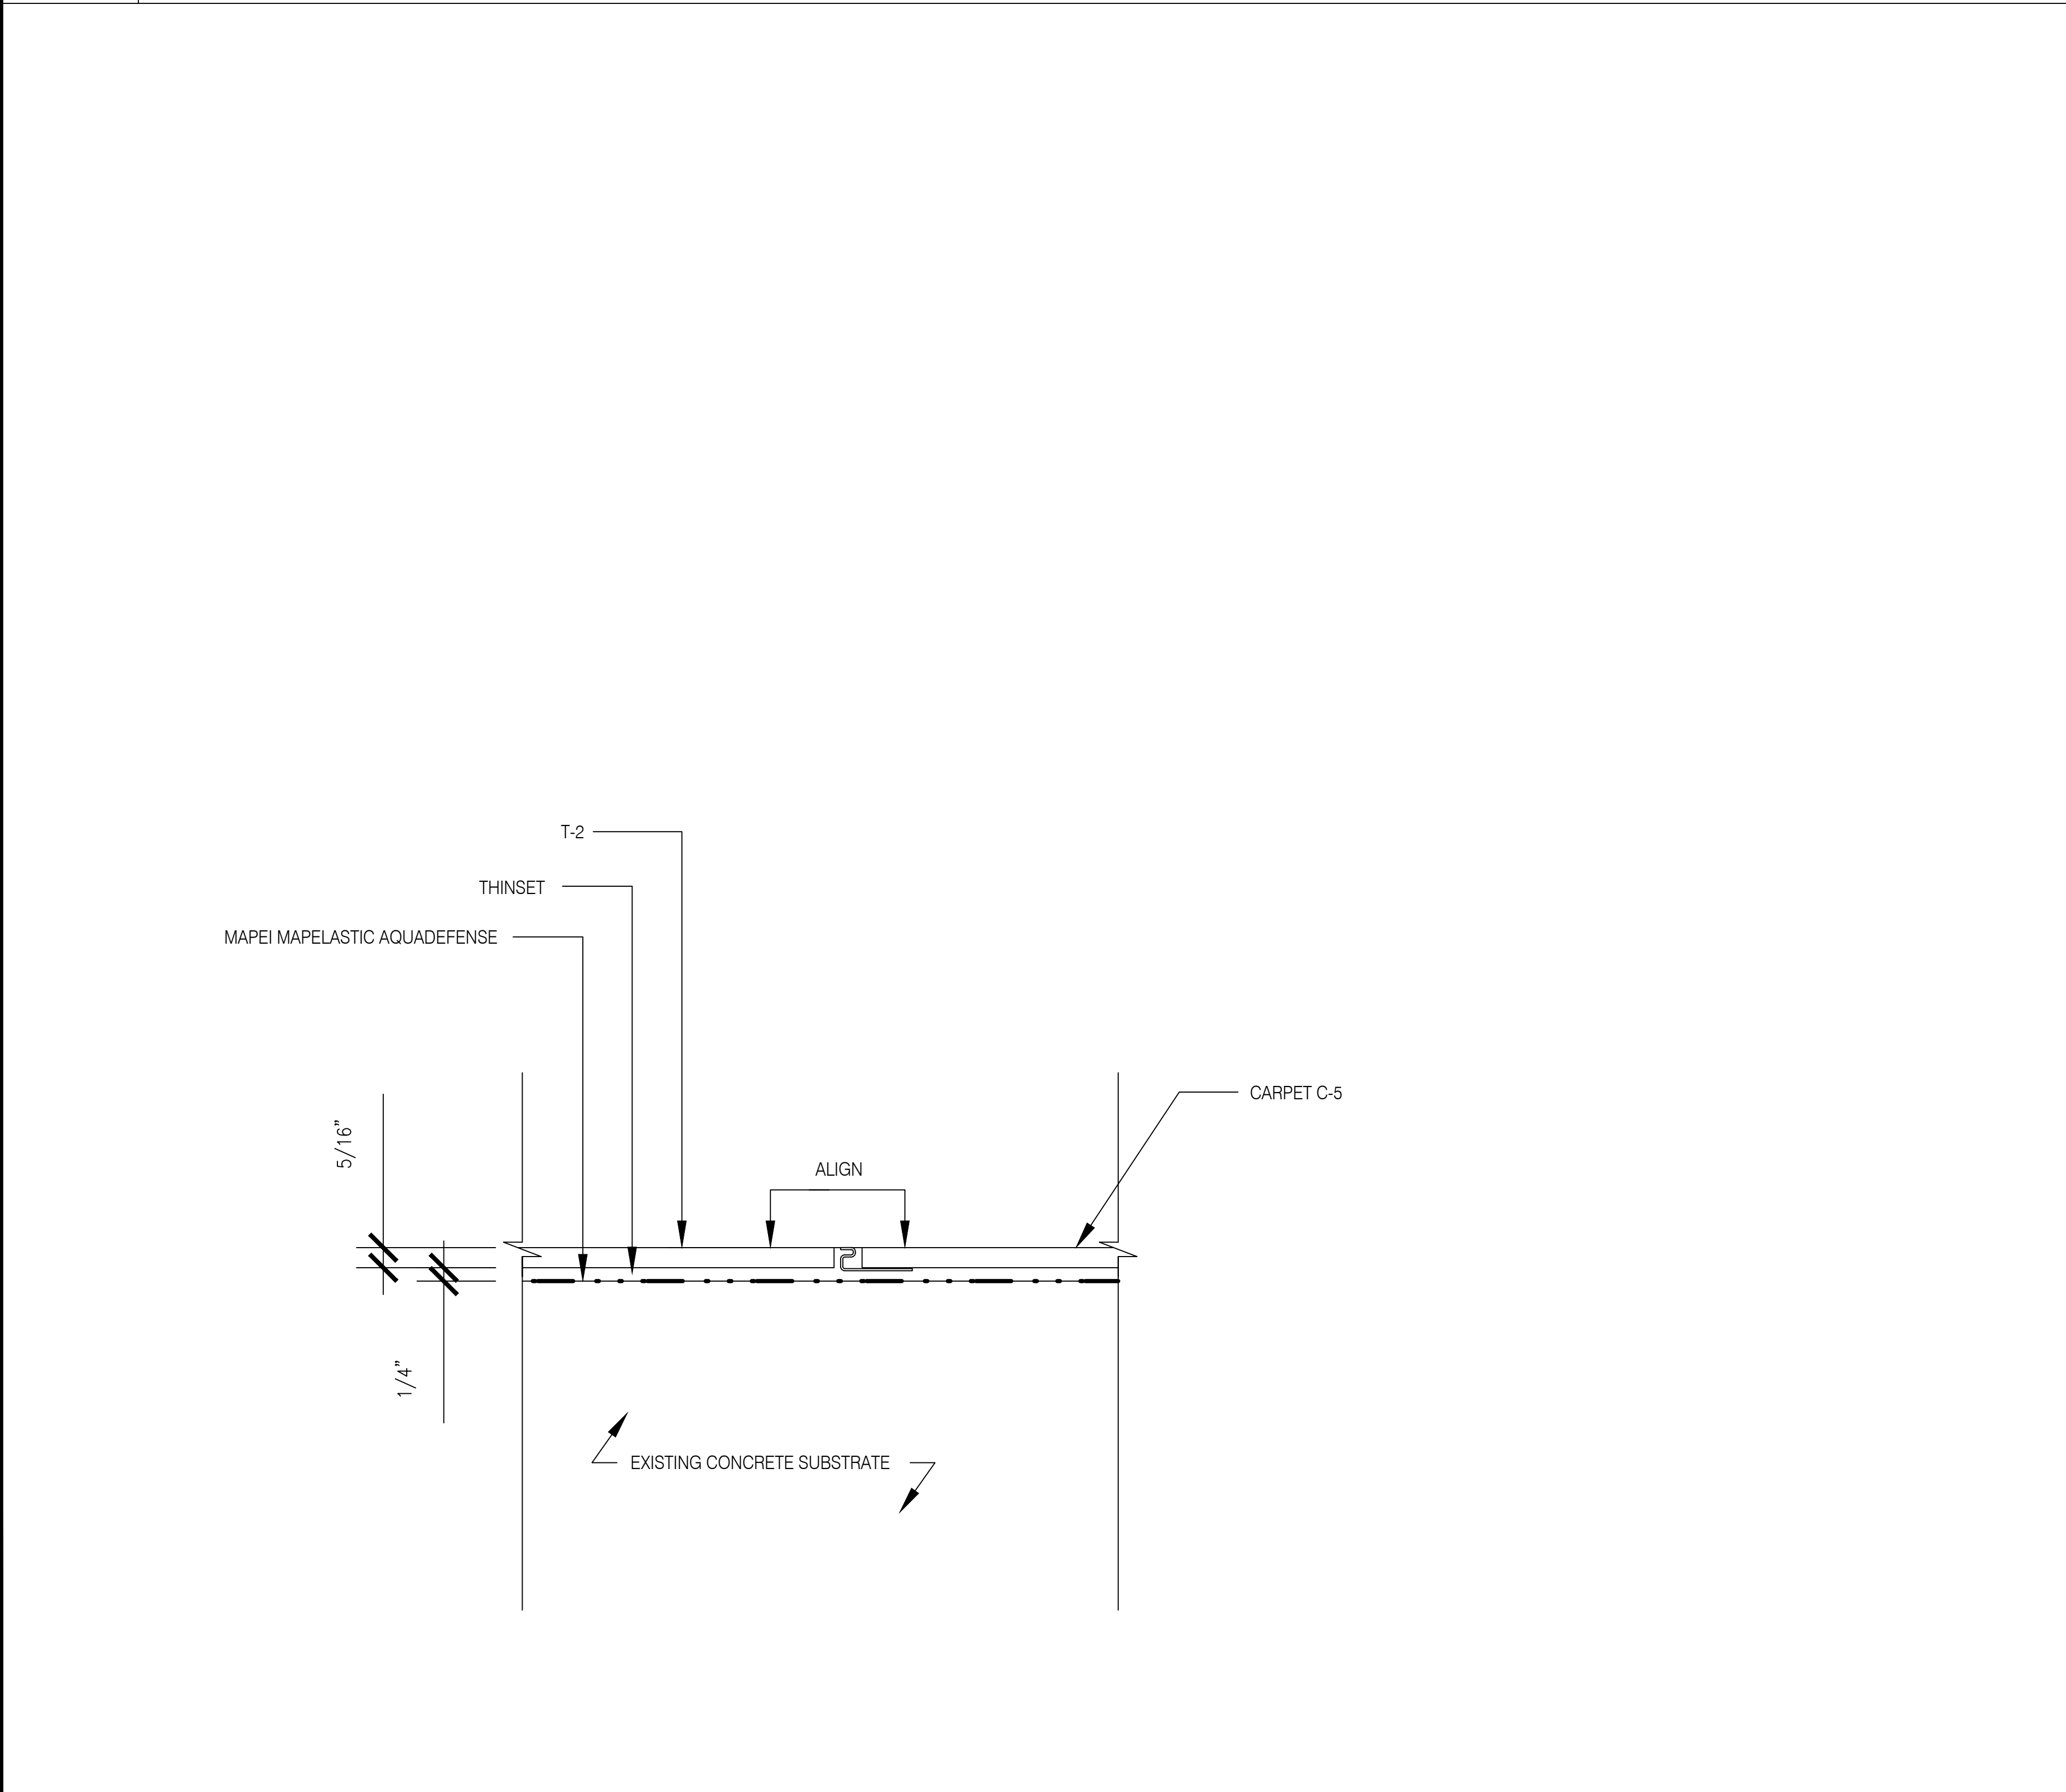

01
8" x 11" - 0" DETAIL: TILE/CARPET TRANSITION AT SHOWROOM PANTRY 311



02
8" x 11" - 0" DETAIL: TILE/WOOD TRANSITION AT SHOWROOM PANTRY 311

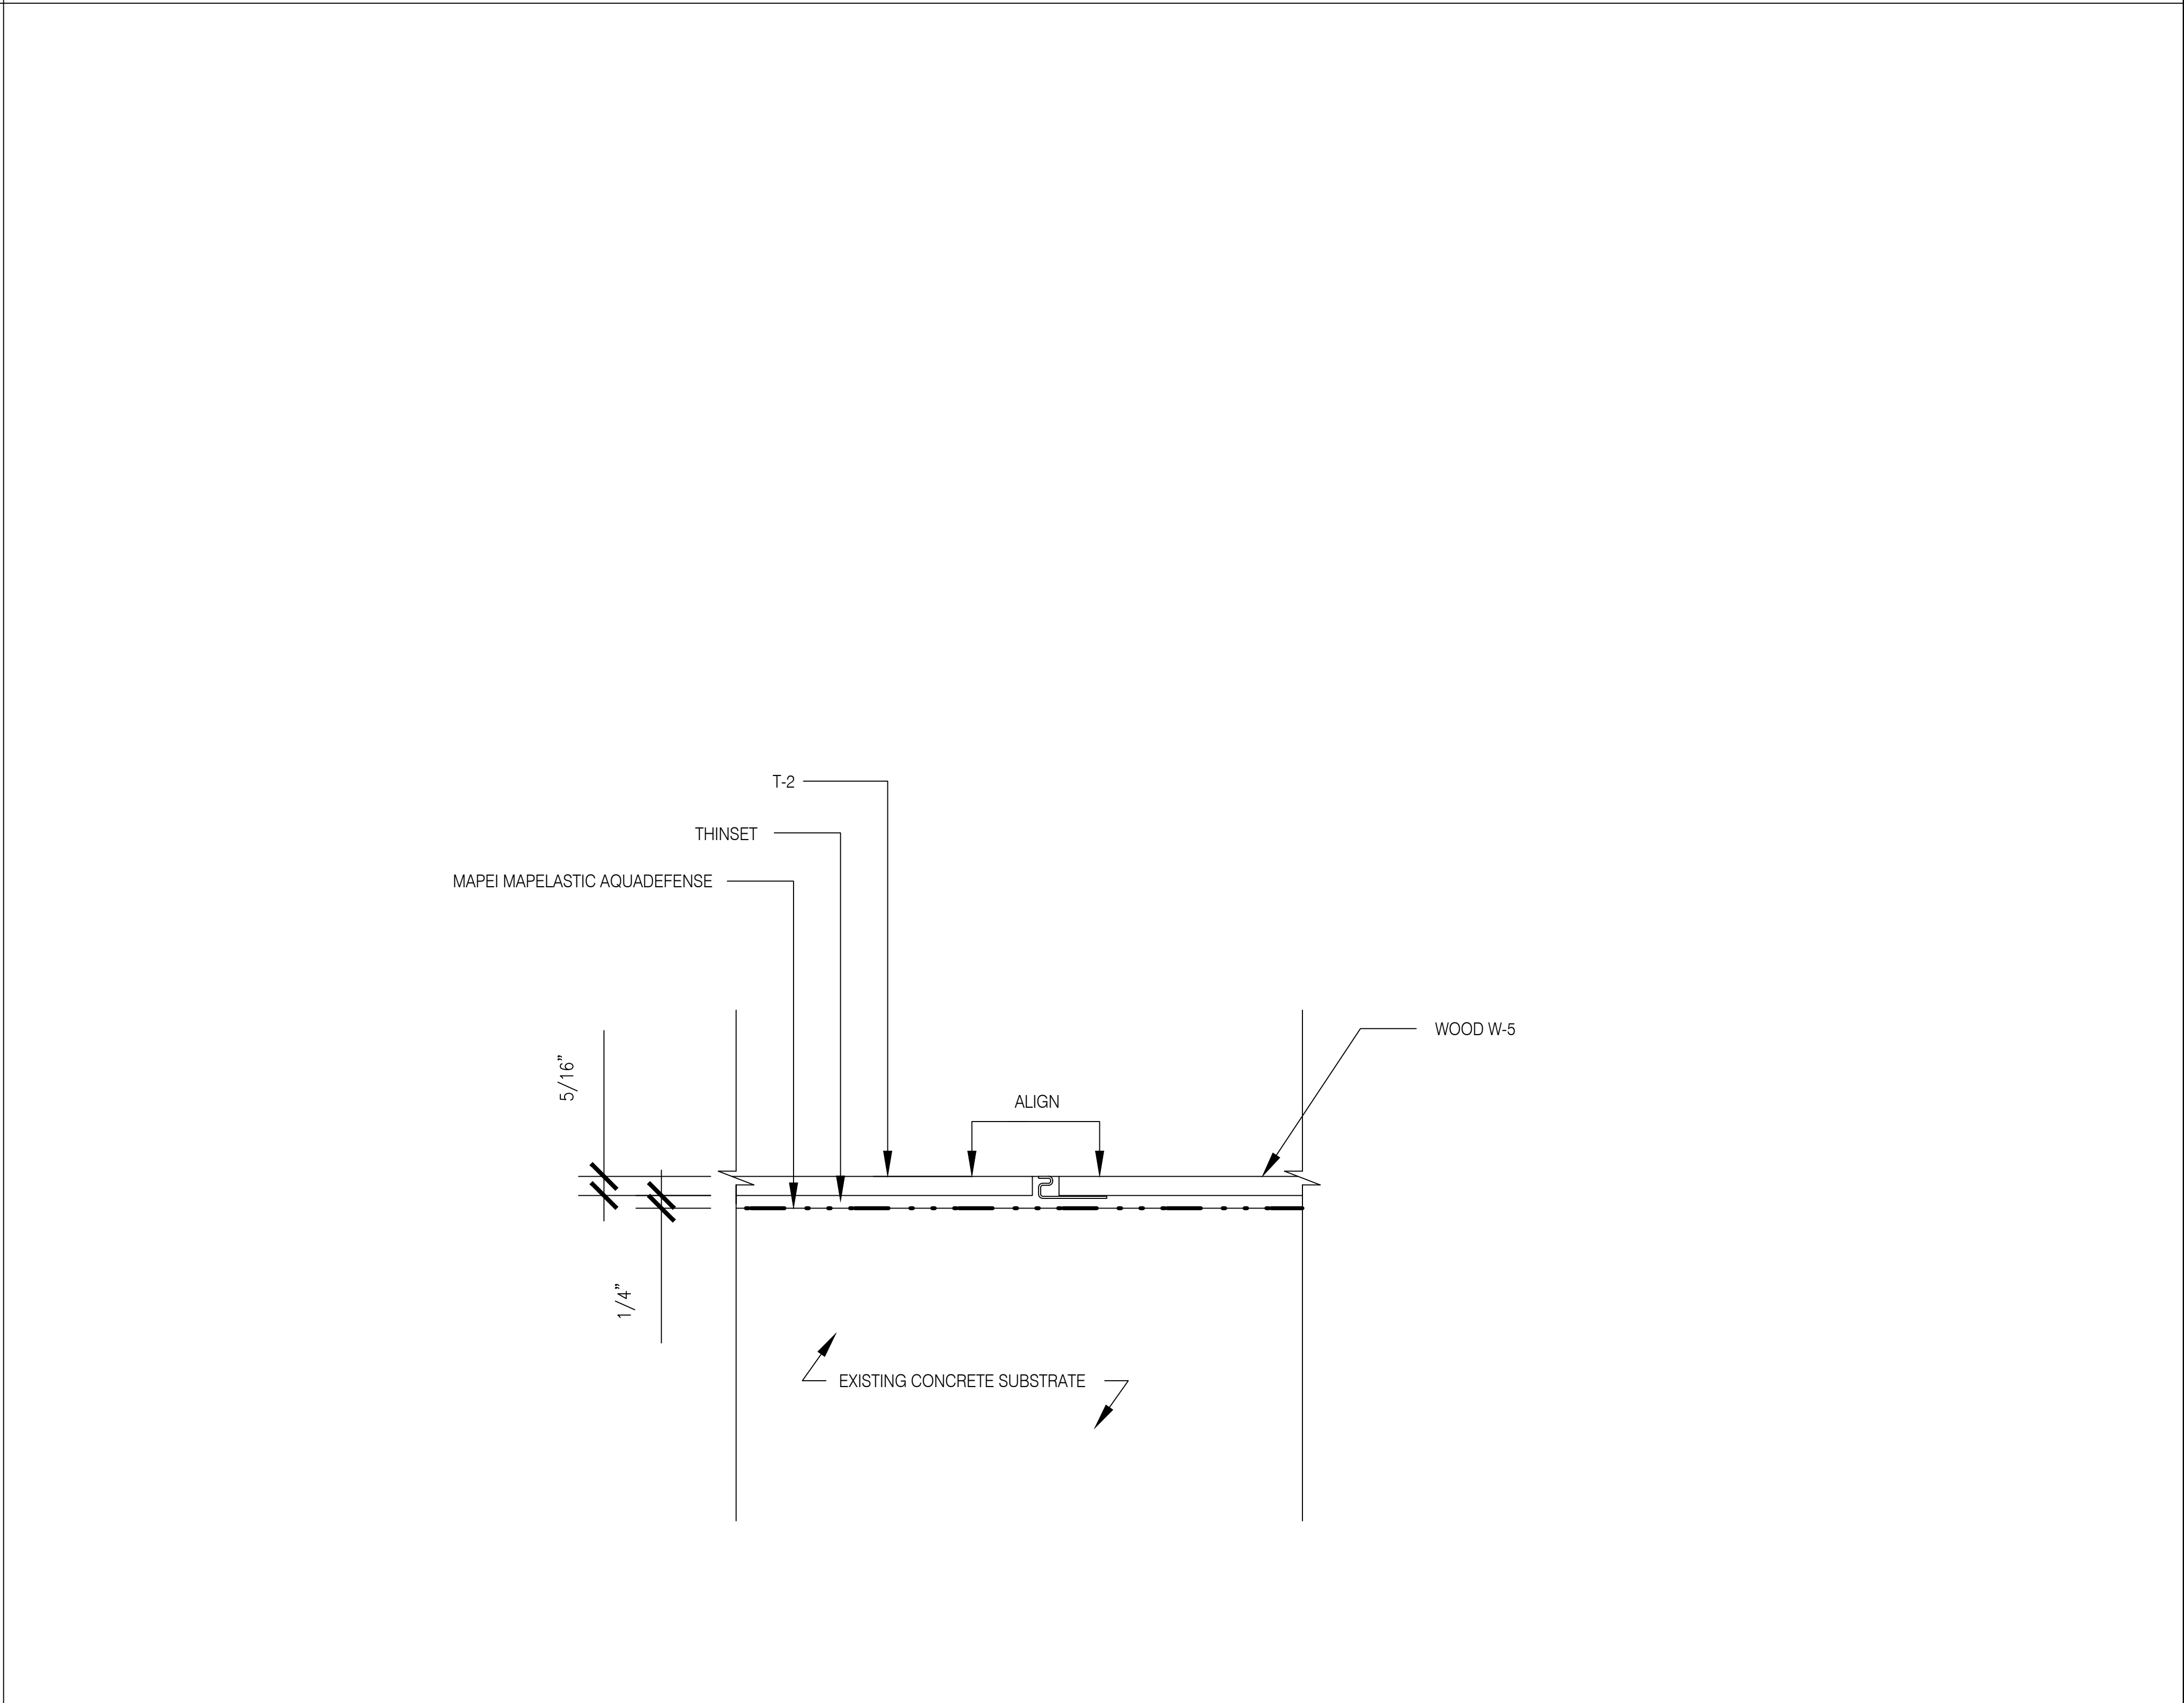

02
8" x 11" - 0" DETAIL: TILE/WOOD TRANSITION AT SHOWROOM PANTRY 311

AUSTRO TILE & STONE, LLC
30-25 93RD STREET
EAST ELMHURST, NY 11369

CONTRACTOR:
JRM CONSTRUCTION
MANAGEMENT, LLC
242 WEST 36TH STREET
11TH FLOOR
NEW YORK, NY 10018

INTERIOR DESIGNER:

ISSUE FOR APPROVAL 09/09/24
ISSUE NAME DATE

WORKSHEET

KENNETH PARK ARCHITECTS
360 LEXINGTON AVENUE
NEW YORK, NY 10017PHONE:
212-599-0044

PROJECT NAME:
LACOSTE
575 5TH AVENUE
NEW YORK, NY 10017

SHEET NAME:
DETAILS
TILE

DATE:
PROJECT NO.:
PRINCIPAL:
DRAWING BY:
CHECKED BY:
SCALE:
DWG No.:
T-202