

JACK RESICK & SONS

RESTROOM RENOVATION

255 GREENWICH STREET

NEW YORK, NY 10007

FLOOR 6-9

DRAWING LEGEND:

CS-001	COVER SHEET, DRAWING LEGEND & MATERIAL LEGEND
T-100	PLAN - 6TH FLOOR BATHROOMS
T-101	ELEVATIONS-6TH FLOOR BATHROOMS
T-102	ELEVATIONS-6TH FLOOR BATHROOMS
T-103	ELEVATIONS-6TH FLOOR BATHROOMS
T-104	ELEVATIONS-6TH FLOOR BATHROOMS
T-105	ELEVATIONS-6TH FLOOR BATHROOMS
T-200	PLAN - 7TH FLOOR BATHROOMS
T-201	ELEVATIONS-7TH FLOOR BATHROOMS
T-202	ELEVATIONS-7TH FLOOR BATHROOMS
T-203	ELEVATIONS-7TH FLOOR BATHROOMS
T-204	ELEVATIONS-7TH FLOOR BATHROOMS
T-300	PLAN - 8TH FLOOR BATHROOMS
T-301	ELEVATIONS-8TH FLOOR BATHROOMS
T-302	ELEVATIONS-8TH FLOOR BATHROOMS
T-303	ELEVATIONS-8TH FLOOR BATHROOMS
T-304	ELEVATIONS-8TH FLOOR BATHROOMS
T-400	PLAN - 9THH FLOOR BATHROOMS
T-401	ELEVATIONS-9TH FLOOR BATHROOMS
T-402	ELEVATIONS-9TH FLOOR BATHROOMS
T-403	ELEVATIONS-9TH FLOOR BATHROOMS
T-404	ELEVATIONS-9TH FLOOR BATHROOMS
T-500	STONE COUNTERTOPS-6TH FLOOR
T-501	STONE COUNTERTOPS-7TH FLOOR
T-502	STONE COUNTERTOPS-8TH FLOOR
T-503	STONE COUNTERTOPS-9TH FLOOR
T-600	DETAILS-TILE
T-601	DETAILS-TILE
T-602	DETAILS-COUNTERTOPS

MATERIAL LEGEND

BASE TILE (BT-1) MANF: CROSSVILLE STYLE: MAIN STREET COLOR: AV214 GALLERY GREY,UNPOLISHED SIZE: 5-7/8" x 11-13/16" CONTACT: INSTALLATION: STACKED GROUT COLOR APPROVAL: MAPEI,KERAPROXY CQ #5101 RAIN	FLOOR TILE (FT-1) MANF: CROSSVILLE STYLE: MAIN STREET COLOR: AV214 GALLERY GREY,UNPOLISHED SIZE: 11-13/16"" x 11-13/16" CONTACT: INSTALLATION: STACKED GROUT COLOR APPROVAL: MAPEI,KERAPROXY CQ, #5101 RAIN	WALL TILE (WT-1) MANF: CROSSVILLE STYLE: READY TO WEAR COLOR: AV313 OFF THE CUFF UNPOLISHED SIZE: 11-13/16" x 23-13/16" CONTACT: INSTALLATION: STACKED GROUT COLOR APPROVAL: MAPEI,KERAPROXY CQ, #5049 LIGHT ALMOND	ACCENT TILE (AT-1) MANF: NEMO STYLE: METRO COLOR: STEEL GLOSS SIZE: 2" x 8" CONTACT: INSTALLATION: STACKED GROUT COLOR APPROVAL: MAPEI, KERAPROXY CQ, #5049 LIGHT ALMOND	QUARTZ COUNTER TOP QT-1 MANF: QUARTZ MASTER STYLE: SILESTONE COLOR: BLANCO MAPLE 14, POLISHED SIZE: 128" X 63"X 3/4" CONTACT:	STONE SADDLE SS MANF: STYLE: COLOR: TBD SIZE: 3/4" THICK CONTACT:
---	---	---	--	---	---

ARCHITECT TO CONFIRM:

GROUT JOINT AT FT-1 TO BE 1/8"
GROUT JOINT AT BT-1 TO BE 1/8"
GROUT JOINT AT WT-1 TO BE 1/8"
GROUT JOINT AT AT-1 TO BE 1/16"

PLEASE NOTE:

NO EXPANSION JOINTS ARE SHOWN IN THE TILE FLOORING AS THERE ARE NO EXPANSION JOINTS SHOWN IN THE ARCHITECTURAL DRAWINGS. IF EXPANSION OR MOVEMENT JOINTS ARE REQUIRED, ARCHITECT TO PROVIDE LOCATION AND DETAILS ACCORDINGLY

PER THE TCNA, "USE OF WALL-WASHER AND COVE-TYPE LIGHTING, WHERE THE LIGHTS ARE LOCATED EITHER AT THE WALL/CEILING INTERFACE OR MOUNTED DIRECTLY ON THE WALL, ARE POPULAR TECHNIQUES FOR PRODUCING DRAMATIC ROOM LIGHTING EFFECTS. WHEN PROPER BACKING SURFACES, INSTALLATION MATERIALS AND METHODS, AND LOCATION OF LIGHT FIXTURES ARE NOT CAREFULLY COORDINATED, THESE LIGHTING TECHNIQUES MAY PRODUCE SHADOWS AND UNDESIRABLE EFFECTS WITH CERAMIC TILES; SIMILAR SHADOWS ARE CREATED FROM SIDE LIGHTING INTERIOR WALLS AND FLOORS WHEN LIGHT SHINES AT THAT ANGLE THROUGH WINDOWS AND DOORS."

PLEASE TAKE NOTE OF THIS AS IT RELATES TO THE TILE IN THIS PROJECT.

AUSTRO TILE & STONE, LLC
30-25 93RD STREET
EAST ELMHURST, NY 11369

CONTRACTOR:
JRM CONSTRUCTION
MANAGEMENT, LLC
242 WEST 36TH STREET
11TH FLOOR
NEW YORK, NY 10018

INTERIOR DESIGNER:

ISSUE FOR APPROVAL 10/09/23

ISSUE NAME DATE

PROJECT:

SPACESMITH
ONE NEW YORK PLAZA SUITE 4200
NEW YORK, NY 10004
PH: 212 260 5583

PROJECT NAME:

JACK RESNICK & SONS
255 GREENWICH STREET
NEW YORK, NY 10007

SHEET NAME:

COVER SHEET

DATE:
PROJECT NO.:
PRINCIPAL:
DRAWING BY:
CHECKED BY:
SCALE: AS NOTED
DWG No.:
CS-001
1 of 29



WOMEN'S
POWDER ROOM

601

WOMEN'S
RESTROOM

602

MEN'S
RESTROOM

603

SINGLE
RESTROOM

TILE STARTING POINT

PREFABRICATED
SHOWER BY OTHERS

STARTING POINT

EQ

EQ

EQ

- TILE STARTING POINT

03 ENLARGED PLAN: 6TH FLOOR BATHROOMS
1/2"=1'-0"

04 ENLARGED PLAN: 6TH FLOOR BATHROOMS

05 ENLARGED PLAN: 6TH FLOOR SINGLE BATHROOM

01	PLAN: 6TH FLOOR BATHROOMS
----	---------------------------

02	PLAN: 6TH FLOOR SINGLE BATHROOM
----	---------------------------------

AUSTRO TILE & STONE, LLC
30-25 93RD STREET
EAST ELMHURST, NY 11369

CONTRACTOR:
JRM CONSTRUCTION
MANAGEMENT, LLC
242 WEST 36TH STREET
11TH FLOOR
NEW YORK, NY 10018

ISSUE FOR APPROVAL	10/09/23
ISSUE NAME	DATE

SPACSMITH
ONE NEW YORK PLAZA
NEW YORK, NY 10004
PH:212 260 5583

JACK RESNICK & SONS
255 GREENWICH STREET
NEW YORK, NY 10007




PLAN
6TH FLOOR BATHROOMS

DATE:
PROJECT NO.:
PRINCIPAL:
DRAWING BY:
CHECKED BY:
SCALE:
DWG No.:
T-100



(BT-1) TILE BASE GROUT JOINTS WILL NOT ALIGN WITH (WT-1) WALL TILE GROUT JOINTS


(AT-1) ACCENT WALL TILE GROUT JOINTS WILL NOT ALIGN WITH (WT-1) WALL TILE GROUT JOINTS

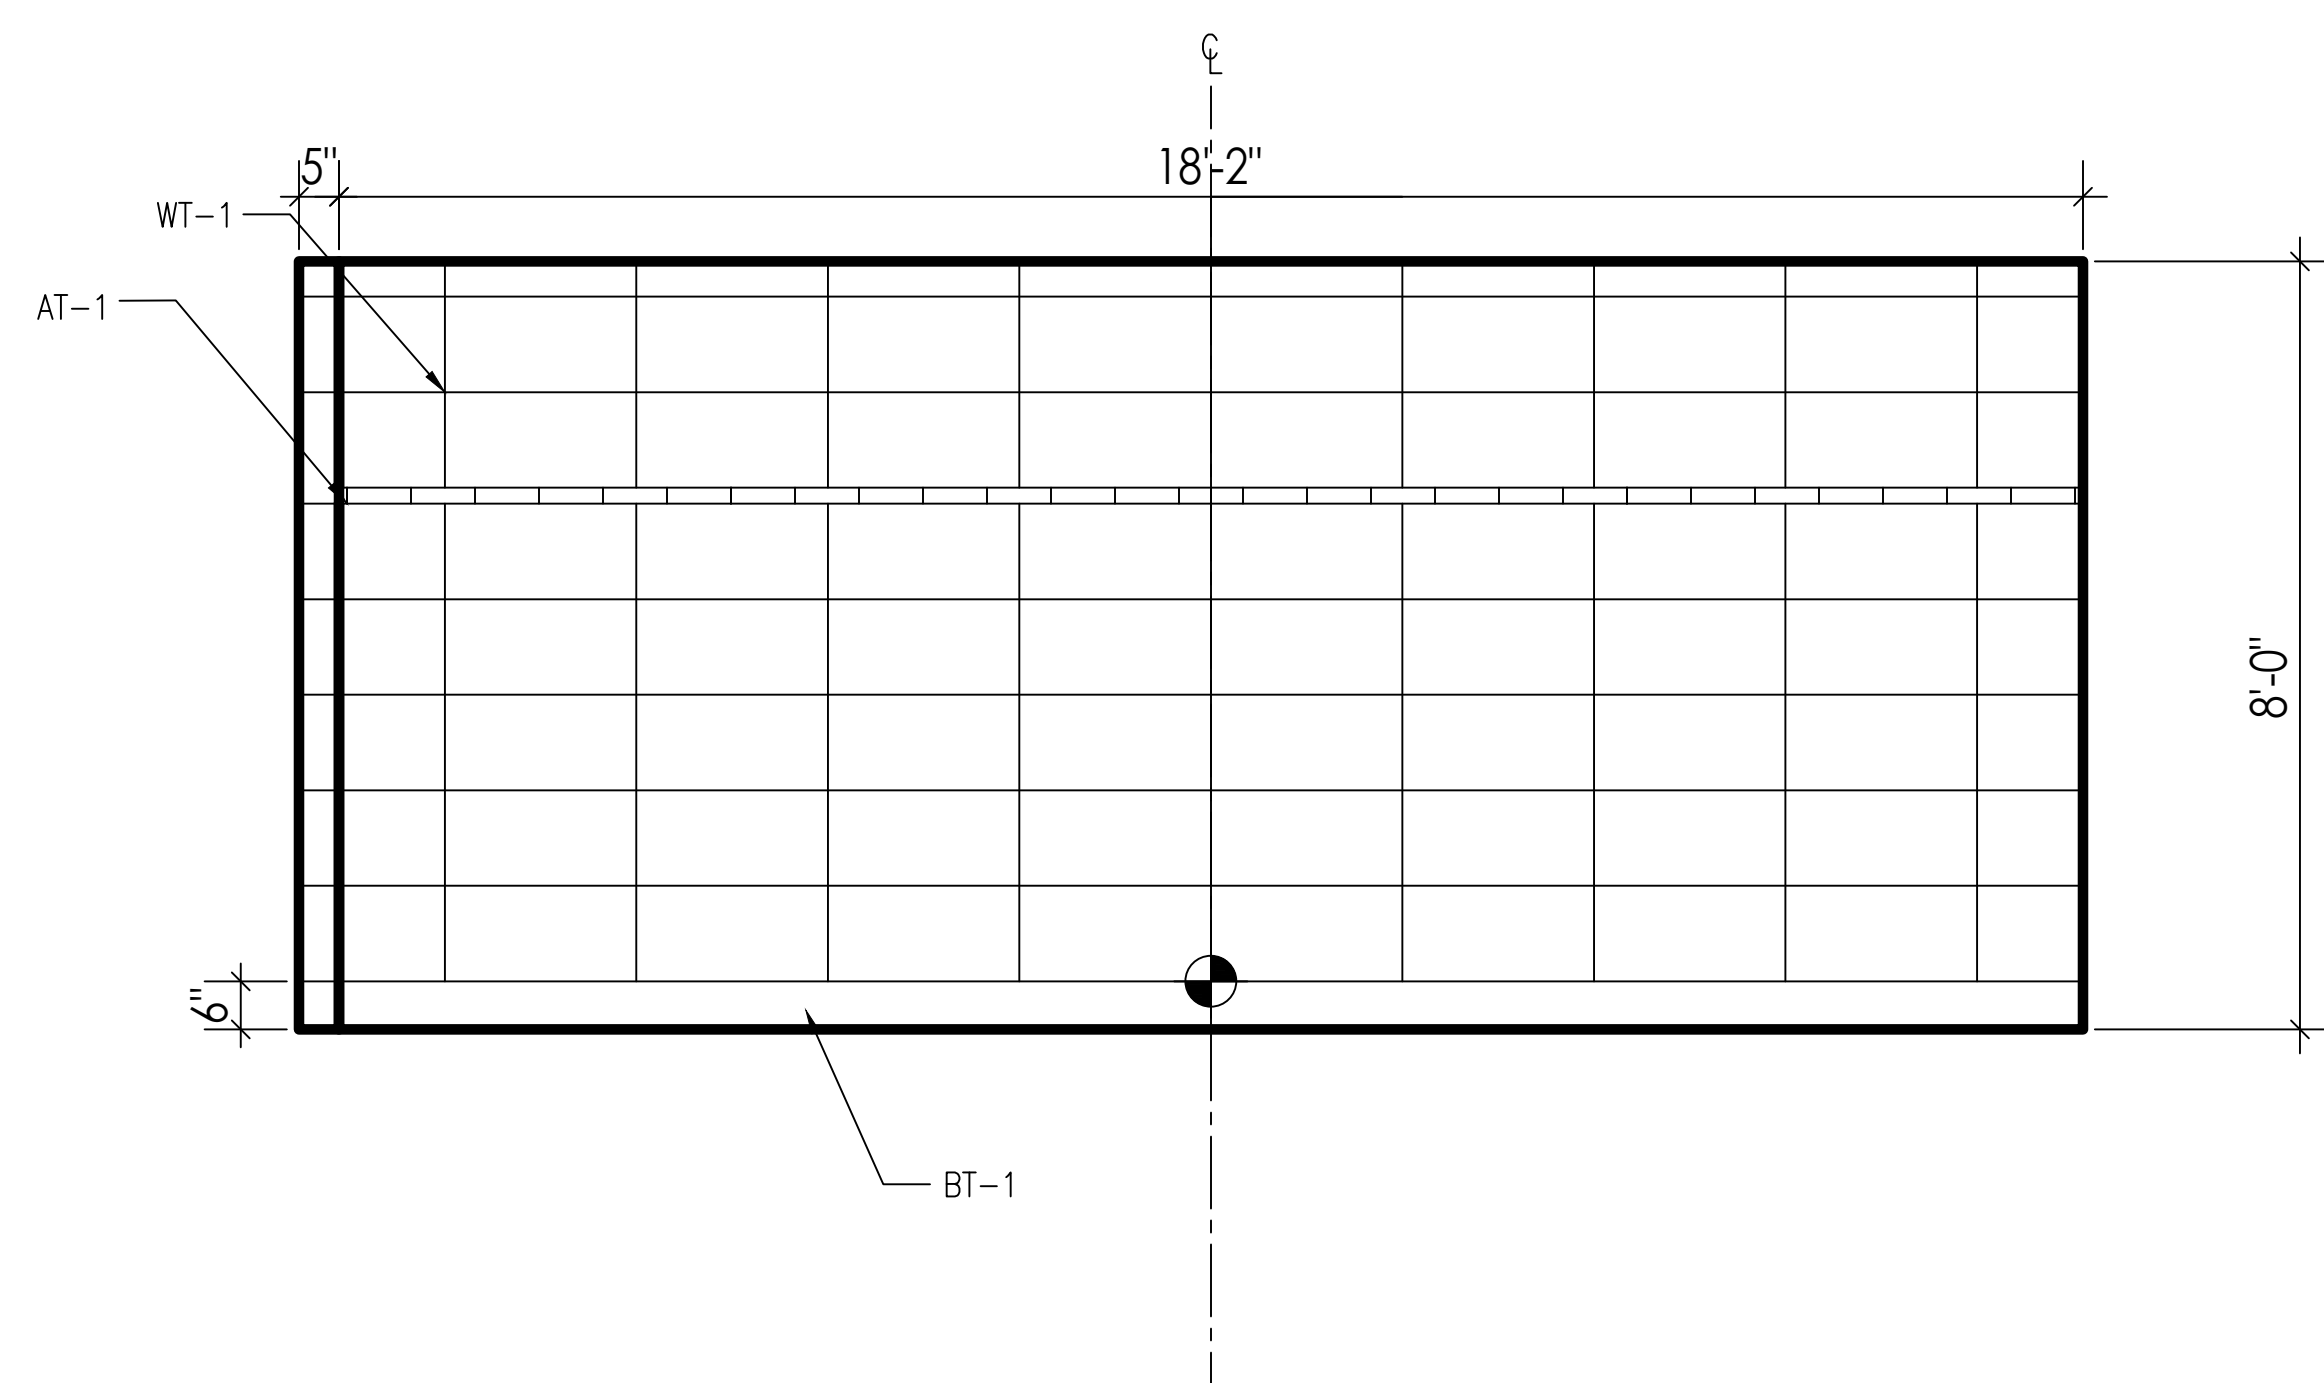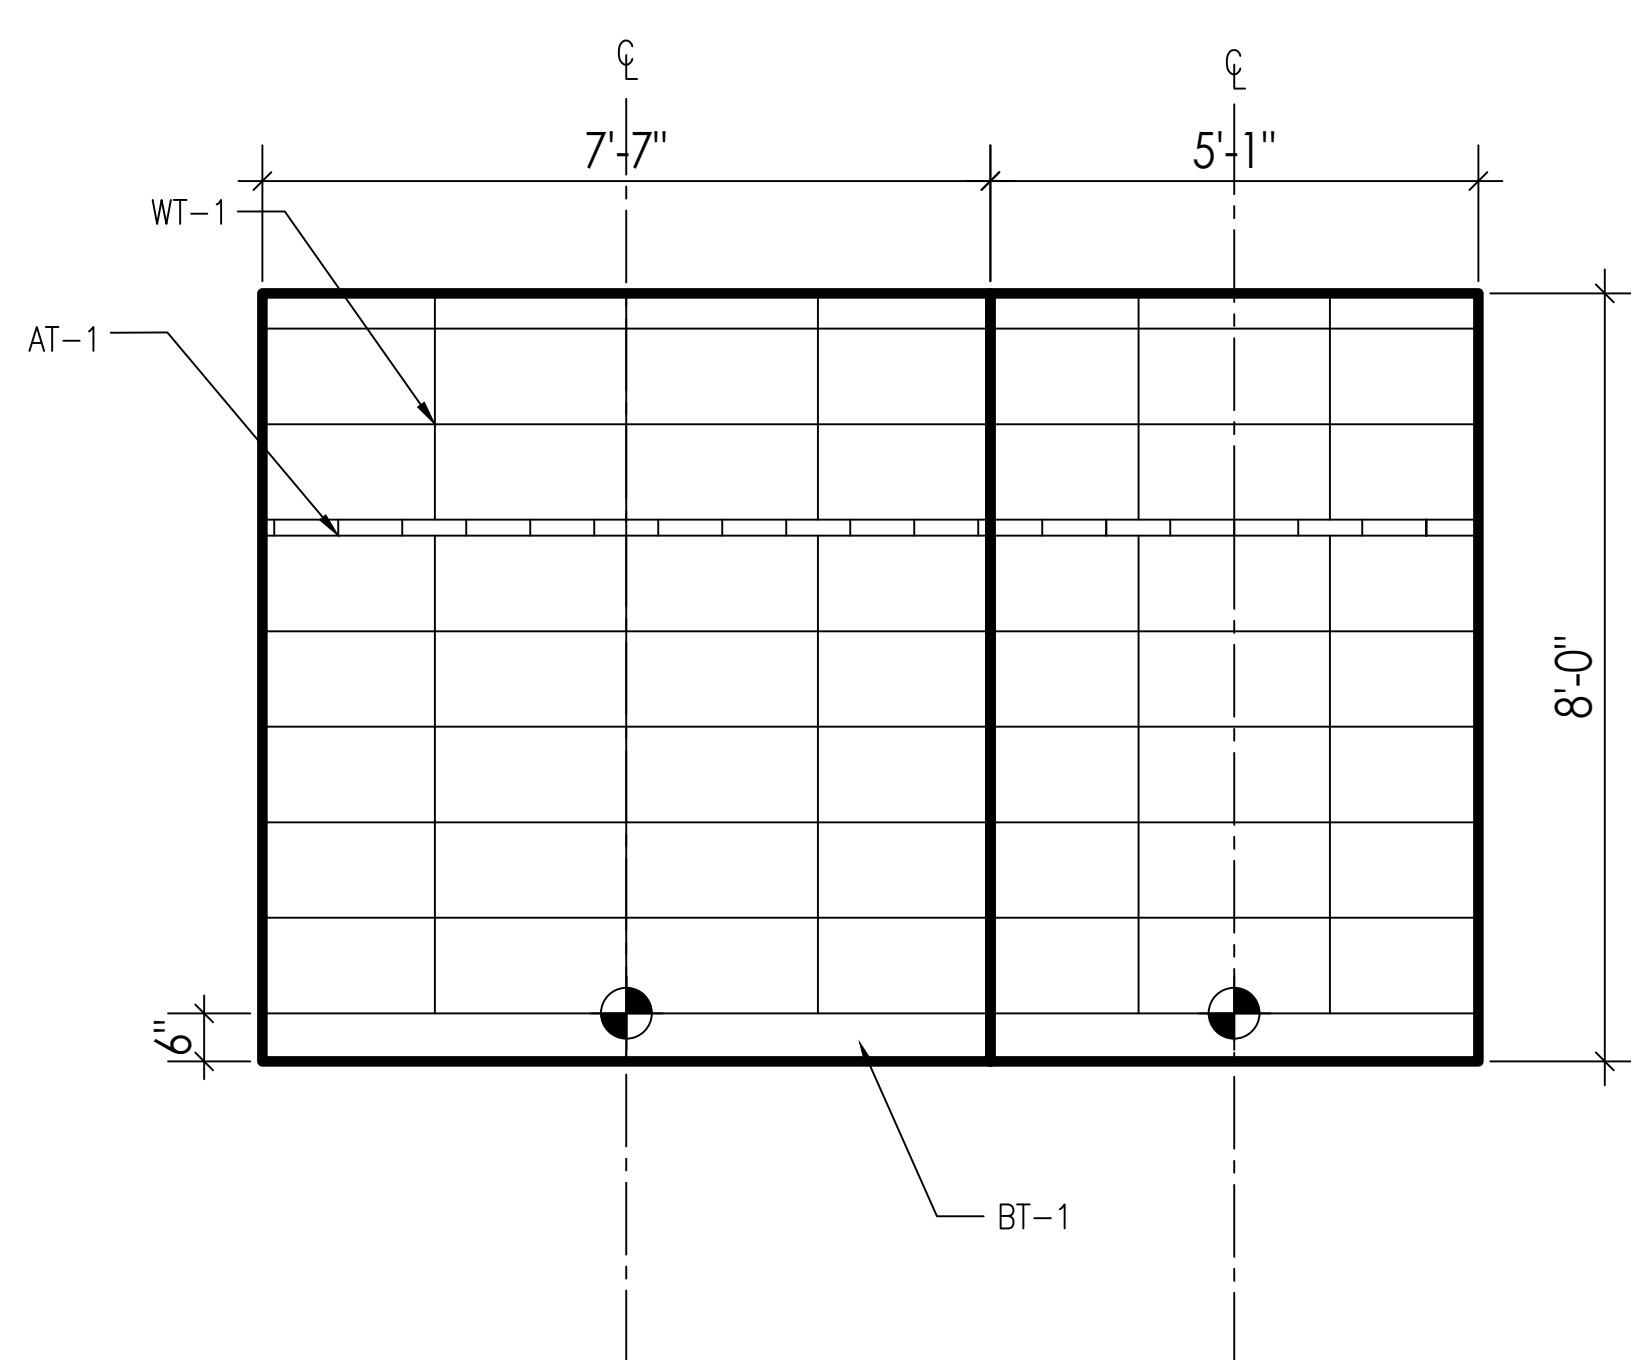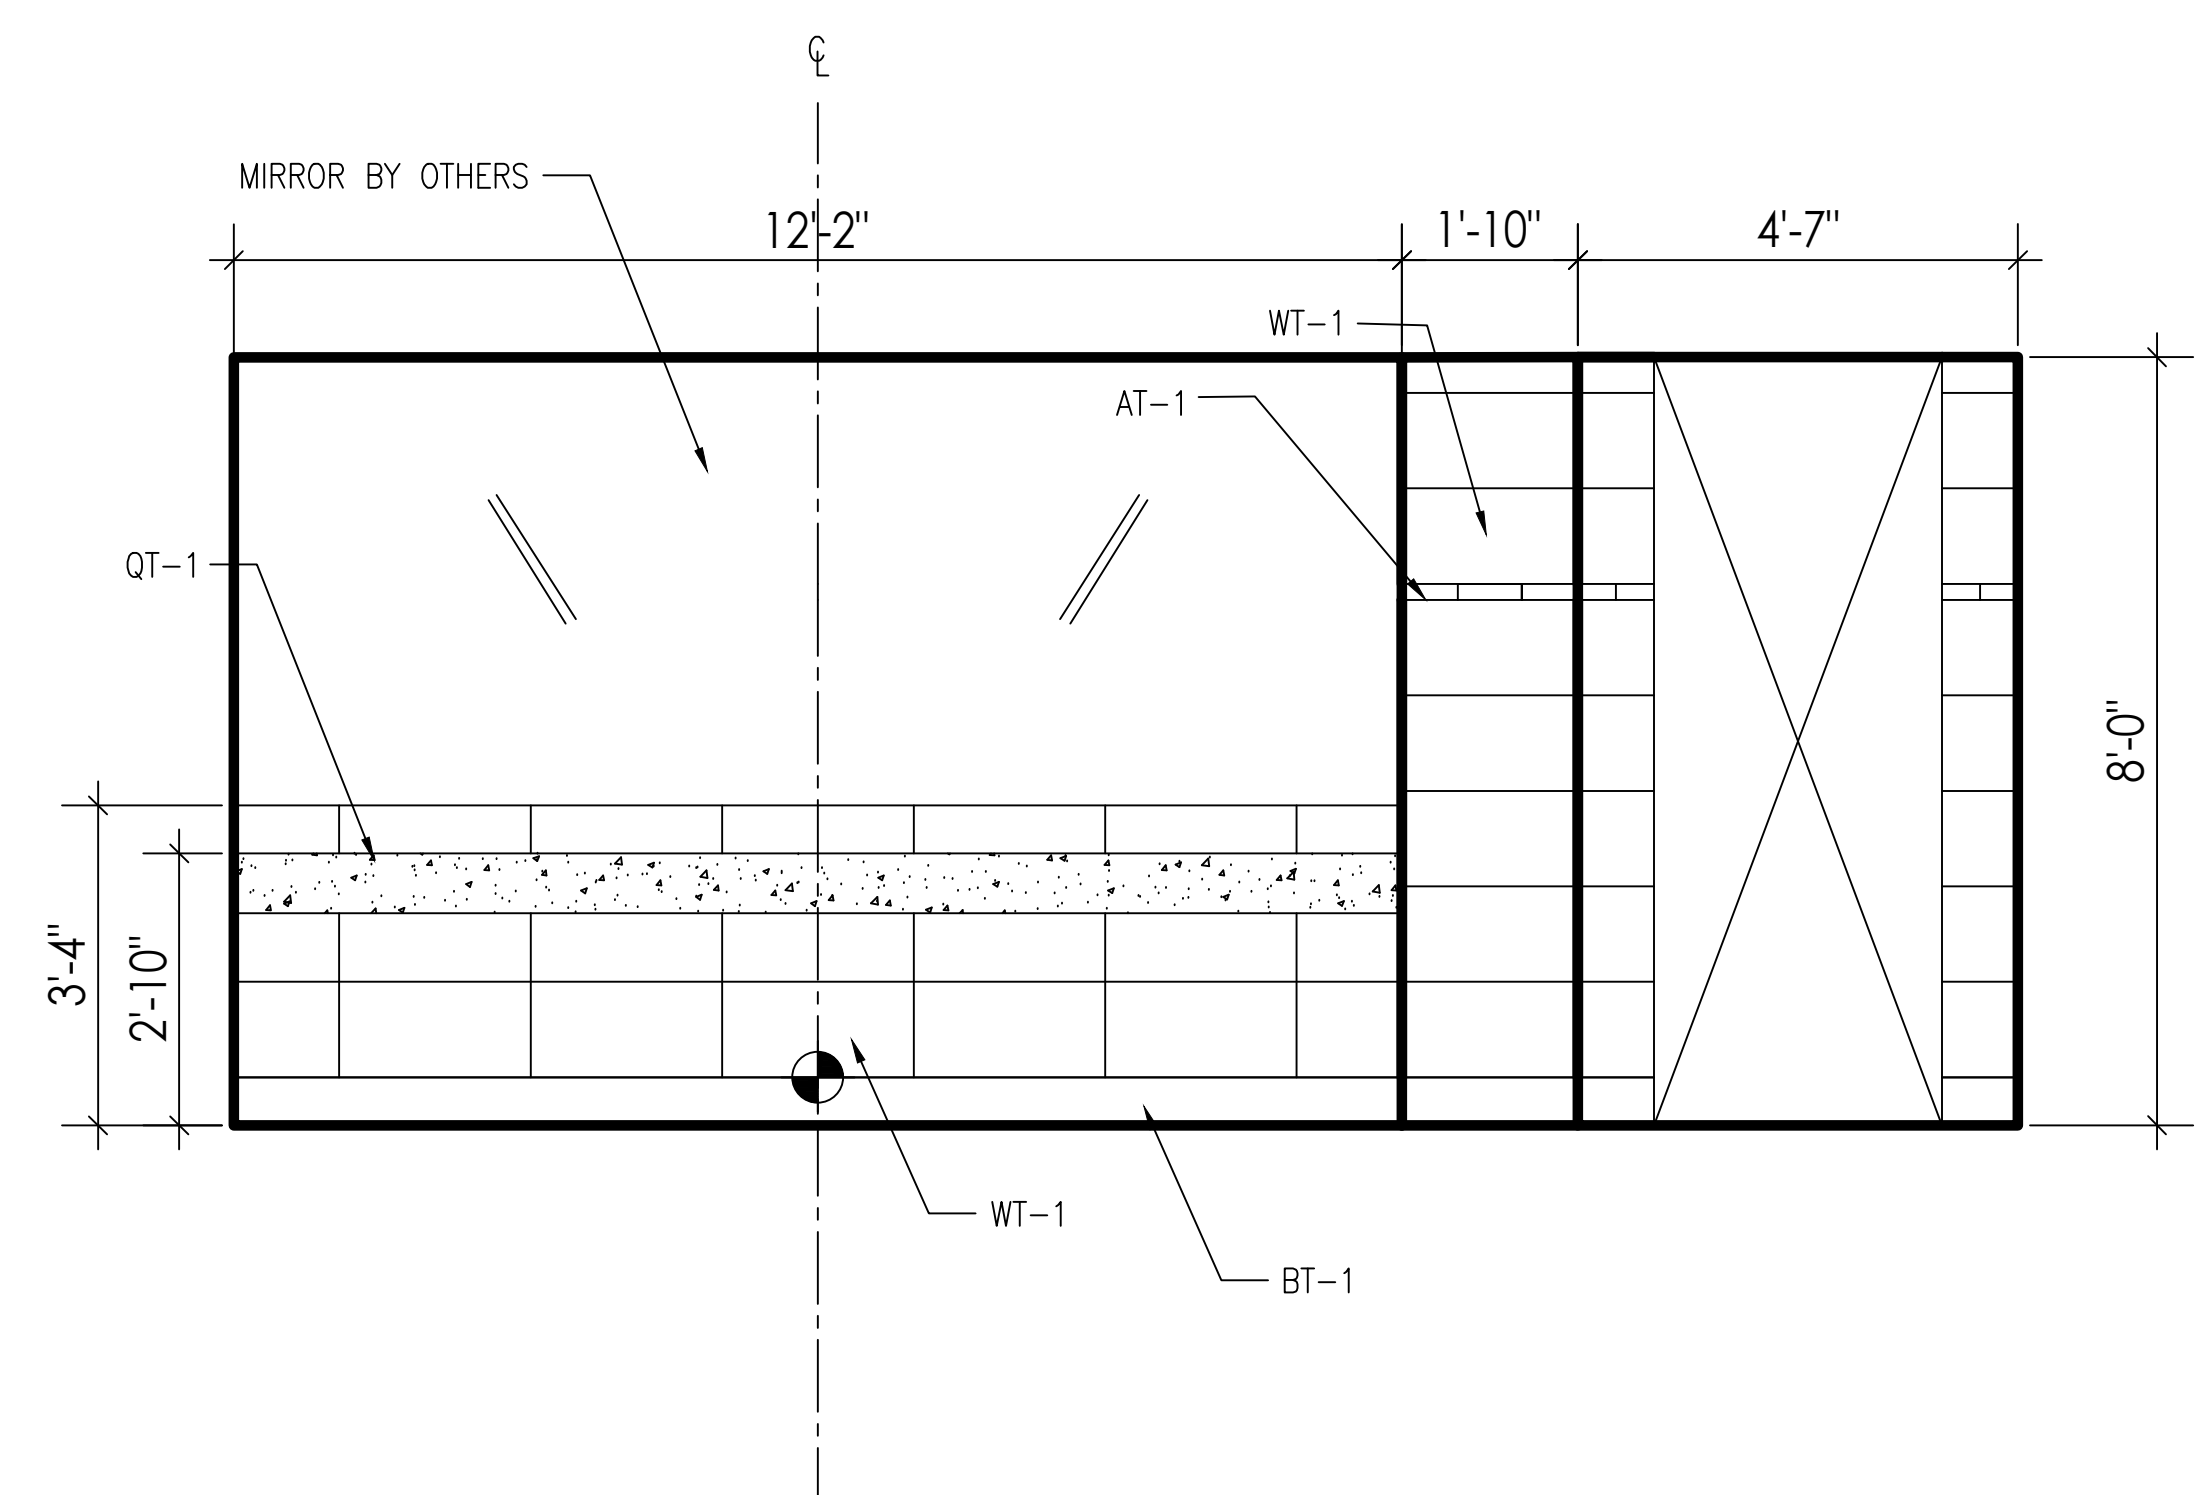


02
1/2"=1'-0" ELEVATIONS: 6TH FLOOR BATHROOMS

03
1/2"=1'-0" ELEVATIONS: 6TH FLOOR BATHROOMS


04
1/2"=1'-0" ELEVATIONS: 6TH FLOOR BATHROOMS

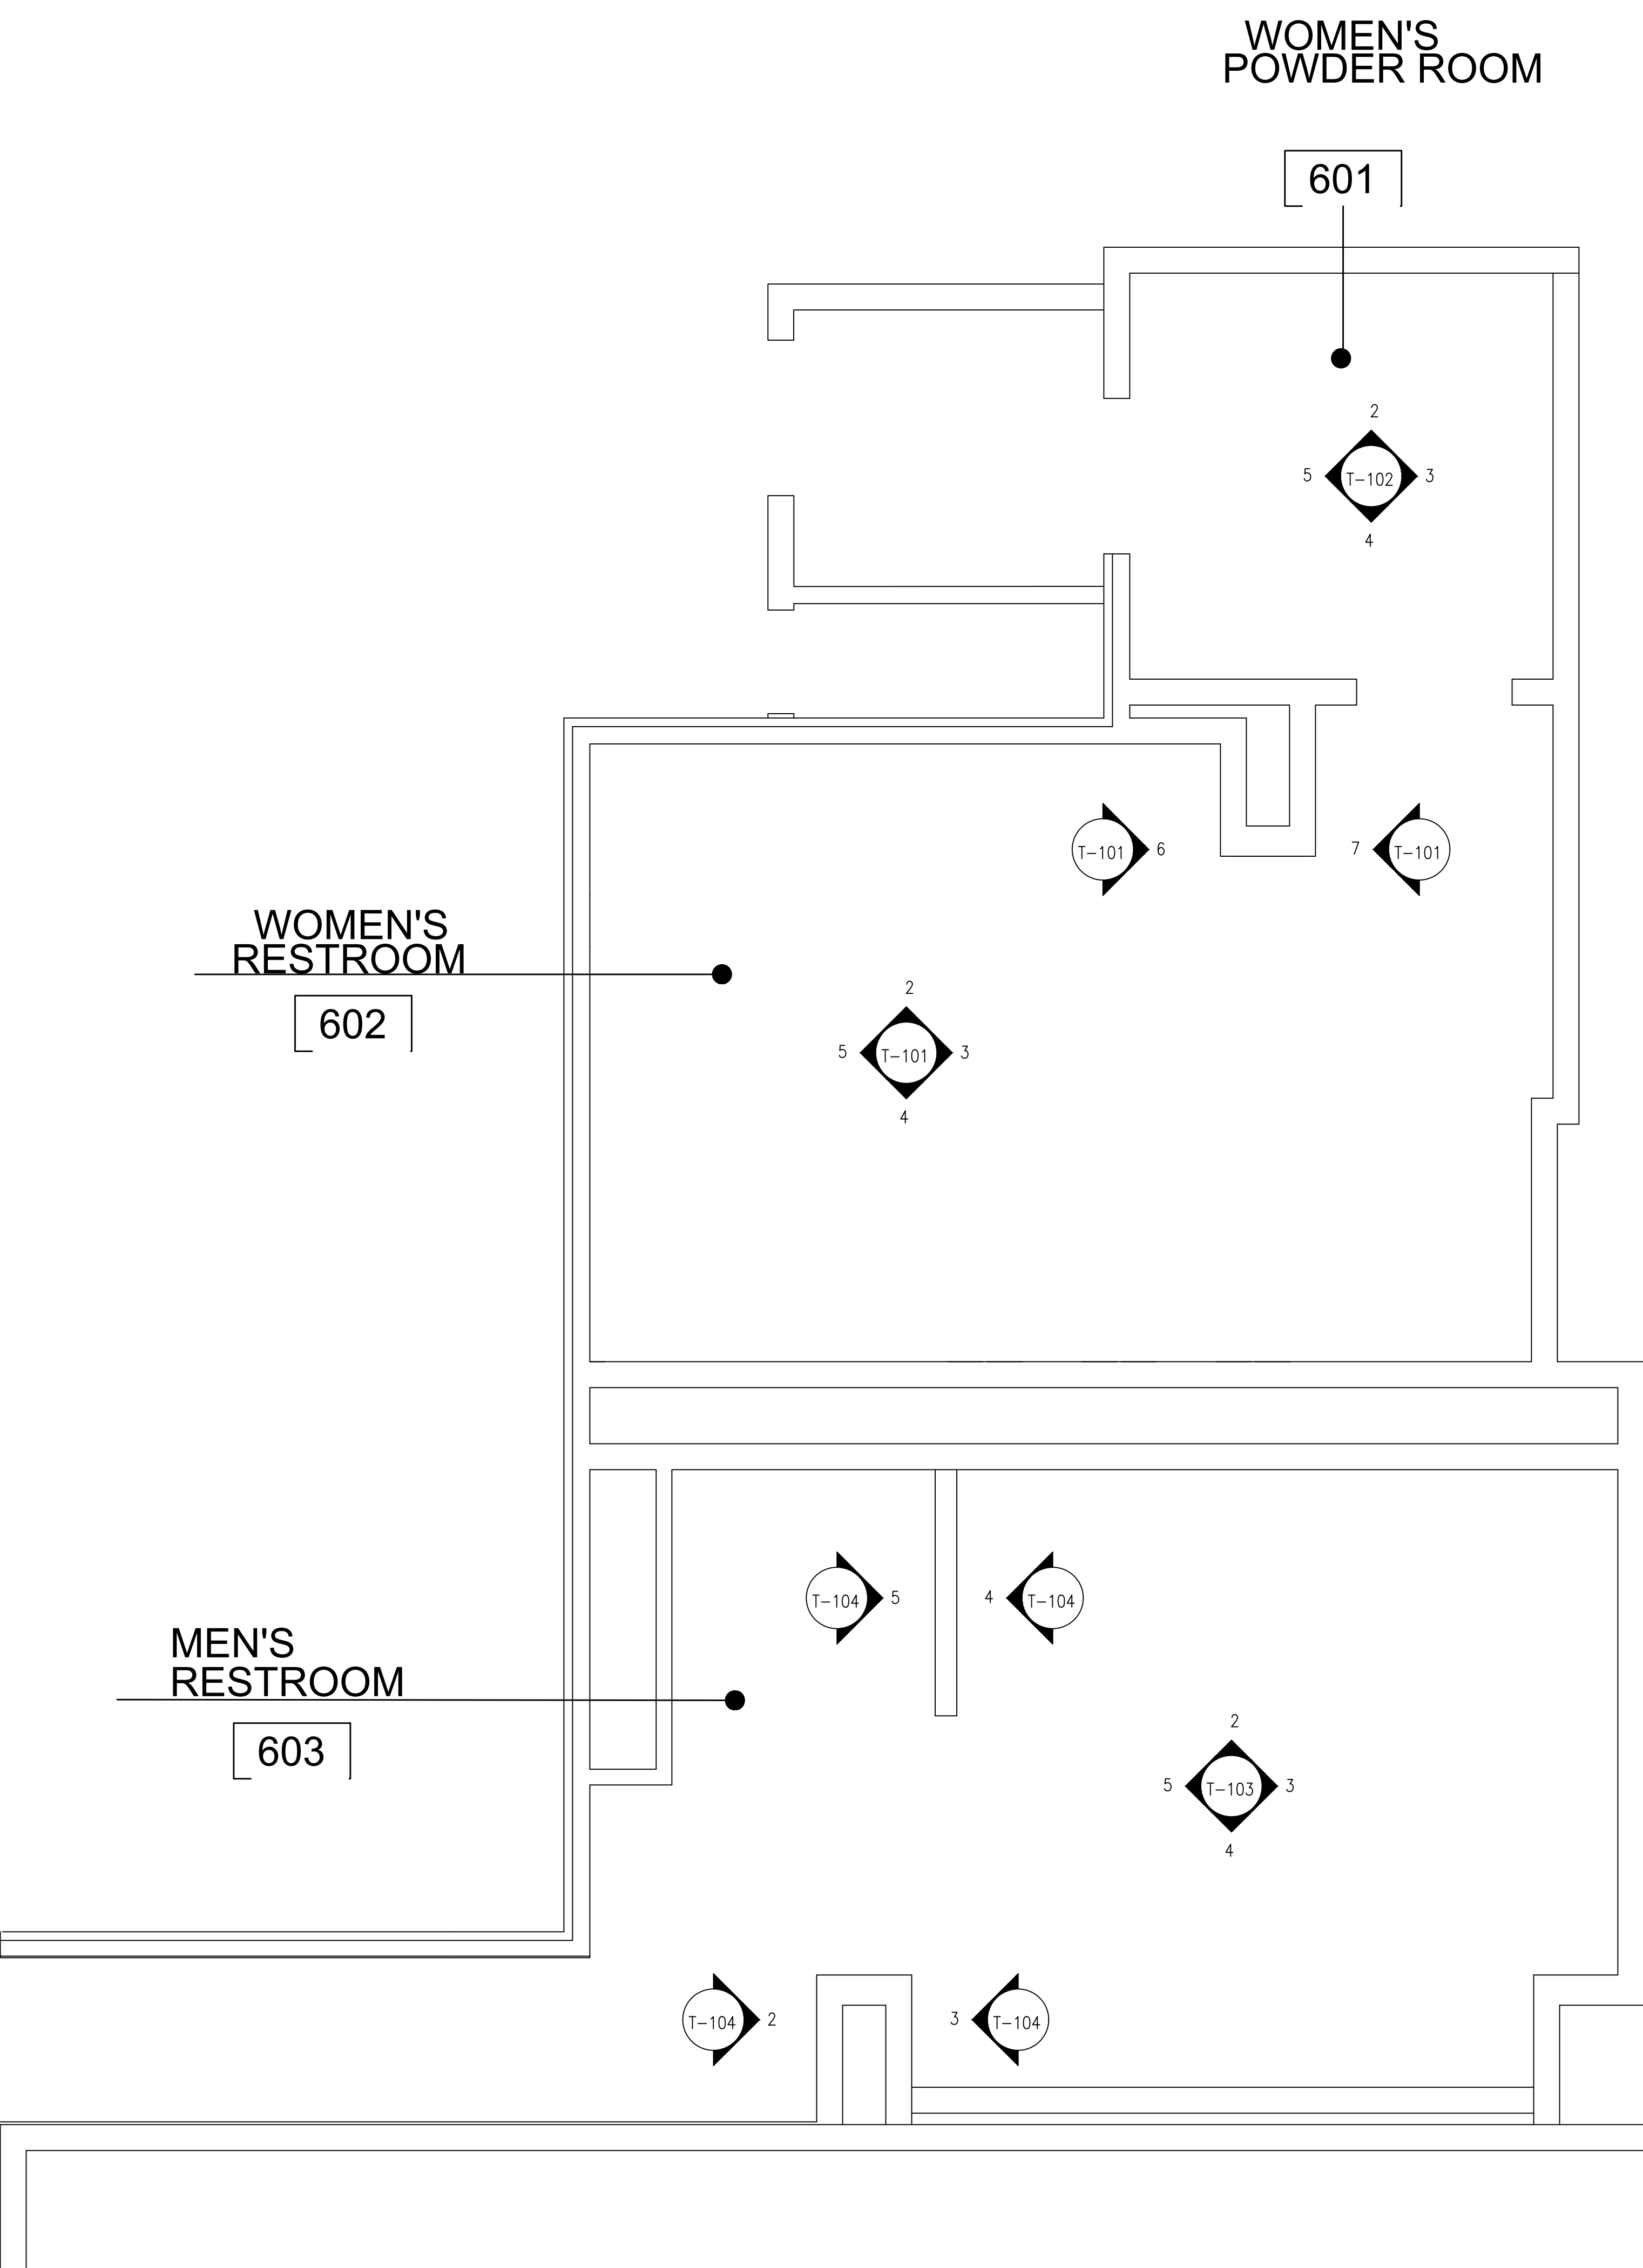


01
1/2"=1'-0" PLAN #2: 6TH FLOOR BATHROOMS

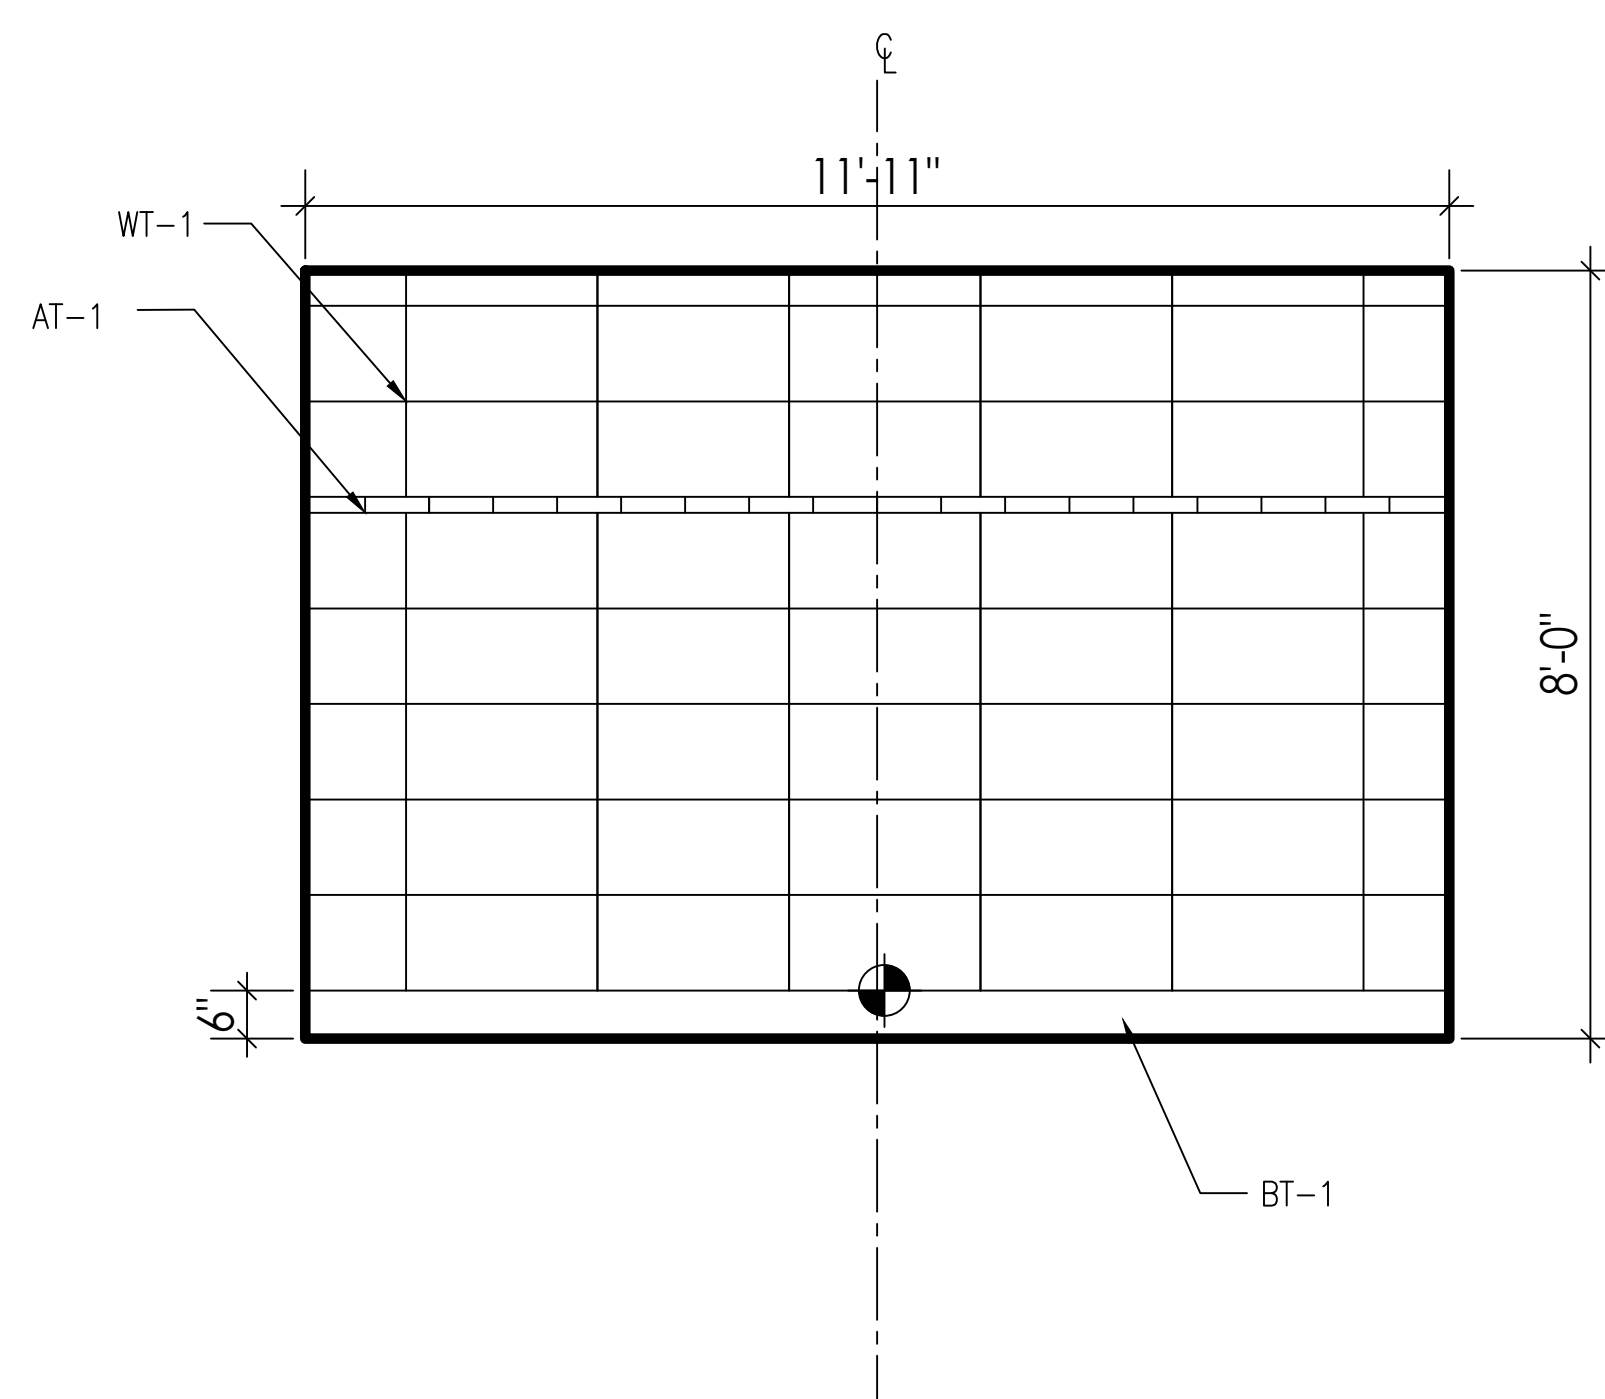

05
1/2"=1'-0" ELEVATIONS: 6TH FLOOR BATHROOMS

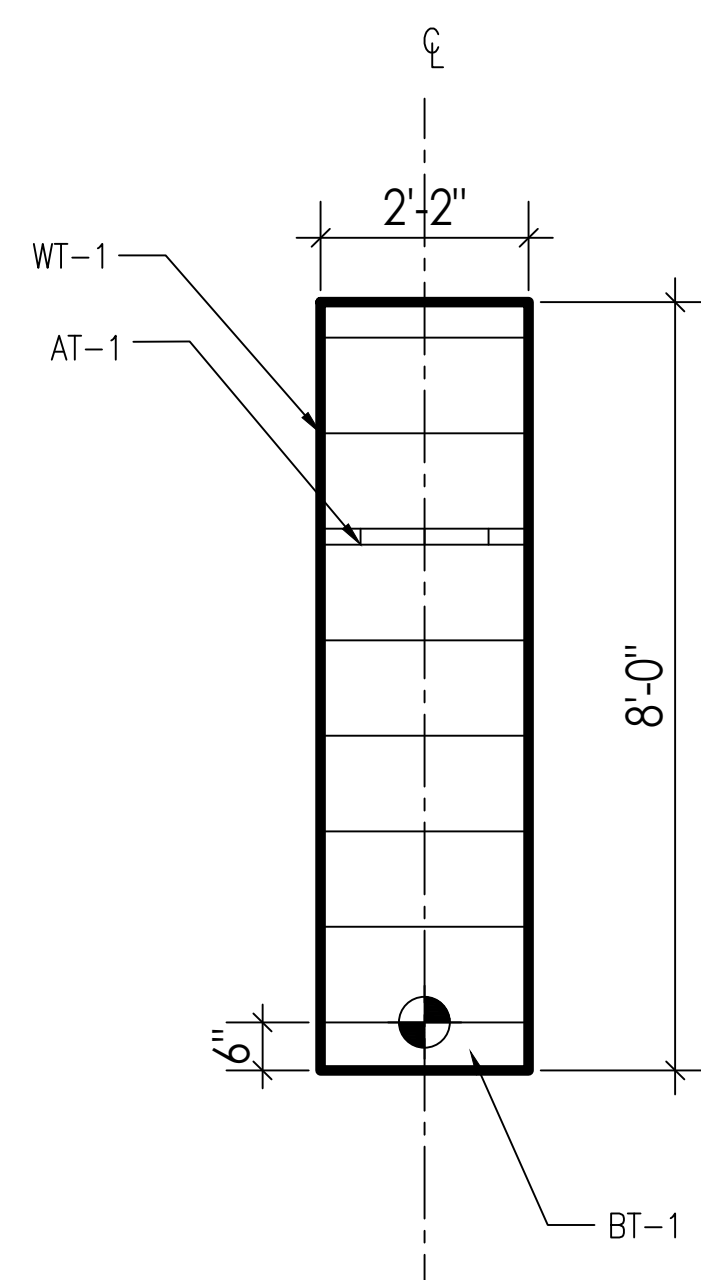

06
1/2"=1'-0" ELEVATIONS: 6TH FLOOR BATHROOMS

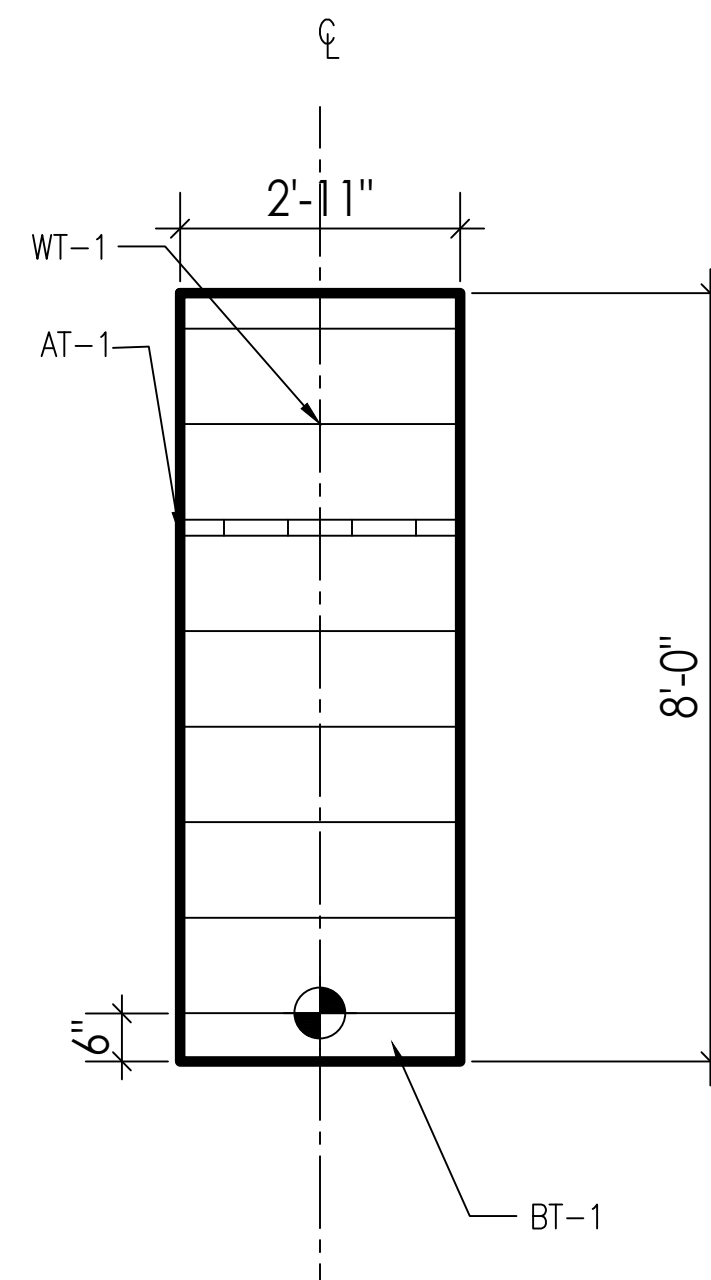

07
1/2"=1'-0" ELEVATIONS: 6TH FLOOR BATHROOMS

AUSTRO TILE & STONE, LLC
30-25 93RD STREET
EAST ELMHURST, NY 11369

CONTRACTOR:
JRM CONSTRUCTION
MANAGEMENT, LLC
242 WEST 36TH STREET
11TH FLOOR
NEW YORK, NY 10018

INTERIOR DESIGNER:

ISSUE FOR APPROVAL 10/09/23
ISSUE NAME DATE

ARCHITECT:
SPACESMITH
ONE NEW YORK PLAZA
NEW YORK, NY 10004
PH:212 260 5583

PROJECT NAME:
JACK RESNICK & SONS
255 GREENWICH STREET
NEW YORK, NY 10007

SHEET NAME:
ELEVATIONS
6TH FLOOR BATHROOMS



DATE:
PROJECT NO.:
PRINCIPAL:
DRAWING BY:
CHECKED BY:
SCALE:
DWG. No.:
T-101
3 of 29




STARTING POINT

(BT-1) TILE BASE GROUT JOINTS WILL NOT ALIGN WITH (WT-1) WALL TILE GROUT JOINTS


(AT-1) ACCENT WALL TILE GROUT JOINTS WILL NOT ALIGN WITH (WT-1) WALL TILE GROUT JOINTS

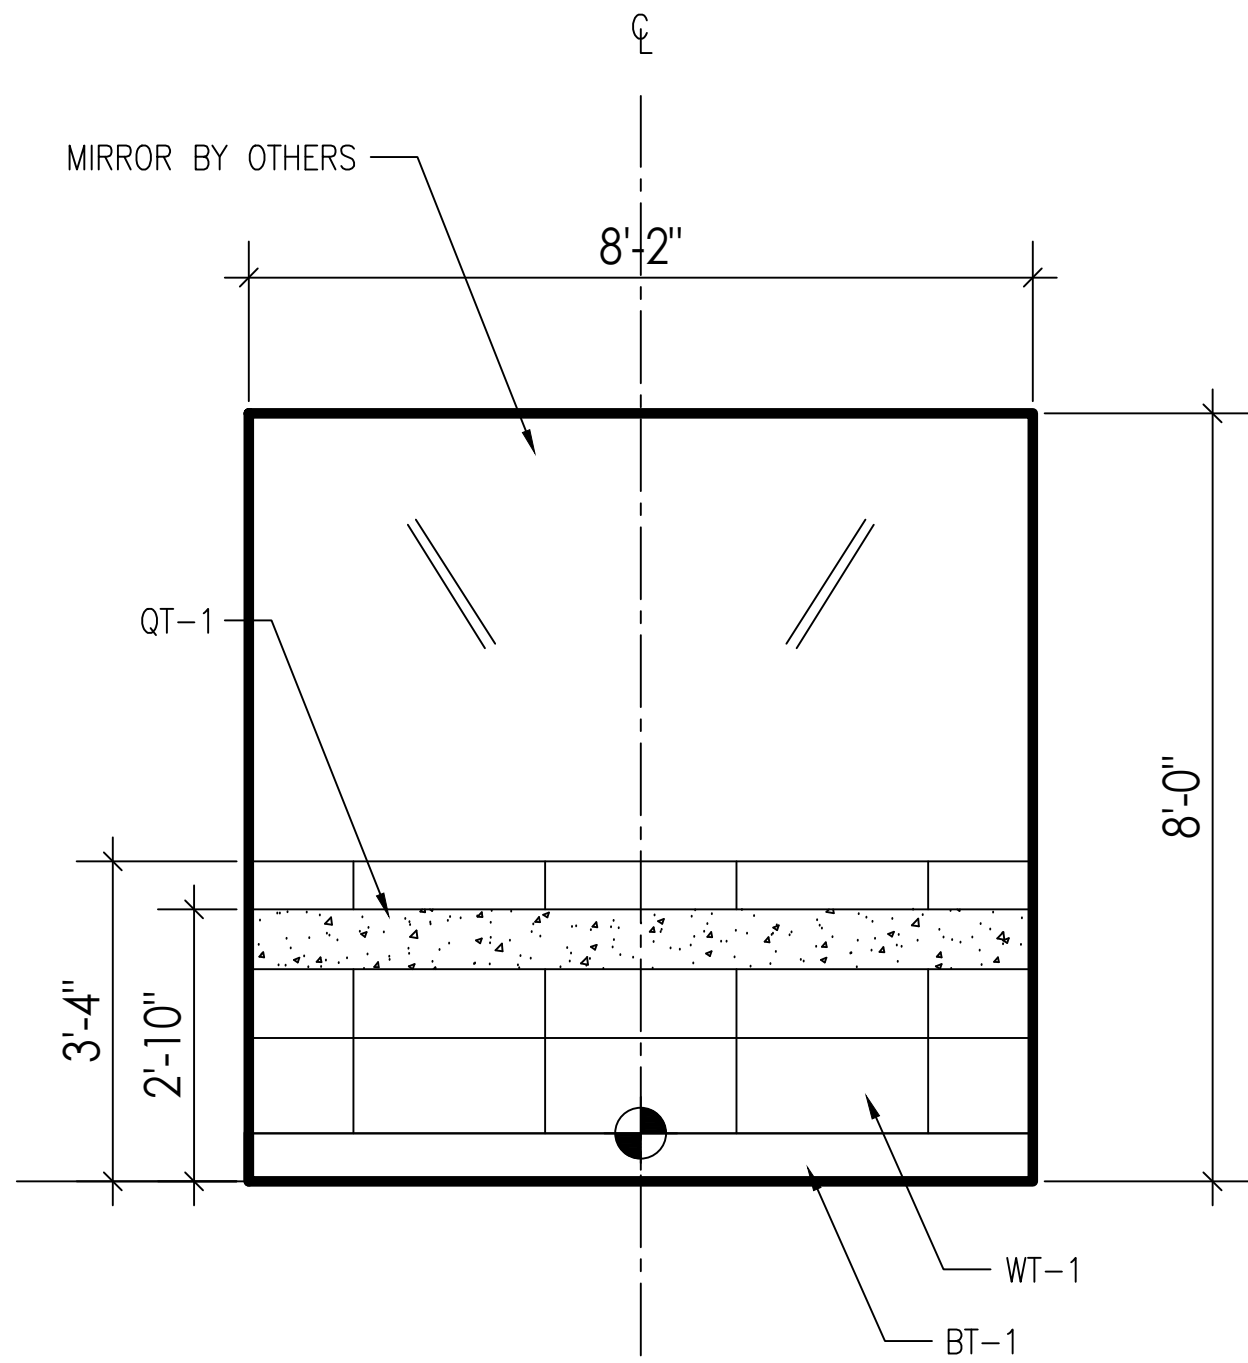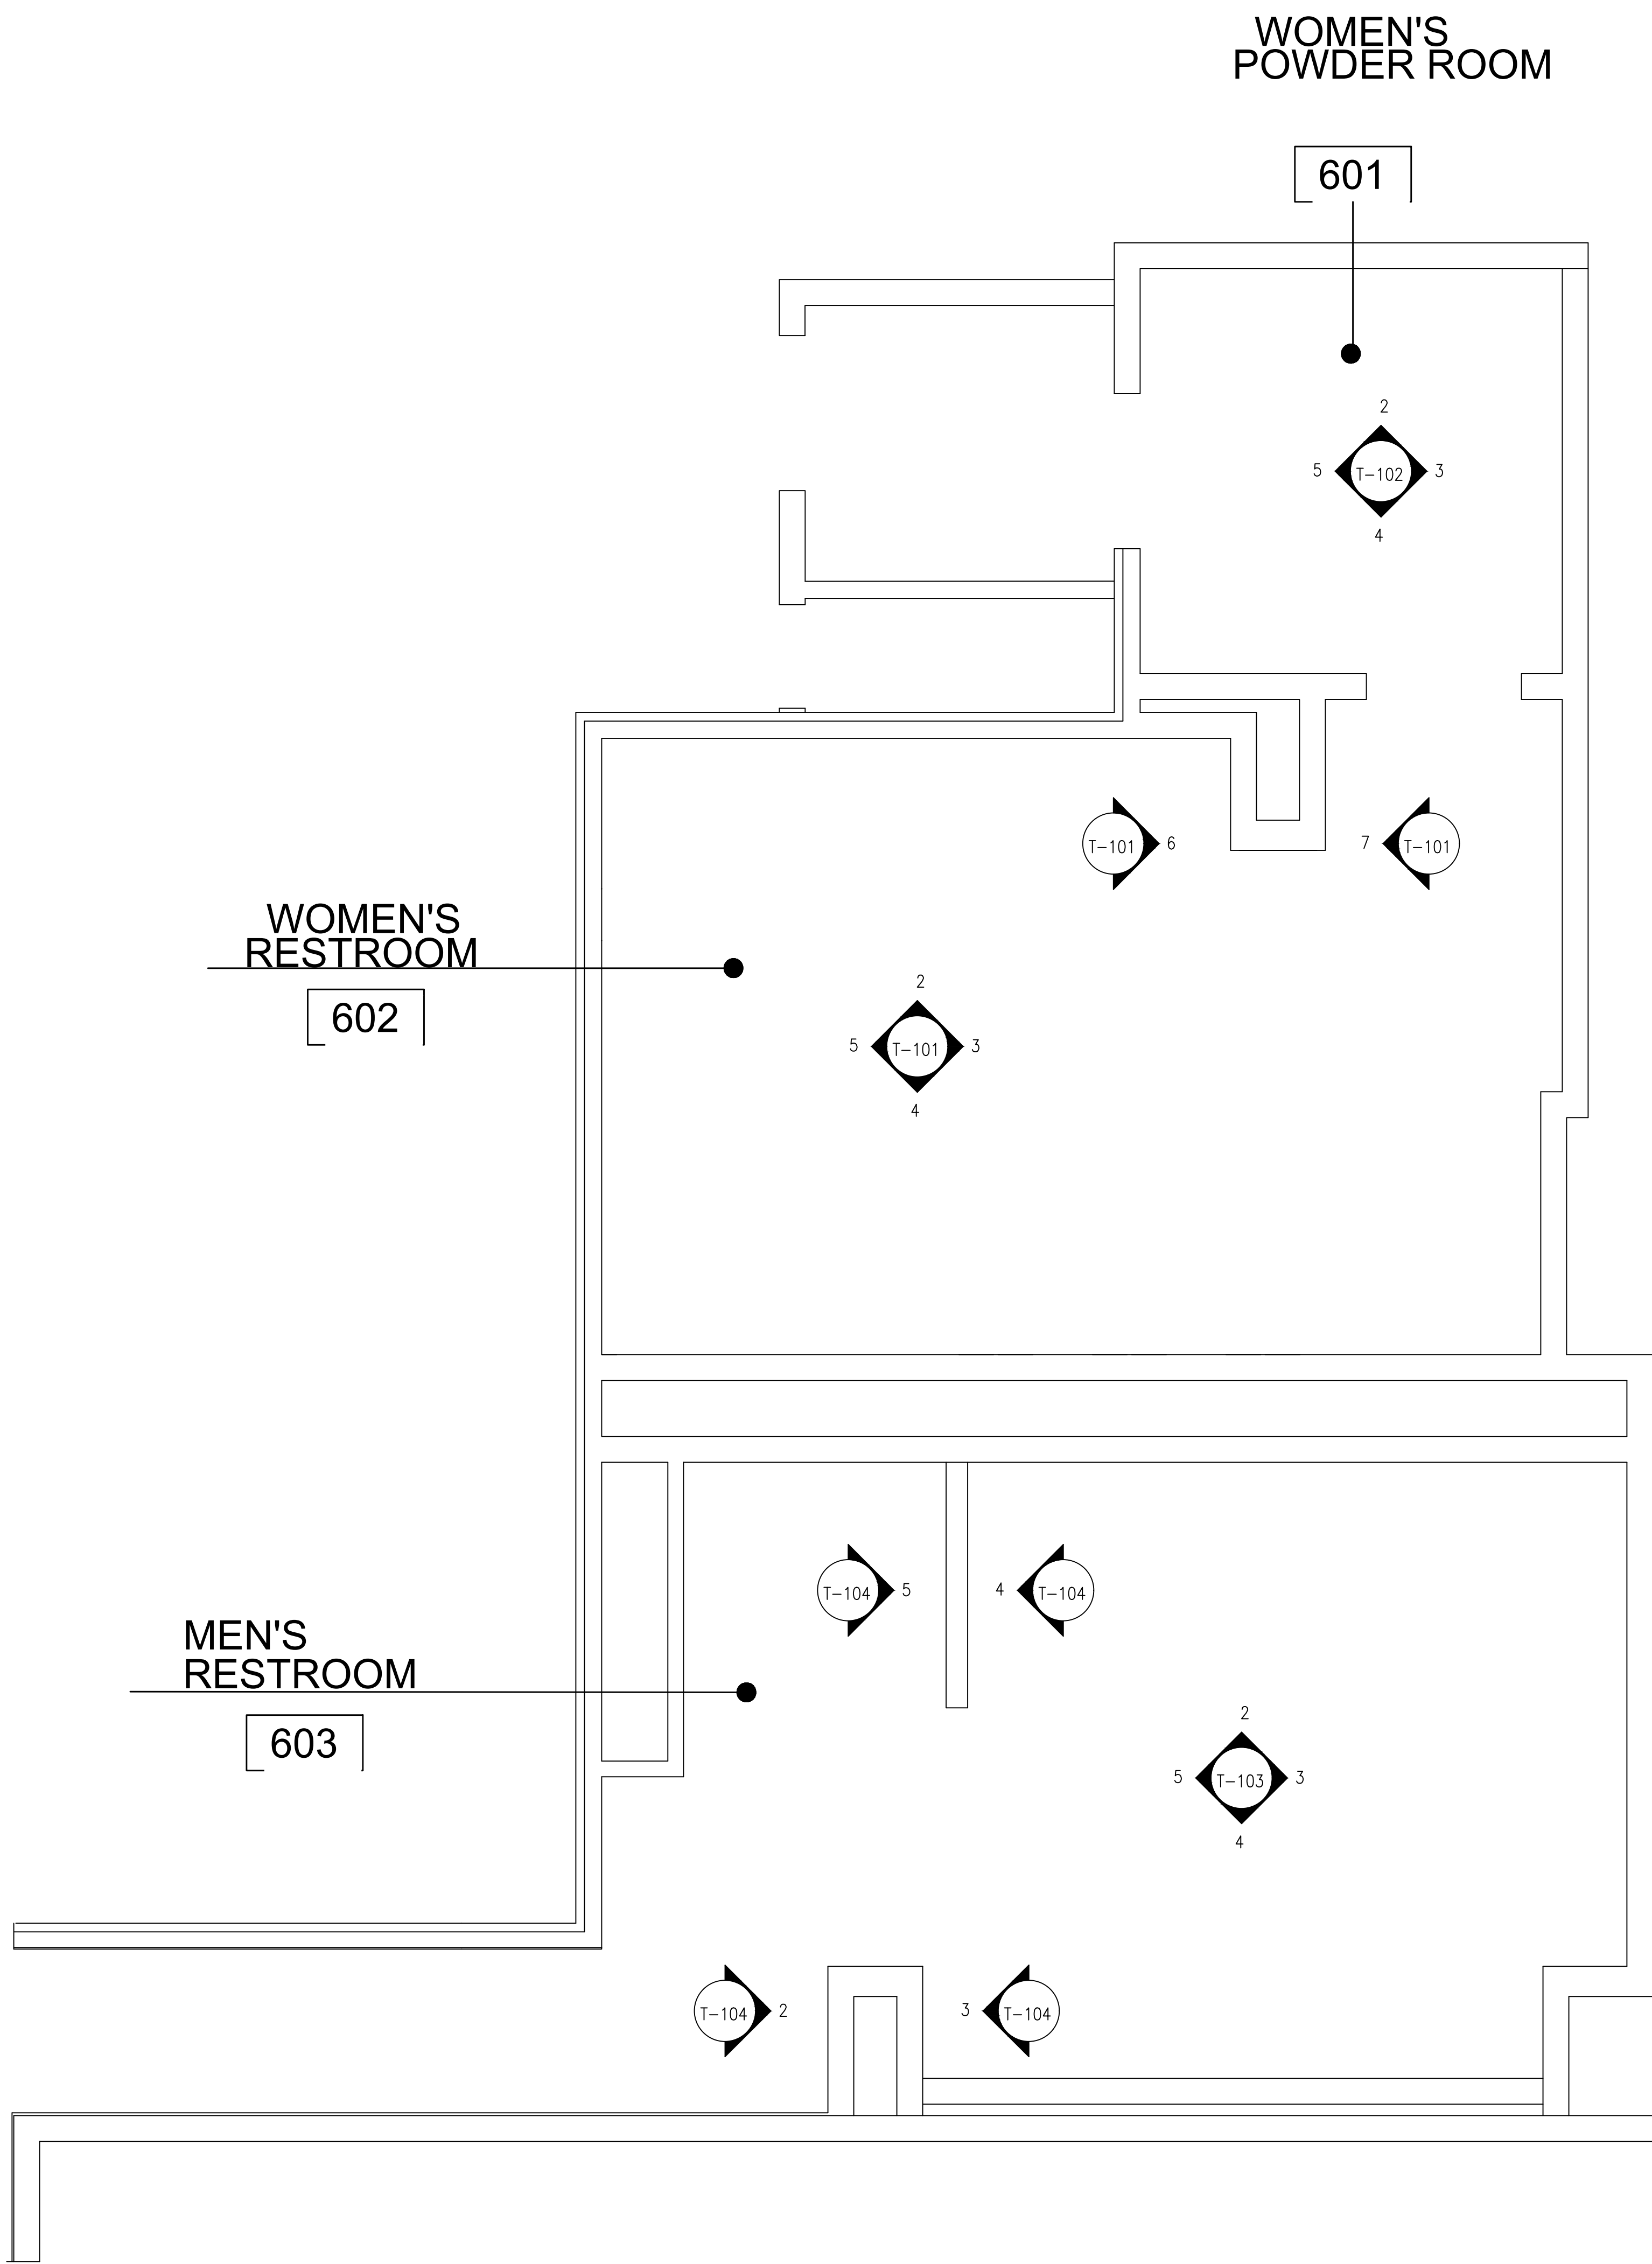


02
1/2"=1'-0" ELEVATIONS: 6TH FLOOR BATHROOMS

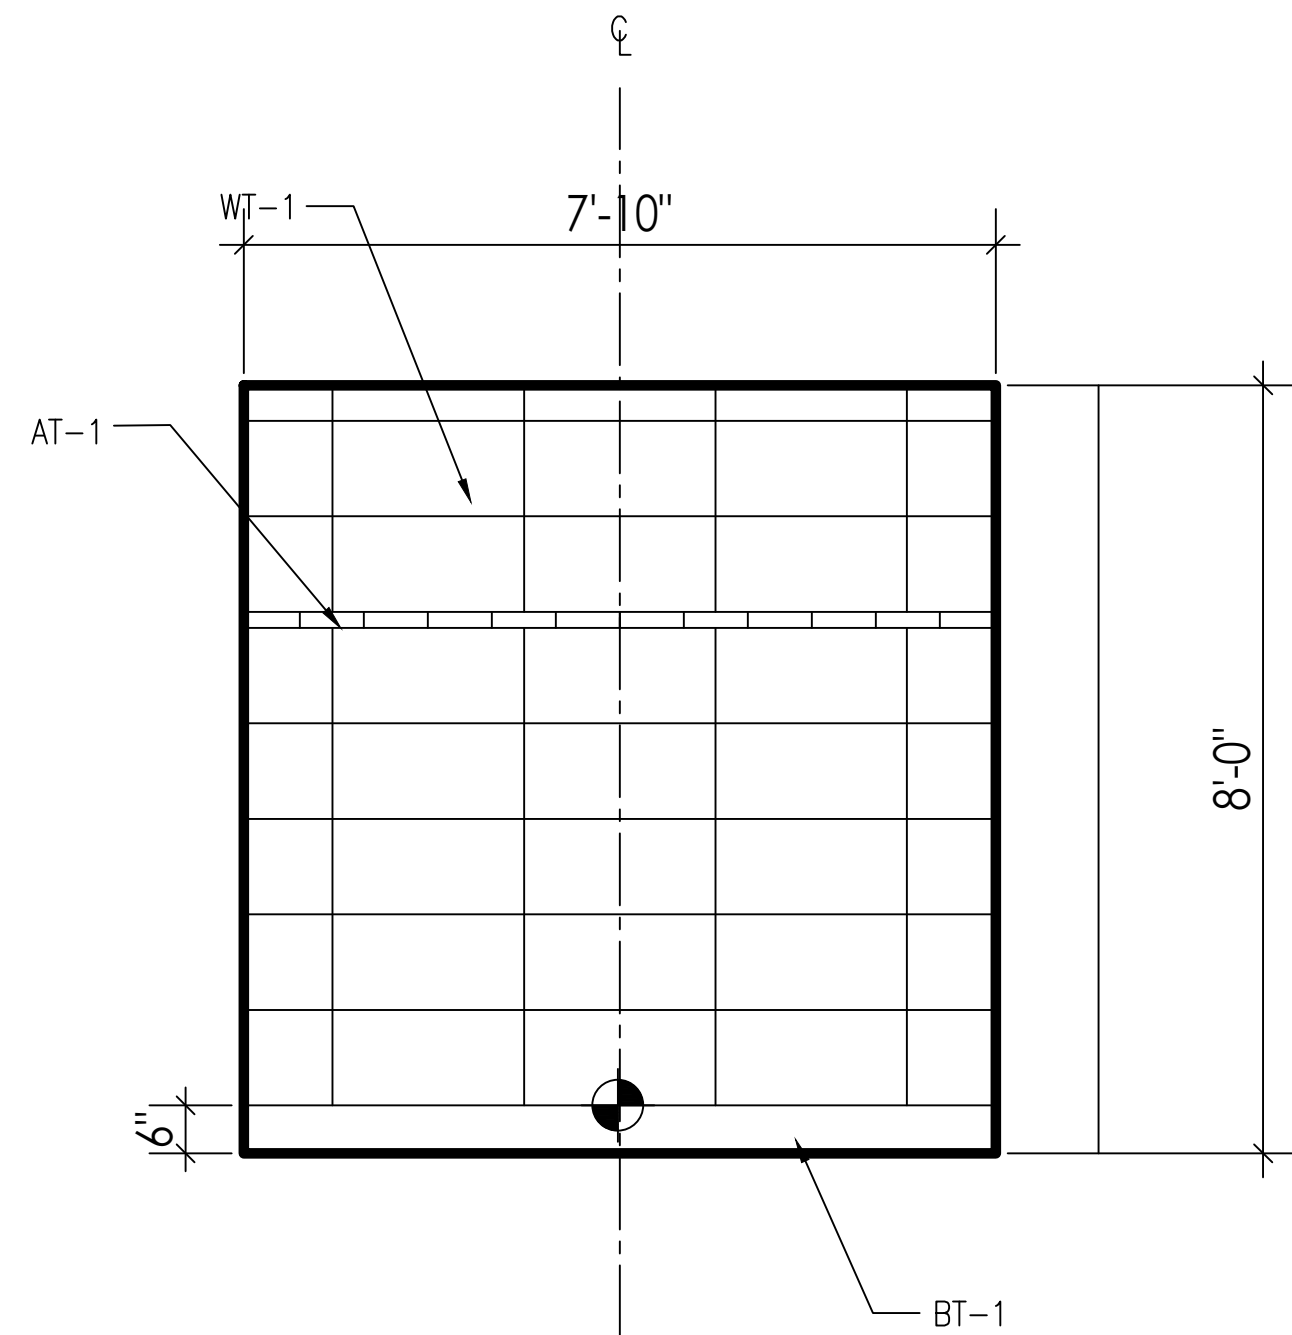

03
1/2"=1'-0" ELEVATIONS: 6TH FLOOR BATHROOMS

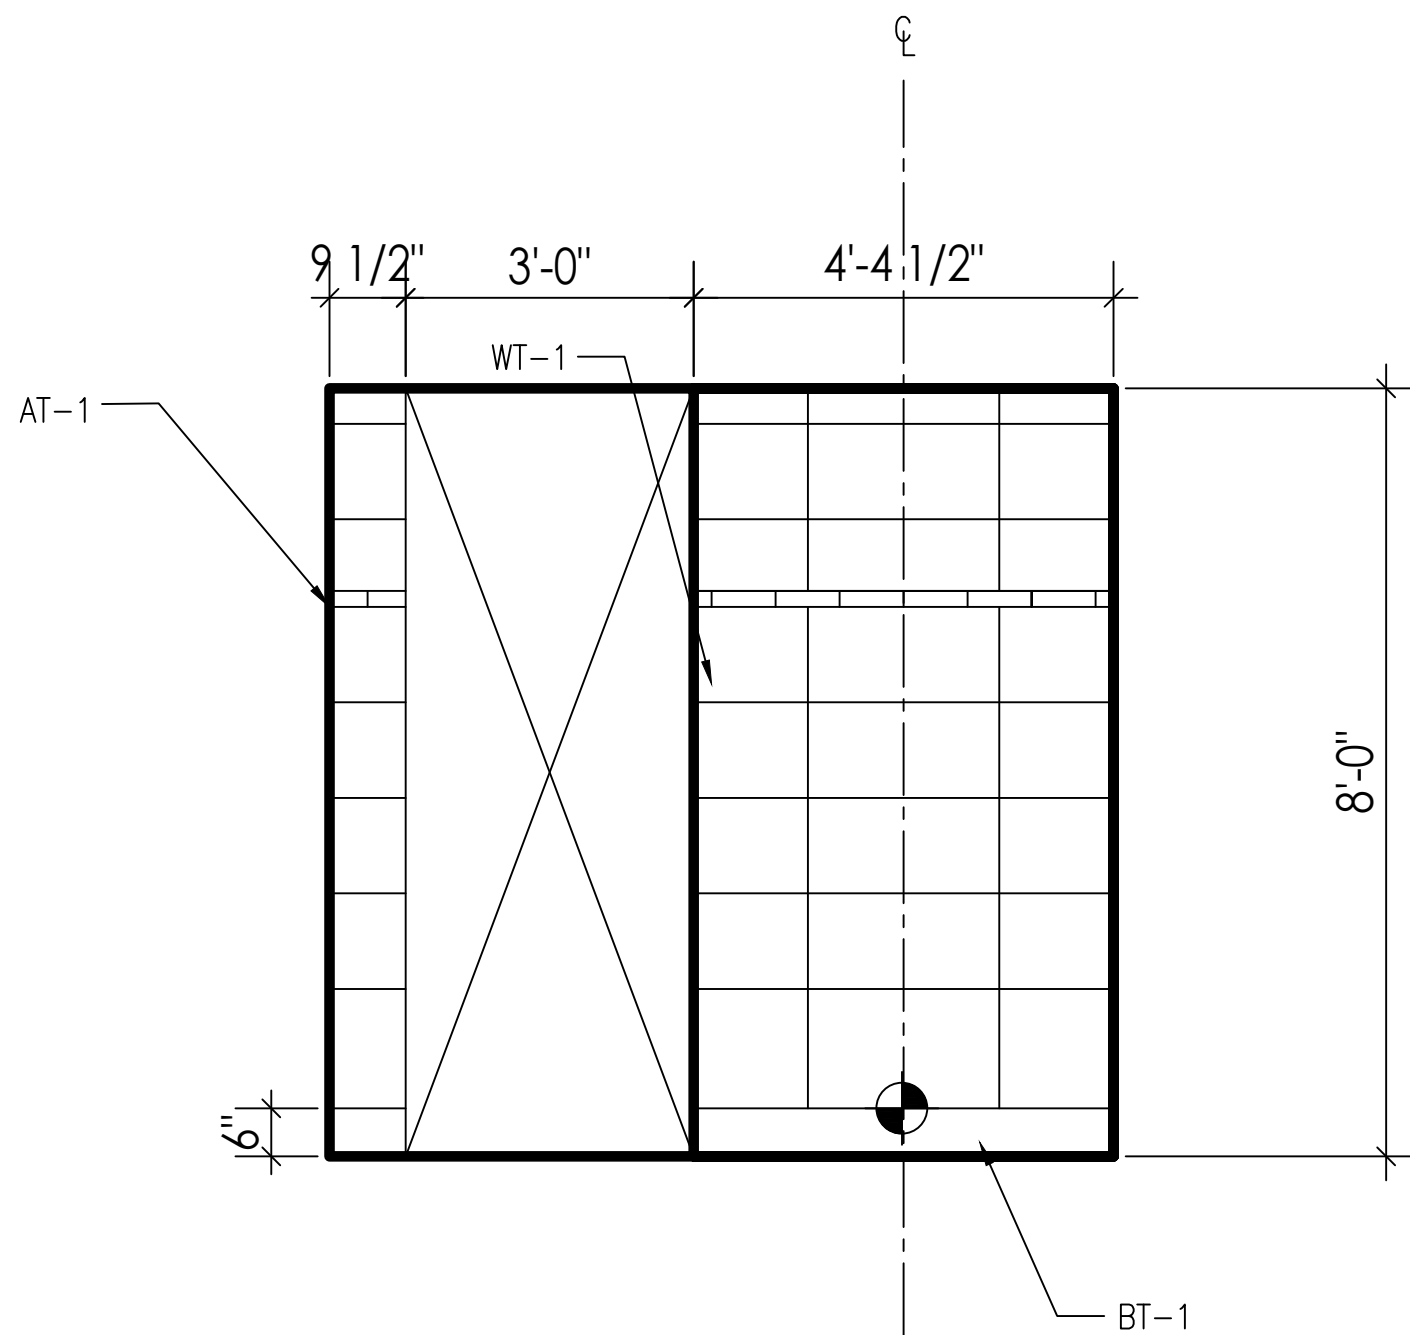

04
1/2"=1'-0" ELEVATIONS: 6TH FLOOR BATHROOMS

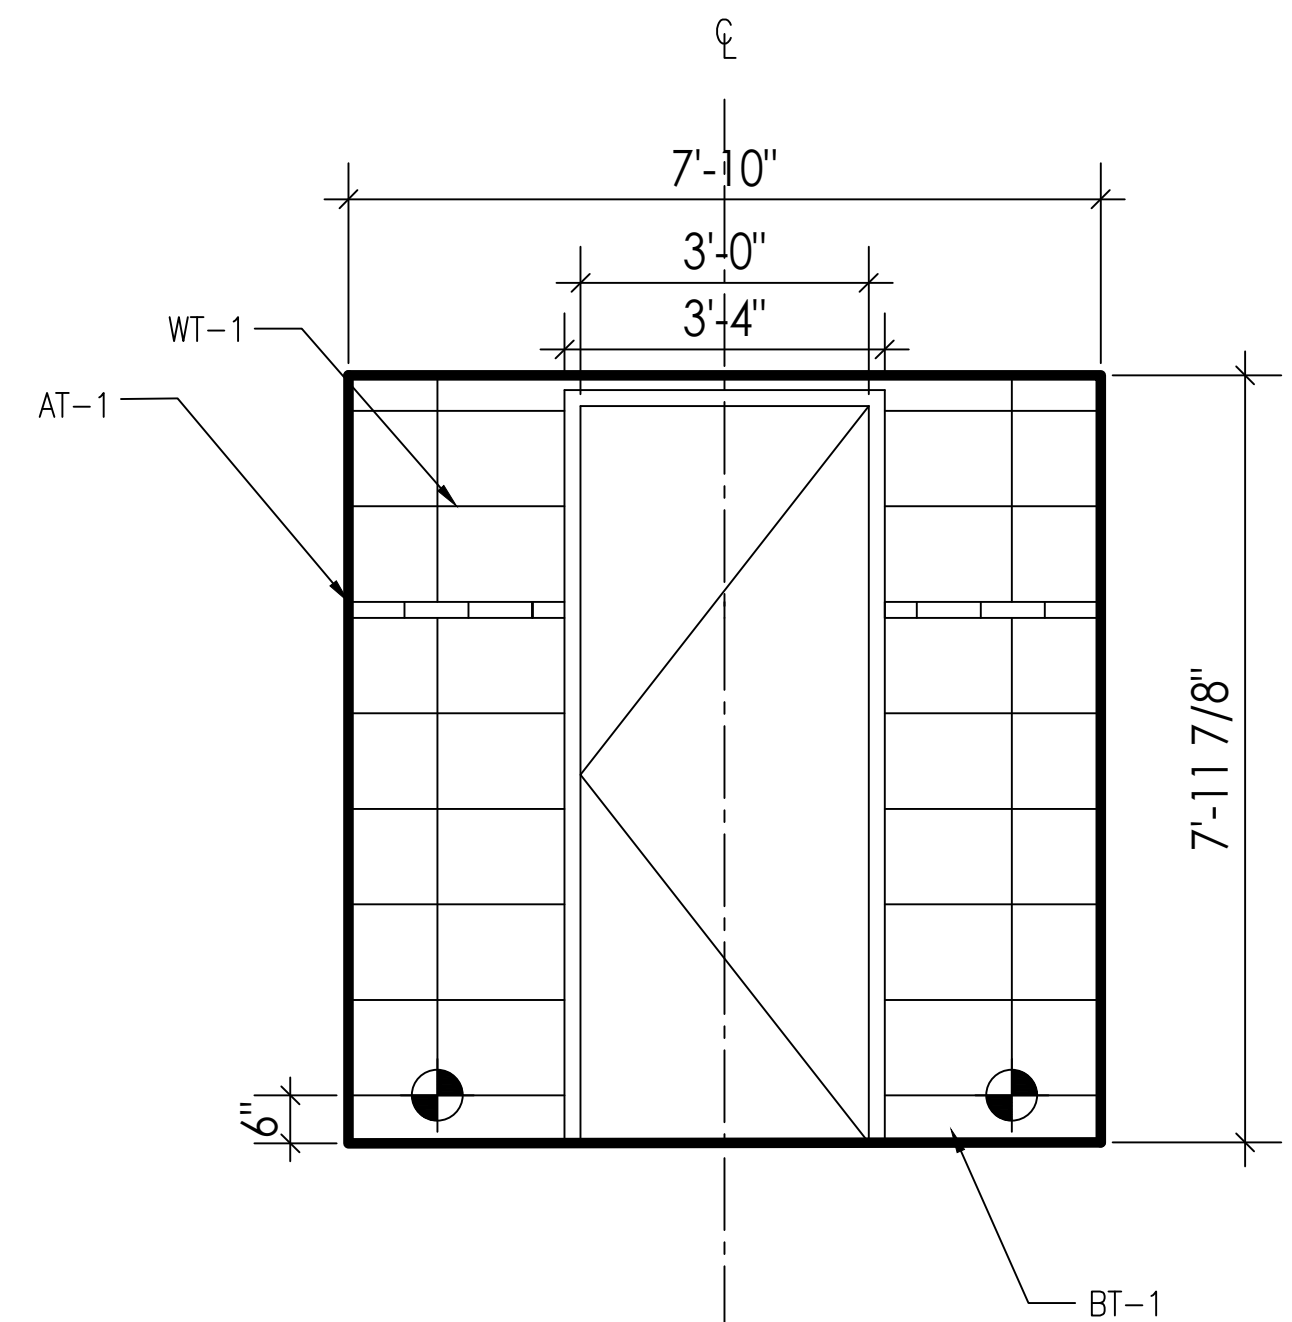

05
1/2"=1'-0" ELEVATIONS: 6TH FLOOR BATHROOMS

AUSTRO TILE & STONE, LLC
30-25 93RD STREET
EAST ELMHURST, NY 11369

CONTRACTOR:
JRM CONSTRUCTION
MANAGEMENT, LLC
242 WEST 36TH STREET
11TH FLOOR
NEW YORK, NY 10018

INTERIOR DESIGNER:

ISSUE FOR APPROVAL 10/09/23
ISSUE NAME DATE

ARCHITECT:

SPACESMITH
ONE NEW YORK PLAZA
NEW YORK, NY 10004
PH:212 260 5583

PROJECT NAME:

JACK RESNICK & SONS
255 GREENWICH STREET
NEW YORK, NY 10007

SHEET NAME:

ELEVATIONS
6TH FLOOR BATHROOMS

DATE:
PROJECT NO.:
PRINCIPAL:
DRAWING BY:
CHECKED BY:
SCALE:
DWG. No.:
T-102





STARTING POINT


(BT-1) TILE BASE GROUT JOINTS WILL NOT ALIGN WITH (WT-1) WALL TILE GROUT JOINTS

(AT-1) ACCENT WALL TILE GROUT JOINTS WILL NOT ALIGN WITH (WT-1) WALL TILE GROUT JOINTS

AUSTRO TILE & STONE, LLC
30-25 93RD STREET
EAST ELMHURST, NY 11369

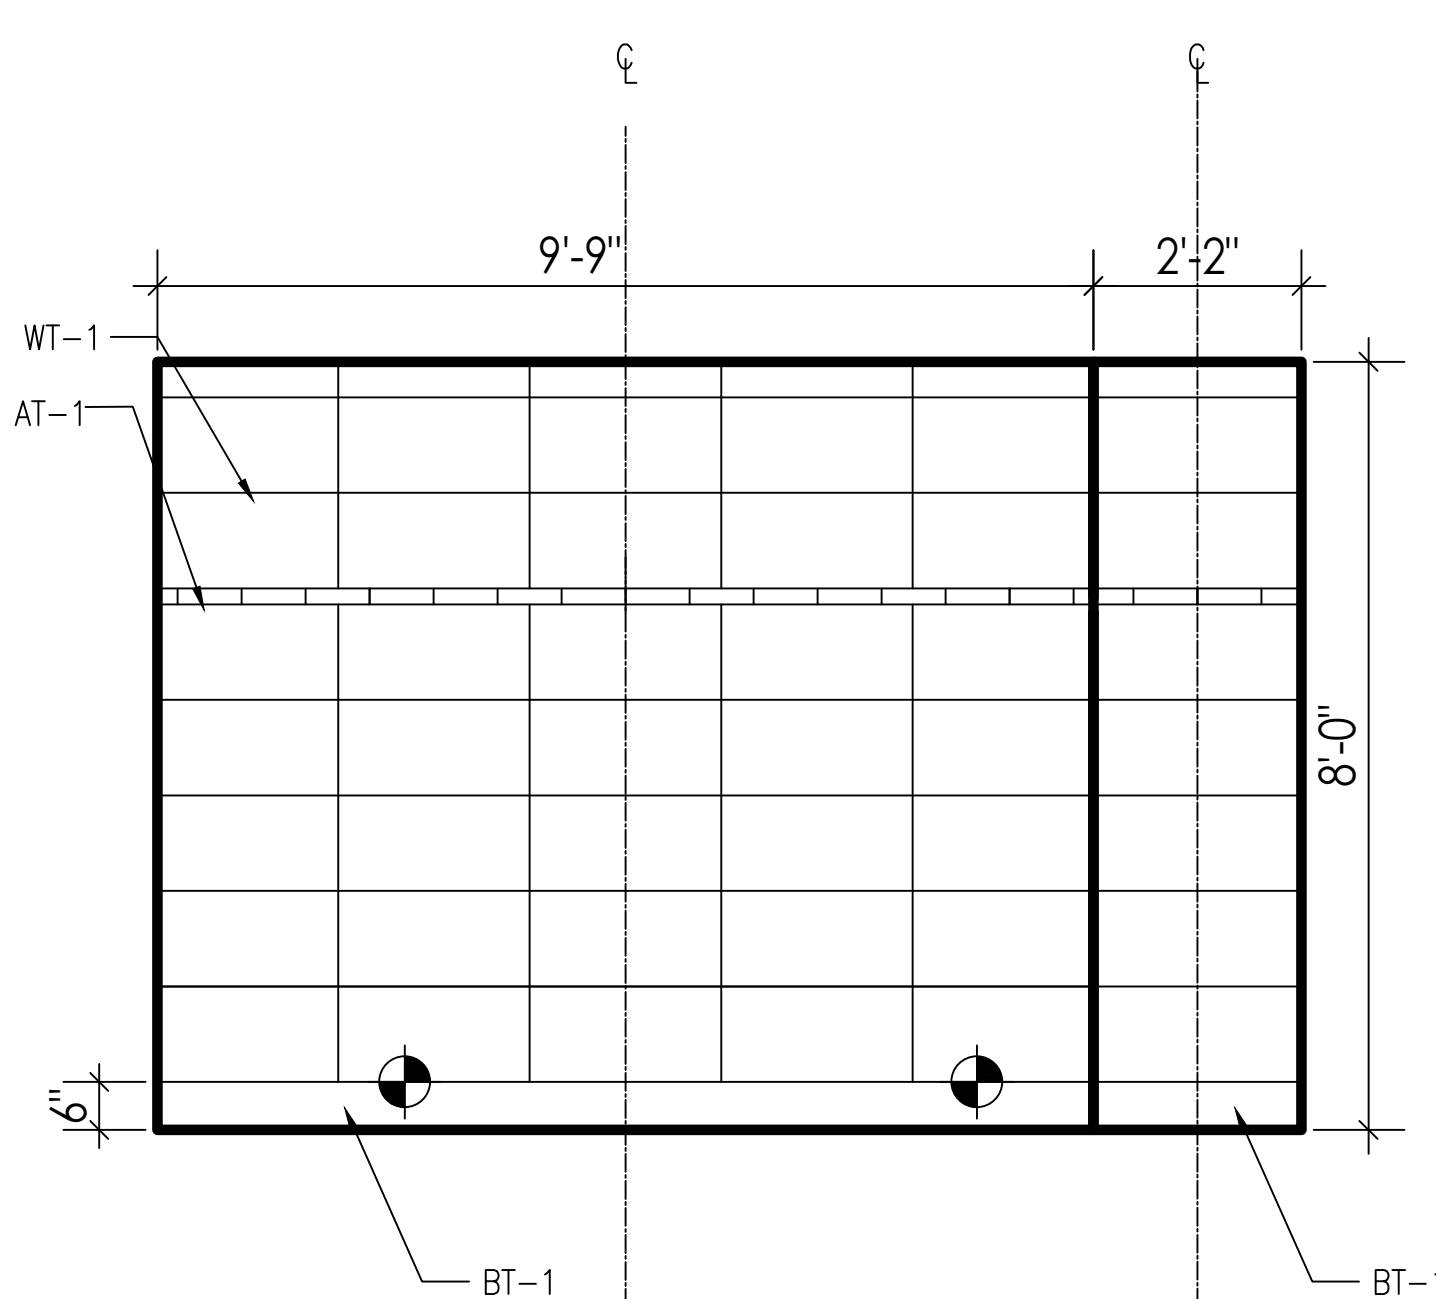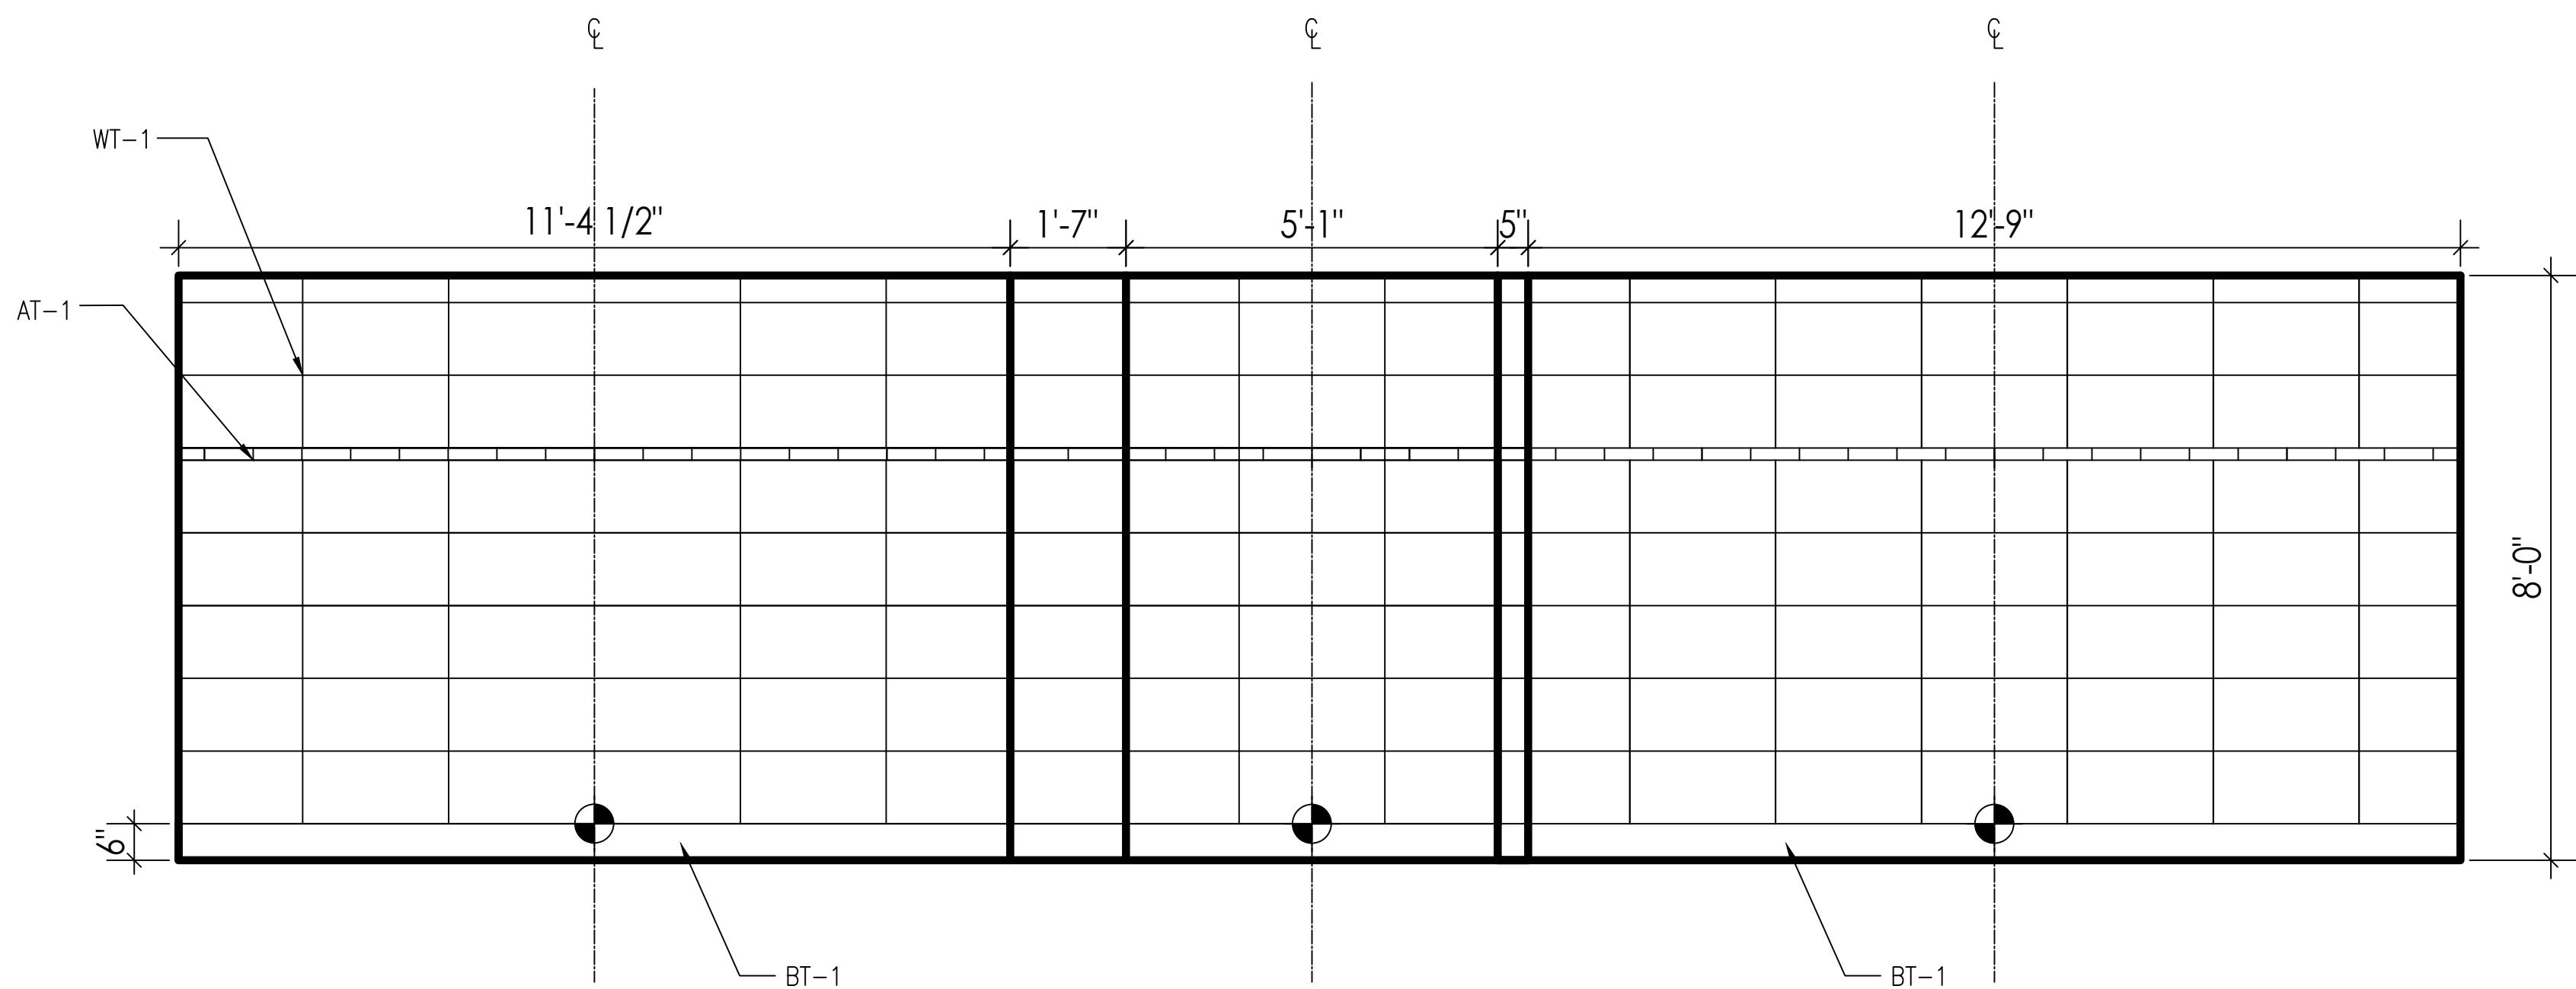


02
1/2"=1'-0" ELEVATIONS: 6TH FLOOR BATHROOMS

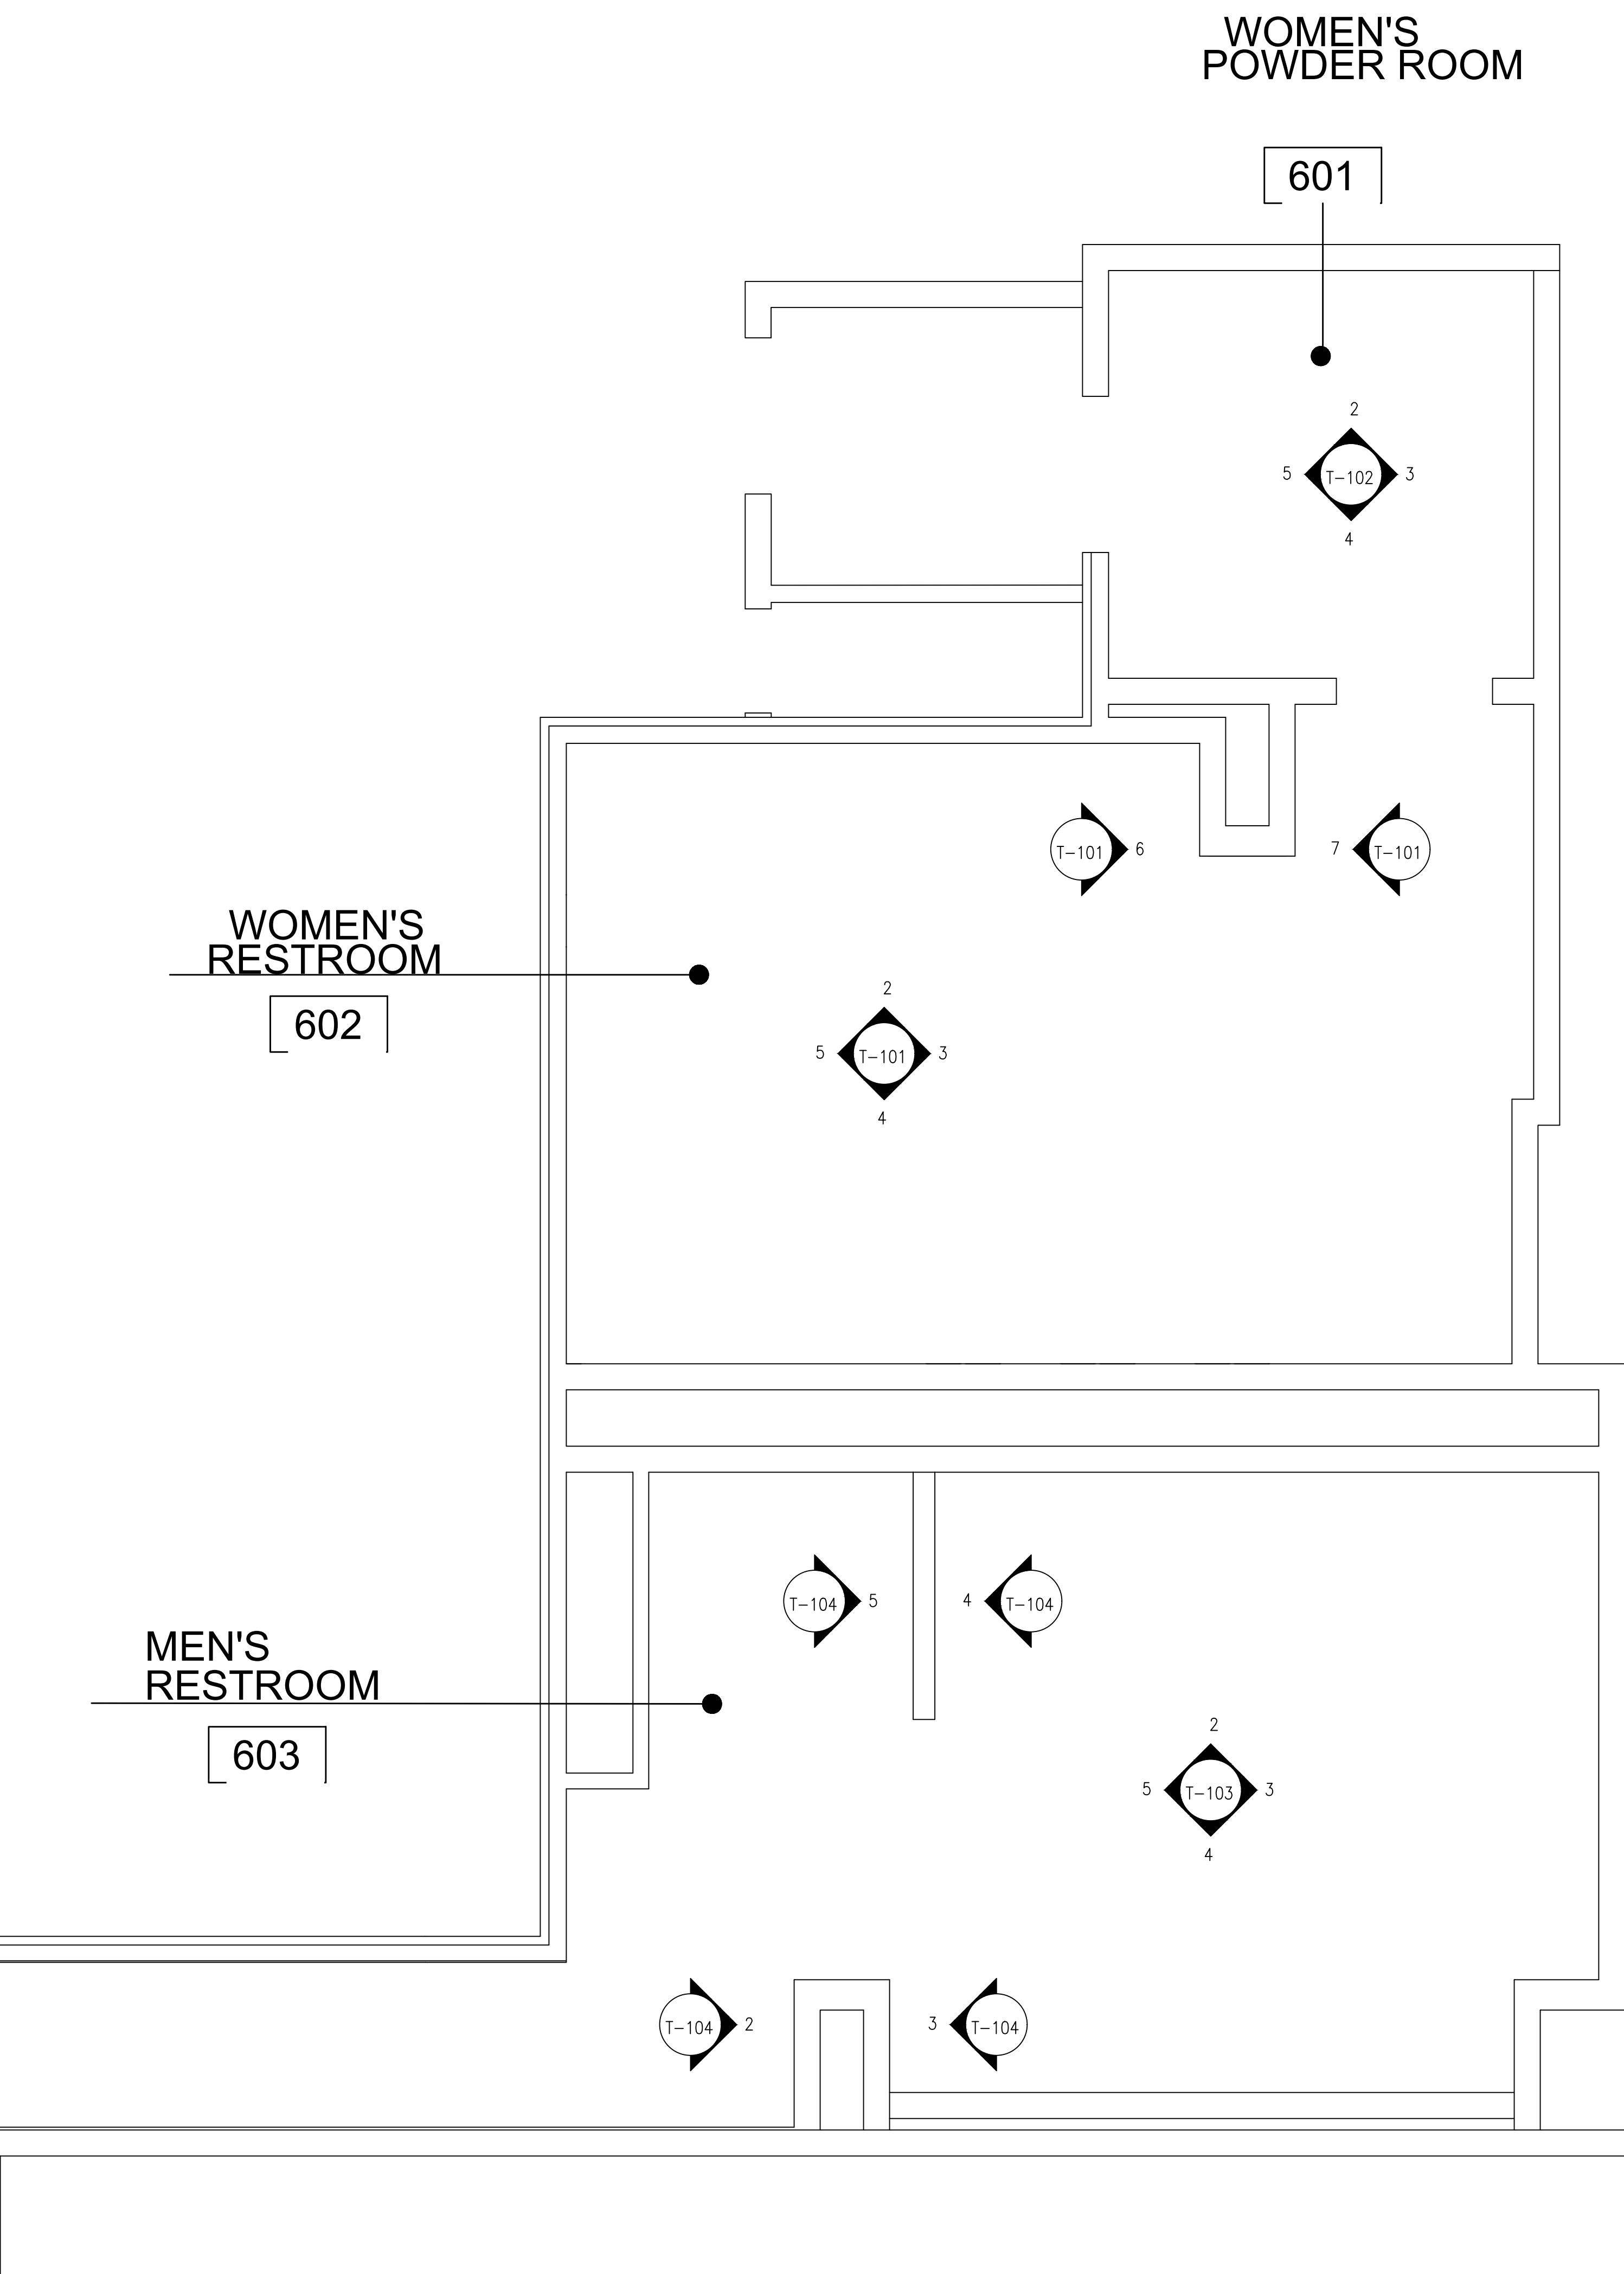


01
1/2"=1'-0" PLAN #2: 6TH FLOOR BATHROOMS

03
1/2"=1'-0" ELEVATIONS: 6TH FLOOR BATHROOMS

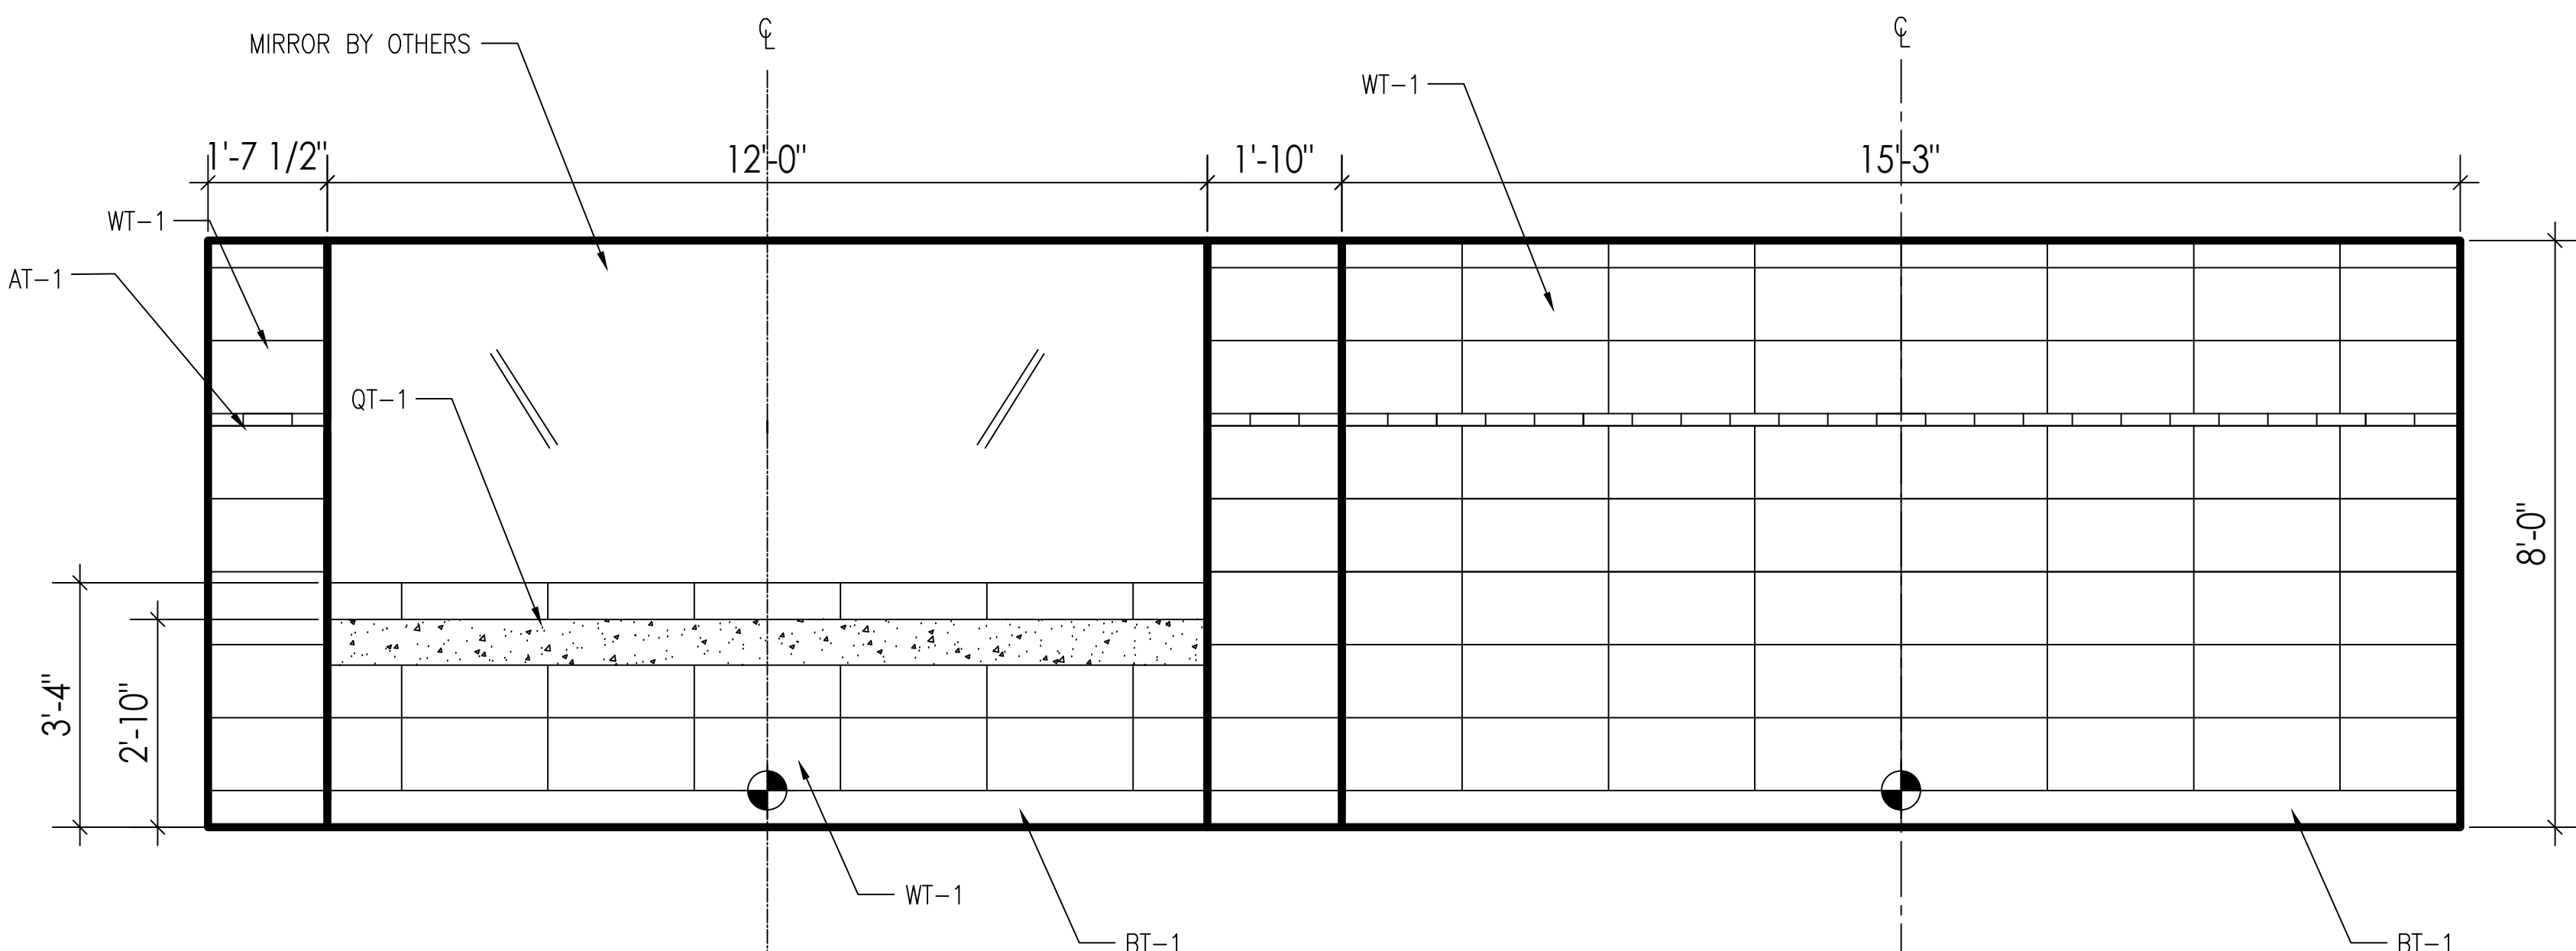

04
1/2"=1'-0" ELEVATIONS: 6TH FLOOR BATHROOMS

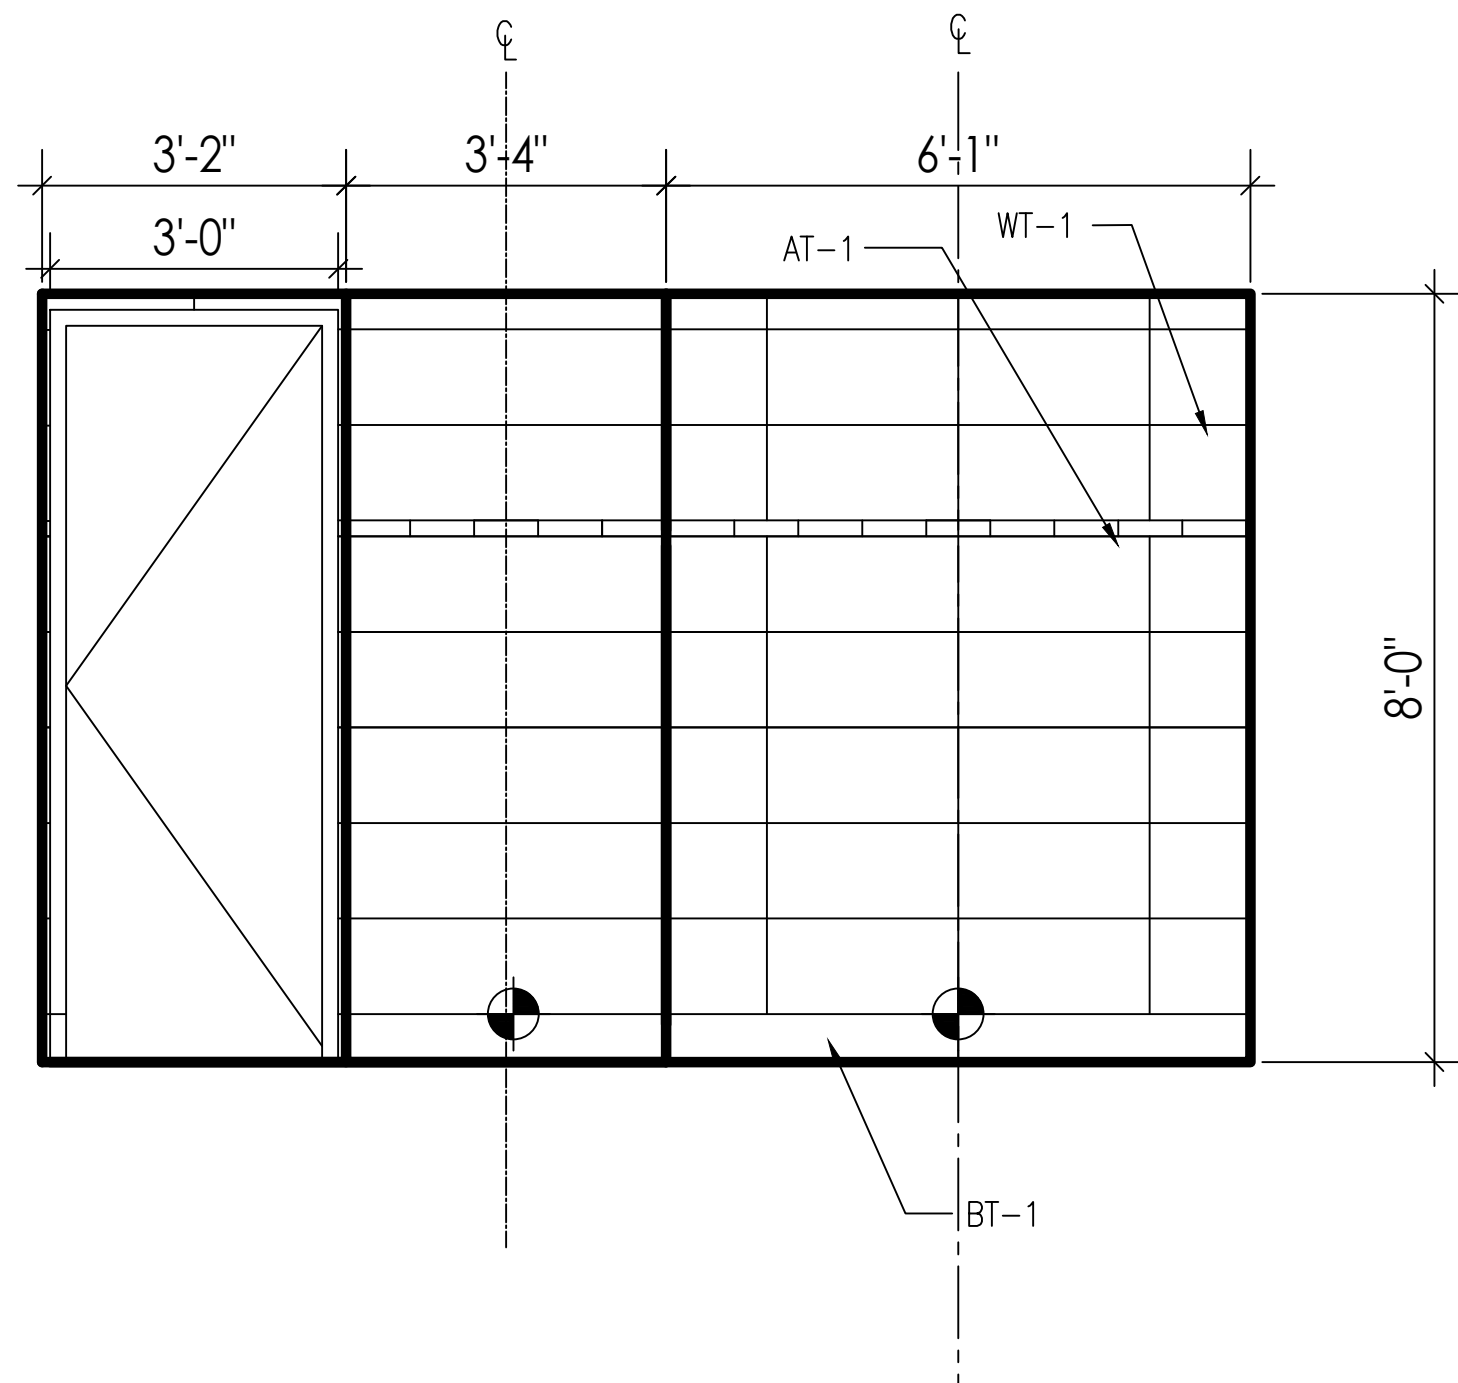

05
1/2"=1'-0" ELEVATIONS: 6TH FLOOR BATHROOMS

CONTRACTOR:
JRM CONSTRUCTION
MANAGEMENT, LLC
242 WEST 36TH STREET
11TH FLOOR
NEW YORK, NY 10018

INTERIOR DESIGNER:

ISSUE FOR APPROVAL 10/09/23

ISSUE NAME DATE

ARCHITECT:

SPACESMITH
ONE NEW YORK PLAZA
NEW YORK, NY 10004
PH:212 260 5583

PROJECT NAME:

JACK RESNICK & SONS
255 GREENWICH STREET
NEW YORK, NY 10007

SHEET NAME:

ELEVATIONS
6TH FLOOR BATHROOMS

DATE:
PROJECT NO.:
PRINCIPAL:
DRAWING BY:
CHECKED BY:
SCALE:
DWG. No.:
T-103


5 of 29




STARTING POINT

(BT-1) TILE BASE GROUT JOINTS WILL NOT ALIGN WITH (WT-1) WALL TILE GROUT JOINTS


(AT-1) ACCENT WALL TILE GROUT JOINTS WILL NOT ALIGN WITH (WT-1) WALL TILE GROUT JOINTS

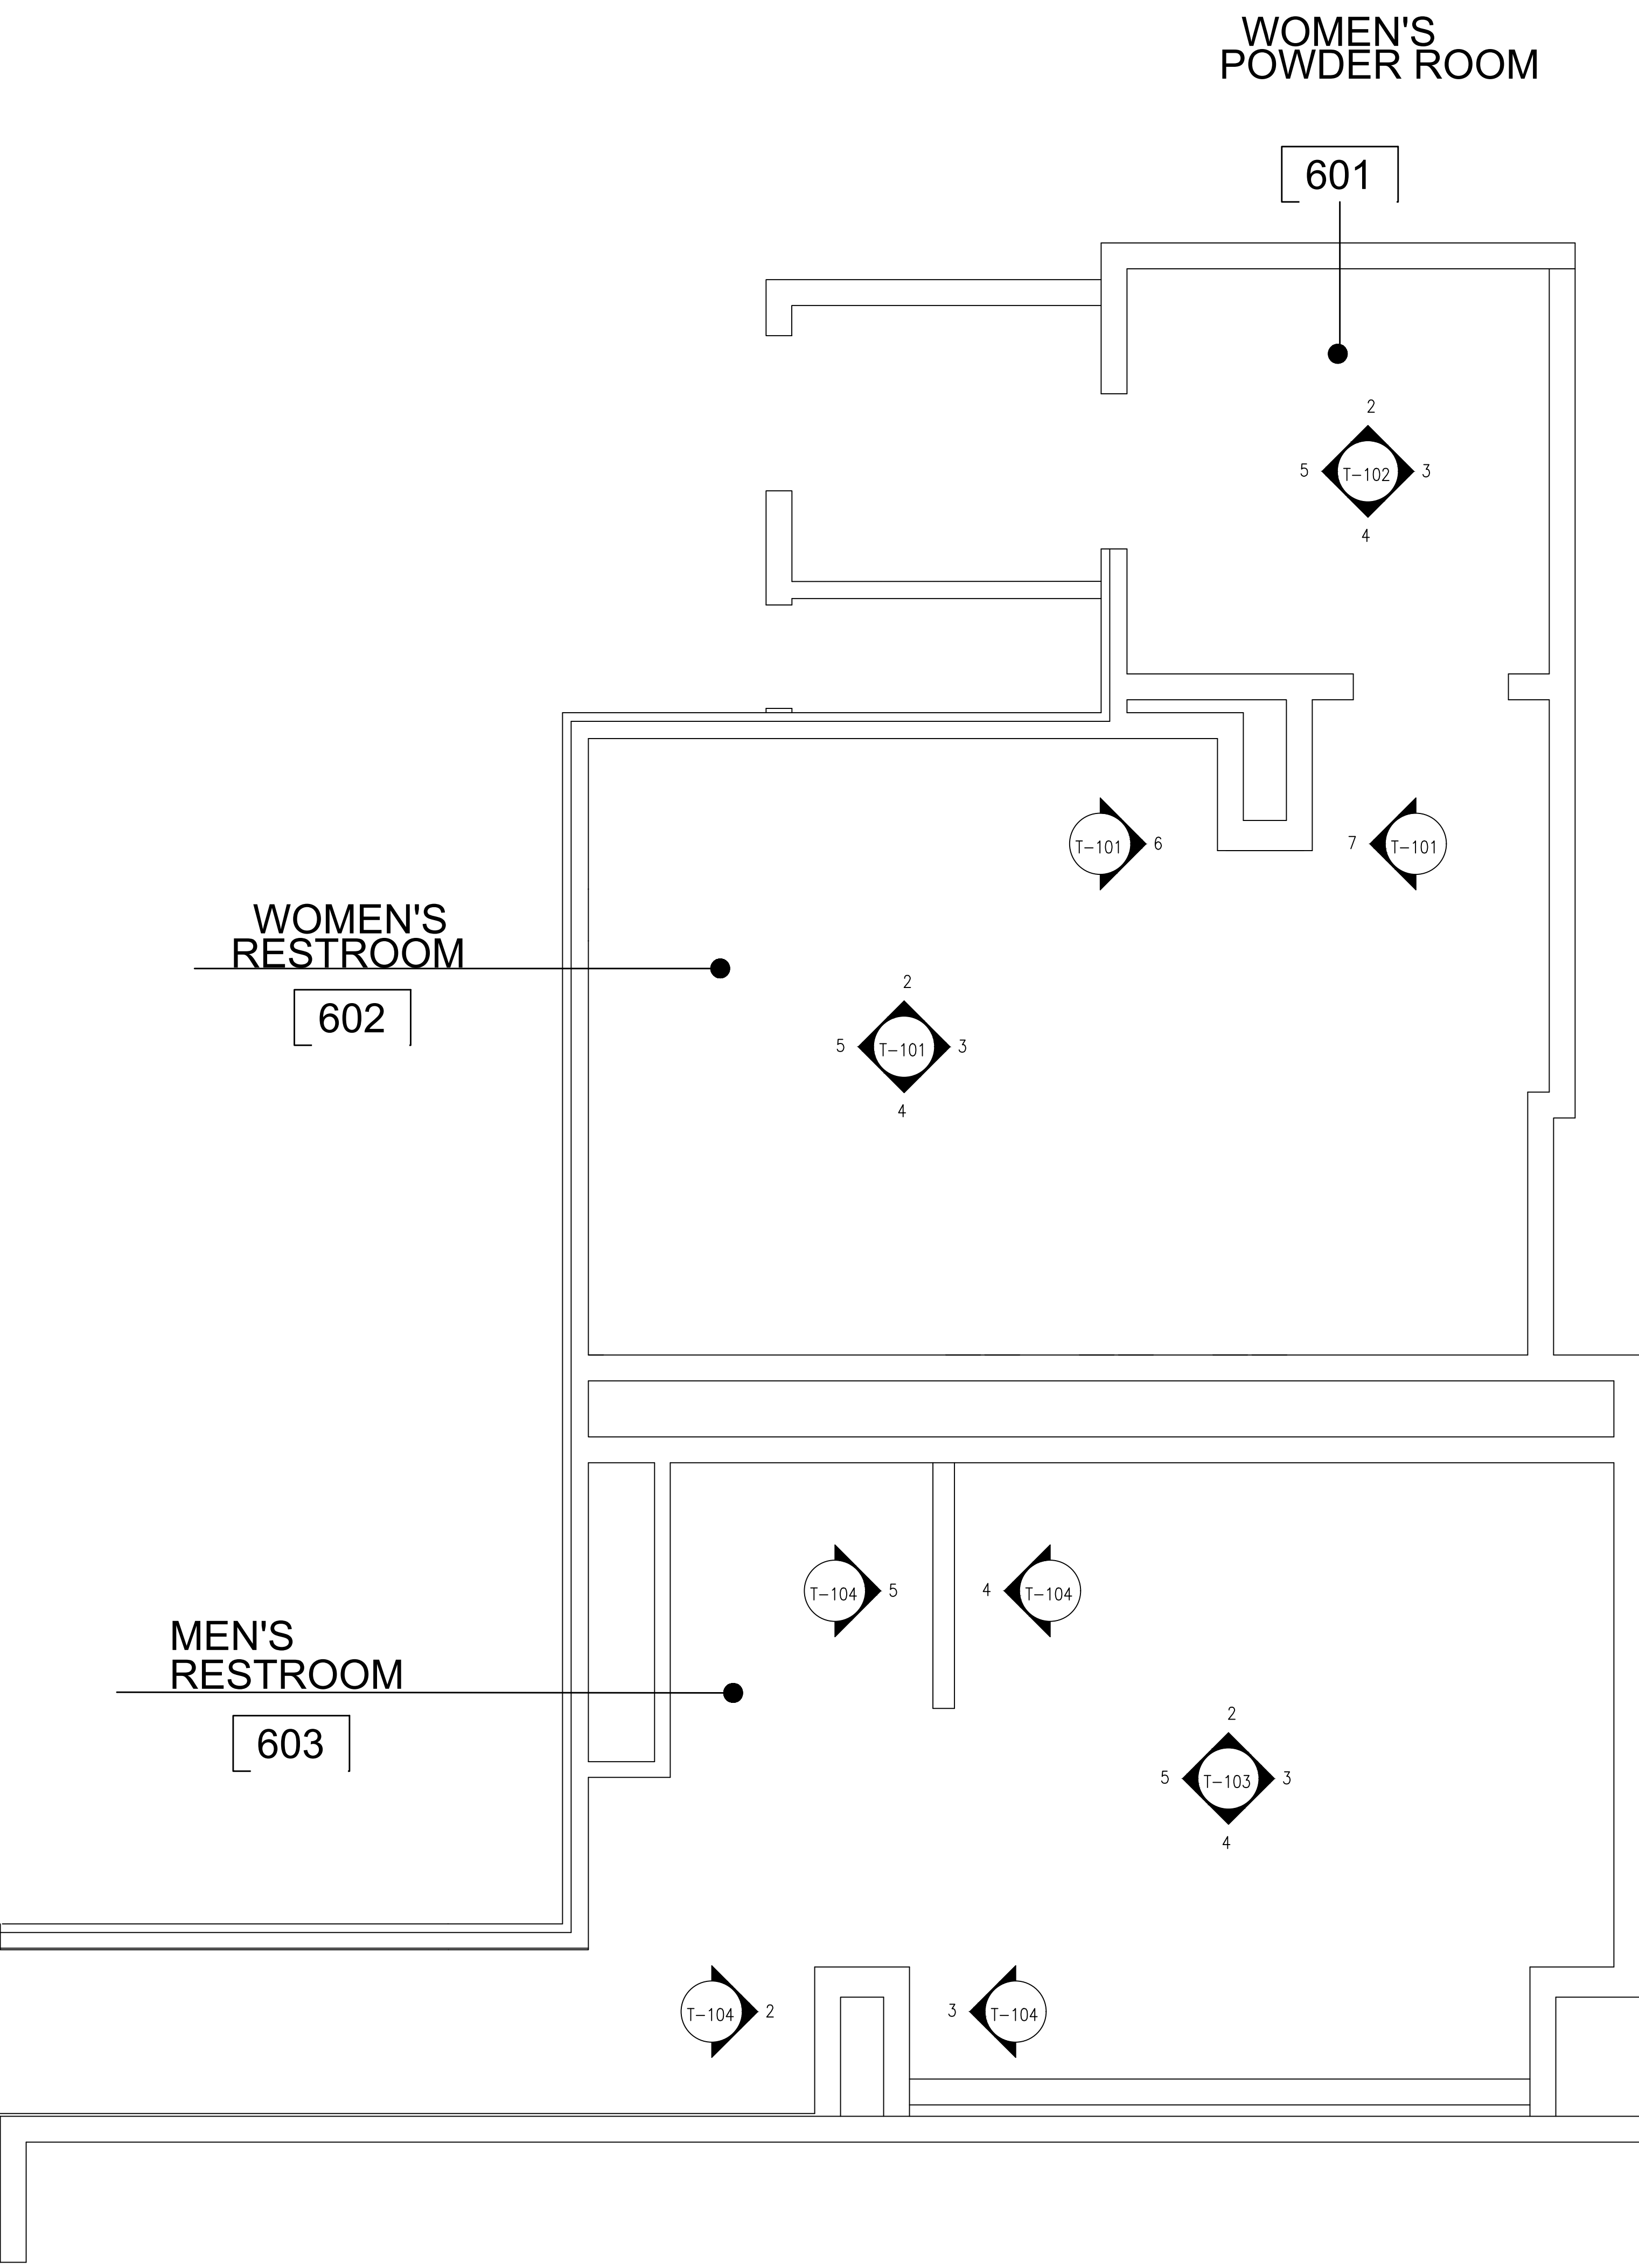


01
1/2"=1'-0" PLAN: 6TH FLOOR SINGLE BATHROOM

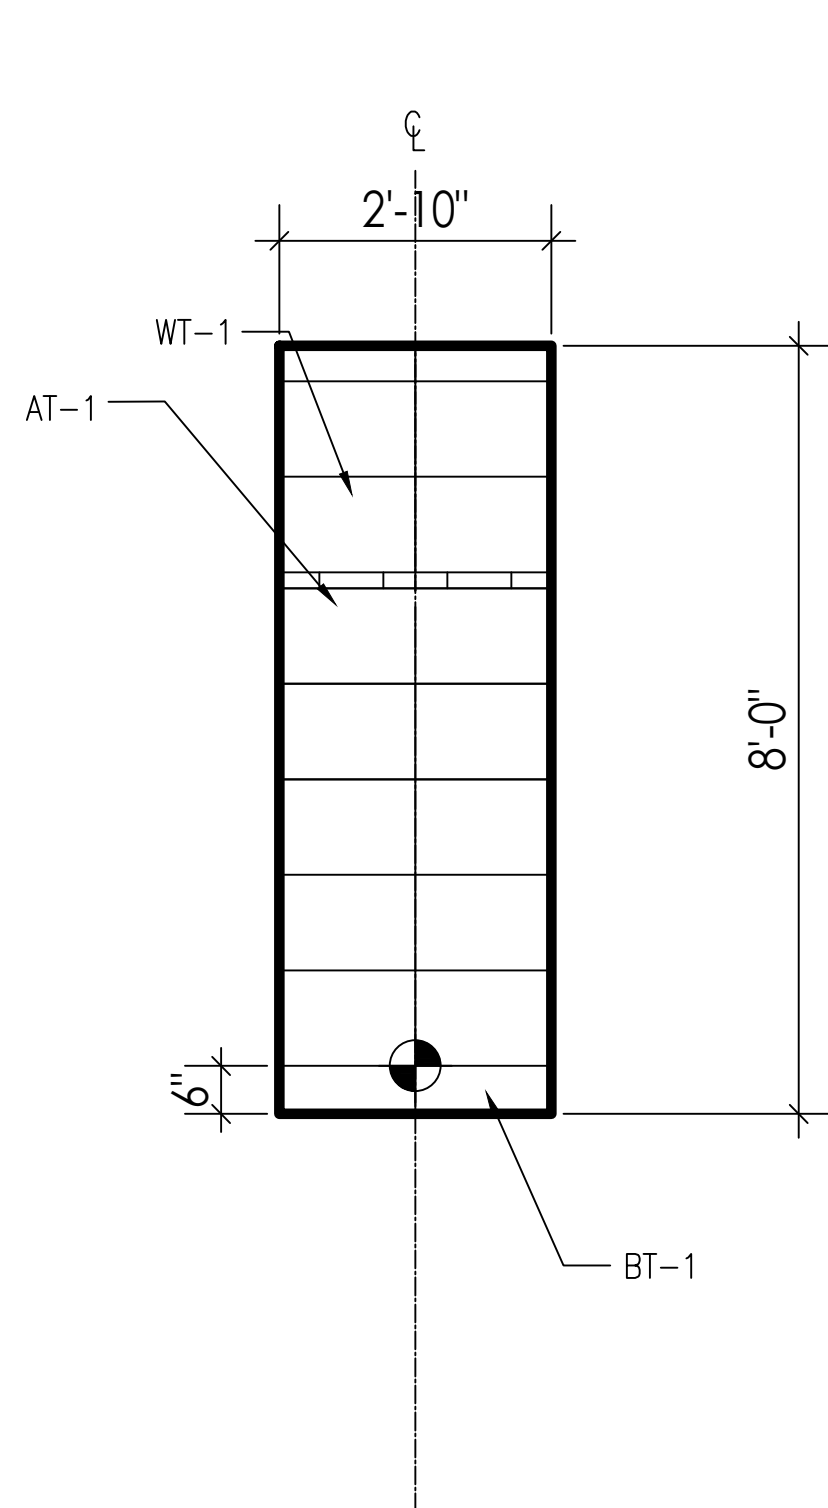


02
1/2"=1'-0" ELEVATIONS: 6TH FLOOR BATHROOMS

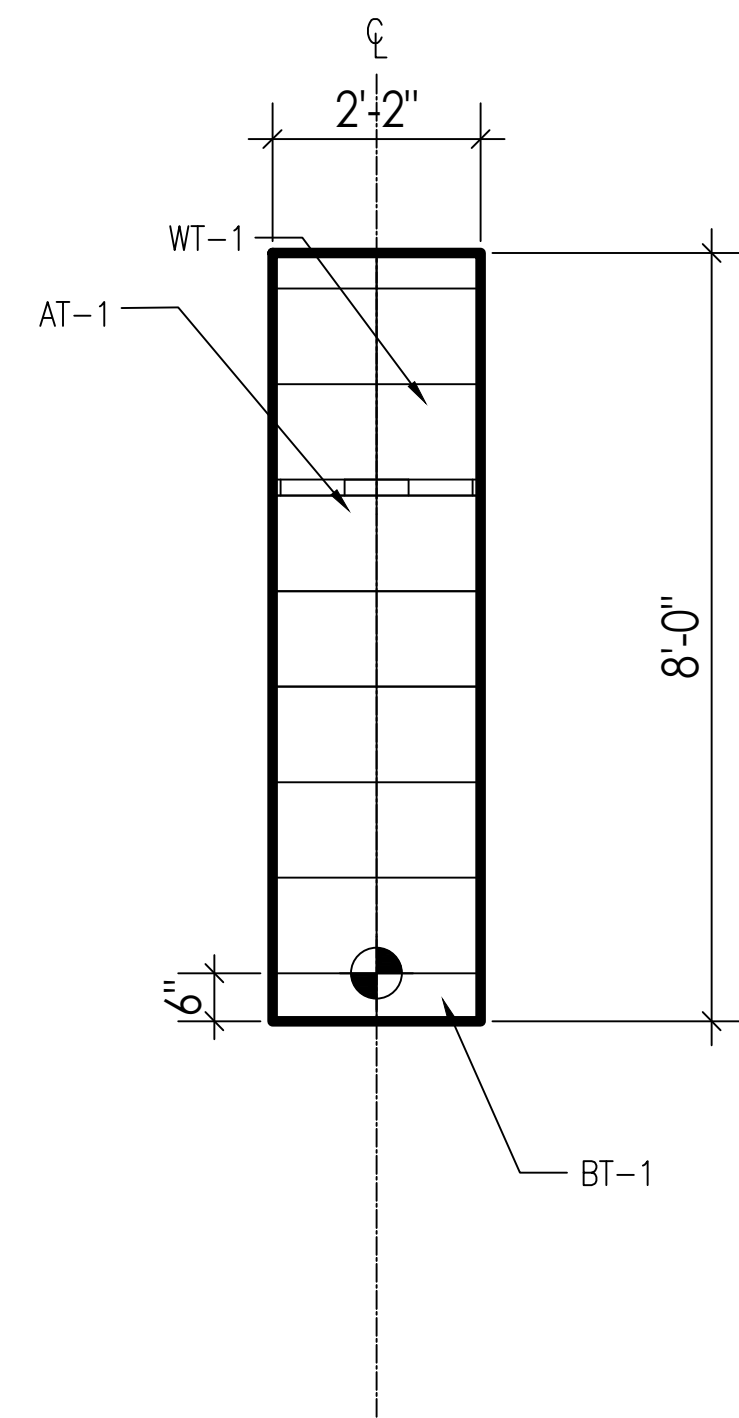

03
1/2"=1'-0" ELEVATIONS: 6TH FLOOR BATHROOMS

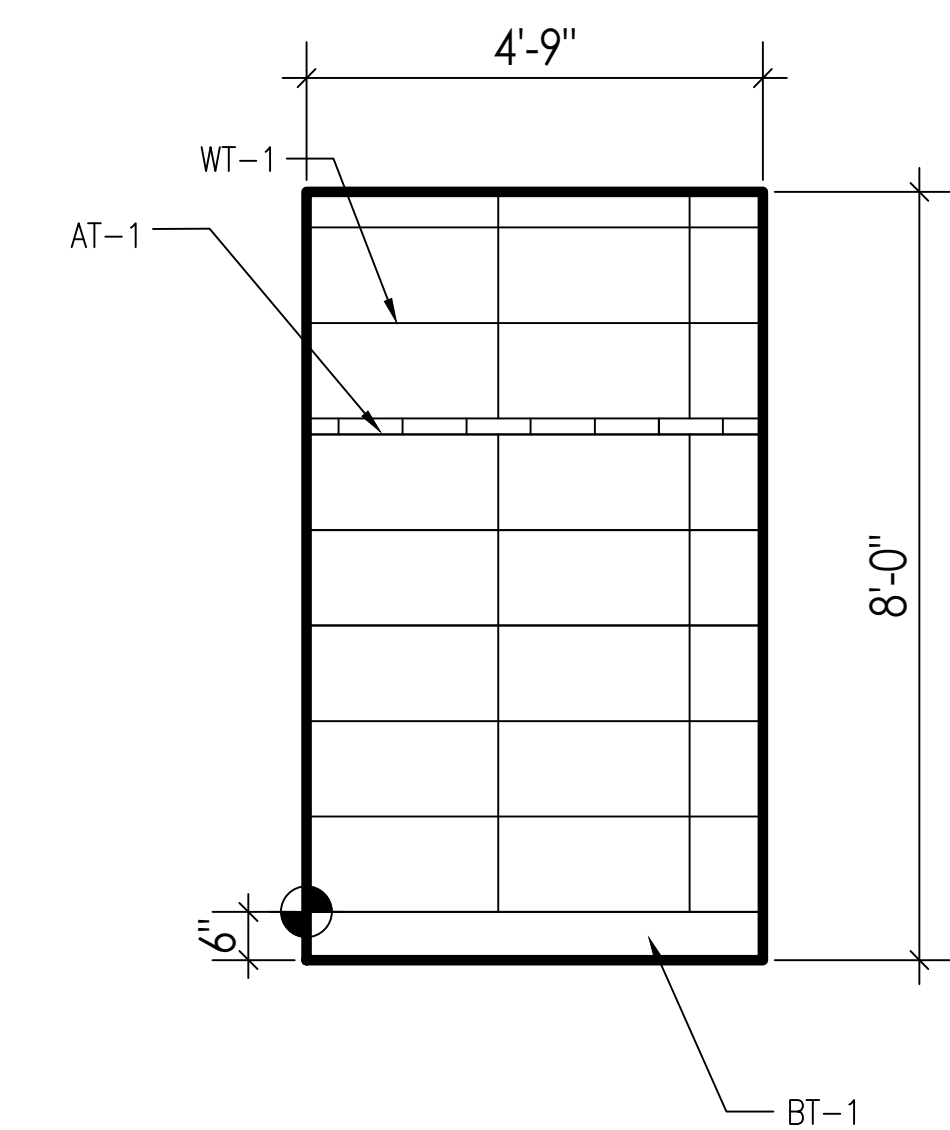

04
1/2"=1'-0" ELEVATIONS: 6TH FLOOR BATHROOMS

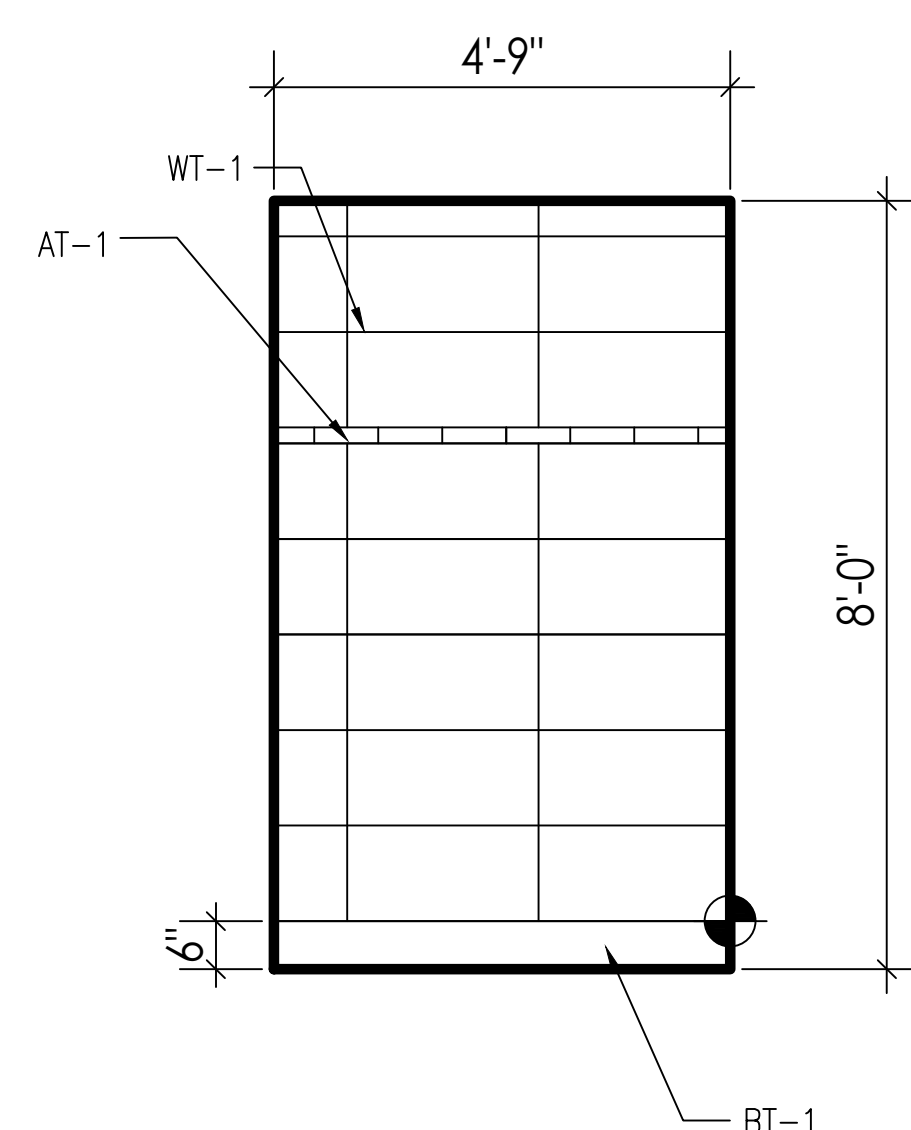

05
1/2"=1'-0" ELEVATIONS: 6TH FLOOR BATHROOMS

AUSTRO TILE & STONE, LLC
30-25 93RD STREET
EAST ELMHURST, NY 11369

CONTRACTOR:
JRM CONSTRUCTION
MANAGEMENT, LLC
242 WEST 36TH STREET
11TH FLOOR
NEW YORK, NY 10018

INTERIOR DESIGNER:

ISSUE FOR APPROVAL 10/09/23
ISSUE NAME DATE

ARCHITECT:
SPACESMITH
ONE NEW YORK PLAZA
NEW YORK, NY 10004
PH:212 260 5583

PROJECT NAME:
JACK RESNICK & SONS
255 GREENWICH STREET
NEW YORK, NY 10007

SHEET NAME:
ELEVATIONS
6TH FLOOR BATHROOMS

DATE:
PROJECT NO.:
PRINCIPAL:
DRAWING BY:
CHECKED BY:
SCALE:
DWG. No.:
T-104
6 of 29





STARTING POINT

(BT-1) TILE BASE GROUT JOINTS WILL NOT ALIGN WITH (WT-1) WALL TILE GROUT JOINTS



(AT-1) ACCENT WALL TILE GROUT JOINTS WILL NOT ALIGN WITH (WT-1) WALL TILE GROUT JOINTS

AUSTRO TILE & STONE, LLC
30-25 93RD STREET
EAST ELMHURST, NY 11369

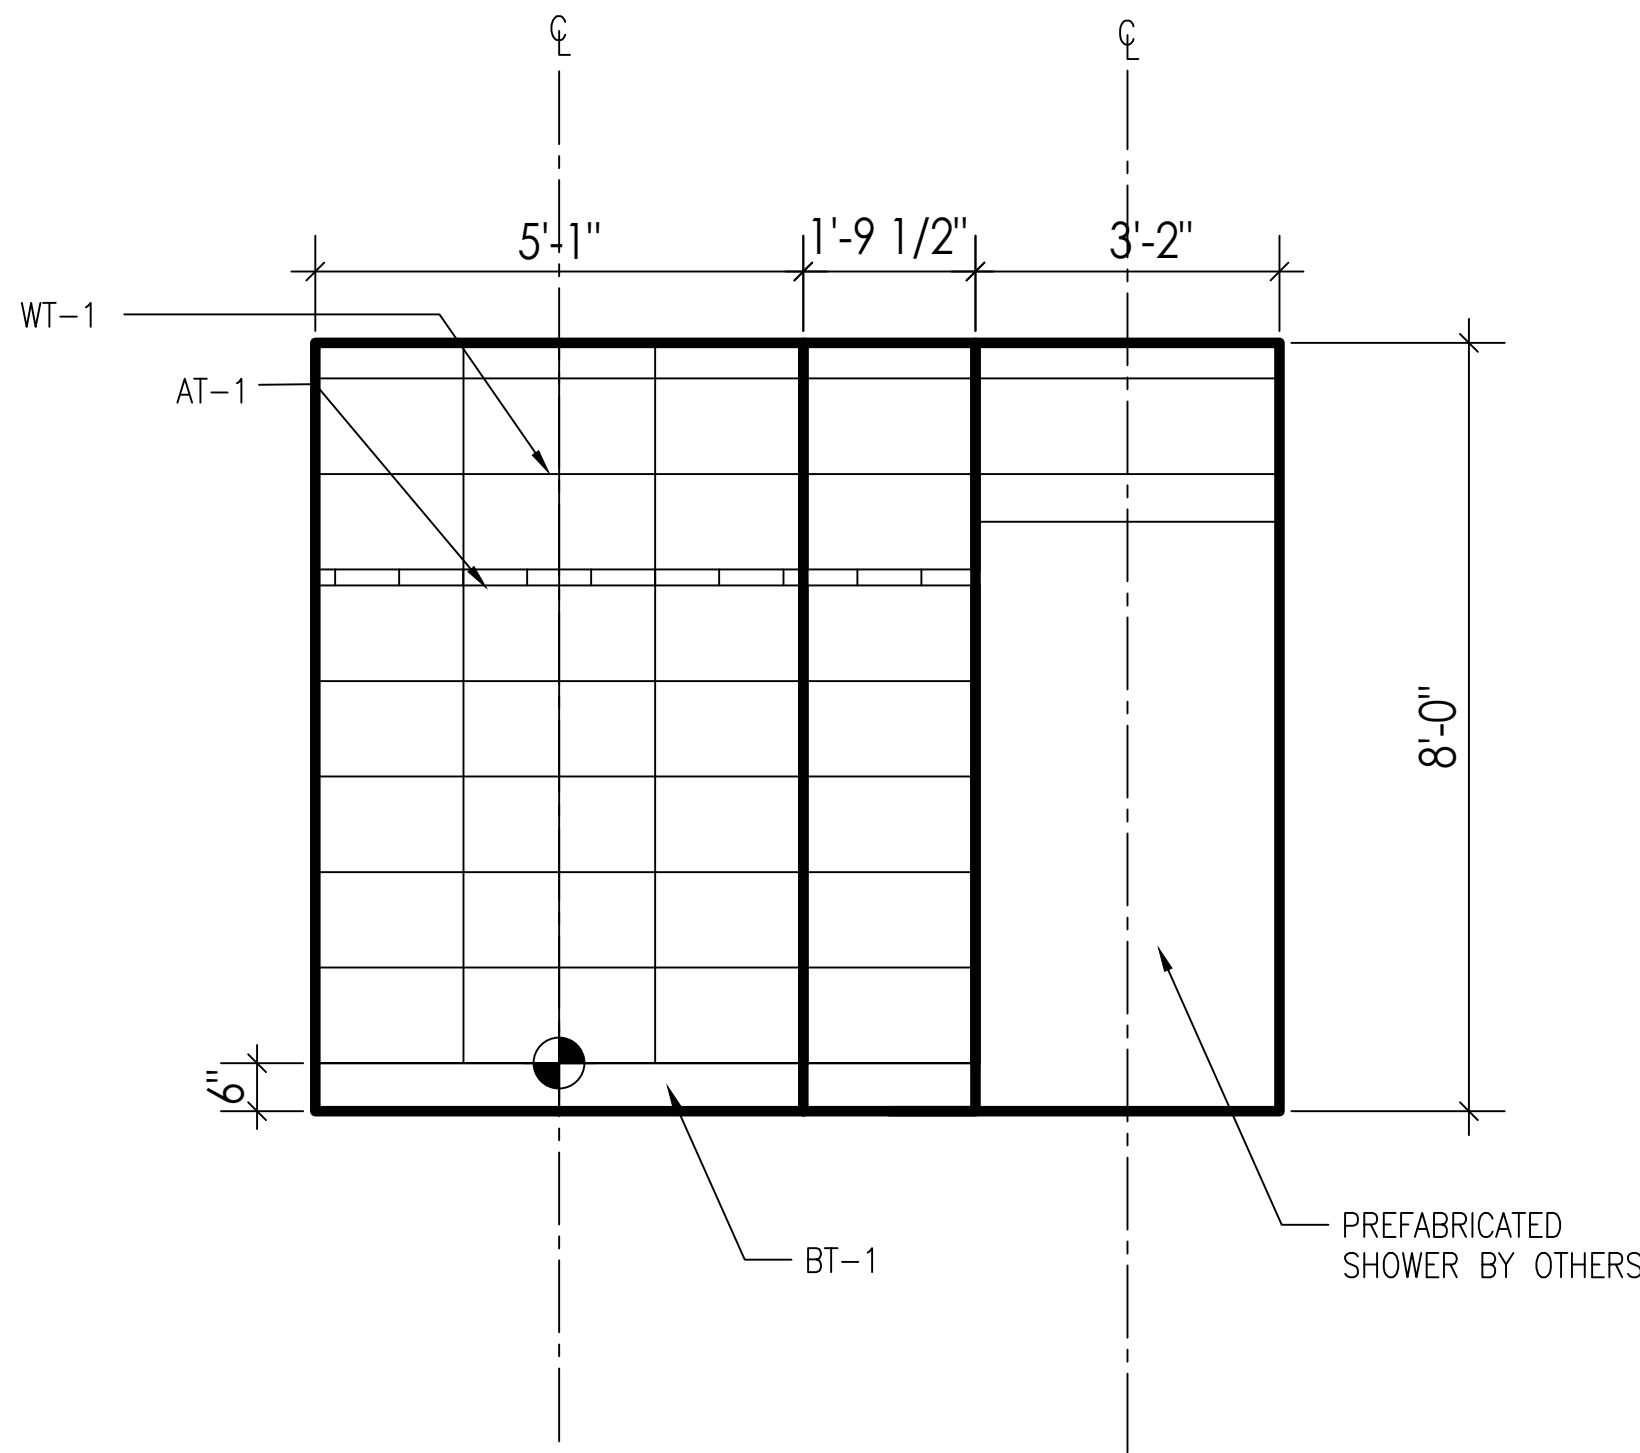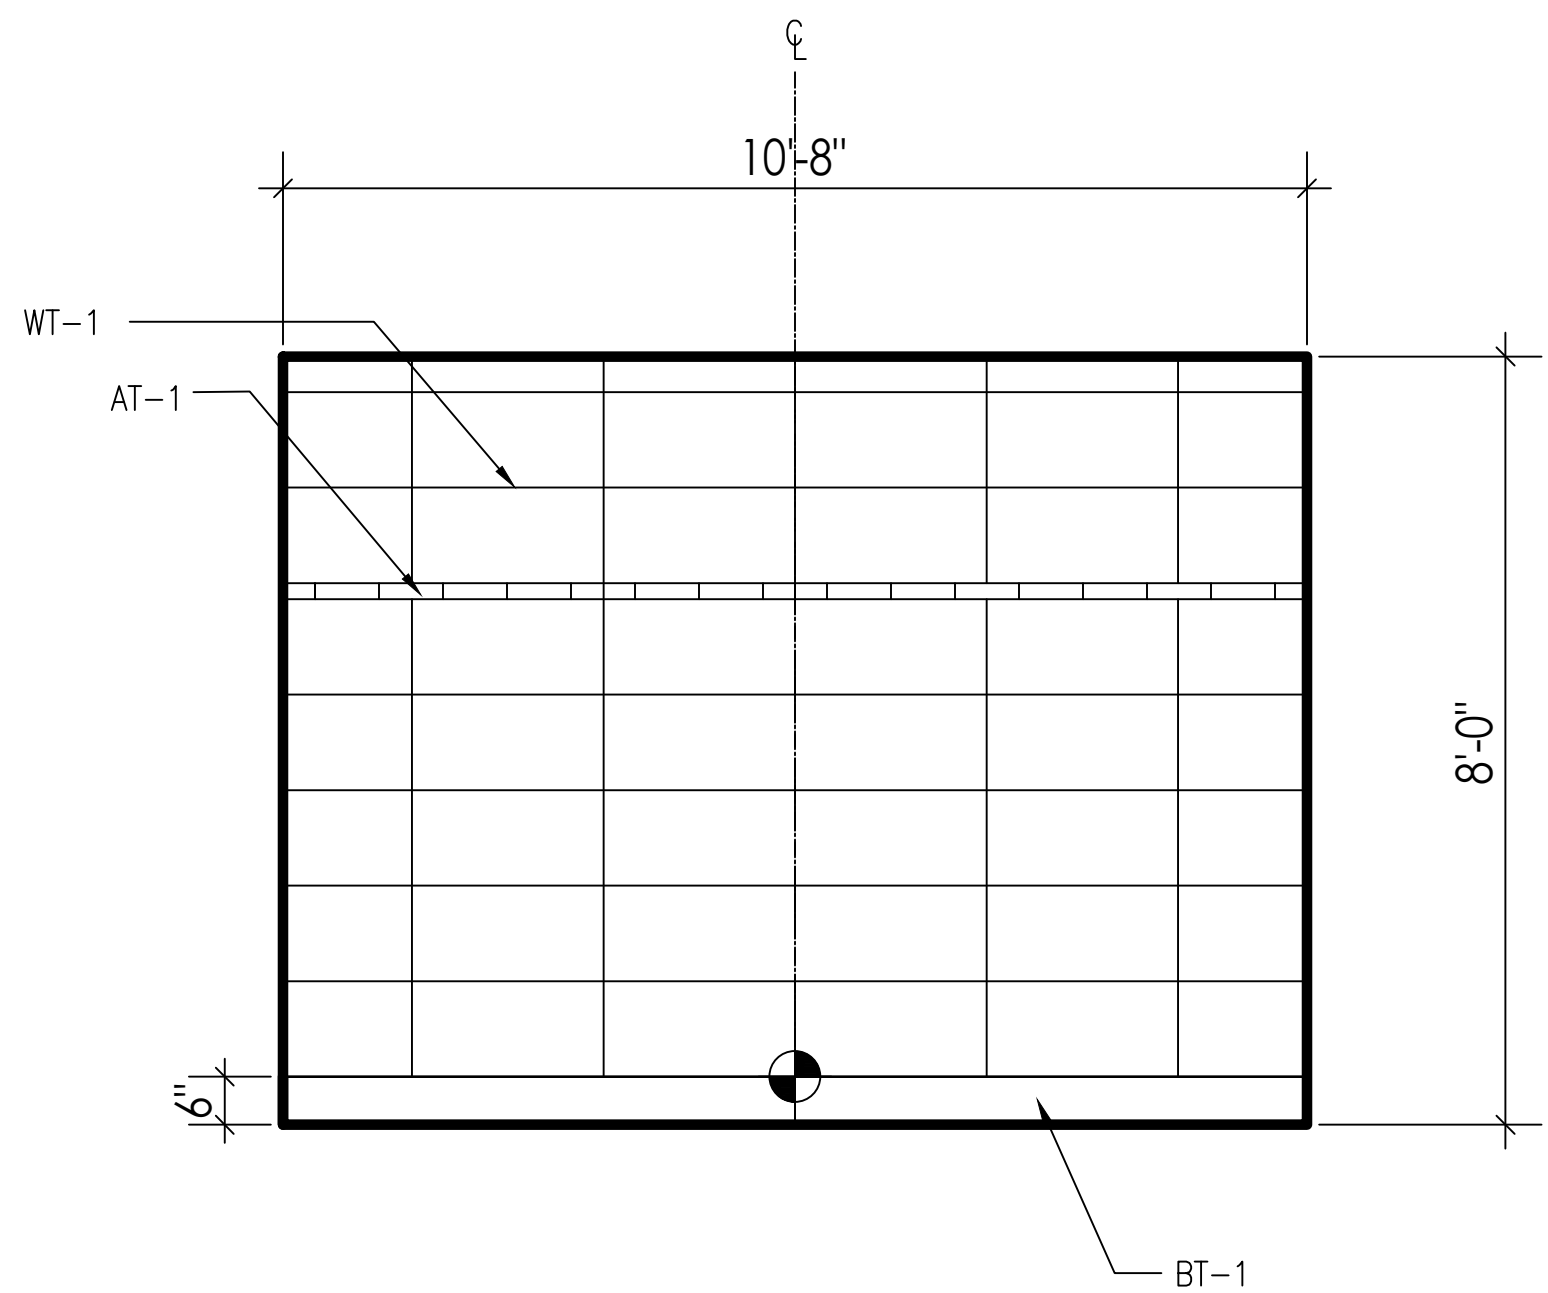



02
1/2"=1'-0" ELEVATIONS: 6TH FLOOR BATHROOMS

03
1/2"=1'-0" ELEVATIONS: 6TH FLOOR BATHROOMS

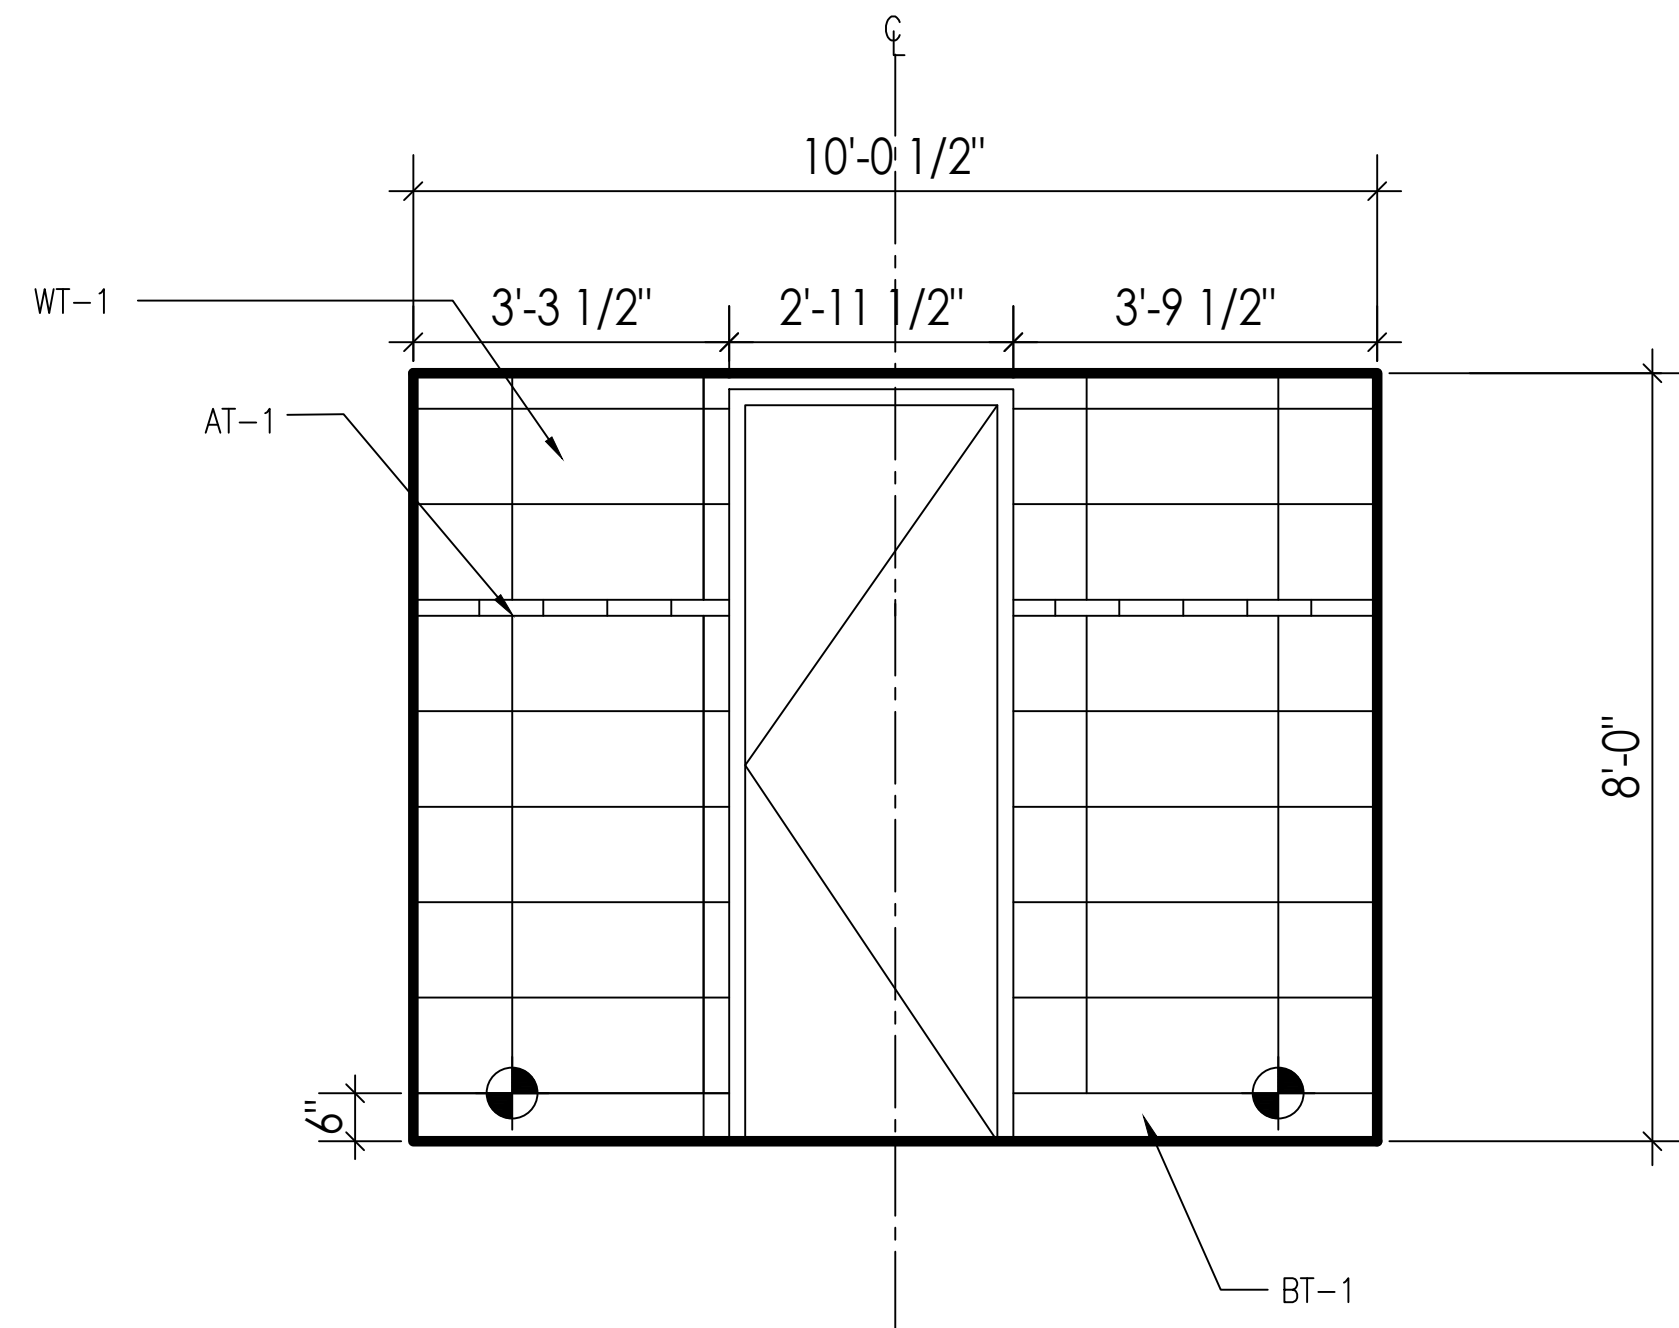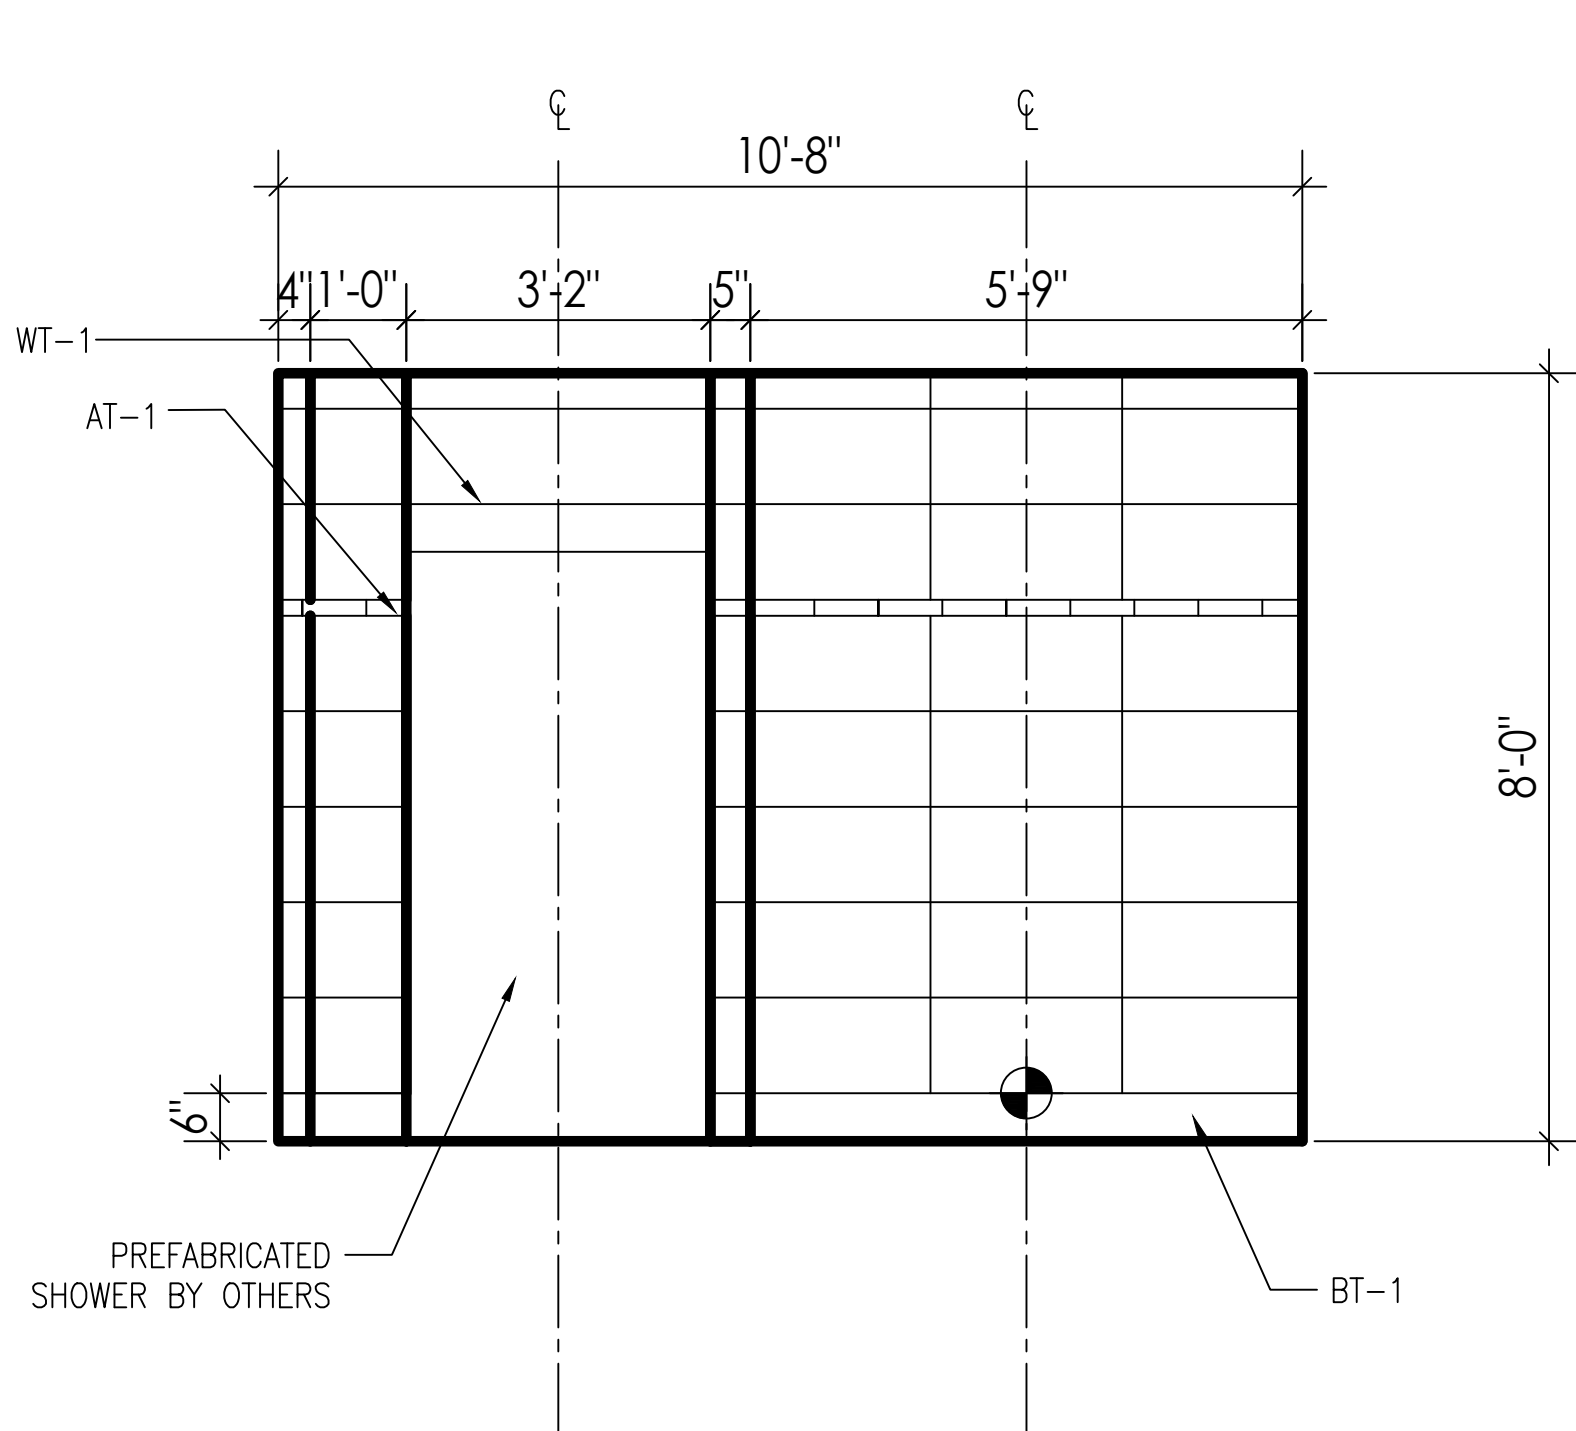


04
1/2"=1'-0" ELEVATIONS: 6TH FLOOR BATHROOMS

05
1/2"=1'-0" ELEVATIONS: 6TH FLOOR BATHROOMS

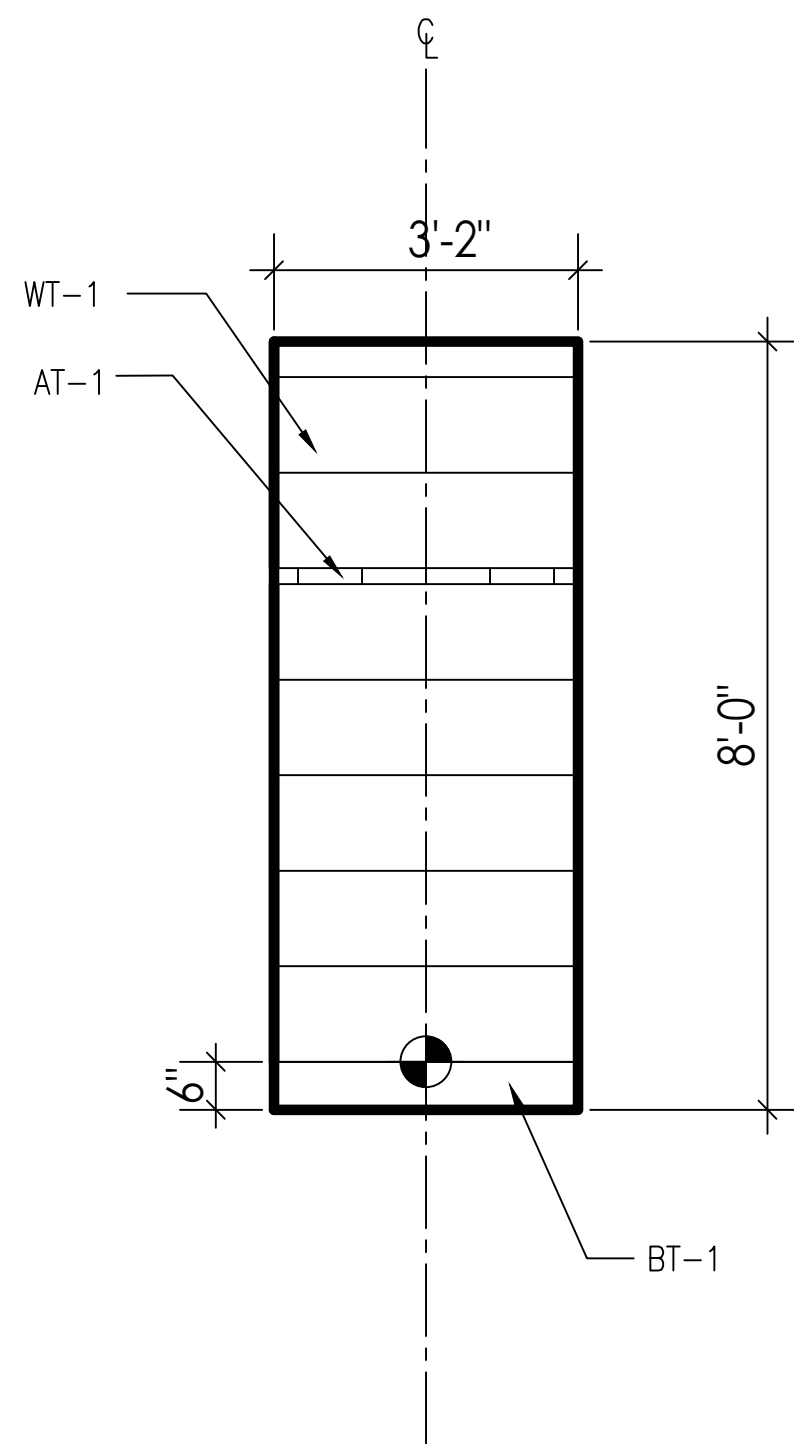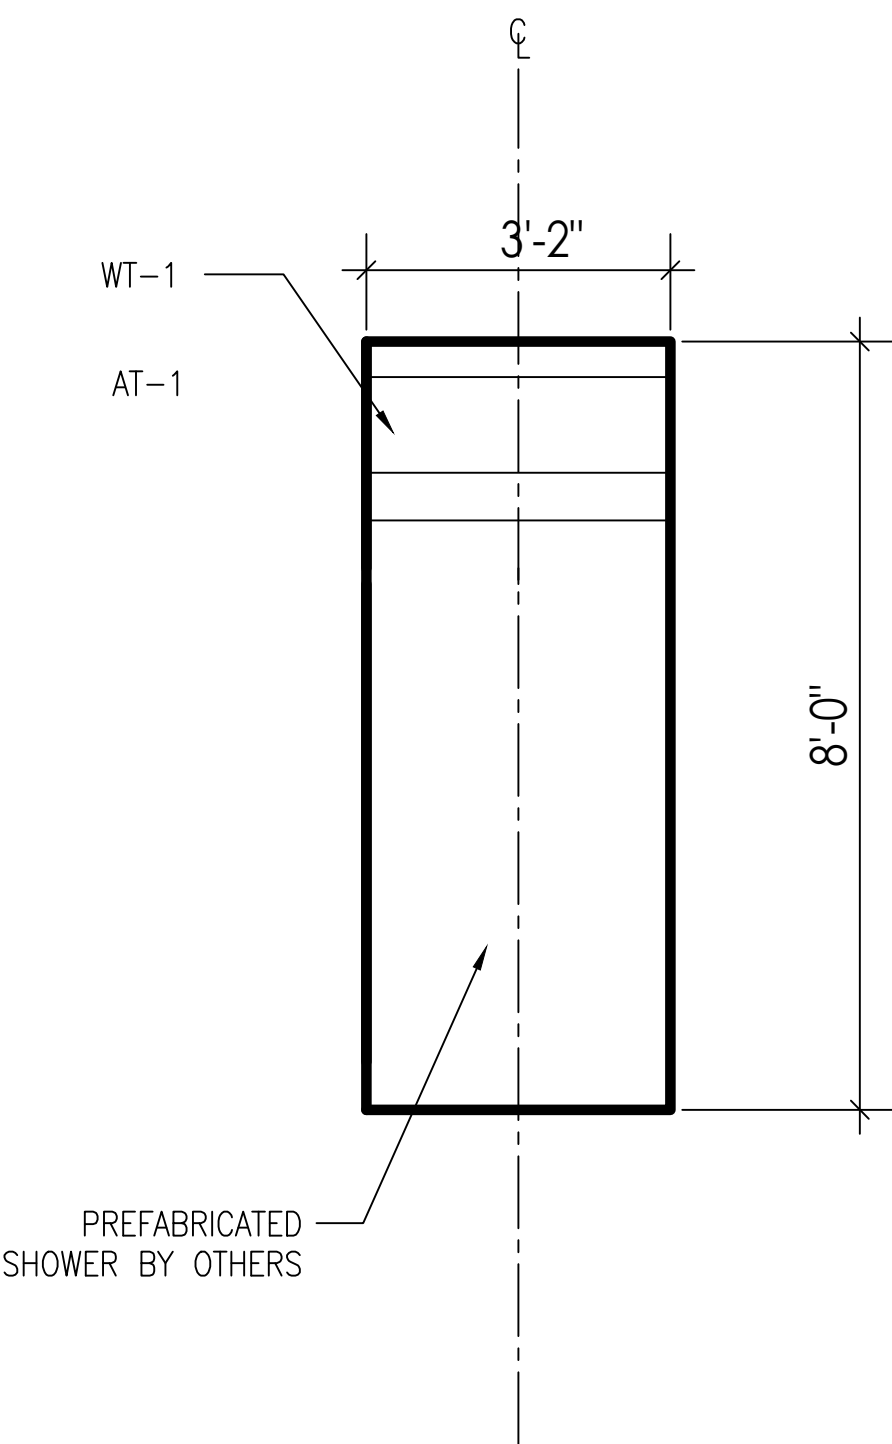

SINGLE
RESTROOM

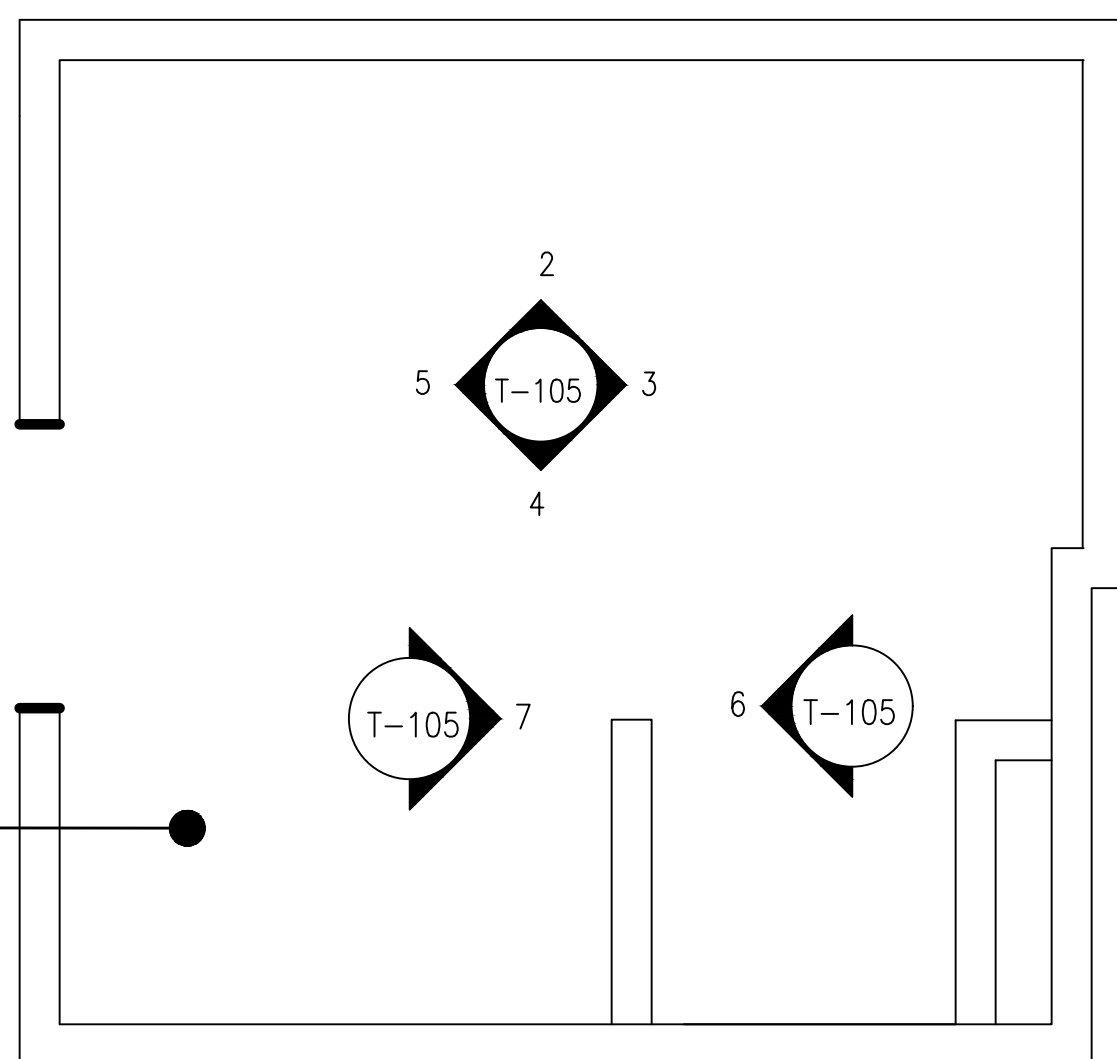

01
1/2"=1'-0" PLAN #2: 6TH FLOOR BATHROOMS

06
1/2"=1'-0" ELEVATIONS: 6TH FLOOR BATHROOMS

07
1/2"=1'-0" ELEVATIONS: 6TH FLOOR BATHROOMS

CONTRACTOR:
JRM CONSTRUCTION
MANAGEMENT, LLC
242 WEST 36TH STREET
11TH FLOOR
NEW YORK, NY 10018

INTERIOR DESIGNER:

ISSUE FOR APPROVAL 10/09/23
ISSUE NAME DATE

ARCHITECT:

SPACESMITH
ONE NEW YORK PLAZA
NEW YORK, NY 10004
PH:212 260 5583

PROJECT NAME:

JACK RESNICK & SONS
255 GREENWICH STREET
NEW YORK, NY 10007

SHEET NAME:




ELEVATIONS
6TH FLOOR BATHROOMS

DATE:
PROJECT NO.:
PRINCIPAL:
DRAWING BY:
CHECKED BY:
SCALE:
DWG. No.:
T-105
7 of 29



(BT-1) TILE BASE GROUT JOINTS WILL NOT ALIGN WITH (WT-1) WALL TILE GROUT JOINTS


(AT-1) ACCENT WALL TILE GROUT JOINTS WILL NOT ALIGN WITH (WT-1) WALL TILE GROUT JOINTS

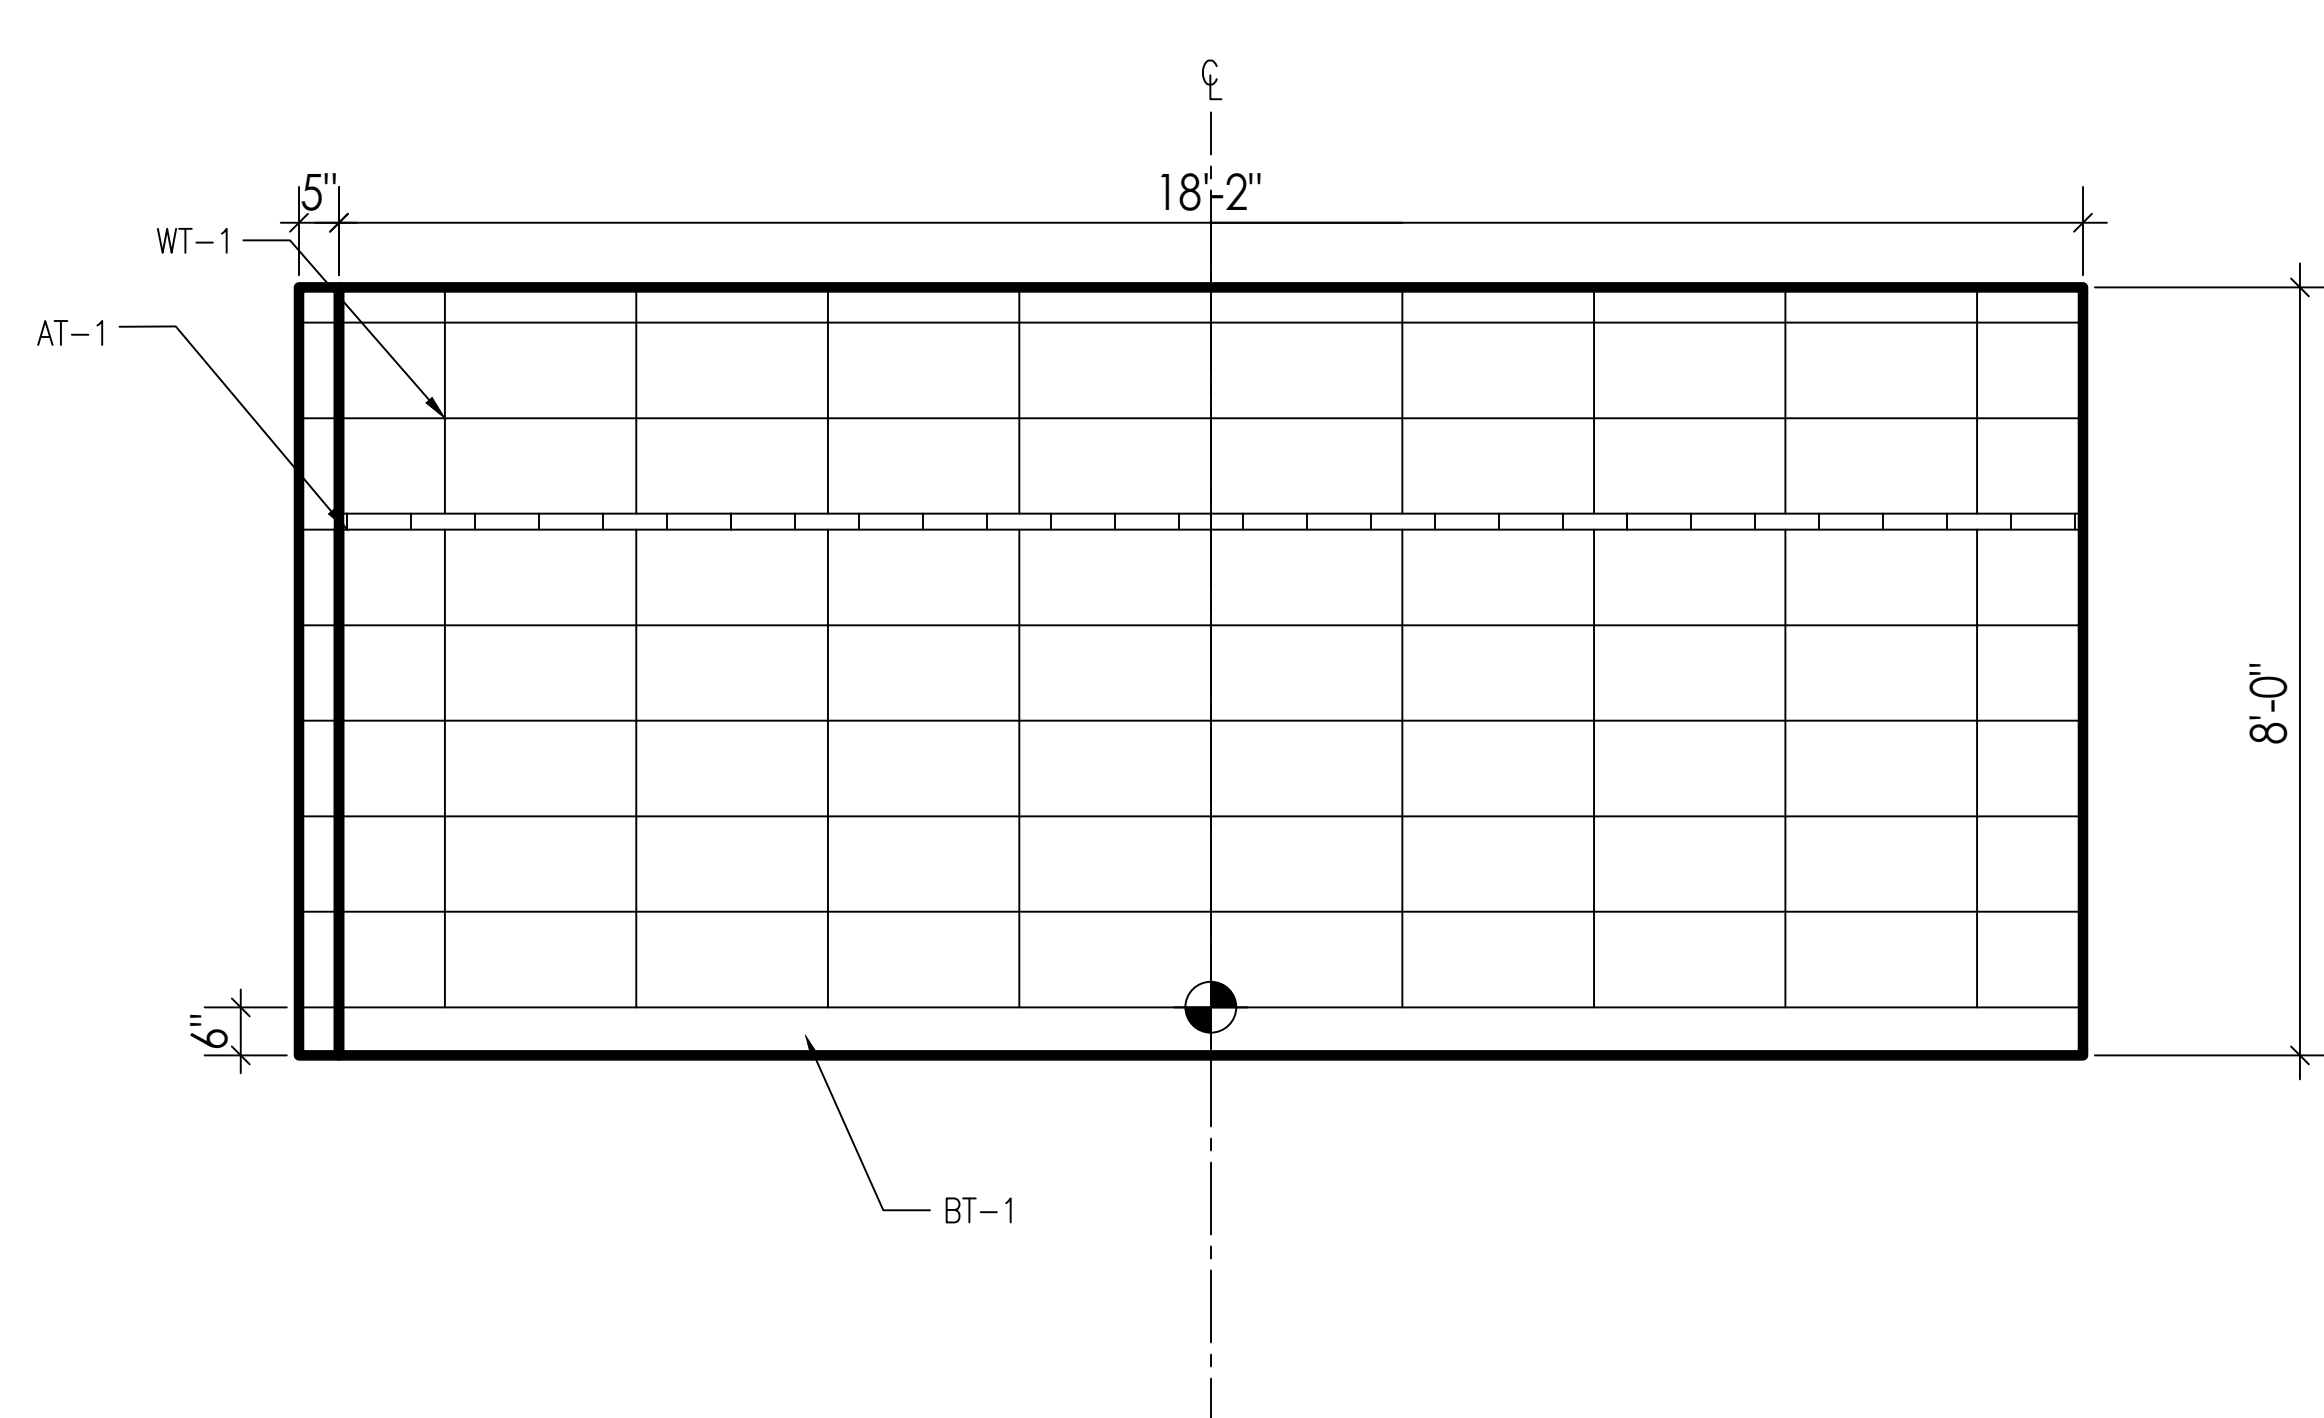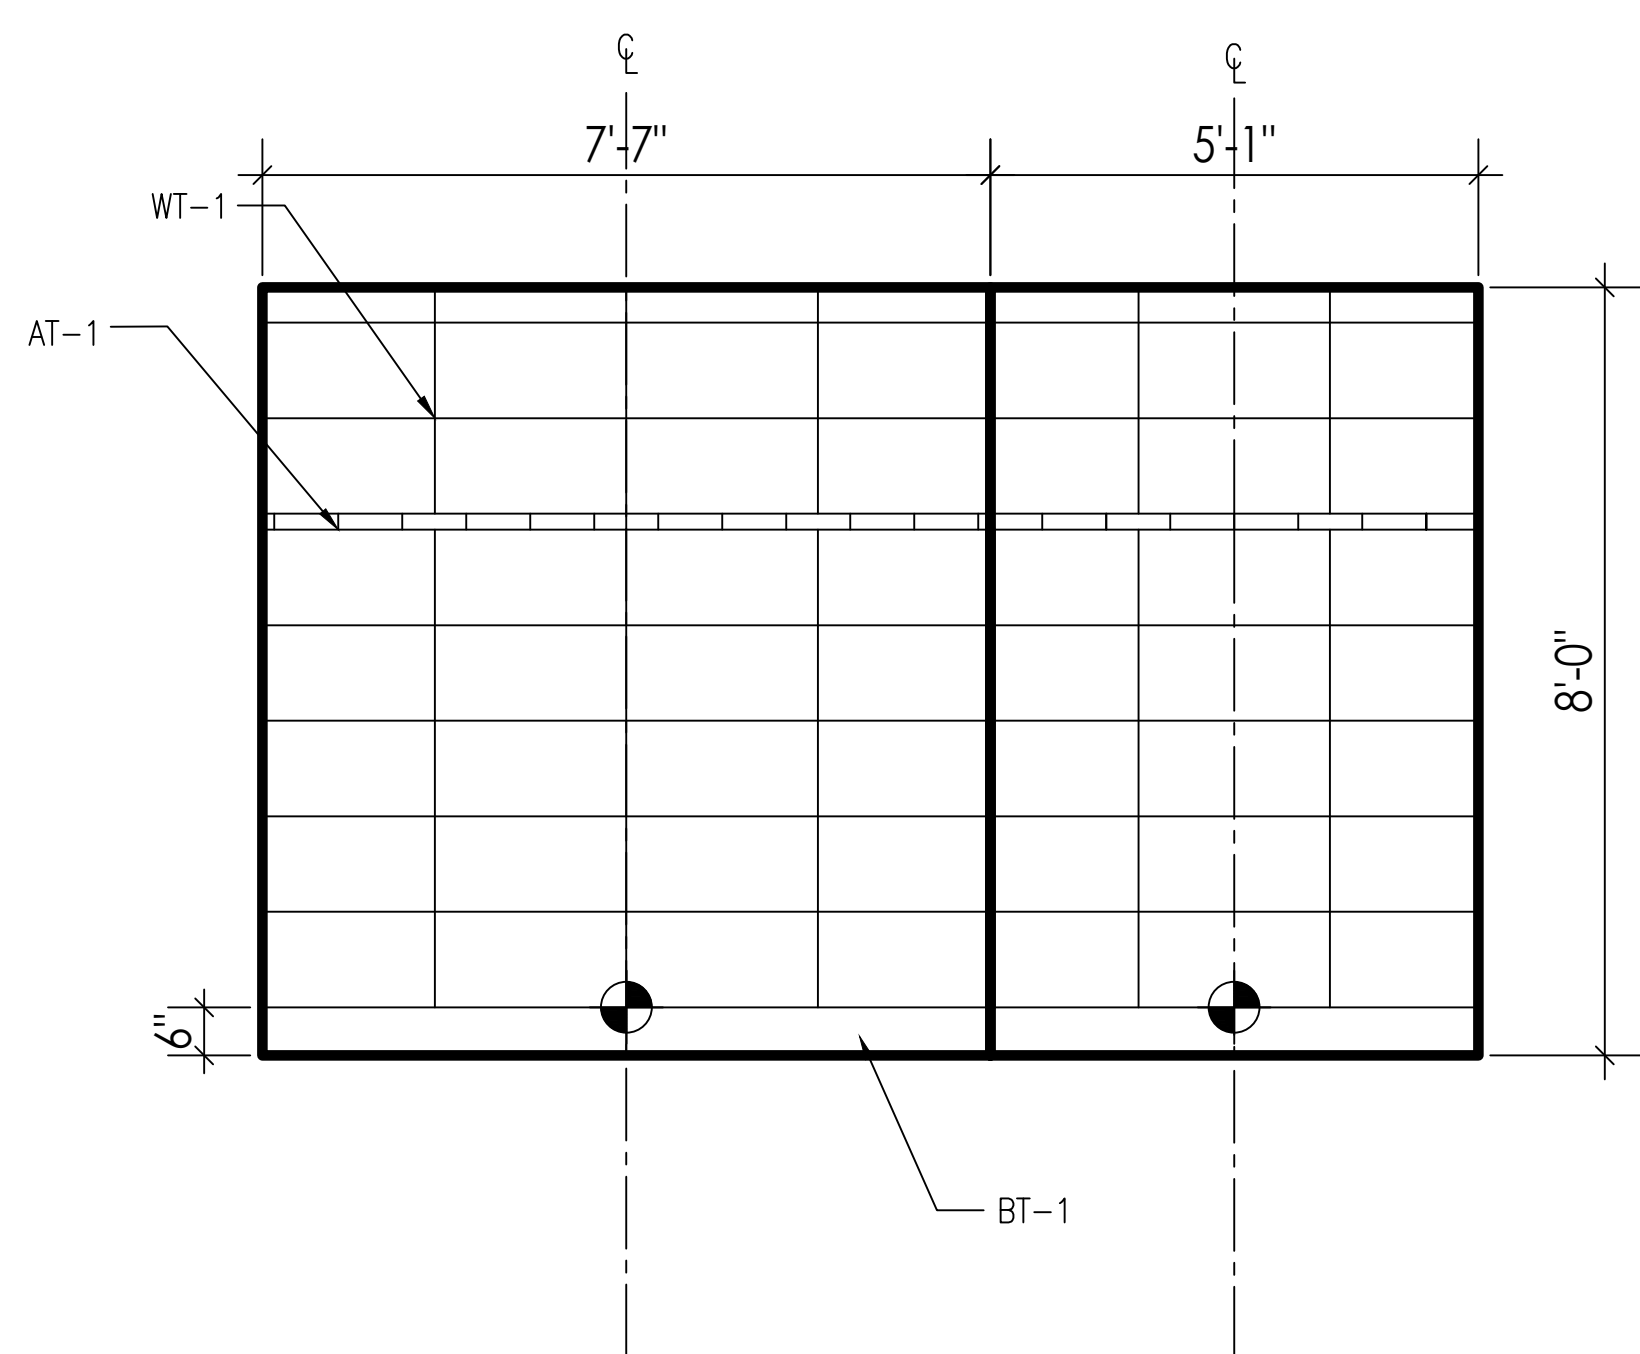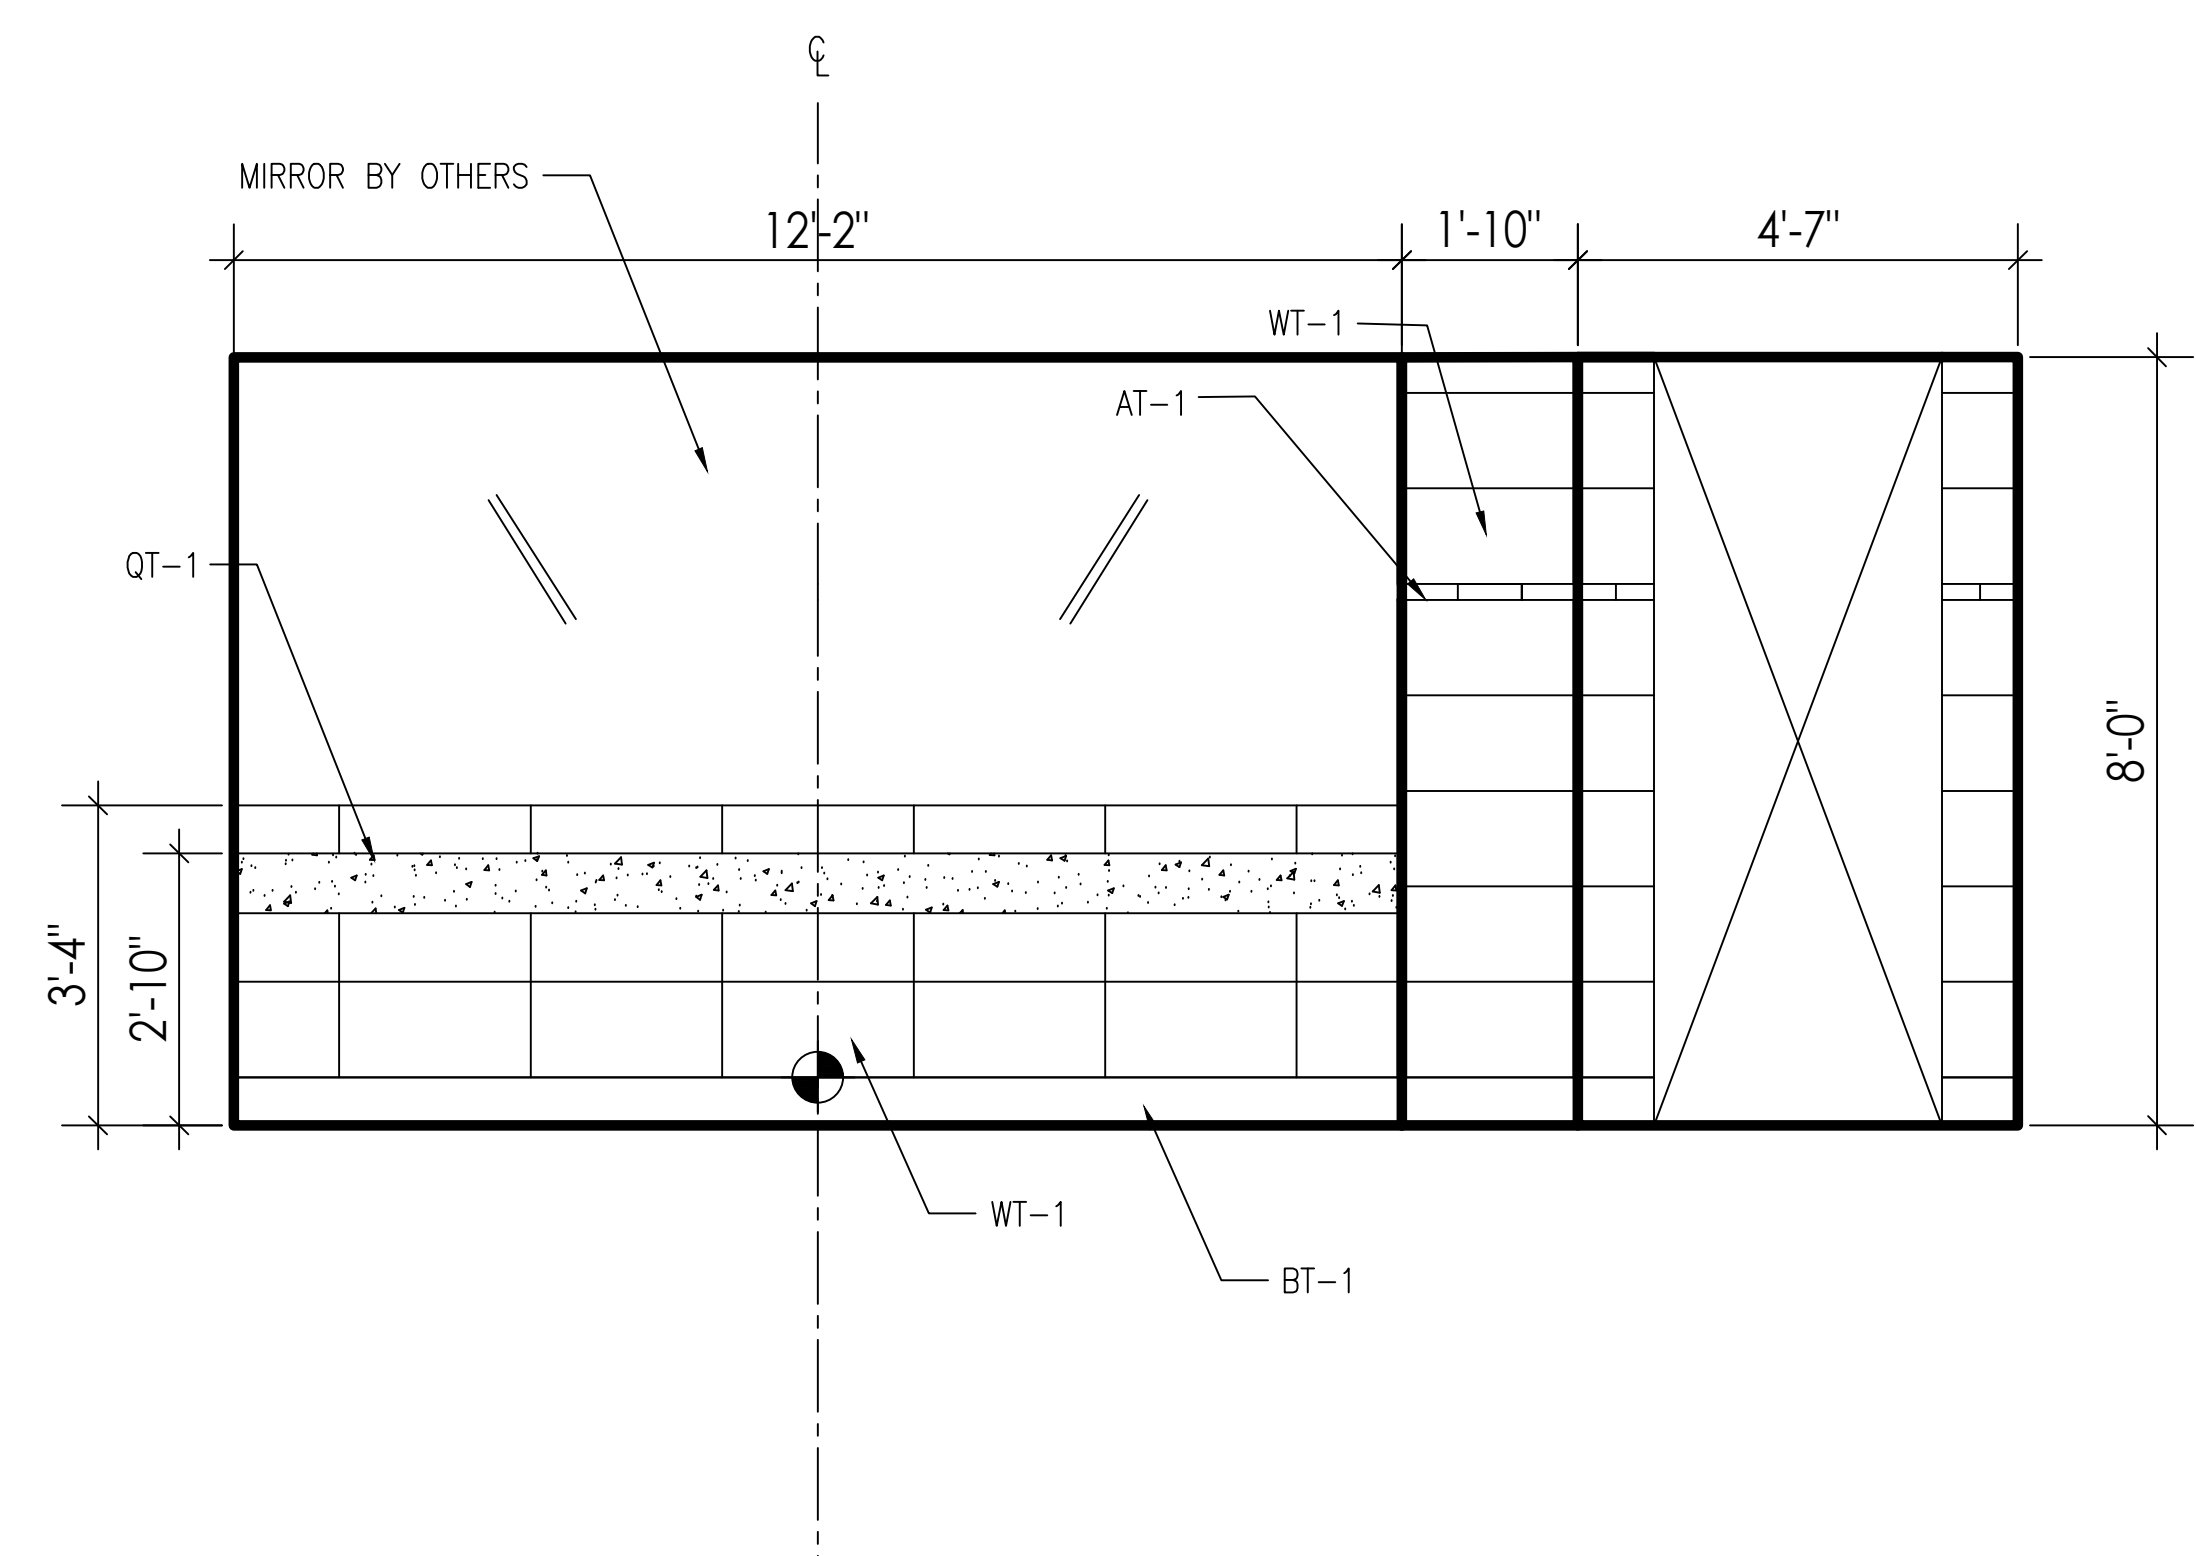


02
1/2"=1'-0" ELEVATIONS: 7TH FLOOR BATHROOMS

03
1/2"=1'-0" ELEVATIONS: 7TH FLOOR BATHROOMS


04
1/2"=1'-0" ELEVATIONS: 7TH FLOOR BATHROOMS

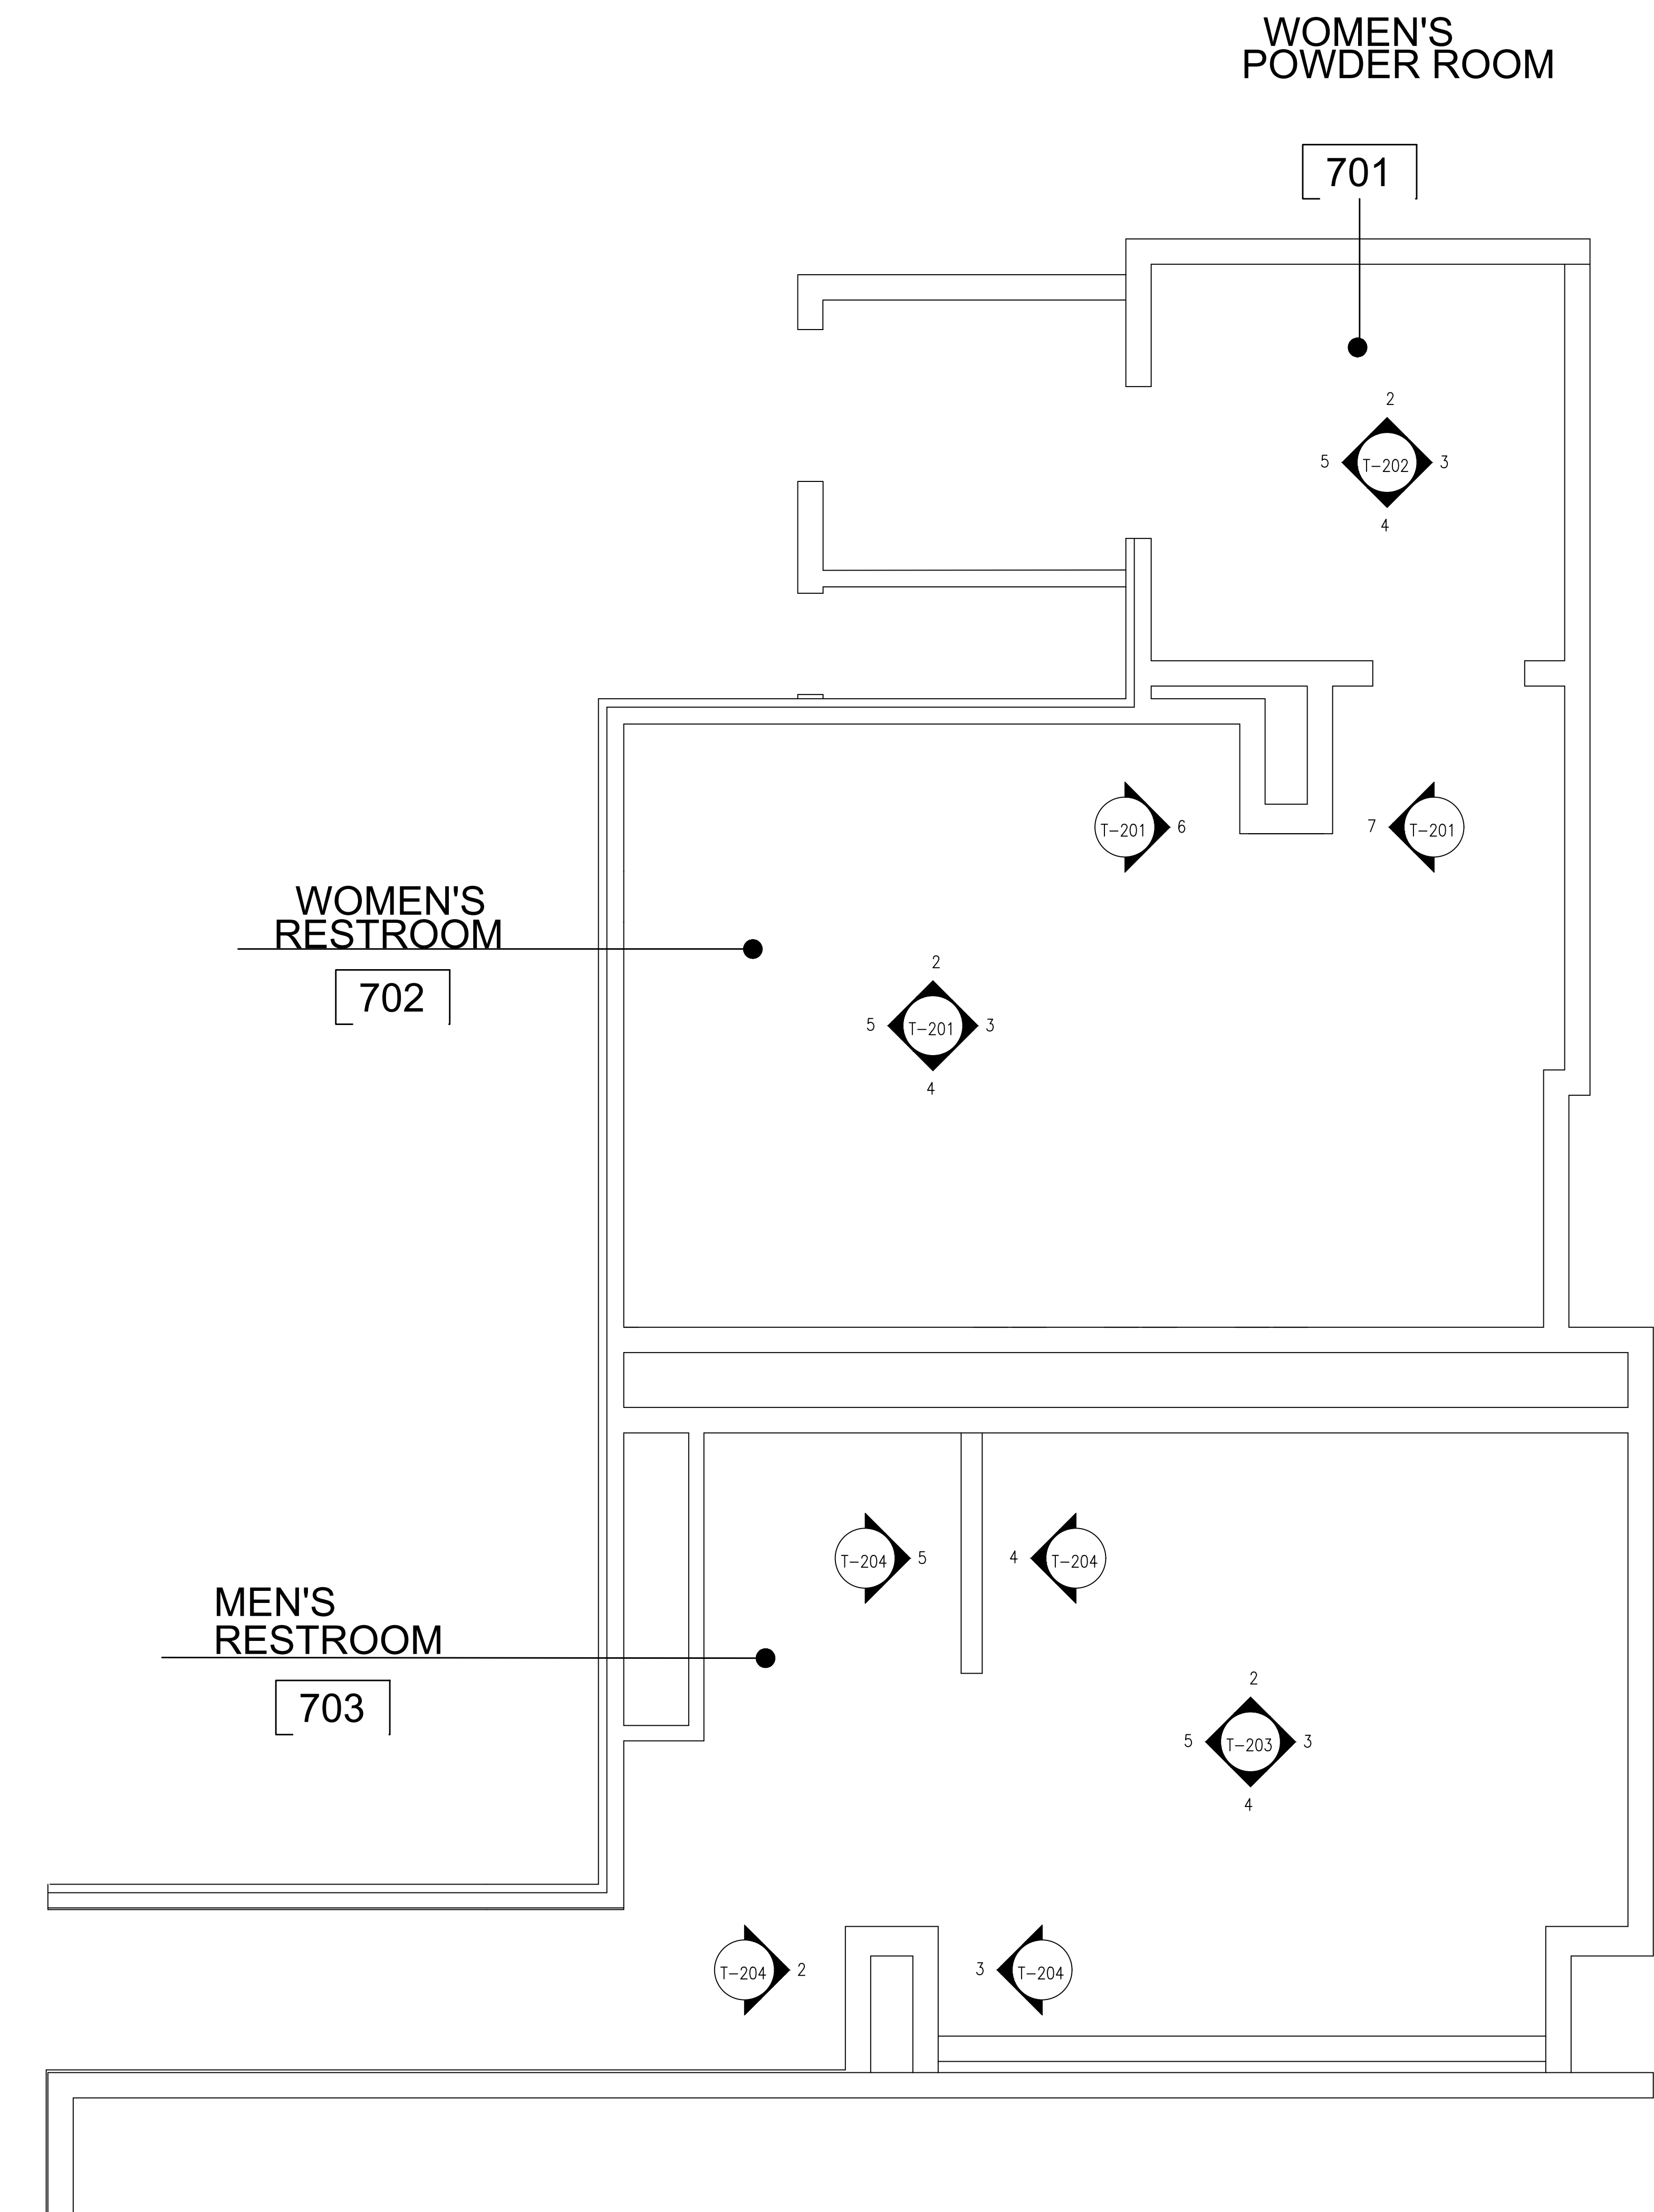


01
1/2"=1'-0" PLAN #2: 7TH FLOOR BATHROOMS

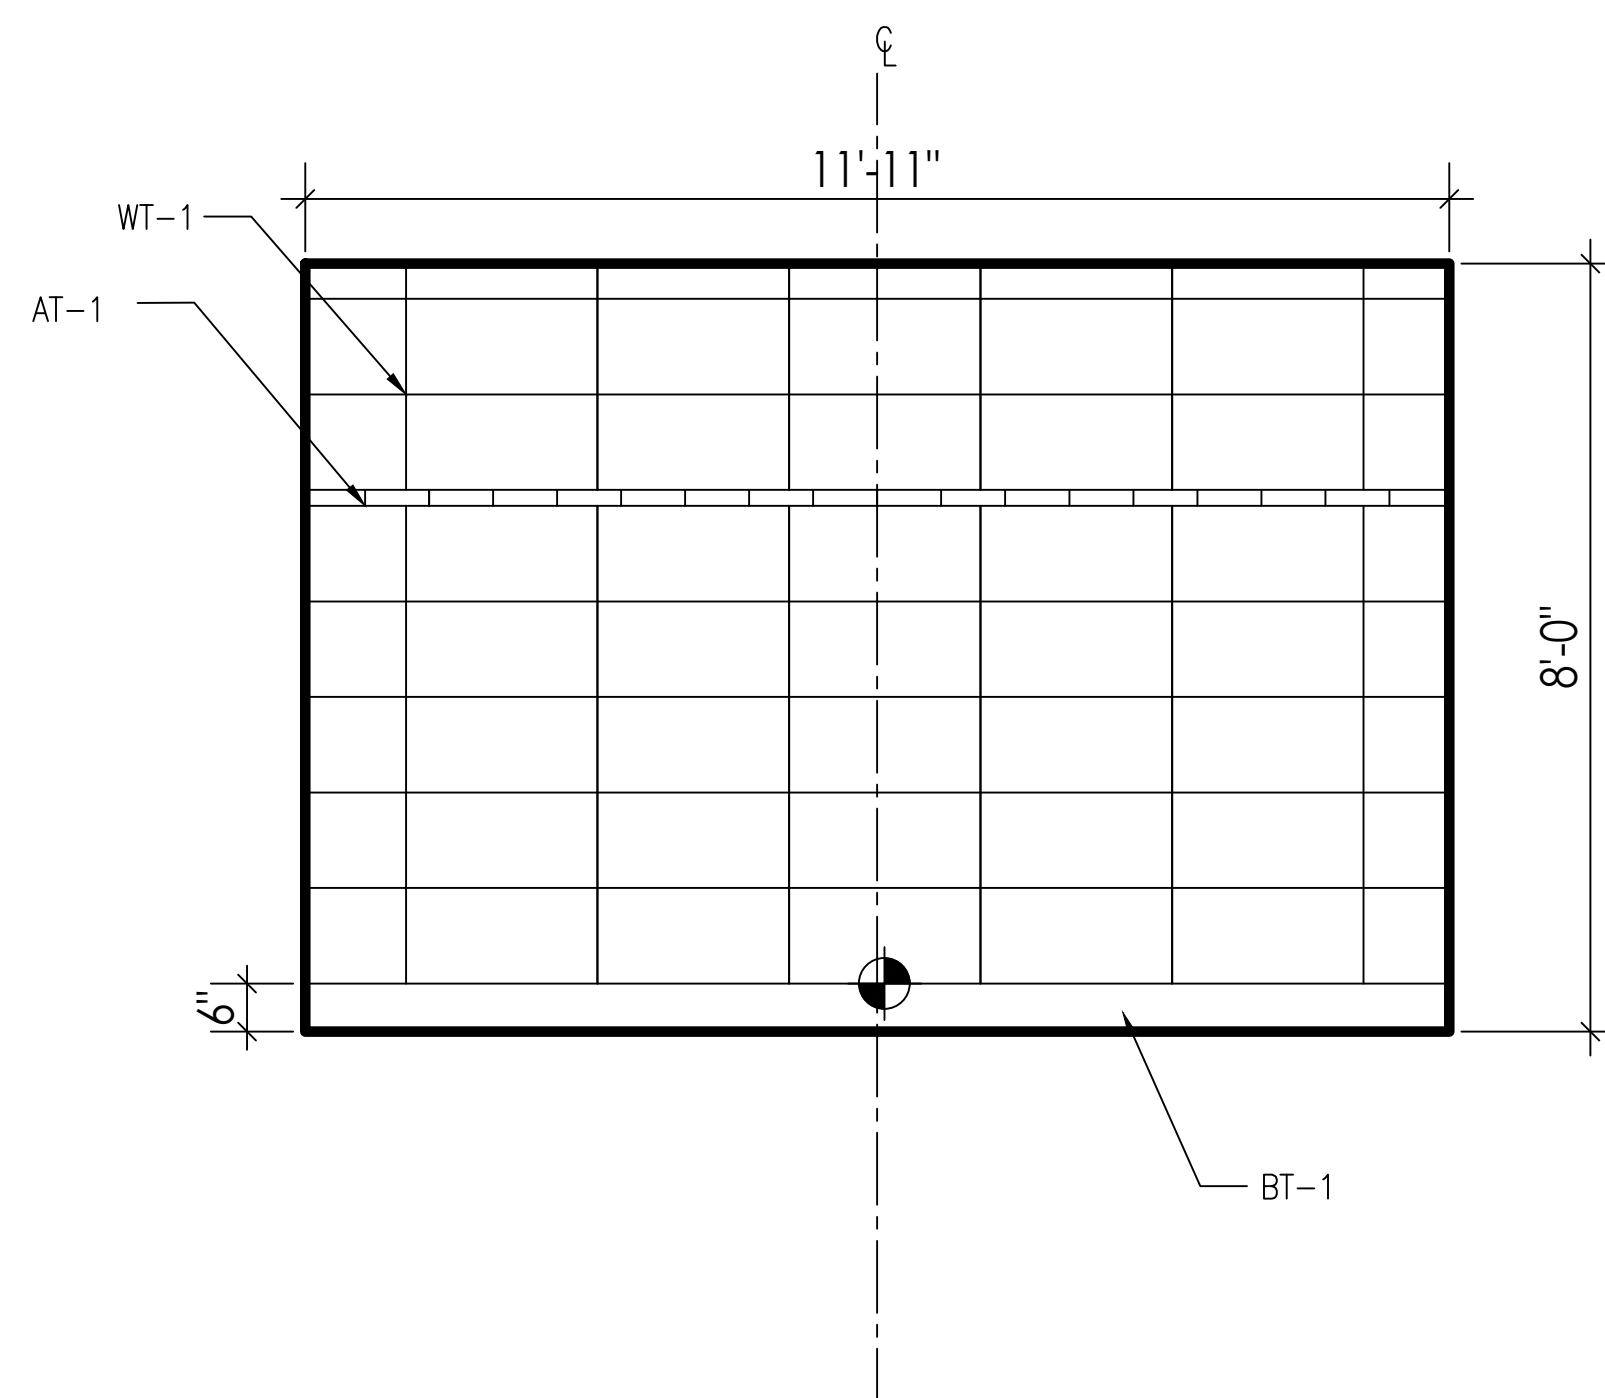

05
1/2"=1'-0" ELEVATIONS: 7TH FLOOR BATHROOMS

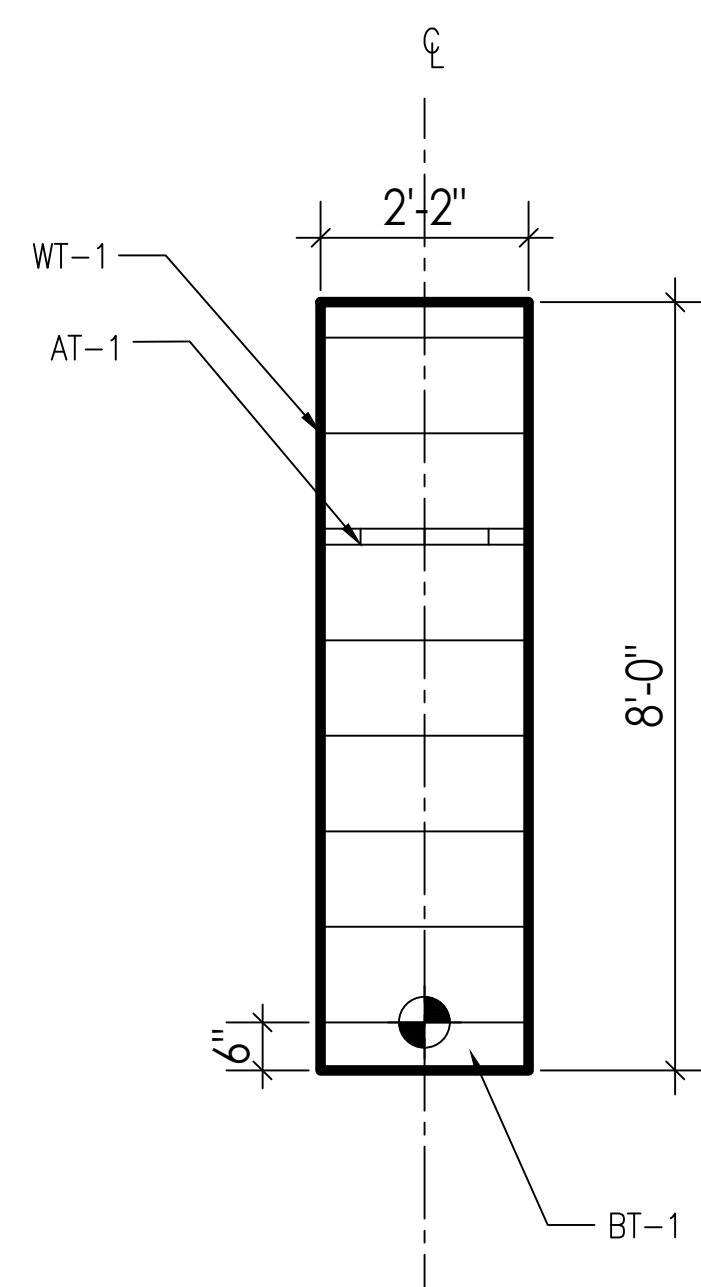

06
1/2"=1'-0" ELEVATIONS: 7TH FLOOR BATHROOMS

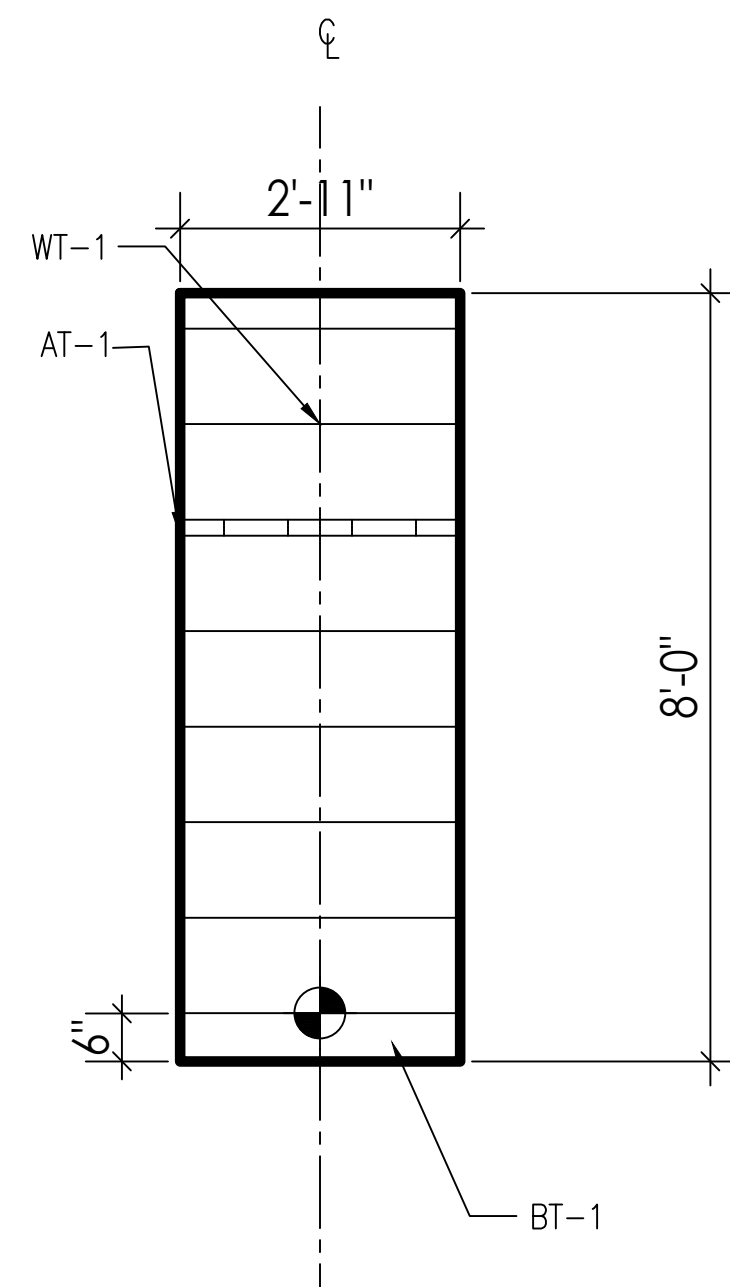

07
1/2"=1'-0" ELEVATIONS: 7TH FLOOR BATHROOMS

AUSTRO TILE & STONE, LLC
30-25 93RD STREET
EAST ELMHURST, NY 11369

CONTRACTOR:
JRM CONSTRUCTION
MANAGEMENT, LLC
242 WEST 36TH STREET
11TH FLOOR
NEW YORK, NY 10018

INTERIOR DESIGNER:

ISSUE FOR APPROVAL 10/09/23
ISSUE NAME DATE

ARCHITECT:
SPACESMITH
ONE NEW YORK PLAZA
NEW YORK, NY 10004
PH:212 260 5583

PROJECT NAME:
JACK RESNICK & SONS
255 GREENWICH STREET
NEW YORK, NY 10007

SHEET NAME:
ELEVATIONS
7TH FLOOR BATHROOMS

DATE:
PROJECT NO.:
PRINCIPAL:
DRAWING BY:
CHECKED BY:
SCALE:
DWG. No.:
T-201
9 of 29






STARTING POINT

(BT-1) TILE BASE GROUT JOINTS WILL NOT ALIGN WITH (WT-1) WALL TILE GROUT JOINTS

(AT-1) ACCENT WALL TILE GROUT JOINTS WILL NOT ALIGN WITH (WT-1) WALL TILE GROUT JOINTS


WOMEN'S
POWDER ROOM

701

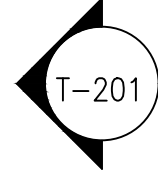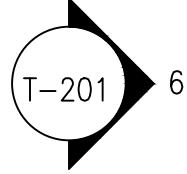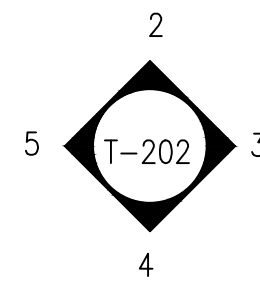







WOMEN'S
RESTROOM

702

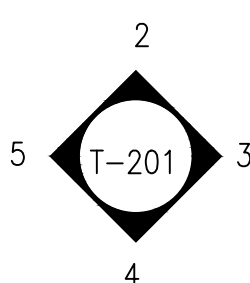


MEN'S
RESTROOM


703

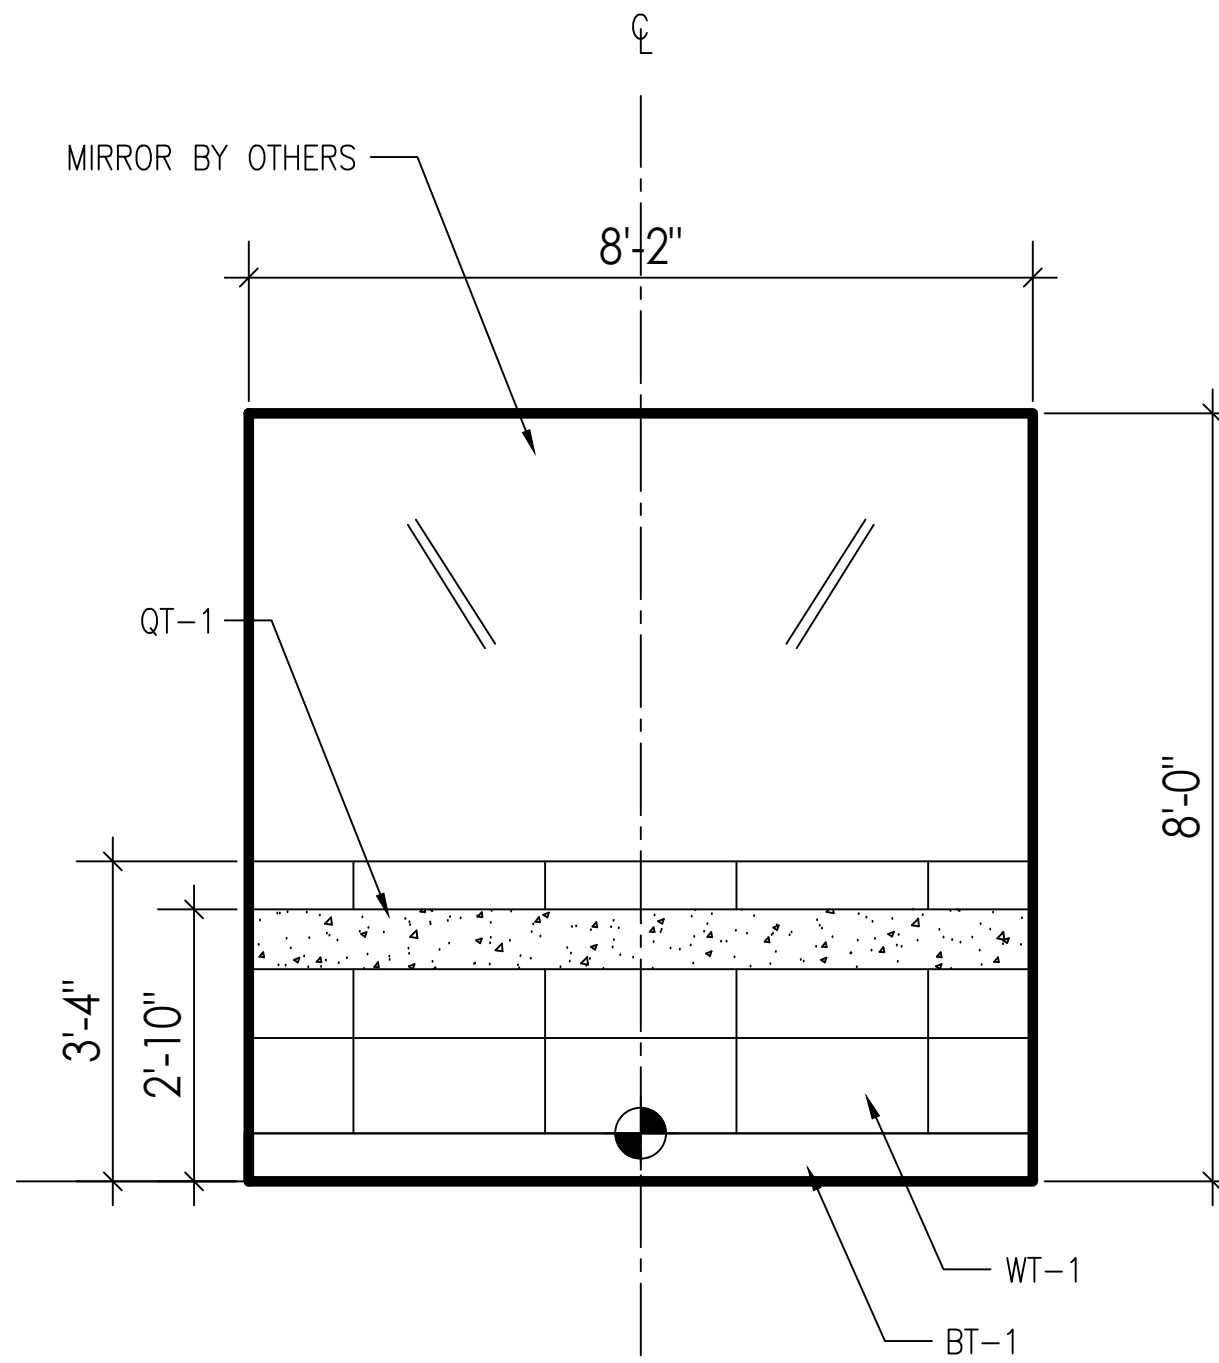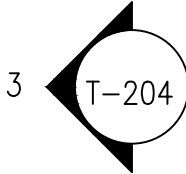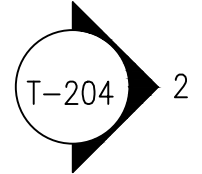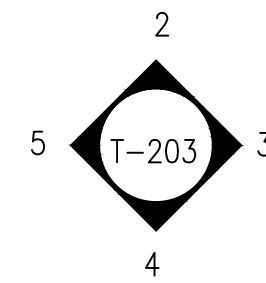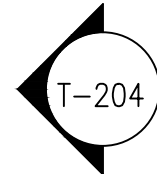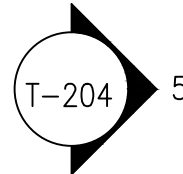


02
1/2"=1'-0" ELEVATIONS: 7TH FLOOR BATHROOMS

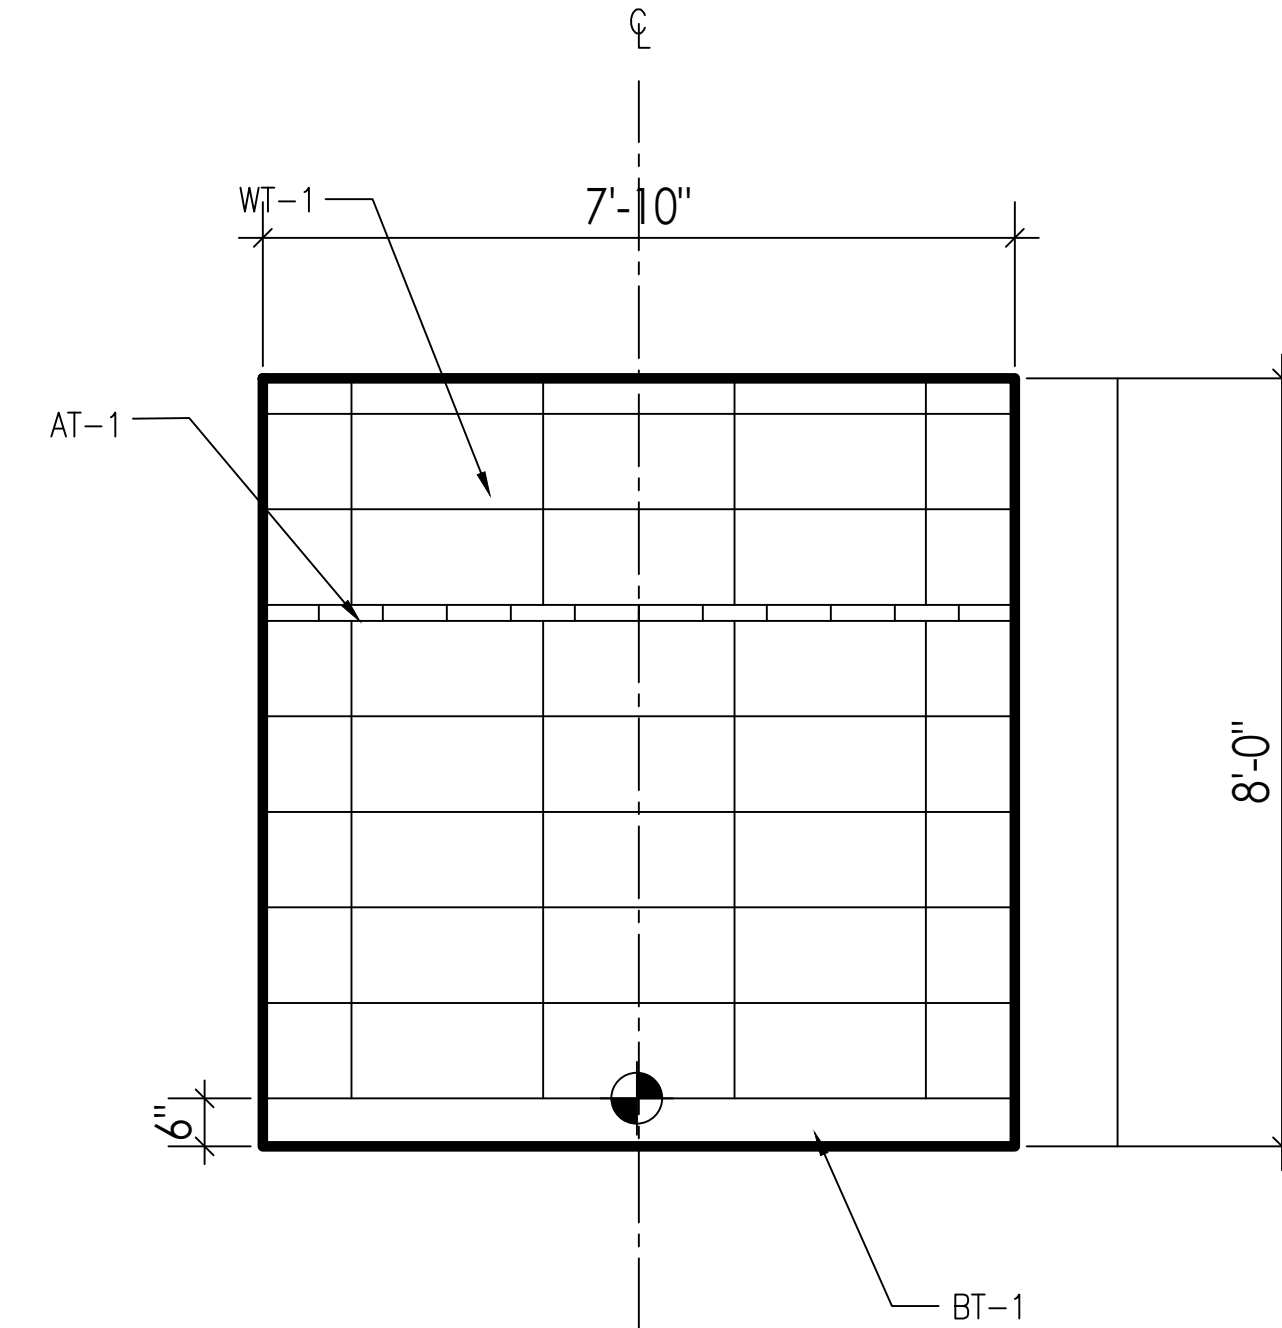

03
1/2"=1'-0" ELEVATIONS: 7TH FLOOR BATHROOMS

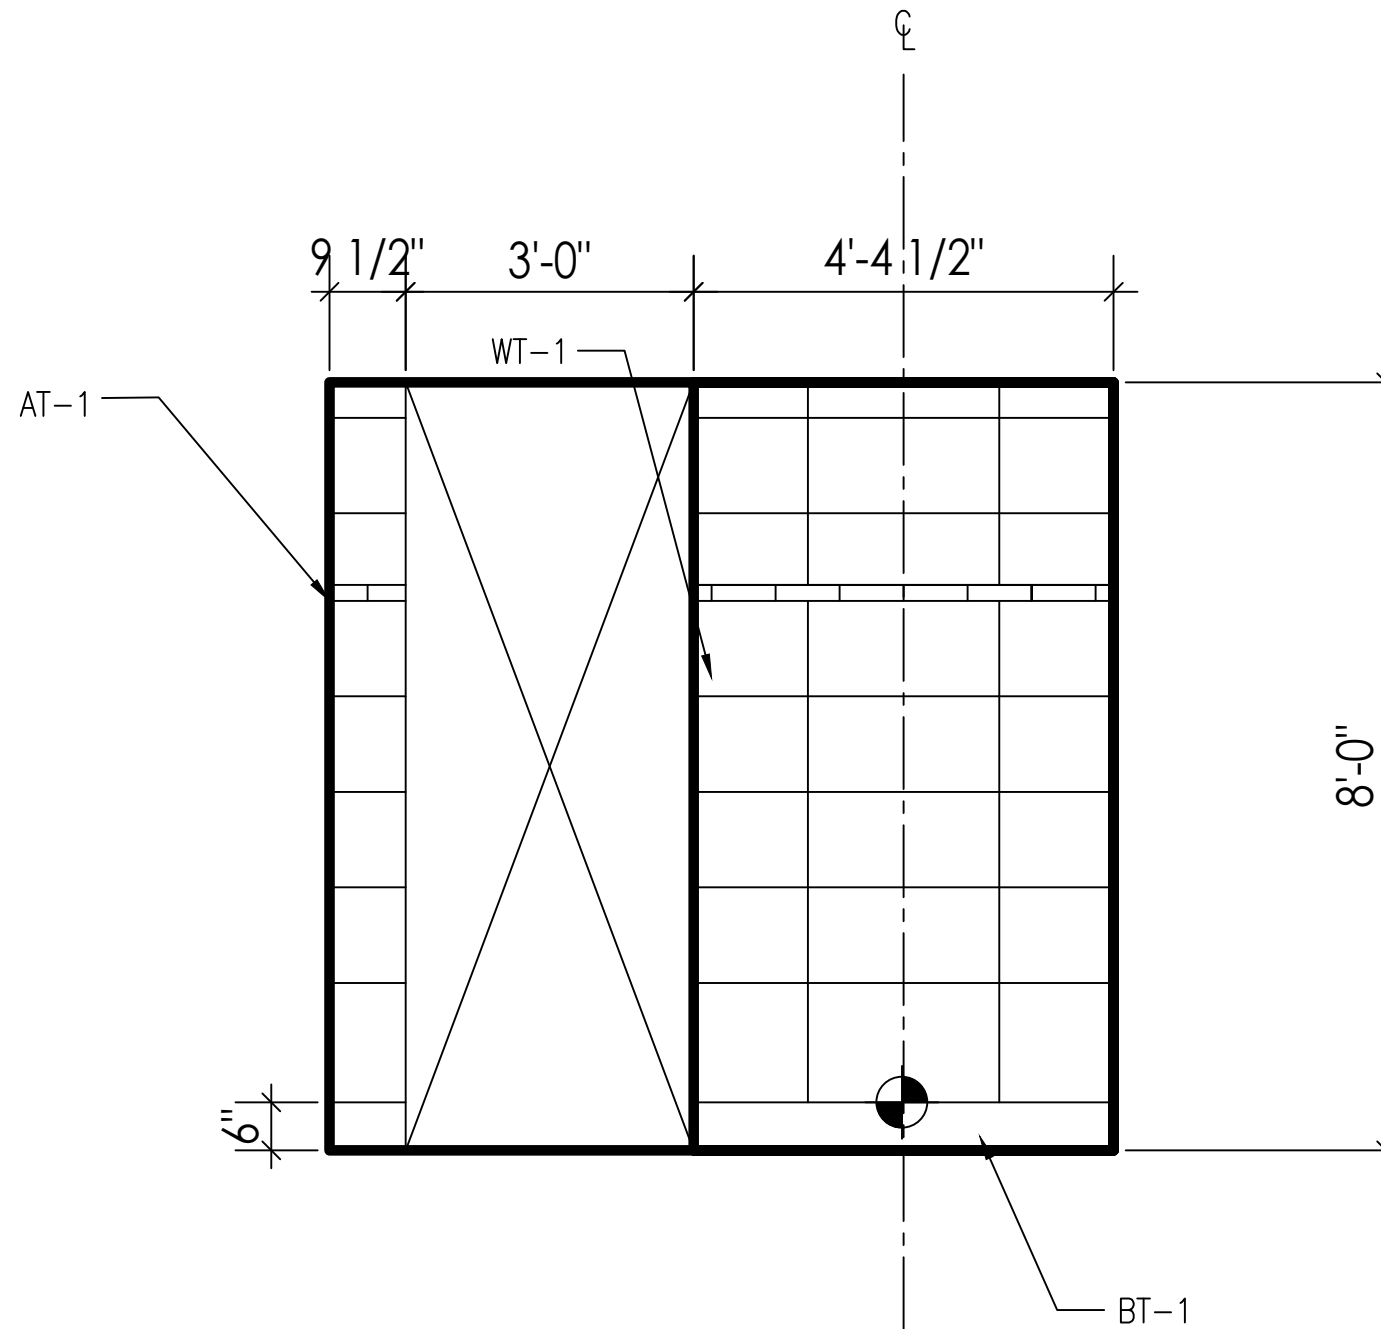

04
1/2"=1'-0" ELEVATIONS: 7TH FLOOR BATHROOMS

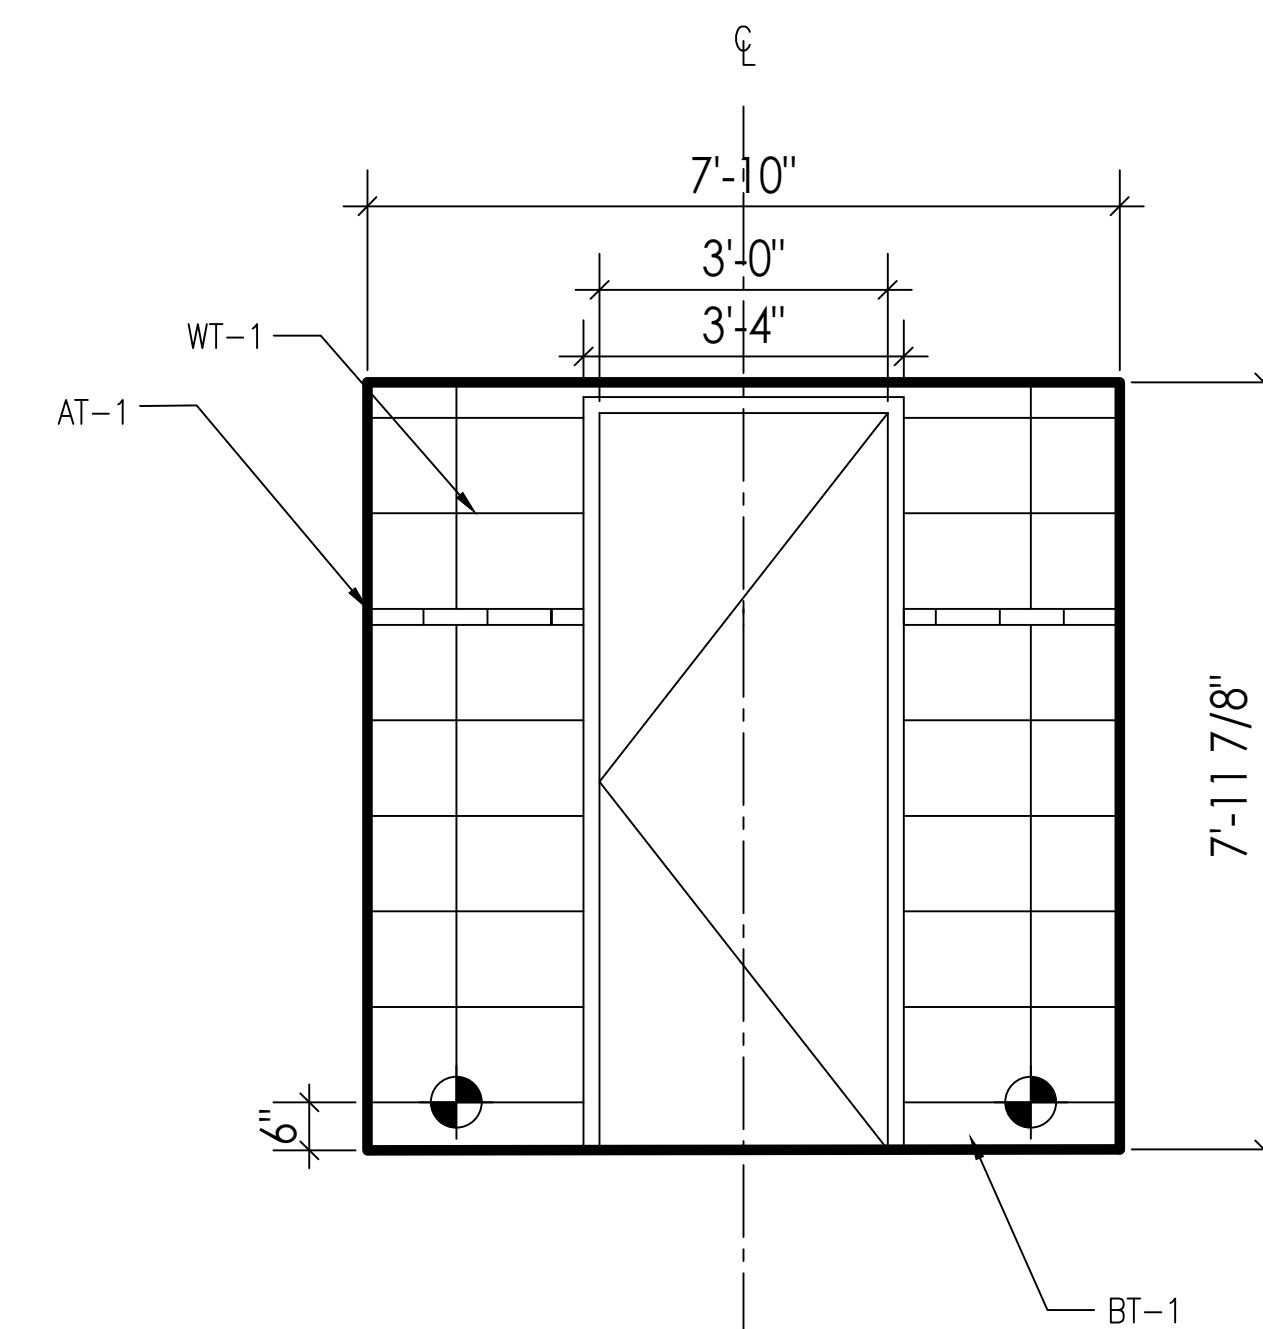

05
1/2"=1'-0" ELEVATIONS: 7TH FLOOR BATHROOMS

AUSTRO TILE & STONE, LLC
30-25 93RD STREET
EAST ELMHURST, NY 11369

CONTRACTOR:
JRM CONSTRUCTION
MANAGEMENT, LLC
242 WEST 36TH STREET
11TH FLOOR
NEW YORK, NY 10018

INTERIOR DESIGNER:

ISSUE FOR APPROVAL 10/09/23
ISSUE NAME DATE

ARCHITECT:

SPACESMITH
ONE NEW YORK PLAZA
NEW YORK, NY 10004
PH:212 260 5583

PROJECT NAME:

JACK RESNICK & SONS
255 GREENWICH STREET
NEW YORK, NY 10007

SHEET NAME:

ELEVATIONS
7TH FLOOR BATHROOMS



DATE:
PROJECT NO.:
PRINCIPAL:
DRAWING BY:
CHECKED BY:
SCALE:
DWG. No.:
T-202



STARTING POINT


(BT-1) TILE BASE GROUT JOINTS WILL NOT ALIGN WITH (WT-1) WALL TILE GROUT JOINTS

(AT-1) ACCENT WALL TILE GROUT JOINTS WILL NOT ALIGN WITH (WT-1) WALL TILE GROUT JOINTS

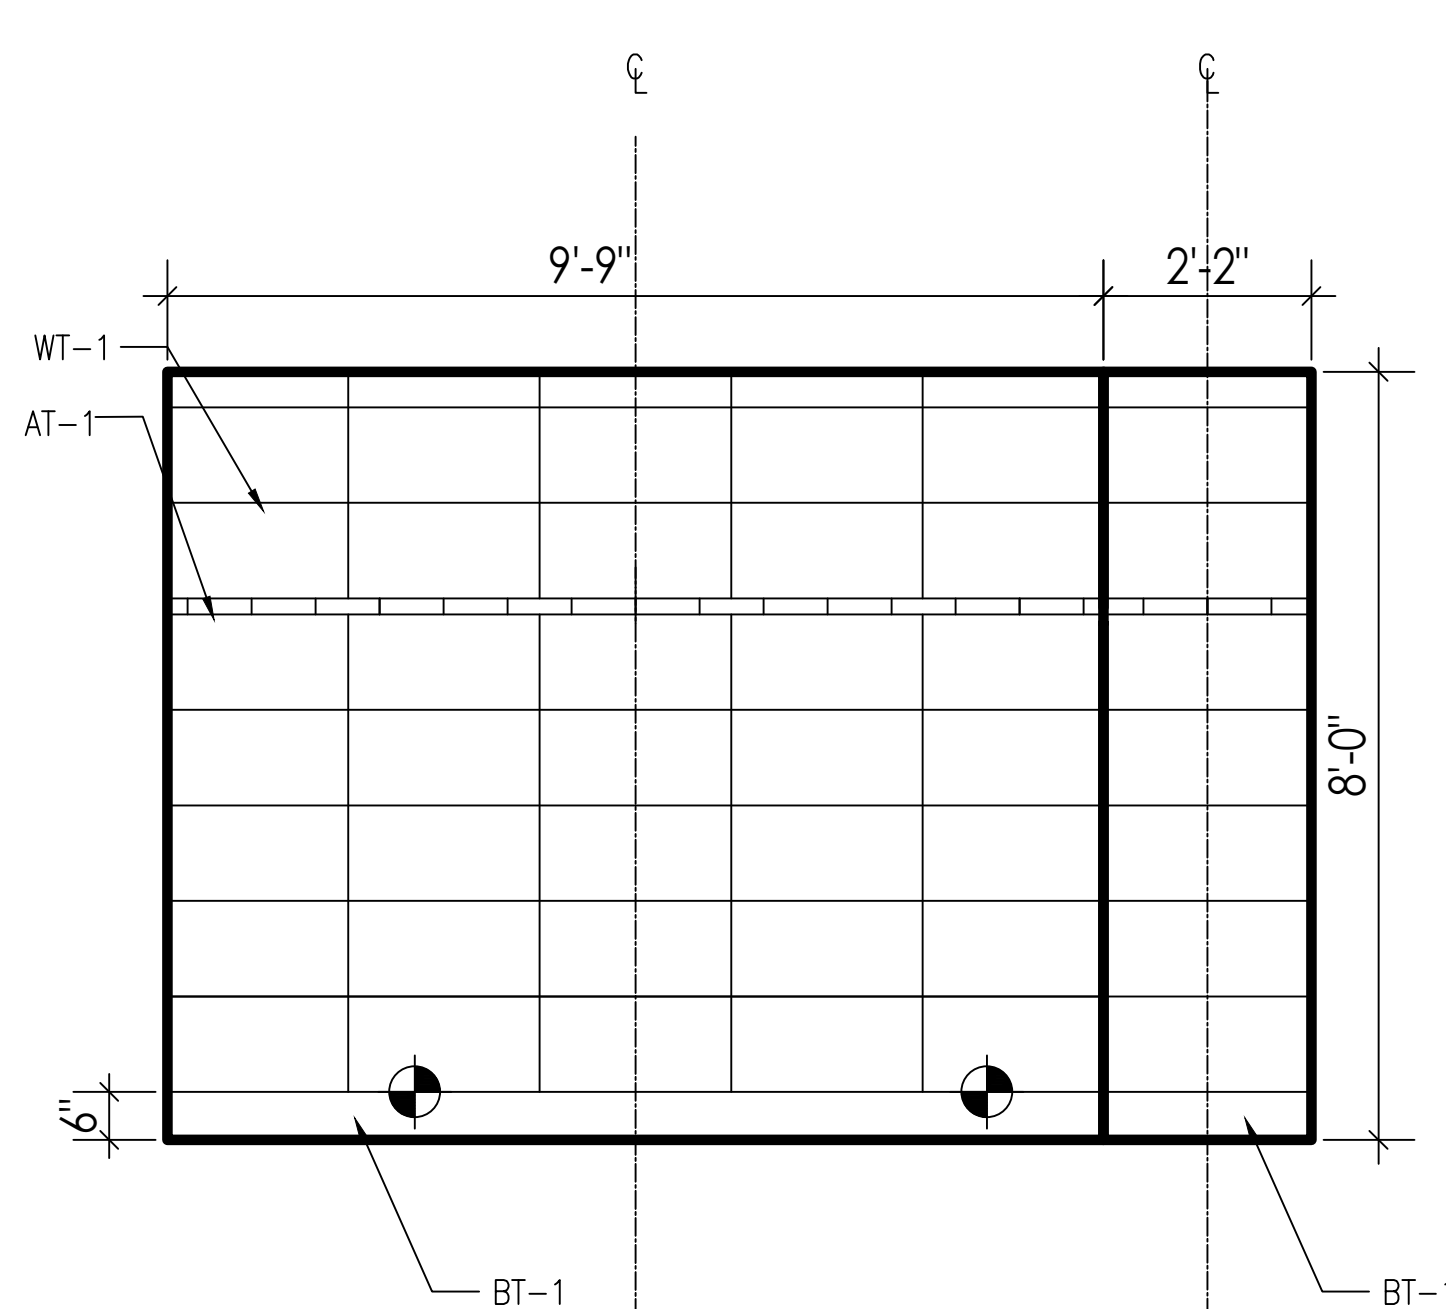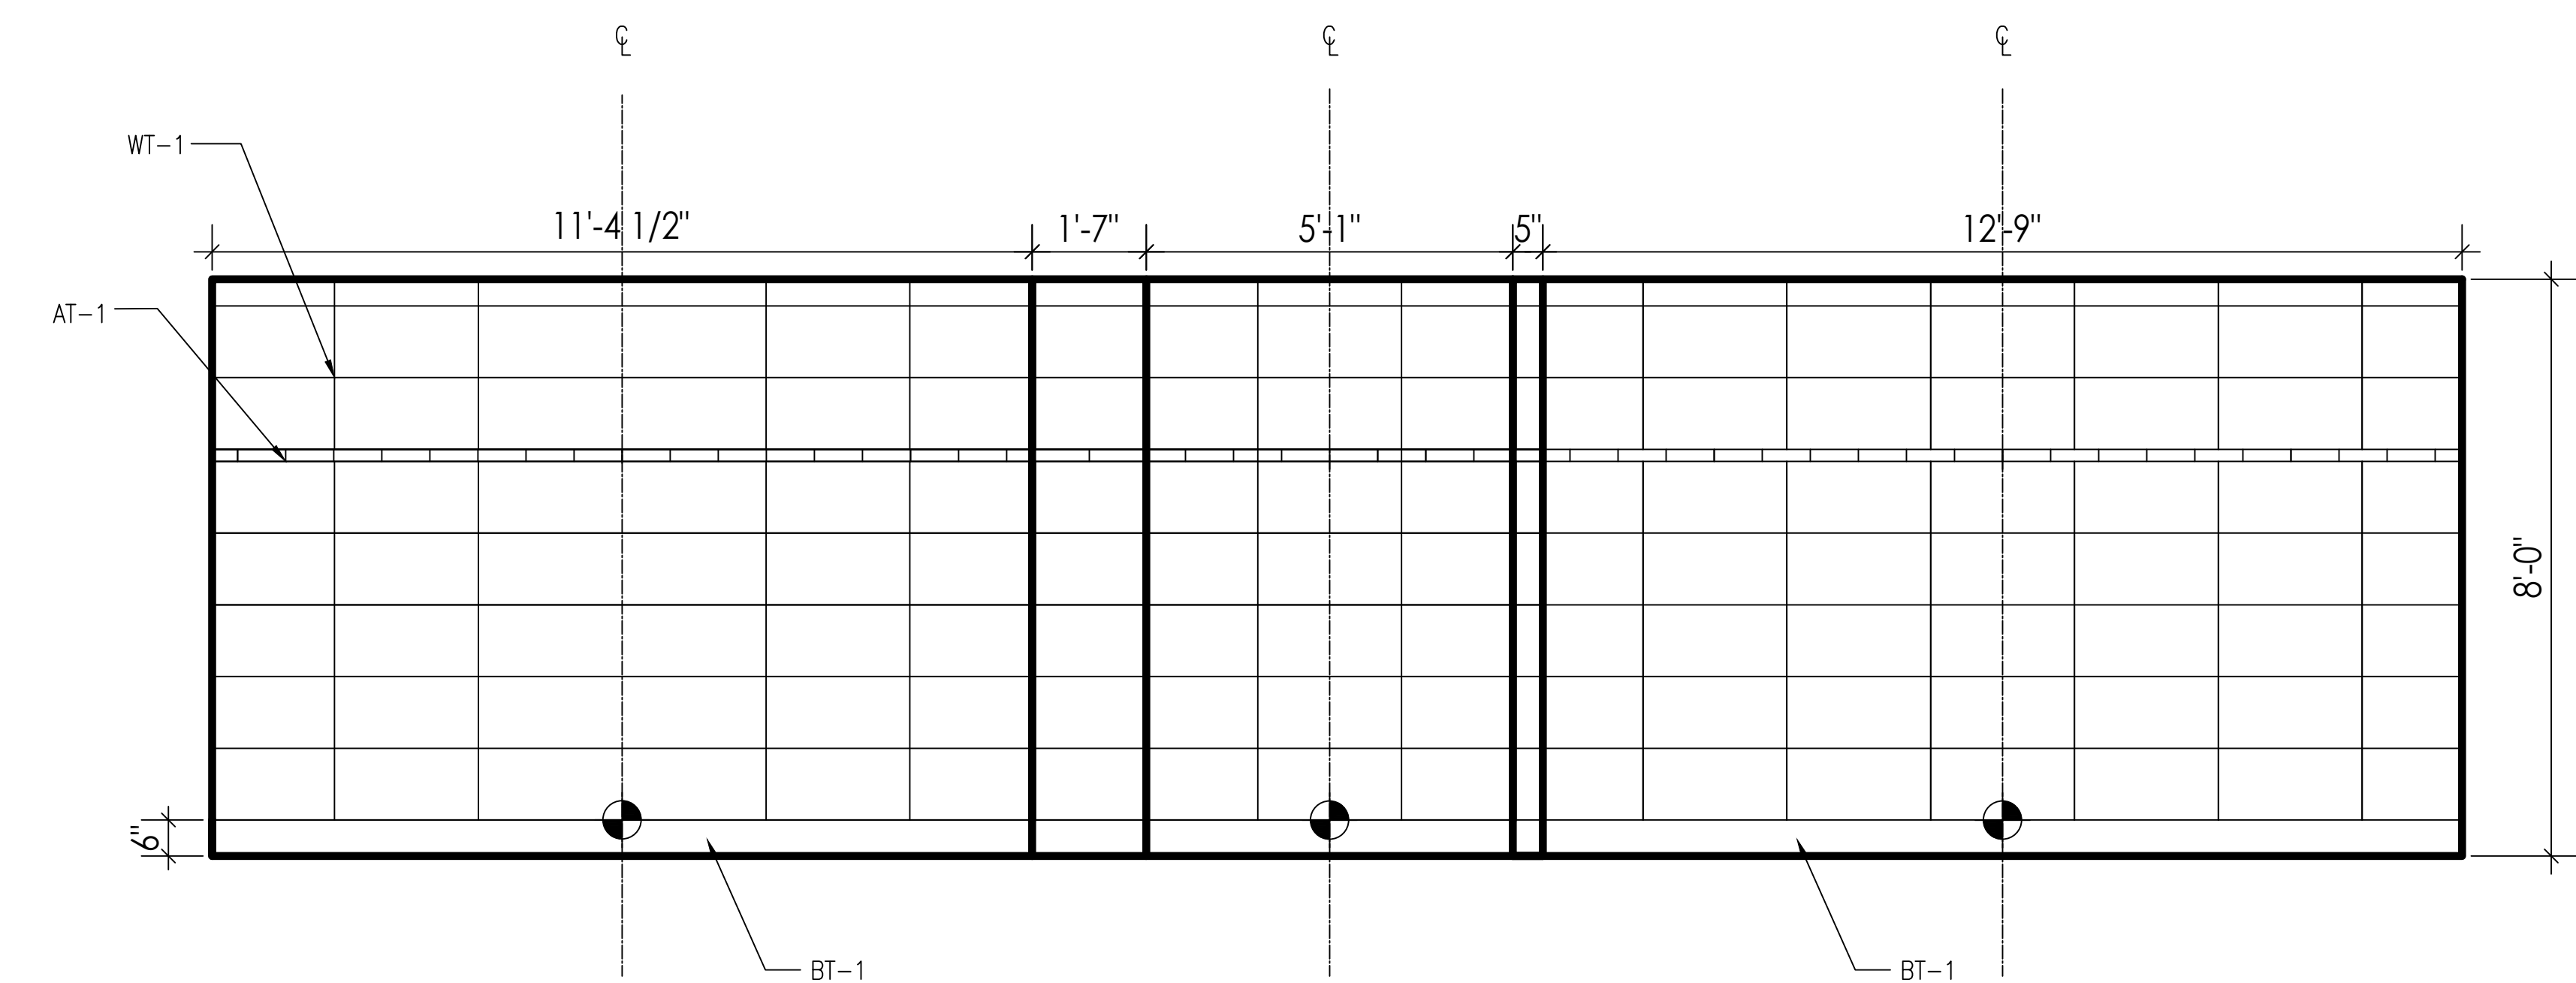


02
1/2"=1'-0" ELEVATIONS: 7TH FLOOR BATHROOMS


03
1/2"=1'-0" ELEVATIONS: 7TH FLOOR BATHROOMS

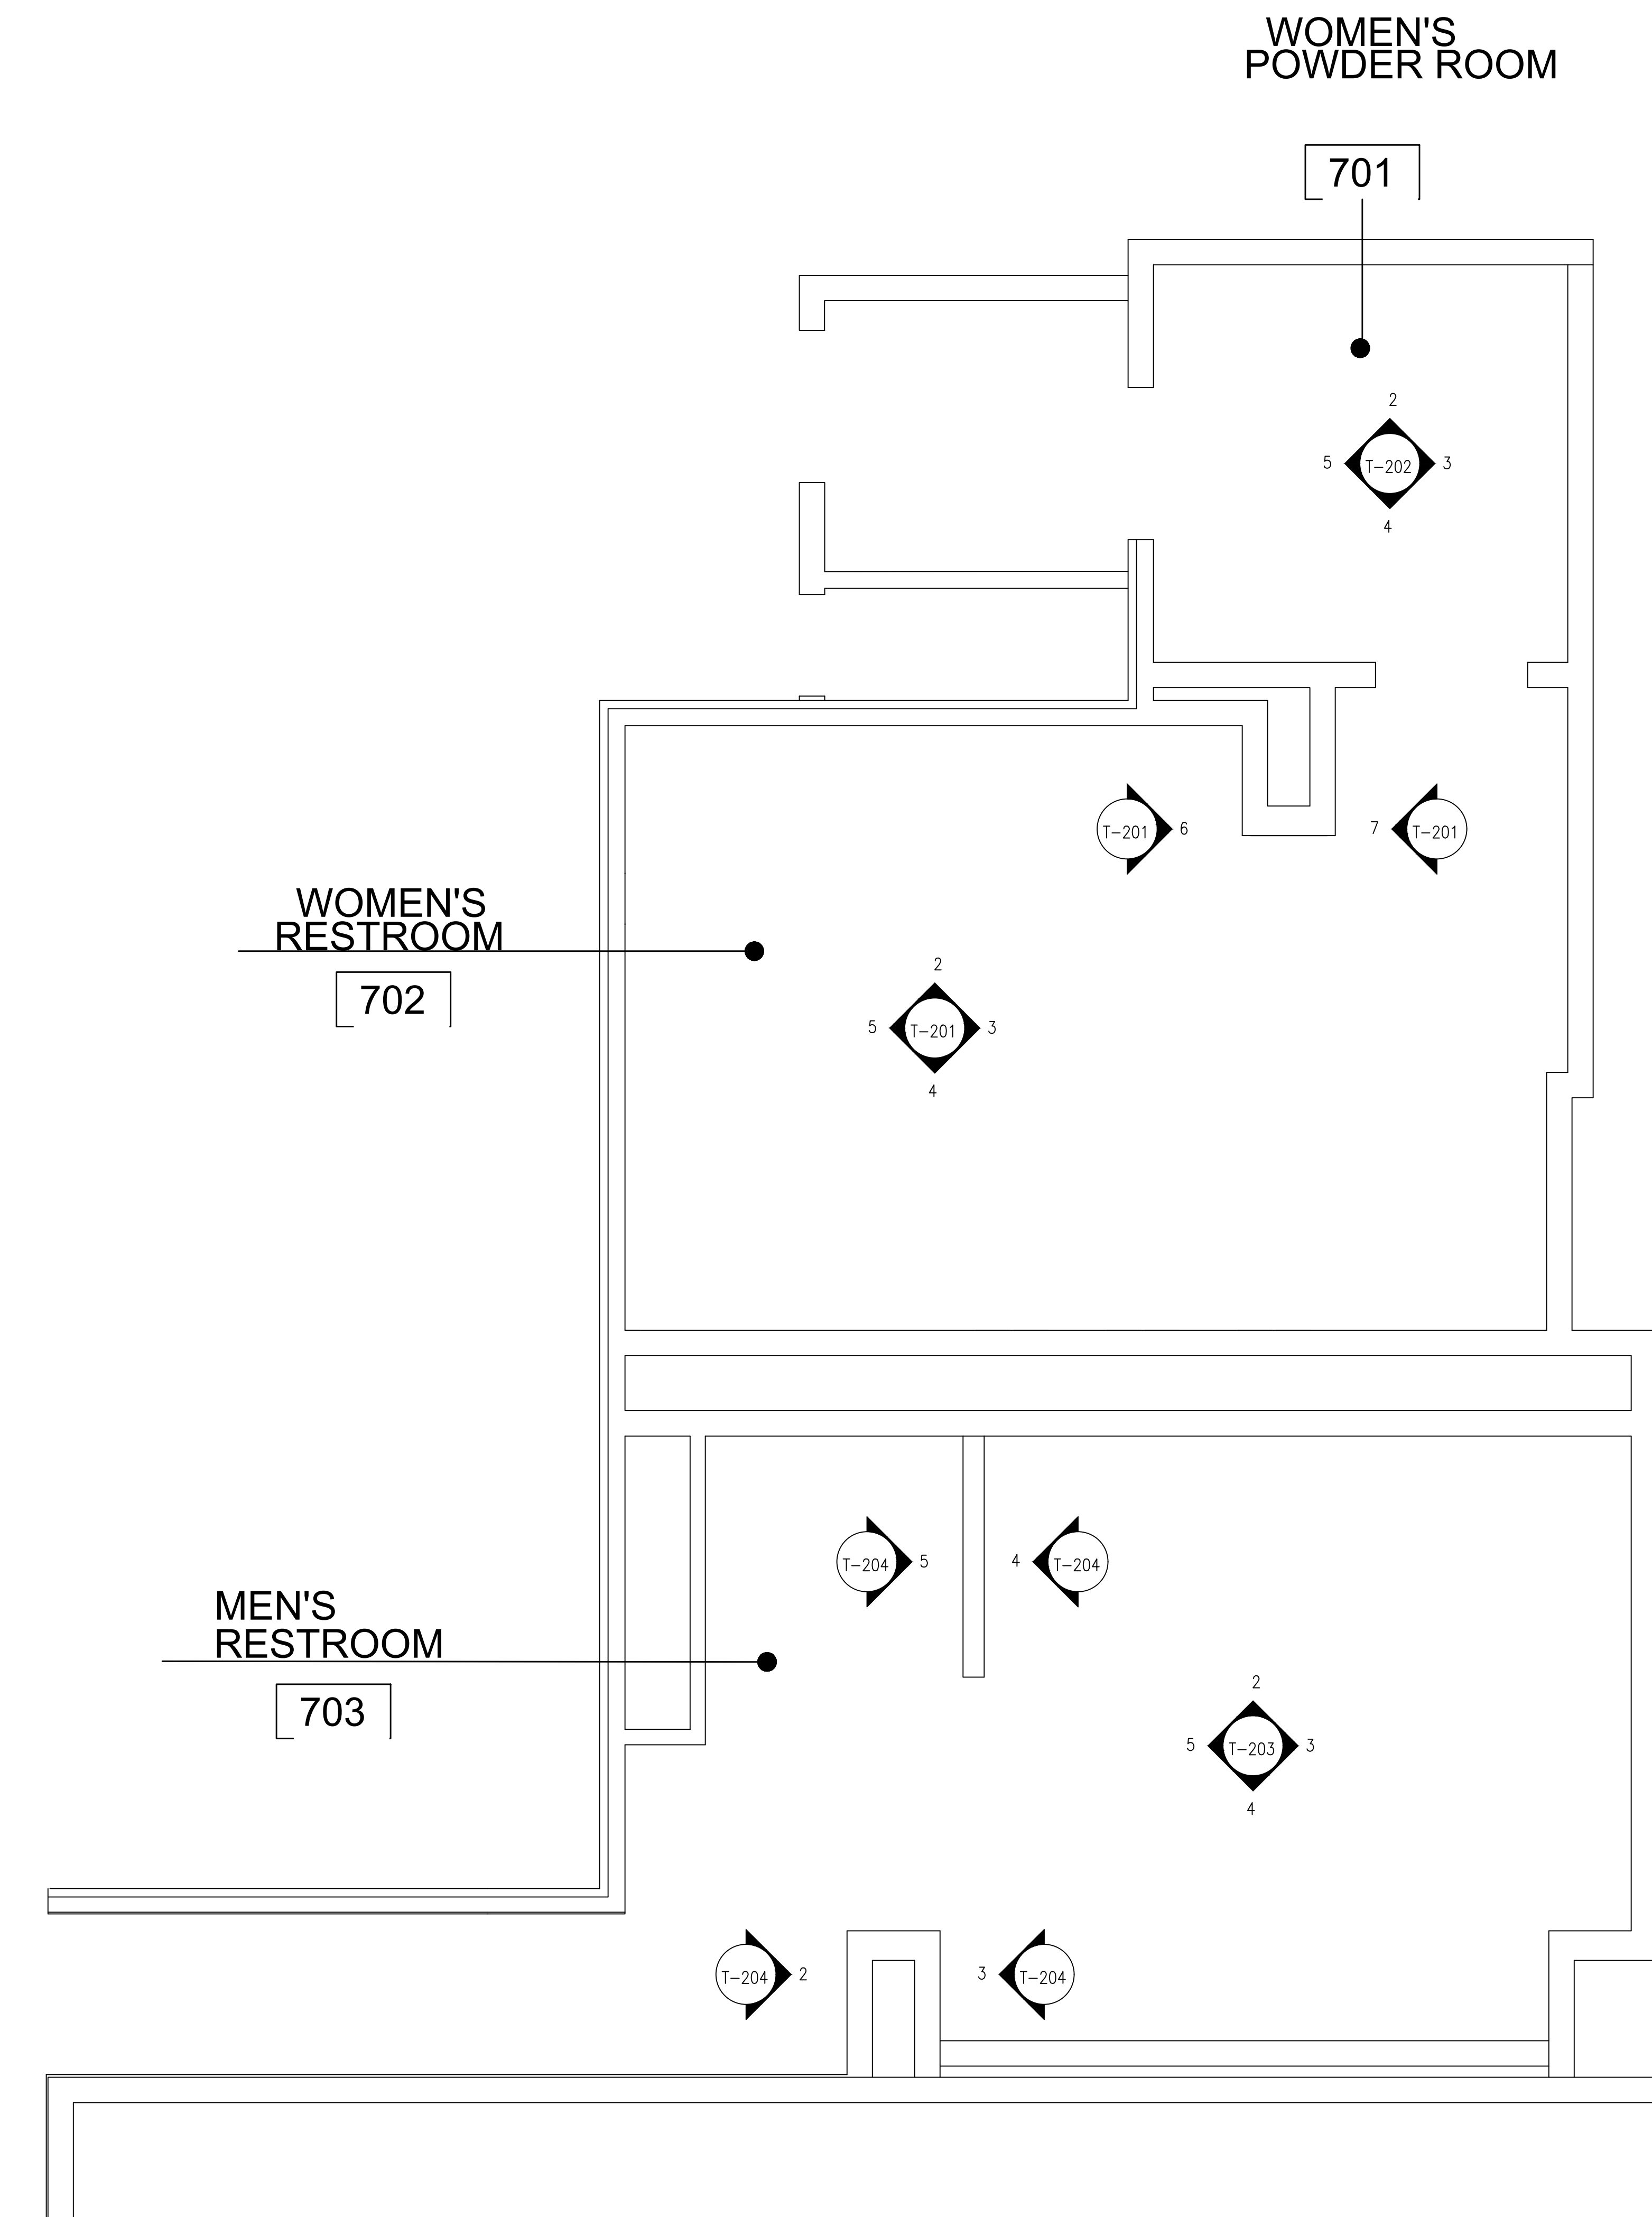

01
1/2"=1'-0" PLAN #2: 7TH FLOOR BATHROOMS

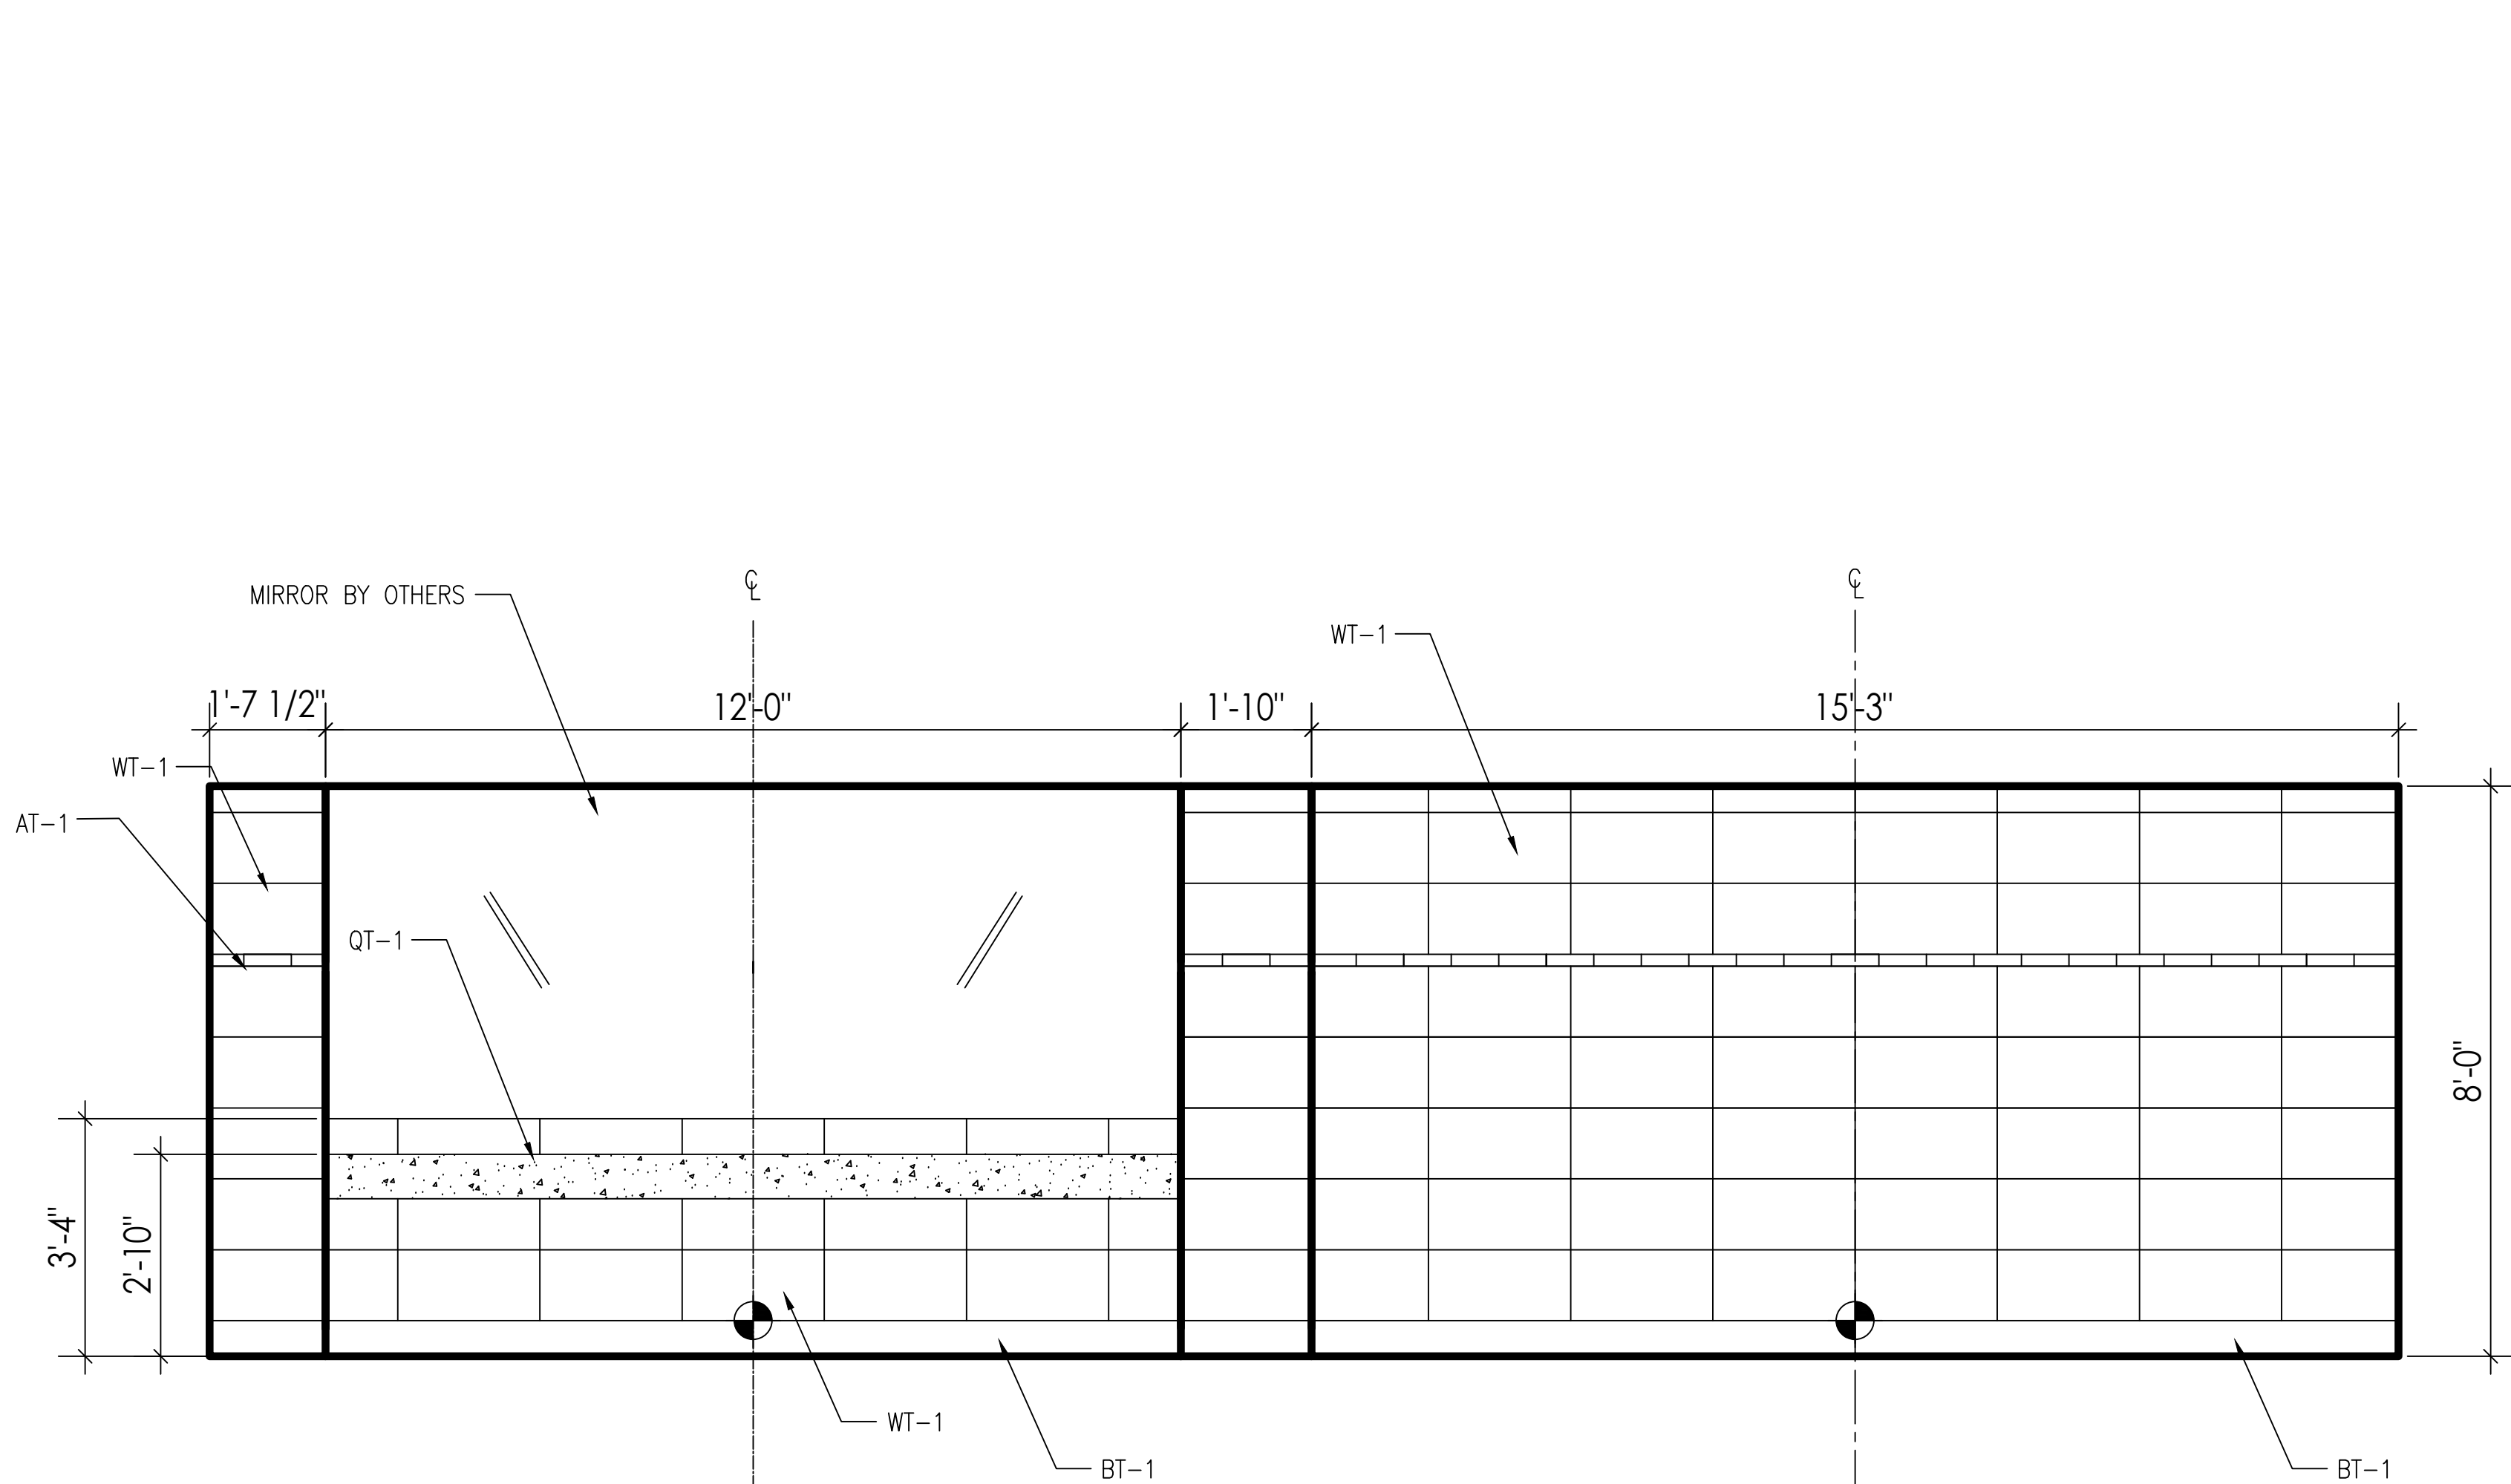

04
1/2"=1'-0" ELEVATIONS: 7TH FLOOR BATHROOMS

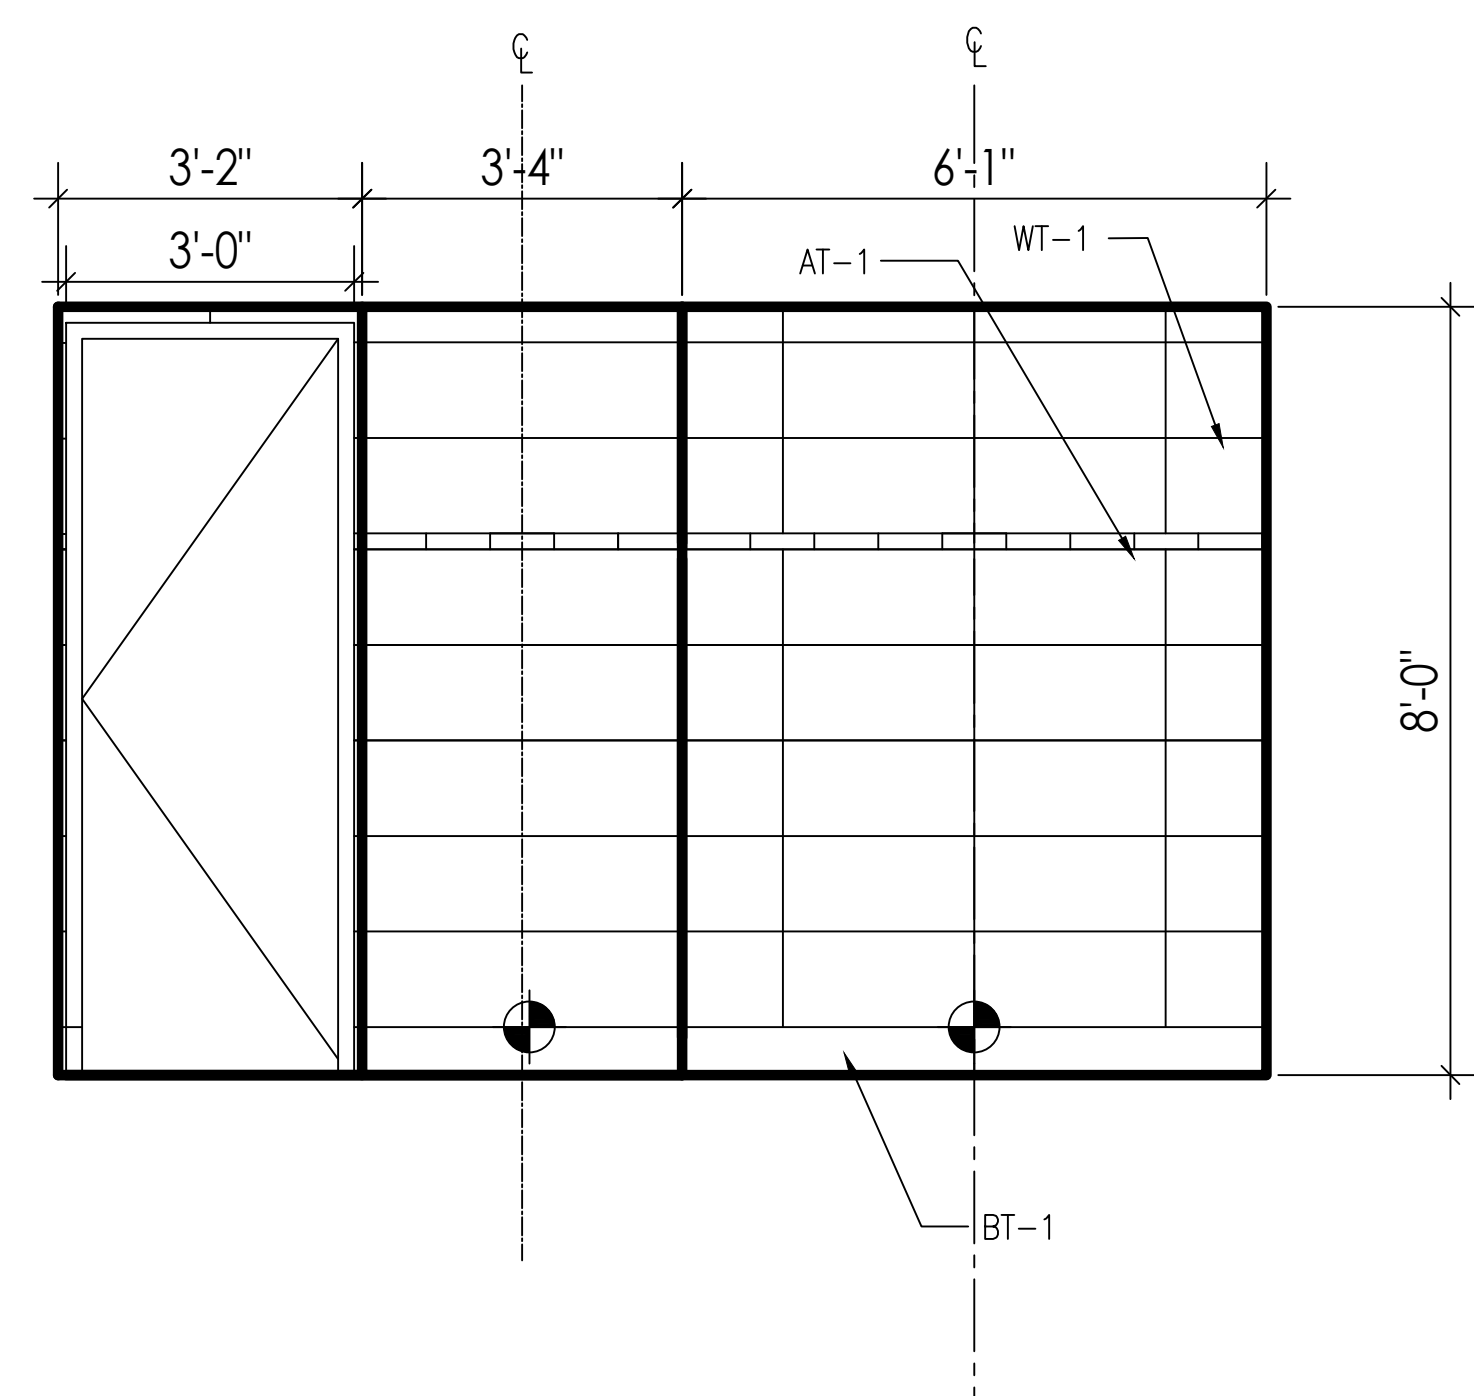

05
1/2"=1'-0" ELEVATIONS: 7TH FLOOR BATHROOMS

AUSTRO TILE & STONE, LLC
30-25 93RD STREET
EAST ELMHURST, NY 11369

CONTRACTOR:
JRM CONSTRUCTION
MANAGEMENT, LLC
242 WEST 36TH STREET
11TH FLOOR
NEW YORK, NY 10018

INTERIOR DESIGNER:

ISSUE FOR APPROVAL 10/09/23
ISSUE NAME DATE

ARCHITECT:
SPACESMITH
ONE NEW YORK PLAZA
NEW YORK, NY 10004
PH:212 260 5583

PROJECT NAME:
JACK RESNICK & SONS
255 GREENWICH STREET
NEW YORK, NY 10007

SHEET NAME:
ELEVATIONS
6TH FLOOR BATHROOMS

DATE:
PROJECT NO.:
PRINCIPAL:
DRAWING BY:
CHECKED BY:
SCALE:
DWG. No.:
T-203
11 of 29






STARTING POINT

(BT-1) TILE BASE GROUT JOINTS WILL NOT ALIGN WITH (WT-1) WALL TILE GROUT JOINTS

(AT-1) ACCENT WALL TILE GROUT JOINTS WILL NOT ALIGN WITH (WT-1) WALL TILE GROUT JOINTS


WOMEN'S
POWDER ROOM

701

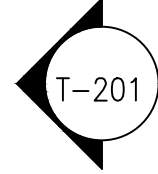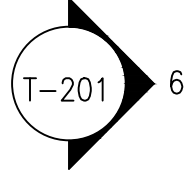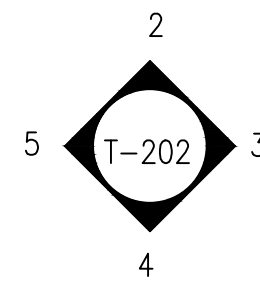







WOMEN'S
RESTROOM

702

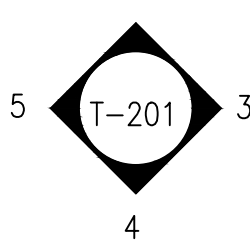



MEN'S
RESTROOM

703

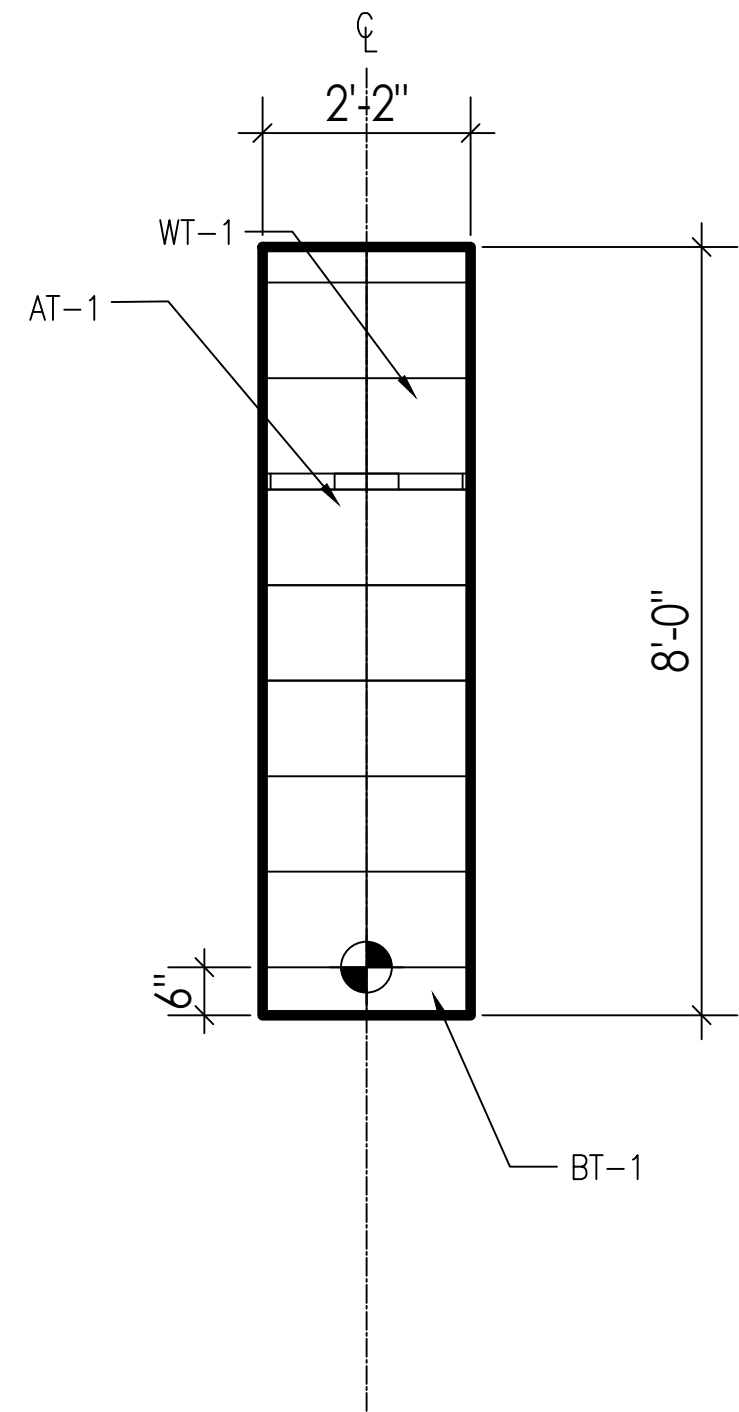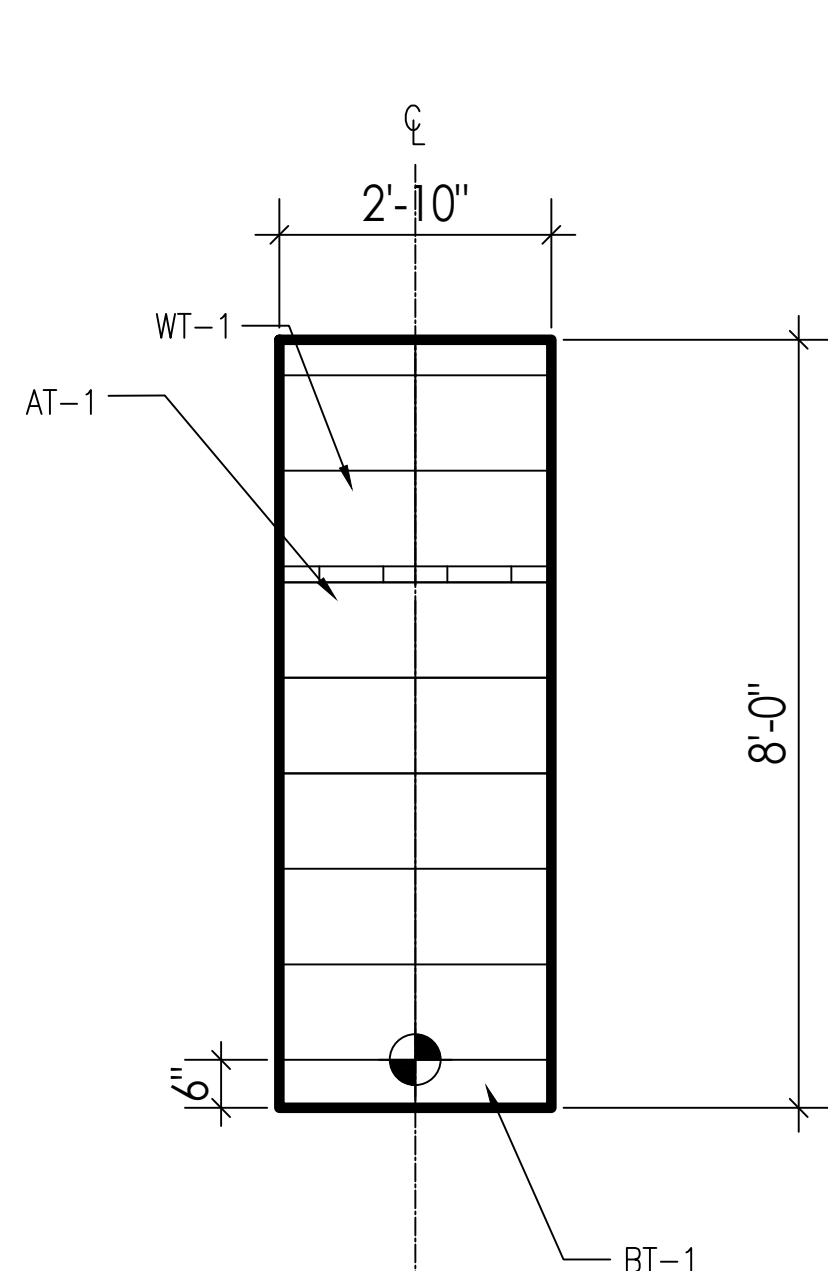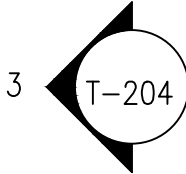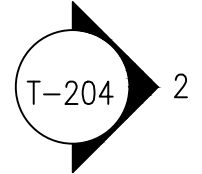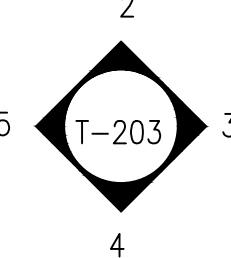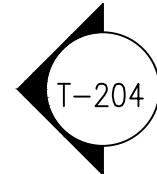

02
1/2"=1'-0" ELEVATIONS: 7TH FLOOR BATHROOMS

03
1/2"=1'-0" ELEVATIONS: 7TH FLOOR BATHROOMS

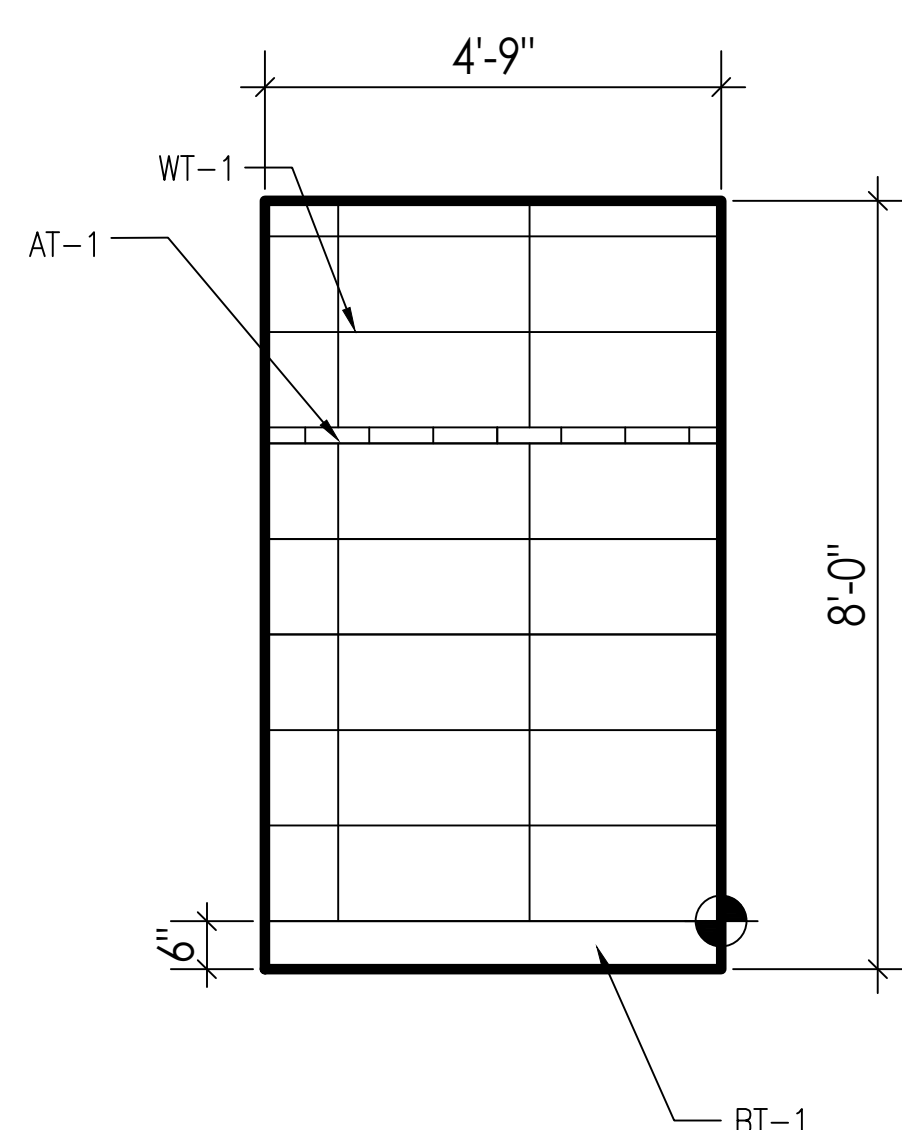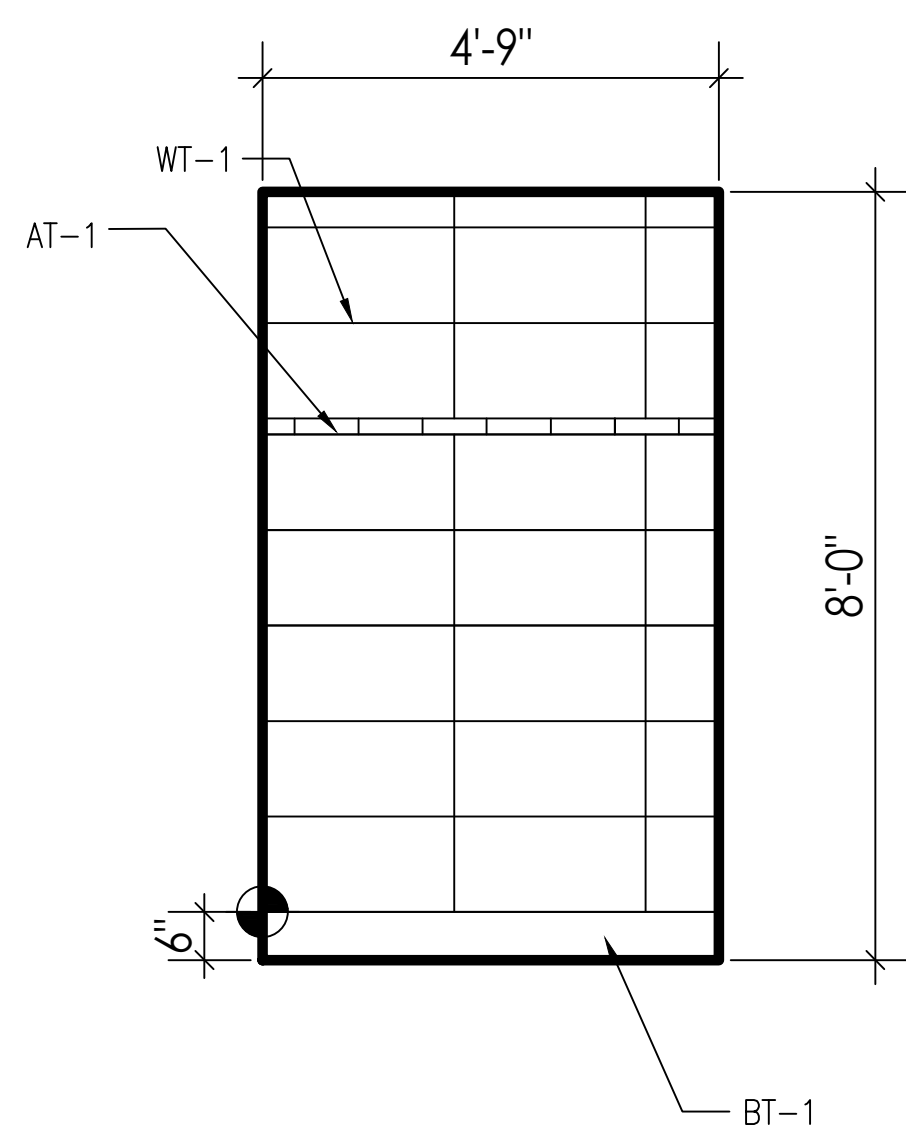

04
1/2"=1'-0" ELEVATIONS: 7TH FLOOR BATHROOMS

05
1/2"=1'-0" ELEVATIONS: 7TH FLOOR BATHROOMS

AUSTRO TILE & STONE, LLC
30-25 93RD STREET
EAST ELMHURST, NY 11369

CONTRACTOR:
JRM CONSTRUCTION
MANAGEMENT, LLC
242 WEST 36TH STREET
11TH FLOOR
NEW YORK, NY 10018

INTERIOR DESIGNER:

ISSUE FOR APPROVAL 10/09/23

ISSUE NAME DATE

ARCHITECT:




SPACESMITH
ONE NEW YORK PLAZA
NEW YORK, NY 10004
PH:212 260 5583

PROJECT NAME:
JACK RESNICK & SONS
255 GREENWICH STREET
NEW YORK, NY 10007

SHEET NAME:
ELEVATIONS
6TH FLOOR BATHROOMS

DATE:
PROJECT NO.:
PRINCIPAL:
DRAWING BY:
CHECKED BY:
SCALE:
DWG. No.:
T-204

12 of 29

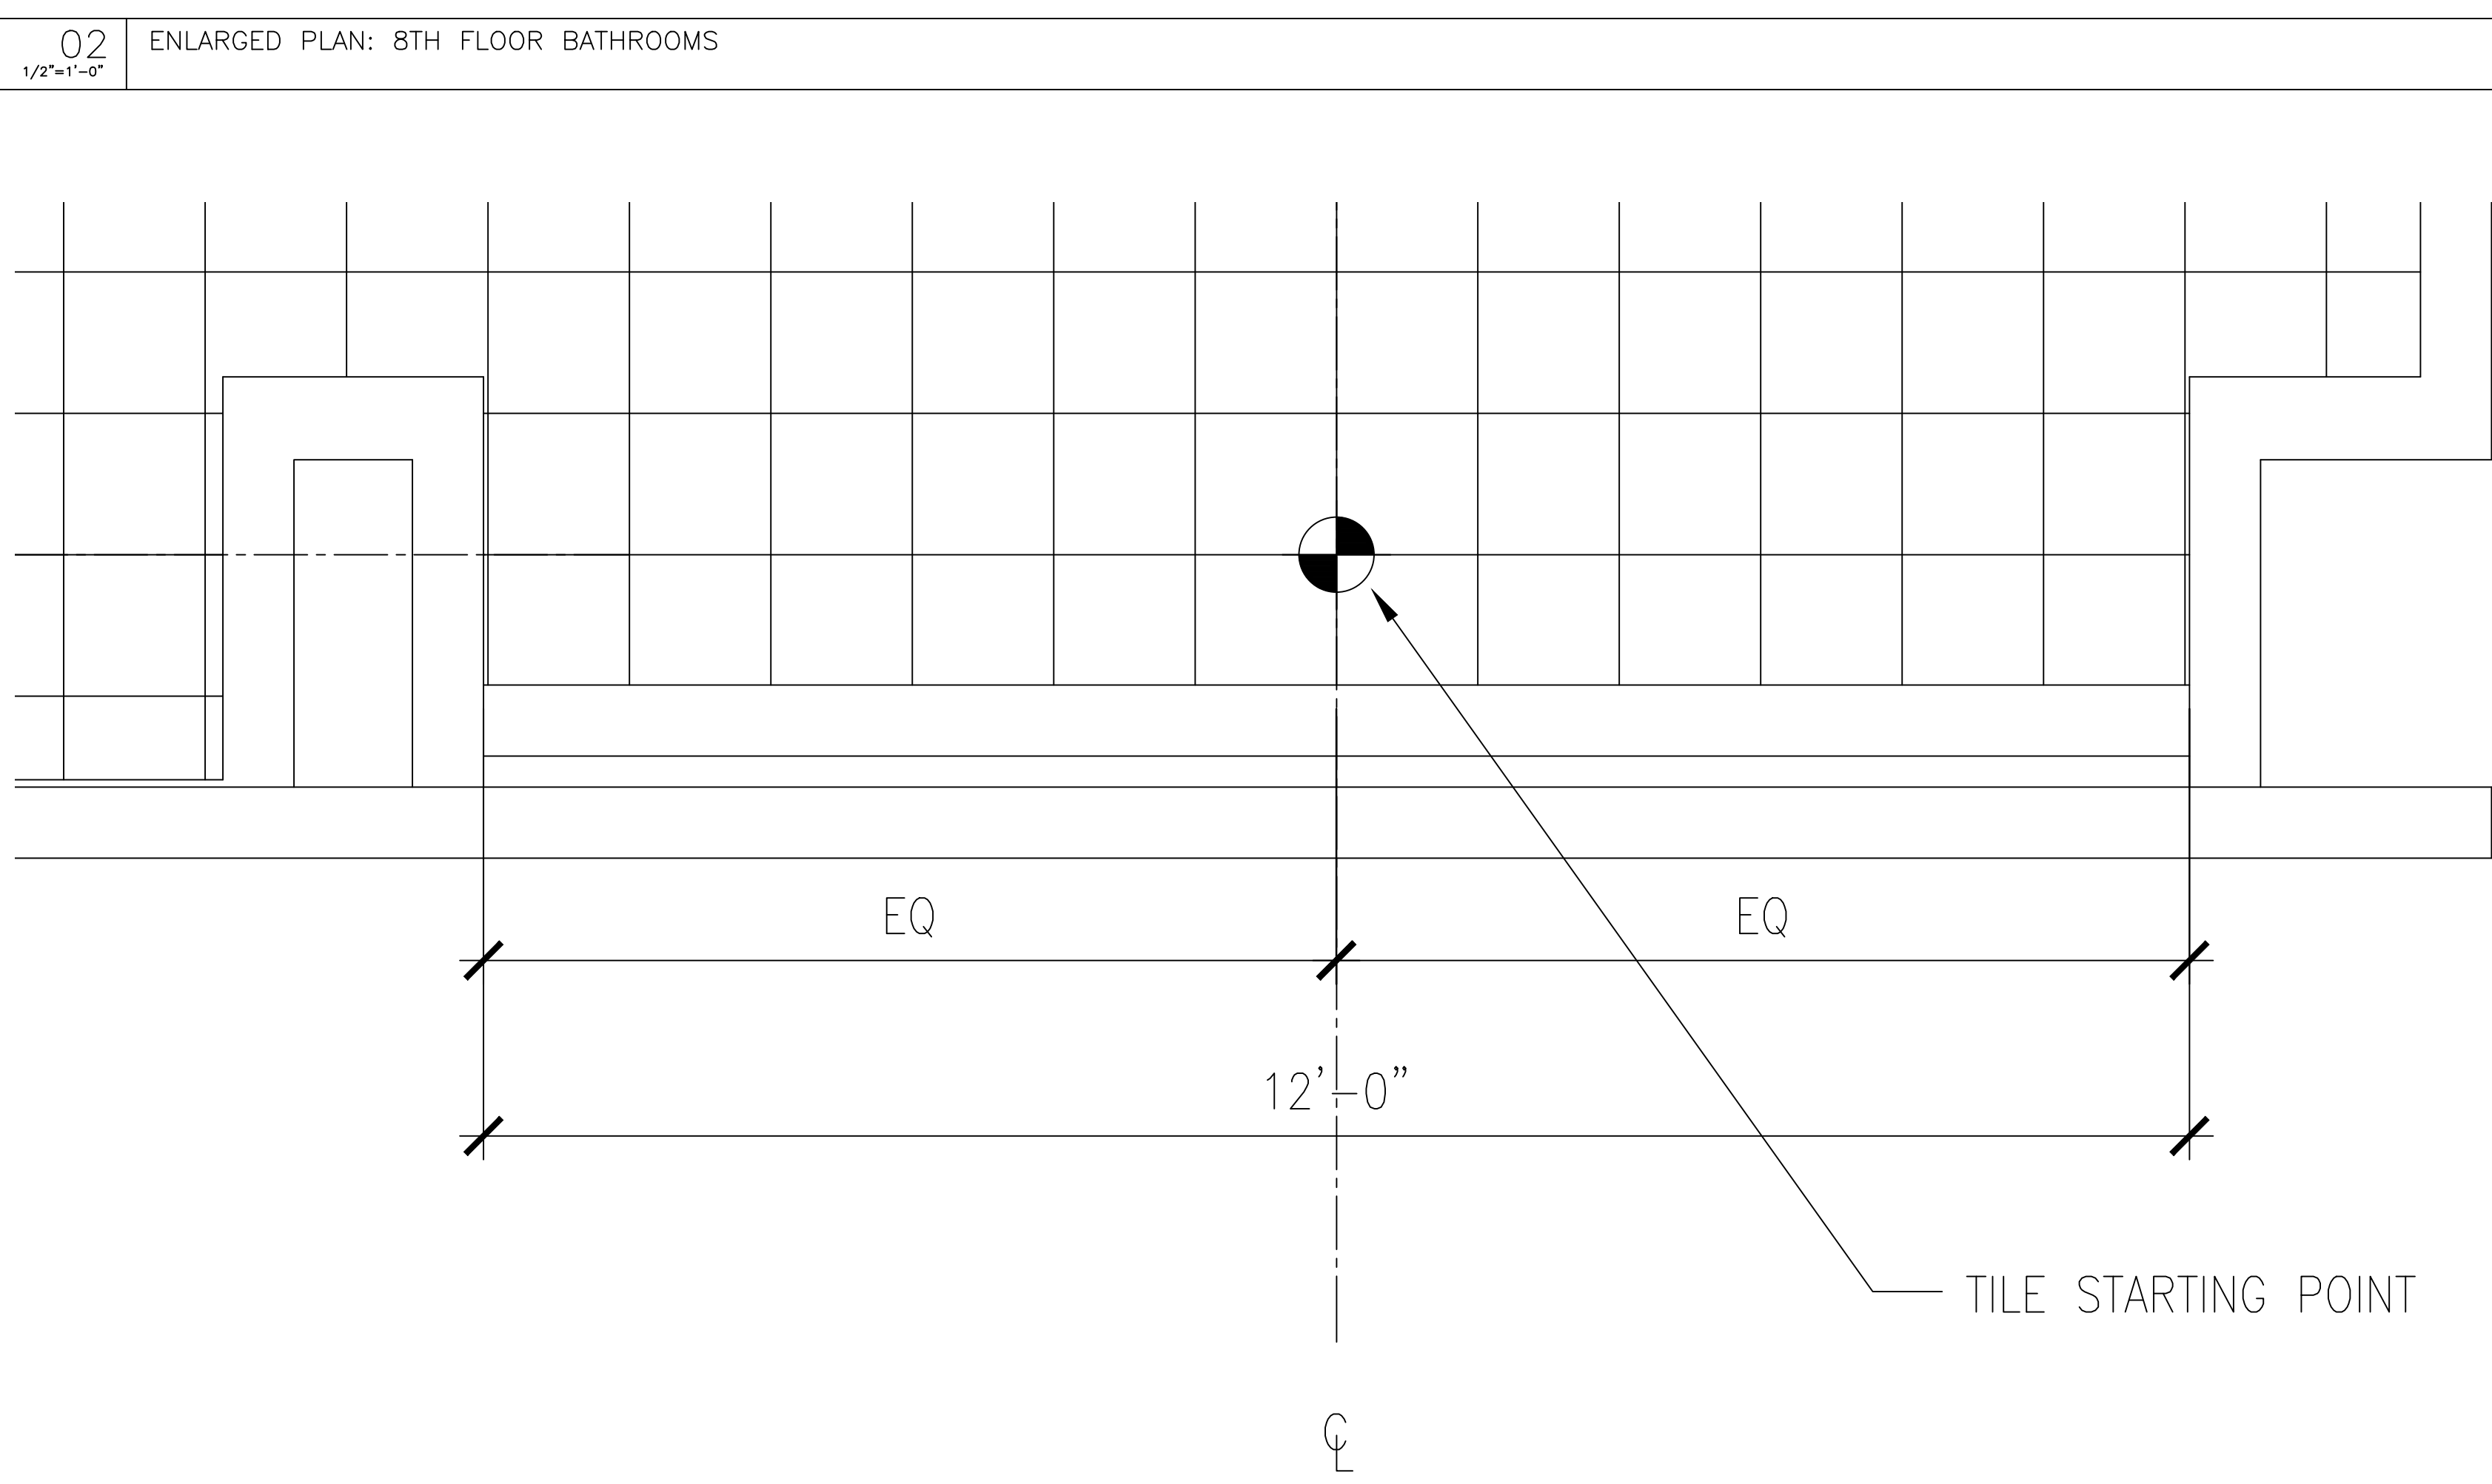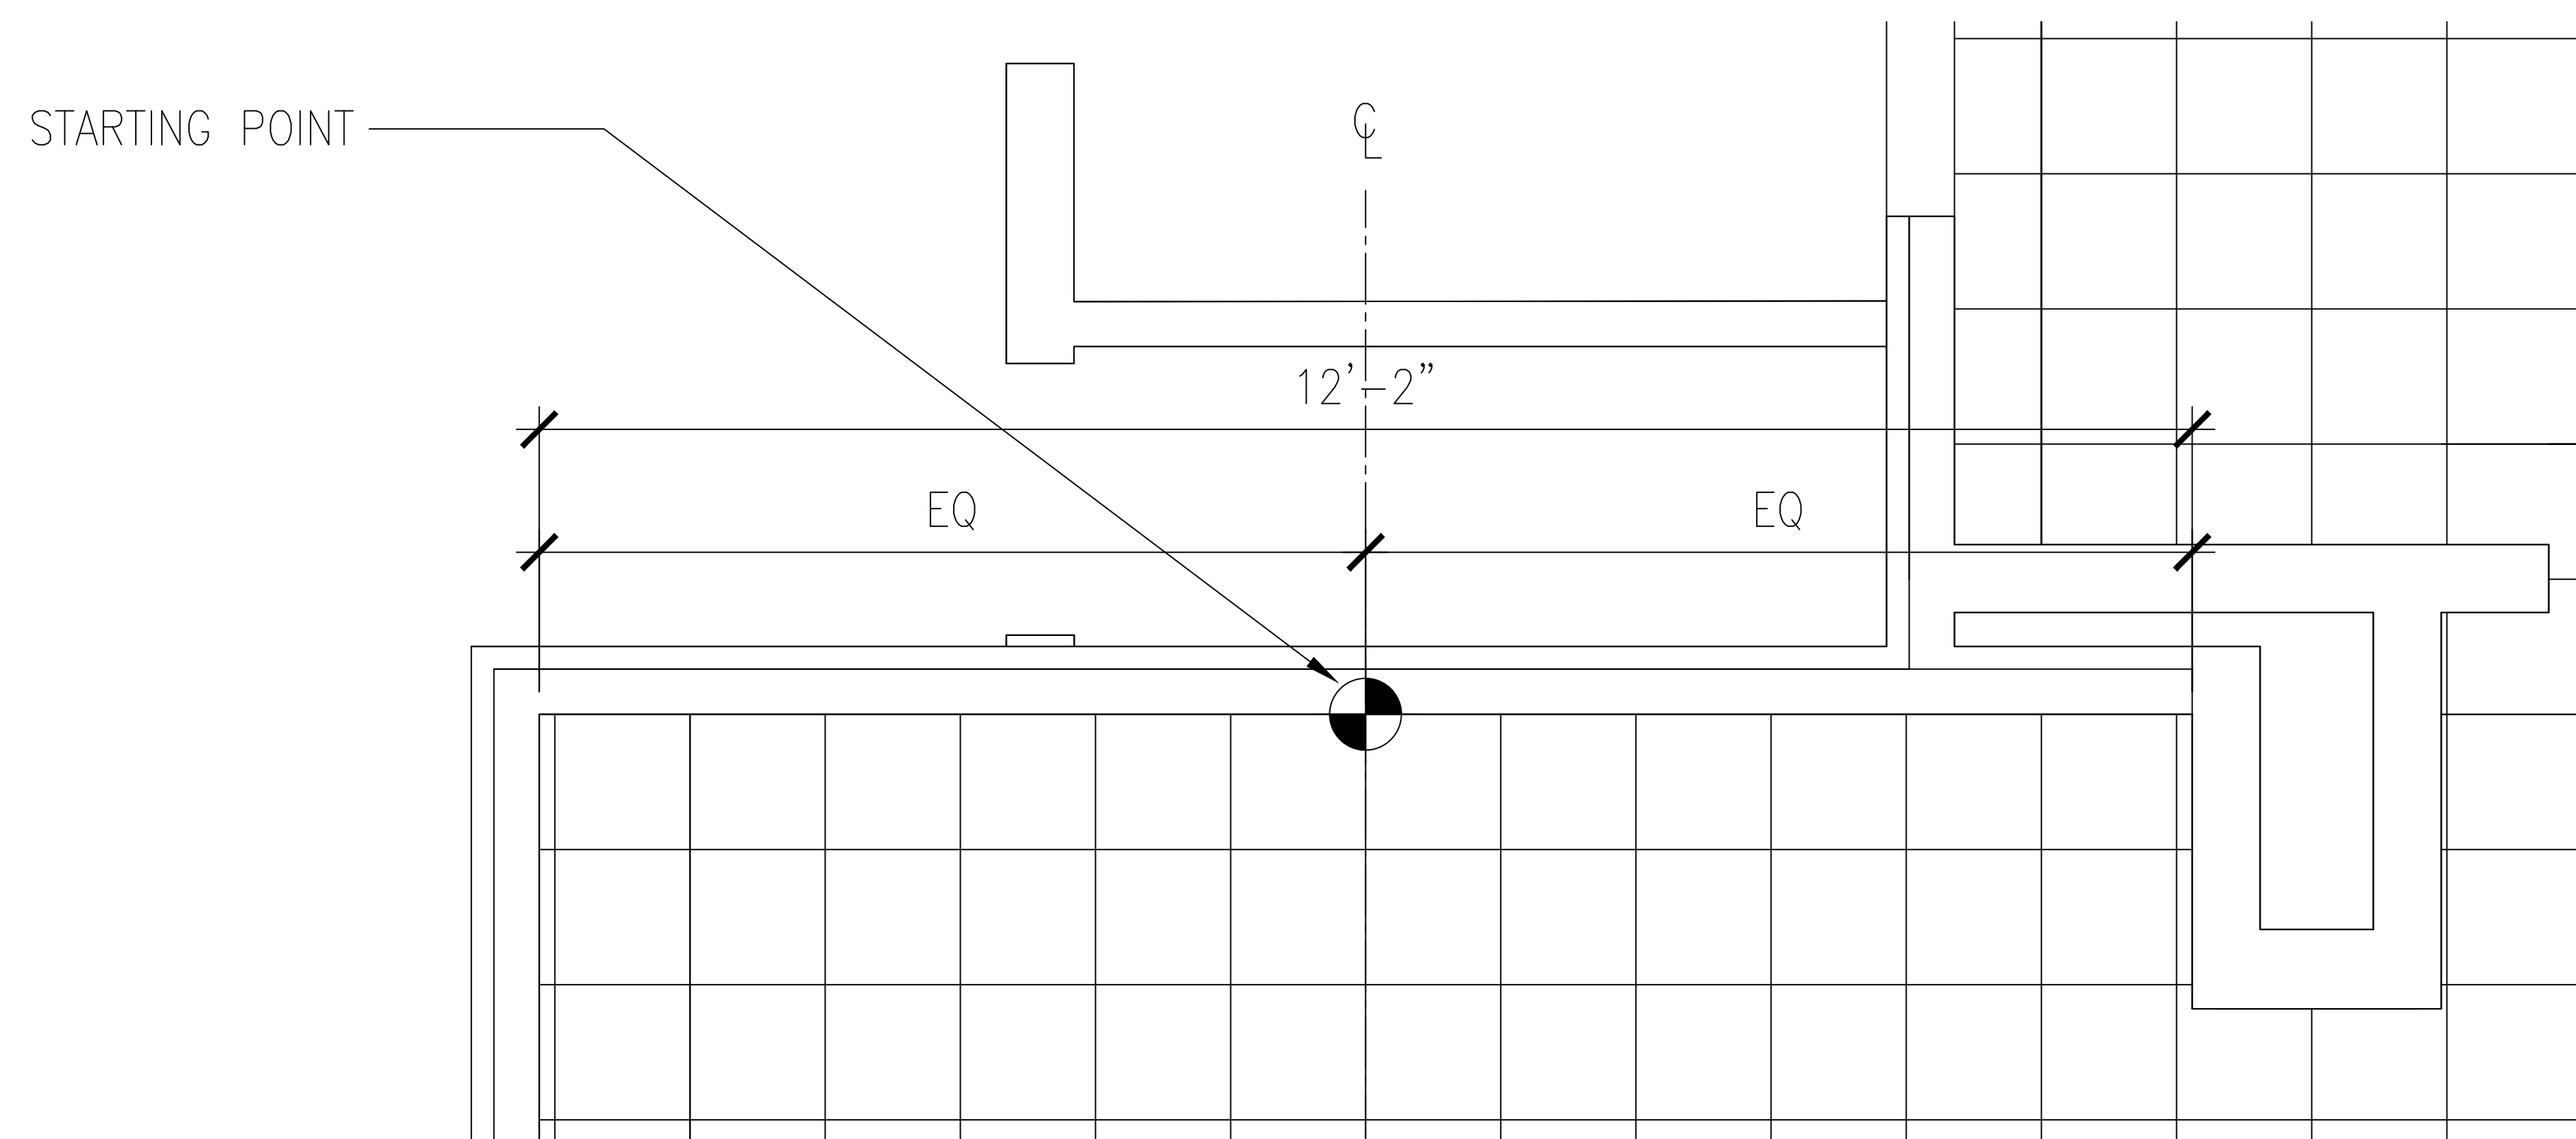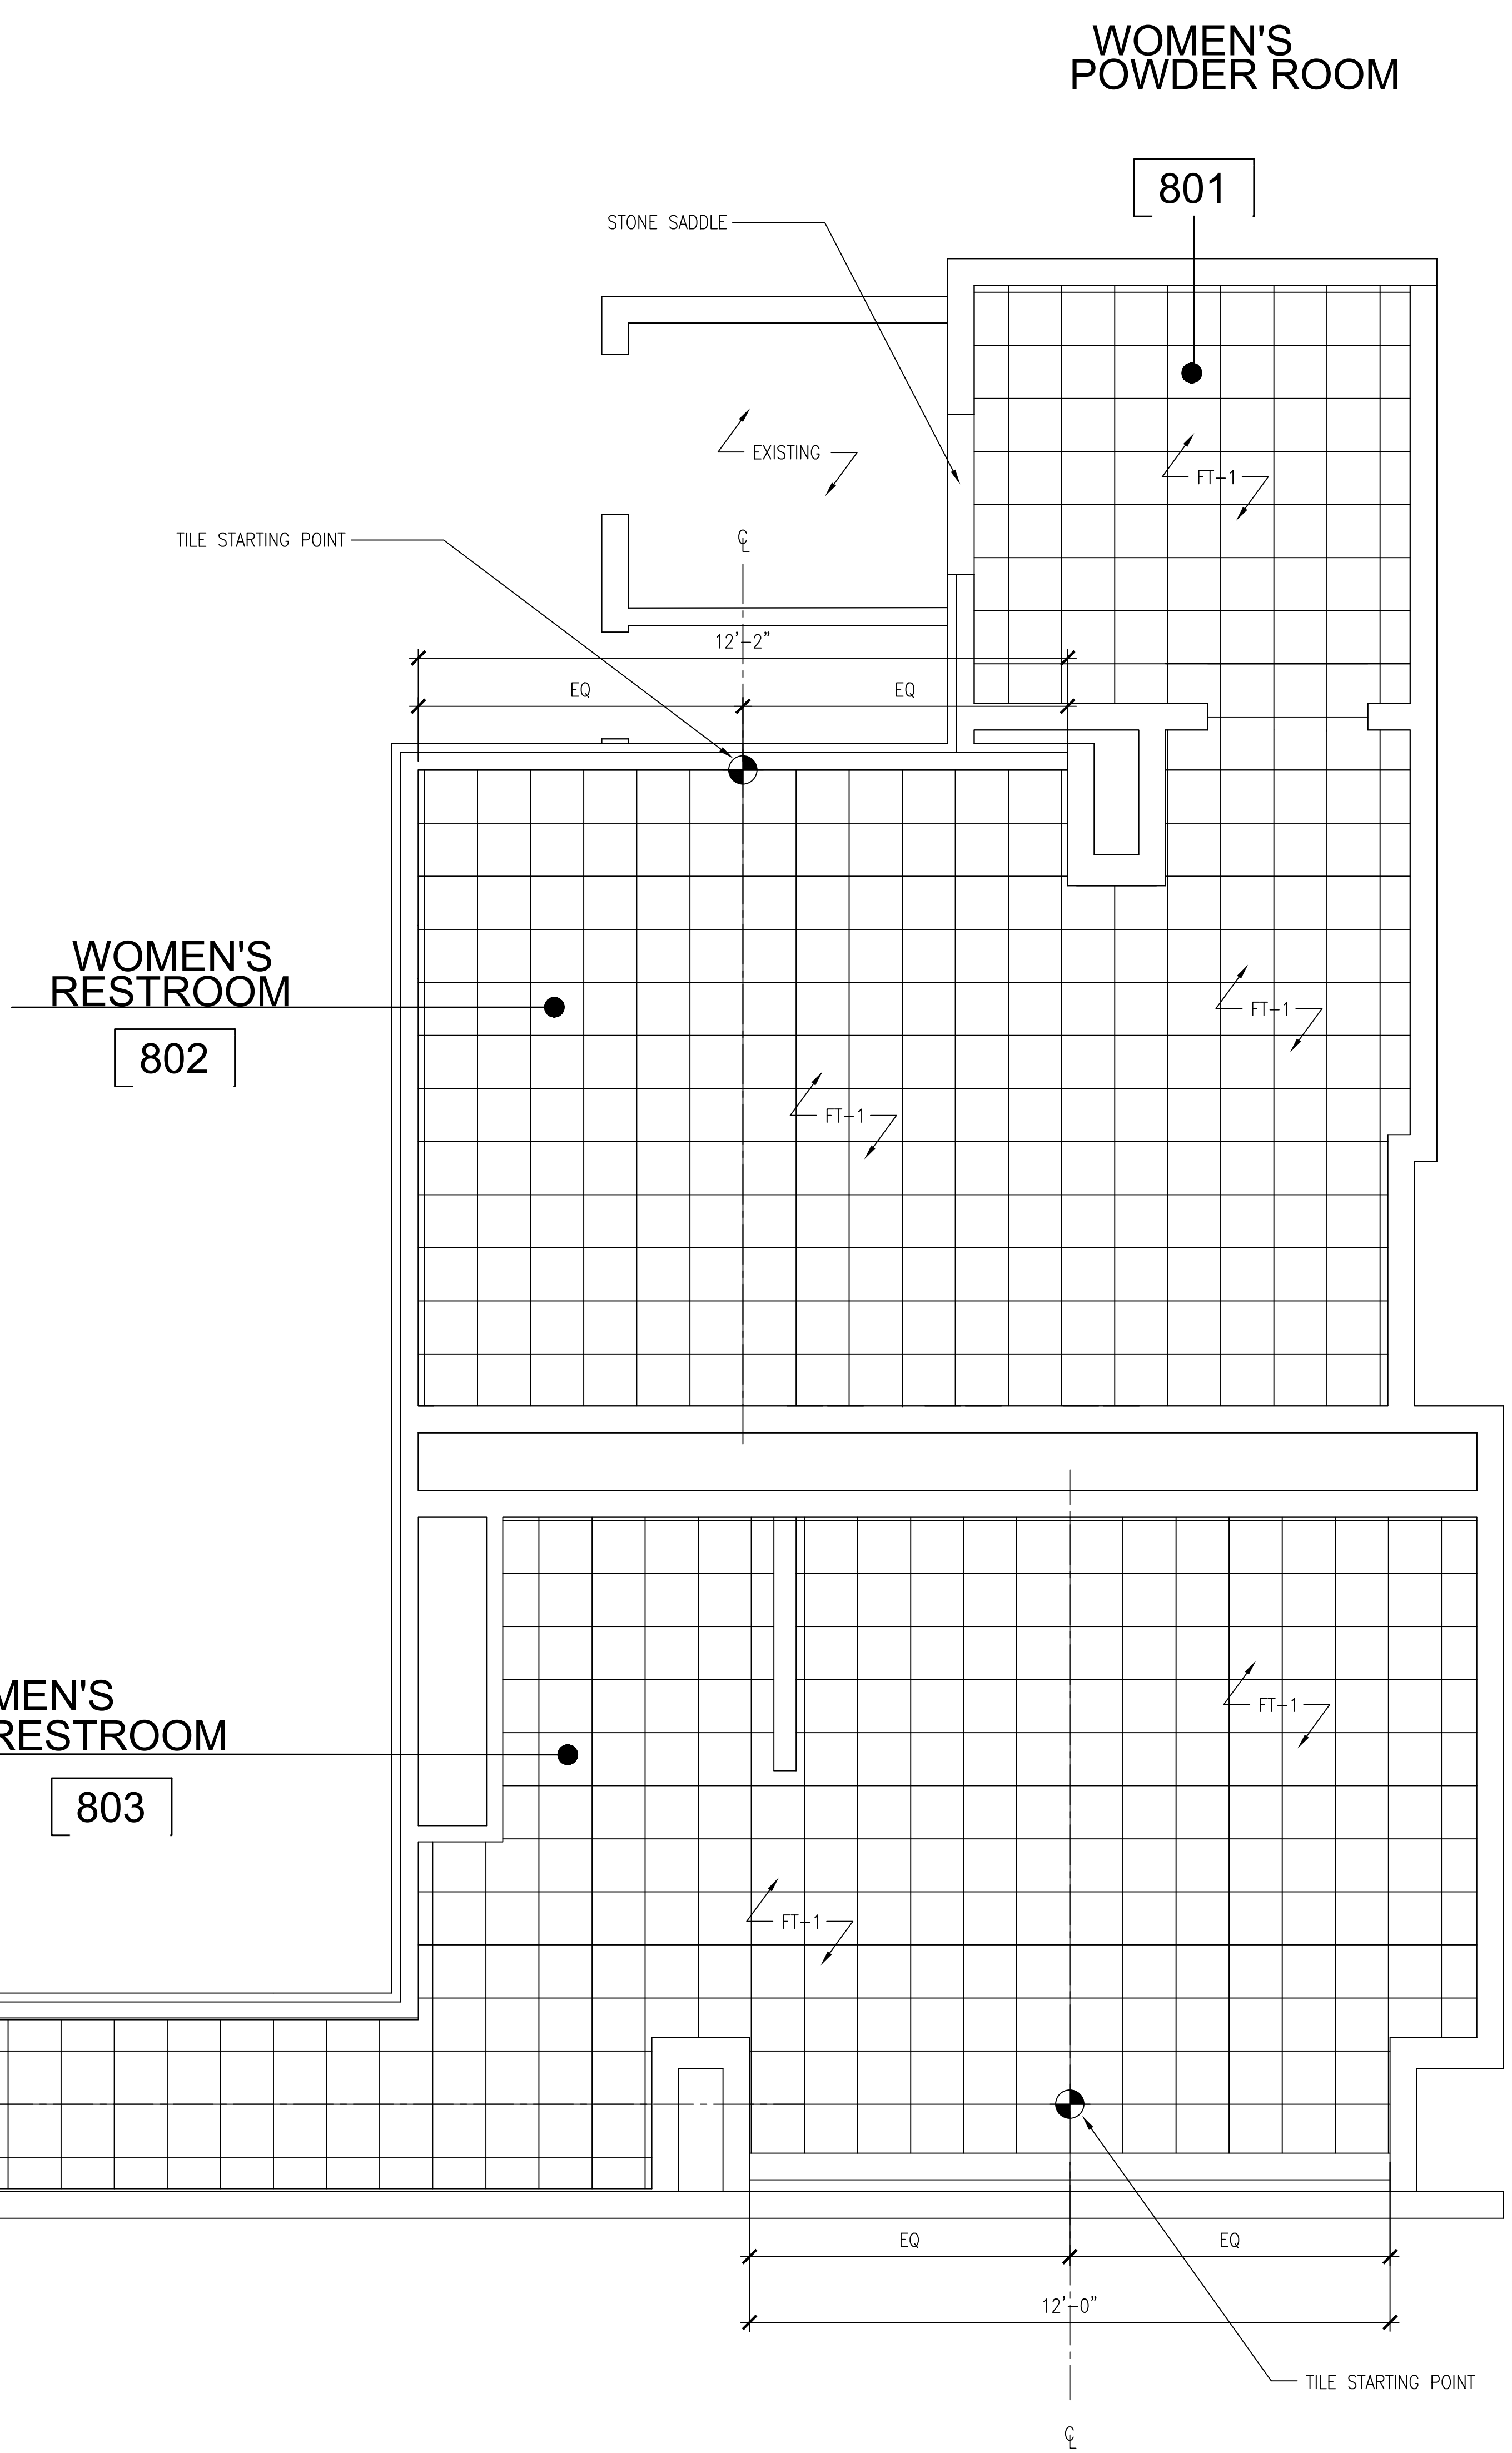

CONTRACTOR:
JRM CONSTRUCTION
MANAGEMENT, LLC
242 WEST 36TH STREET
11TH FLOOR
NEW YORK, NY 10018

INTERIOR DESIGNER:

ISSUE FOR APPROVAL 10/09/23
ISSUE NAME DATE

ARCHITECT:
SPACESMITH
ONE NEW YORK PLAZA
NEW YORK, NY 10004
PH:212 260 5583

PROJECT NAME:
JACK RESNICK & SONS
255 GREENWICH STREET
NEW YORK, NY 10007

SHEET NAME:
PLAN
8TH FLOOR BATHROOMS




DATE:
PROJECT NO.:
PRINCIPAL:
DRAWING BY:
CHECKED BY:
SCALE:
DWG. No.:
T-300
13 of 29



(BT-1) TILE BASE GROUT JOINTS WILL NOT ALIGN WITH (WT-1) WALL TILE GROUT JOINTS

(AT-1) ACCENT WALL TILE GROUT JOINTS WILL NOT ALIGN WITH (WT-1) WALL TILE GROUT JOINTS

AUSTRO TILE & STONE, LLC
30-25 93RD STREET
EAST ELMHURST, NY 11369

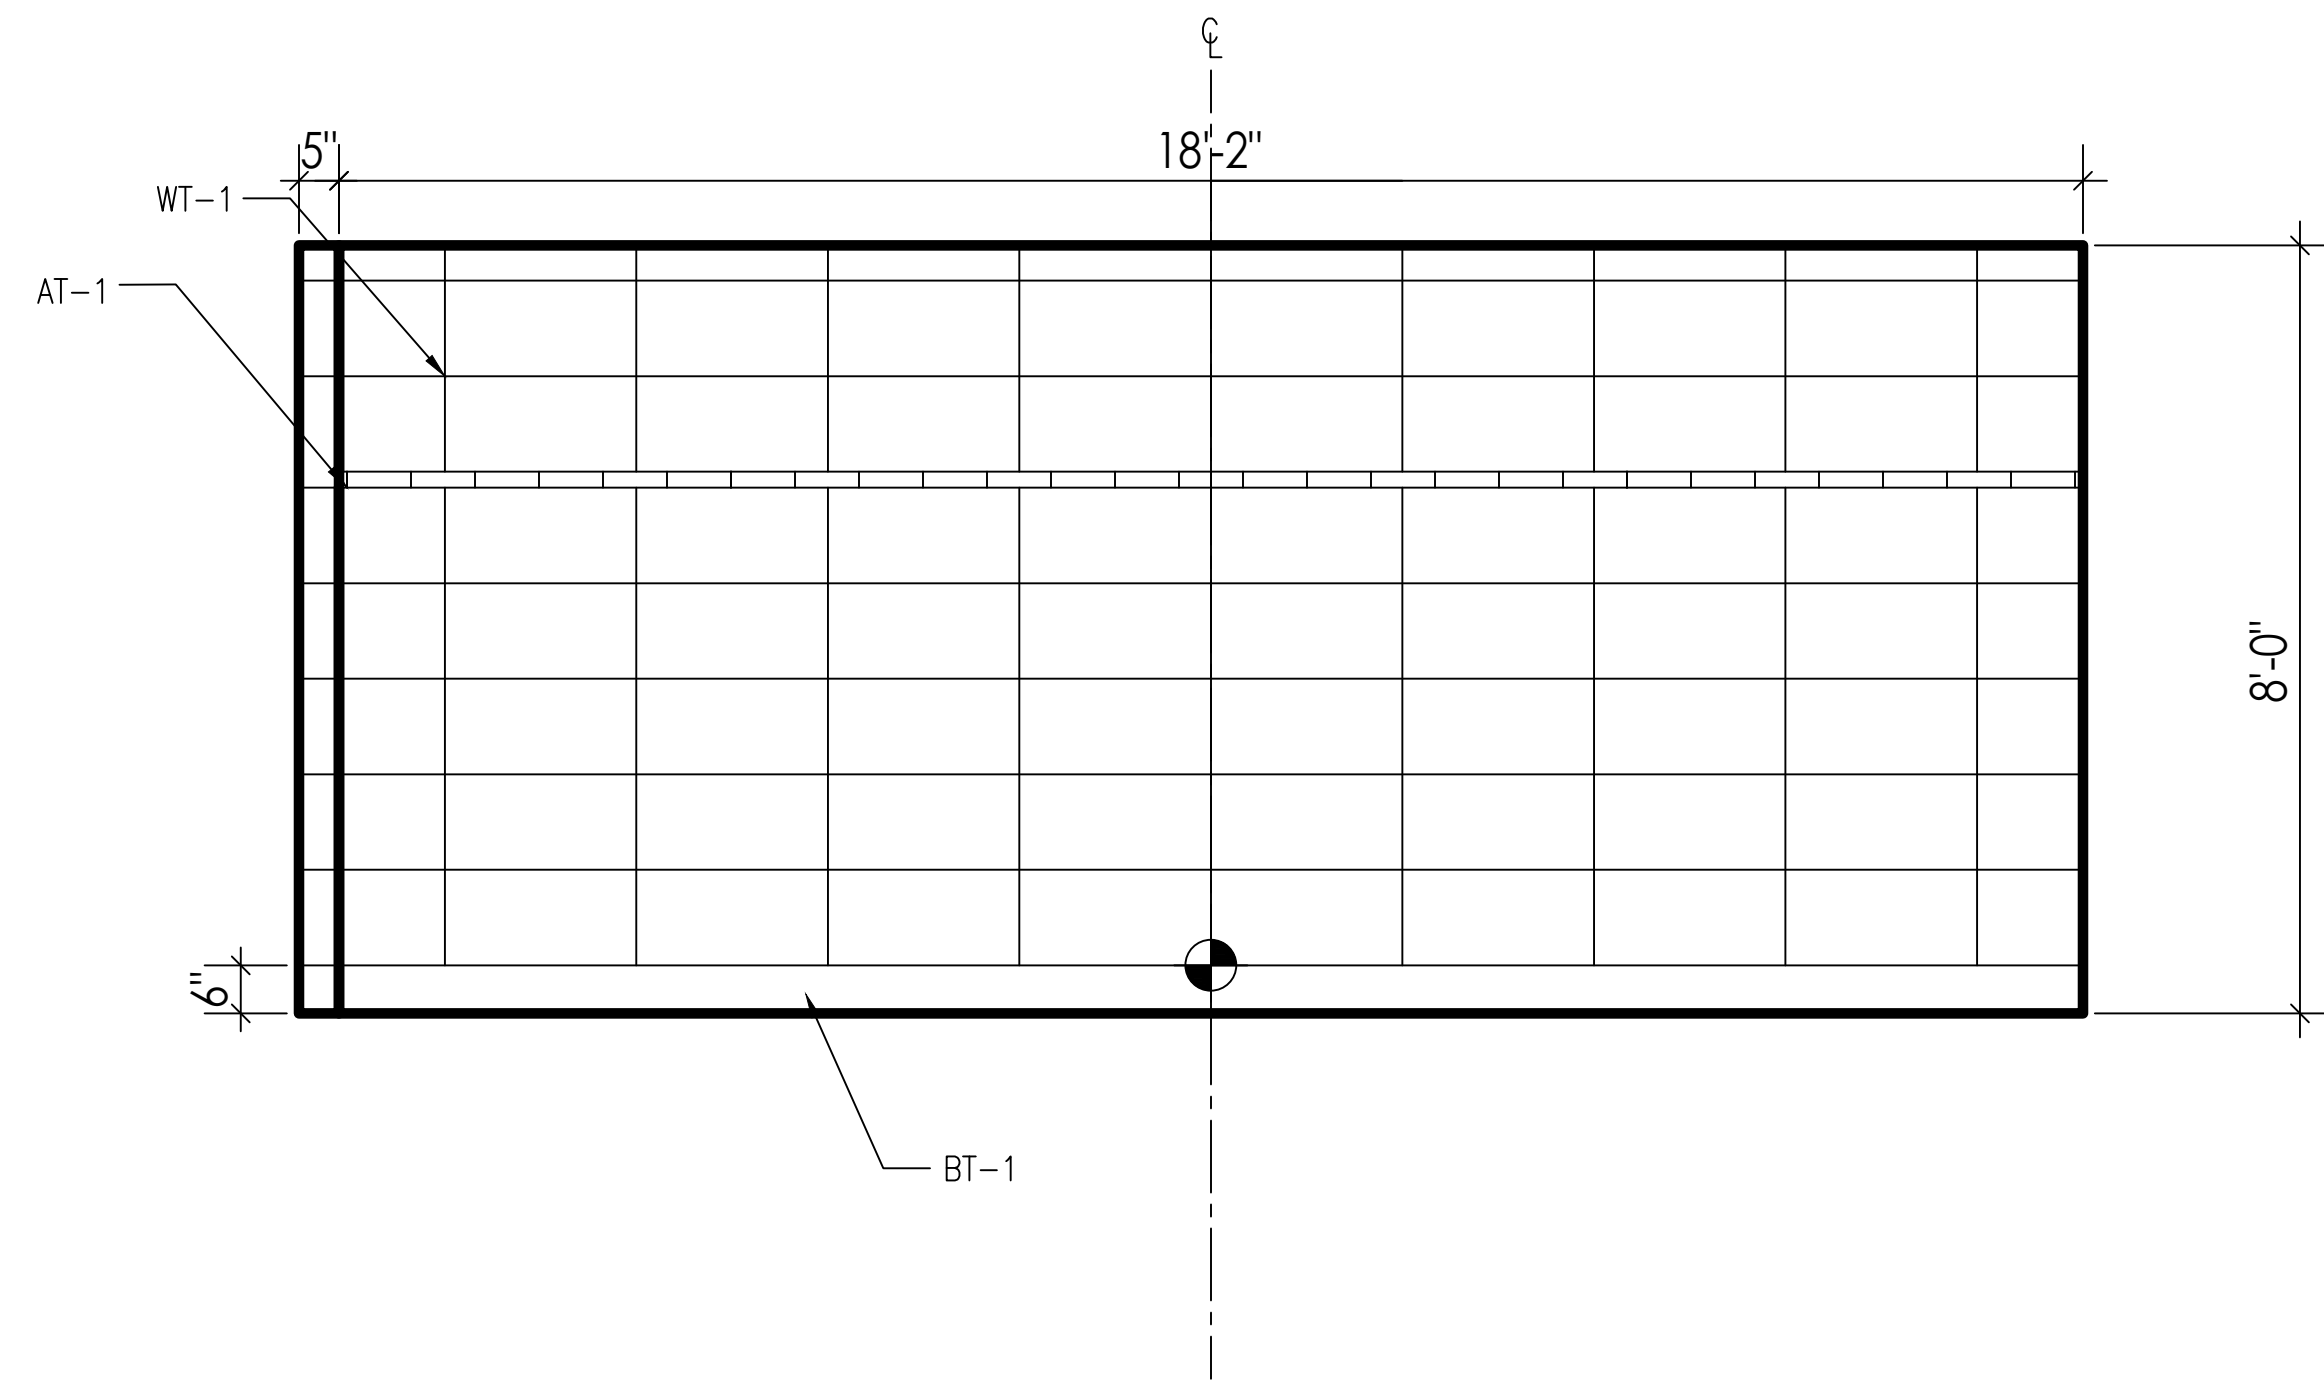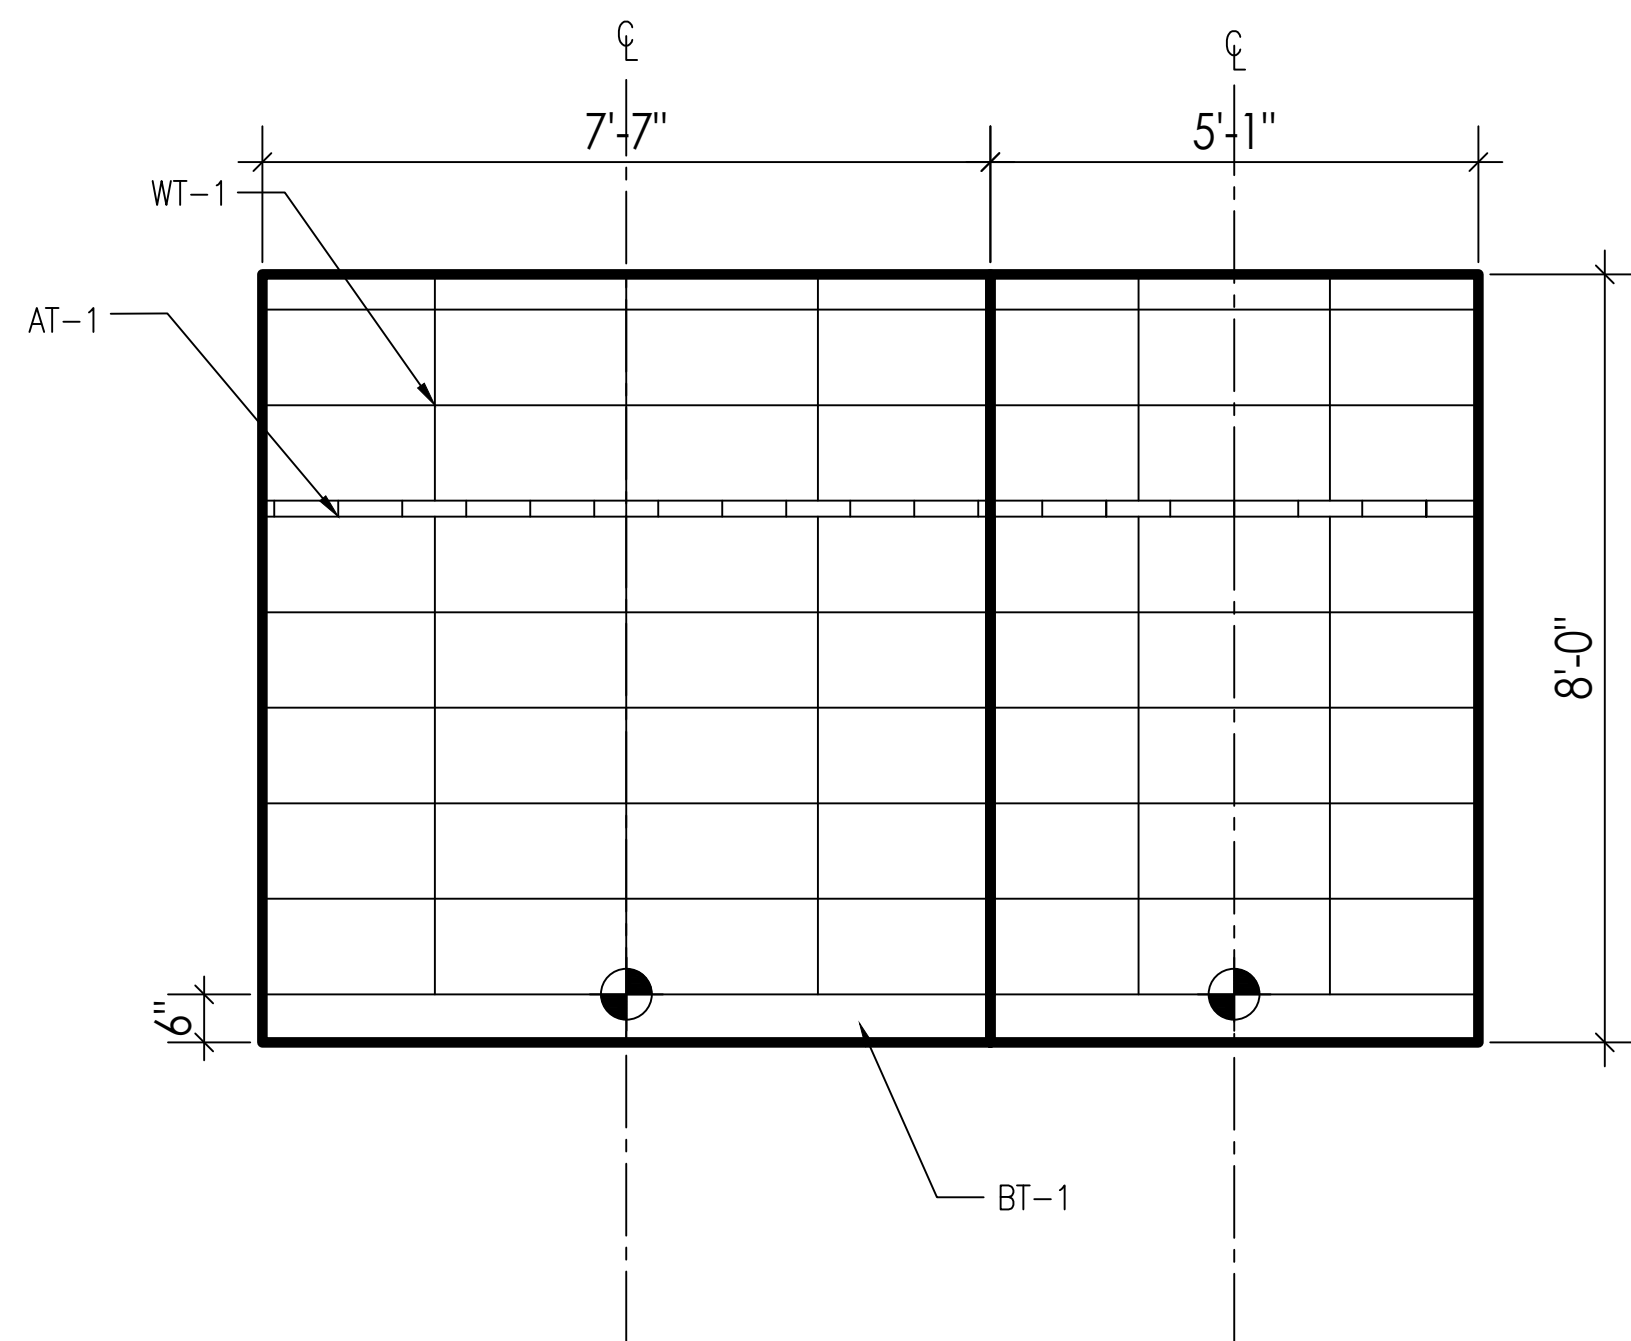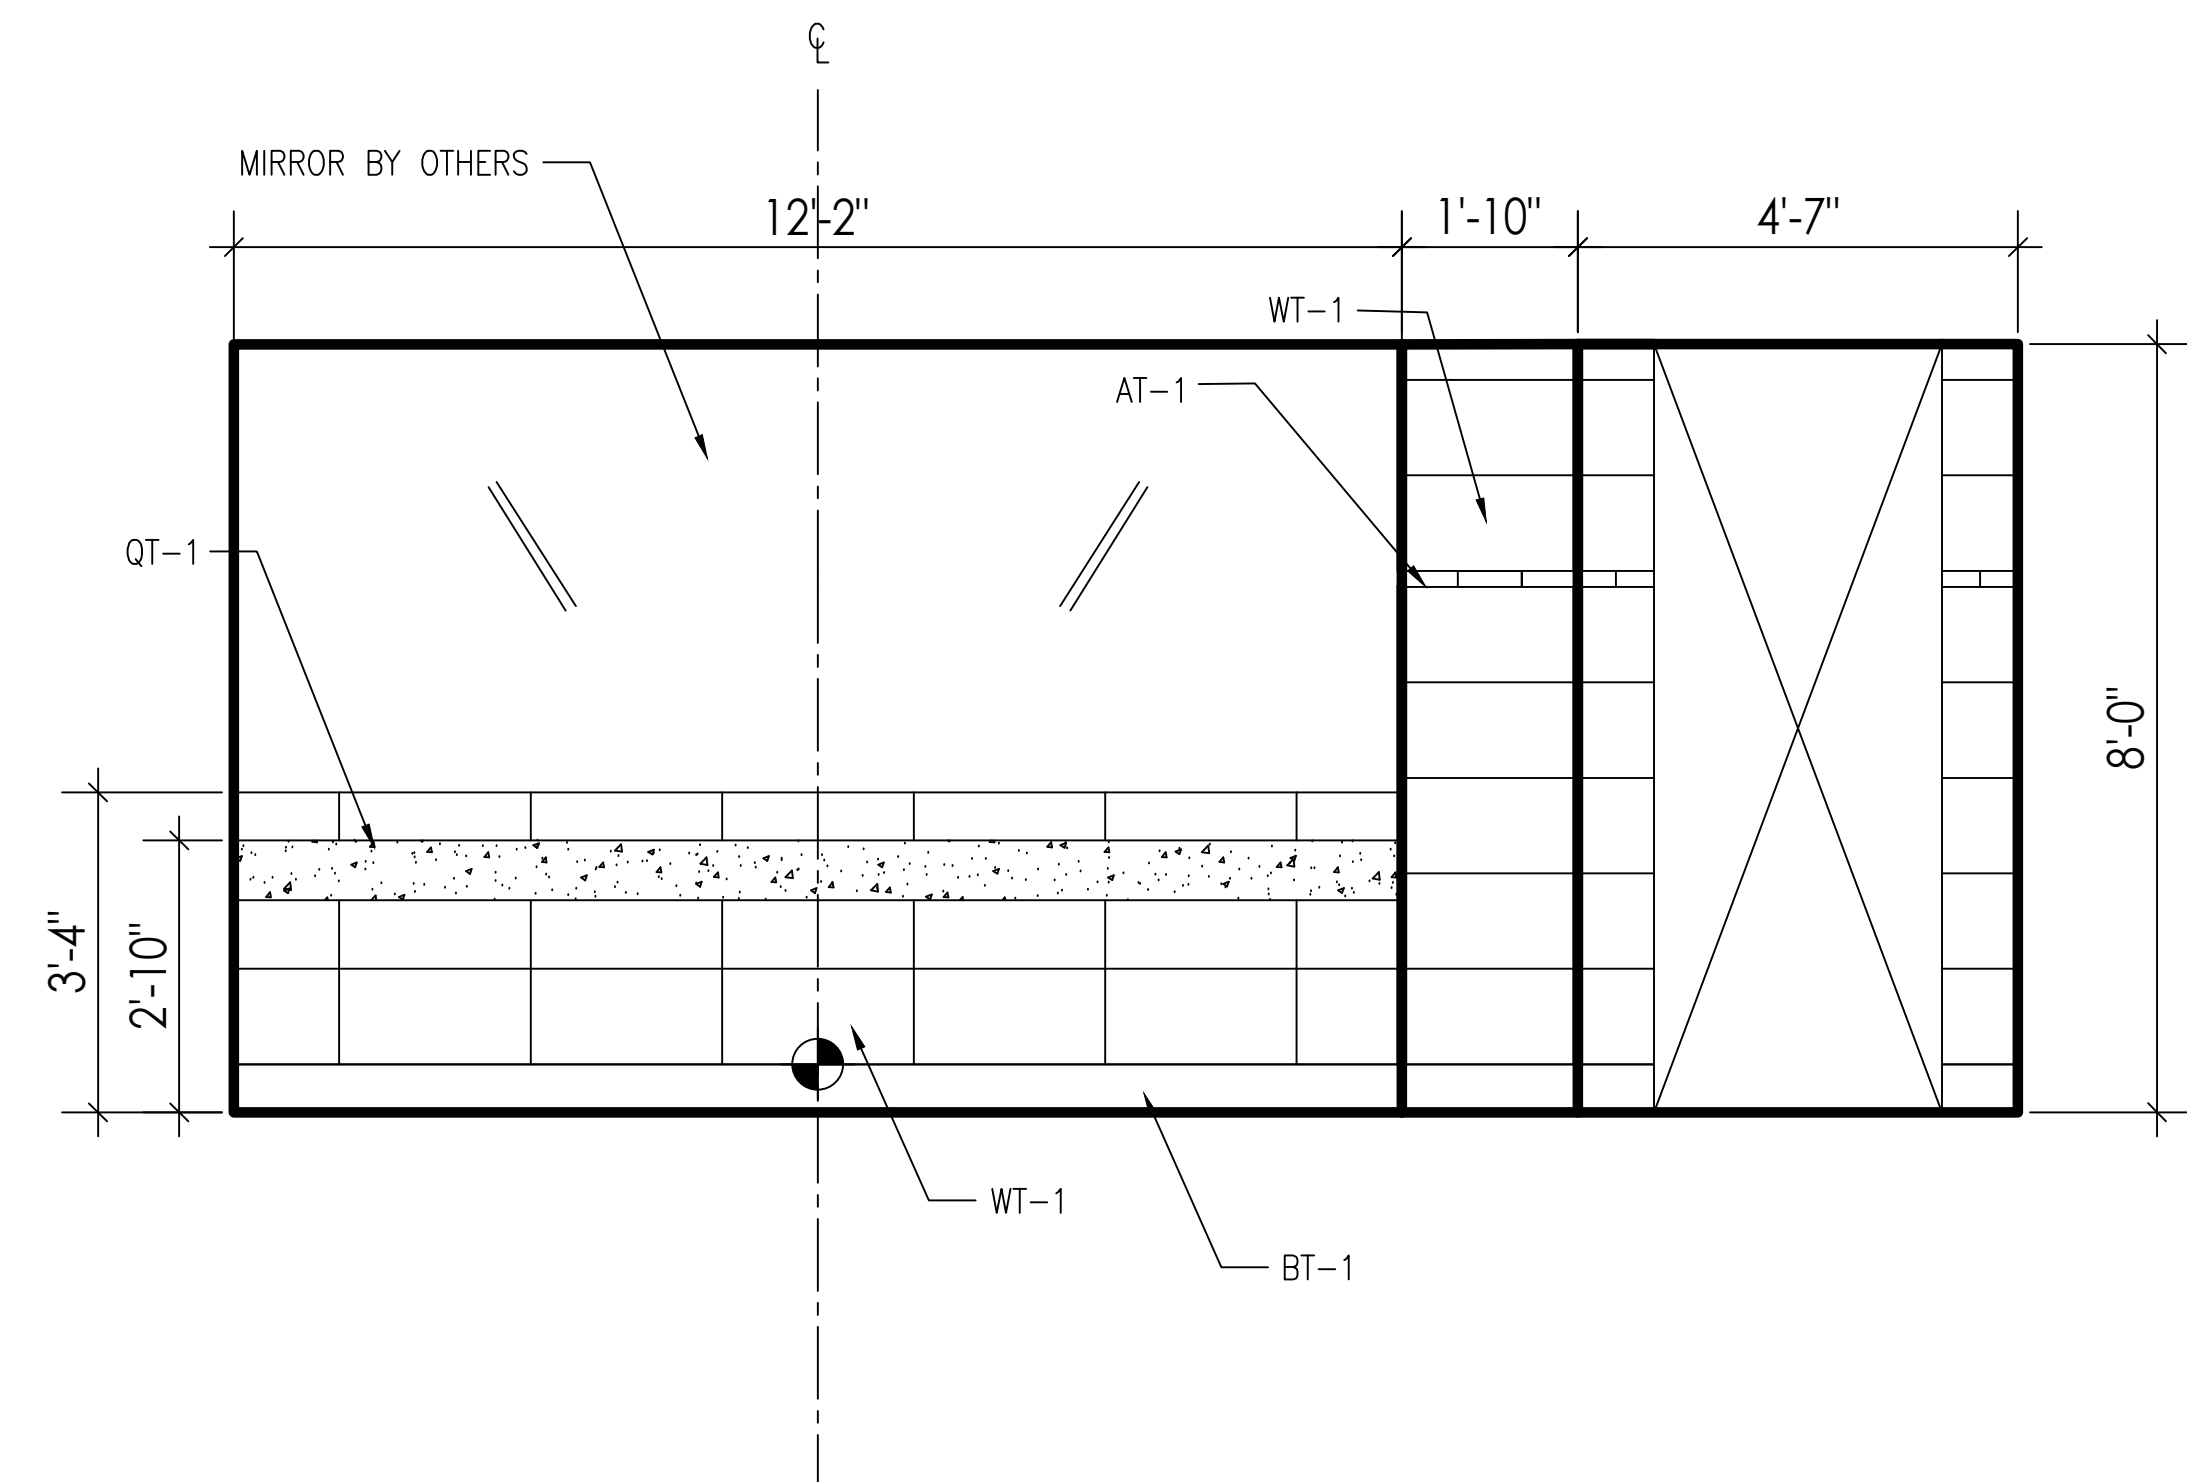



02
1/2"=1'-0" ELEVATIONS: 8TH FLOOR BATHROOMS

03
1/2"=1'-0" ELEVATIONS: 8TH FLOOR BATHROOMS

04
1/2"=1'-0" ELEVATIONS: 8TH FLOOR BATHROOMS


WOMEN'S POWDER ROOM

801

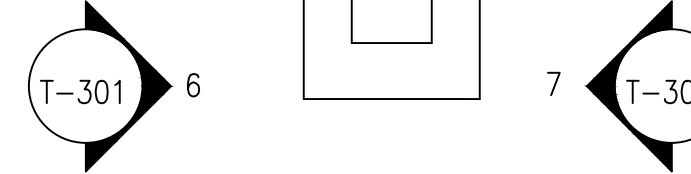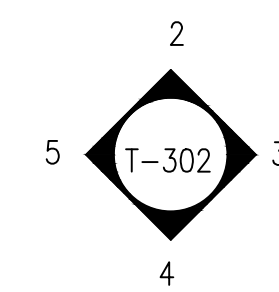




WOMEN'S RESTROOM

802

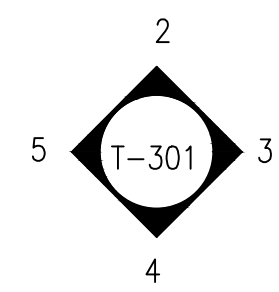


MEN'S RESTROOM


803

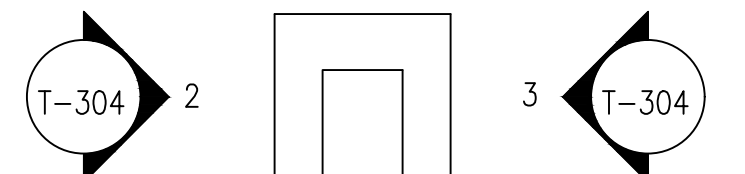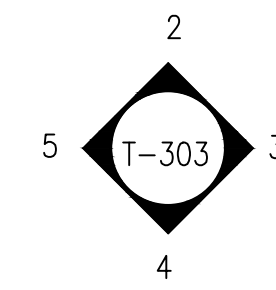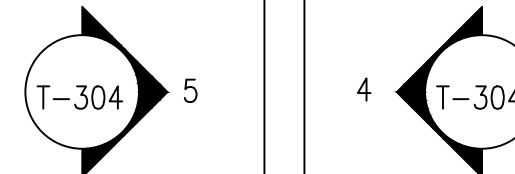


01
1/2"=1'-0" PLAN #2: 8TH FLOOR BATHROOMS

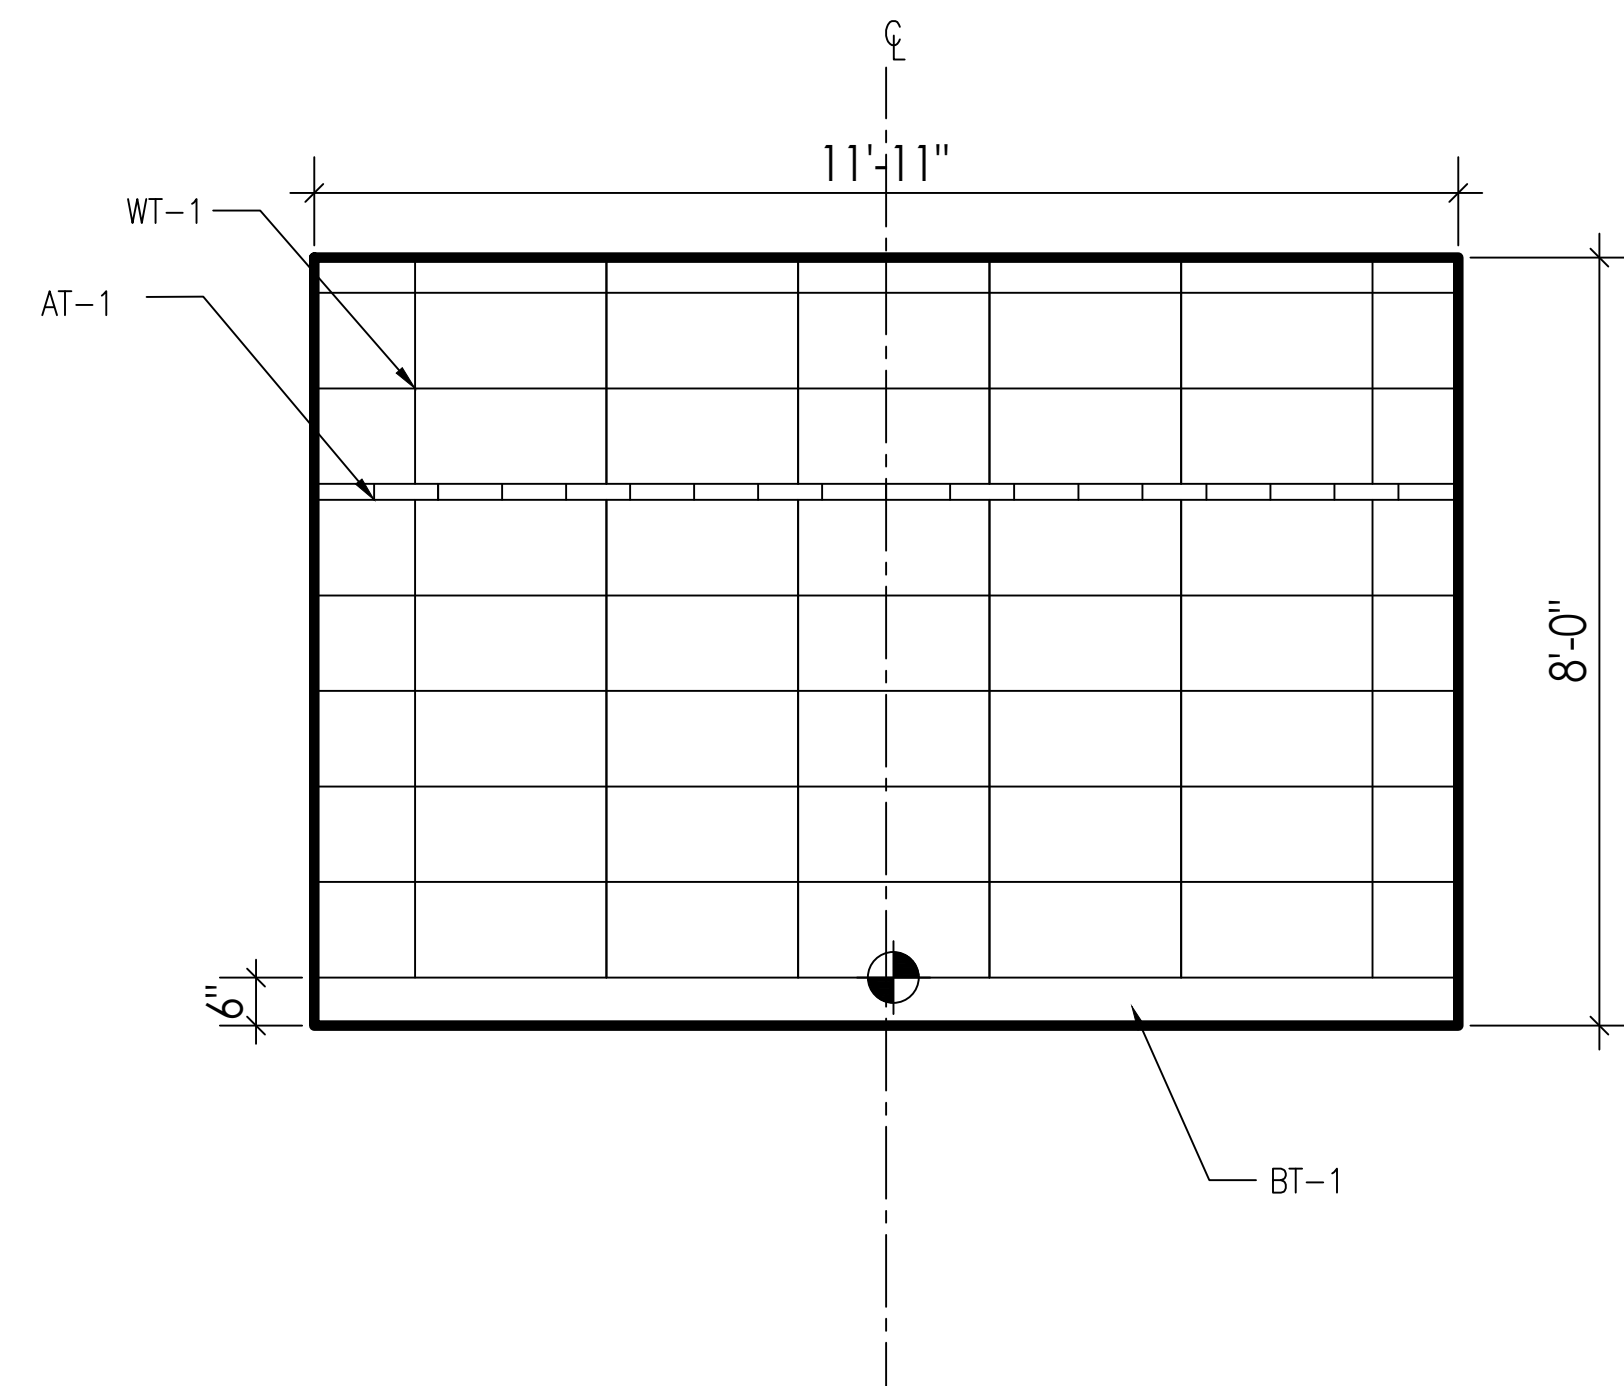

05
1/2"=1'-0" ELEVATIONS: 8TH FLOOR BATHROOMS

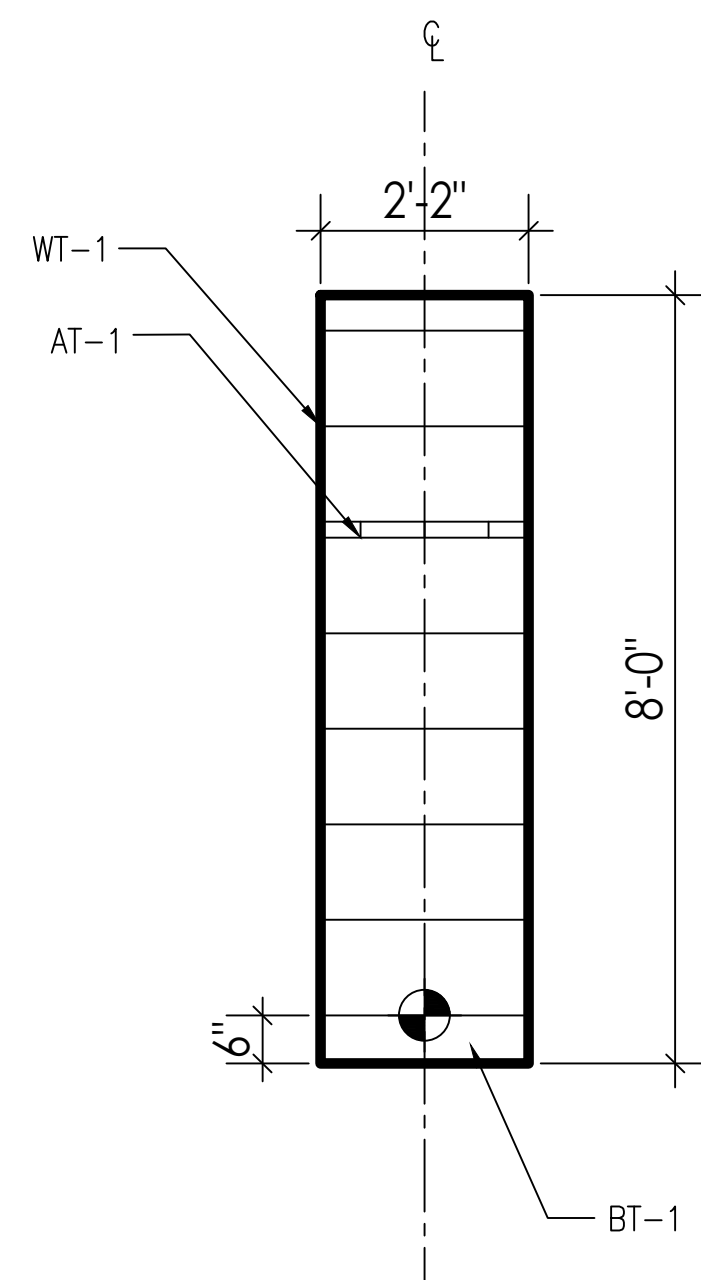

06
1/2"=1'-0" ELEVATIONS: 8TH FLOOR BATHROOMS

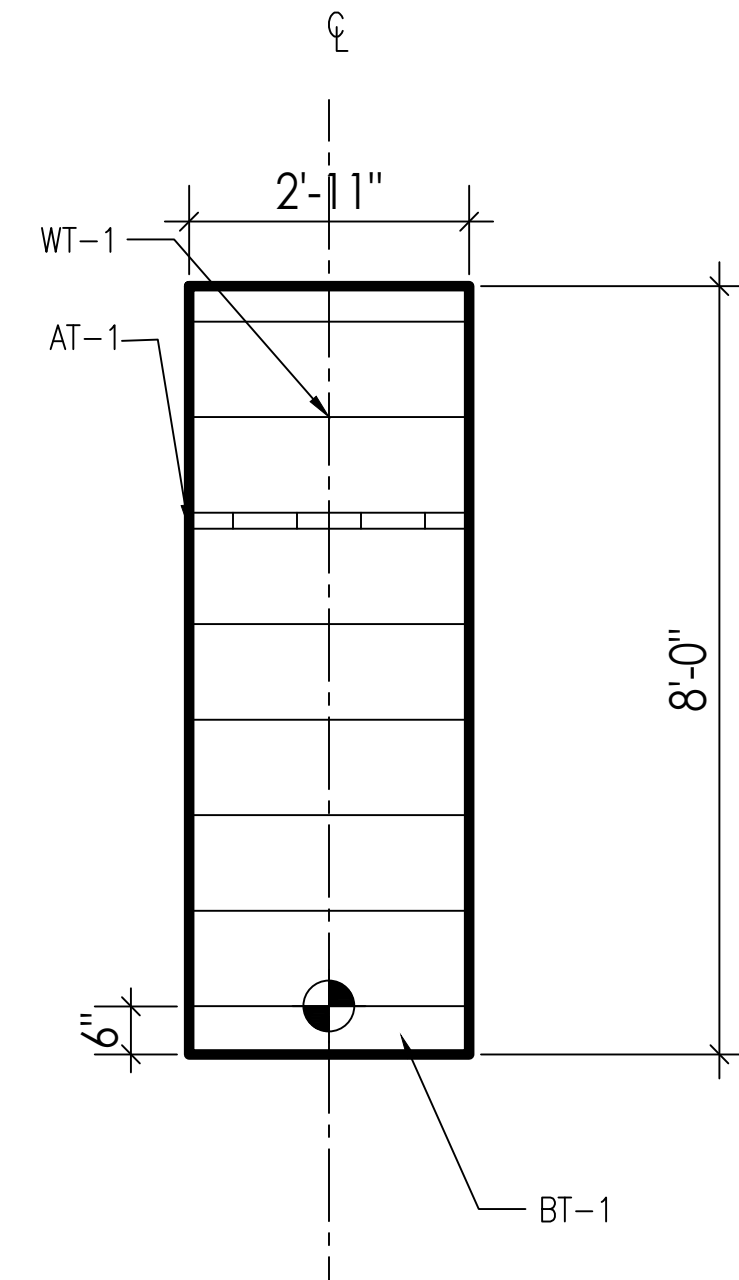

07
1/2"=1'-0" ELEVATIONS: 8TH FLOOR BATHROOMS

CONTRACTOR:
JRM CONSTRUCTION
MANAGEMENT, LLC
242 WEST 36TH STREET
11TH FLOOR
NEW YORK, NY 10018

INTERIOR DESIGNER:

ISSUE FOR APPROVAL 10/09/23

ISSUE NAME DATE

ARCHITECT:
SPACESMITH
ONE NEW YORK PLAZA
NEW YORK, NY 10004
PH:212 260 5583

PROJECT NAME:
JACK RESNICK & SONS
255 GREENWICH STREET
NEW YORK, NY 10007

SHEET NAME:
ELEVATIONS
8TH FLOOR BATHROOMS

DATE:
PROJECT NO.:
PRINCIPAL:
DRAWING BY:
CHECKED BY:
SCALE:
DWG. No.:
T-301
14 of 29




STARTING POINT

(BT-1) TILE BASE GROUT JOINTS WILL NOT ALIGN WITH (WT-1) WALL TILE GROUT JOINTS

(AT-1) ACCENT WALL TILE GROUT JOINTS WILL NOT ALIGN WITH (WT-1) WALL TILE GROUT JOINTS


WOMEN'S
POWDER ROOM

801

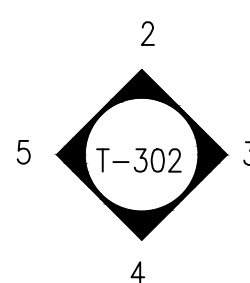






WOMEN'S
RESTROOM

802

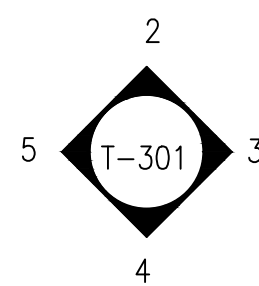


MEN'S
RESTROOM


803

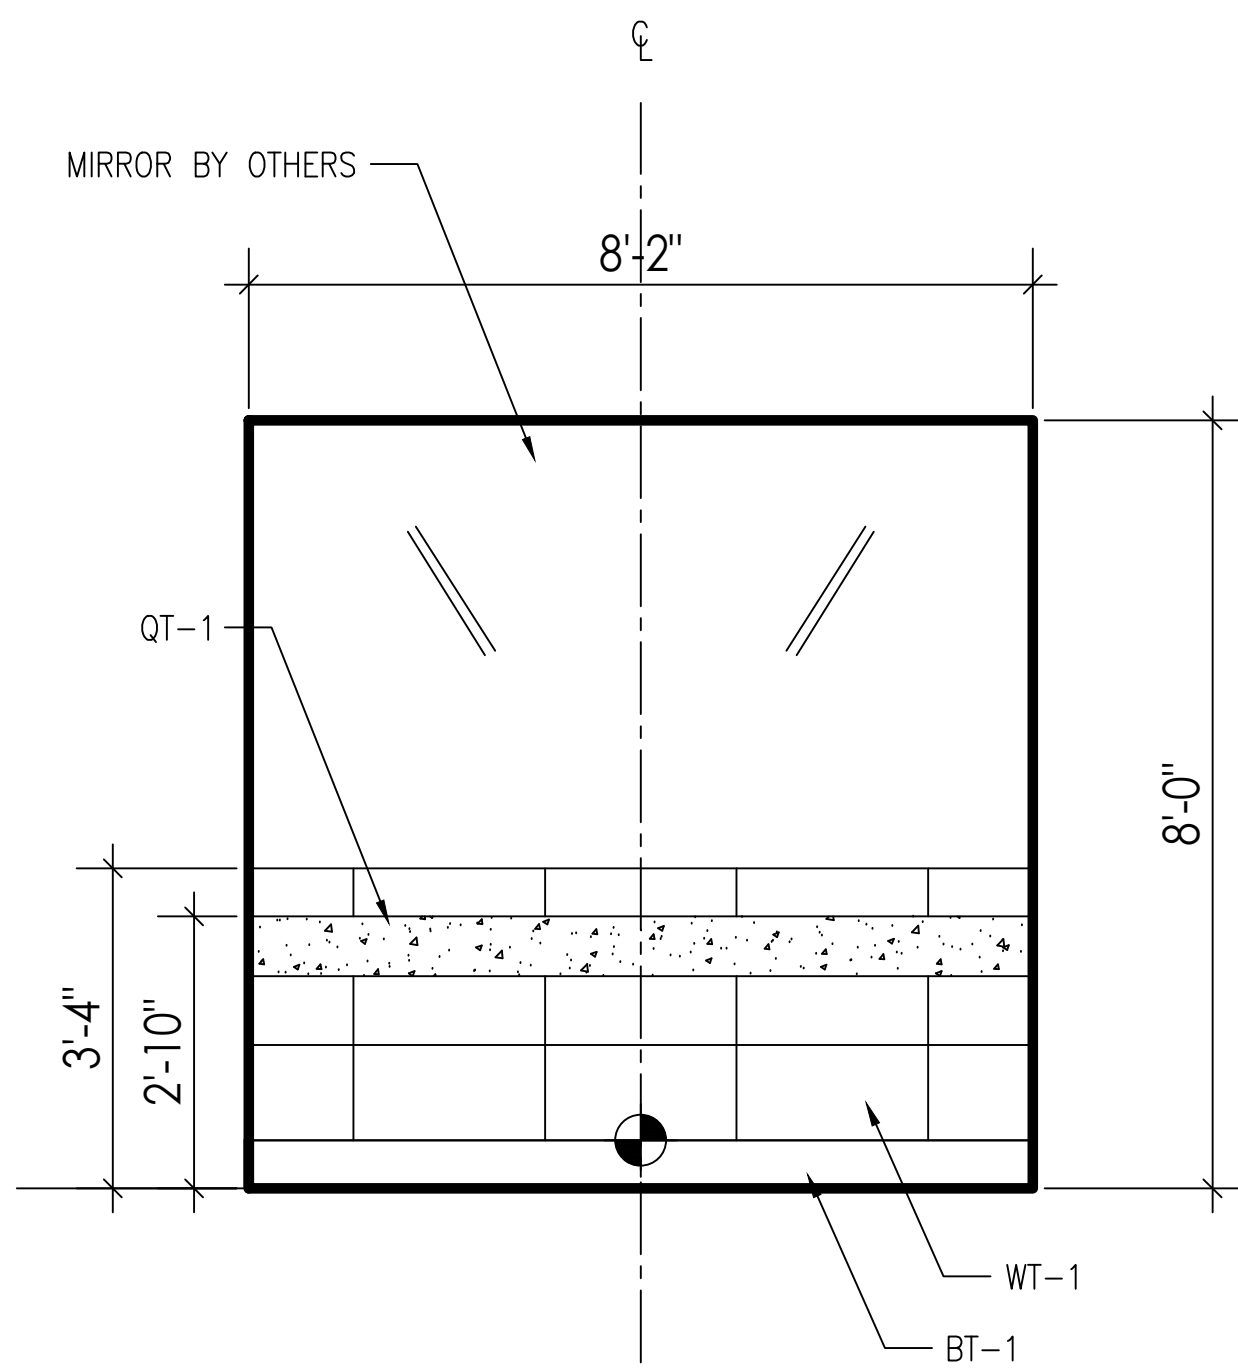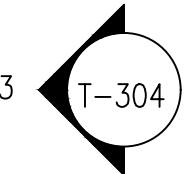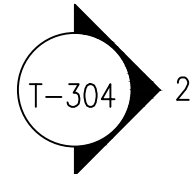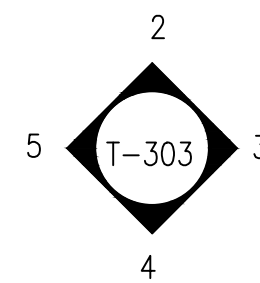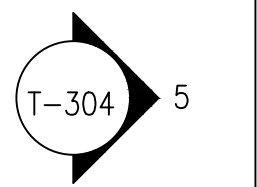


02
1/2"=1'-0" ELEVATIONS: 8TH FLOOR BATHROOMS

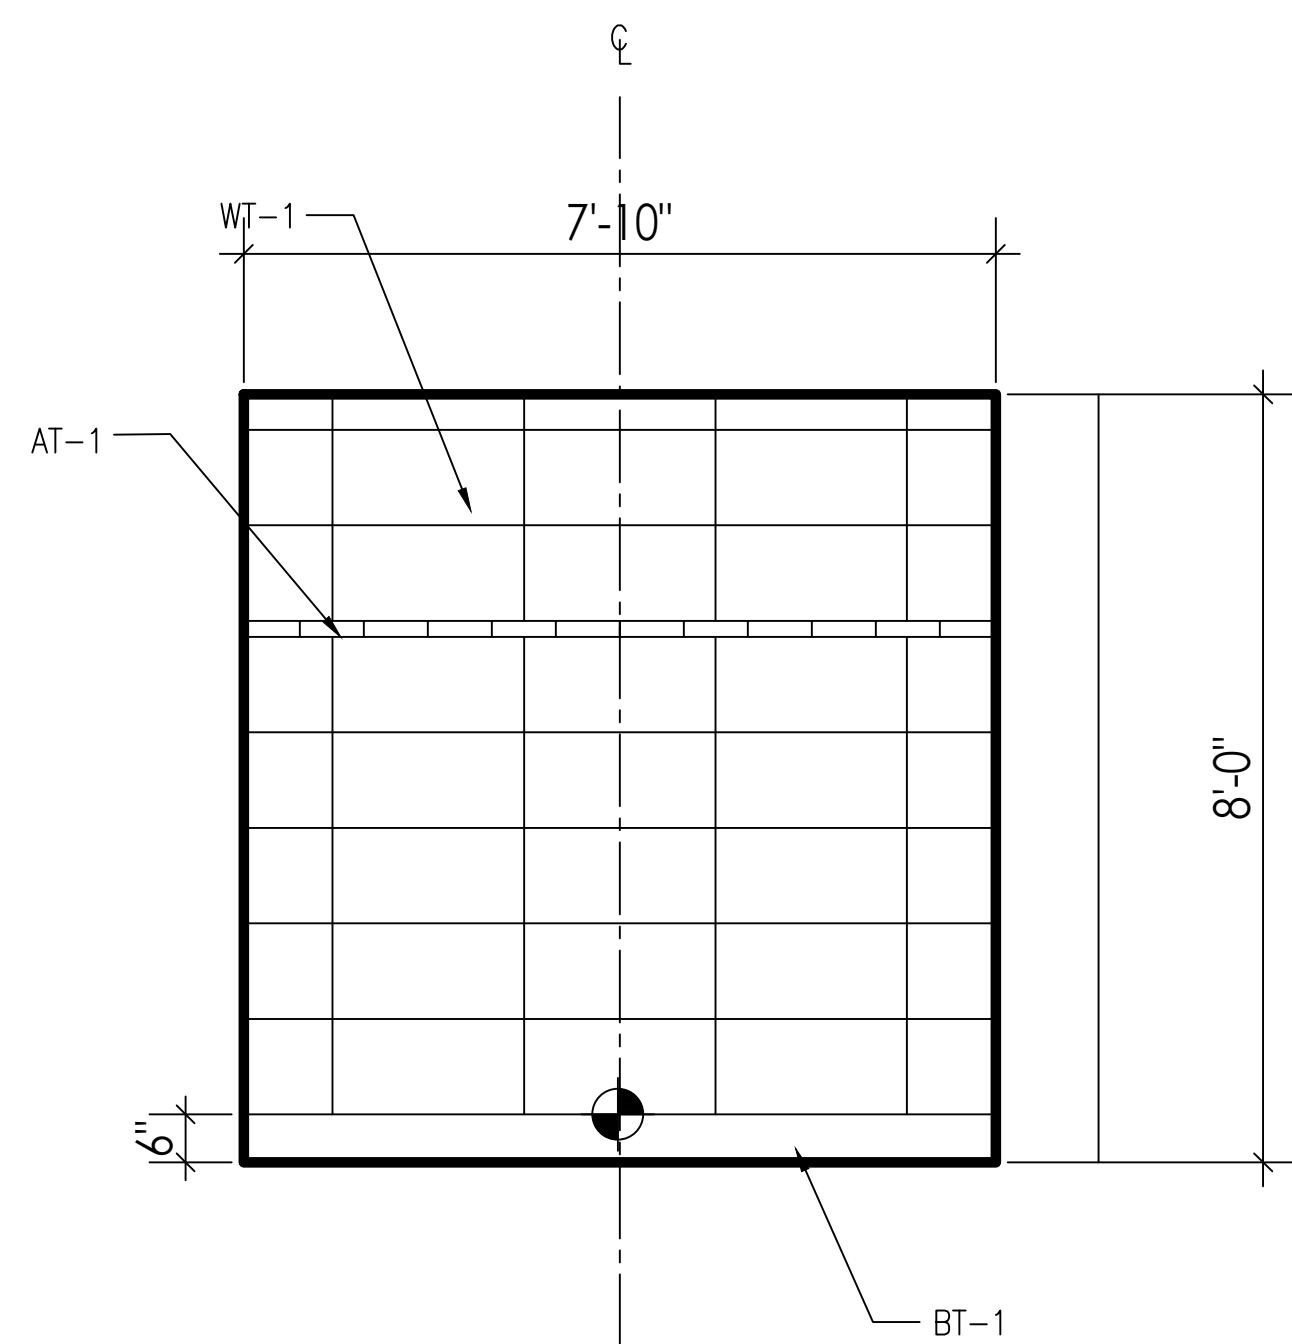

03
1/2"=1'-0" ELEVATIONS: 8TH FLOOR BATHROOMS

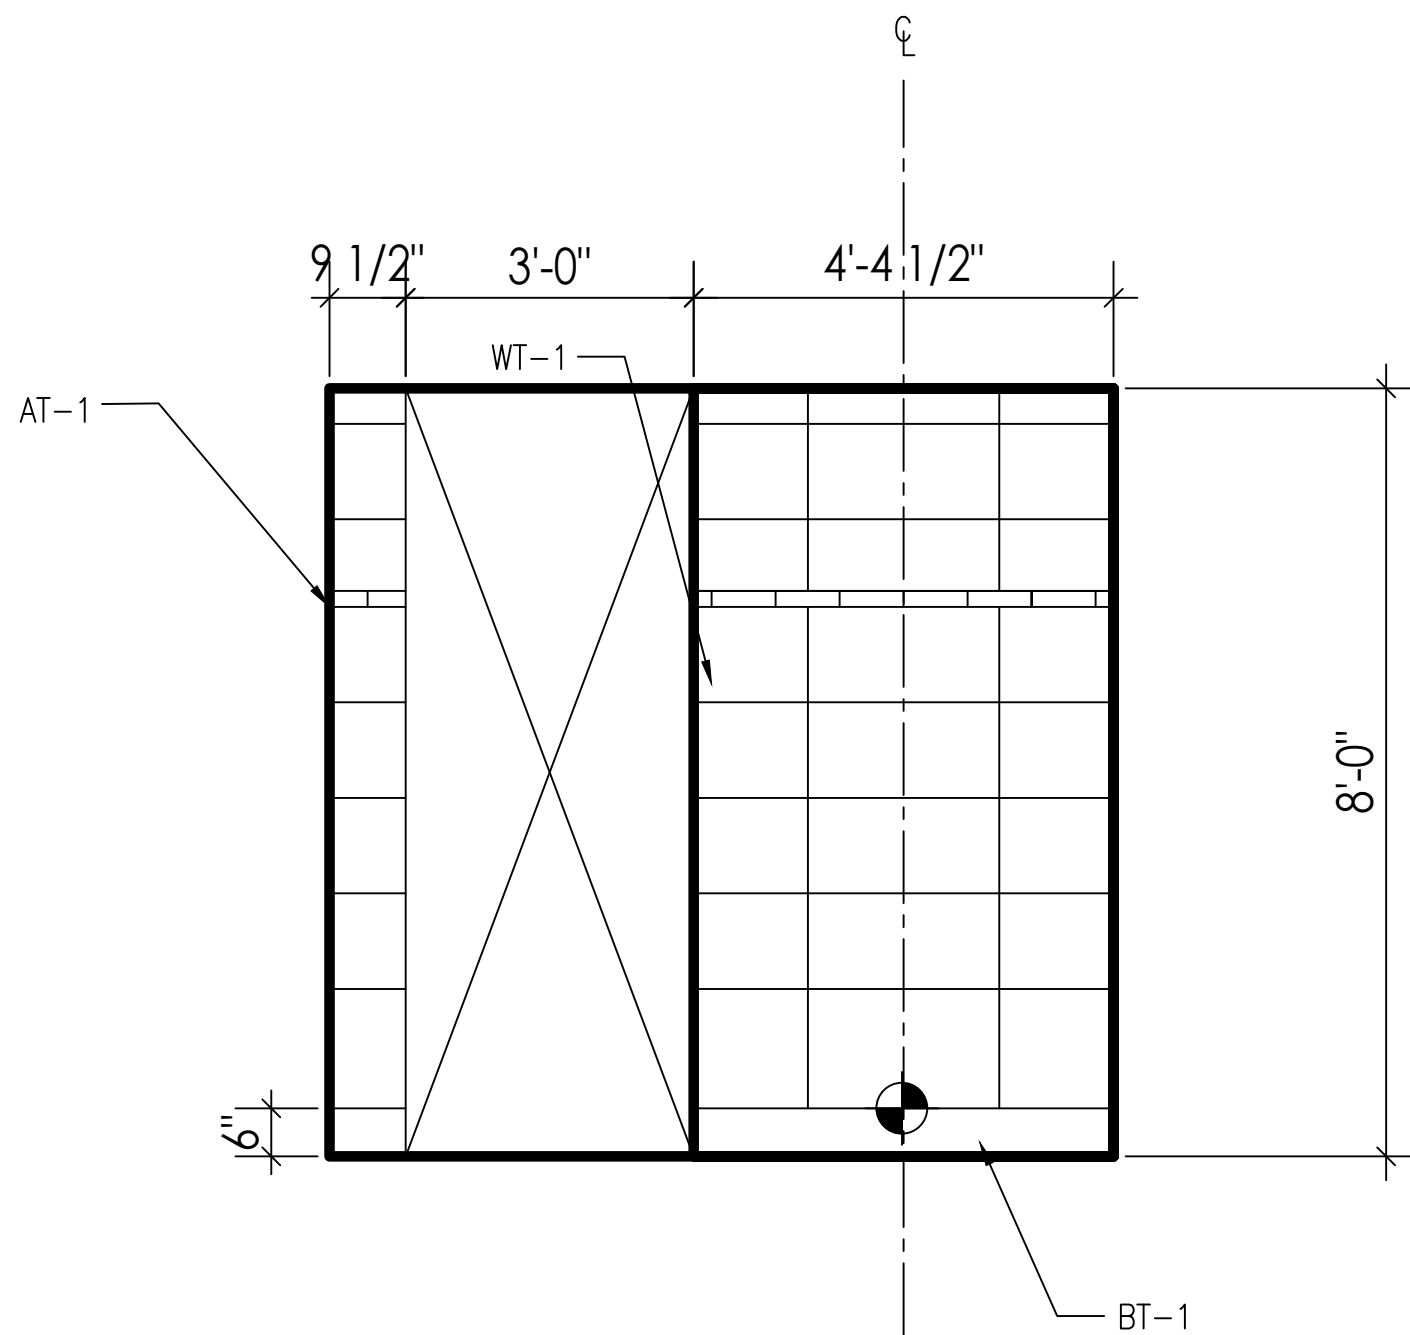

04
1/2"=1'-0" ELEVATIONS: 8TH FLOOR BATHROOMS

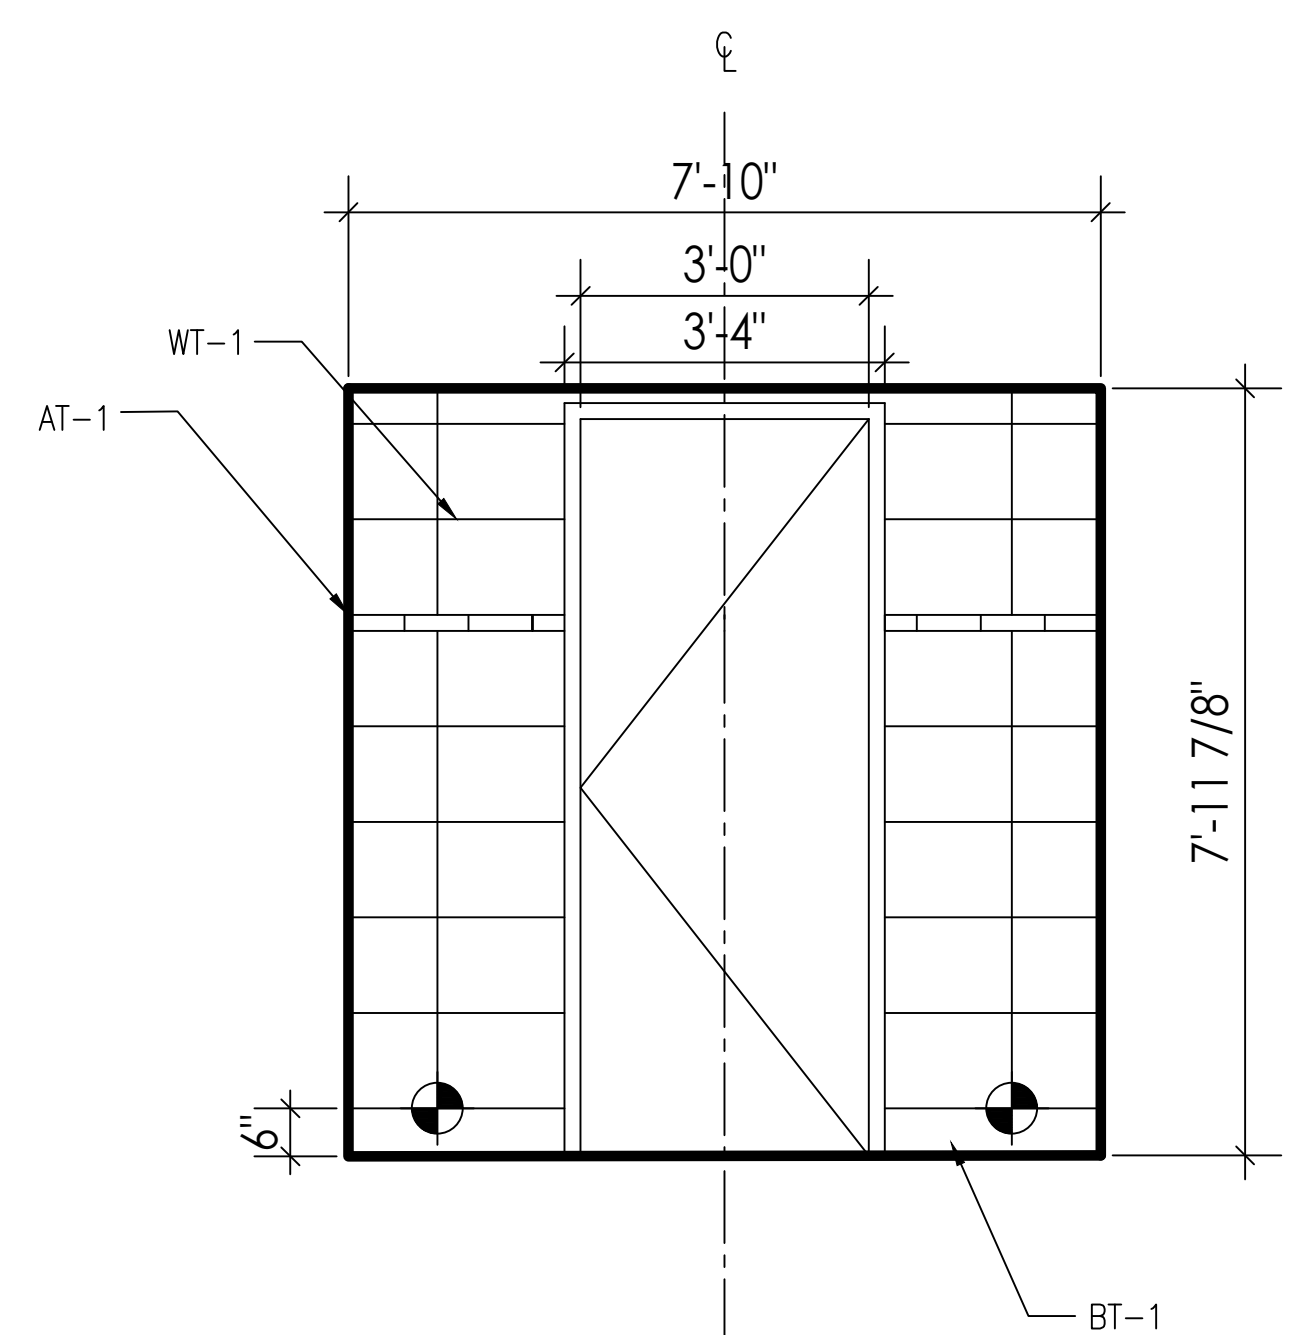

05
1/2"=1'-0" ELEVATIONS: 8TH FLOOR BATHROOMS

AUSTRO TILE & STONE, LLC
30-25 93RD STREET
EAST ELMHURST, NY 11369

CONTRACTOR:
JRM CONSTRUCTION
MANAGEMENT, LLC
242 WEST 36TH STREET
11TH FLOOR
NEW YORK, NY 10018

INTERIOR DESIGNER:

ISSUE FOR APPROVAL 10/09/23

ISSUE NAME DATE

ARCHITECT:

SPACESMITH
ONE NEW YORK PLAZA
NEW YORK, NY 10004
PH:212 260 5583

PROJECT NAME:

JACK RESNICK & SONS
255 GREENWICH STREET
NEW YORK, NY 10007

SHEET NAME:

ELEVATIONS
8TH FLOOR BATHROOMS

DATE:
PROJECT NO.:
PRINCIPAL:
DRAWING BY:
CHECKED BY:
SCALE:
DWG. No.:
T-302

15 of 29





STARTING POINT

(BT-1) TILE BASE GROUT JOINTS WILL NOT ALIGN WITH (WT-1) WALL TILE GROUT JOINTS

(AT-1) ACCENT WALL TILE GROUT JOINTS WILL NOT ALIGN WITH (WT-1) WALL TILE GROUT JOINTS

AUSTRO TILE & STONE, LLC
30-25 93RD STREET
EAST ELMHURST, NY 11369

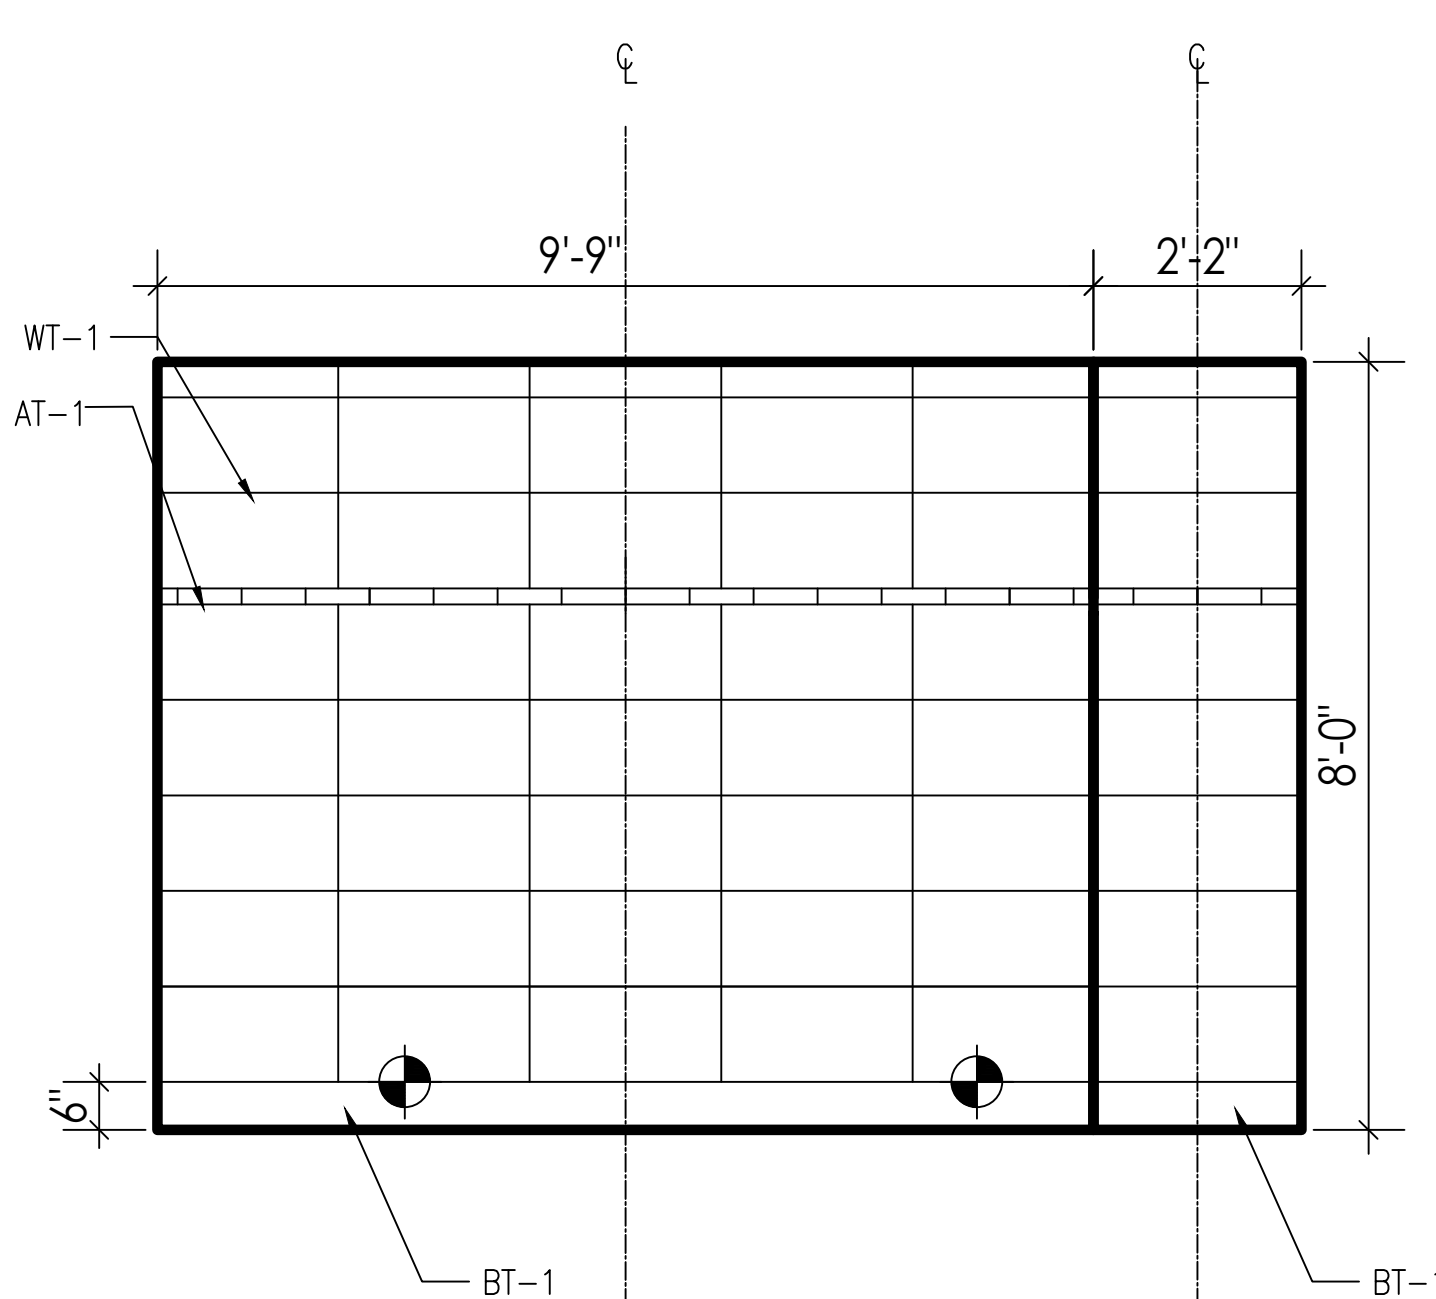
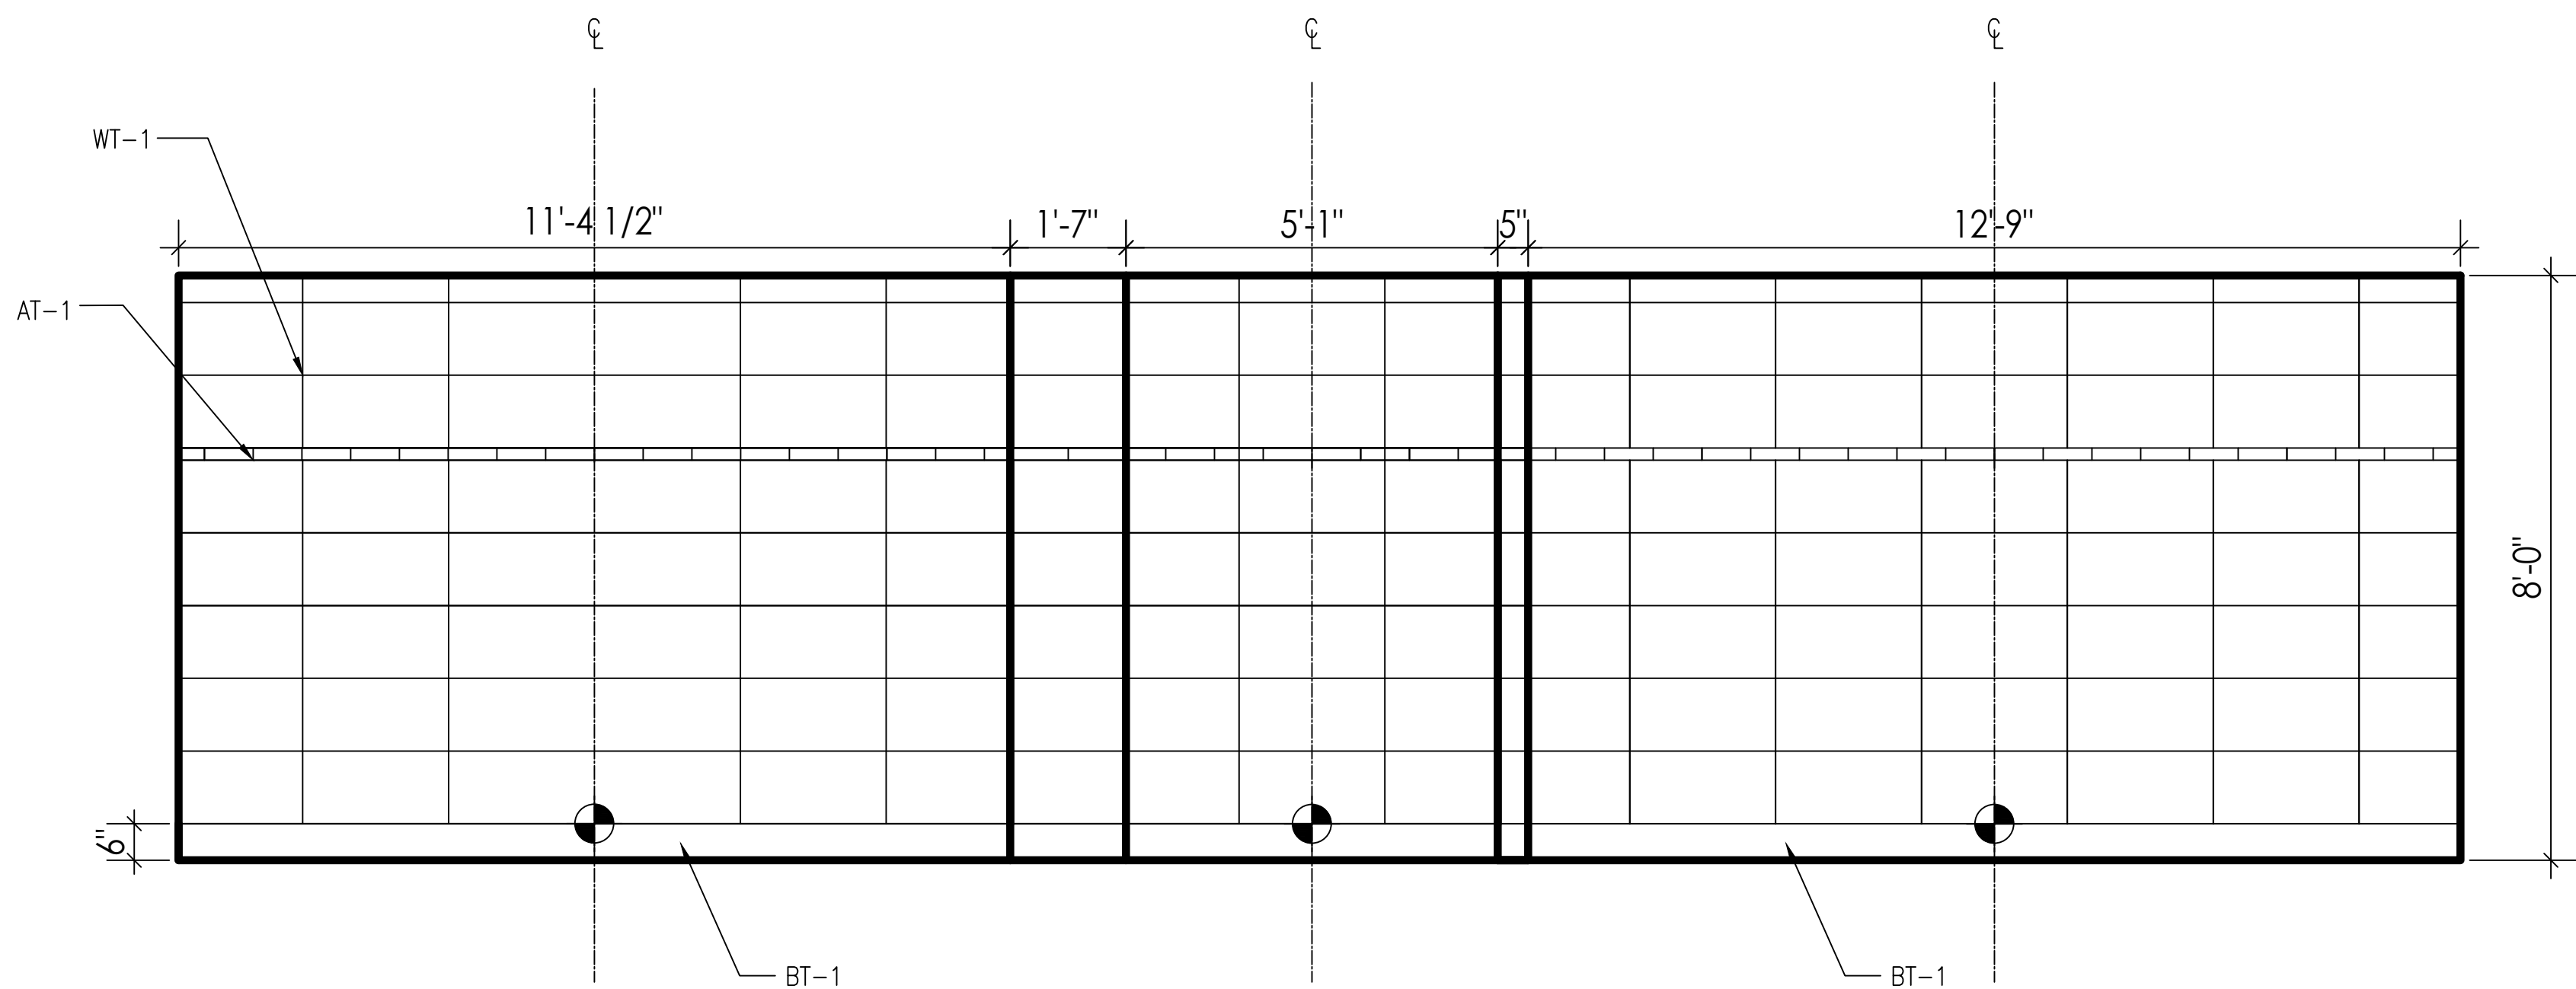


02
1/2"=1'-0" ELEVATIONS: 8TH FLOOR BATHROOMS

03
1/2"=1'-0" ELEVATIONS: 8TH FLOOR BATHROOMS


WOMEN'S
POWDER ROOM

801

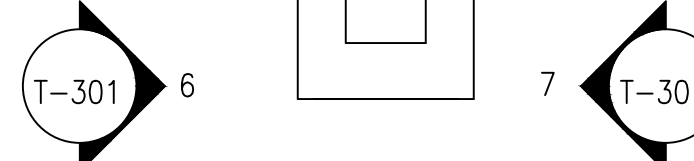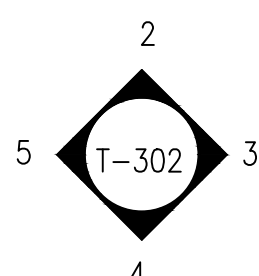






WOMEN'S
RESTROOM

802

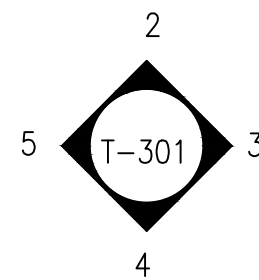


MEN'S
RESTROOM

803

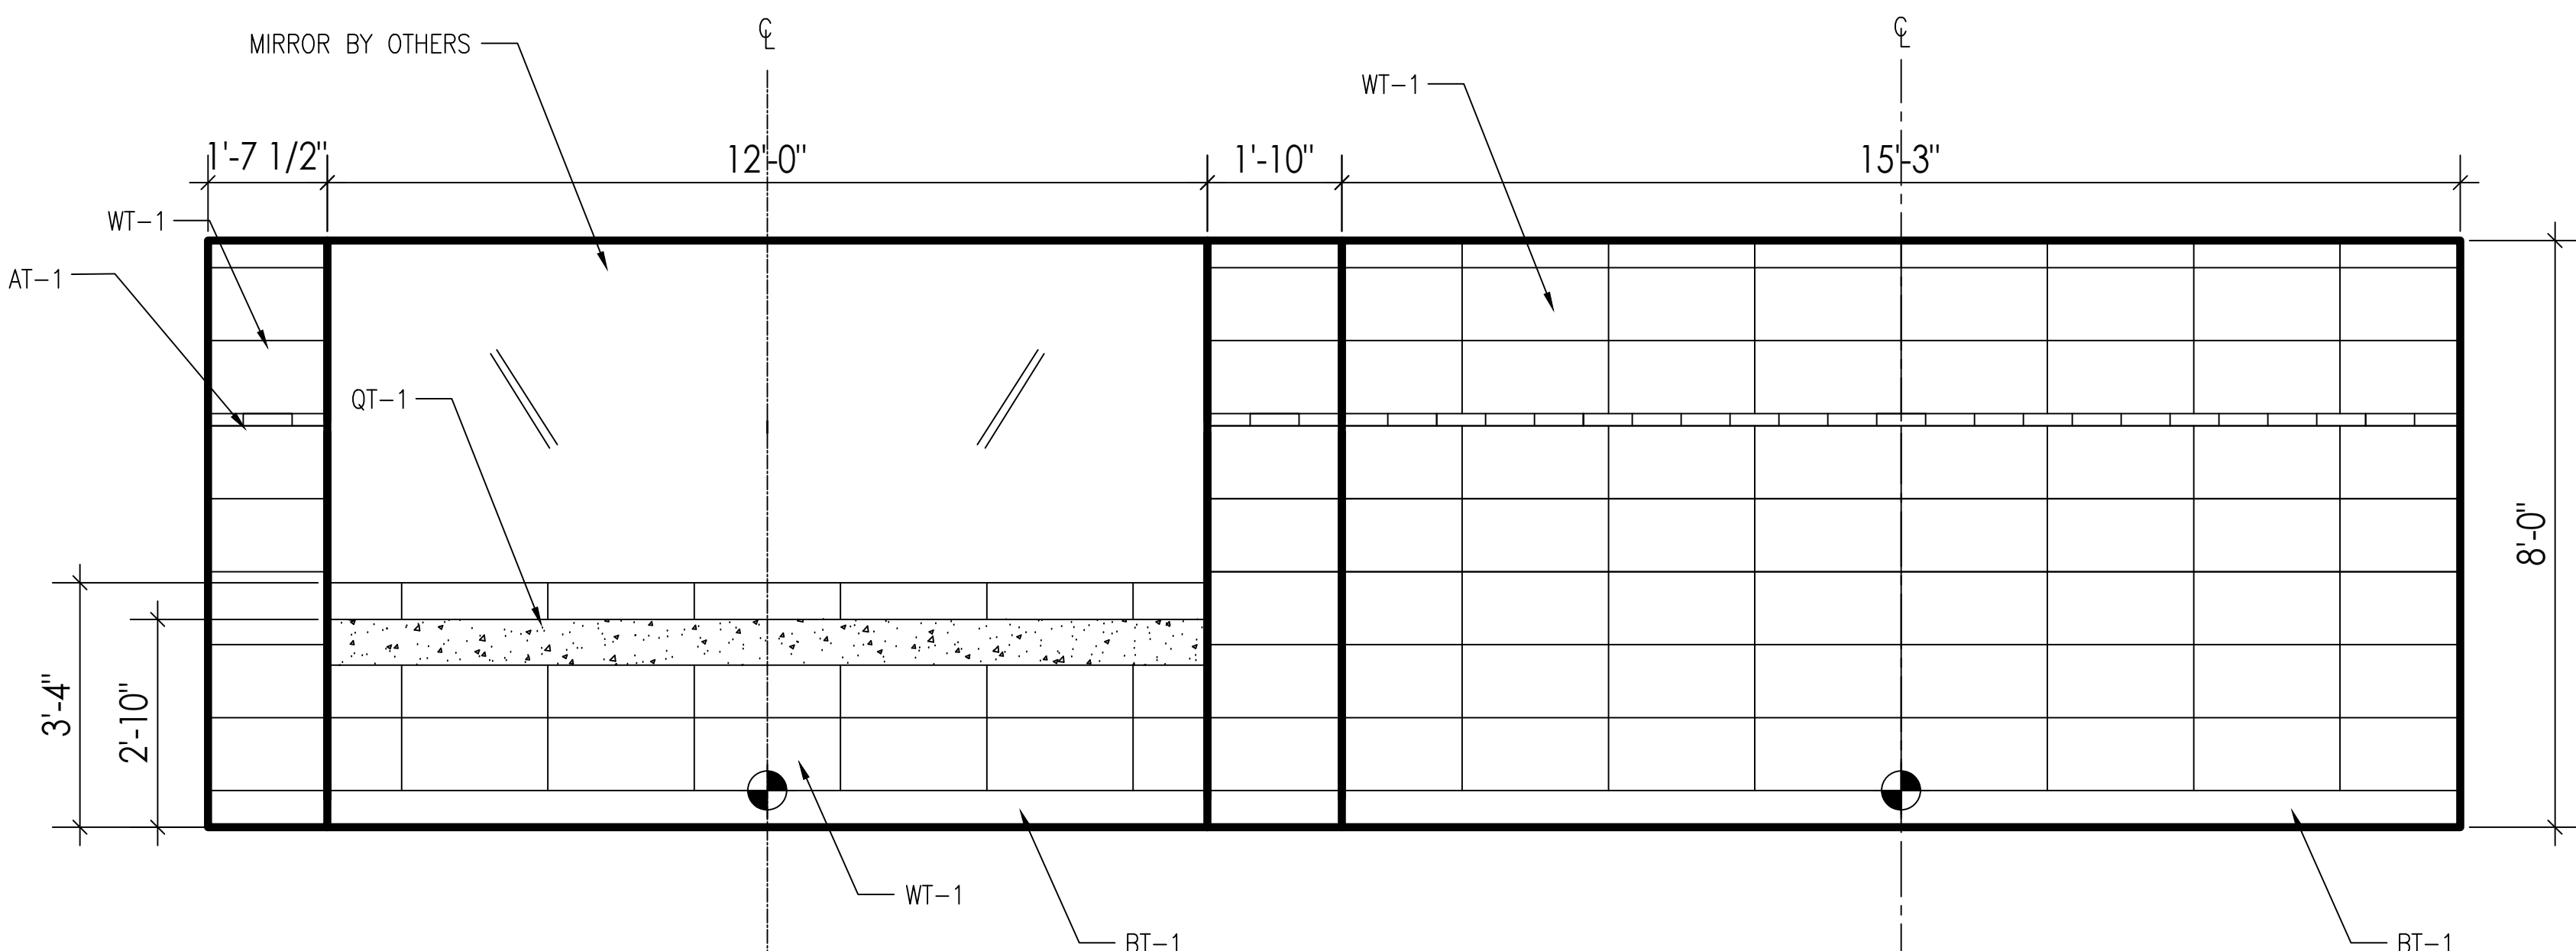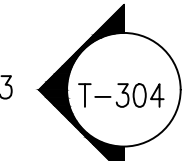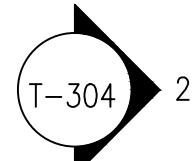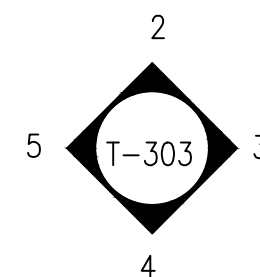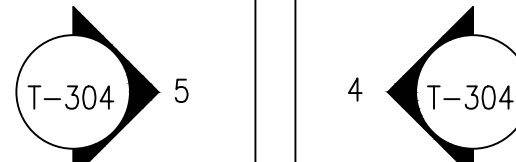

04
1/2"=1'-0" ELEVATIONS: 8TH FLOOR BATHROOMS

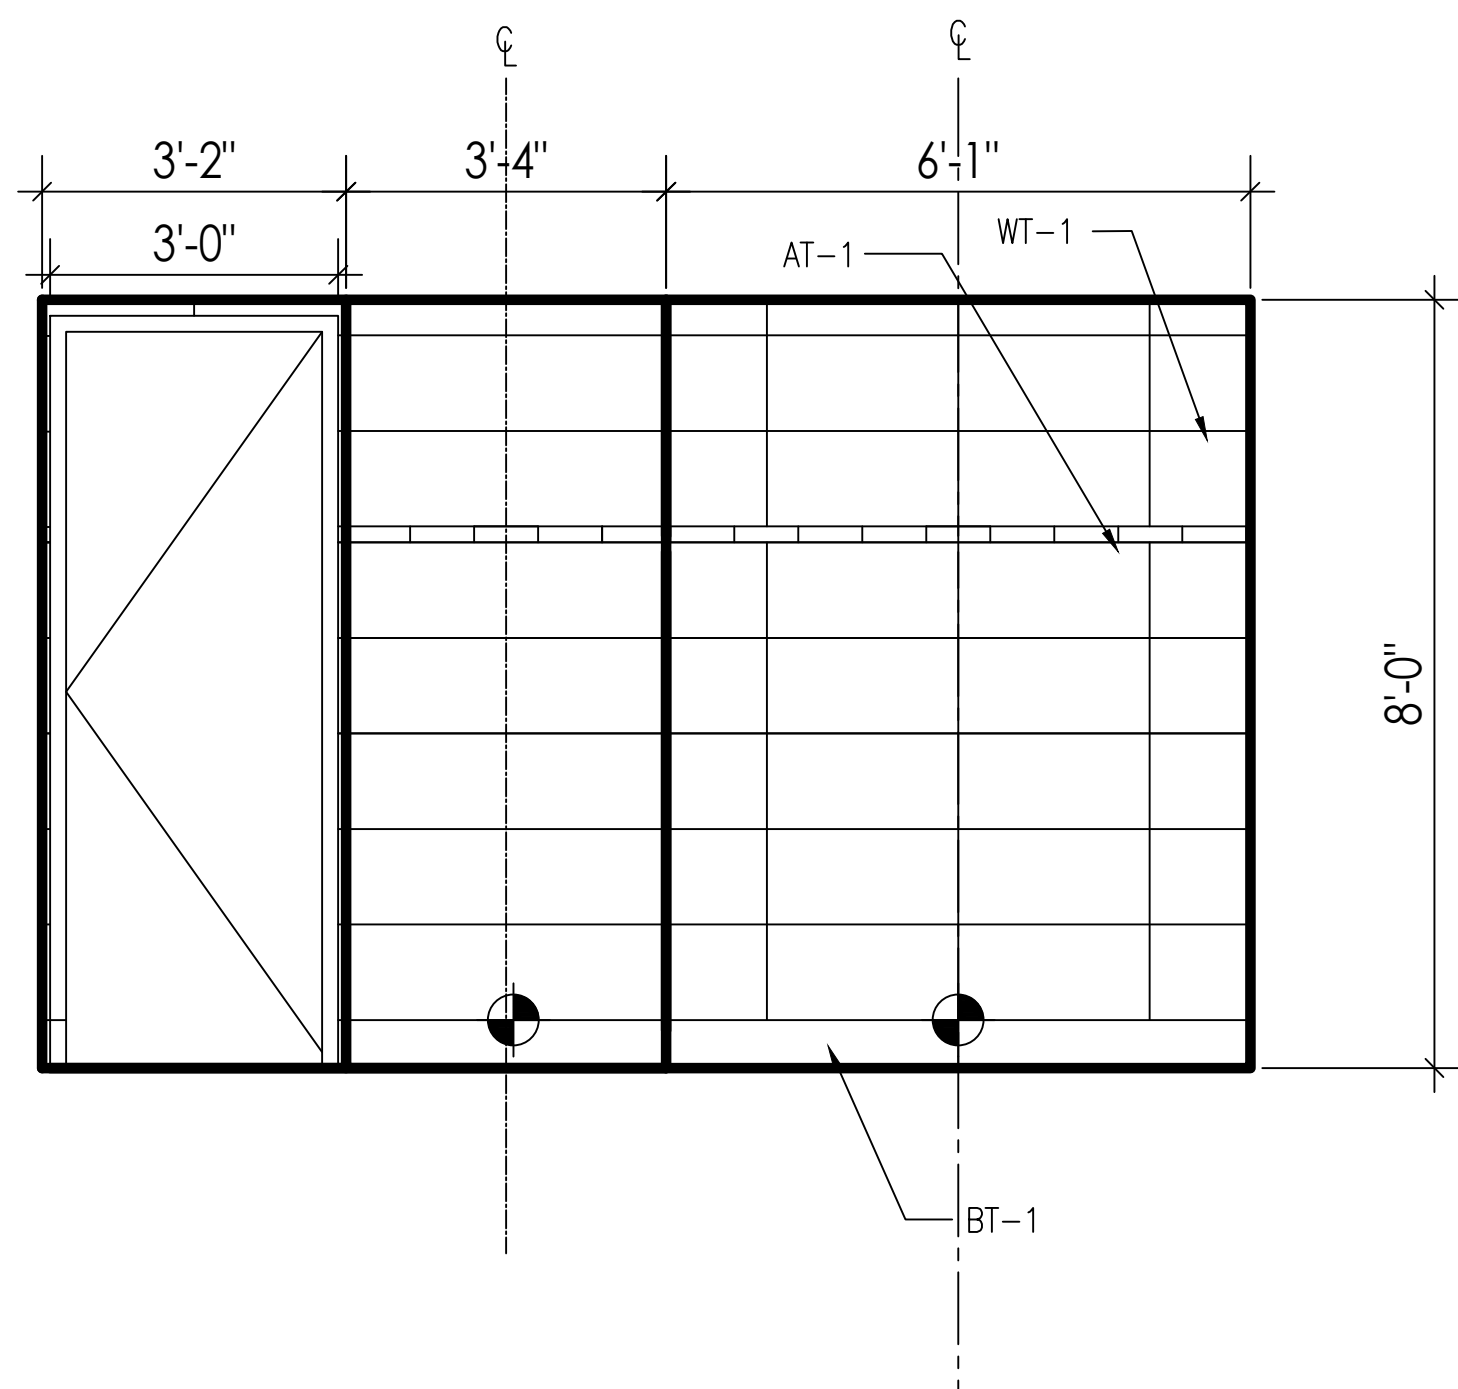

05
1/2"=1'-0" ELEVATIONS: 8TH FLOOR BATHROOMS

01
1/2"=1'-0" PLAN #2: 8TH FLOOR BATHROOMS

CONTRACTOR:
JRM CONSTRUCTION
MANAGEMENT, LLC
242 WEST 36TH STREET
11TH FLOOR
NEW YORK, NY 10018

INTERIOR DESIGNER:

ISSUE FOR APPROVAL 10/09/23
ISSUE NAME DATE

ARCHITECT:

SPACESMITH
ONE NEW YORK PLAZA
NEW YORK, NY 10004
PH:212 260 5583

PROJECT NAME:

JACK RESNICK & SONS
255 GREENWICH STREET
NEW YORK, NY 10007

SHEET NAME:

ELEVATIONS
8TH FLOOR BATHROOMS

DATE:
PROJECT NO.:
PRINCIPAL:
DRAWING BY:
CHECKED BY:
SCALE:
DWG. No.:
T-303




STARTING POINT

(BT-1) TILE BASE GROUT JOINTS WILL NOT ALIGN WITH (WT-1) WALL TILE GROUT JOINTS

(AT-1) ACCENT WALL TILE GROUT JOINTS WILL NOT ALIGN WITH (WT-1) WALL TILE GROUT JOINTS


WOMEN'S
POWDER ROOM

801

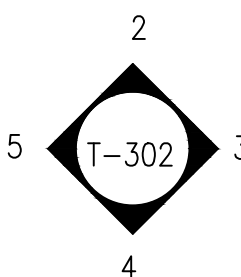





WOMEN'S
RESTROOM

802

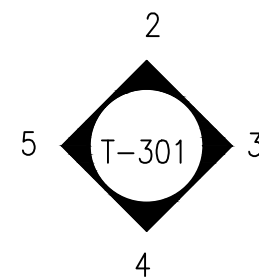



MEN'S
RESTROOM

803

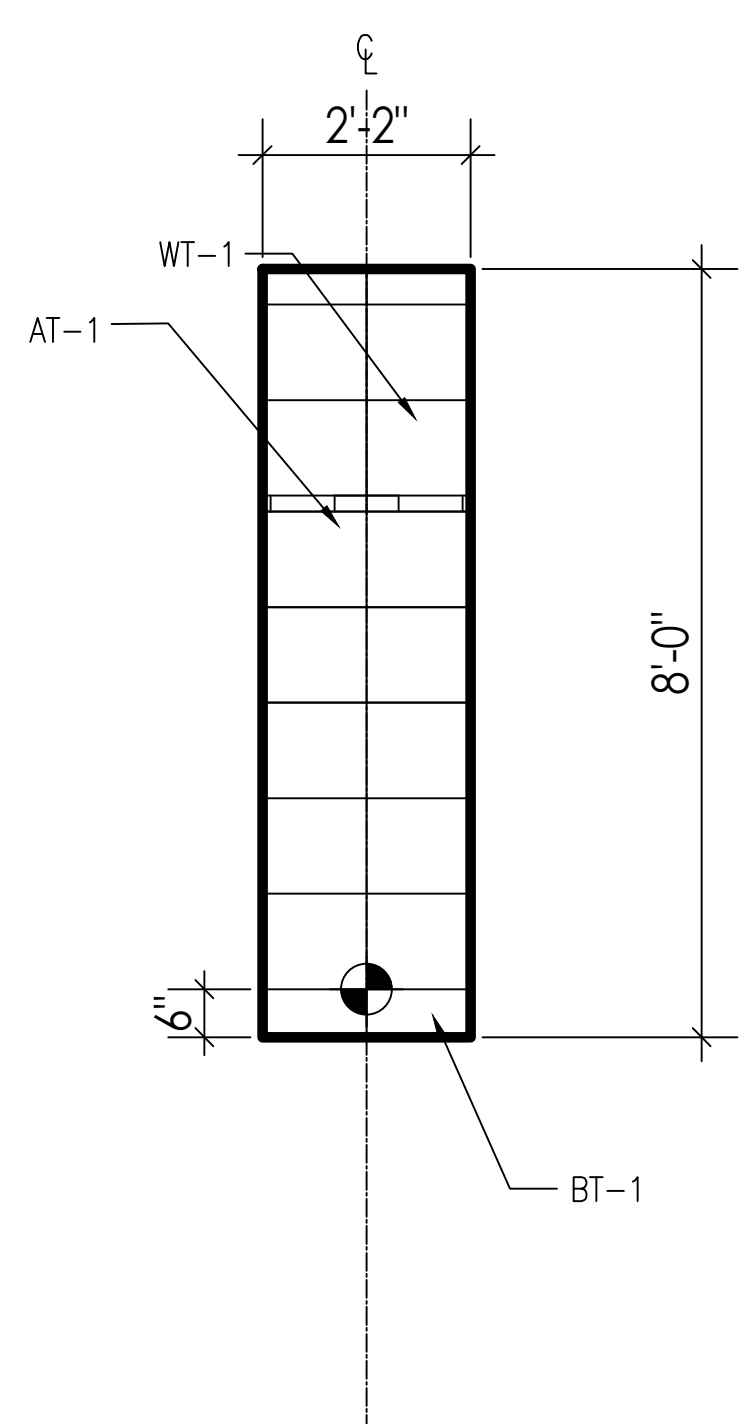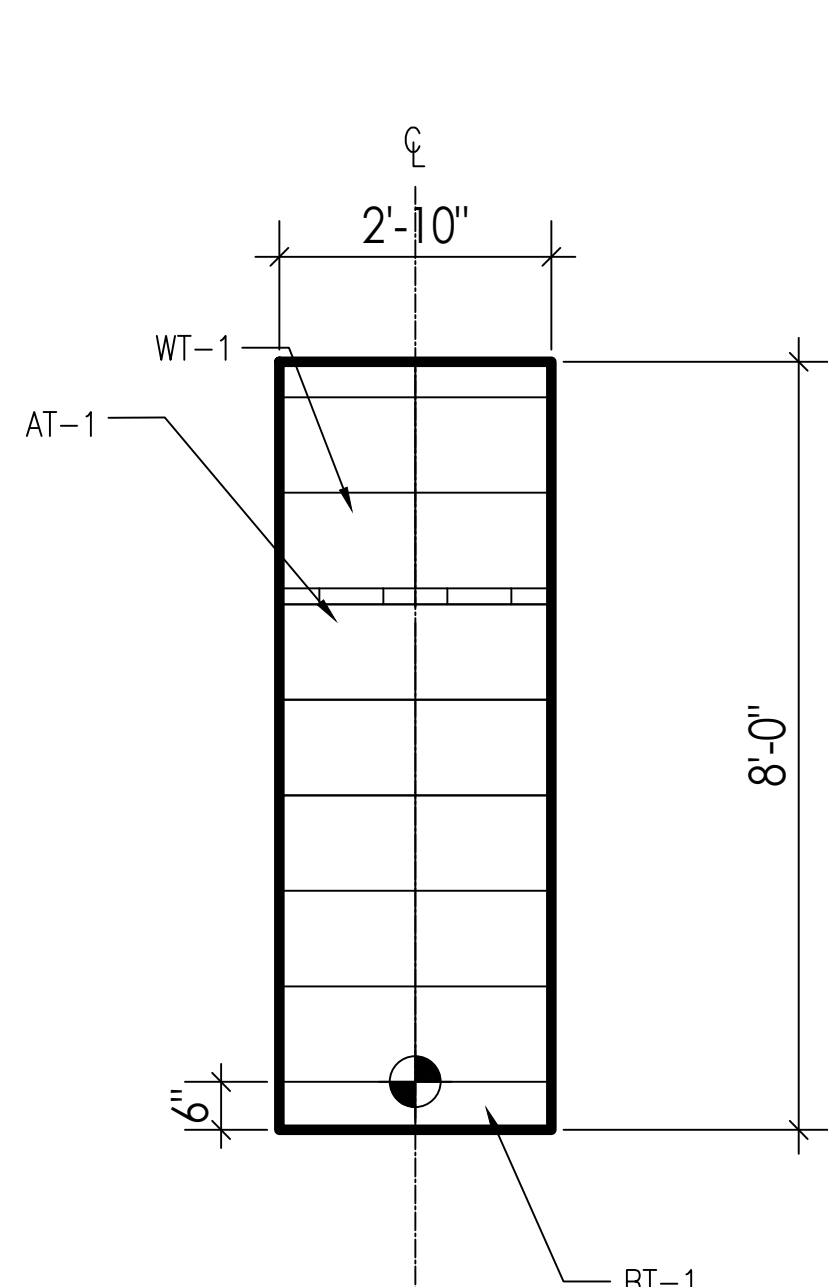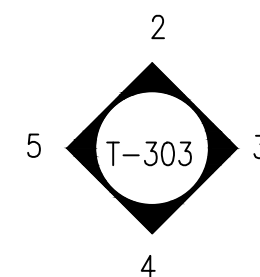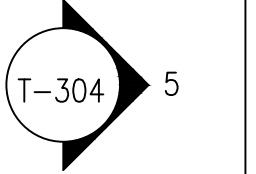

02
1/2"=1'-0" ELEVATIONS: 8TH FLOOR BATHROOMS

03
1/2"=1'-0" ELEVATIONS: 8TH FLOOR BATHROOMS

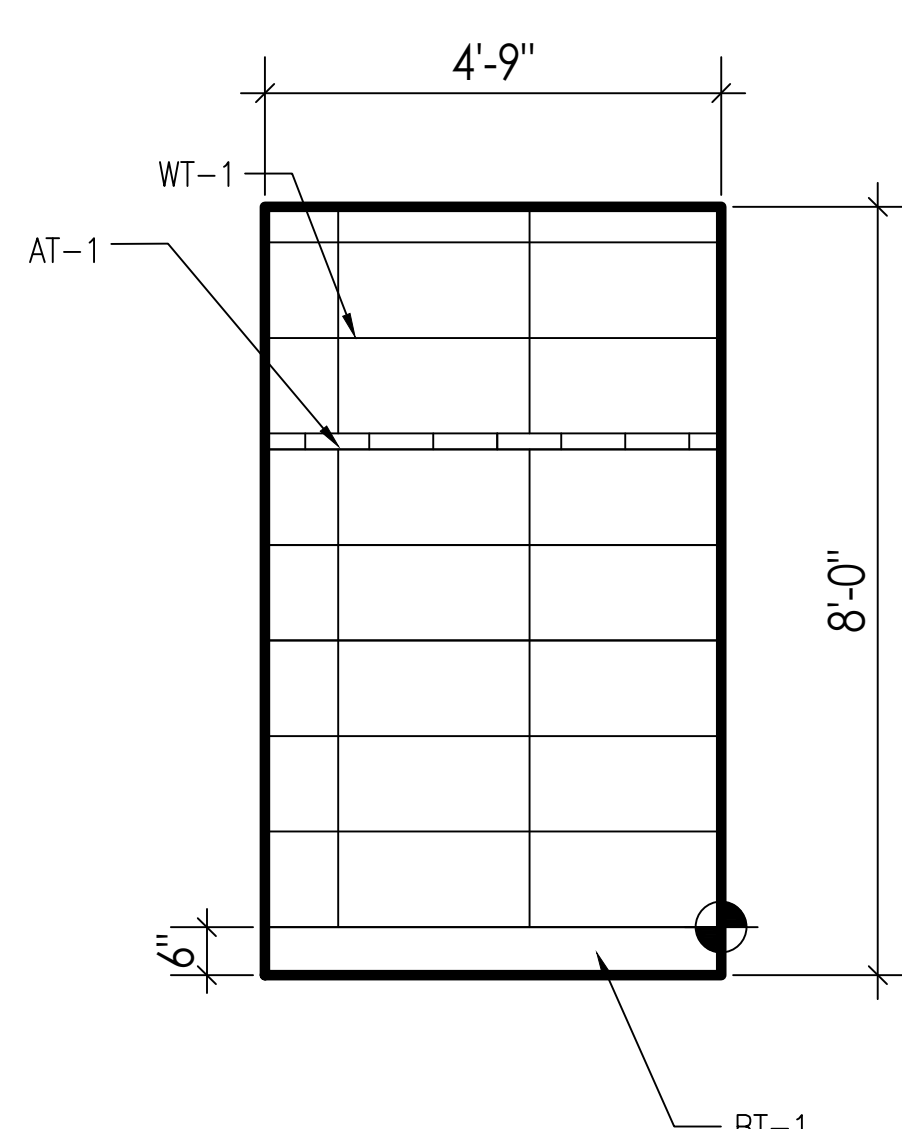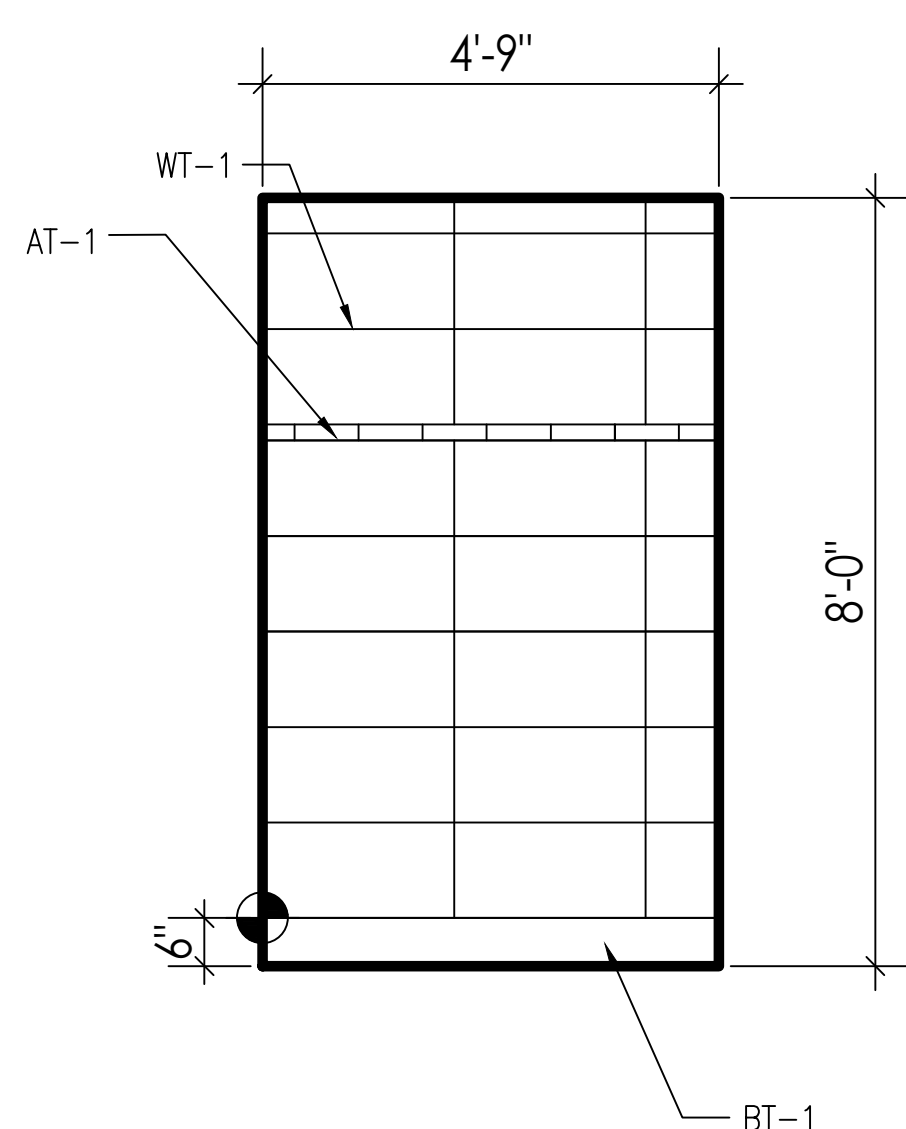

04
1/2"=1'-0" ELEVATIONS: 8TH FLOOR BATHROOMS

05
1/2"=1'-0" ELEVATIONS: 8TH FLOOR BATHROOMS

AUSTRO TILE & STONE, LLC
30-25 93RD STREET
EAST ELMHURST, NY 11369

CONTRACTOR:
JRM CONSTRUCTION
MANAGEMENT, LLC
242 WEST 36TH STREET
11TH FLOOR
NEW YORK, NY 10018

INTERIOR DESIGNER:

ISSUE FOR APPROVAL 10/09/23
ISSUE NAME DATE

ARCHITECT:
SPACESMITH
ONE NEW YORK PLAZA
NEW YORK, NY 10004
PH:212 260 5583

PROJECT NAME:
JACK RESNICK & SONS
255 GREENWICH STREET
NEW YORK, NY 10007

SHEET NAME:
ELEVATIONS
8TH FLOOR BATHROOMS

DATE:
PROJECT NO.:
PRINCIPAL:
DRAWING BY:
CHECKED BY:
SCALE:
DWG. No.:
T-304
17 of 29



STARTING POINT

WOMEN'S
POWDER ROOM

901

STONE SADDLE -

EXISTING

TILE STARTING POINT

12'	12'
-----	-----

A free-body diagram of the foot (FT) is shown. It consists of a horizontal line representing the foot, with a vertical line segment extending upwards from its right end. An arrow points from the right end of the horizontal line, pointing up and to the right at approximately a 45-degree angle. The label 'FT' is placed to the right of the horizontal line.

WOMEN'S
RESTROOM

902

MEN'S
RESTROOM

903

STONE SADDLE —

Q —

12'

 TILE STARTING POINT

3

STARTING POINT

C

12' - 2"

EQ

EQ

02 ENLARGED PLAN: 9TH FLOOR BATHROOMS
1/2"=1'-0"

02
1/2"-1'-0"

Figure 10-10 is a technical drawing showing a wall and floor layout. The wall is 12'-0" high and 24'-0" wide. The floor is 24'-0" wide. The wall is divided into two equal sections (EQ) by a vertical centerline. A tile starting point is marked on the wall, indicated by a dashed line and an arrow labeled "TILE STARTING POINT".

EQ

EC

12' 10"

C

- TILE STARTING POINT

03 ENLARGED PLAN: 9TH FLOOR BATHROOMS
1/2"=1'-0"

$$\frac{1}{2}'' = 1' - 0$$

AUSTRO TILE & STONE, LLC
30-25 93RD STREET
EAST ELMHURST, NY 11369

CONTRACTOR:
JRM CONSTRUCTION
MANAGEMENT, LLC
242 WEST 36TH STREET
11TH FLOOR
NEW YORK, NY 10018

INTERIOR DESIGNER

[illegible]

ISSUE FOR APPROVAL	10/09/23
ISSUE NAME	DATE

ABSTRACT:

SPACSMITH
ONE NEW YORK PLAZA
NEW YORK, NY 10004
PH:212 260 5583

PROJECT MAN

JACK RESNICK & SONS
255 GREENWICH STREET
NEW YORK, NY 10007

QUEST. NAME:

PLAN
9TH FLOOR BATHROOMS

DATE:
PROJECT NO.:
PRINCIPAL:
DRAWING BY:
CHECKED BY:
SCALE:
DWG No.:




T-400



(BT-1) TILE BASE GROUT JOINTS WILL NOT ALIGN WITH (WT-1) WALL TILE GROUT JOINTS

(AT-1) ACCENT WALL TILE GROUT JOINTS WILL NOT ALIGN WITH (WT-1) WALL TILE GROUT JOINTS

AUSTRO TILE & STONE, LLC
30-25 93RD STREET
EAST ELMHURST, NY 11369

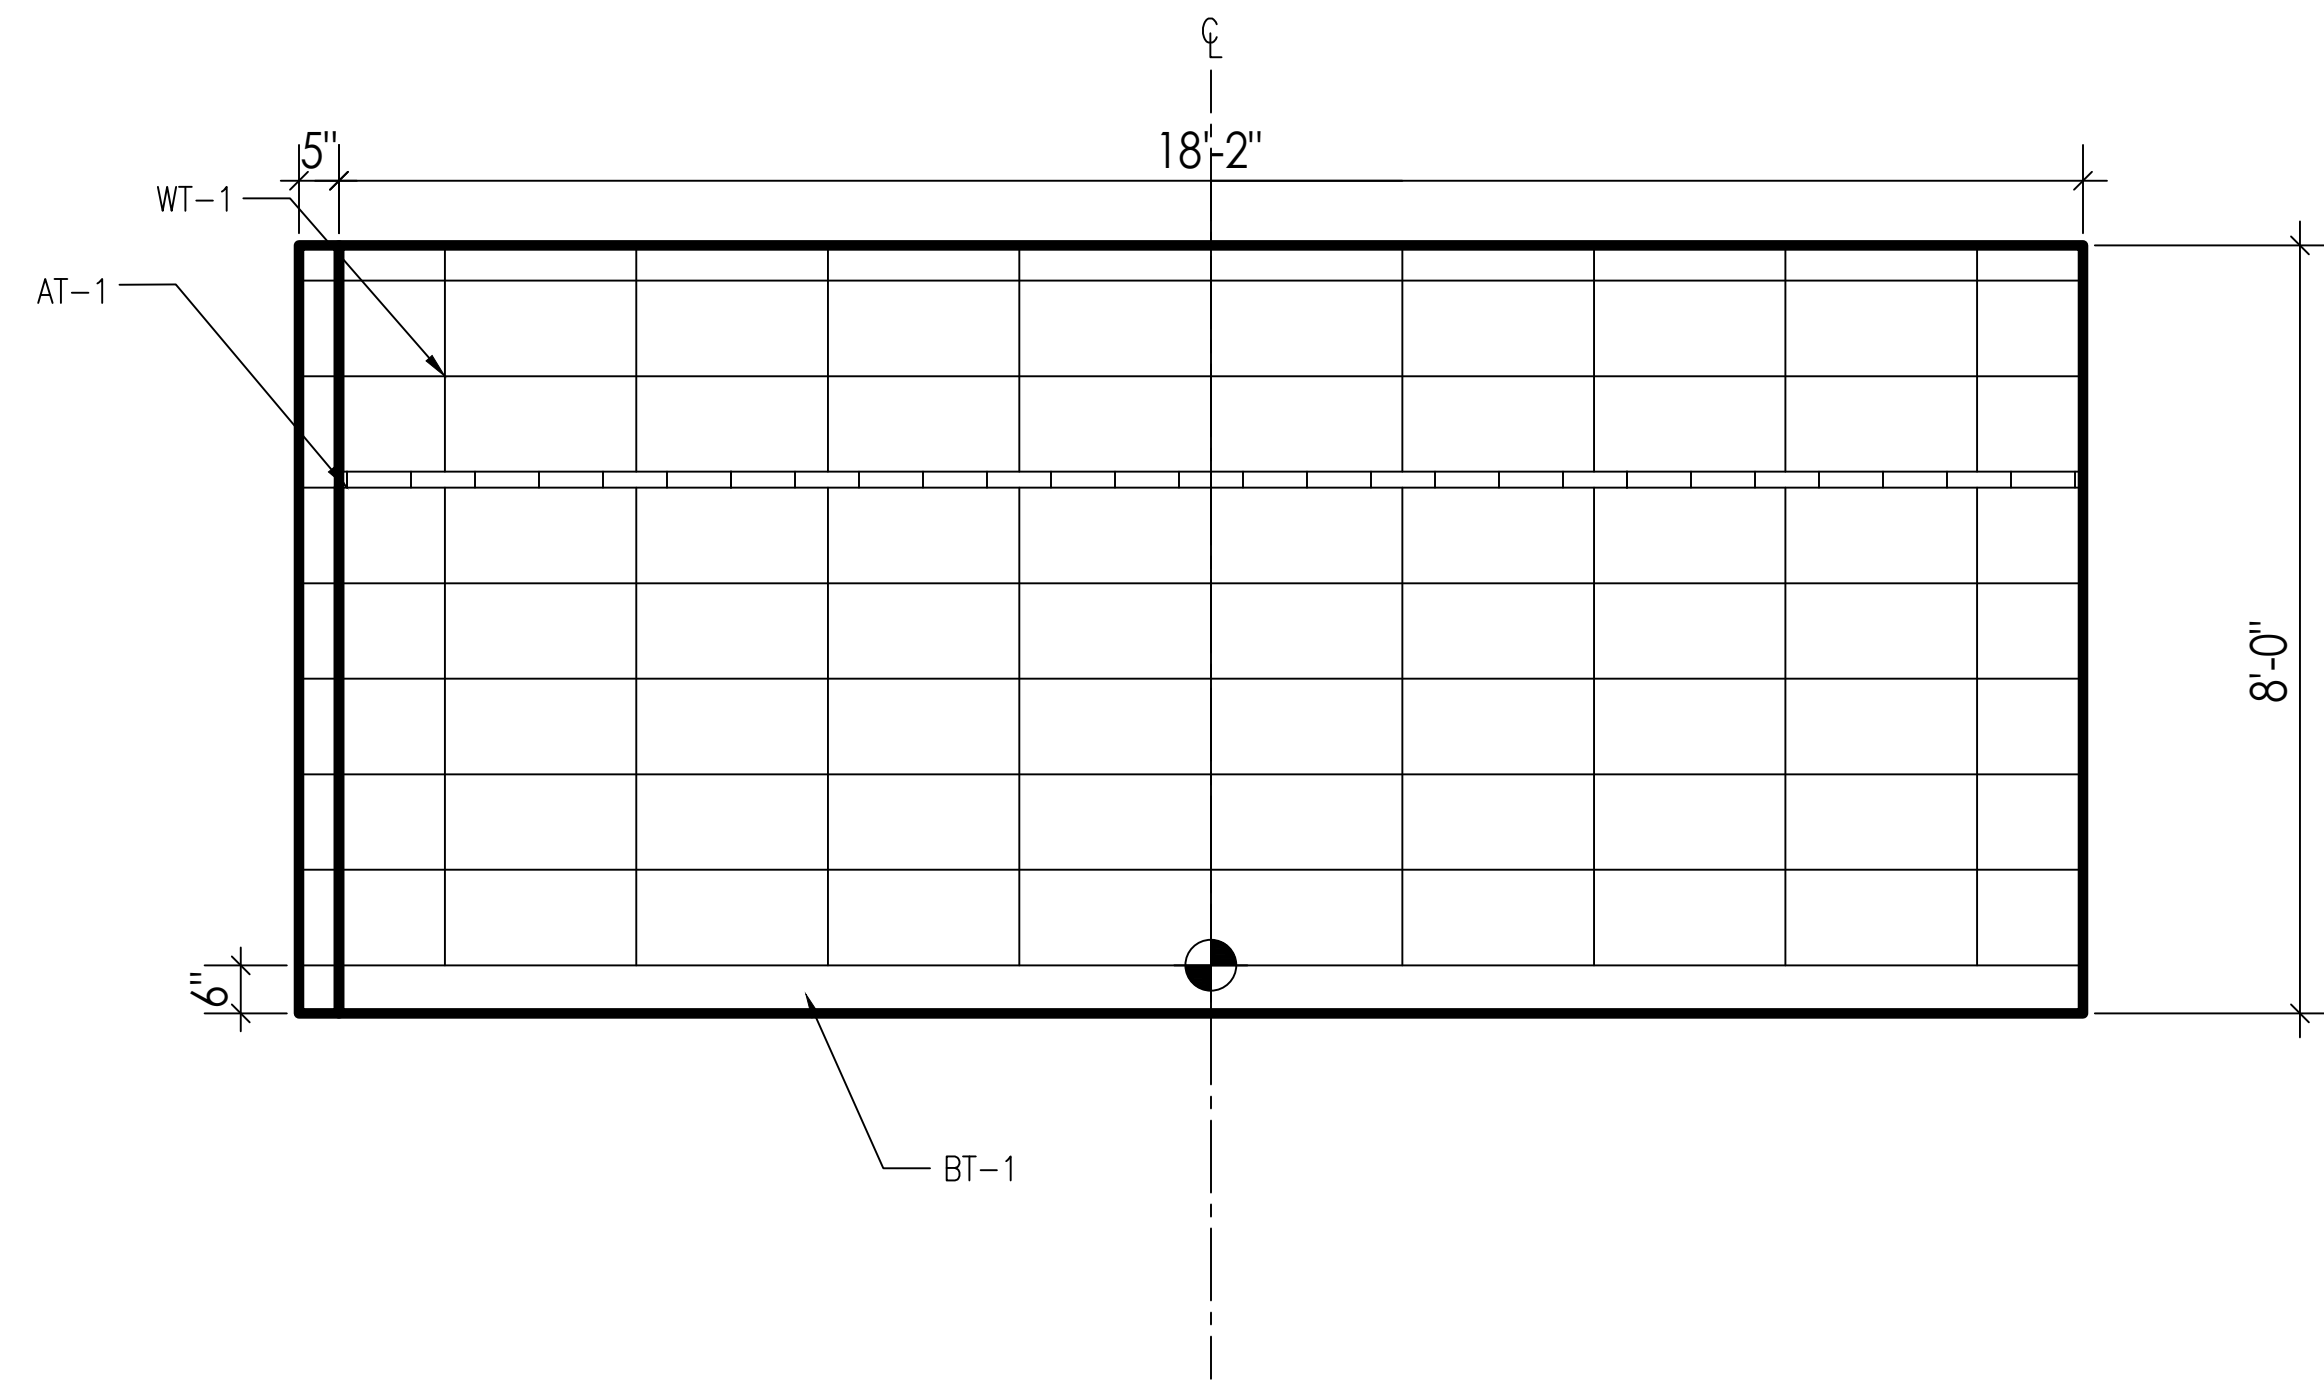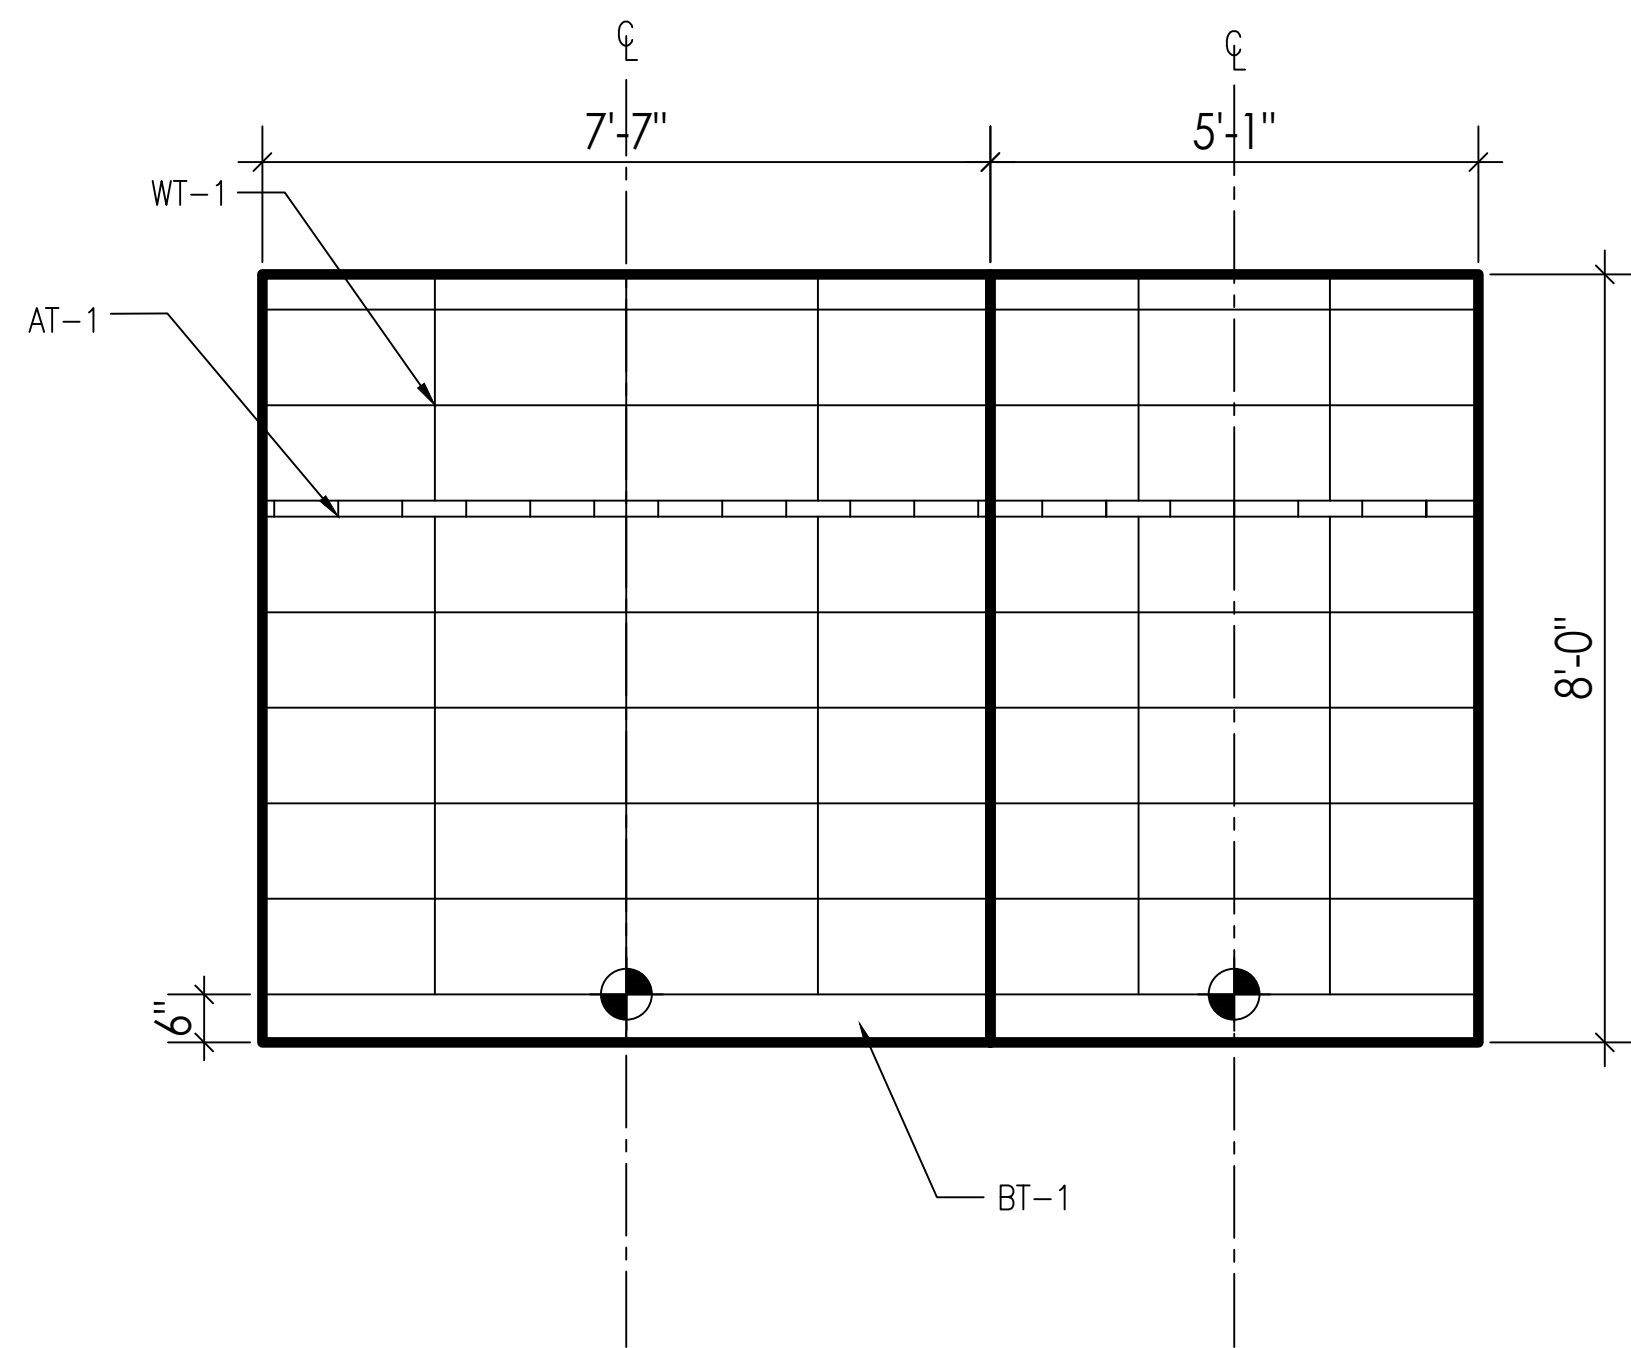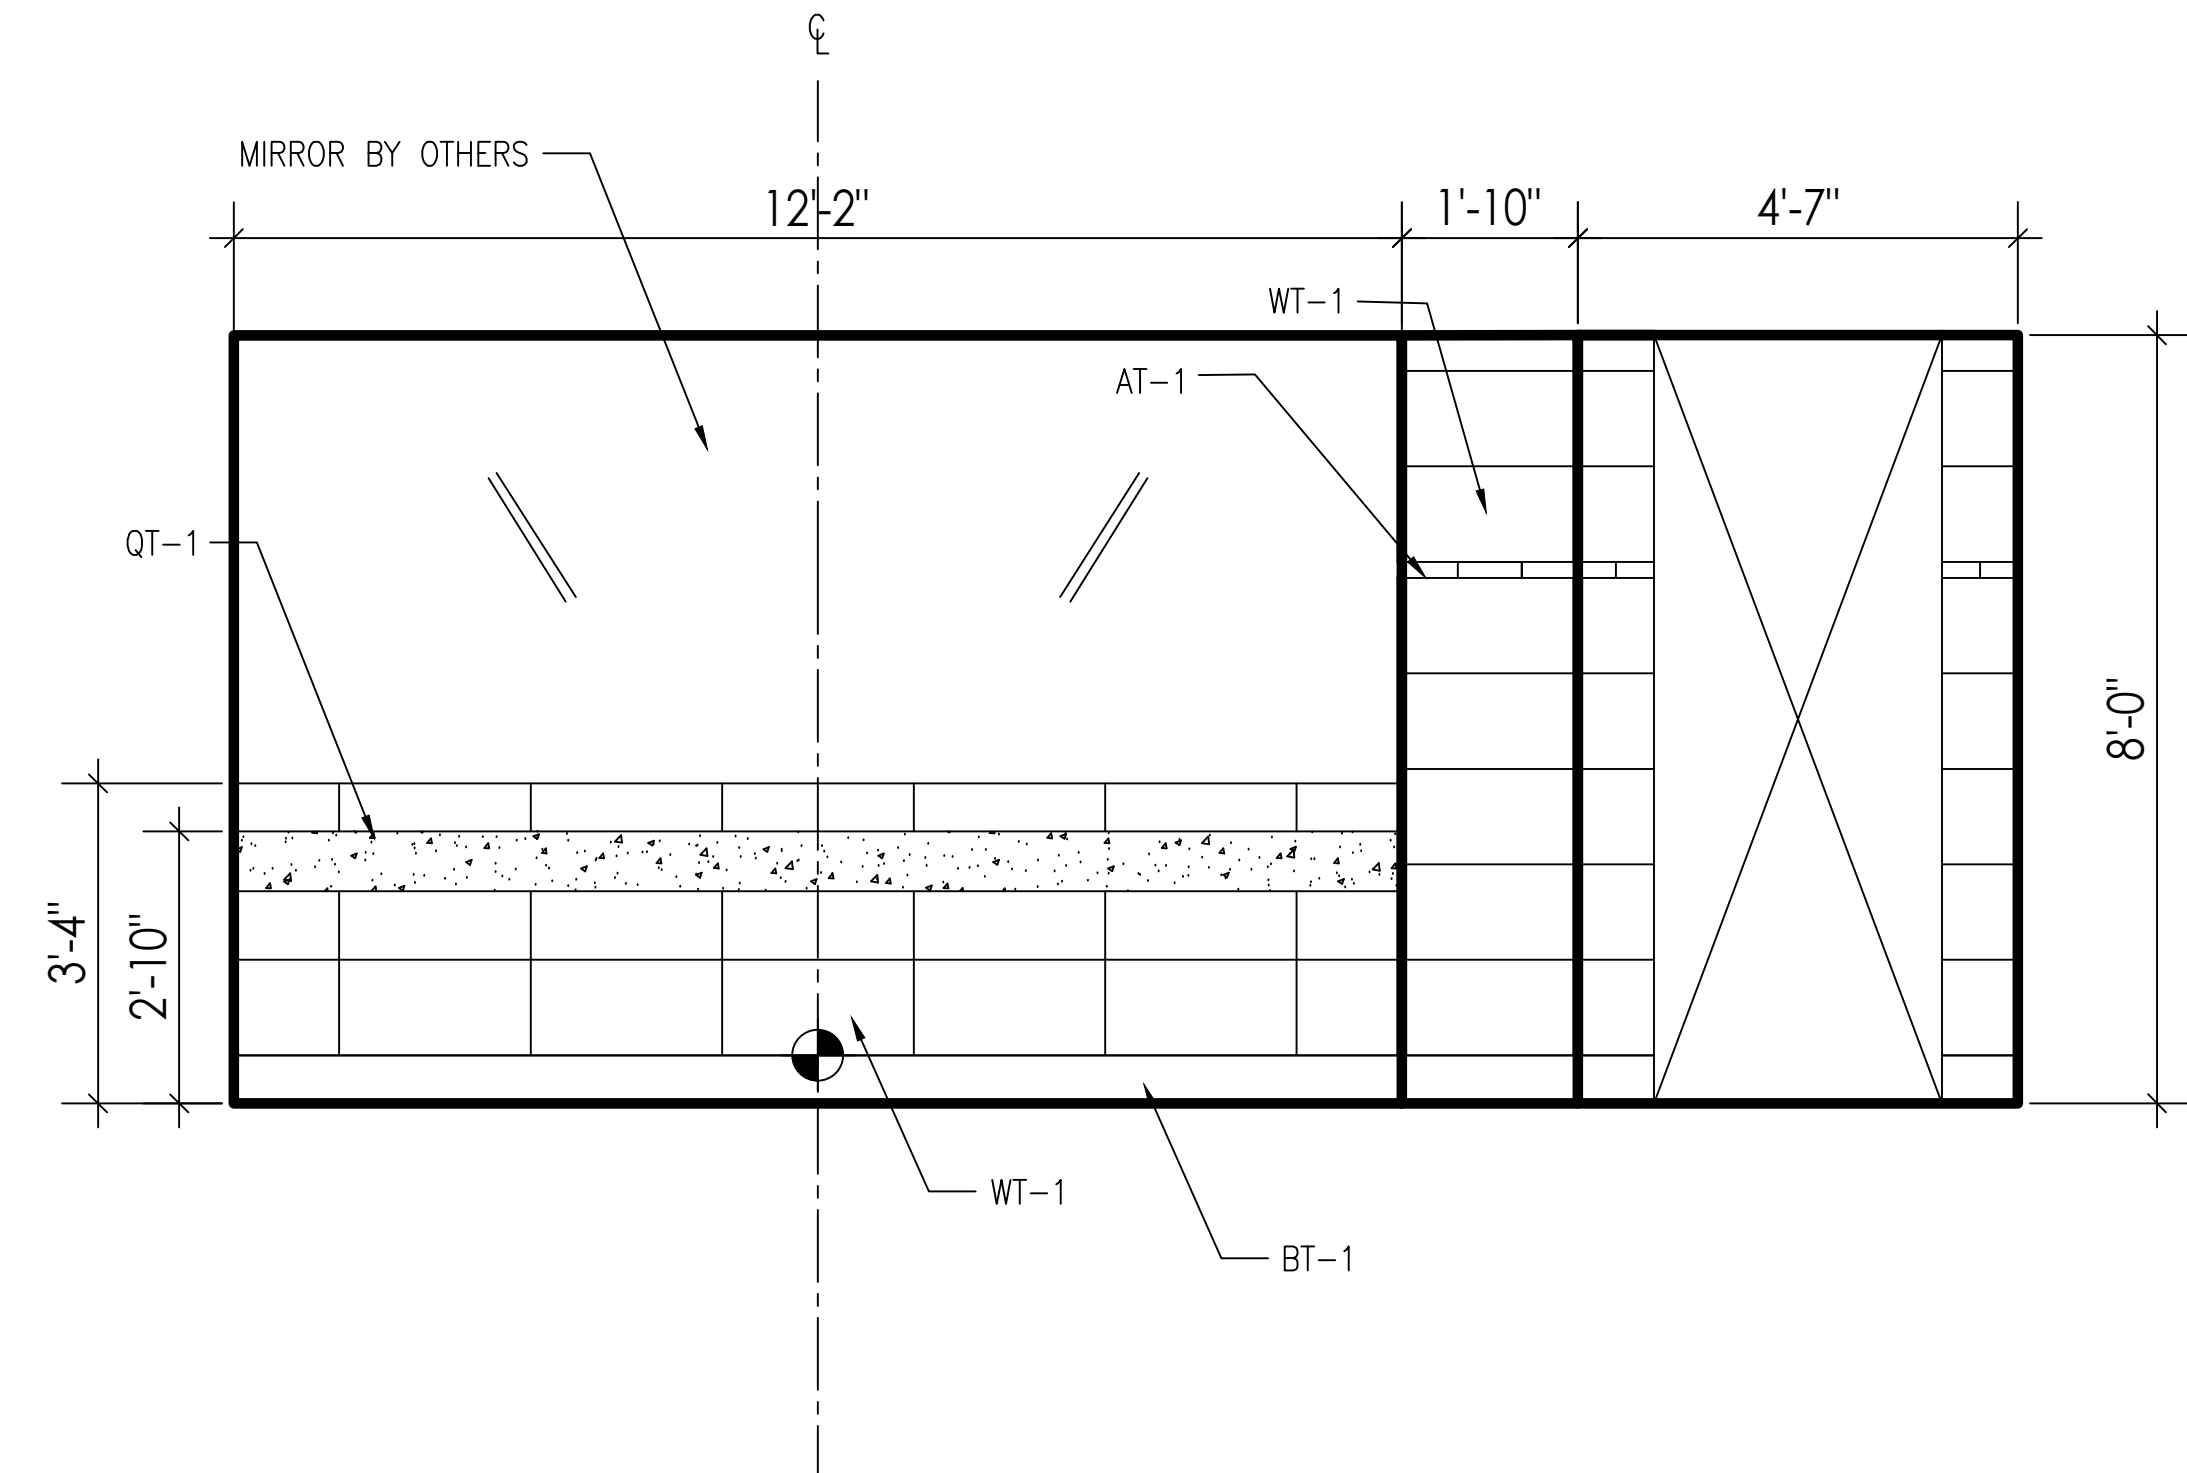



02
1/2"=1'-0" ELEVATIONS: 9TH FLOOR BATHROOMS

03
1/2"=1'-0" ELEVATIONS: 9TH FLOOR BATHROOMS

04
1/2"=1'-0" ELEVATIONS: 9TH FLOOR BATHROOMS


WOMEN'S POWDER ROOM

901

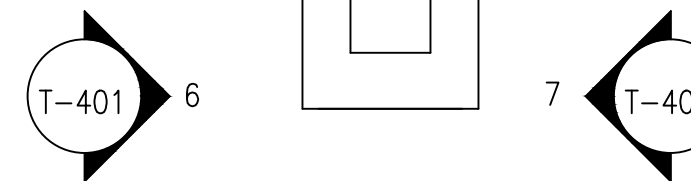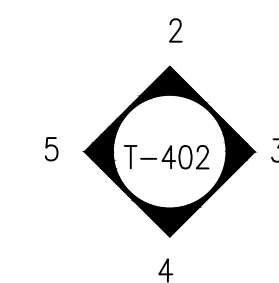




WOMEN'S RESTROOM

902

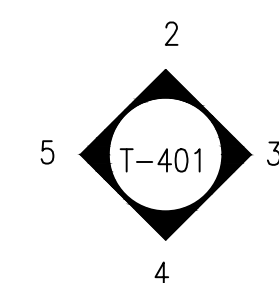


MEN'S RESTROOM


903

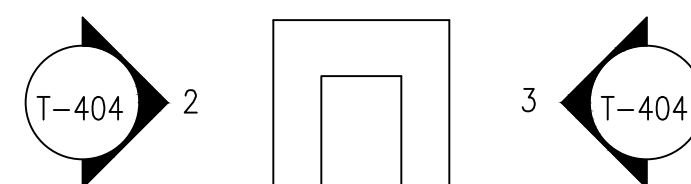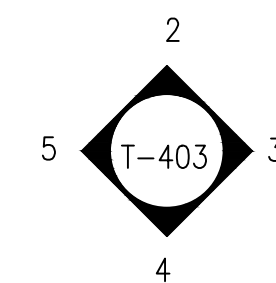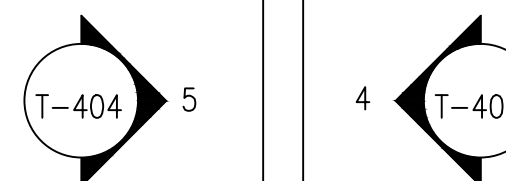


01
1/2"=1'-0" PLAN #2: 9TH FLOOR BATHROOMS

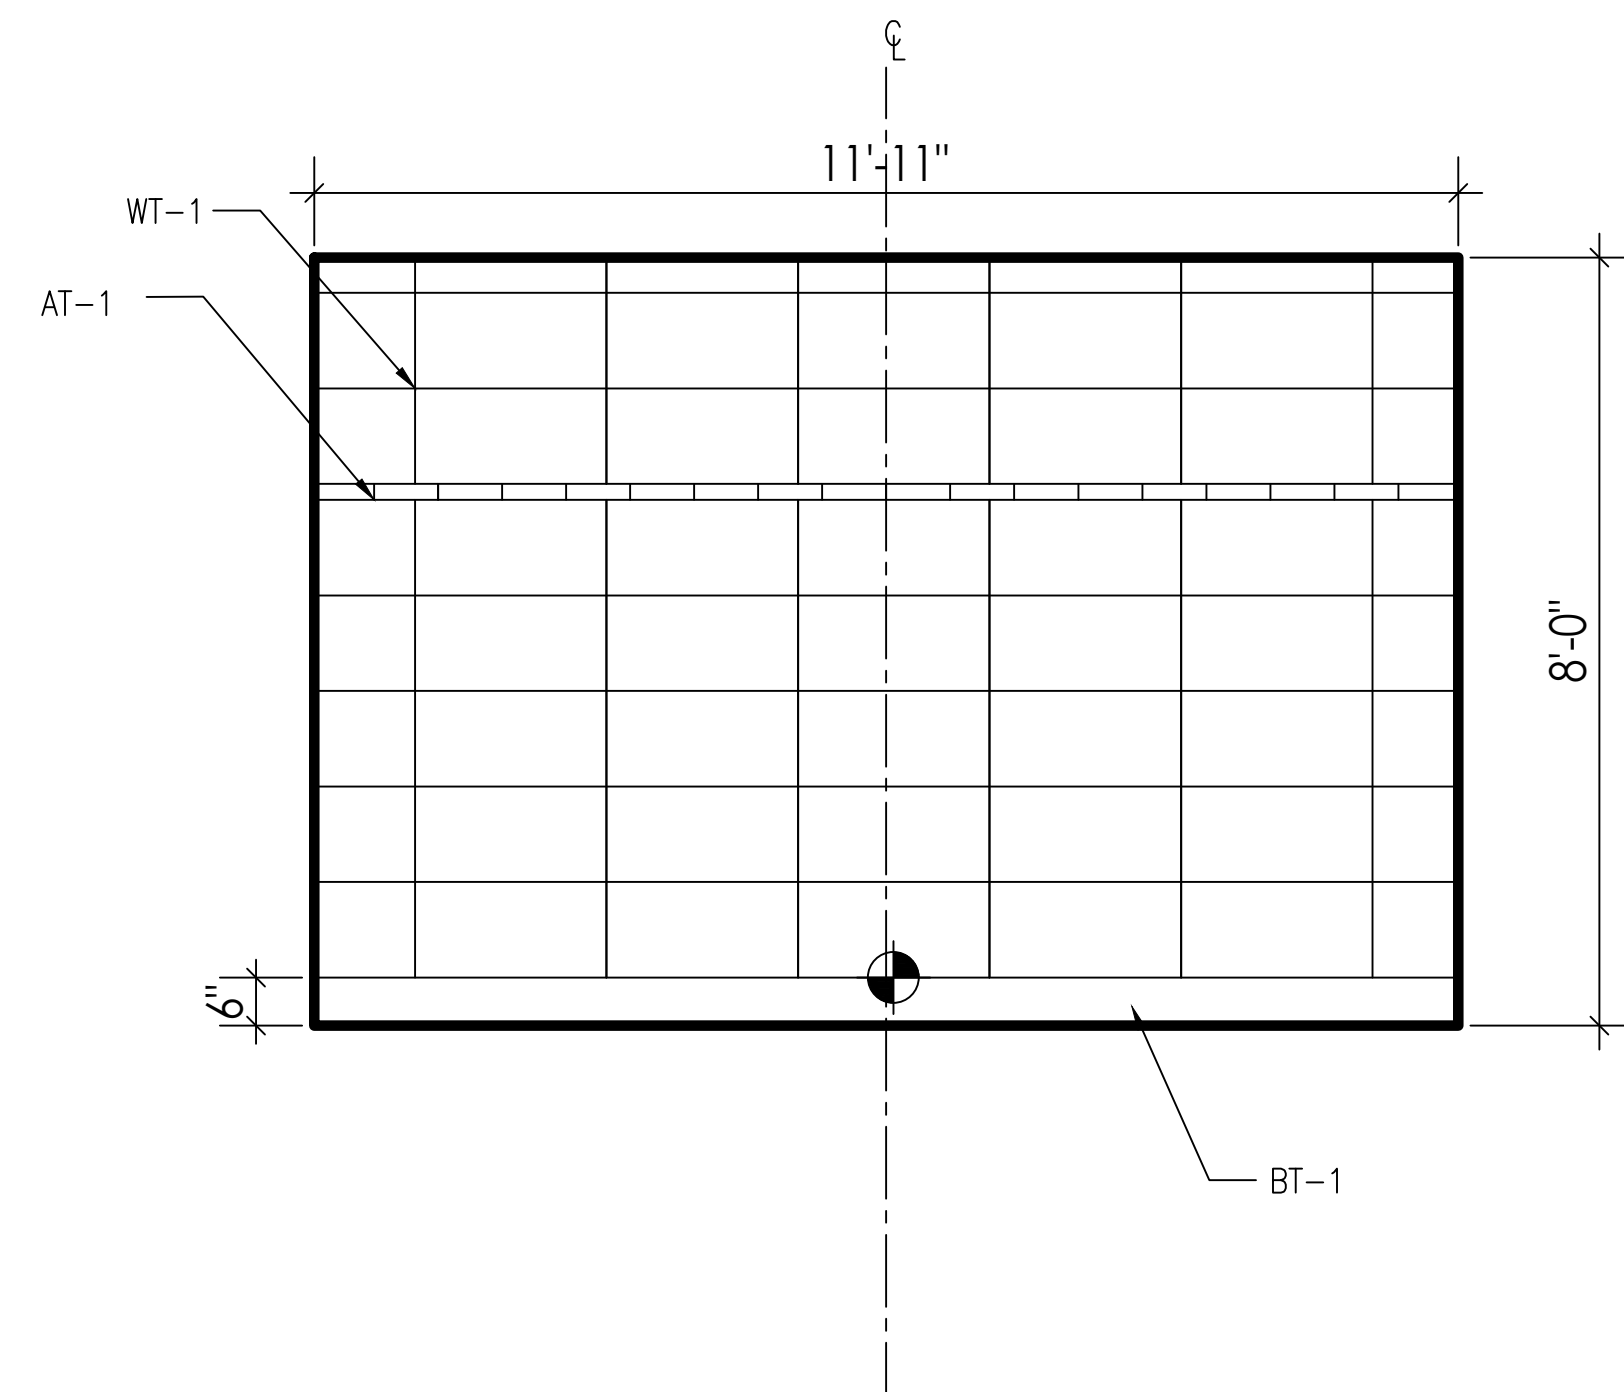

05
1/2"=1'-0" ELEVATIONS: 9TH FLOOR BATHROOMS

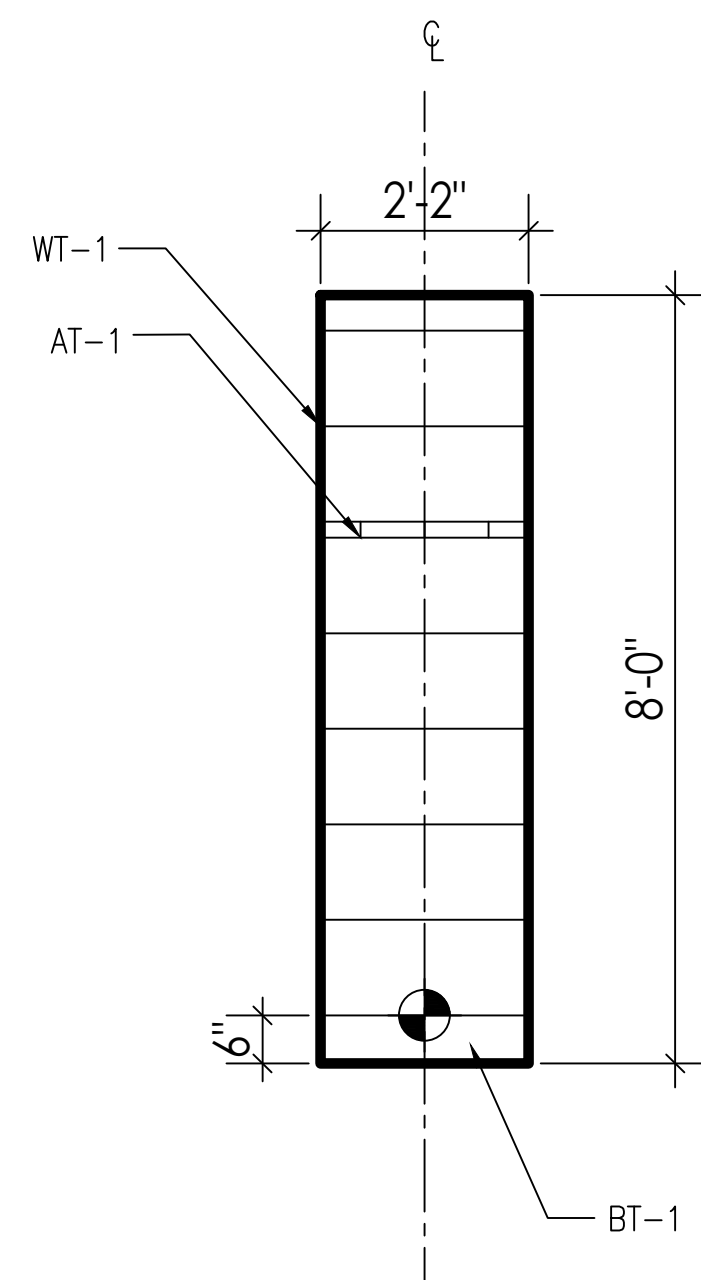

06
1/2"=1'-0" ELEVATIONS: 9TH FLOOR BATHROOMS

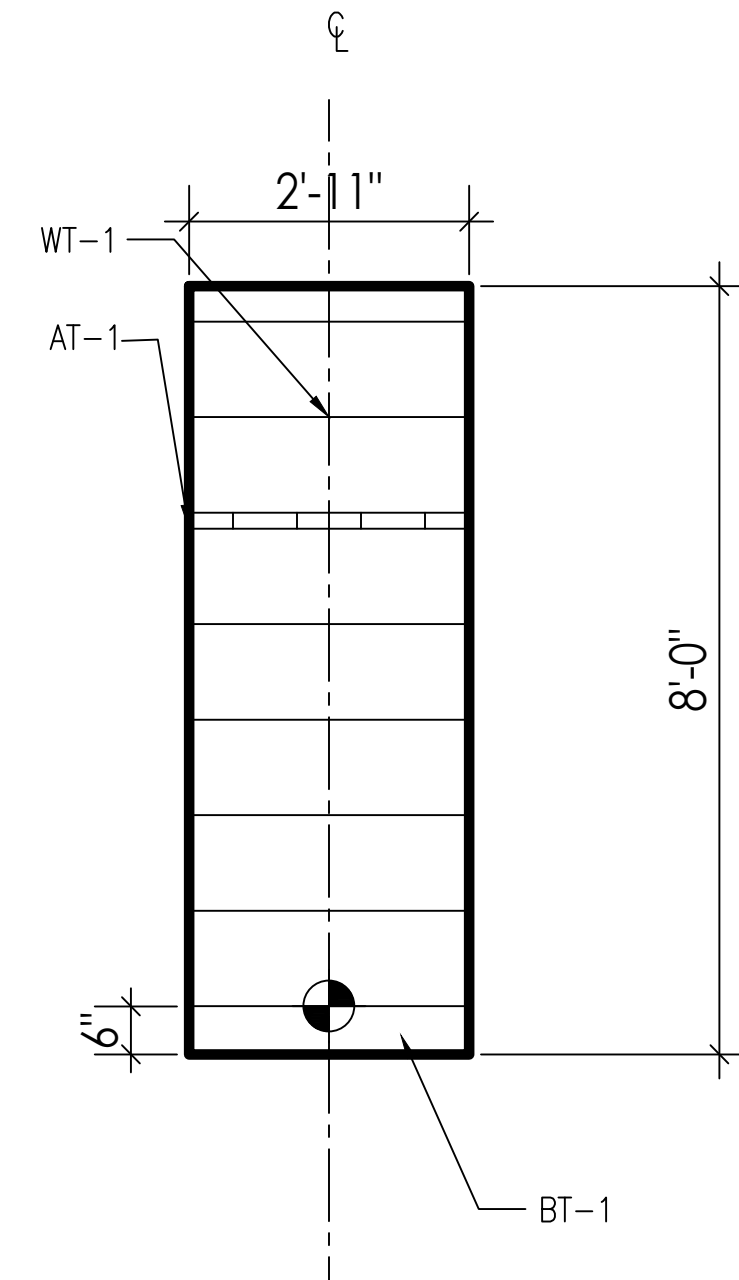

07
1/2"=1'-0" ELEVATIONS: 9TH FLOOR BATHROOMS

CONTRACTOR:
JRM CONSTRUCTION
MANAGEMENT, LLC
242 WEST 36TH STREET
11TH FLOOR
NEW YORK, NY 10018

INTERIOR DESIGNER:

ISSUE FOR APPROVAL 10/09/23
ISSUE NAME DATE

ARCHITECT:
SPACESMITH
ONE NEW YORK PLAZA
NEW YORK, NY 10004
PH:212 260 5583

PROJECT NAME:
JACK RESNICK & SONS
255 GREENWICH STREET
NEW YORK, NY 10007

SHEET NAME:
ELEVATIONS
9TH FLOOR BATHROOMS

DATE:
PROJECT NO.:
PRINCIPAL:
DRAWING BY:
CHECKED BY:
SCALE:
DWG. No.:
T-401
19 of 29




STARTING POINT

(BT-1) TILE BASE GROUT JOINTS WILL NOT ALIGN WITH (WT-1) WALL TILE GROUT JOINTS

(AT-1) ACCENT WALL TILE GROUT JOINTS WILL NOT ALIGN WITH (WT-1) WALL TILE GROUT JOINTS


WOMEN'S
POWDER ROOM

901

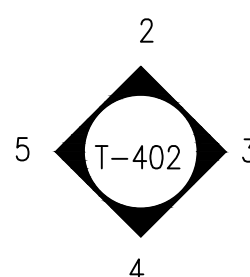




WOMEN'S
RESTROOM

902

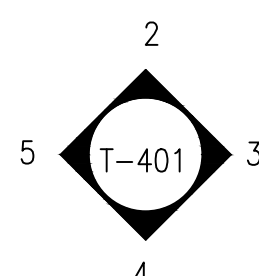


MEN'S
RESTROOM


903

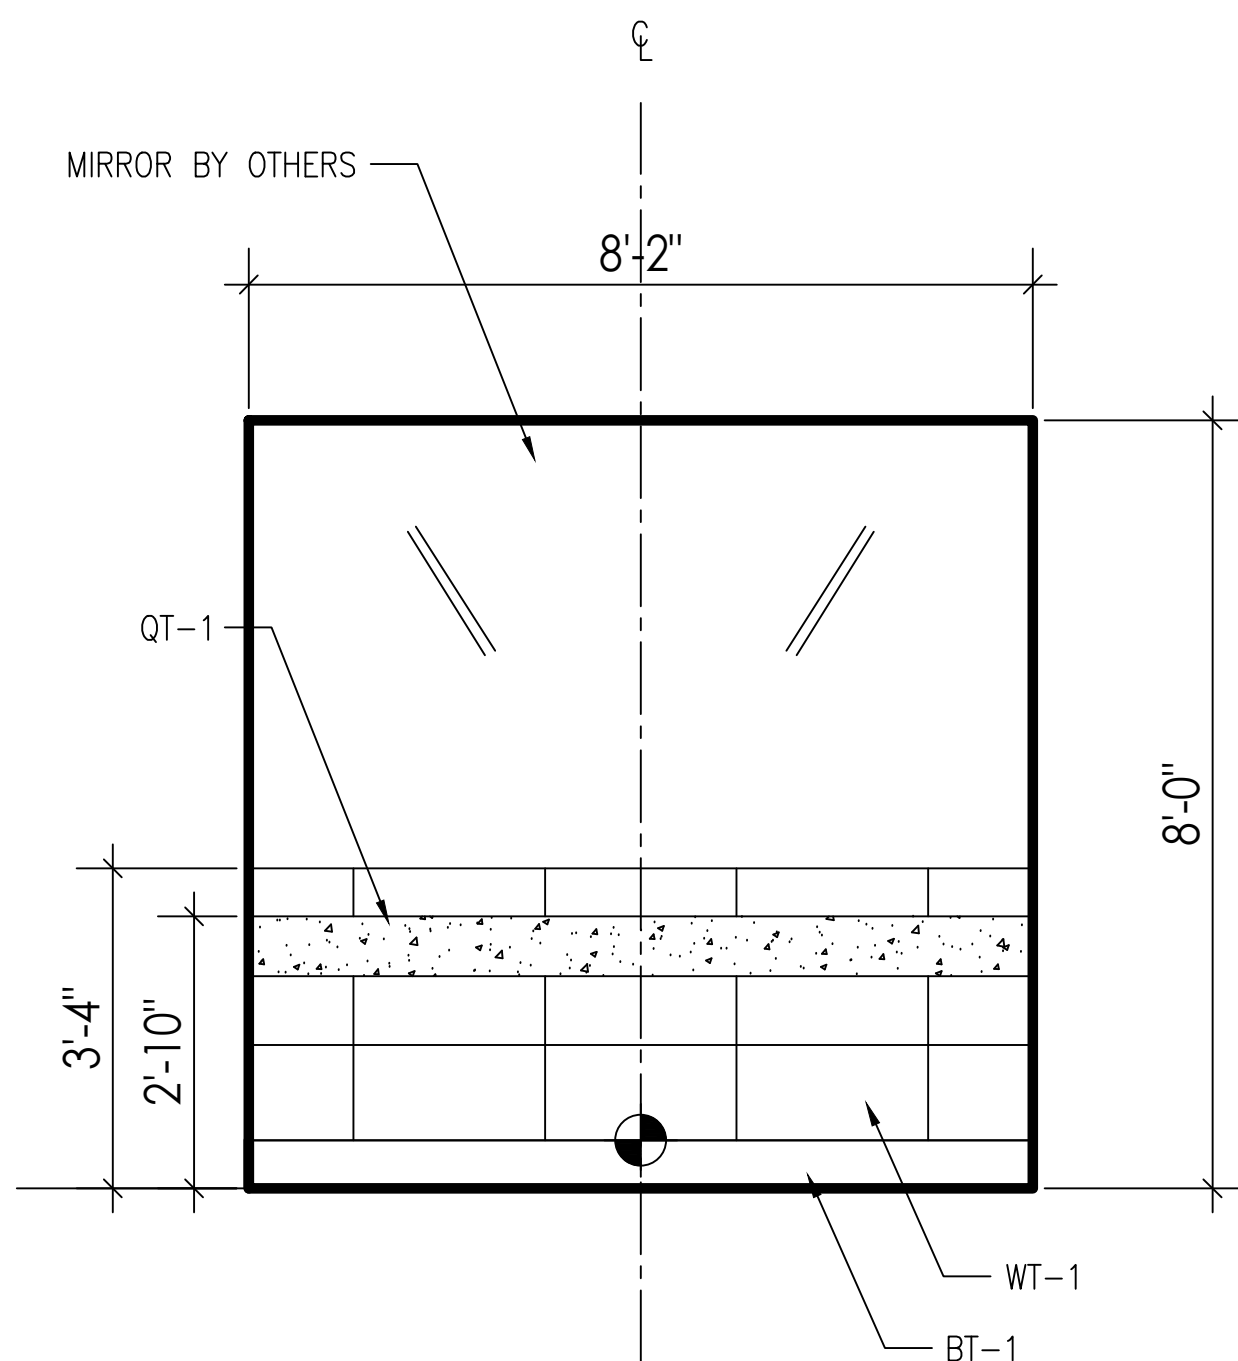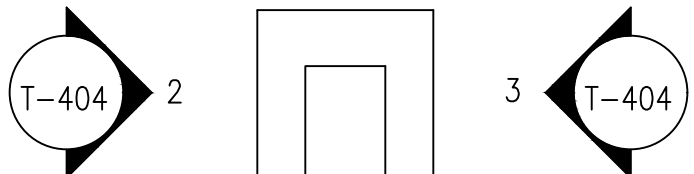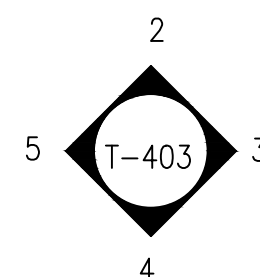


02
1/2"=1'-0" ELEVATIONS: 9TH FLOOR BATHROOMS

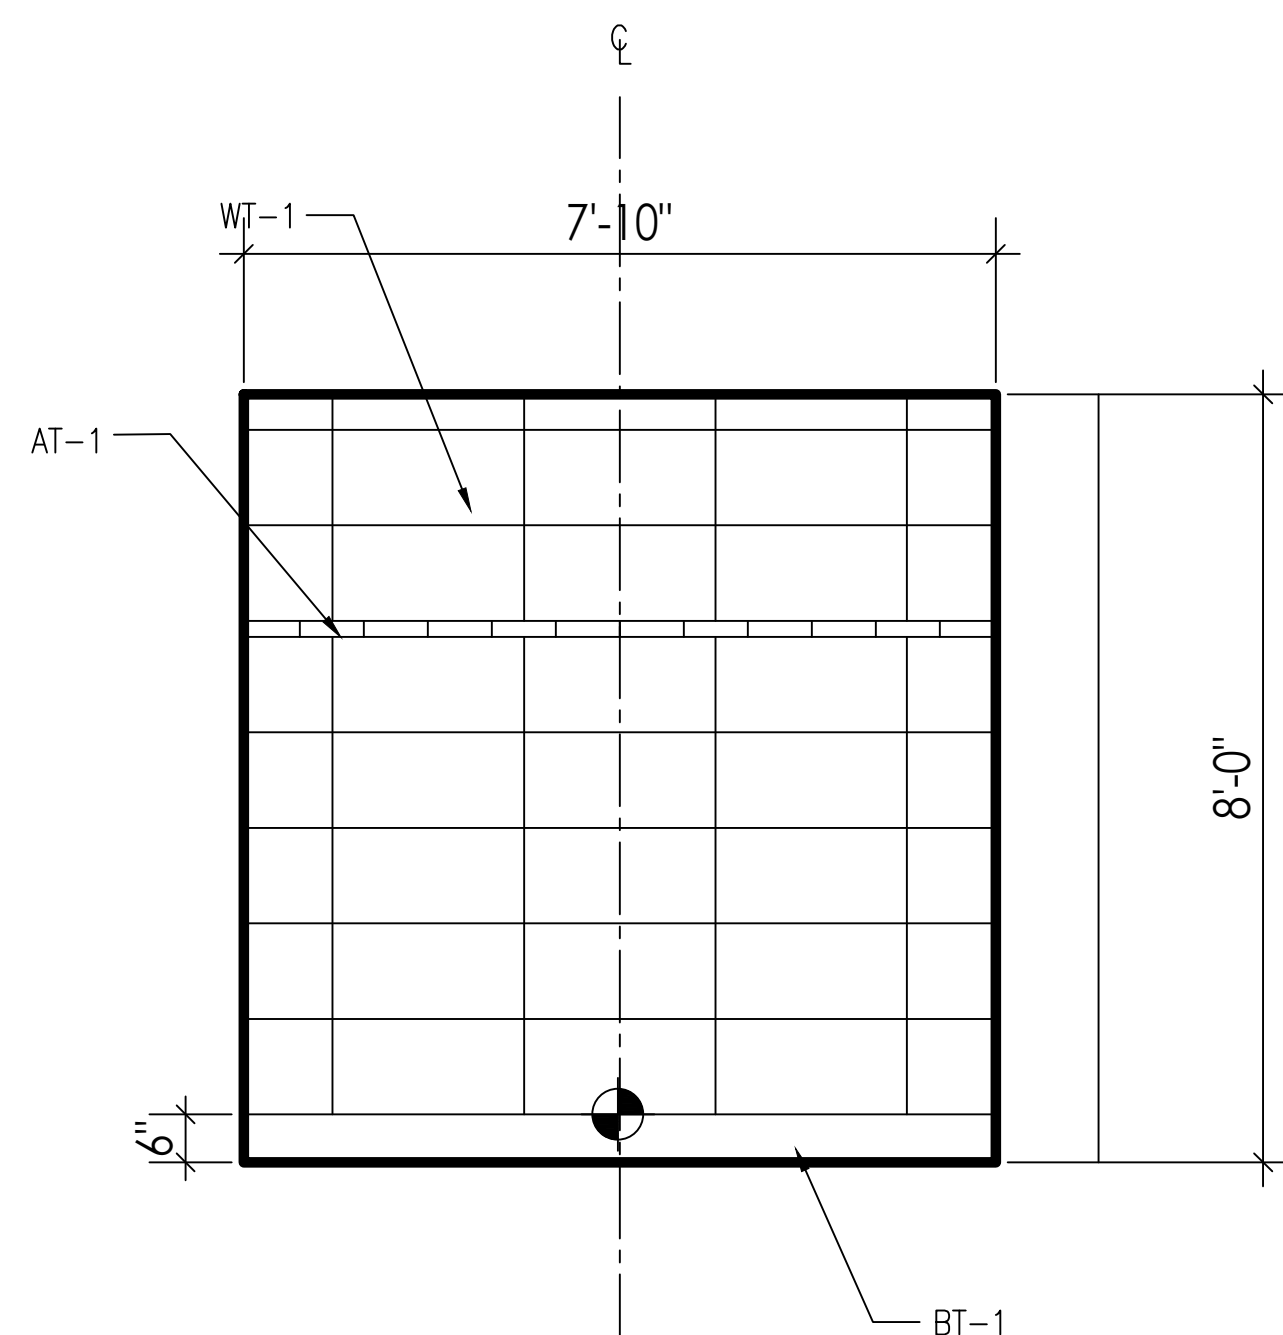

03
1/2"=1'-0" ELEVATIONS: 9TH FLOOR BATHROOMS

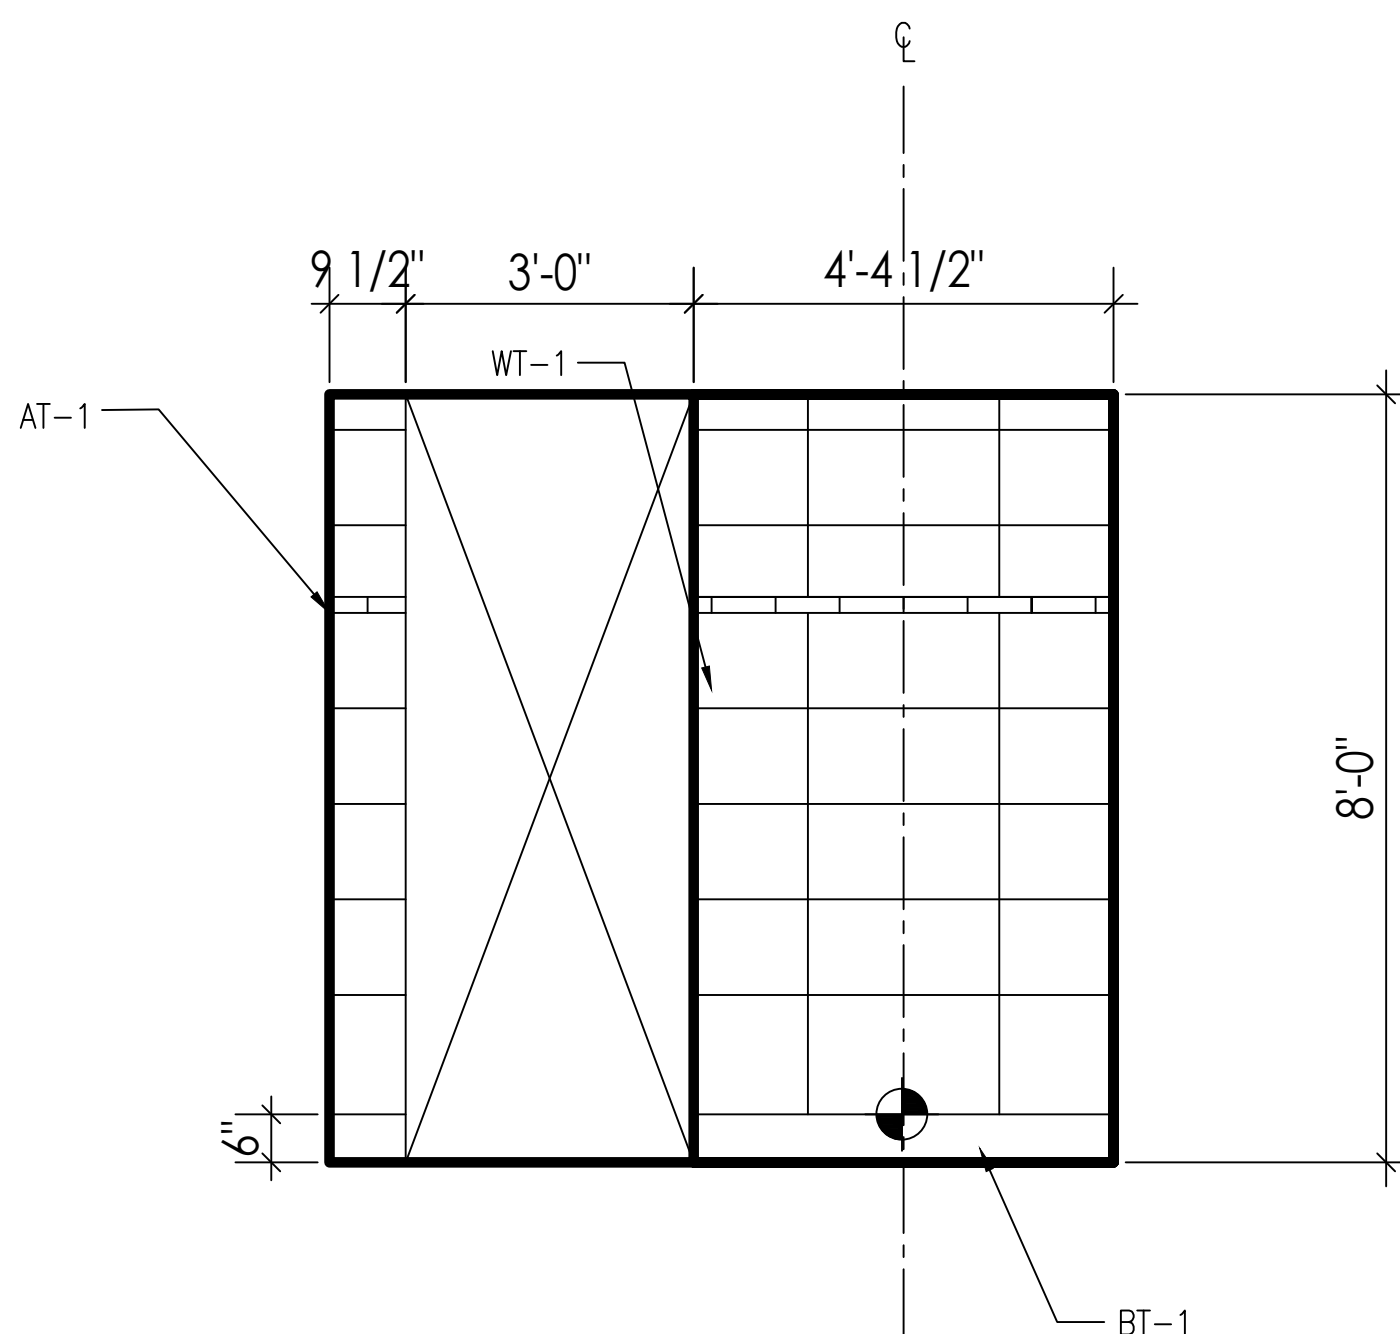

04
1/2"=1'-0" ELEVATIONS: 9TH FLOOR BATHROOMS

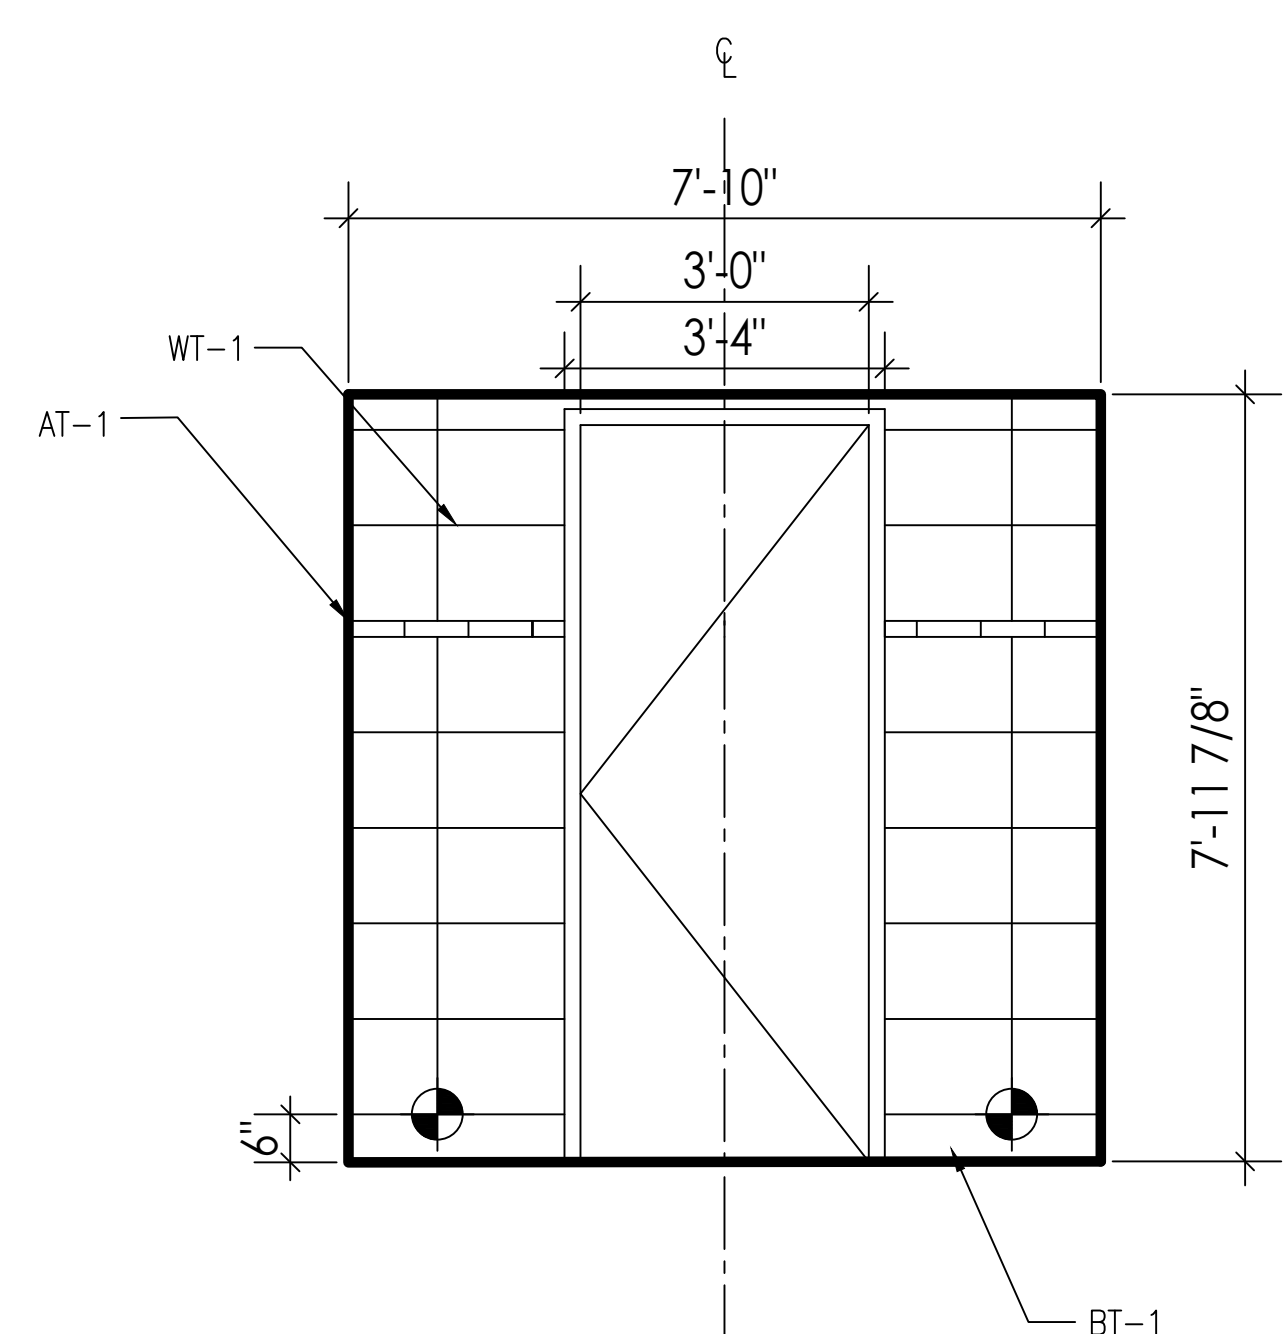

05
1/2"=1'-0" ELEVATIONS: 9TH FLOOR BATHROOMS

AUSTRO TILE & STONE, LLC
30-25 93RD STREET
EAST ELMHURST, NY 11369

CONTRACTOR:
JRM CONSTRUCTION
MANAGEMENT, LLC
242 WEST 36TH STREET
11TH FLOOR
NEW YORK, NY 10018

INTERIOR DESIGNER:

ISSUE FOR APPROVAL 10/09/23
ISSUE NAME DATE

ARCHITECT:
SPACESMITH
ONE NEW YORK PLAZA
NEW YORK, NY 10004
PH:212 260 5583

PROJECT NAME:
JACK RESNICK & SONS
255 GREENWICH STREET
NEW YORK, NY 10007

SHEET NAME:
ELEVATIONS
9TH FLOOR BATHROOMS

DATE:
PROJECT NO.:
PRINCIPAL:
DRAWING BY:
CHECKED BY:
SCALE:
DWG. No.:
T-402
20 of 29





STARTING POINT

(BT-1) TILE BASE GROUT JOINTS WILL NOT ALIGN WITH (WT-1) WALL TILE GROUT JOINTS

(AT-1) ACCENT WALL TILE GROUT JOINTS WILL NOT ALIGN WITH (WT-1) WALL TILE GROUT JOINTS

AUSTRO TILE & STONE, LLC
30-25 93RD STREET
EAST ELMHURST, NY 11369

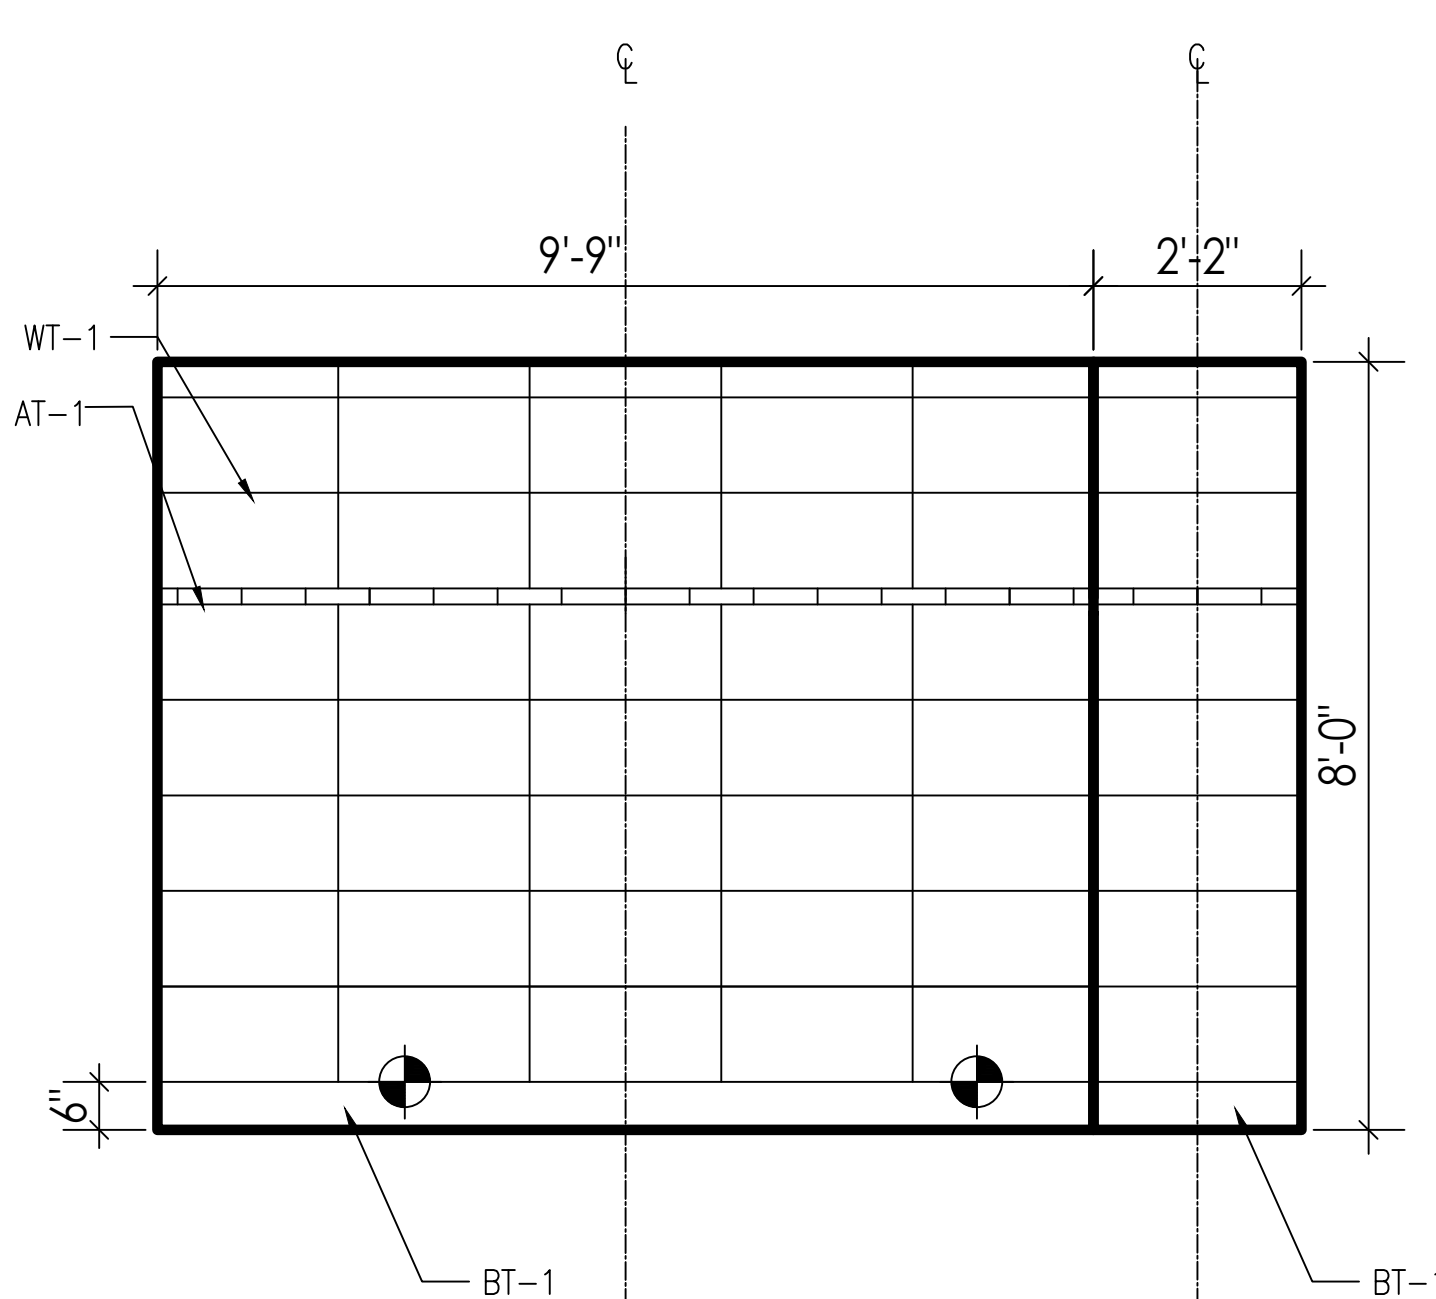
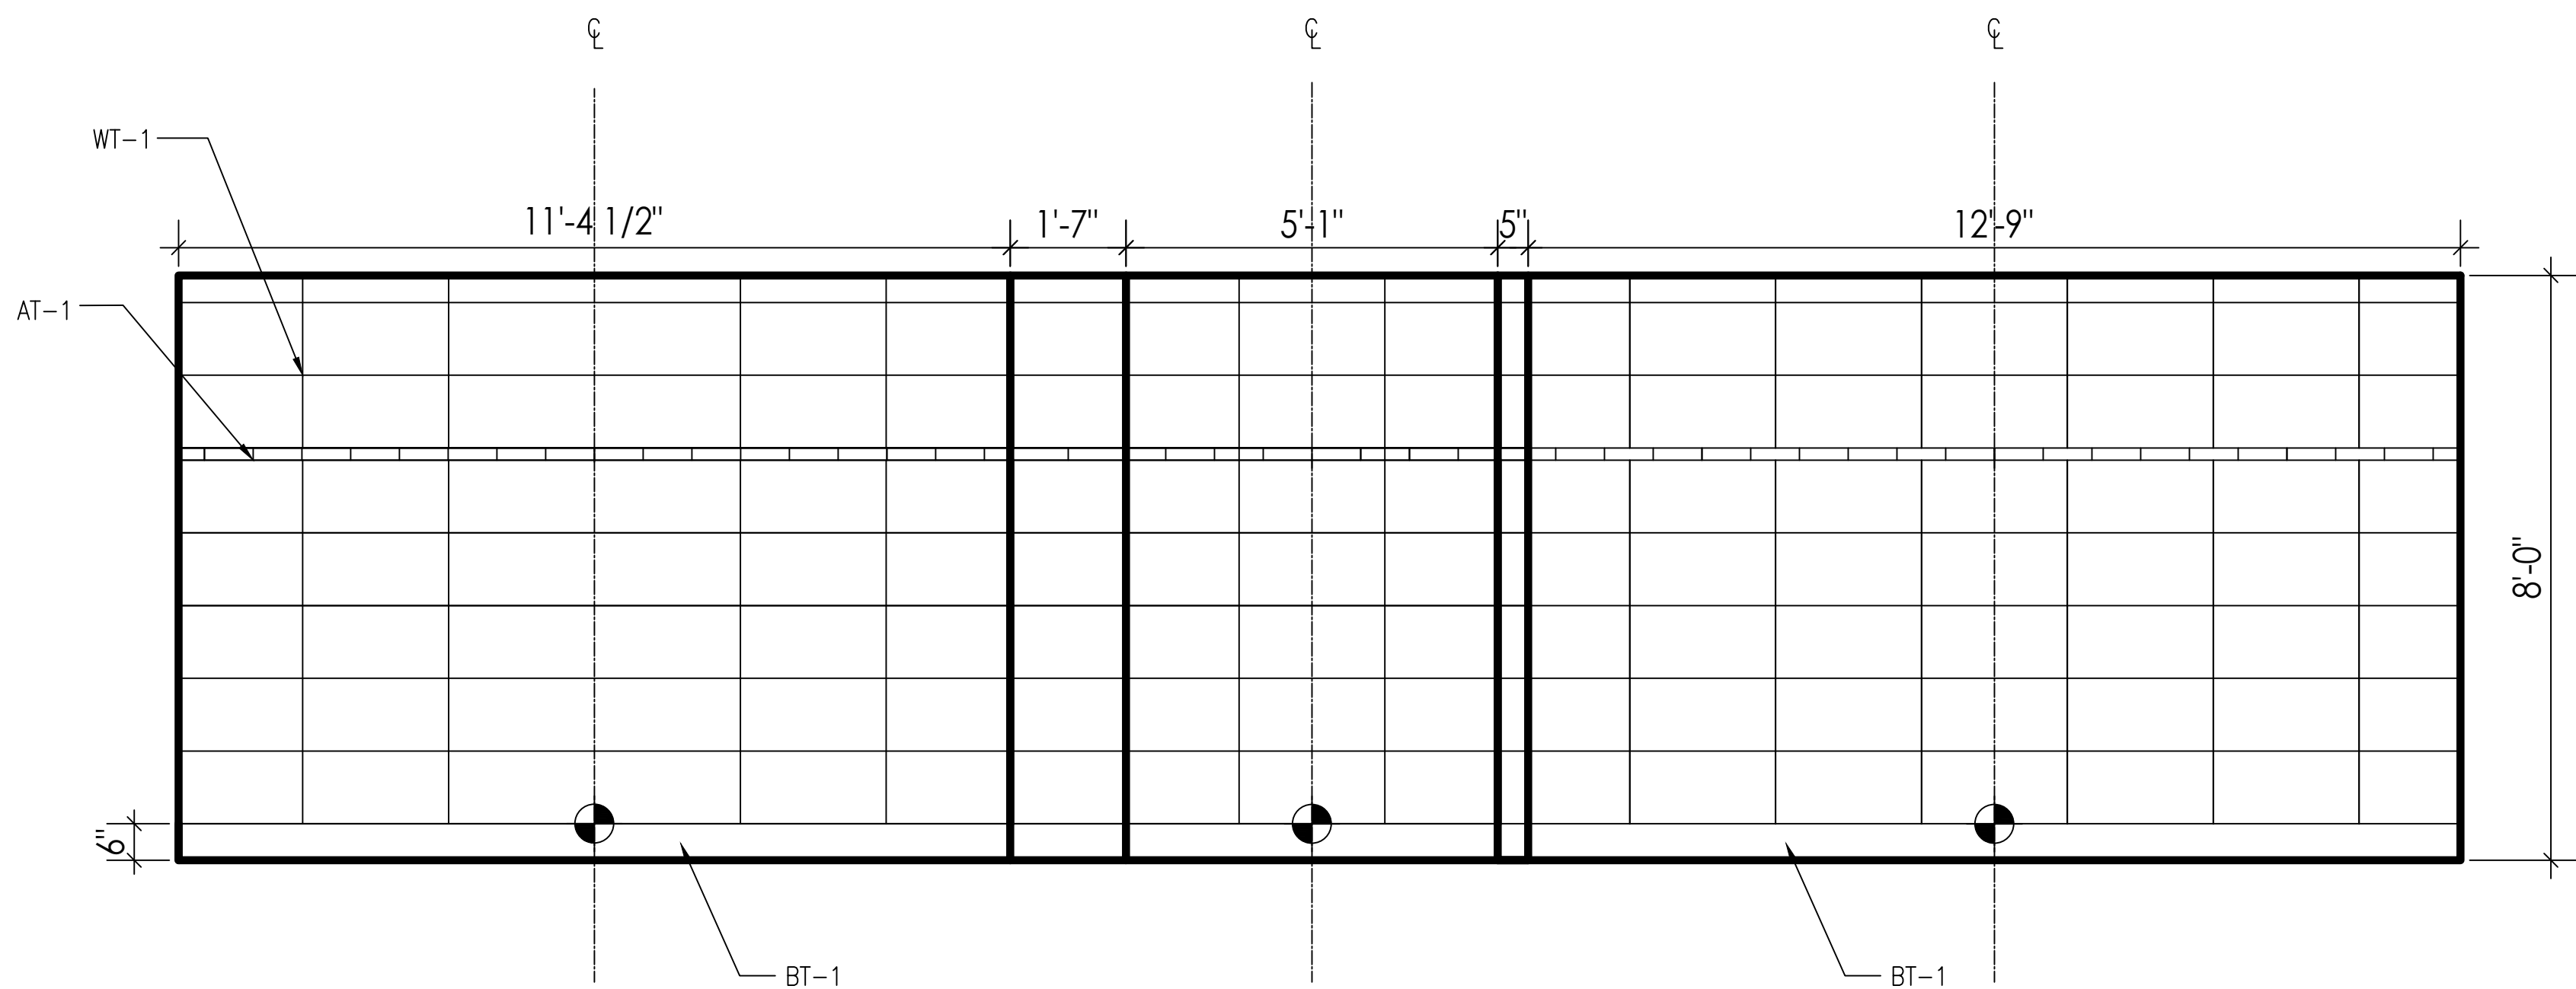


02
1/2"=1'-0" ELEVATIONS: 9TH FLOOR BATHROOMS

03
1/2"=1'-0" ELEVATIONS: 9TH FLOOR BATHROOMS


WOMEN'S POWDER ROOM

901

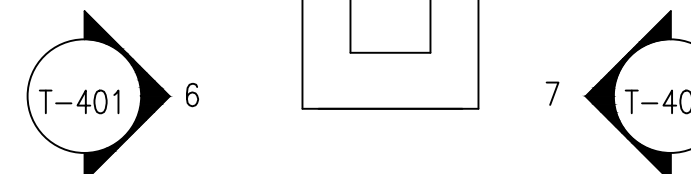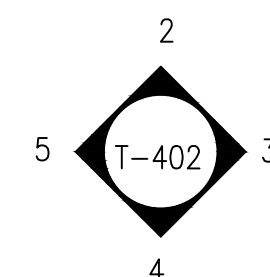





WOMEN'S RESTROOM

902

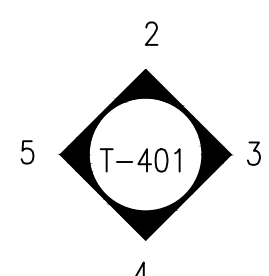


MEN'S RESTROOM

903

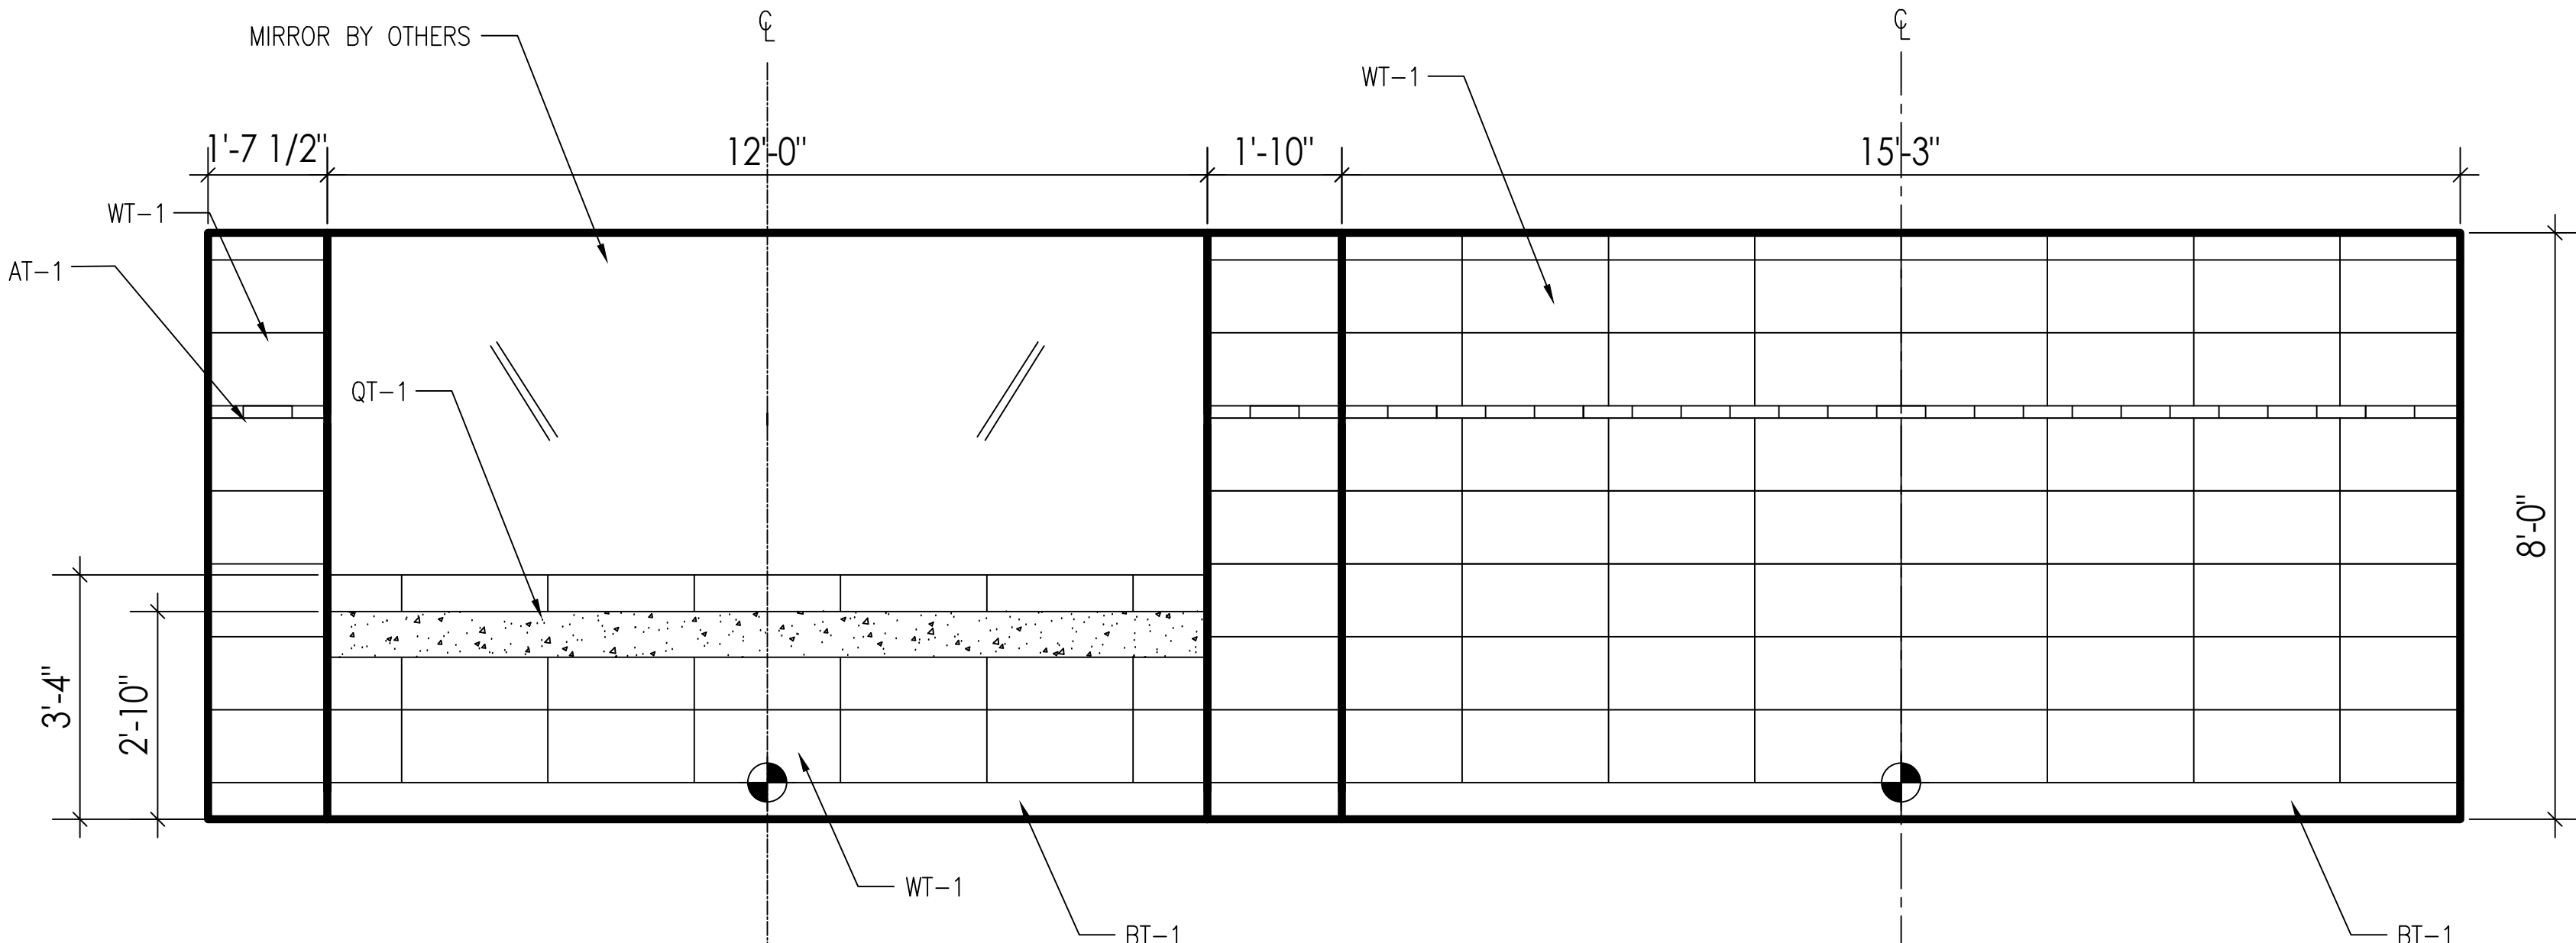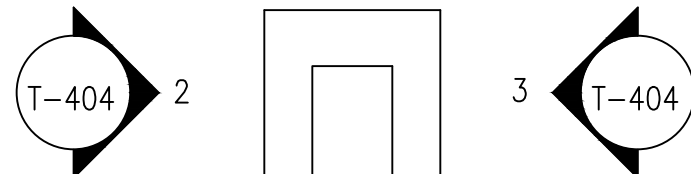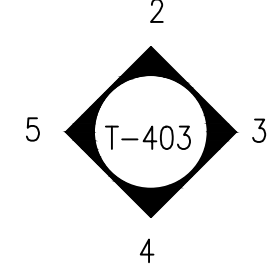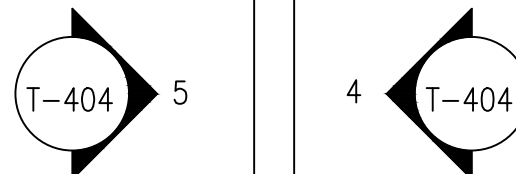

04
1/2"=1'-0" ELEVATIONS: 9TH FLOOR BATHROOMS

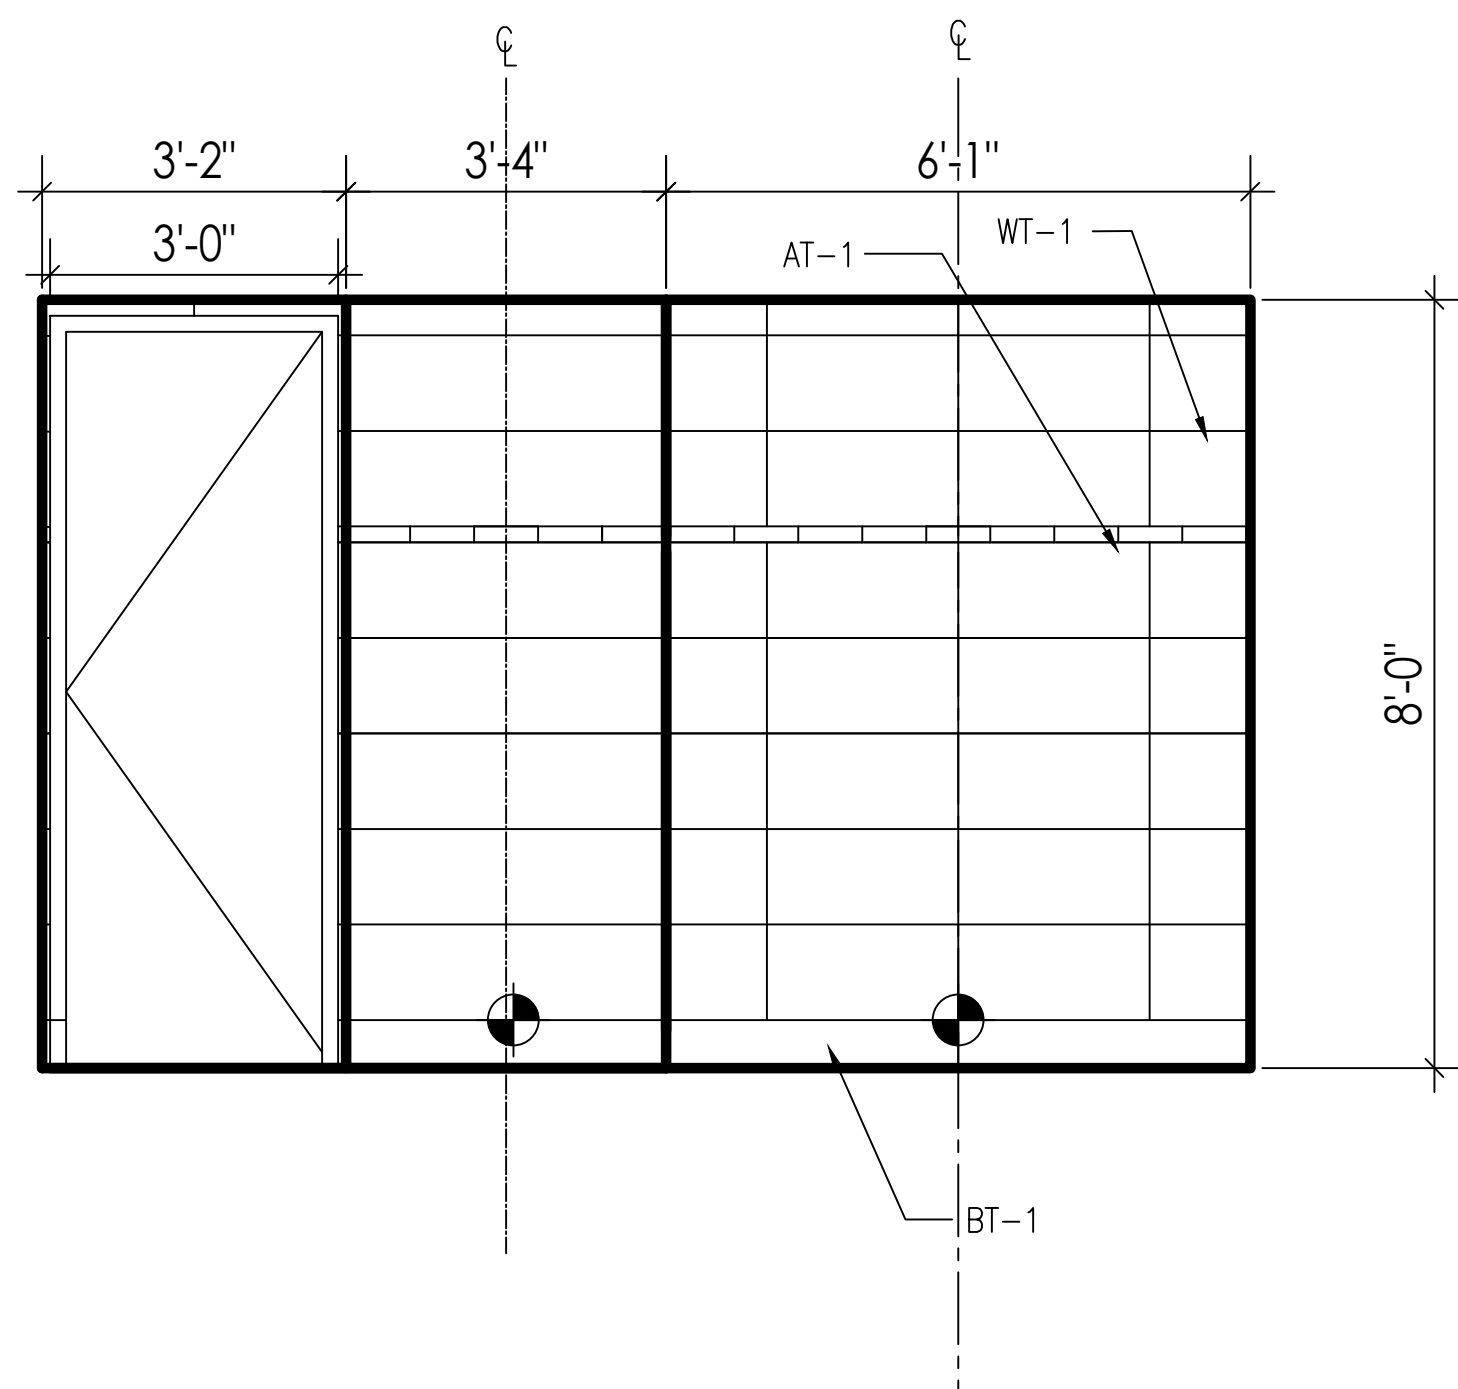

05
1/2"=1'-0" ELEVATIONS: 9TH FLOOR BATHROOMS

01
1/2"=1'-0" PLAN #2: 9TH FLOOR BATHROOMS

CONTRACTOR:
JRM CONSTRUCTION
MANAGEMENT, LLC
242 WEST 36TH STREET
11TH FLOOR
NEW YORK, NY 10018

INTERIOR DESIGNER:

ISSUE FOR APPROVAL 10/09/23
ISSUE NAME DATE

ARCHITECT:

SPACESMITH
ONE NEW YORK PLAZA
NEW YORK, NY 10004
PH:212 260 5583

PROJECT NAME:

JACK RESNICK & SONS
255 GREENWICH STREET
NEW YORK, NY 10007

SHEET NAME:

ELEVATIONS
9TH FLOOR BATHROOMS

DATE:
PROJECT NO.:
PRINCIPAL:
DRAWING BY:
CHECKED BY:
SCALE:
DWG. No.:
T-403

21 of 29




STARTING POINT

(BT-1) TILE BASE GROUT JOINTS WILL NOT ALIGN WITH (WT-1) WALL TILE GROUT JOINTS

(AT-1) ACCENT WALL TILE GROUT JOINTS WILL NOT ALIGN WITH (WT-1) WALL TILE GROUT JOINTS


WOMEN'S
POWDER ROOM

901

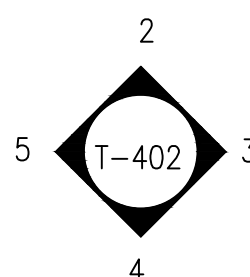








WOMEN'S
RESTROOM

902

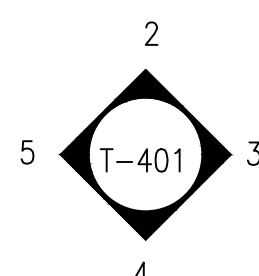



MEN'S
RESTROOM

903

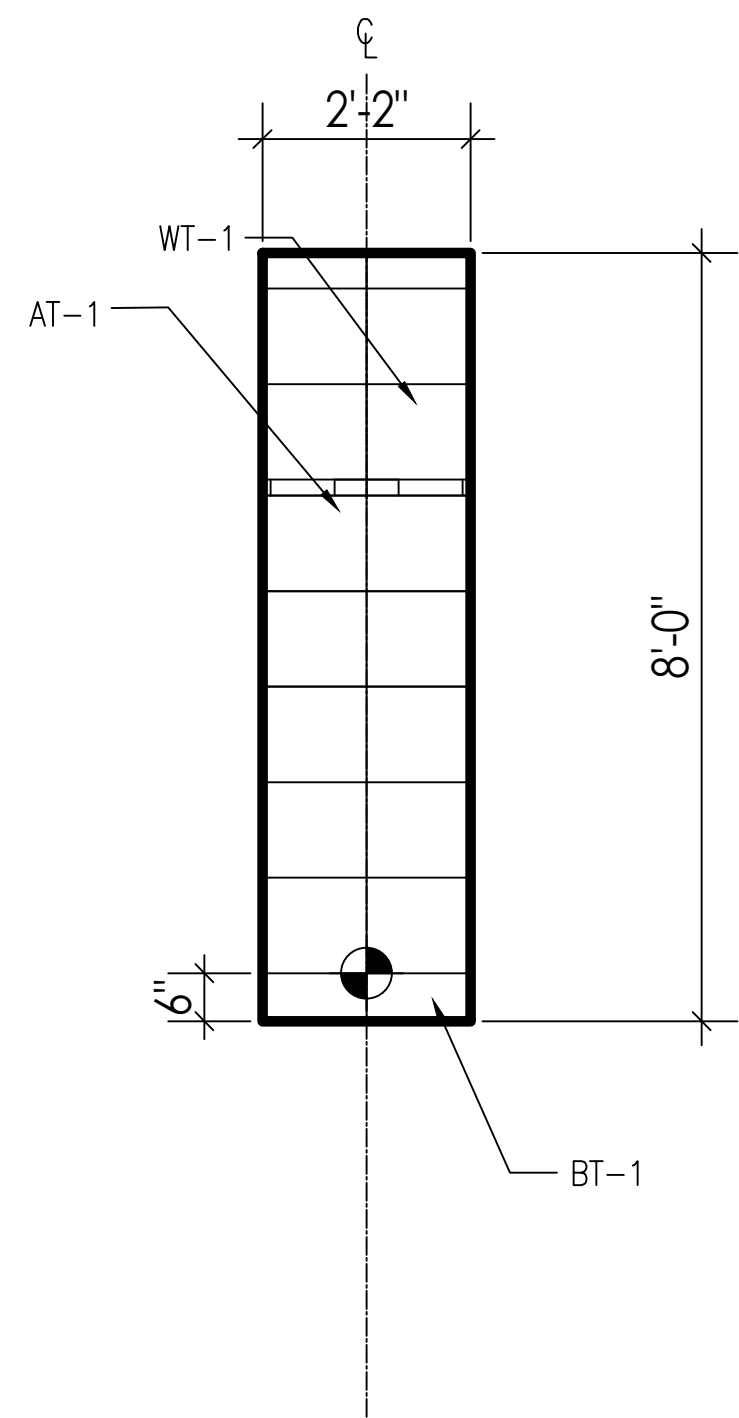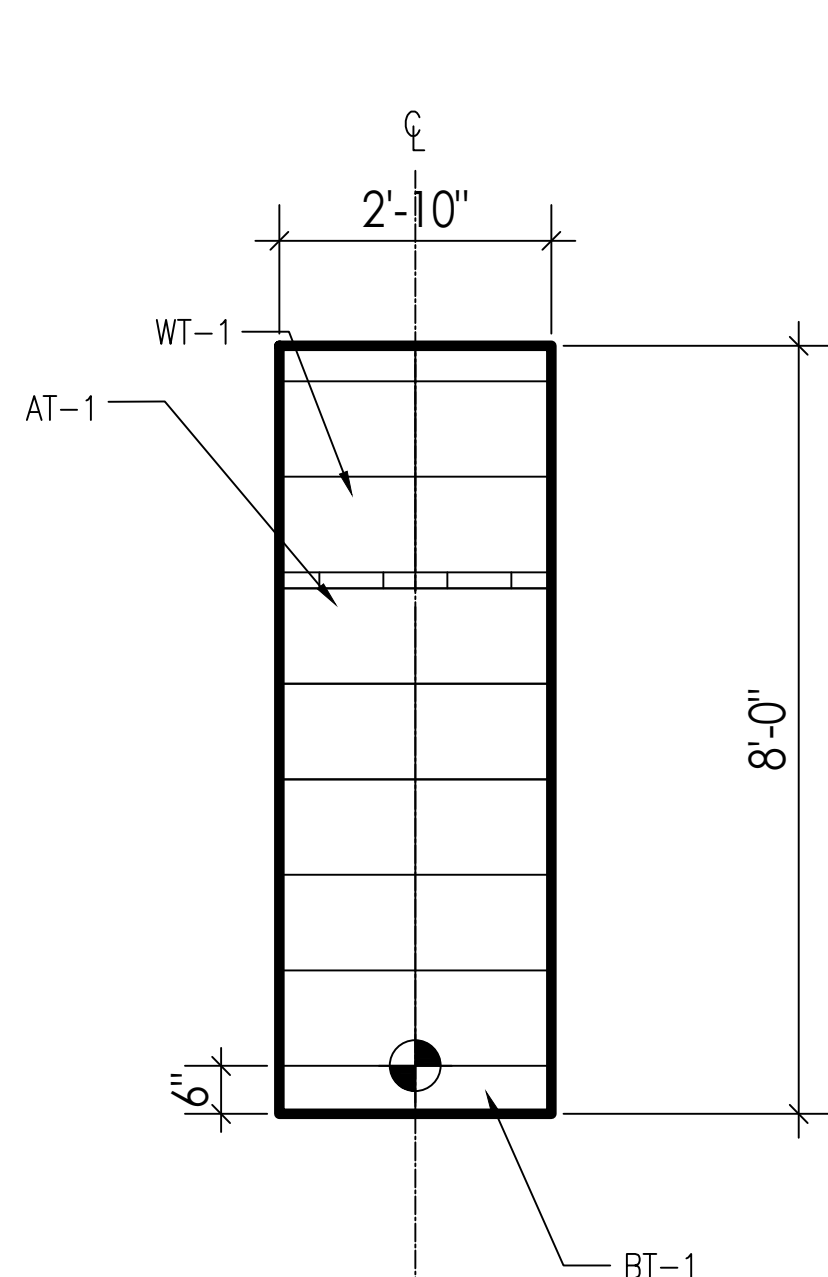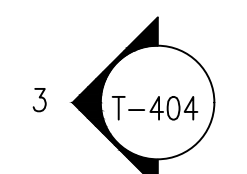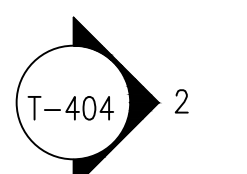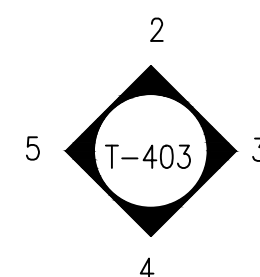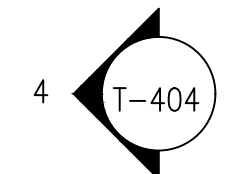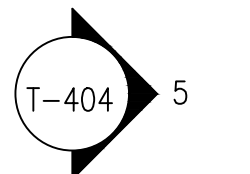

02
1/2"=1'-0" ELEVATIONS: 9TH FLOOR BATHROOMS

03
1/2"=1'-0" ELEVATIONS: 9TH FLOOR BATHROOMS

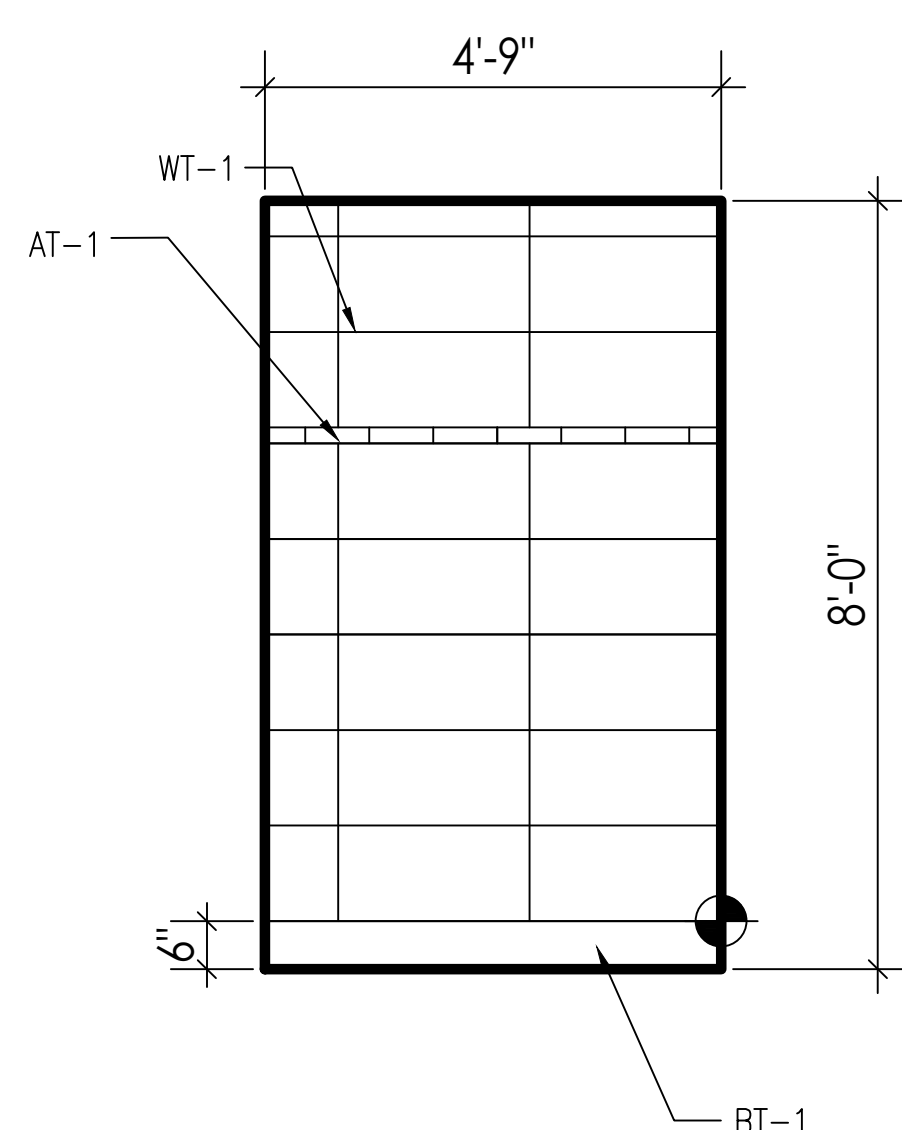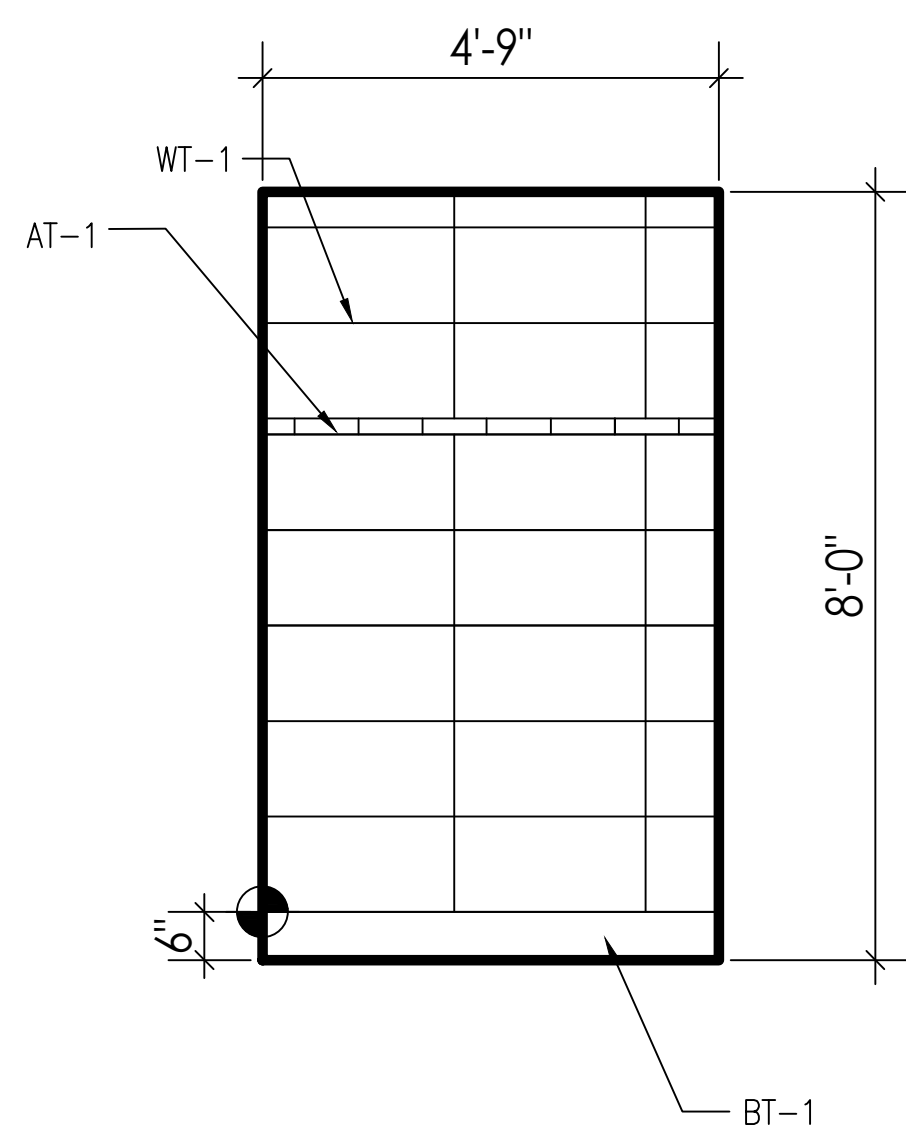

04
1/2"=1'-0" ELEVATIONS: 9TH FLOOR BATHROOMS

05
1/2"=1'-0" ELEVATIONS: 9TH FLOOR BATHROOMS

01
1/2"=1'-0" PLAN #2: 9TH FLOOR BATHROOMS

AUSTRO TILE & STONE, LLC
30-25 93RD STREET
EAST ELMHURST, NY 11369

CONTRACTOR:
JRM CONSTRUCTION
MANAGEMENT, LLC
242 WEST 36TH STREET
11TH FLOOR
NEW YORK, NY 10018

INTERIOR DESIGNER:


ISSUE FOR APPROVAL 10/09/23
ISSUE NAME DATE

ARCHITECT:
SPACESMITH
ONE NEW YORK PLAZA
NEW YORK, NY 10004
PH:212 260 5583


PROJECT NAME:
JACK RESNICK & SONS
255 GREENWICH STREET
NEW YORK, NY 10007

SHEET NAME:
ELEVATIONS
9TH FLOOR BATHROOMS


DATE:
PROJECT NO.:
PRINCIPAL:
DRAWING BY:
CHECKED BY:
SCALE:
DWG. No.:
T-404
22 of 29

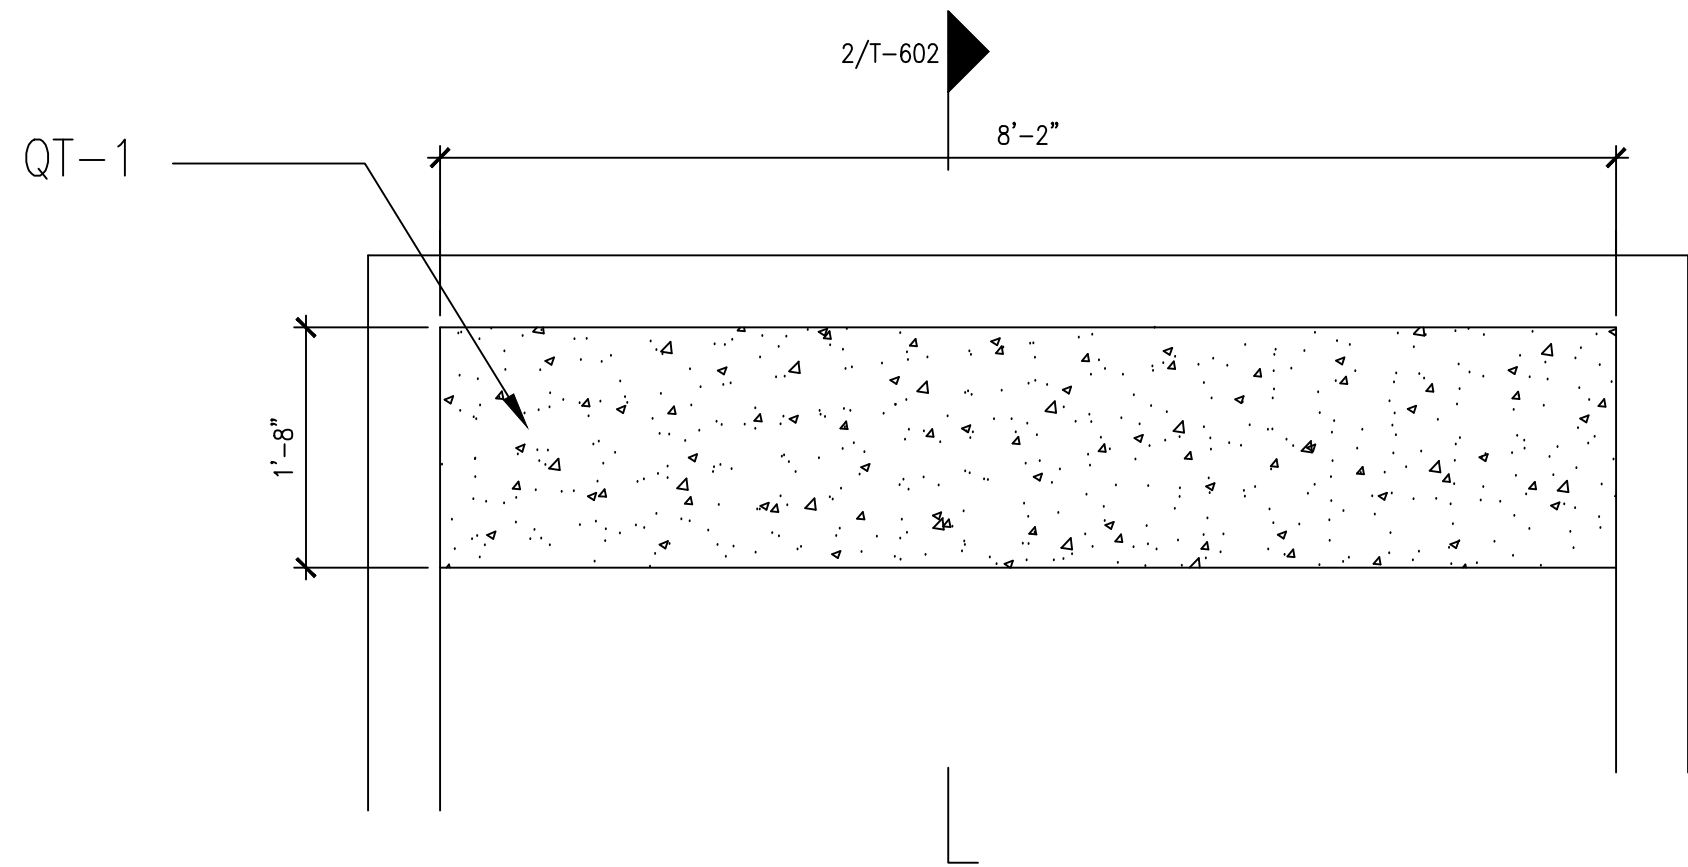


01 3/4"x1'-0" STONE COUNTERTOPS -6TH FLOOR WOMEN'S POWDER ROOM

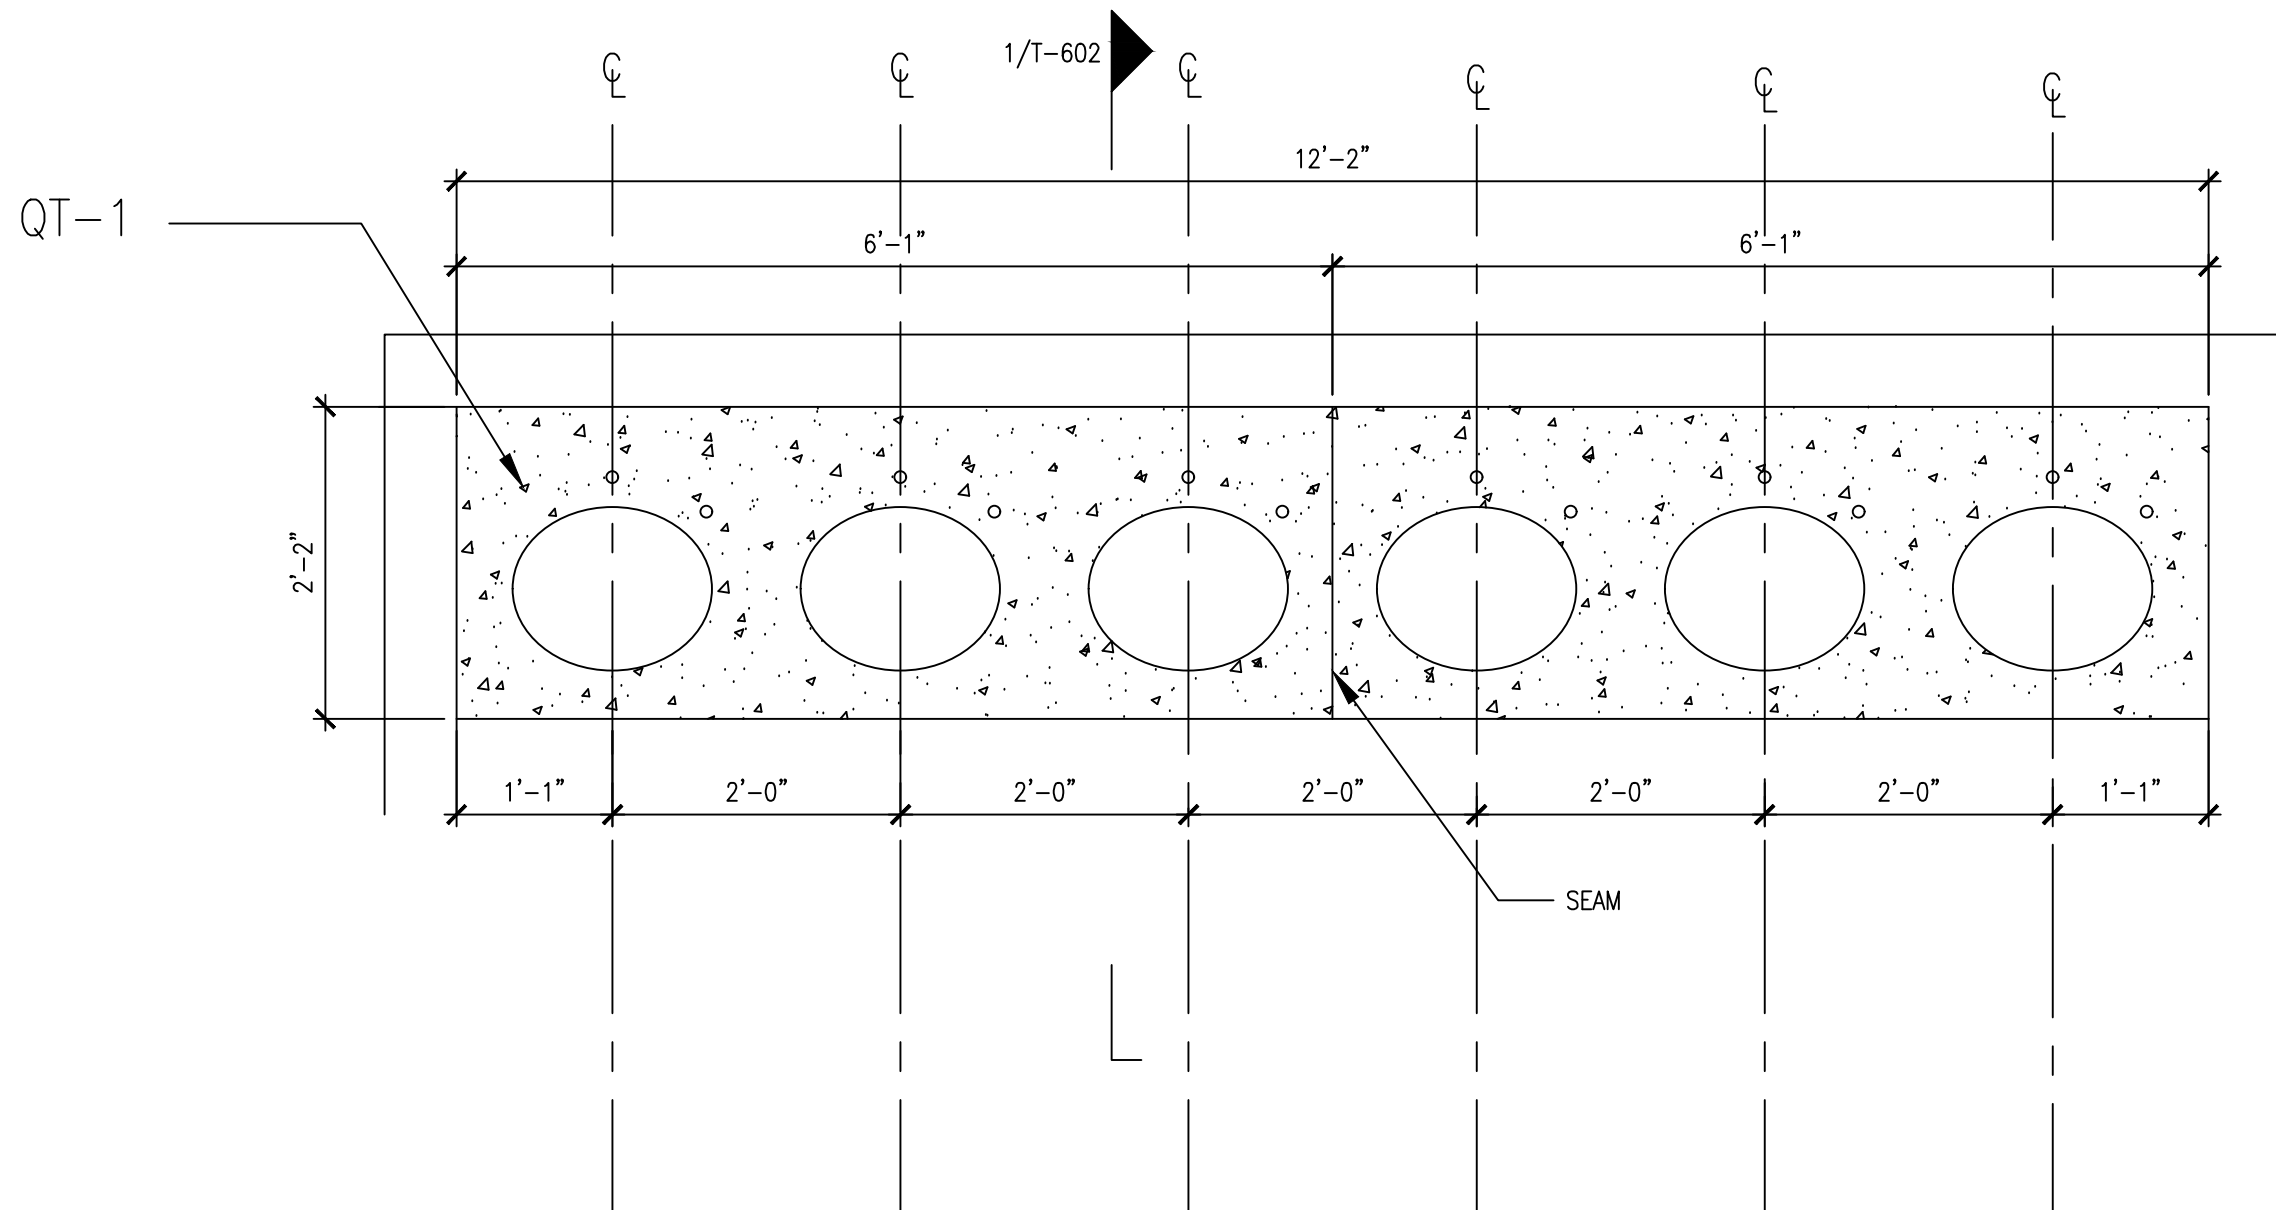


02 3/4"x1'-0" STONE COUNTERTOPS -6TH FLOOR WOMEN'S RESTROOM

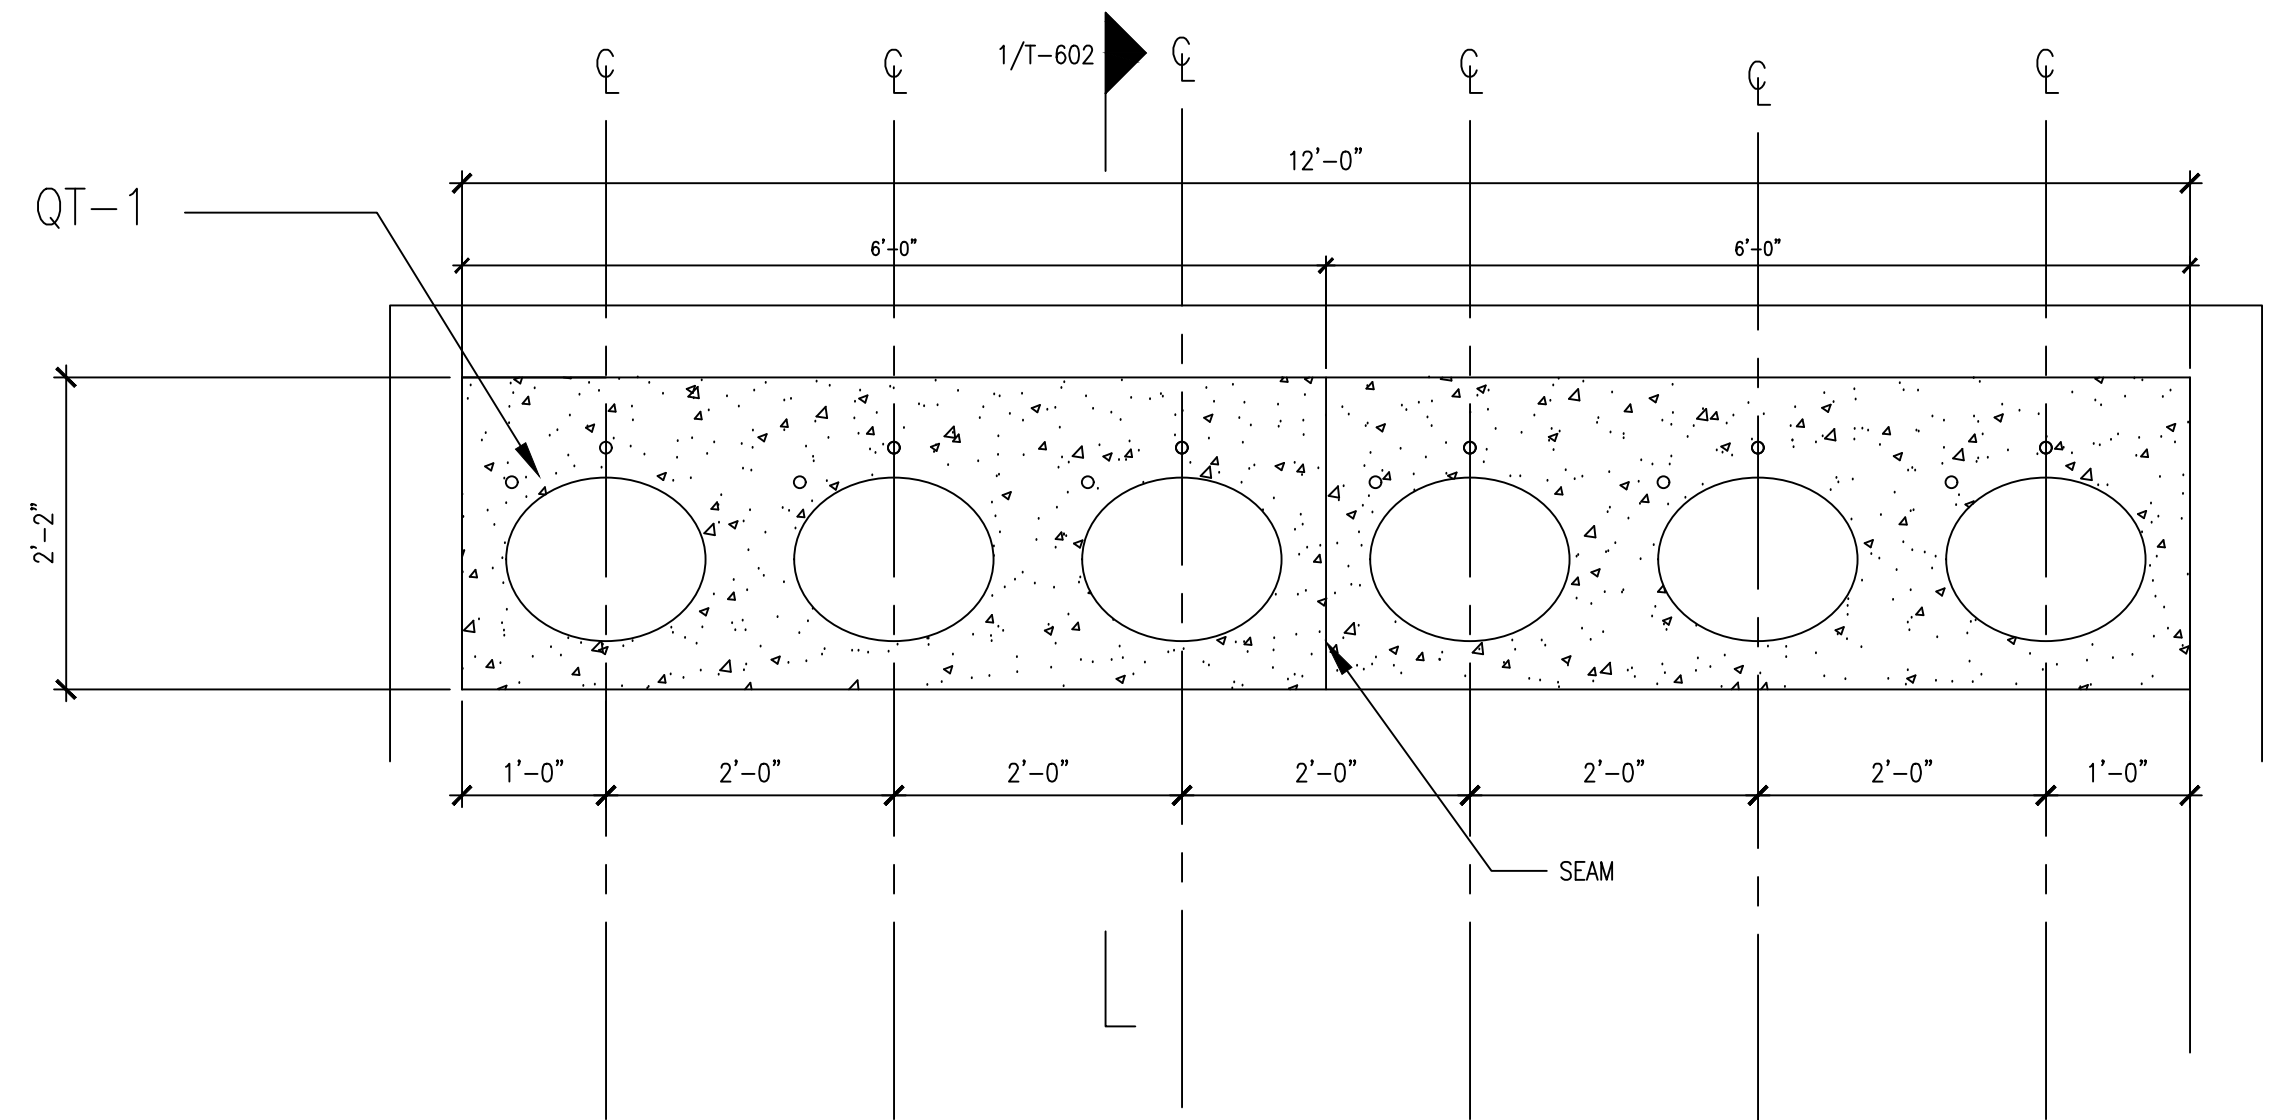

03 3/4"x1'-0" STONE COUNTERTOPS -6TH FLOOR MEN'S RESTROOM

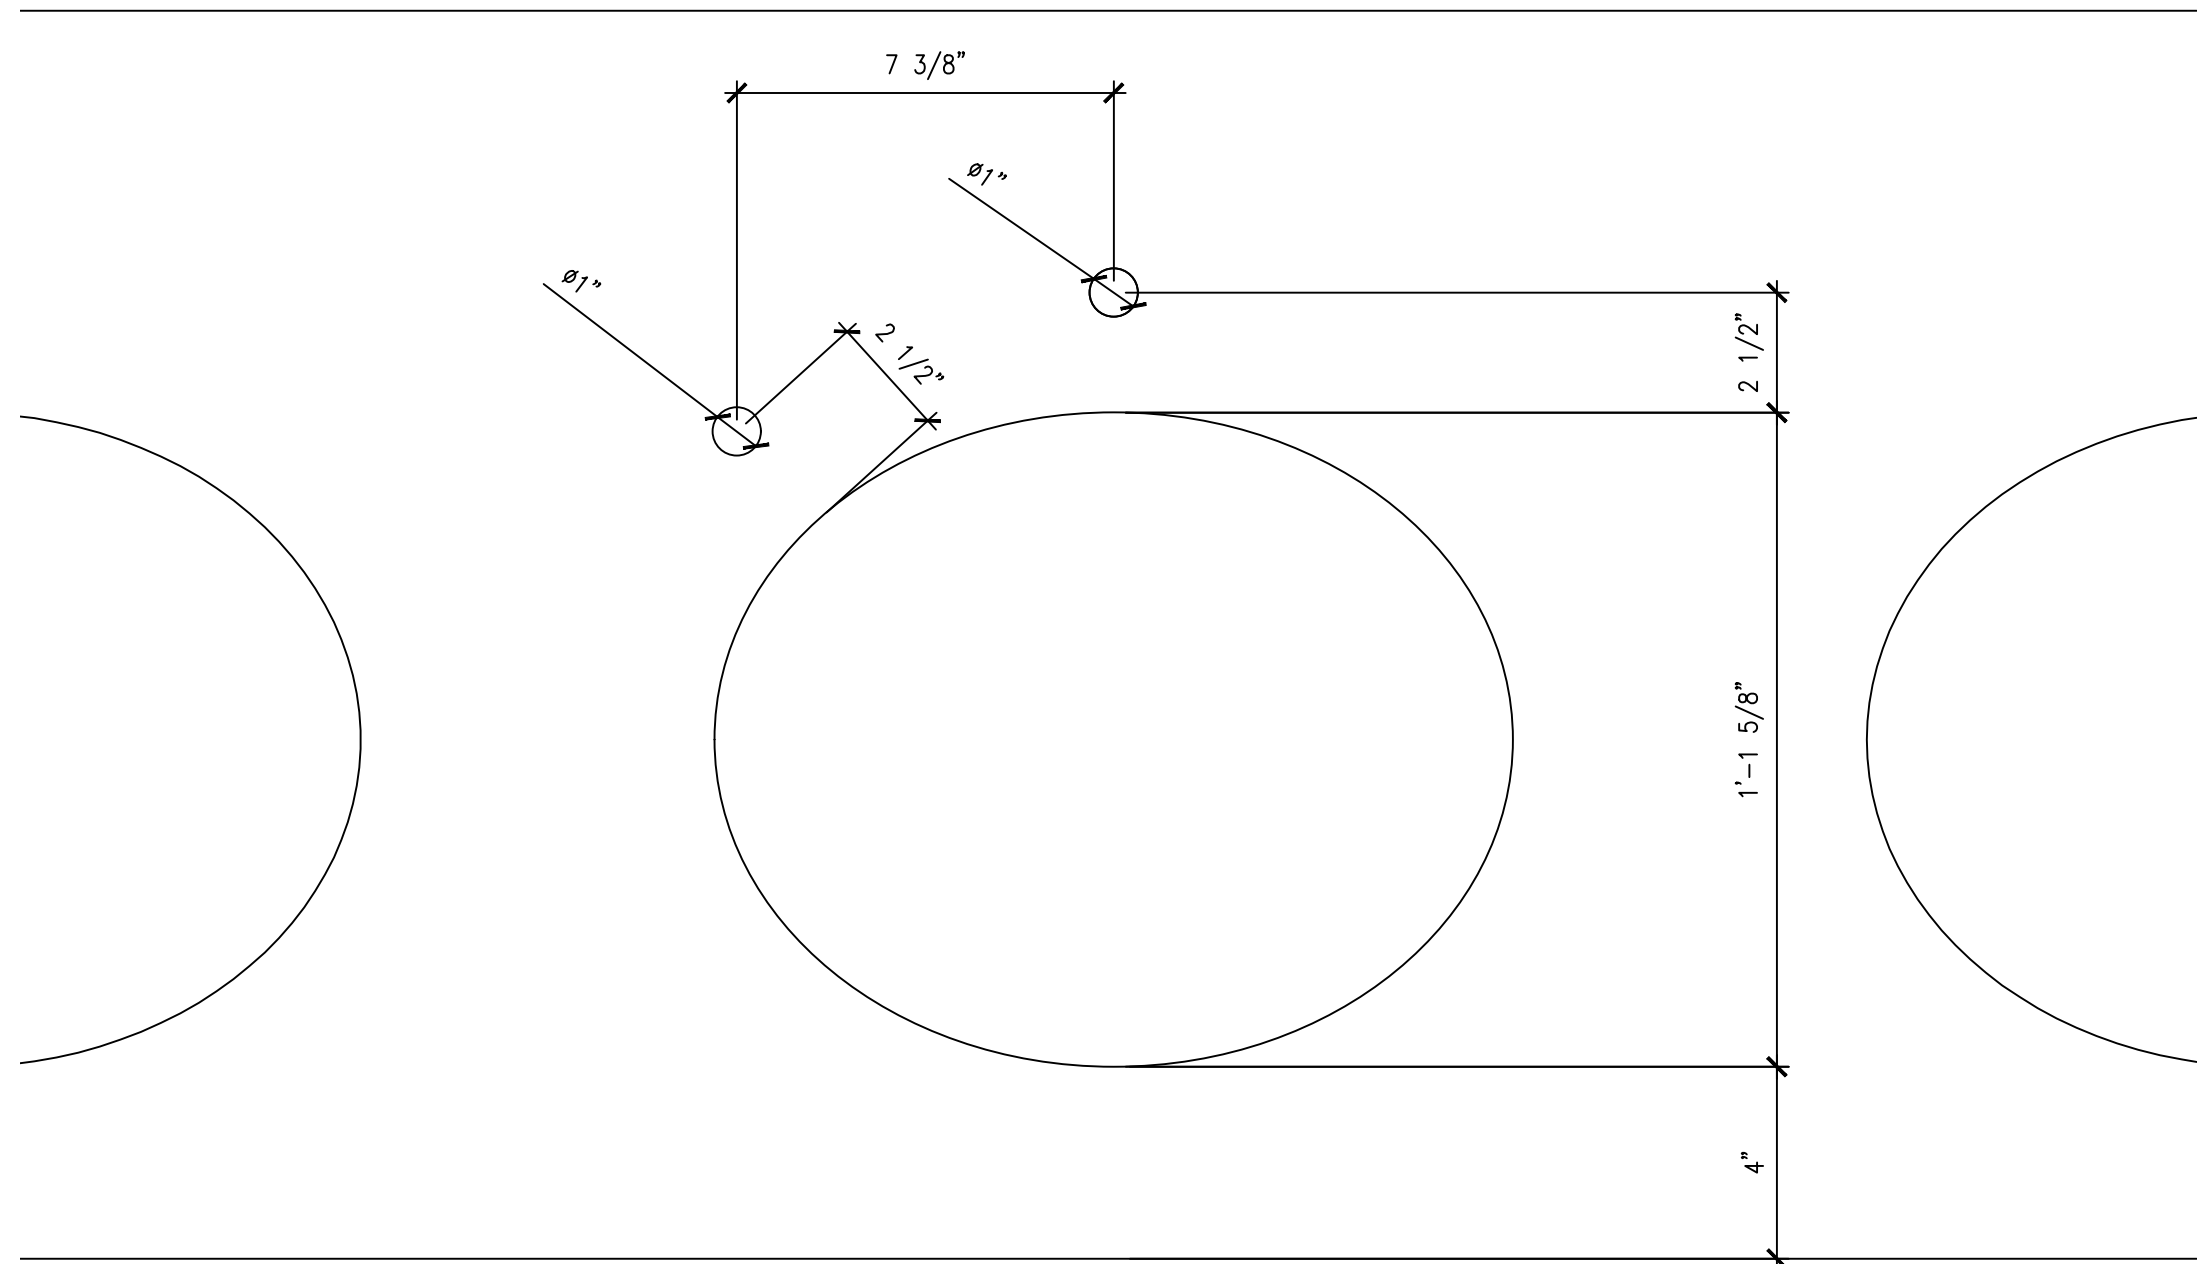

05 3/4"x1'-0" STONE COUNTERTOPS -6TH FLOOR MEN'S DETAIL VIEW

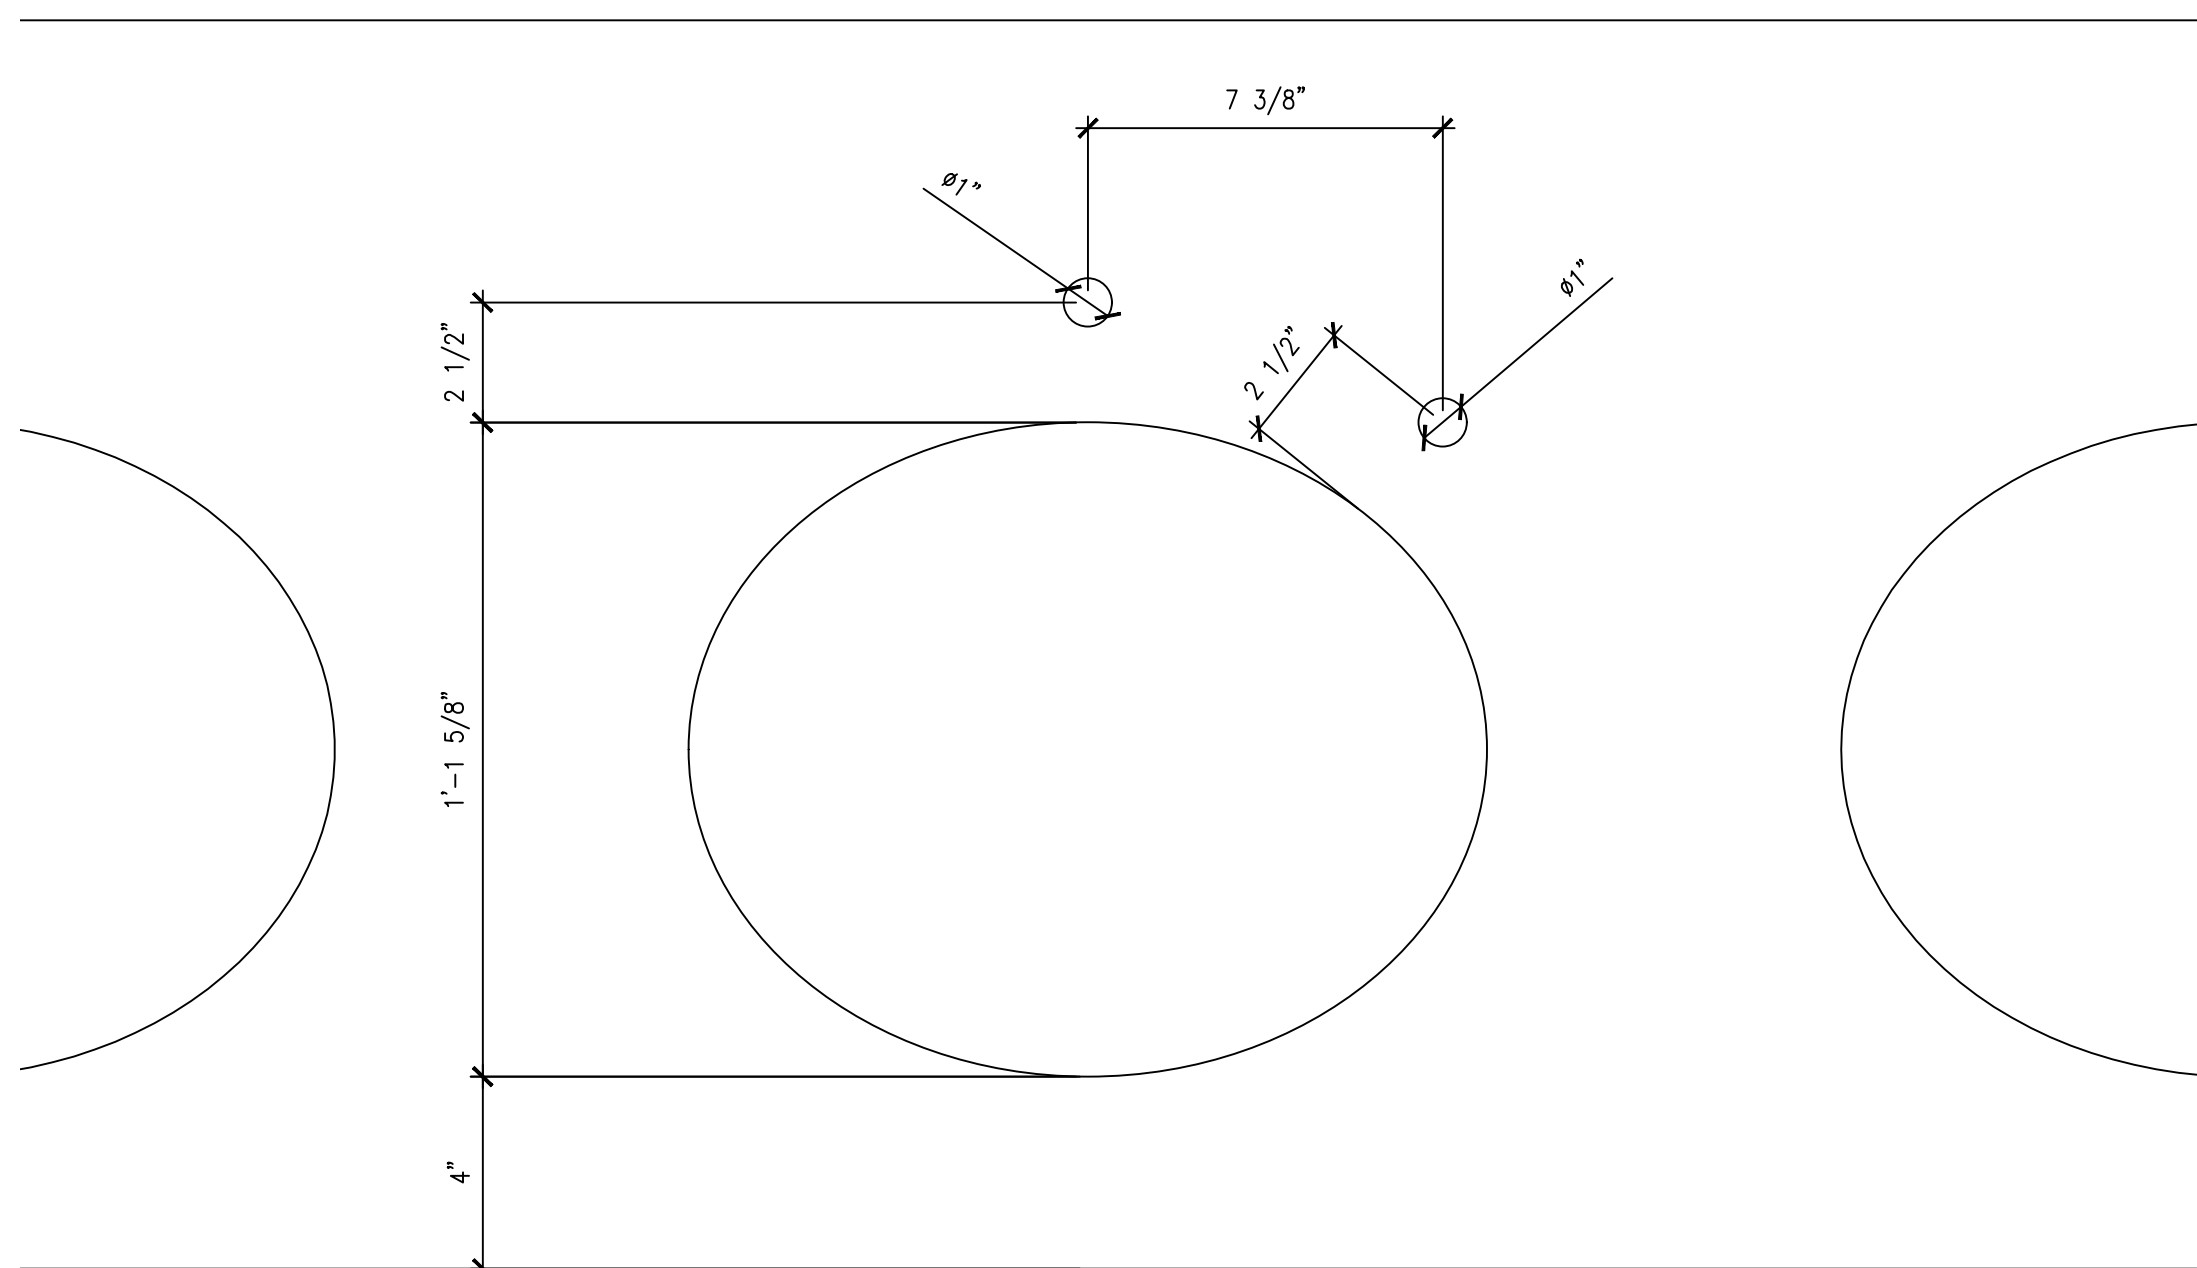

04 3/4"x1'-0" STONE COUNTERTOPS -6TH FLOOR WOMEN'S DETAIL VIEW

AUSTRO TILE & STONE, LLC
30-25 93RD STREET
EAST ELMHURST, NY 11369

CONTRACTOR: JRM CONSTRUCTION
MANAGEMENT, LLC
242 WEST 36TH STREET
11TH FLOOR
NEW YORK, NY 10018

INTERIOR DESIGNER:


ISSUE FOR APPROVAL 10/09/23
ISSUE NAME DATE

ARCHITECT: SPACESMITH
ONE NEW YORK PLAZA SUITE 4200
NEW YORK, NY 1004
PH: 212 260 5583


PROJECT NAME: JACK RESNICK & SONS
255 GREENWICH STREET
NEW YORK, NY 10007

SHEET NAME: STONE COUNTERTOPS
6TH FLOOR


DATE: _____
PROJECT NO.: _____
PRINCIPAL: _____
DRAWING BY: _____
CHECKED BY: _____
SCALE: _____
DWG No.: T-500
23 of 29

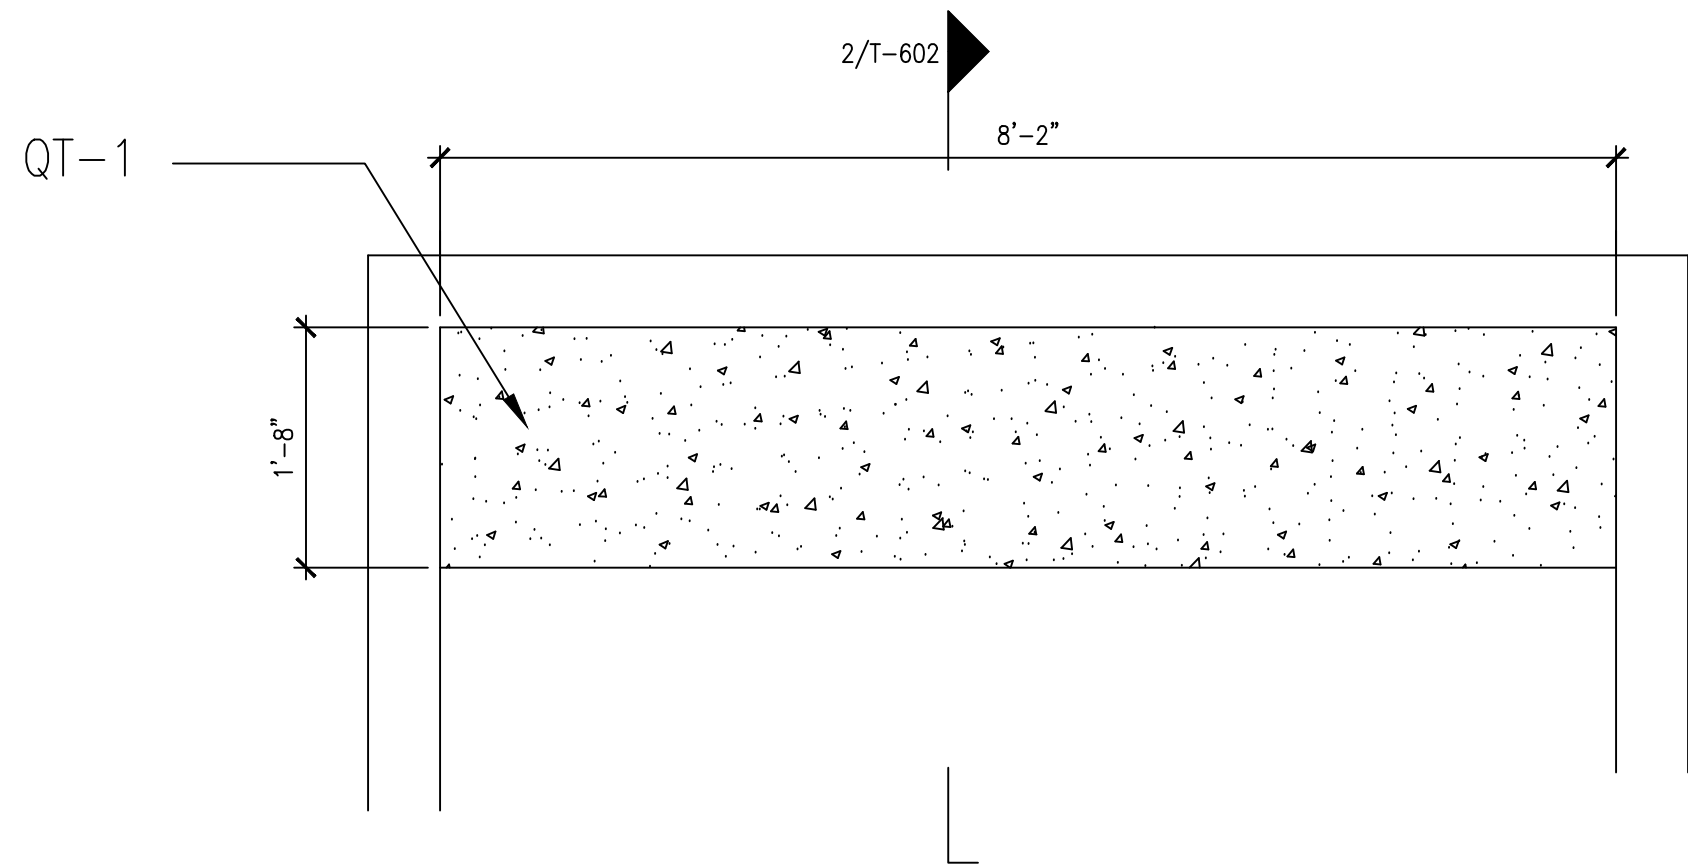


01 3/4"x1'-0" STONE COUNTERTOPS -7TH FLOOR WOMEN'S POWDER ROOM

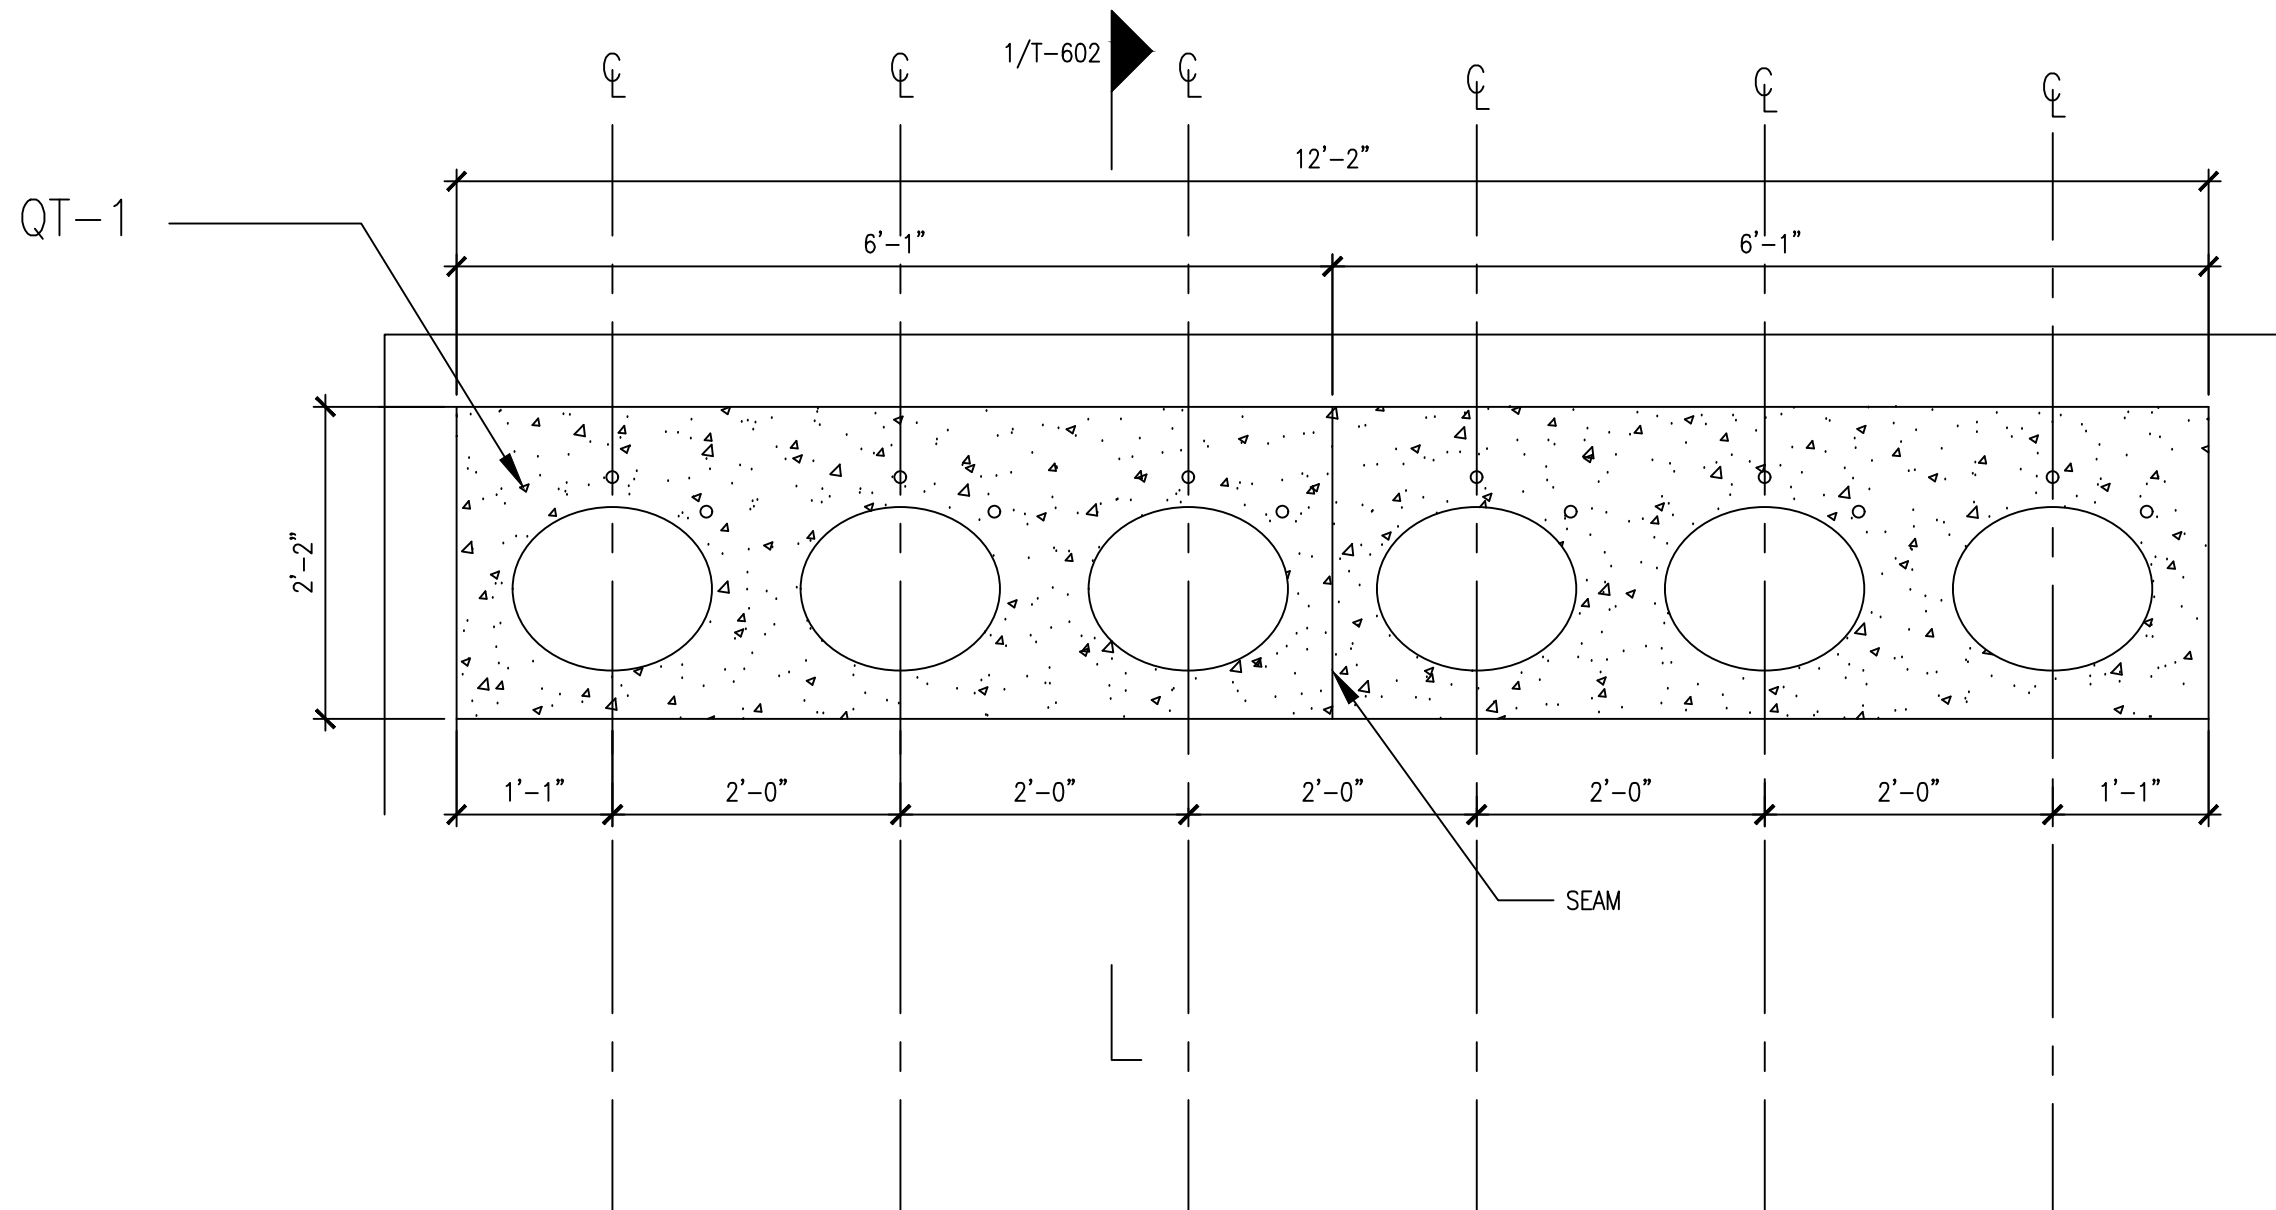


02 3/4"x1'-0" STONE COUNTERTOPS -7TH FLOOR WOMEN'S RESTROOM

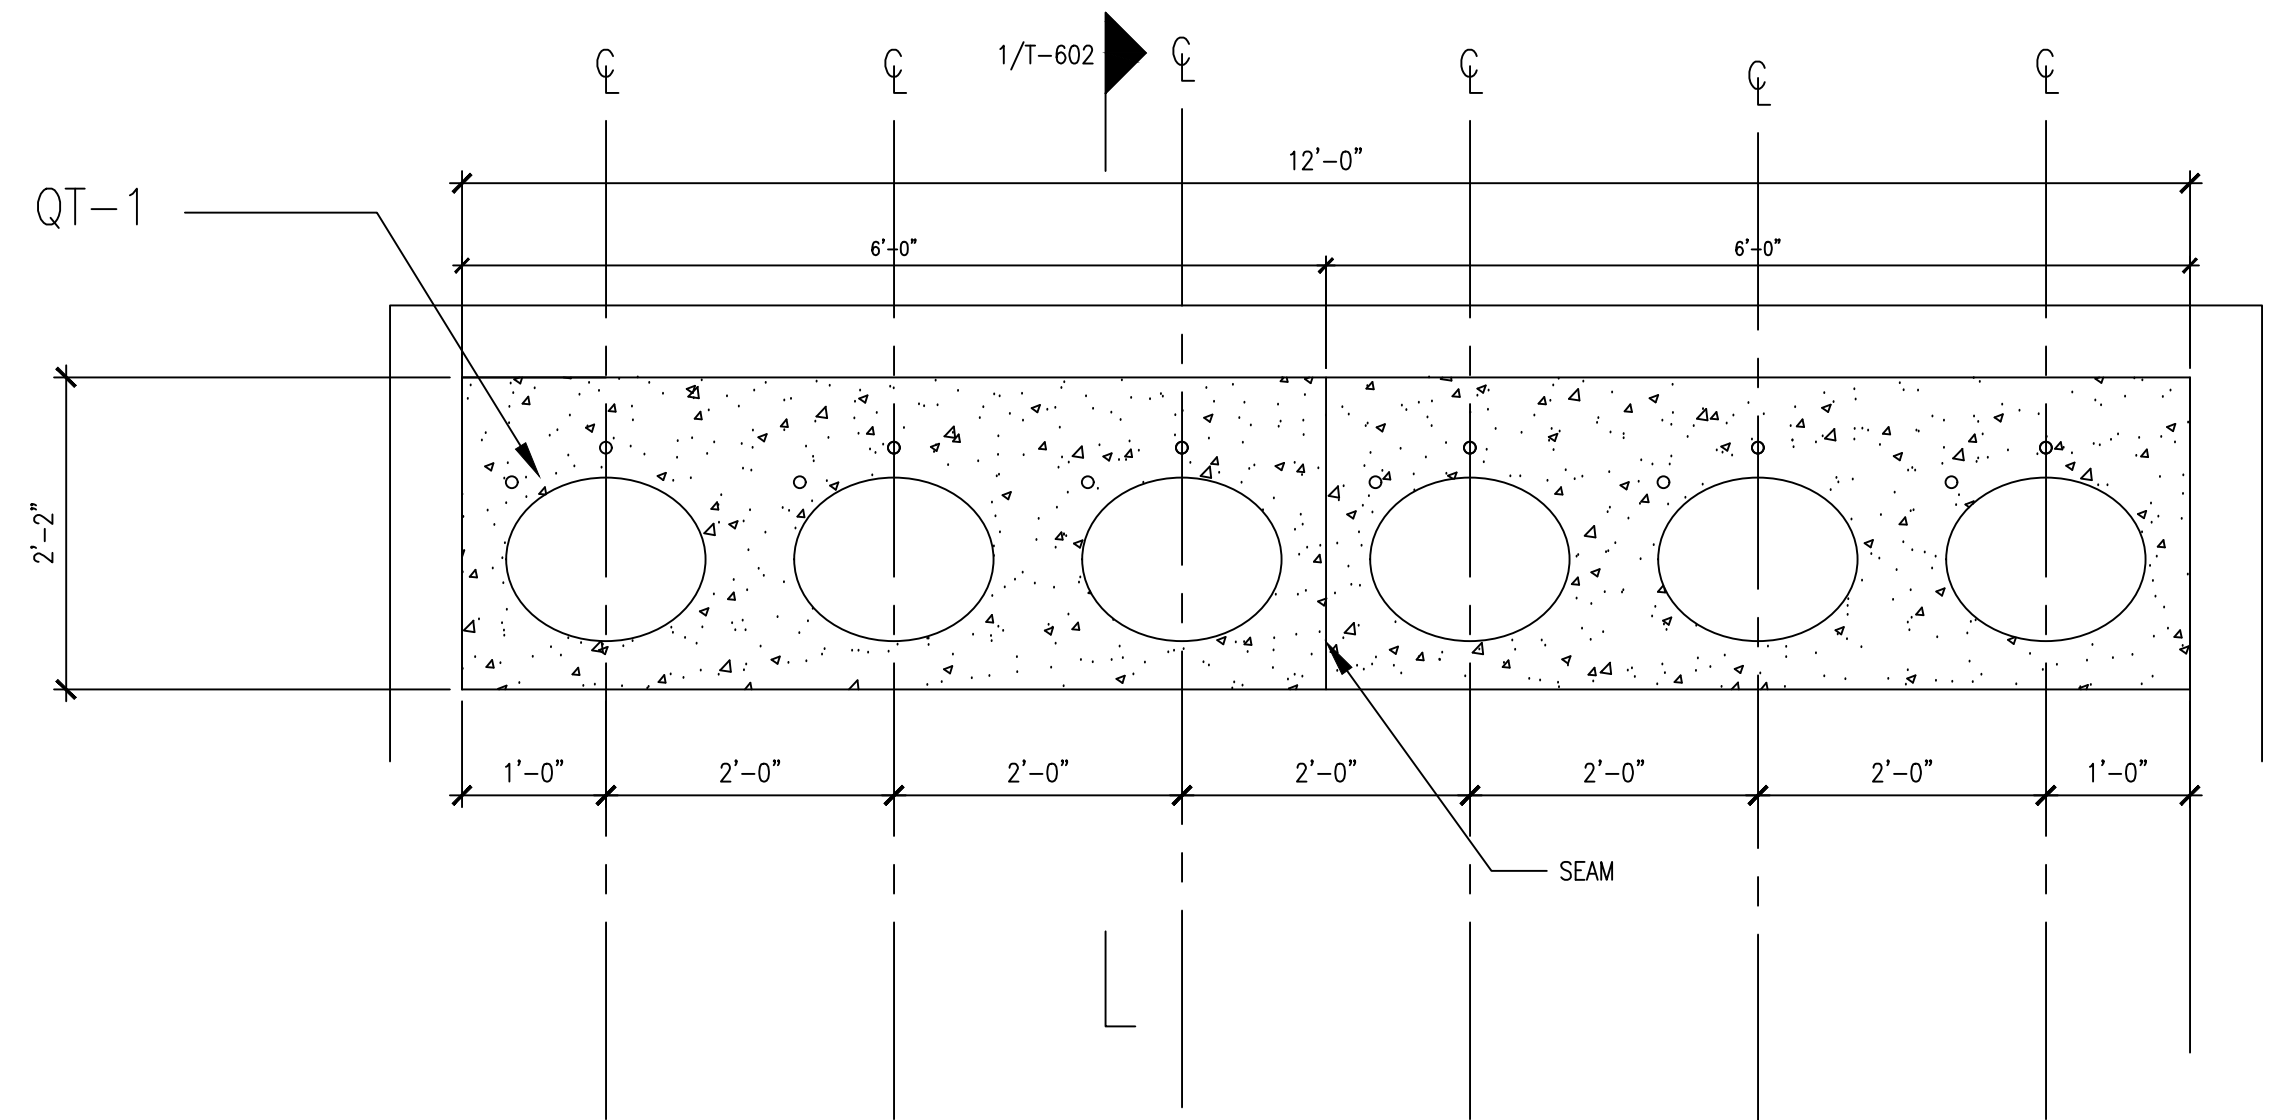

03 3/4"x1'-0" STONE COUNTERTOPS -7TH FLOOR MEN'S RESTROOM

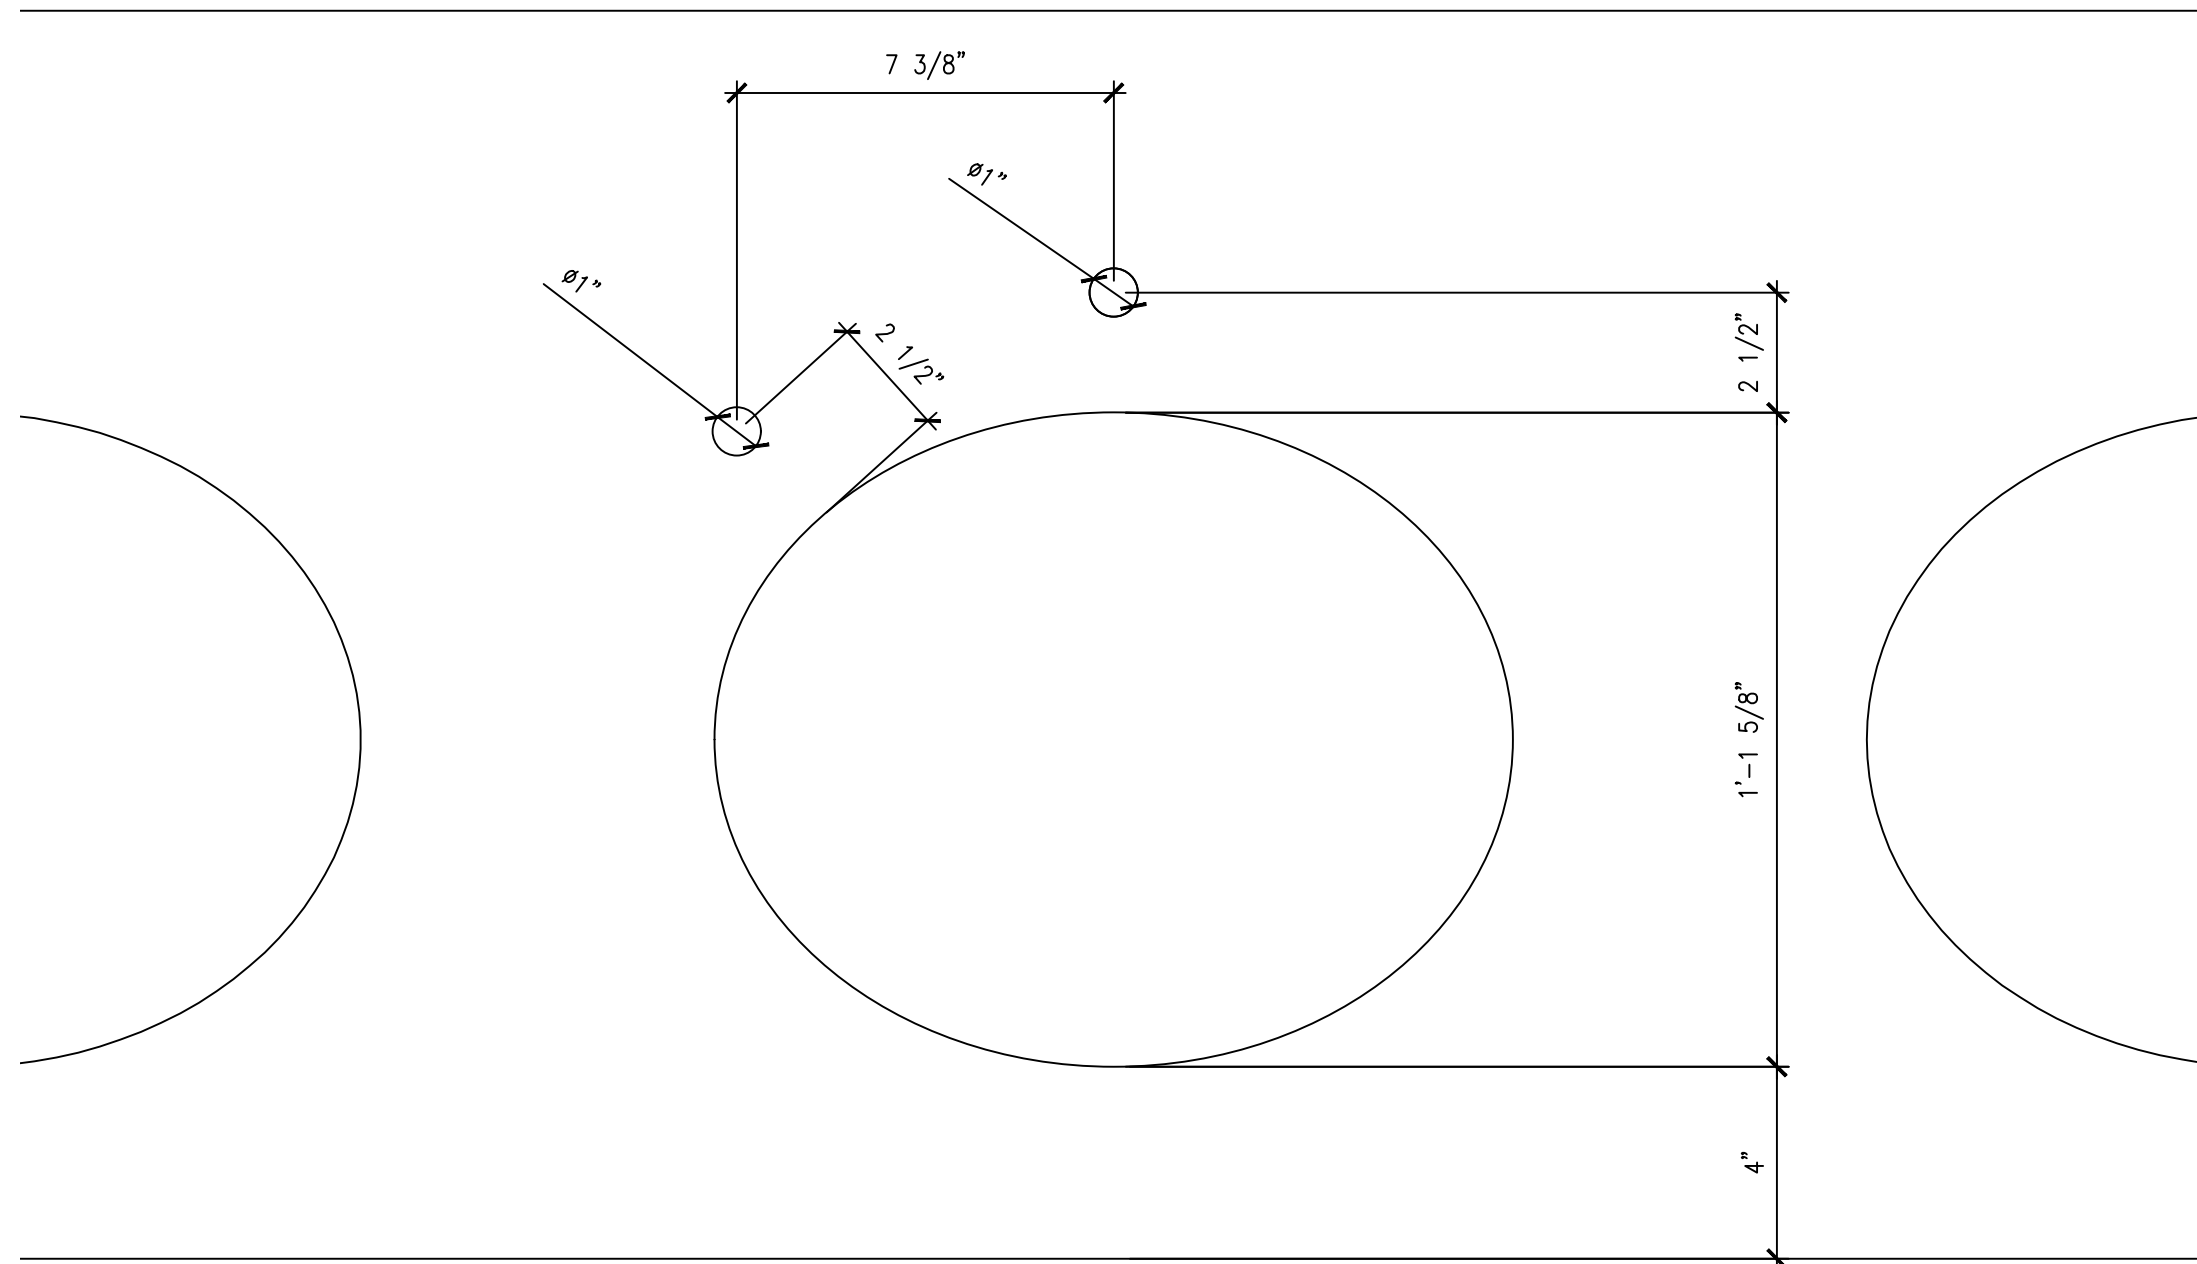

05 3/4"x1'-0" STONE COUNTERTOPS -7TH FLOOR MEN'S DETAIL VIEW

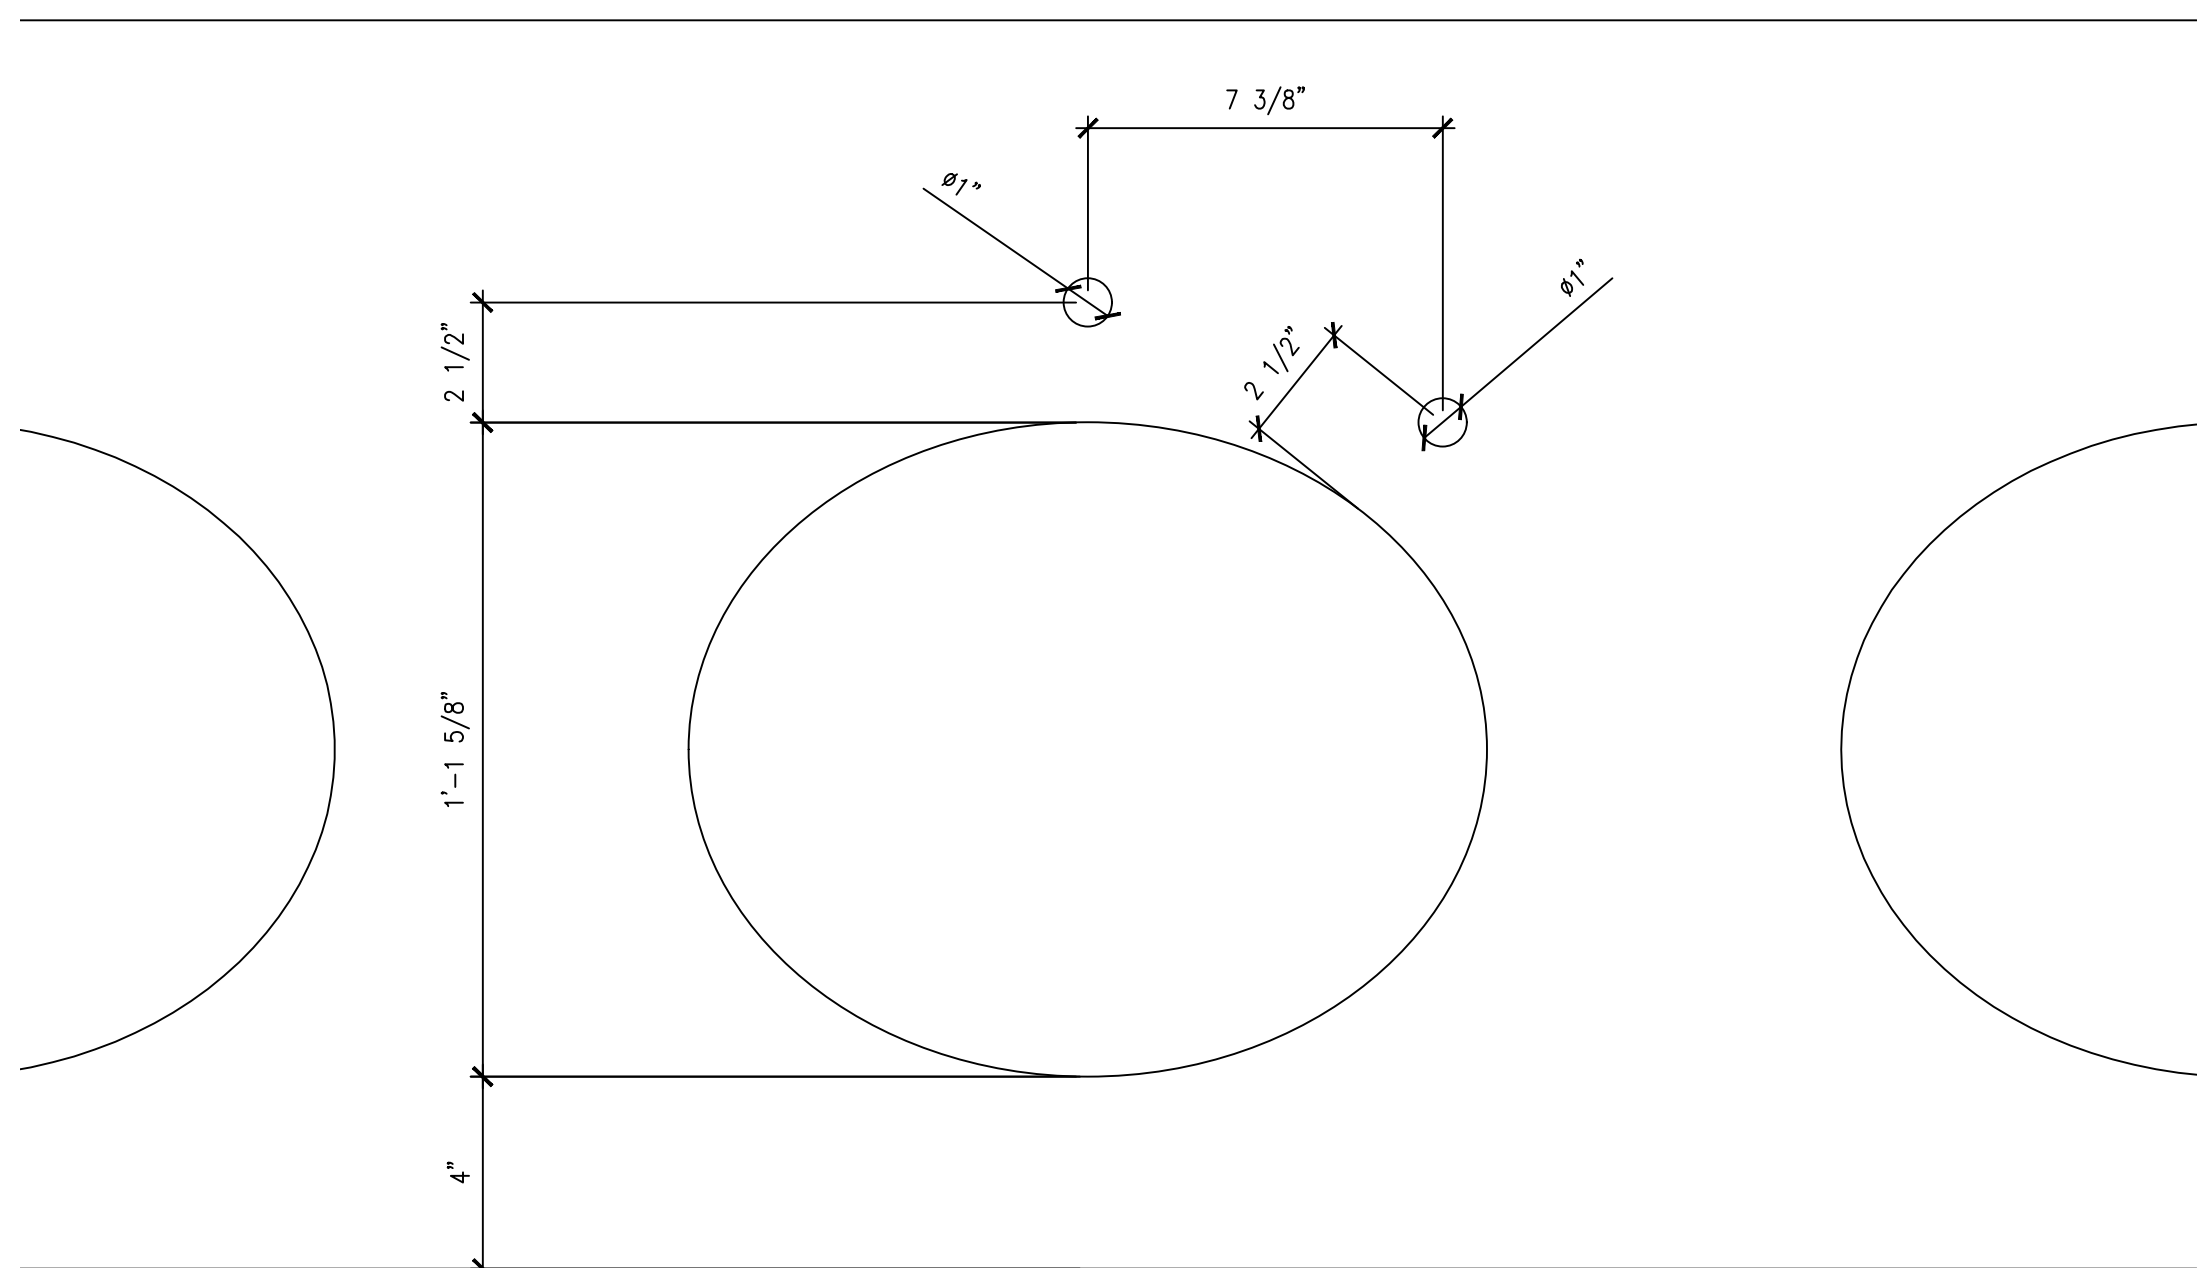

04 3/4"x1'-0" STONE COUNTERTOPS -7TH FLOOR WOMEN'S DETAIL VIEW

AUSTRO TILE & STONE, LLC
30-25 93RD STREET
EAST ELMHURST, NY 11369

CONTRACTOR: JRM CONSTRUCTION
MANAGEMENT, LLC
242 WEST 36TH STREET
11TH FLOOR
NEW YORK, NY 10018

INTERIOR DESIGNER:


ISSUE FOR APPROVAL 10/09/23
ISSUE NAME DATE

ARCHITECT: SPACESMITH
ONE NEW YORK PLAZA SUITE 4200
NEW YORK, NY 1004
PH: 212 260 5583


PROJECT NAME: JACK RESNICK & SONS
255 GREENWICH STREET
NEW YORK, NY 10007

SHEET NAME: STONE COUNTERTOPS
7TH FLOOR


DATE:
PROJECT NO.:
PRINCIPAL:
DRAWING BY:
CHECKED BY:
SCALE:
DWG No.:
T-501
24 of 29

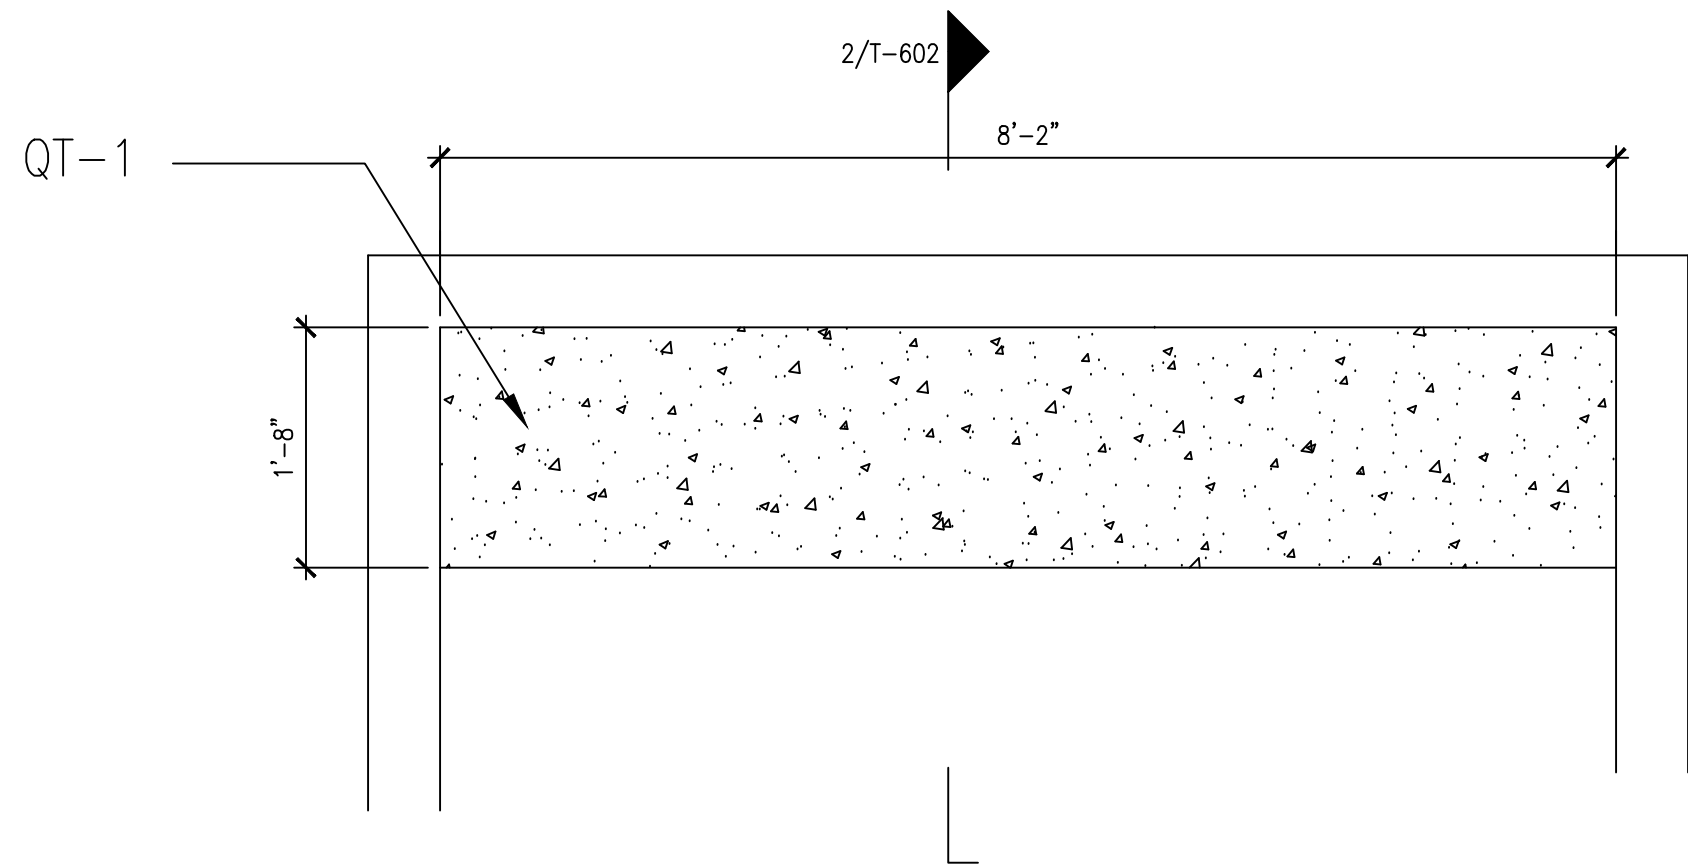


01 3/4"x1'-0" STONE COUNTERTOPS --8TH FLOOR WOMEN'S POWDER ROOM

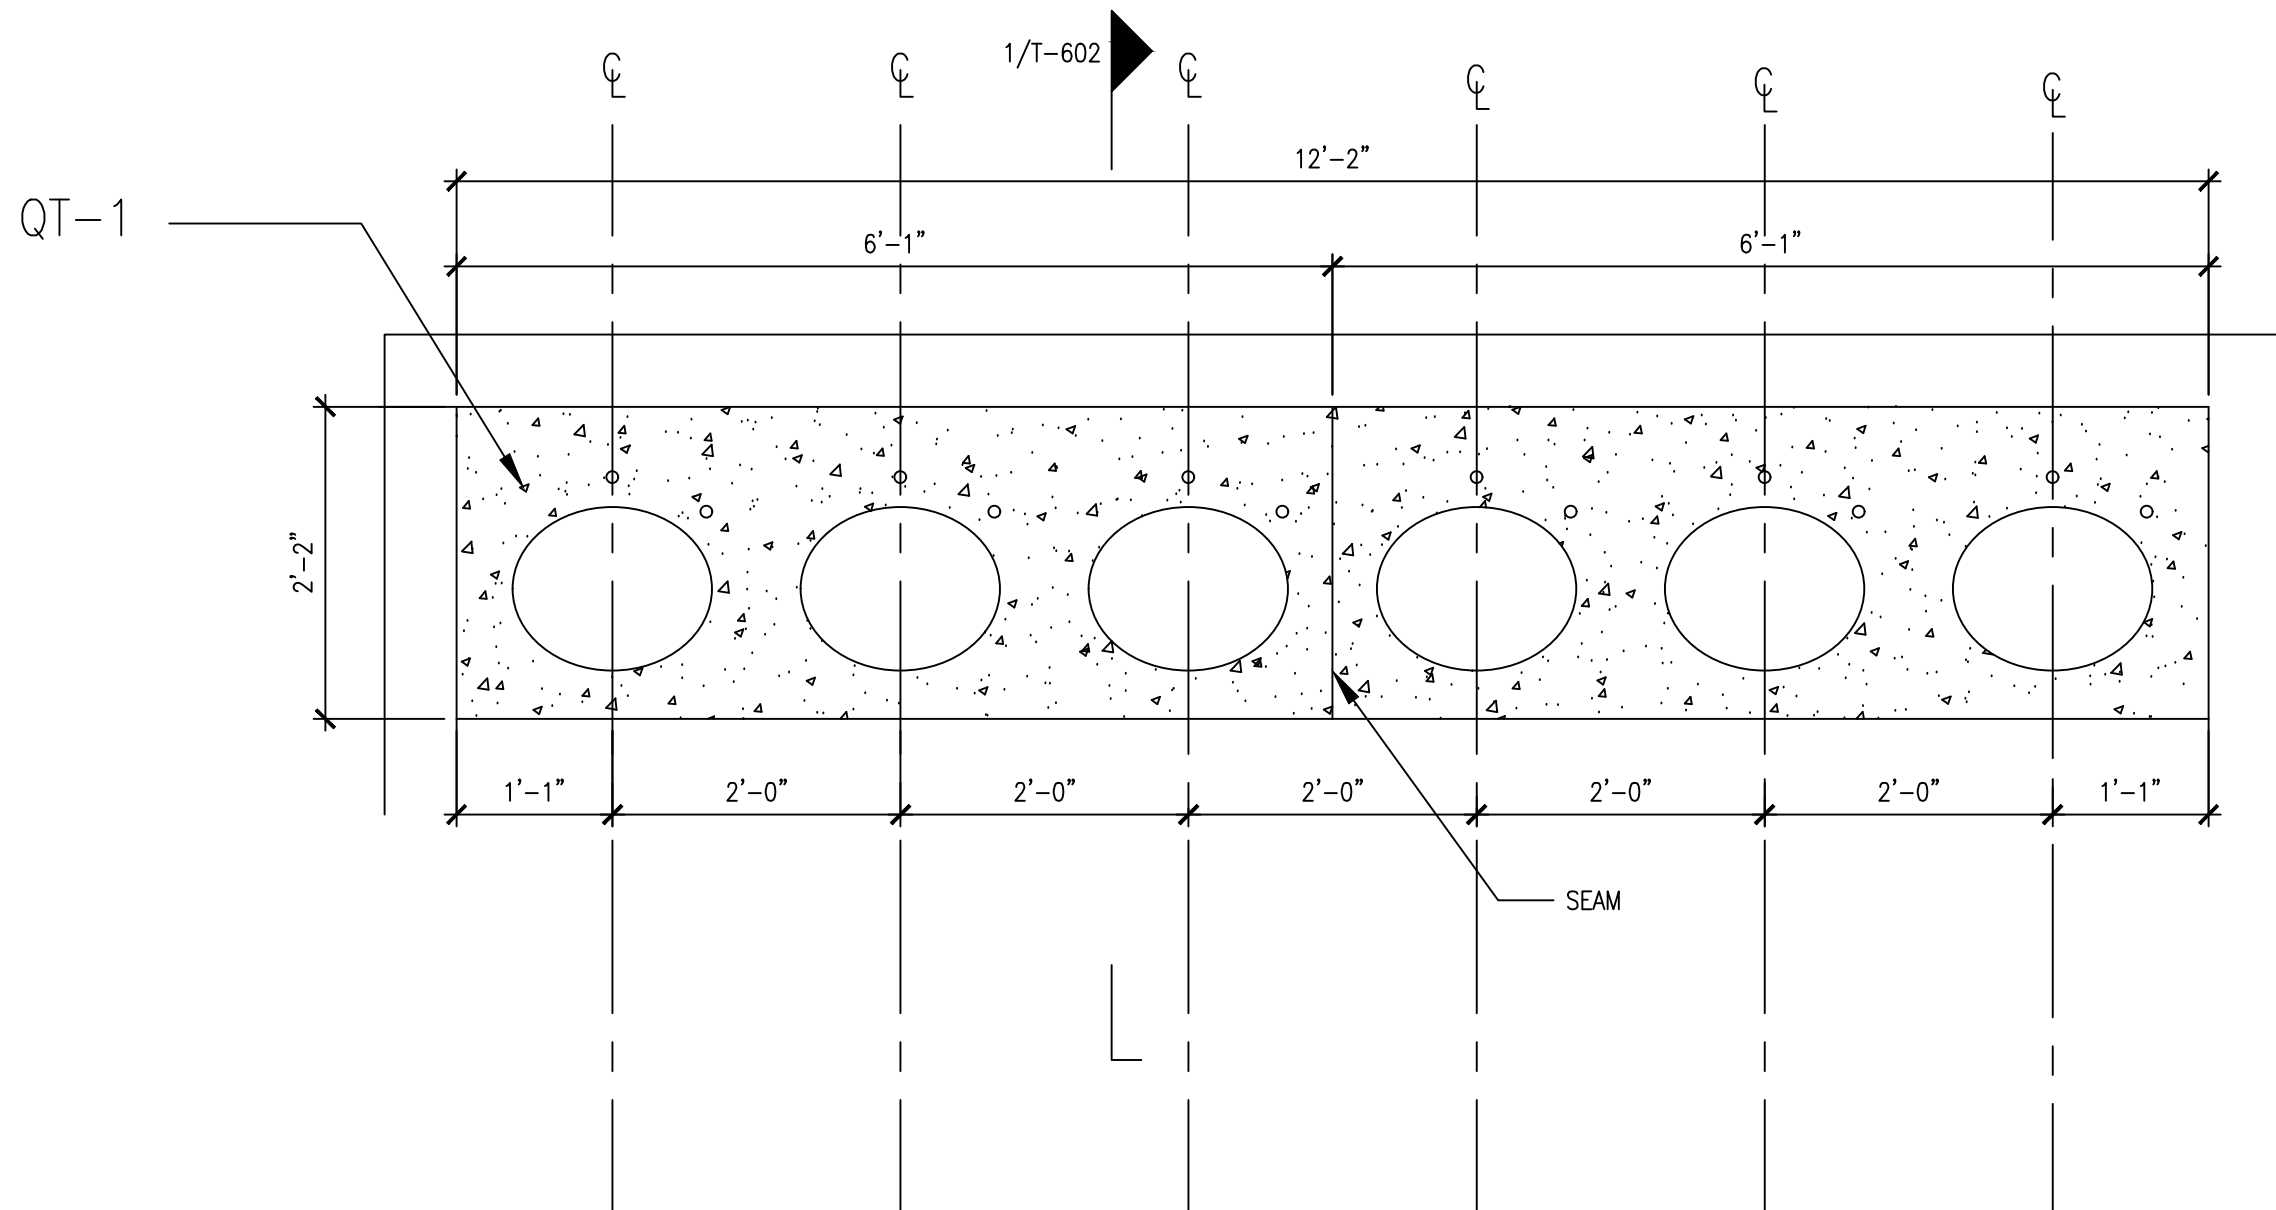


02 3/4"x1'-0" STONE COUNTERTOPS --8TH FLOOR WOMEN'S RESTROOM

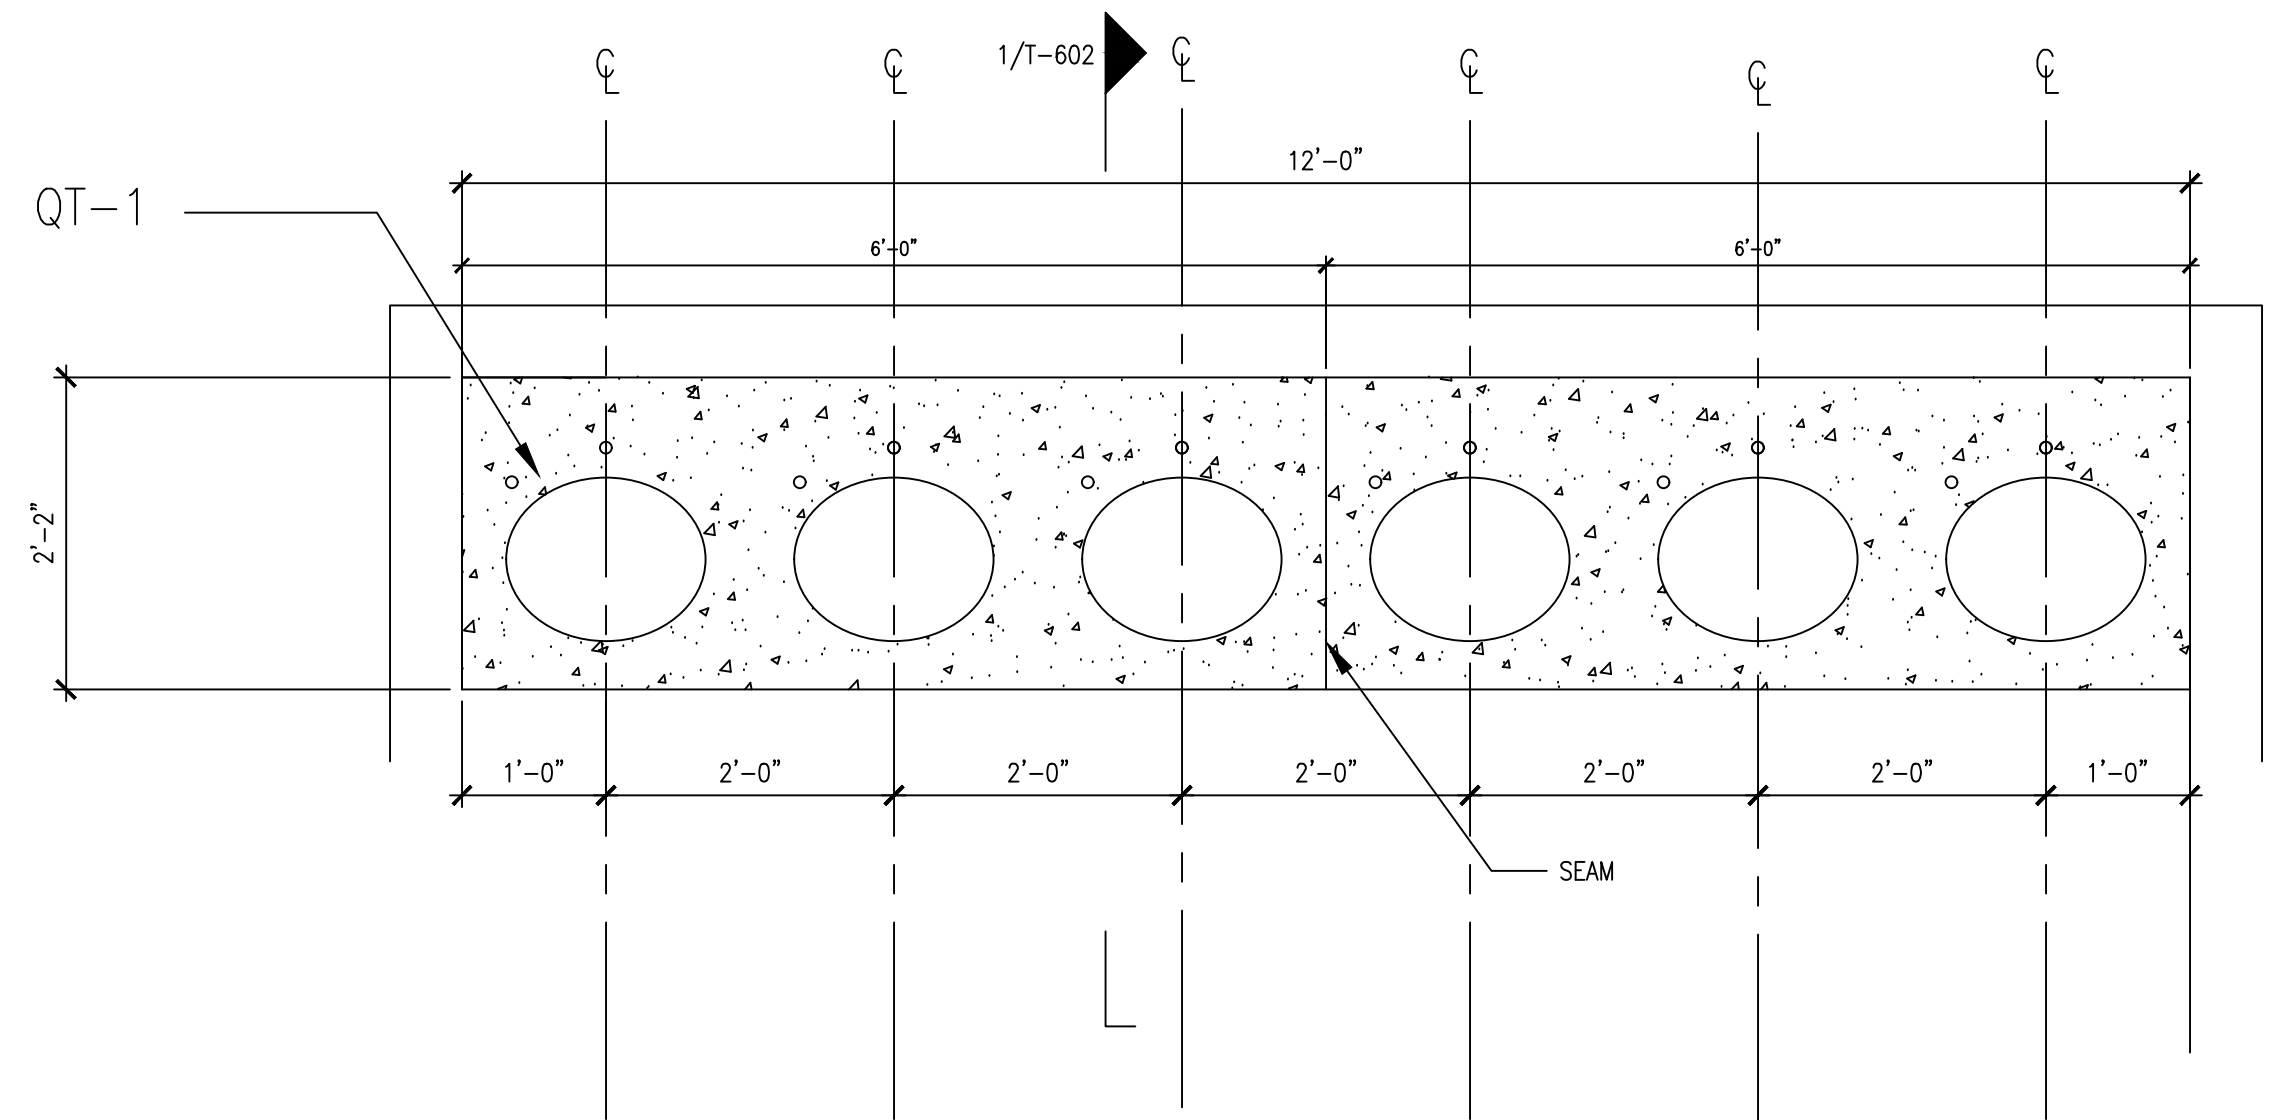

03 3/4"x1'-0" STONE COUNTERTOPS --8TH FLOOR MEN'S RESTROOM

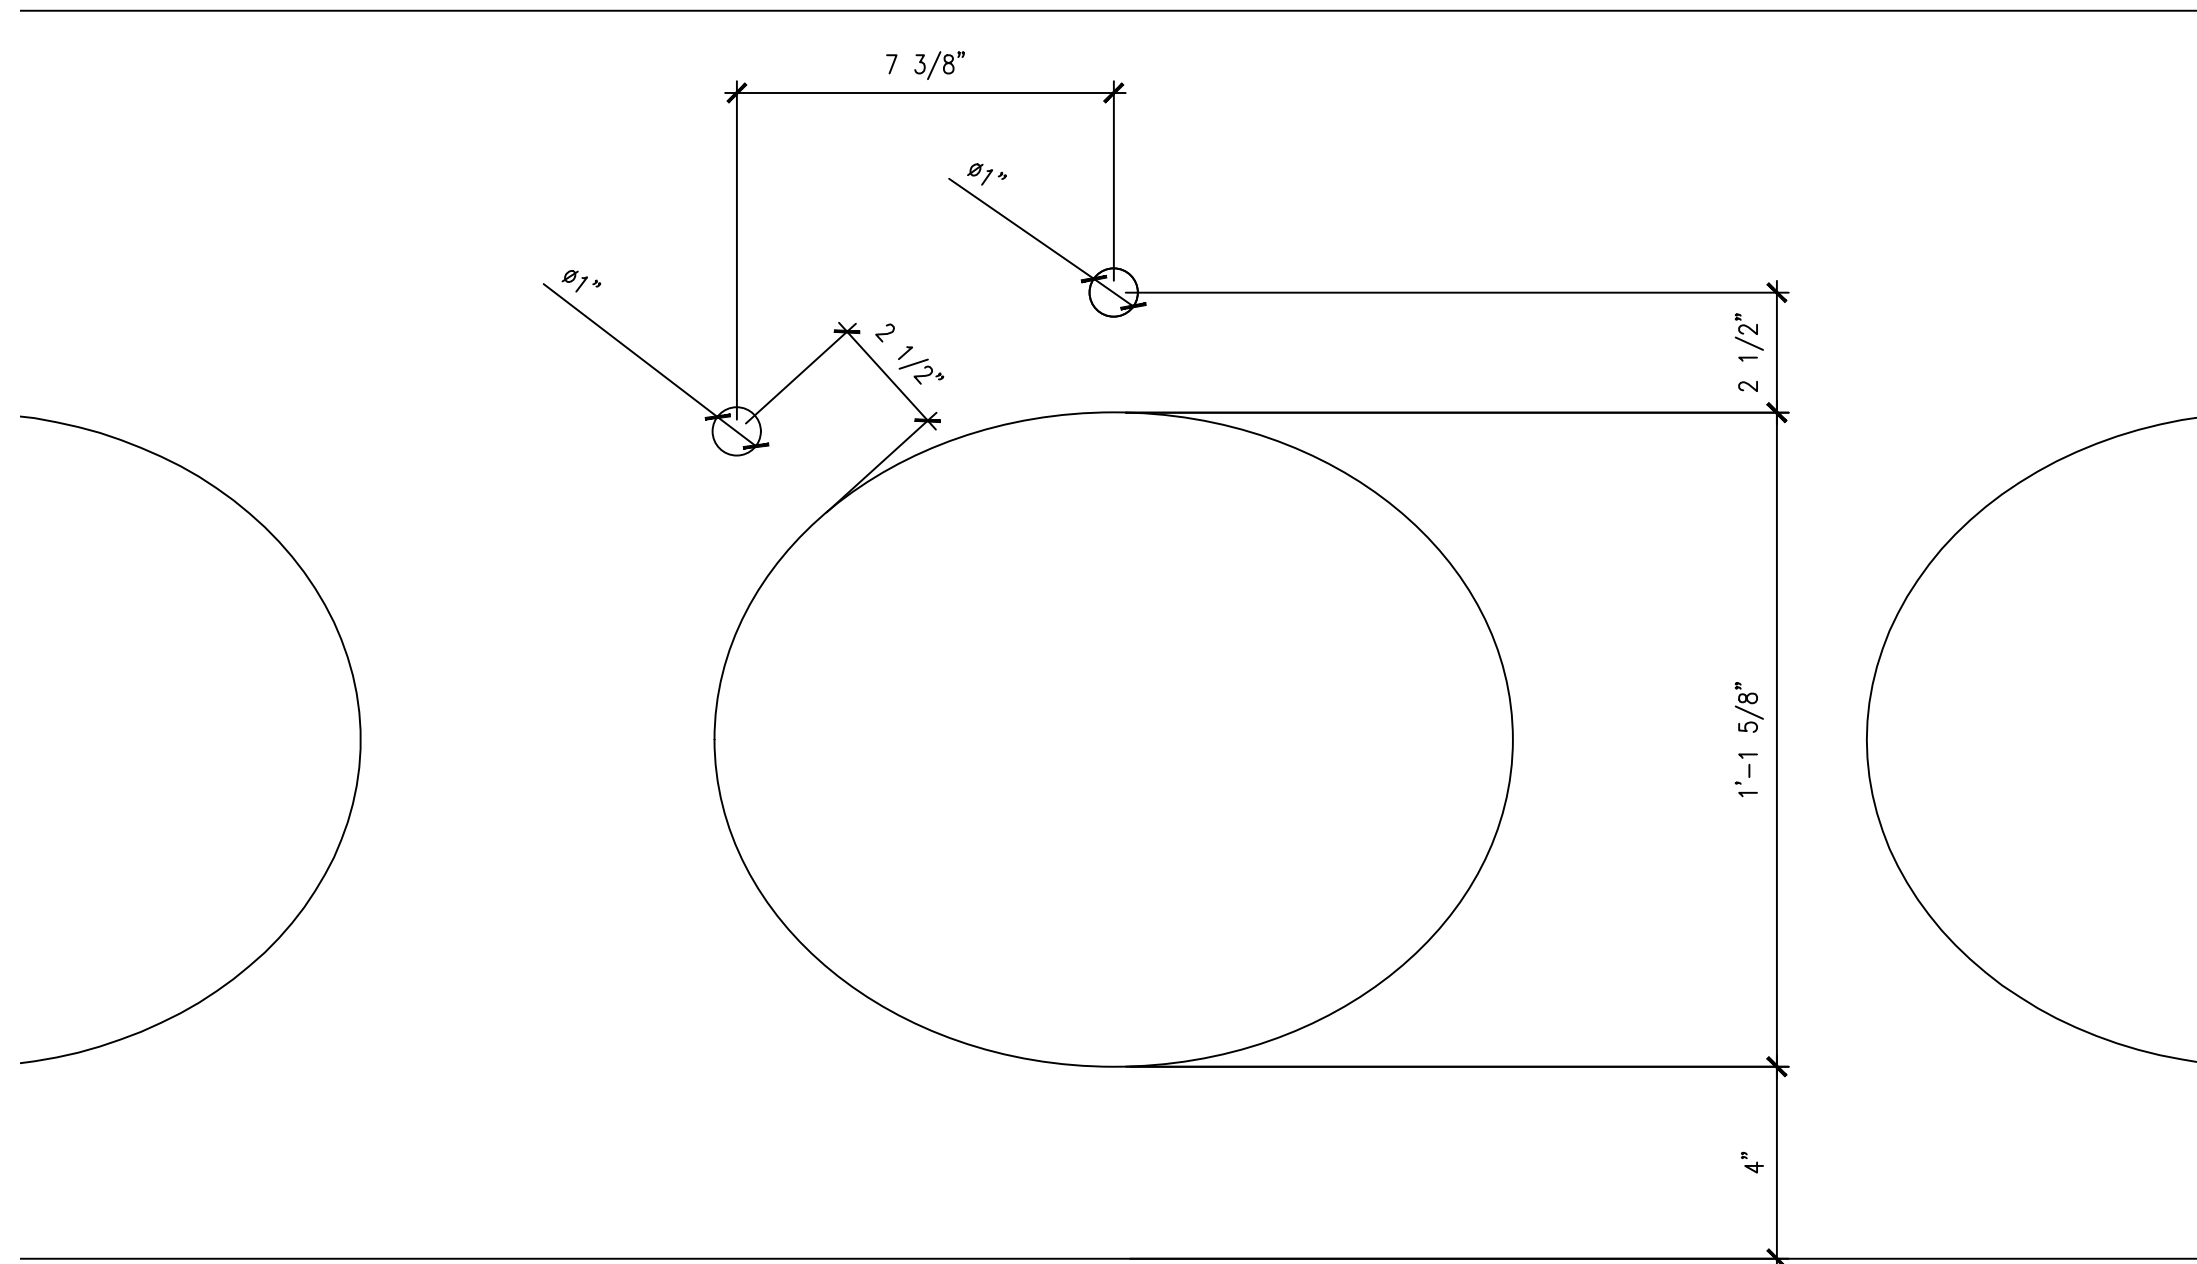

05 3/4"x1'-0" STONE COUNTERTOPS --8TH FLOOR MEN'S DETAIL VIEW

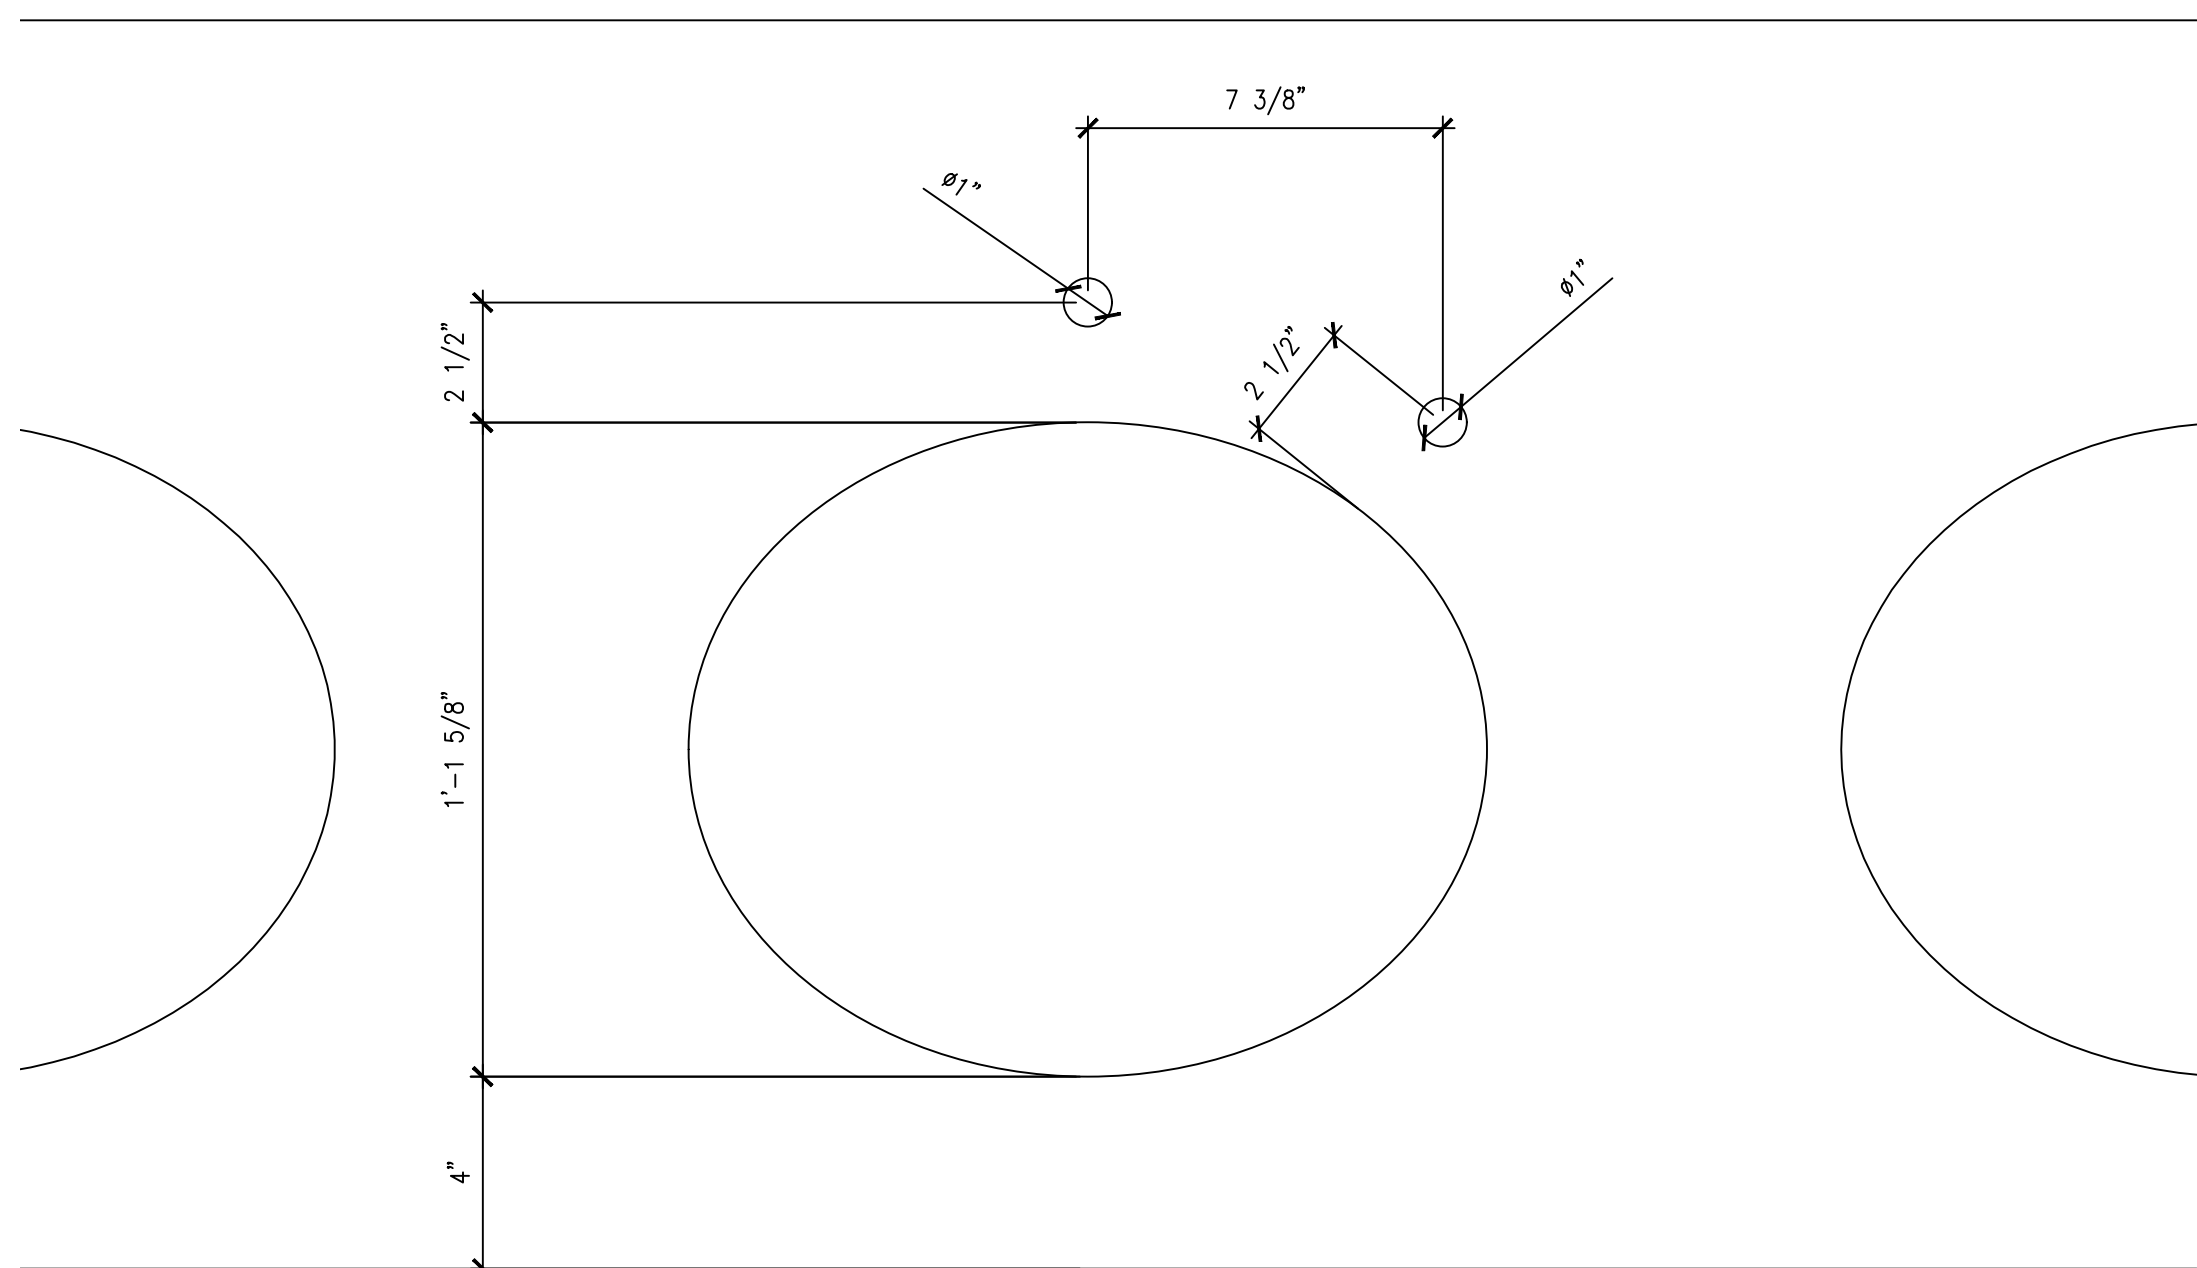

04 3/4"x1'-0" STONE COUNTERTOPS --8TH FLOOR WOMEN'S DETAIL VIEW

AUSTRO TILE & STONE, LLC
30-25 93RD STREET
EAST ELMHURST, NY 11369

CONTRACTOR: JRM CONSTRUCTION
MANAGEMENT, LLC
242 WEST 36TH STREET
11TH FLOOR
NEW YORK, NY 10018

INTERIOR DESIGNER:


ISSUE FOR APPROVAL 10/09/23
ISSUE NAME DATE

ARCHITECT: SPACESMITH
ONE NEW YORK PLAZA SUITE 4200
NEW YORK, NY 1004
PH: 212 260 5583


PROJECT NAME: JACK RESNICK & SONS
255 GREENWICH STREET
NEW YORK, NY 10007

SHEET NAME: STONE COUNTERTOPS
8TH FLOOR


DATE: _____
PROJECT NO.: _____
PRINCIPAL: _____
DRAWING BY: _____
CHECKED BY: _____
SCALE: _____
DWG No.: T-502
25 of 29

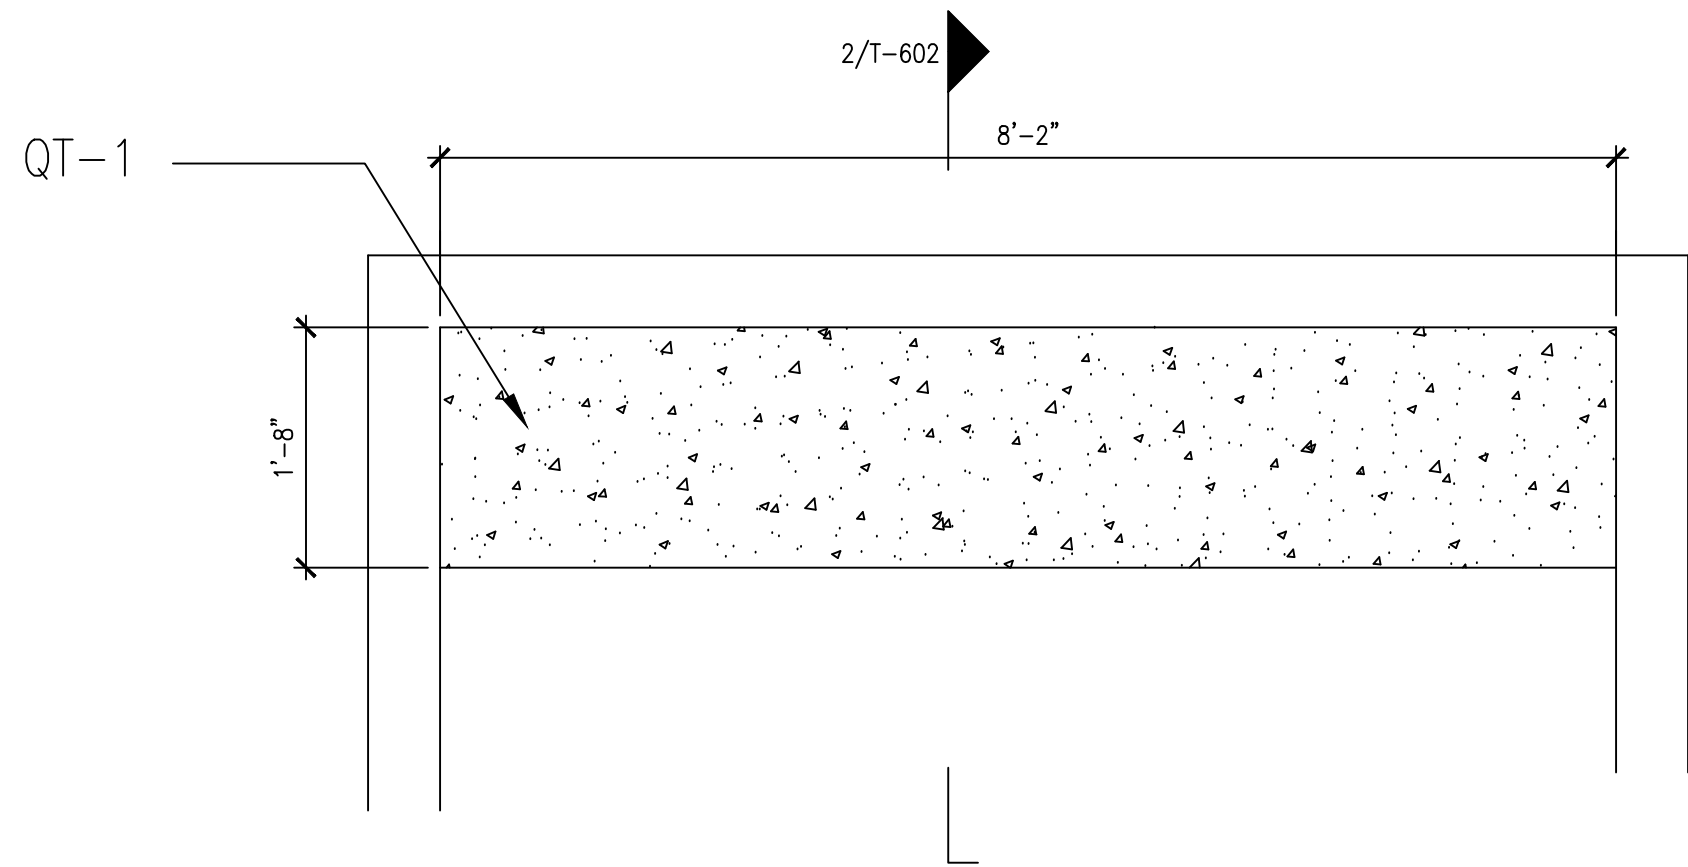


01 3/4"x1'-0" STONE COUNTERTOPS -9TH FLOOR WOMEN'S POWDER ROOM

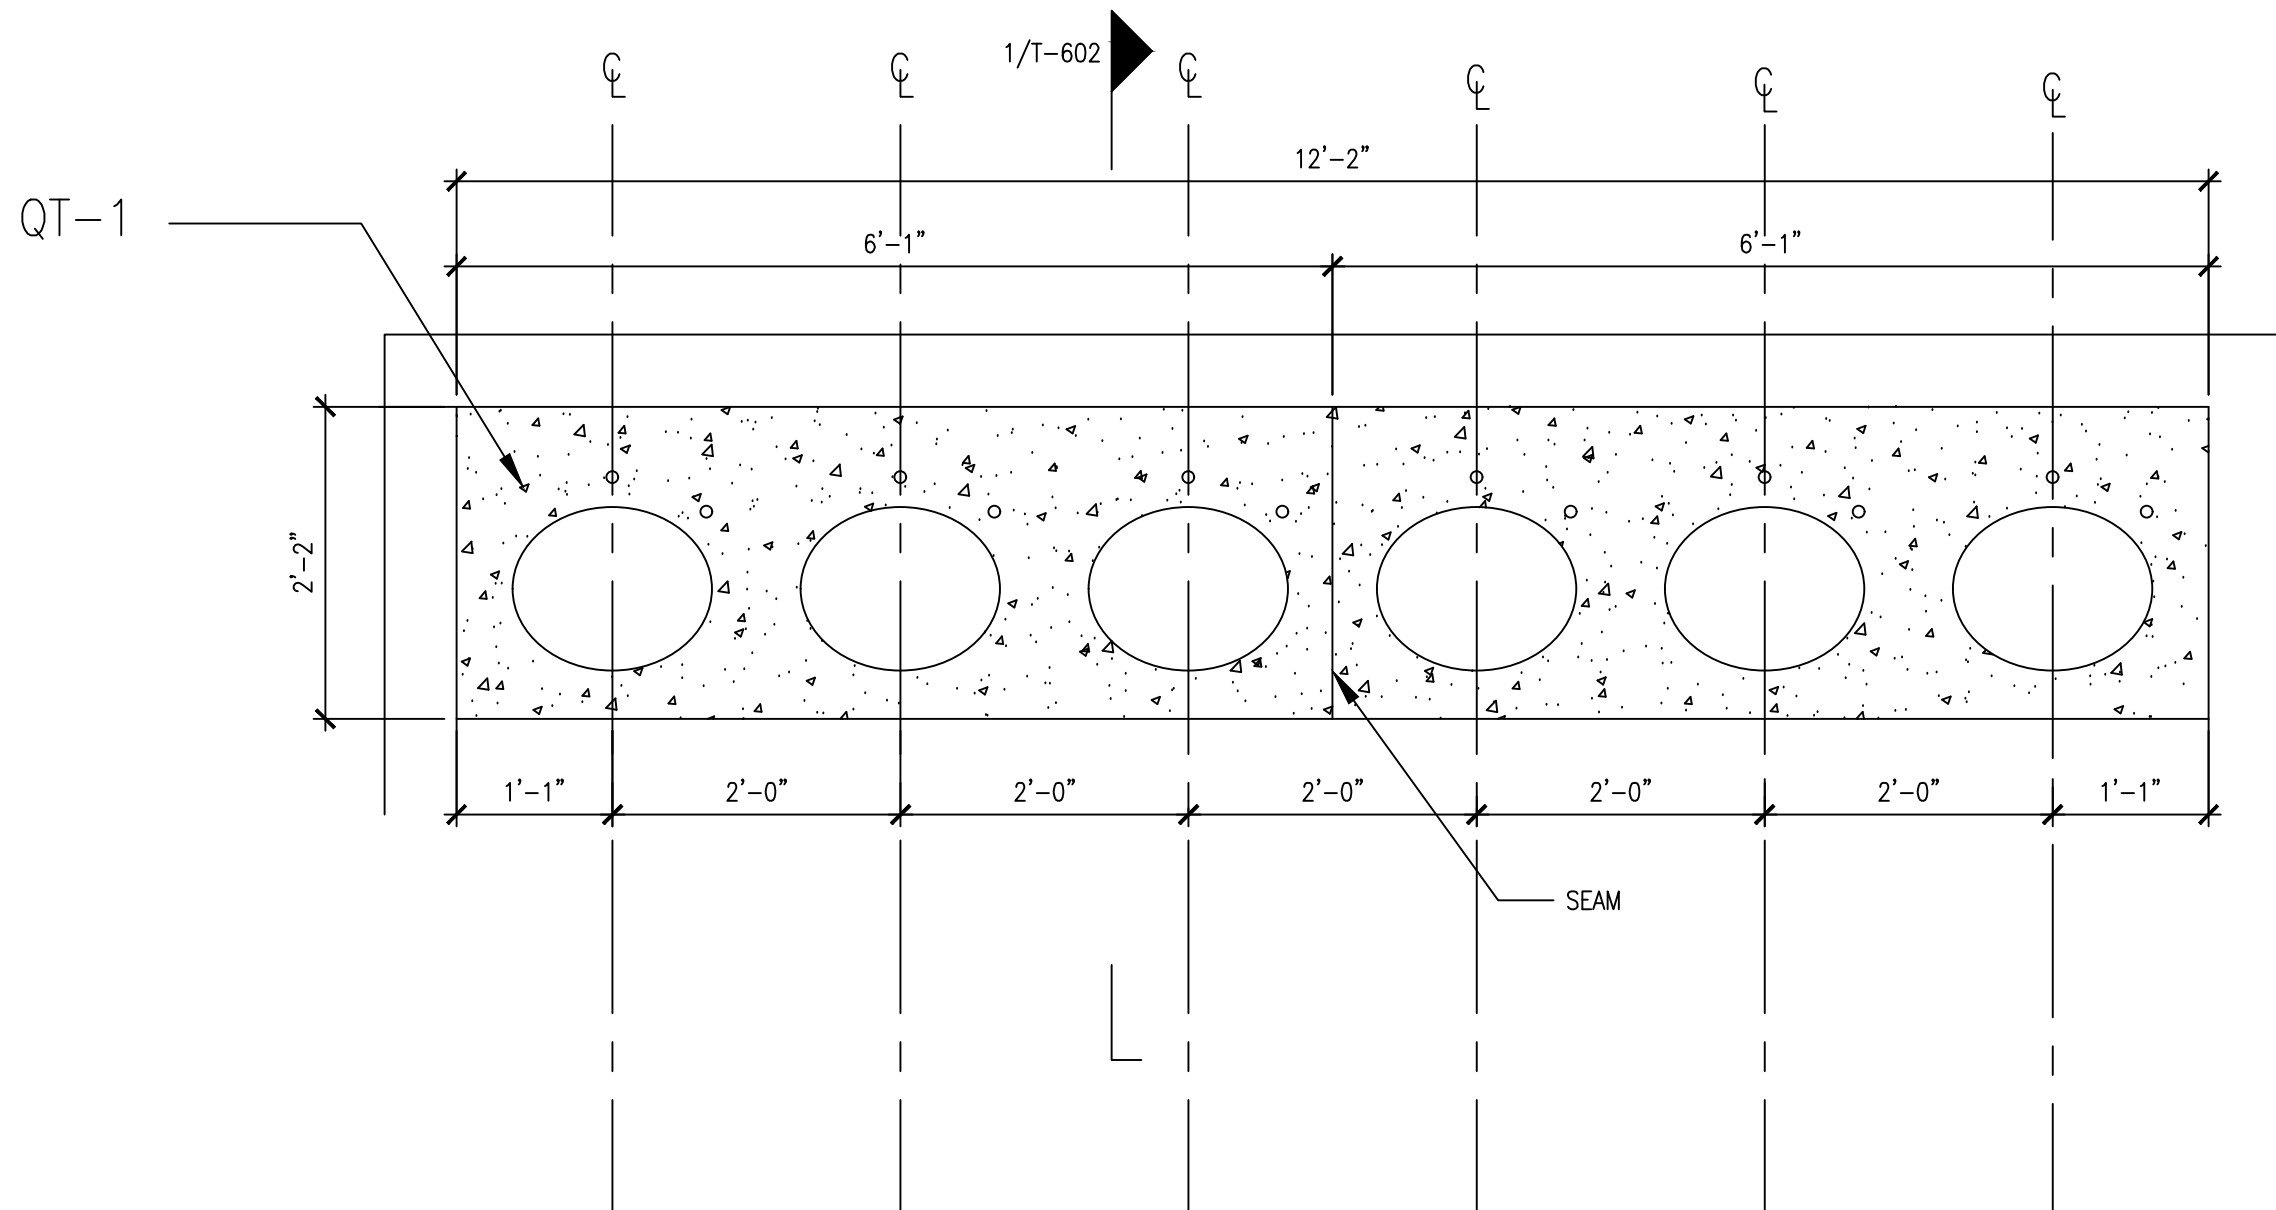


02 3/4"x1'-0" STONE COUNTERTOPS -9TH FLOOR WOMEN'S RESTROOM

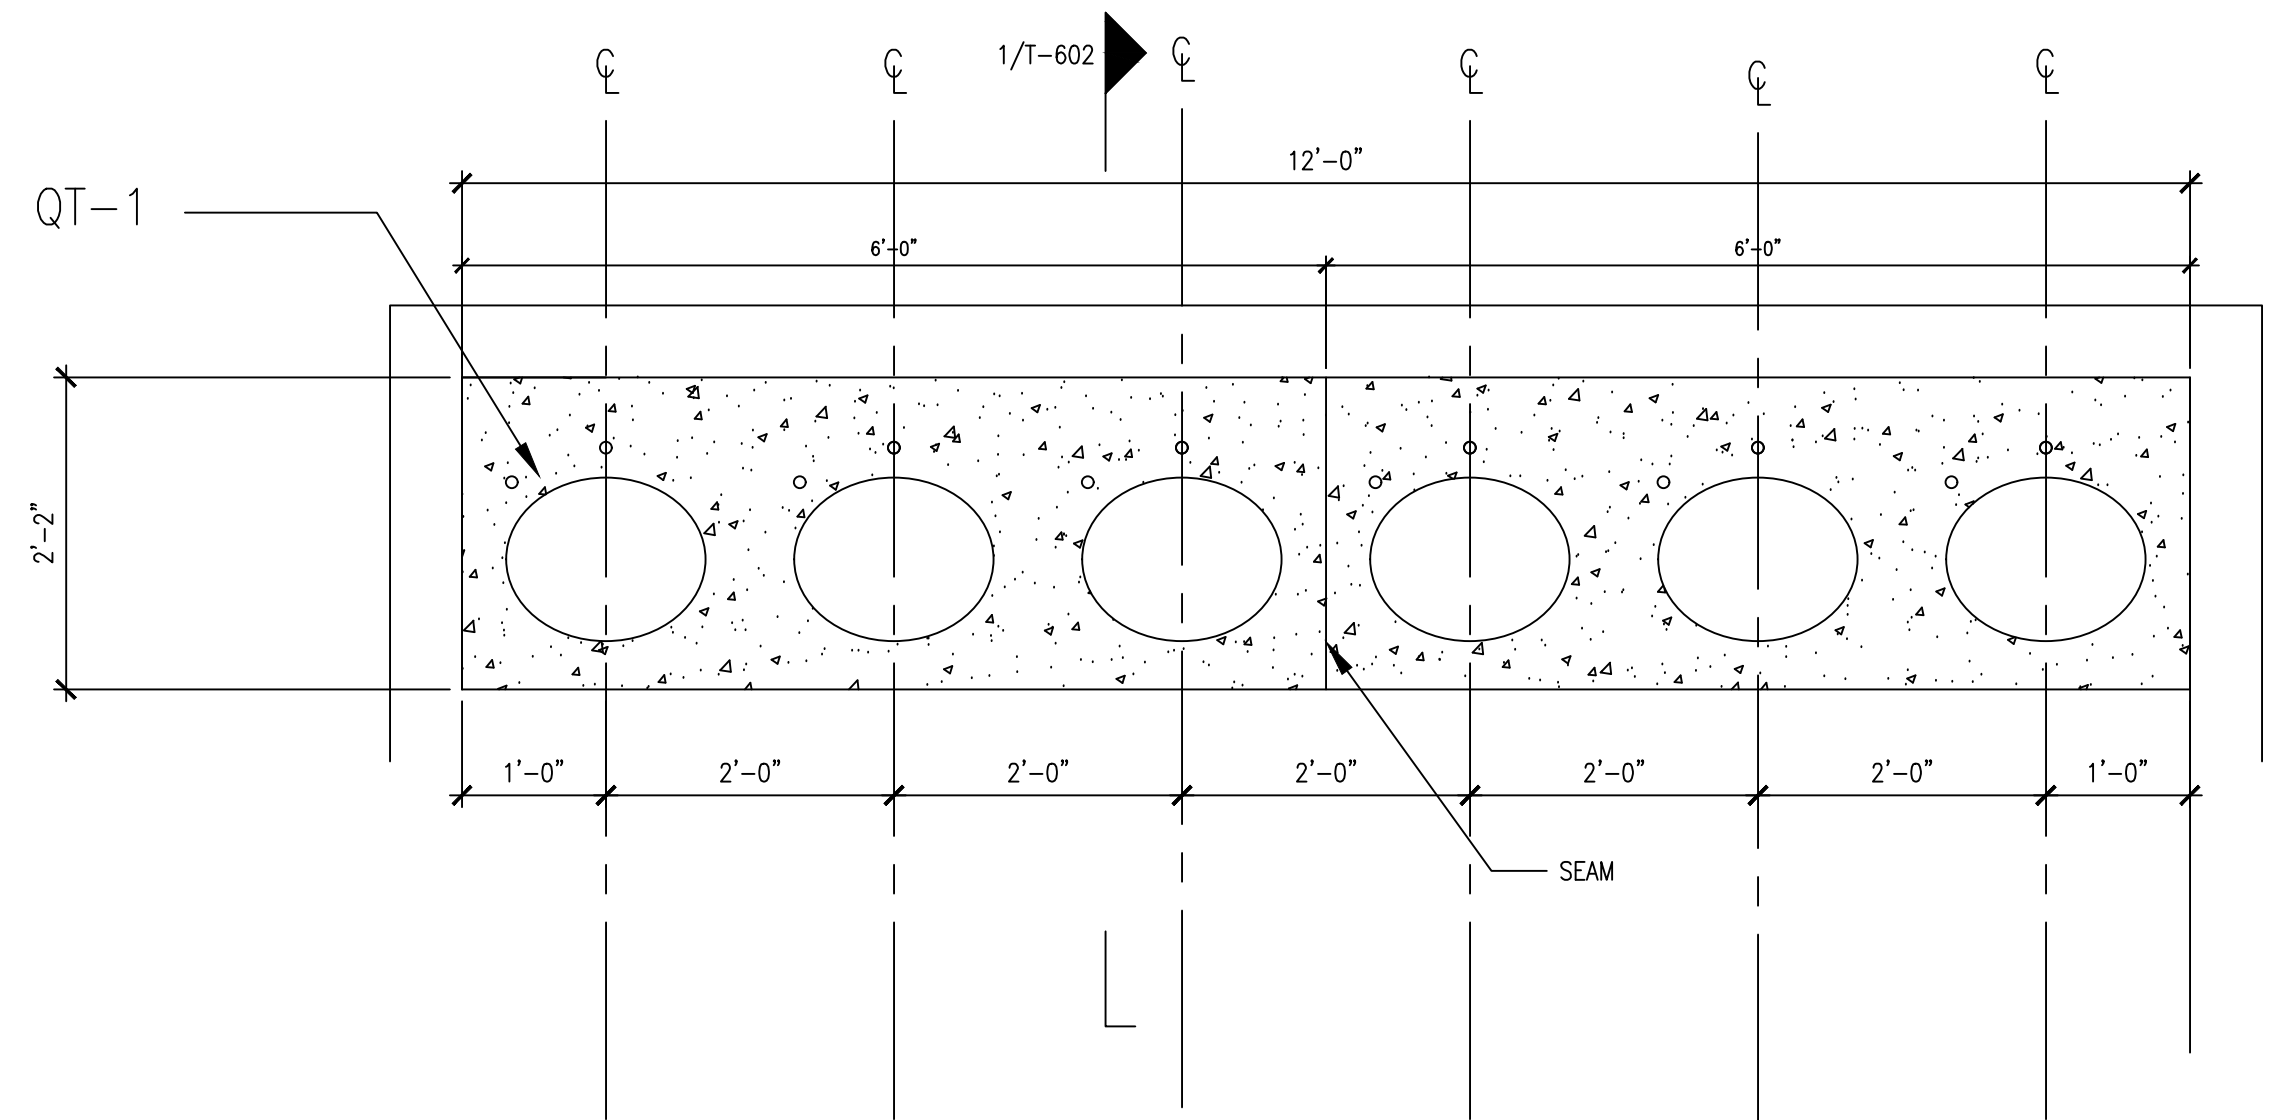

03 3/4"x1'-0" STONE COUNTERTOPS -9TH FLOOR MEN'S RESTROOM

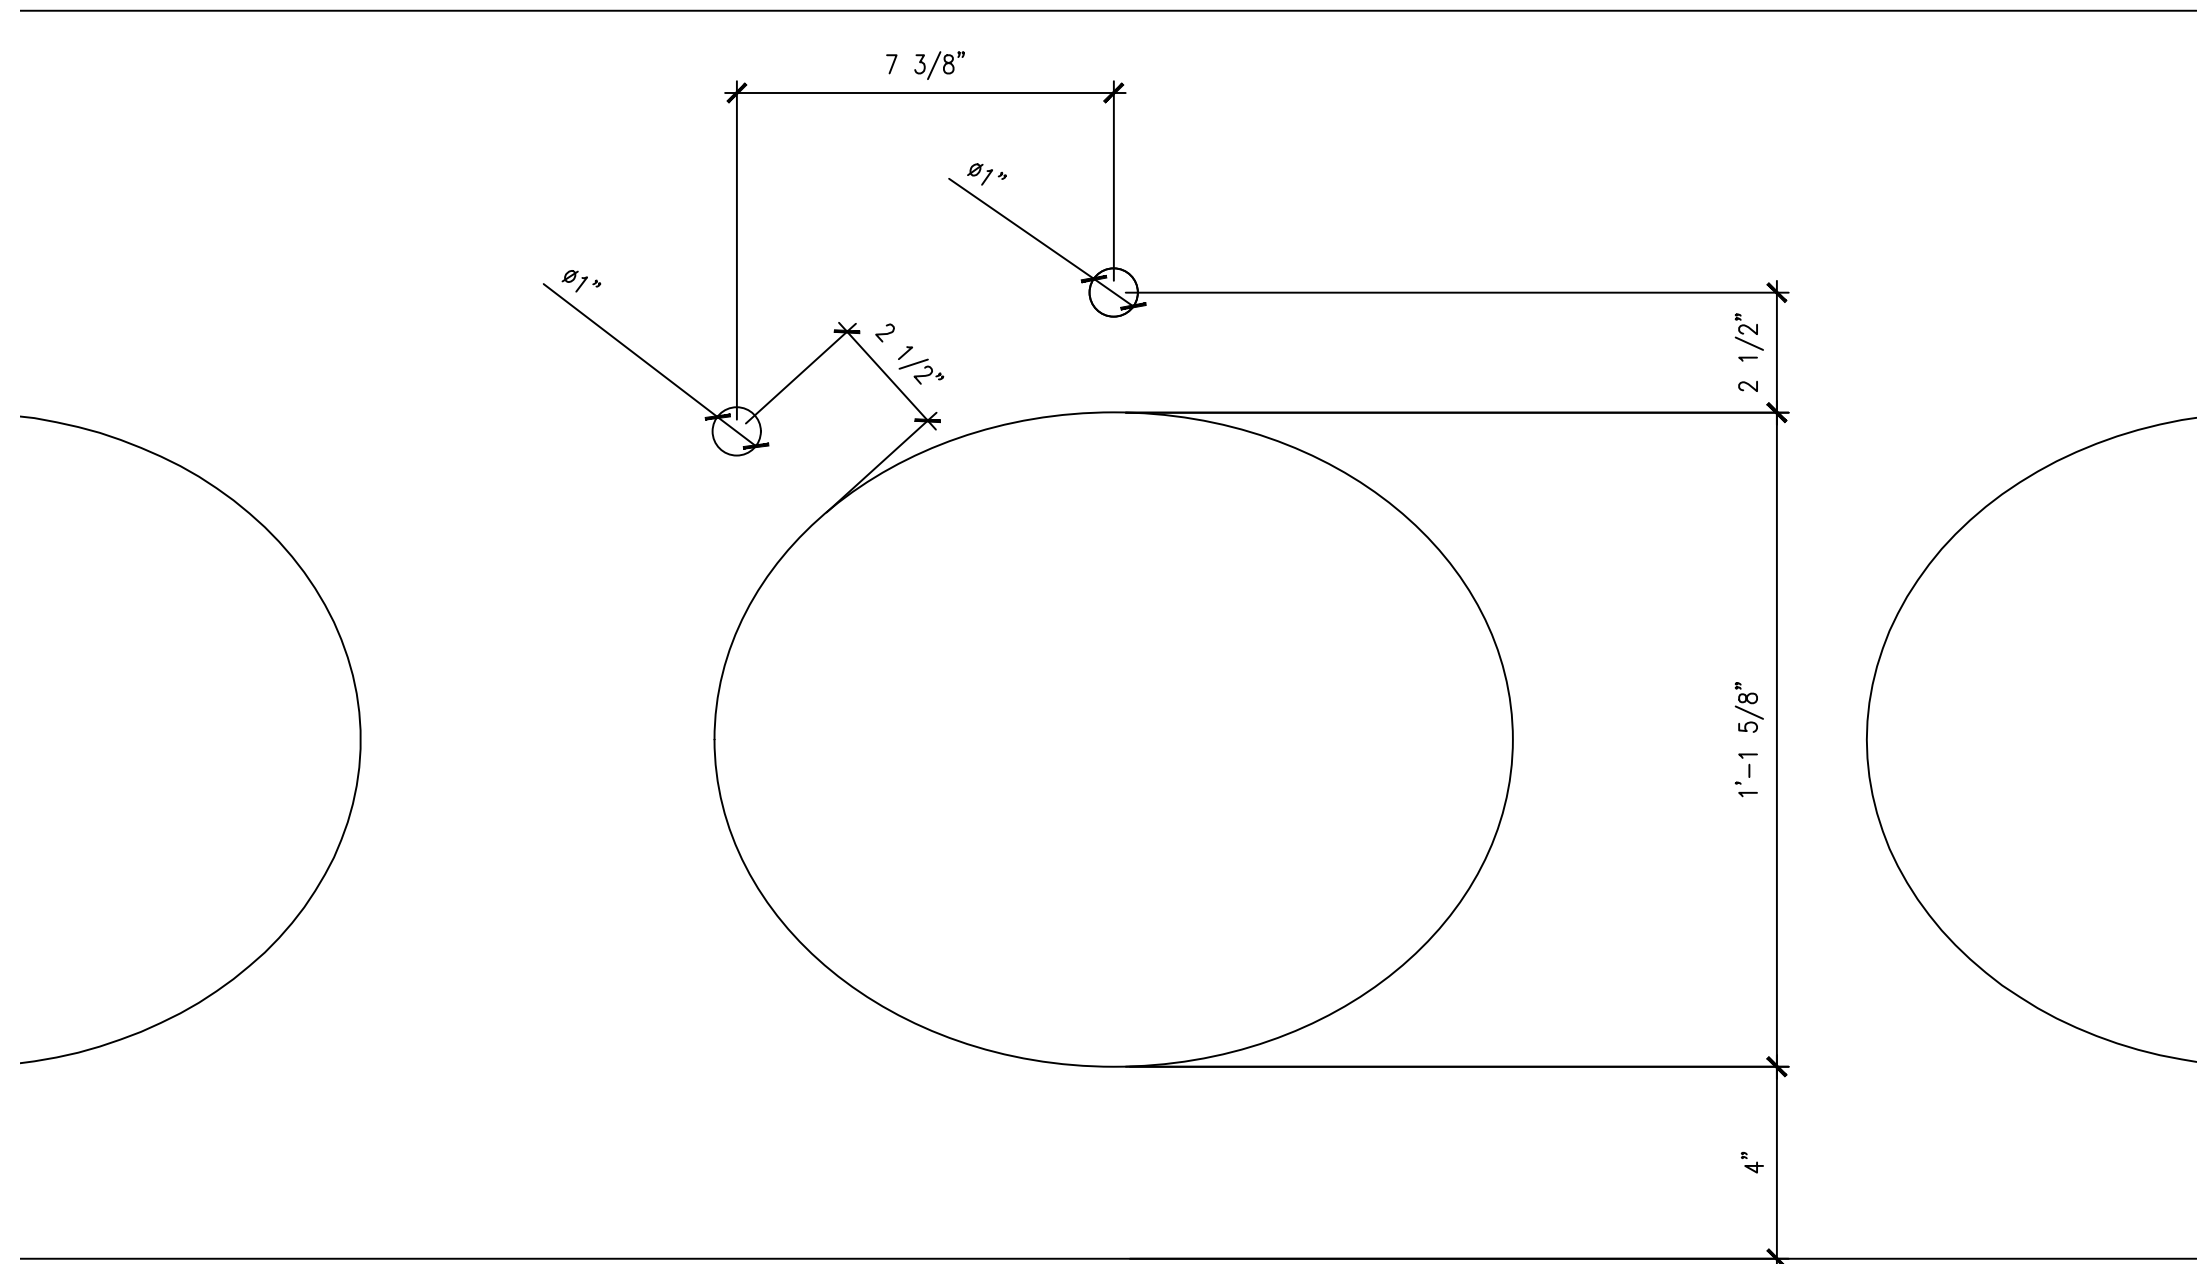

05 3/4"x1'-0" STONE COUNTERTOPS -9TH FLOOR MEN'S DETAIL VIEW

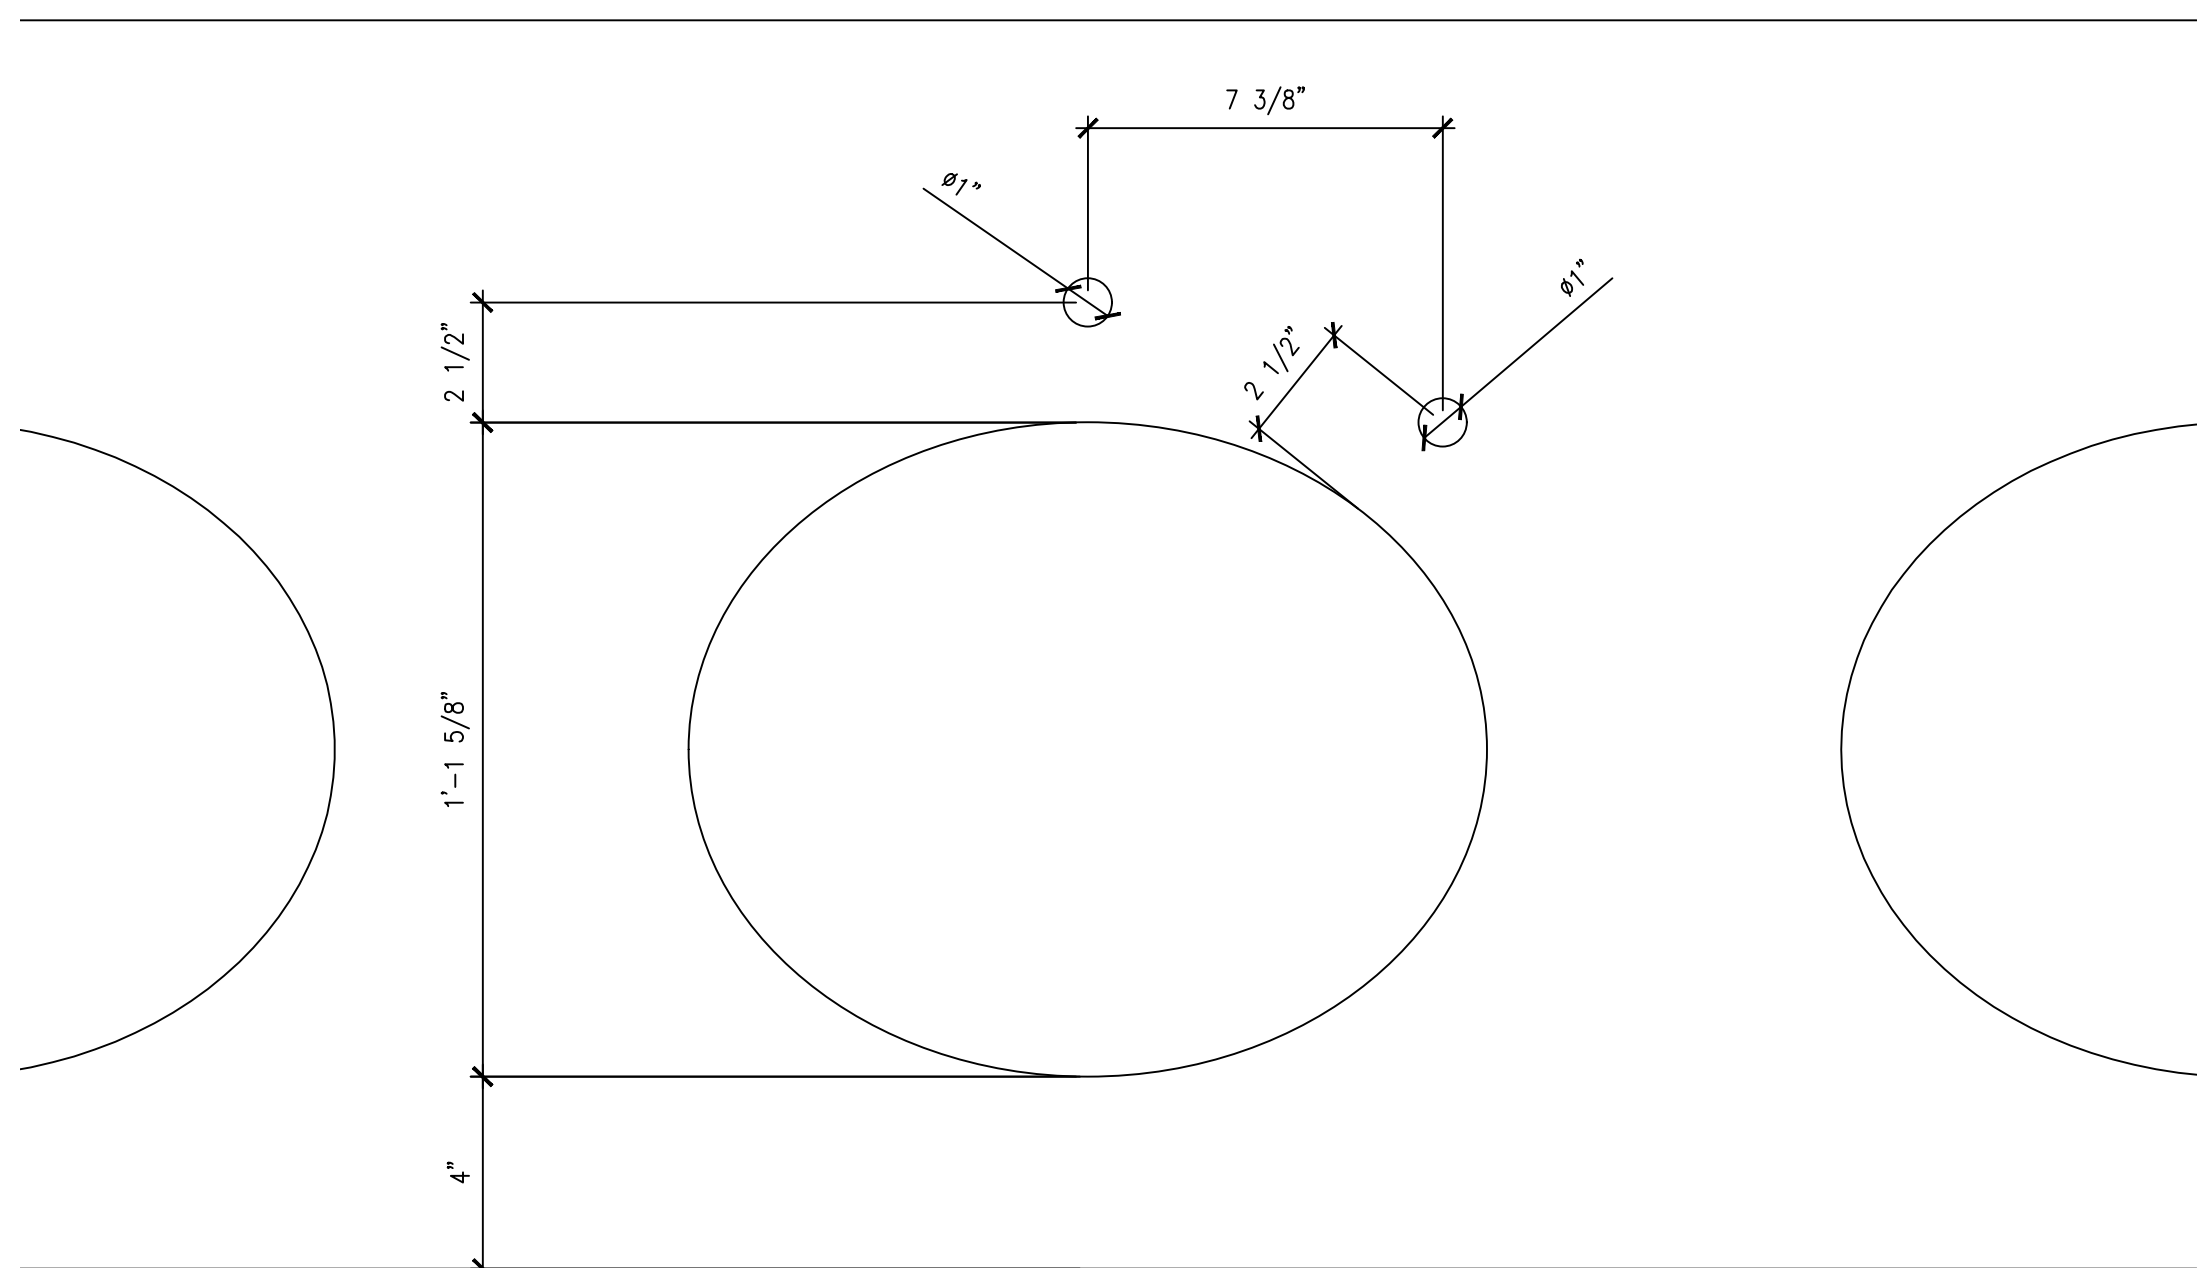

04 3/4"x1'-0" STONE COUNTERTOPS -9TH FLOOR WOMEN'S DETAIL VIEW

AUSTRO TILE & STONE, LLC
30-25 93RD STREET
EAST ELMHURST, NY 11369

CONTRACTOR:
JRM CONSTRUCTION
MANAGEMENT, LLC
242 WEST 36TH STREET
11TH FLOOR
NEW YORK, NY 10018

INTERIOR DESIGNER:


ISSUE FOR APPROVAL 10/09/23
ISSUE NAME DATE

ARCHITECT:
SPACESMITH
ONE NEW YORK PLAZA SUITE 4200
NEW YORK, NY 1004
PH: 212 260 5583


PROJECT NAME:
JACK RESNICK & SONS
255 GREENWICH STREET
NEW YORK, NY 10007

SHEET NAME:
STONE COUNTERTOPS
9TH FLOOR


DATE:
PROJECT NO.:
PRINCIPAL:
DRAWING BY:
CHECKED BY:
SCALE:
DWG No.:
T-503
26 of 29

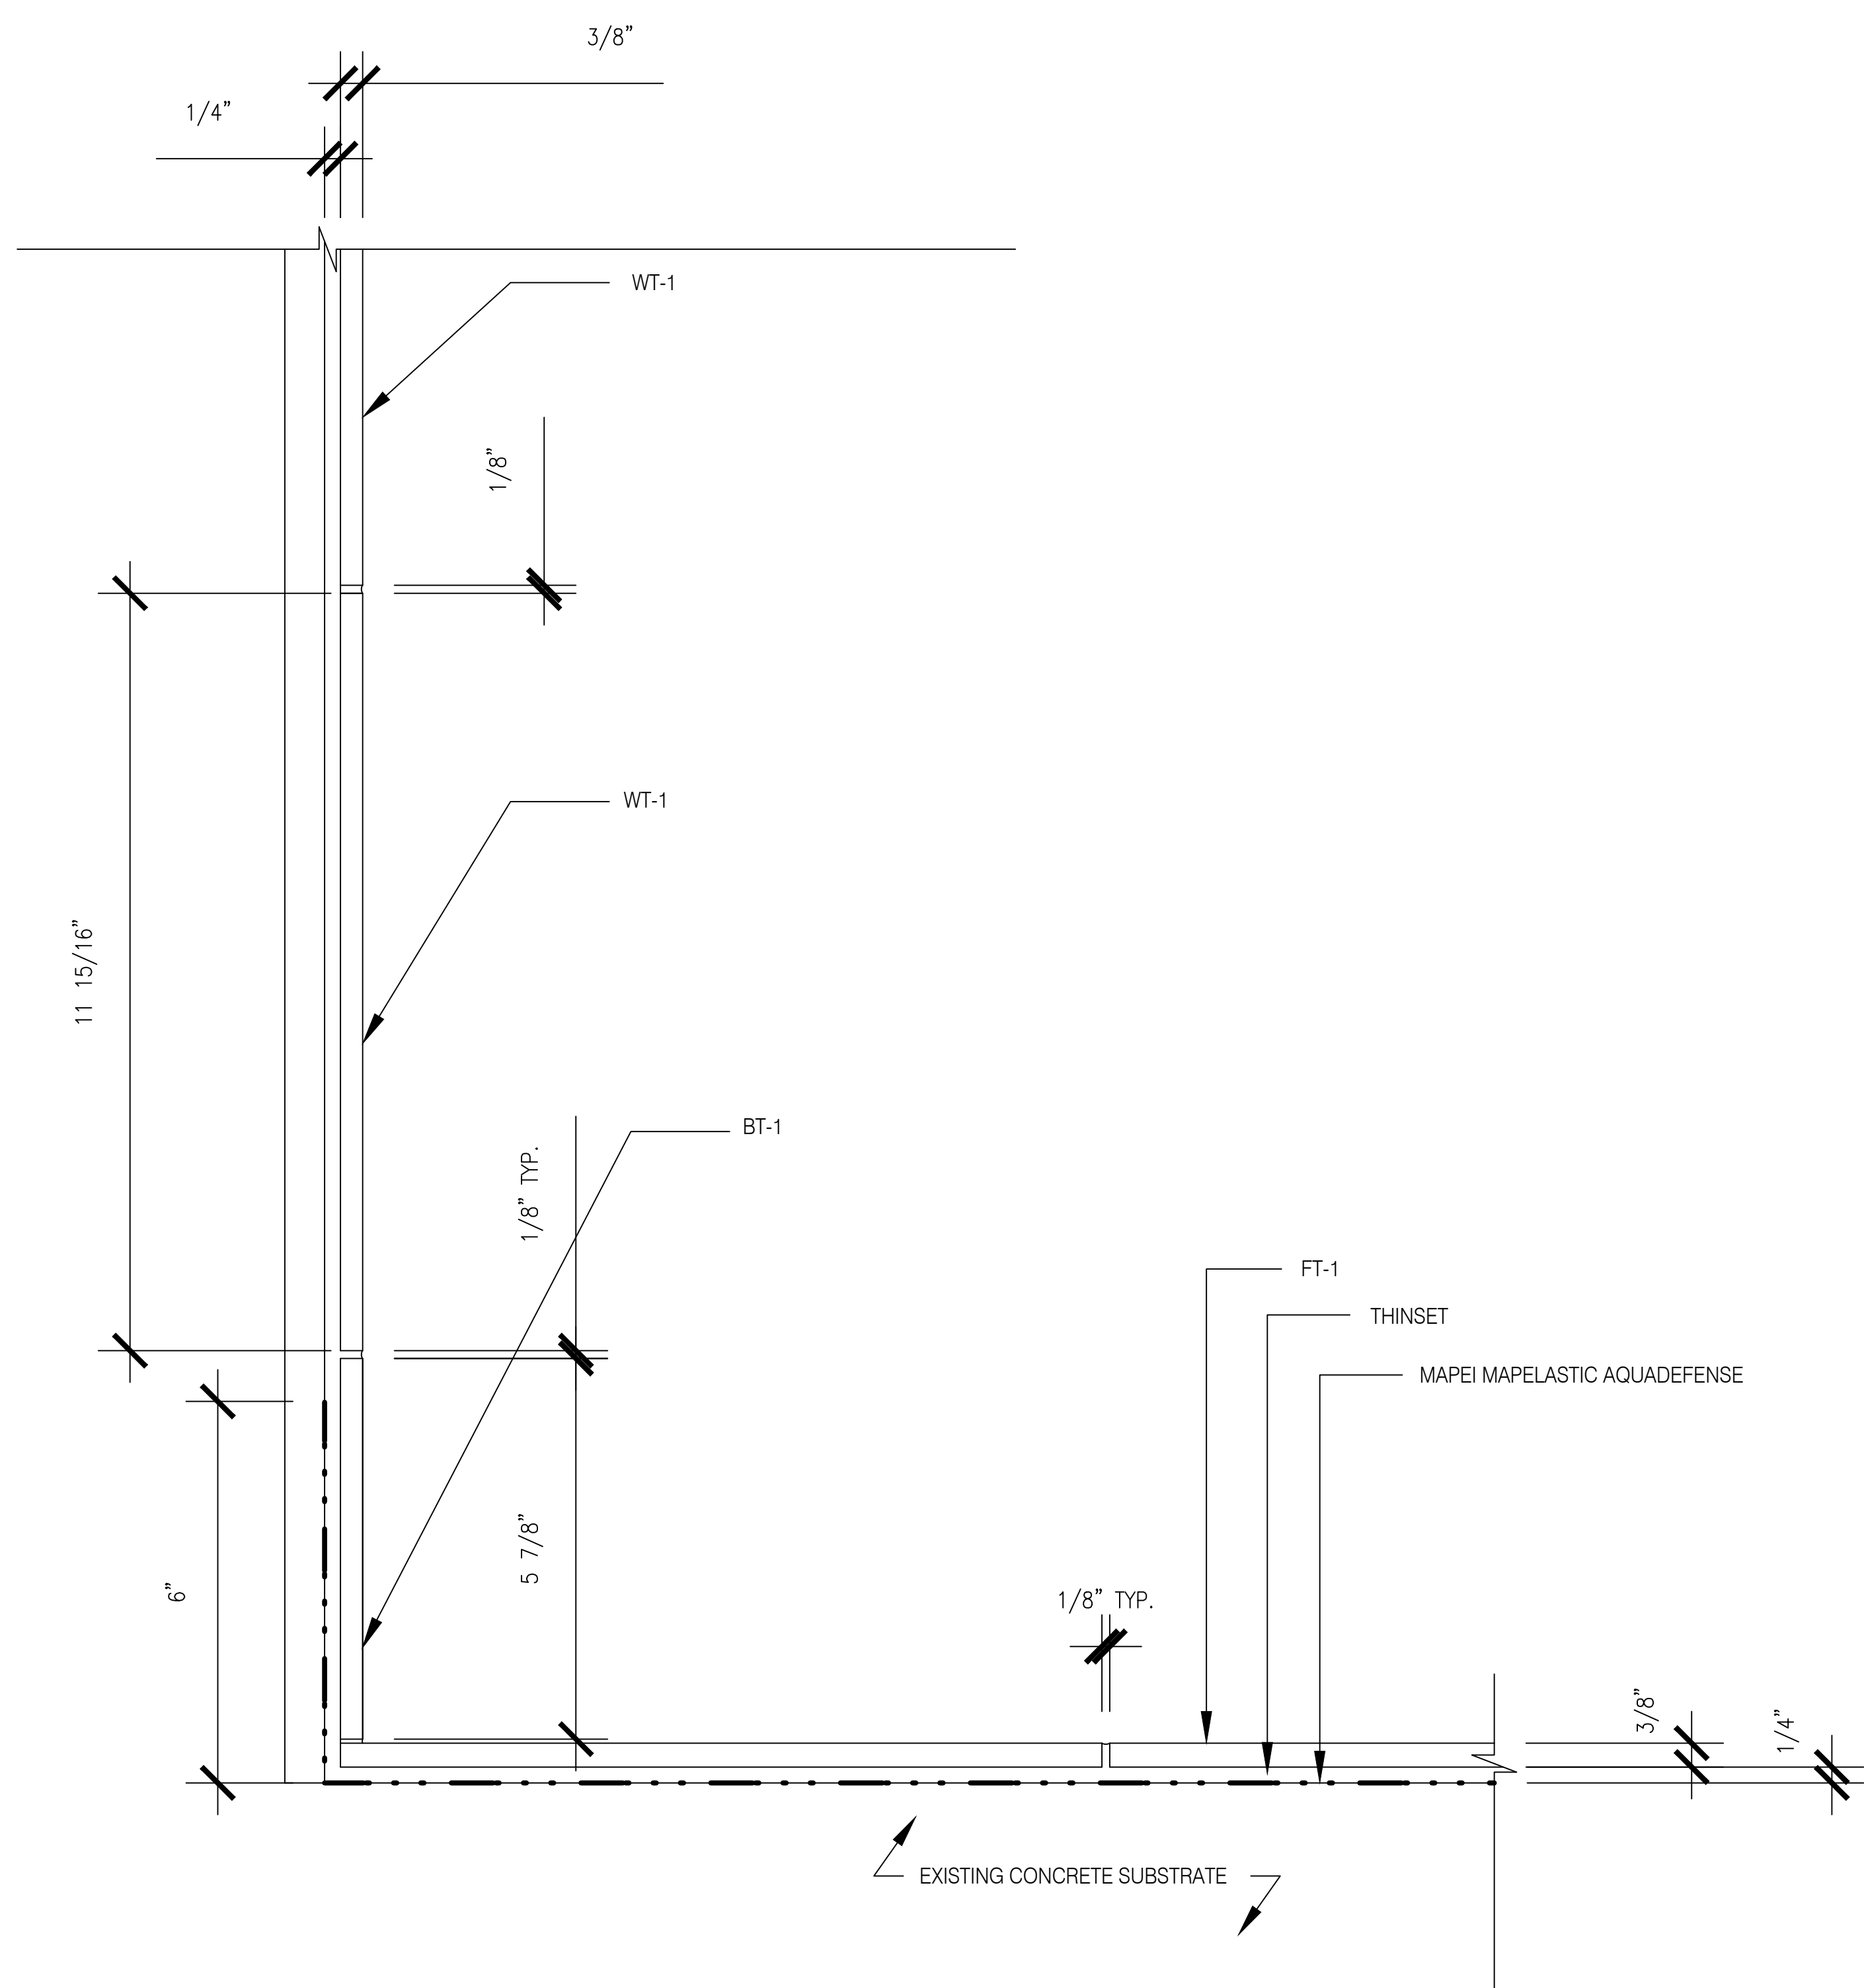

01
DETAIL: FLOOR/BASE/WALL TILE

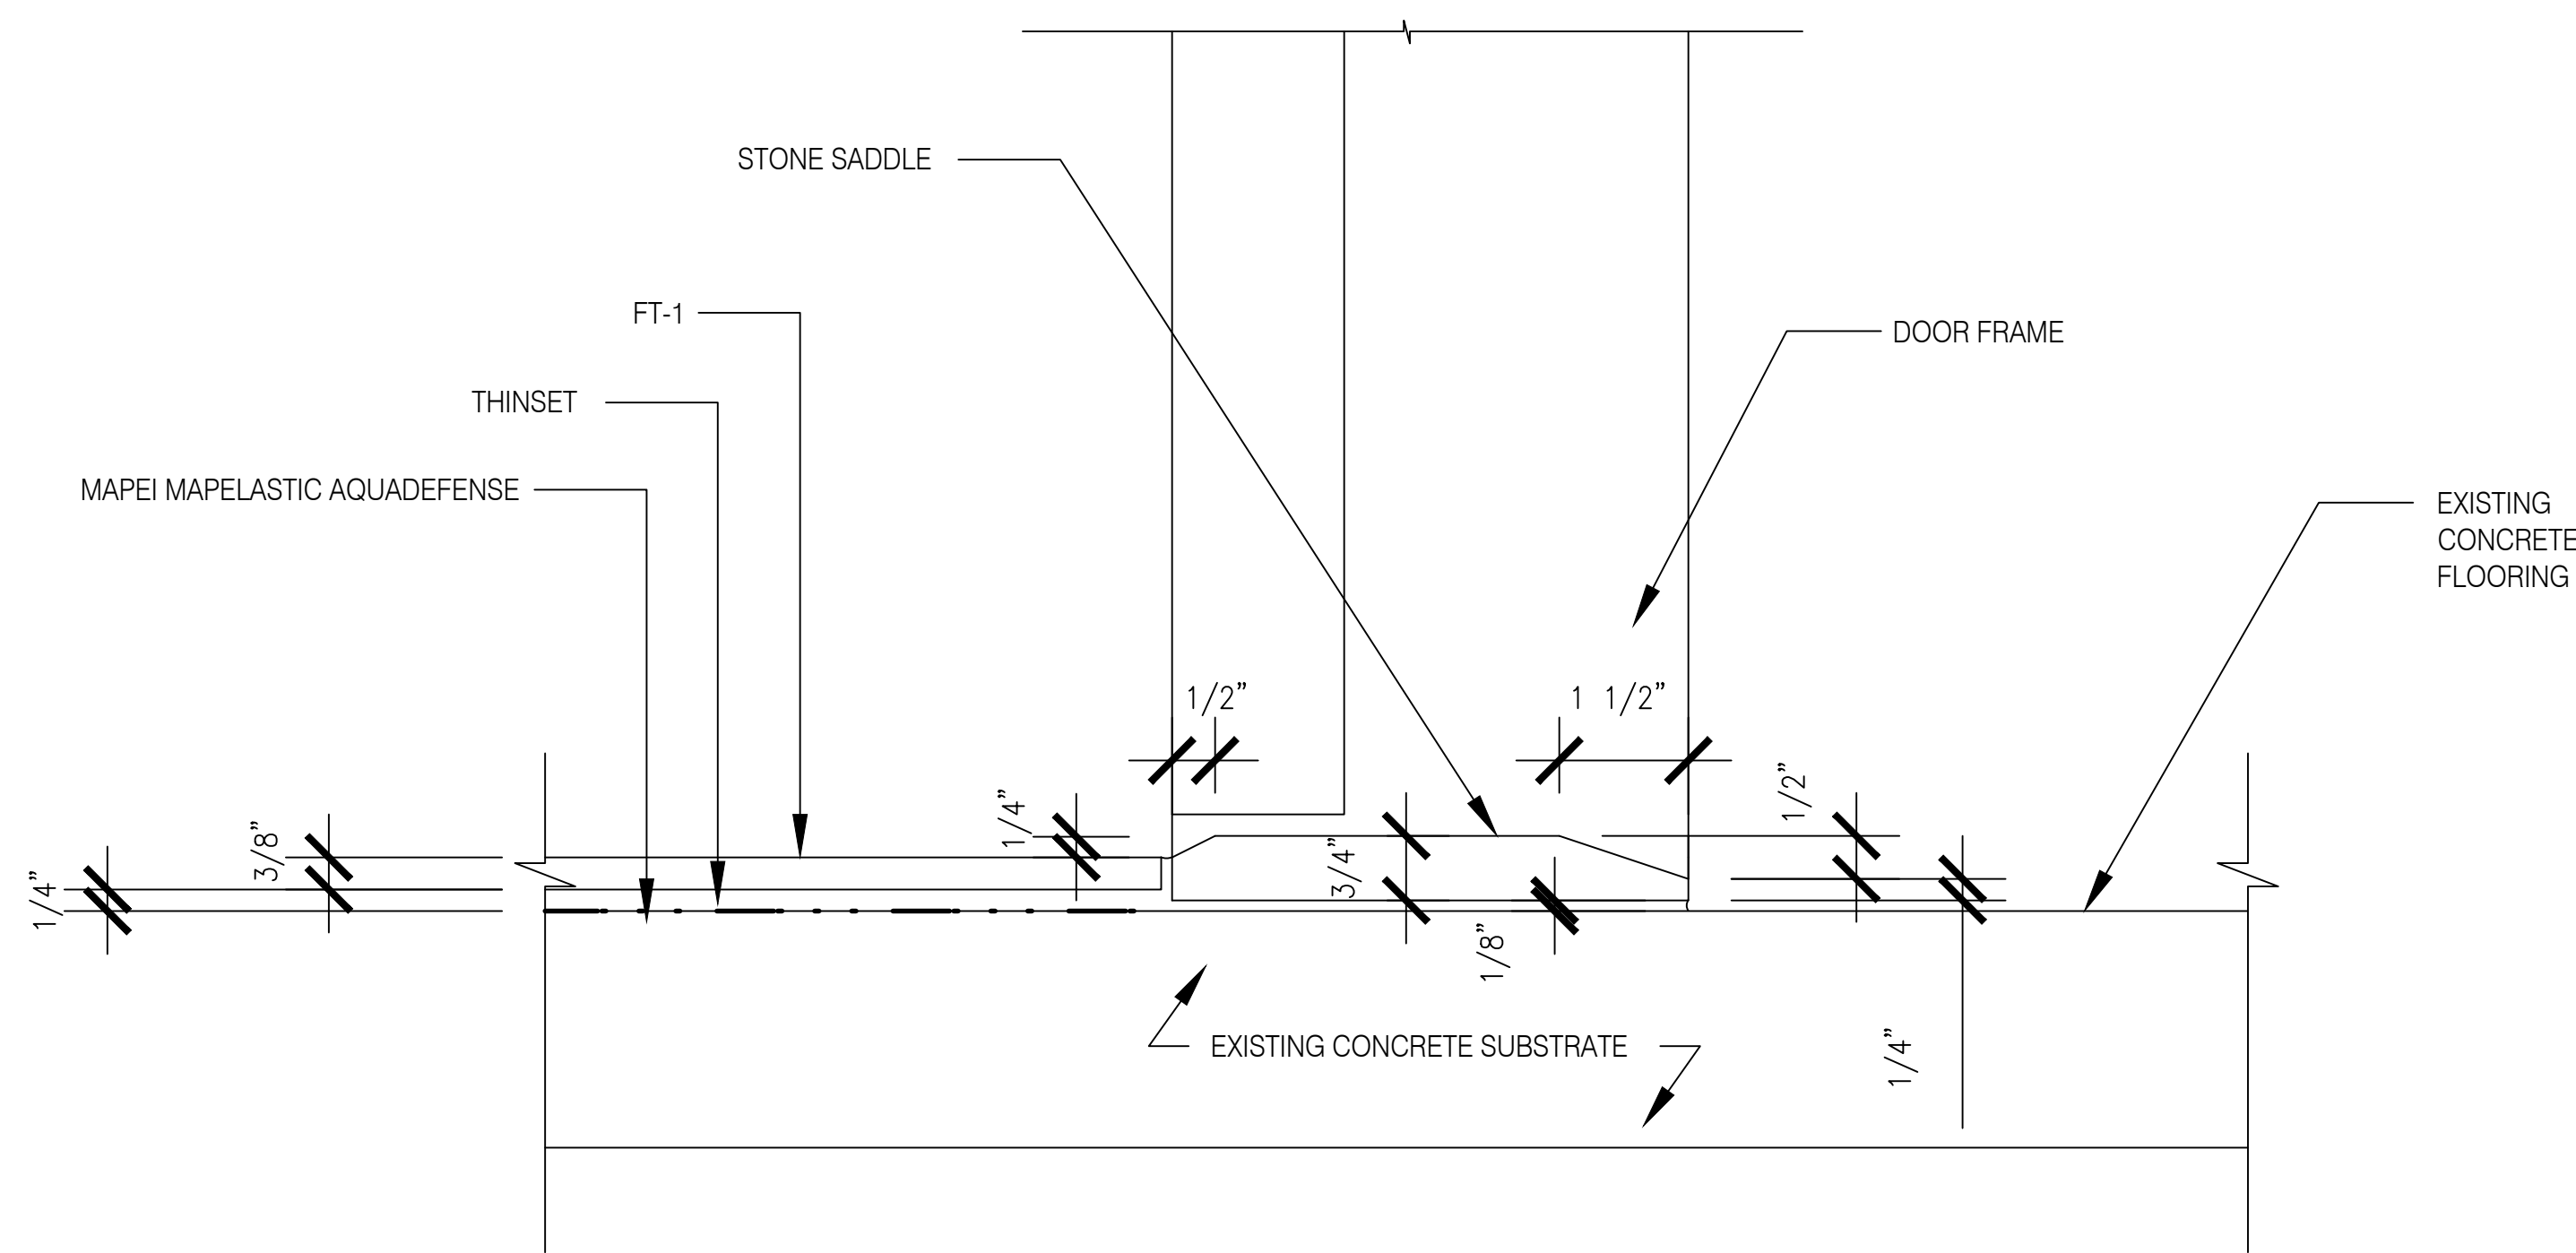

02
DETAIL: STONE SADDLE

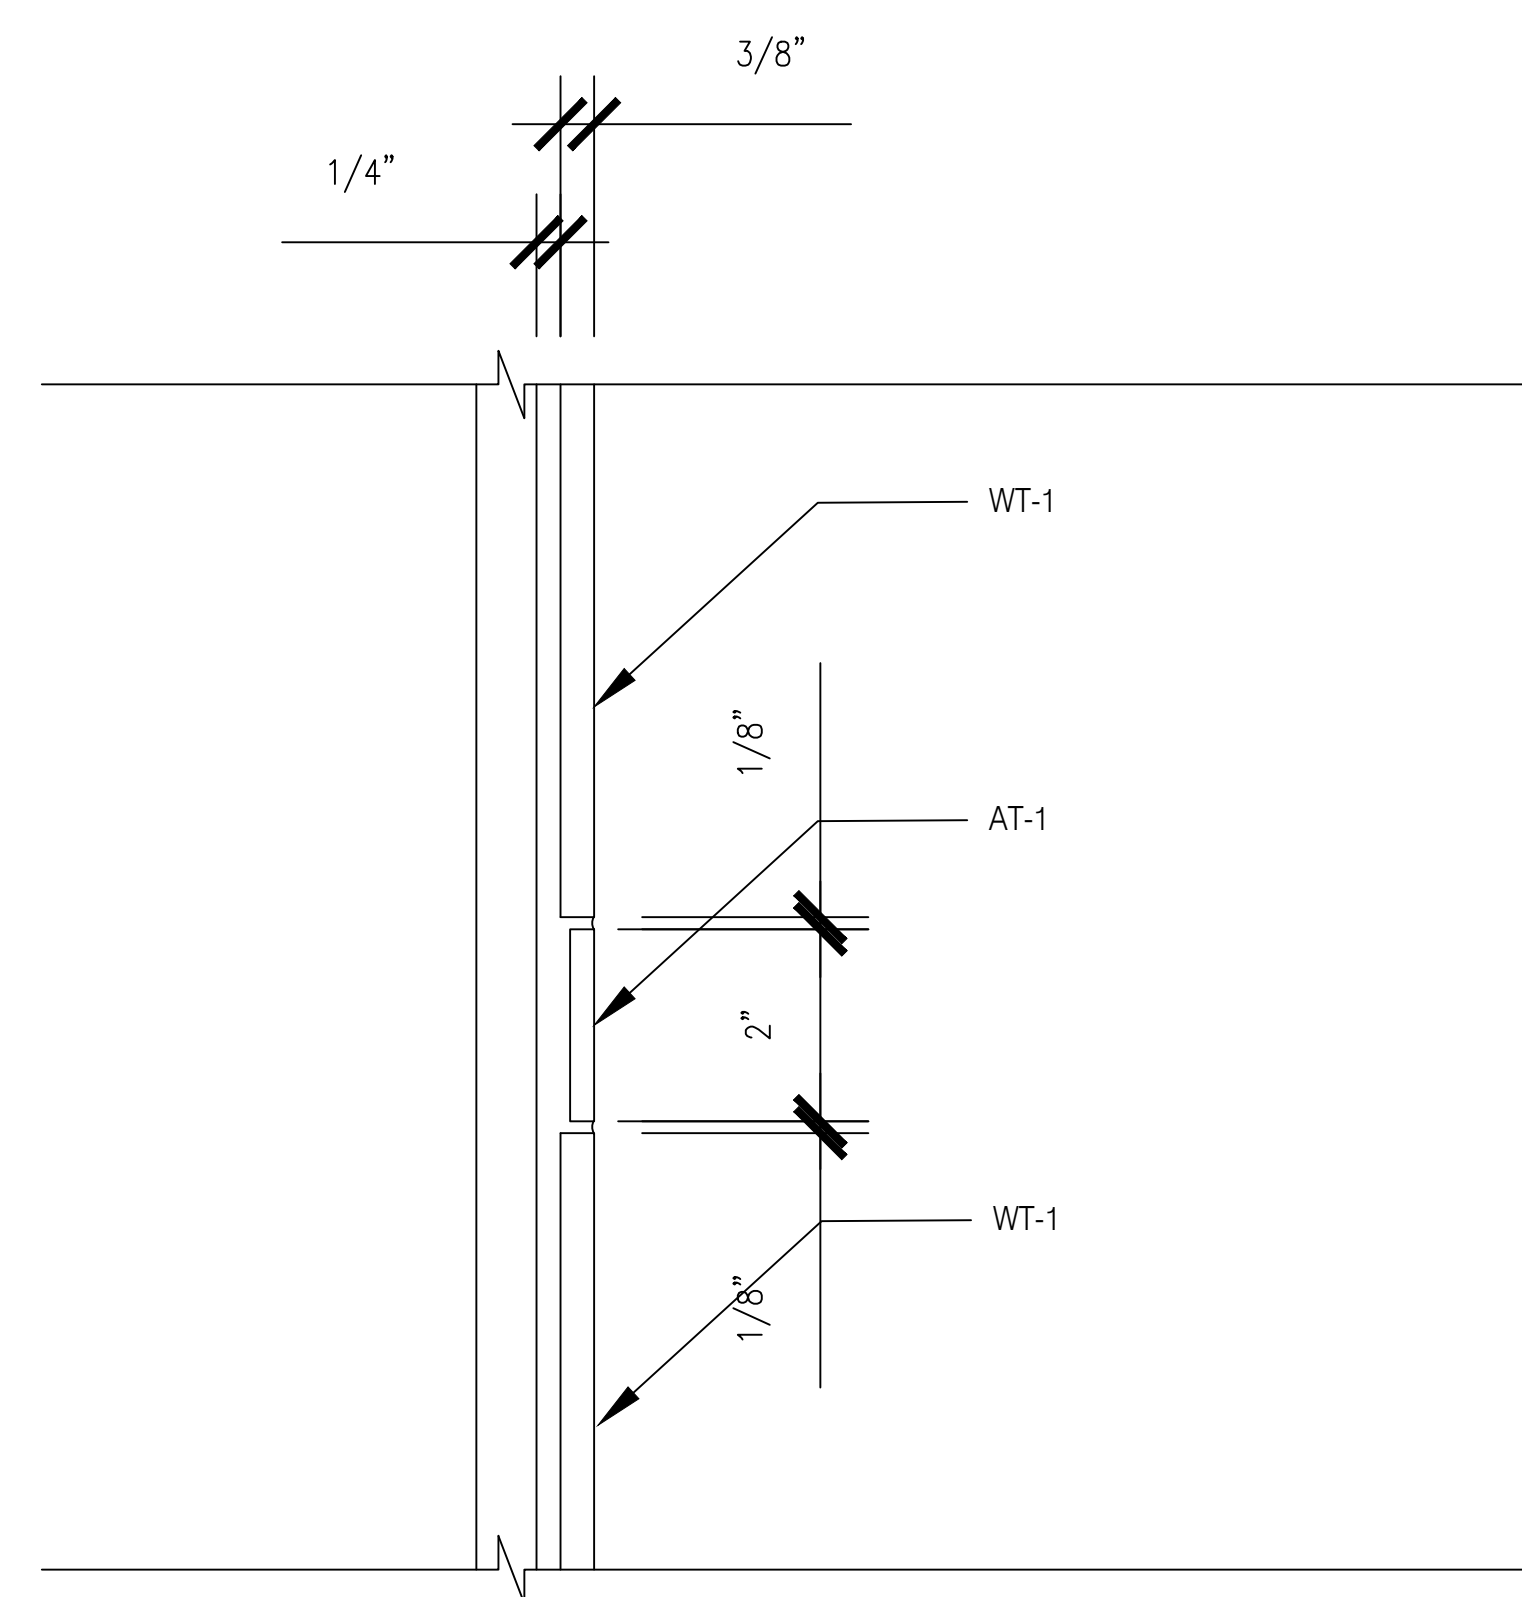

03
DETAIL: WALL/ACCENT TILE

AUSTRO TILE & STONE, LLC
30-25 93RD STREET
EAST ELMHURST, NY 11369

CONTRACTOR:
JRM CONSTRUCTION
MANAGEMENT, LLC
242 WEST 36TH STREET
11TH FLOOR
NEW YORK, NY 10018

INTERIOR DESIGNER:


ISSUE FOR APPROVAL 10/09/23
ISSUE NAME DATE

PROJECT NAME:
SPACESMITH
ONE NEW YORK PLAZA SUITE 4200
NEW YORK, NY 10004
PH: 212 620 5583


JACK RESNICK & SONS
255 GREENWICH STREET
NEW YORK, NY 10007

DETAILS
TILE

DATE:
PROJECT NO.:
PRINCIPAL:
DRAWING BY:
CHECKED BY:
SCALE:
DWG No.:
T-600
27 of 29

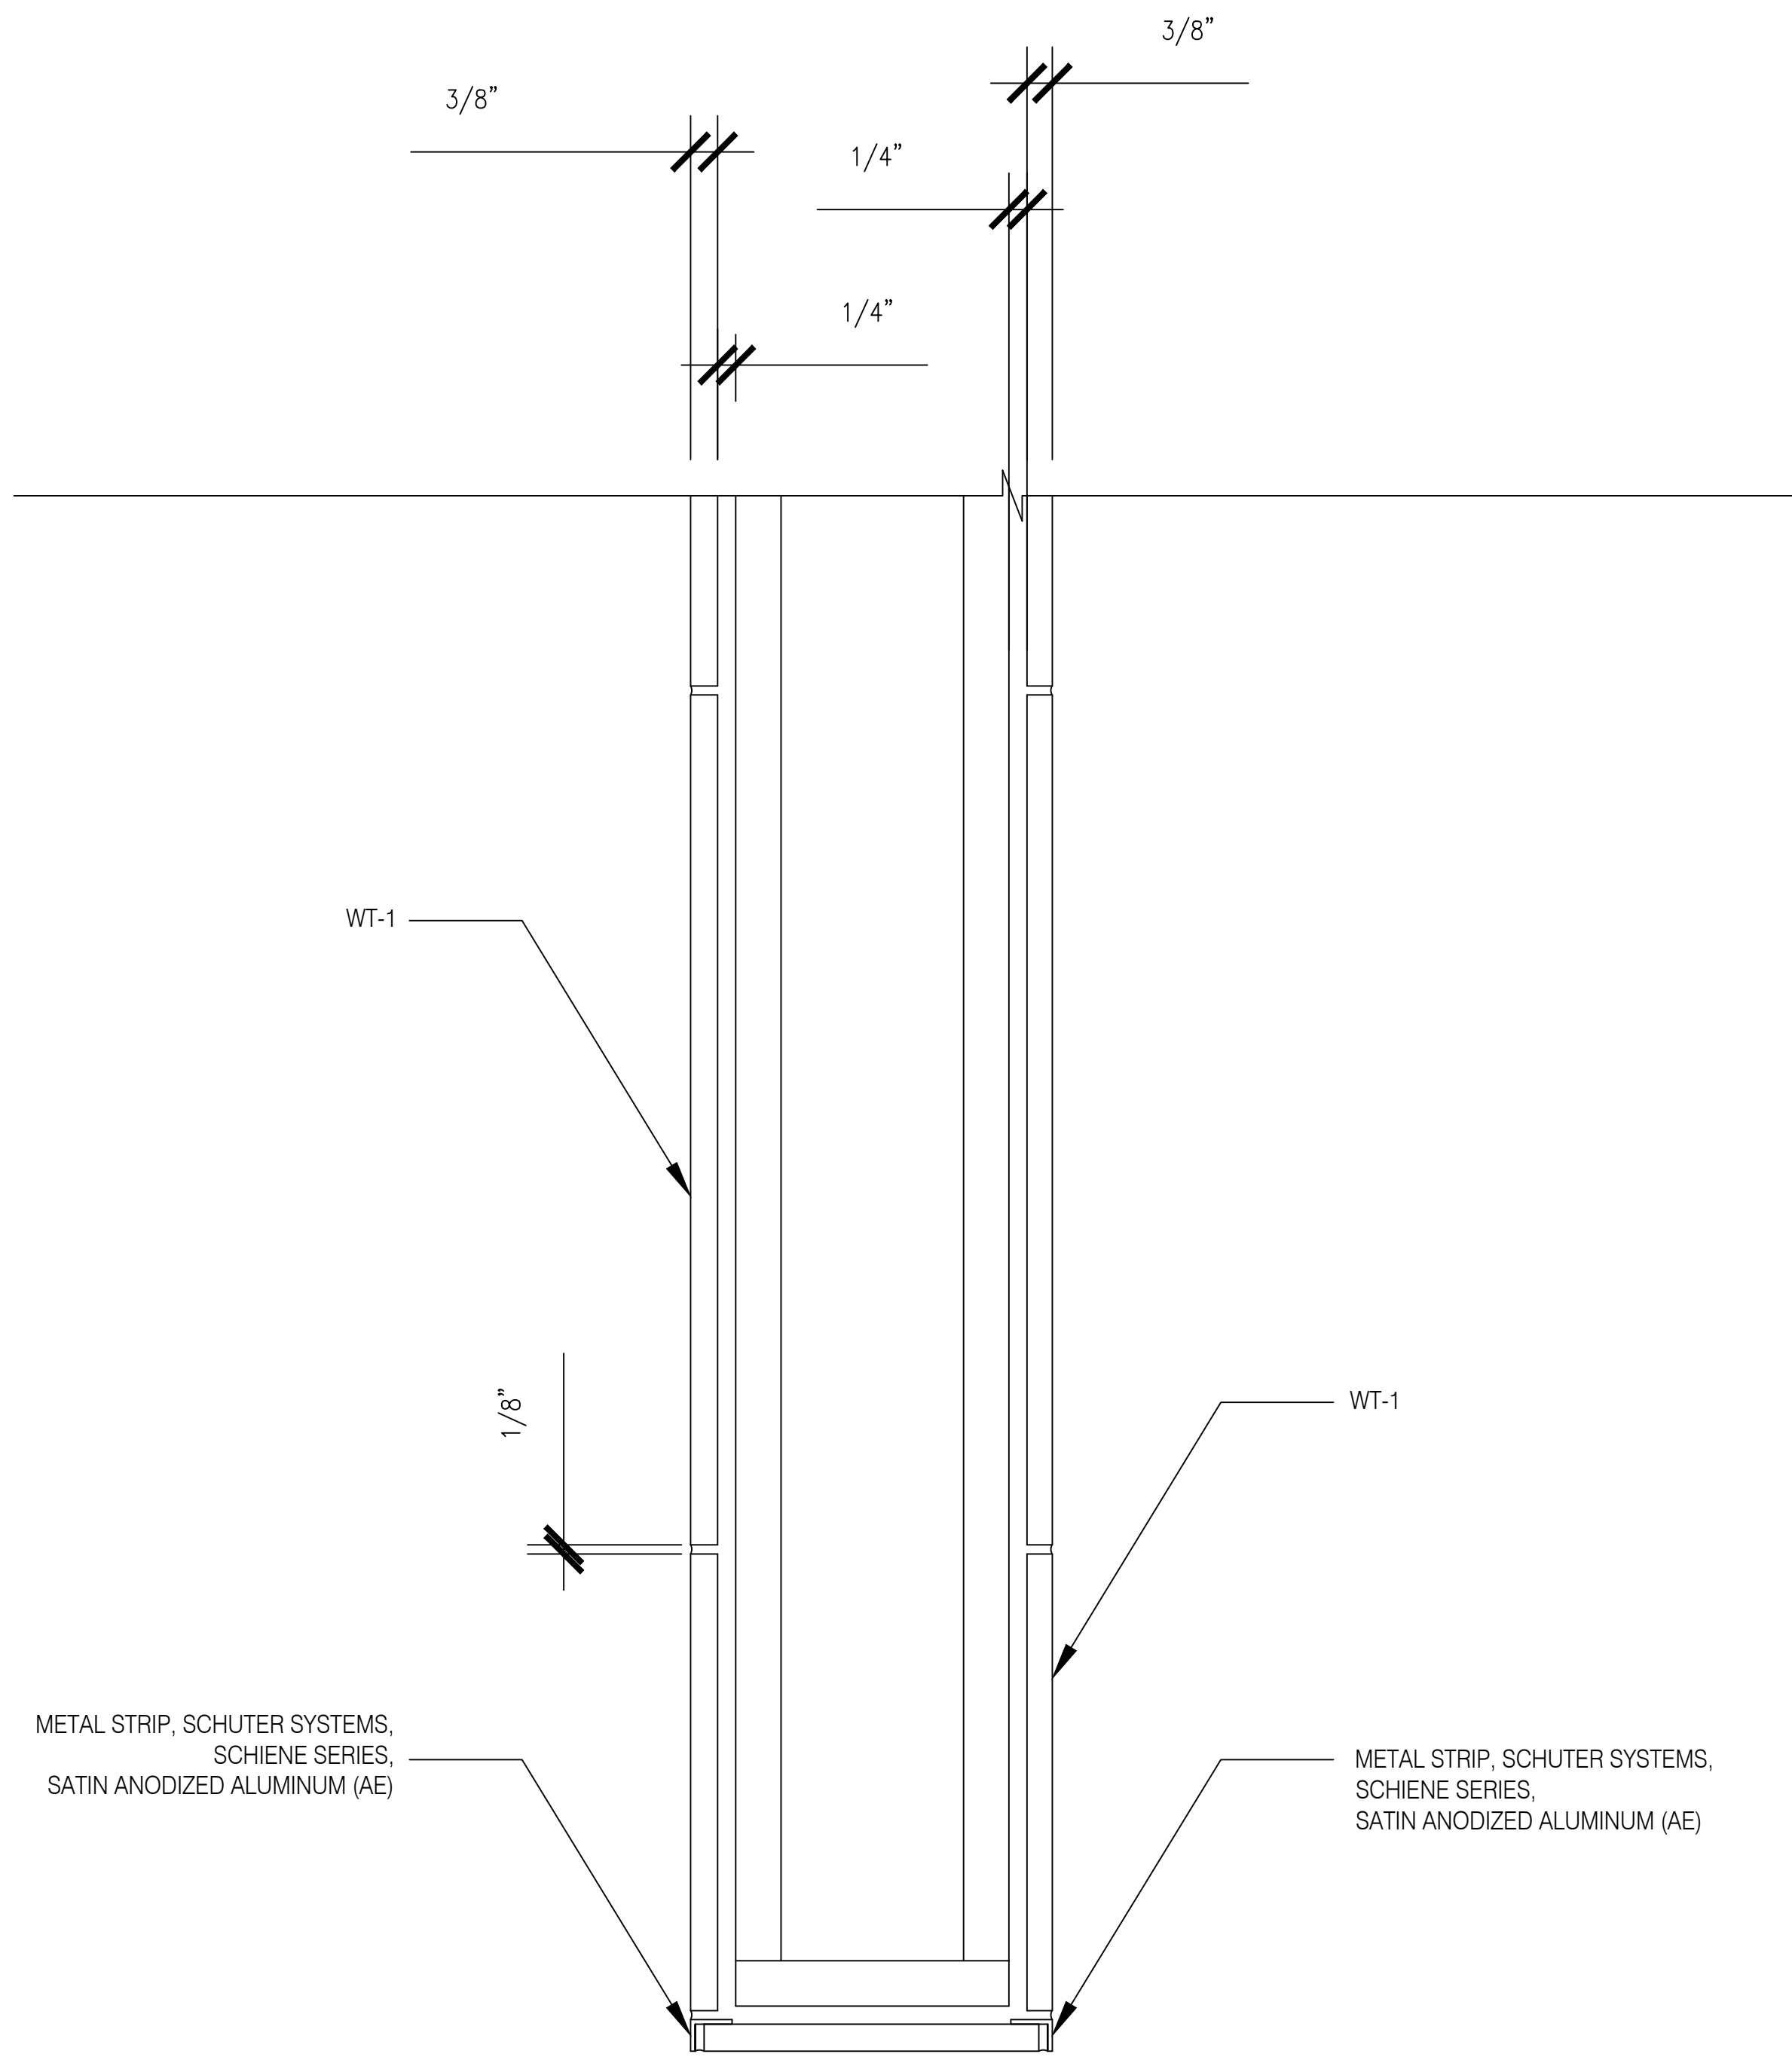

01
DETAIL: WALL TILE CORNERS

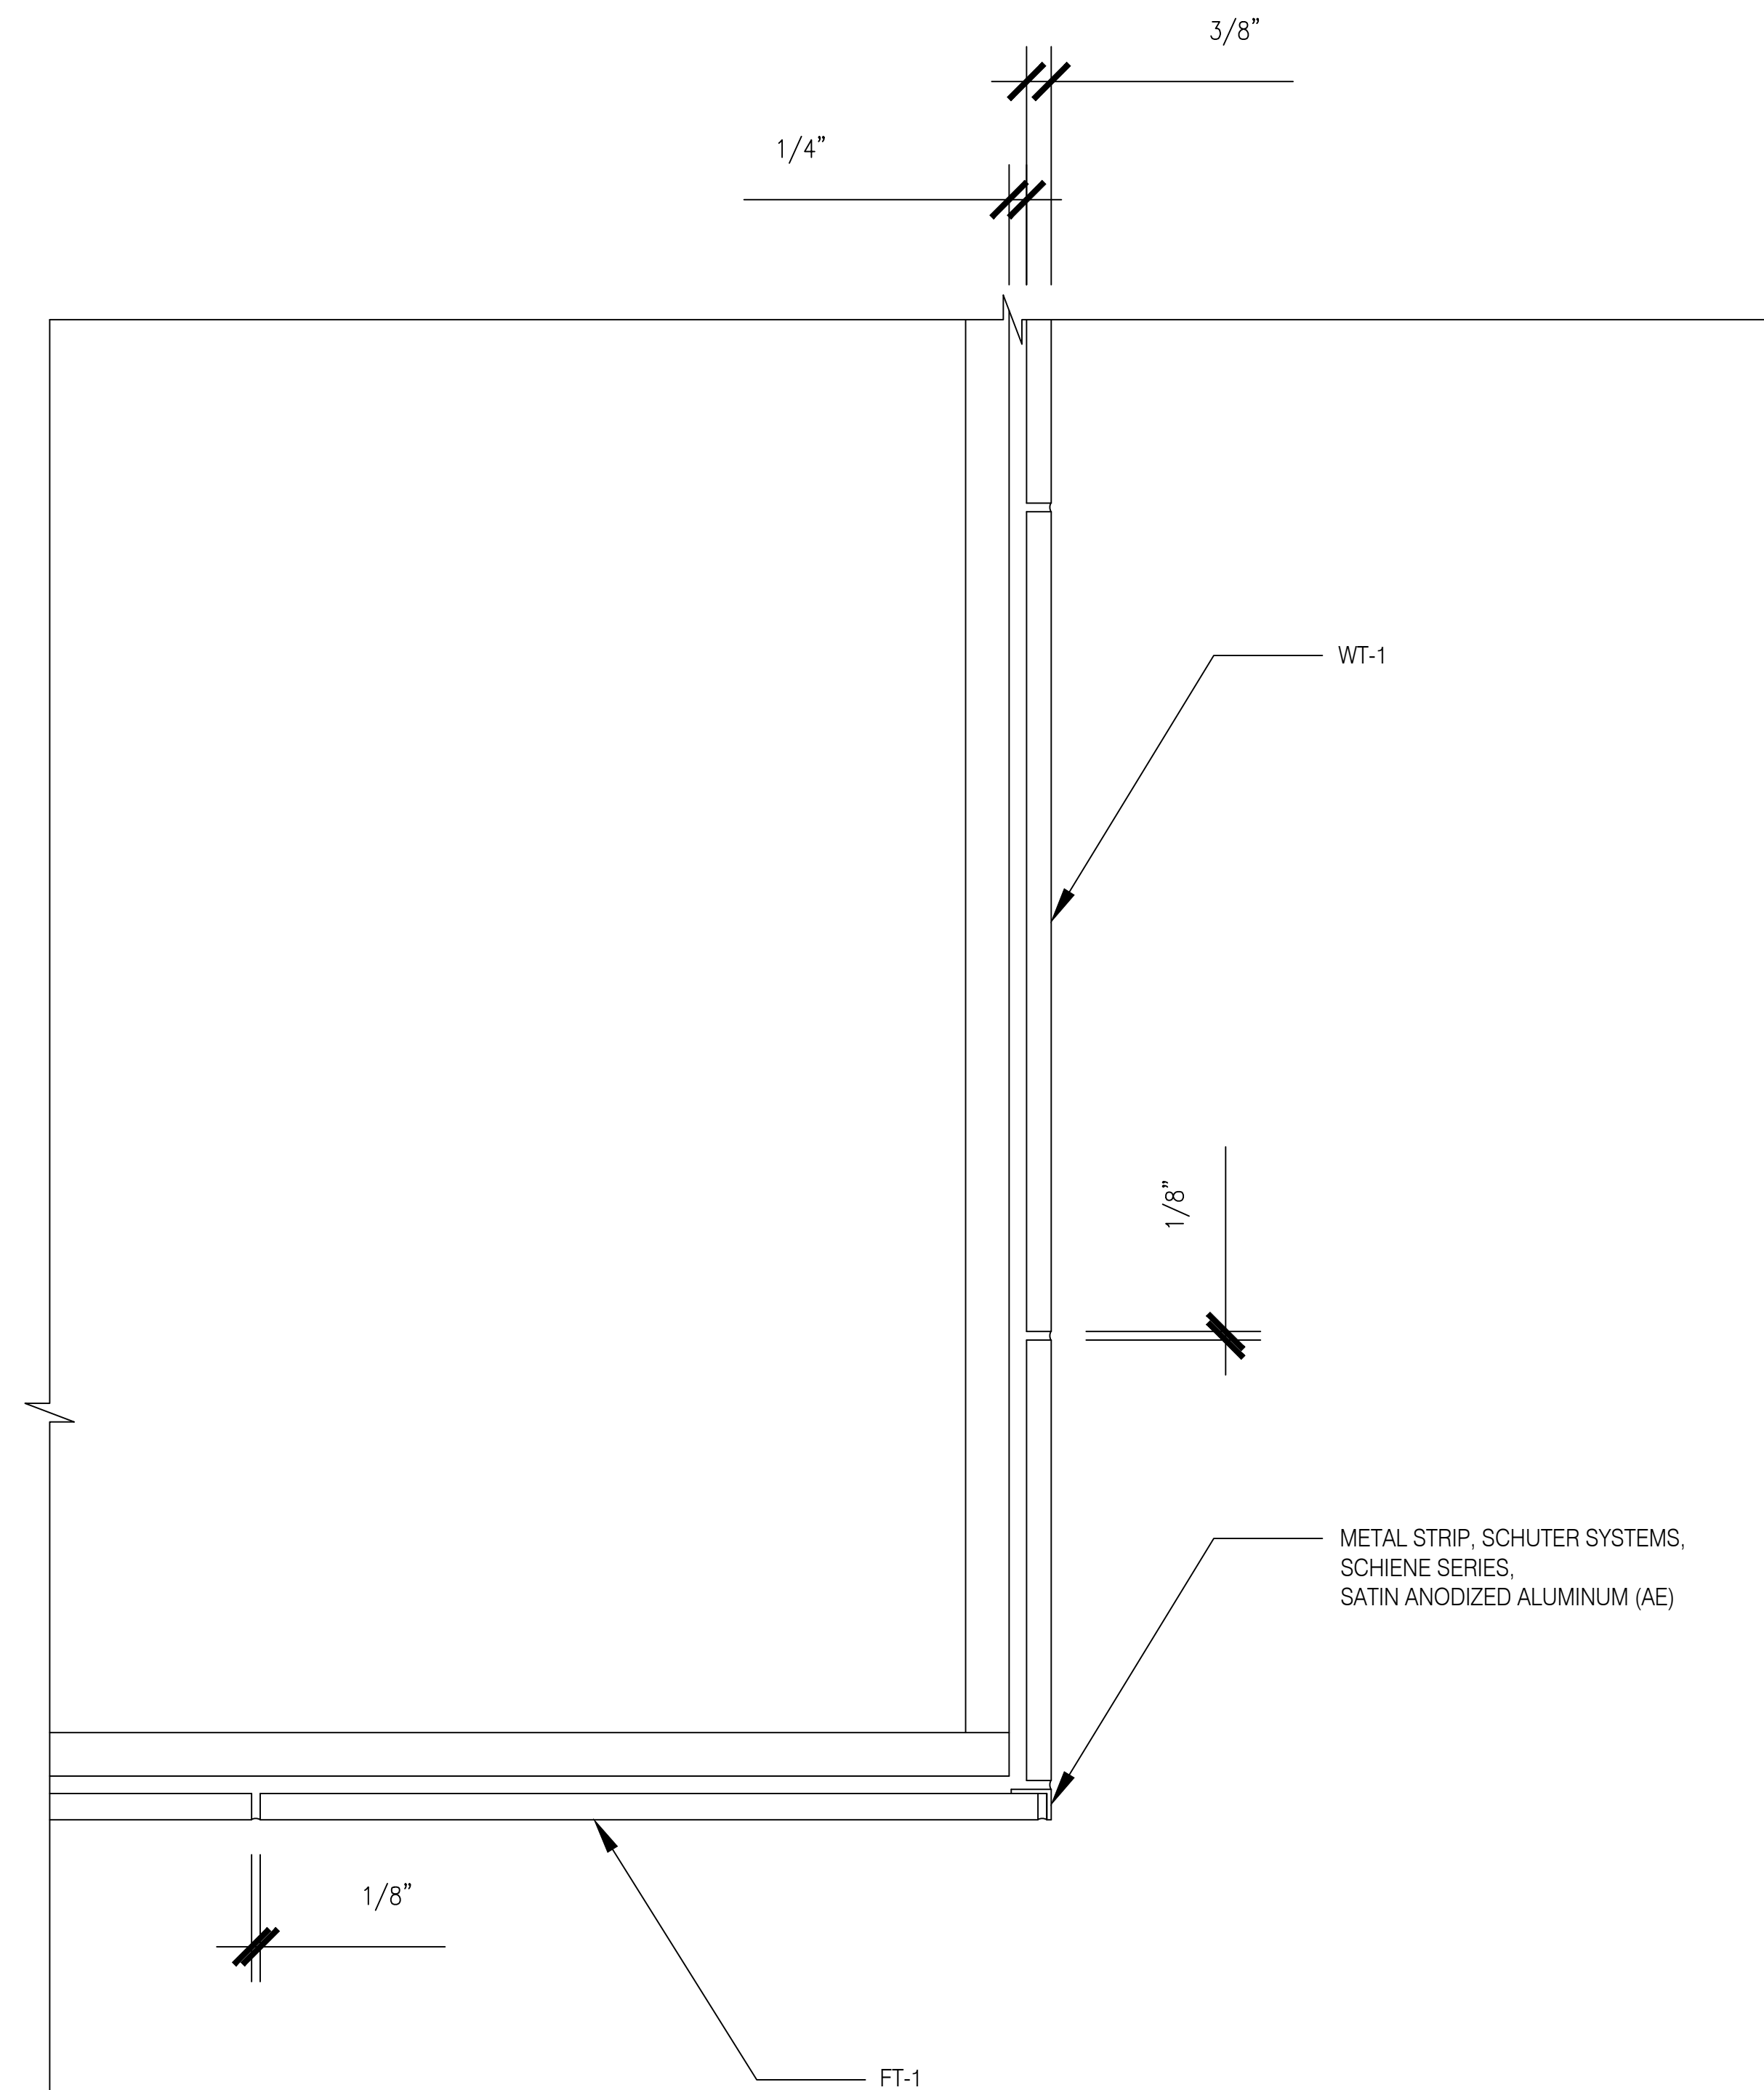

02
DETAIL: WALL TILE CORNERS

AUSTRO TILE & STONE, LLC
30-25 93RD STREET
EAST ELMHURST, NY 11369

CONTRACTOR:
JRM CONSTRUCTION
MANAGEMENT, LLC
242 WEST 36TH STREET
11TH FLOOR
NEW YORK, NY 10018

INTERIOR DESIGNER:

ISSUE FOR APPROVAL	10/09/23
ISSUE NAME	DATE

ARCHITECT:
SPACESMITH
ONE NEW YORK PLAZA SUITE 4200
NEW YORK, NY 10004
PH: 212 620 5583

PROJECT NAME:
JACK RESNICK & SONS
255 GREENWICH STREET
NEW YORK, NY 10007

SHEET NAME:
DETAILS
TILE

DATE:	
PROJECT NO.:	
PRINCIPAL:	
DRAWING BY:	
CHECKED BY:	
SCALE:	
DWG No.:	
T-601	
28 of 29	

